



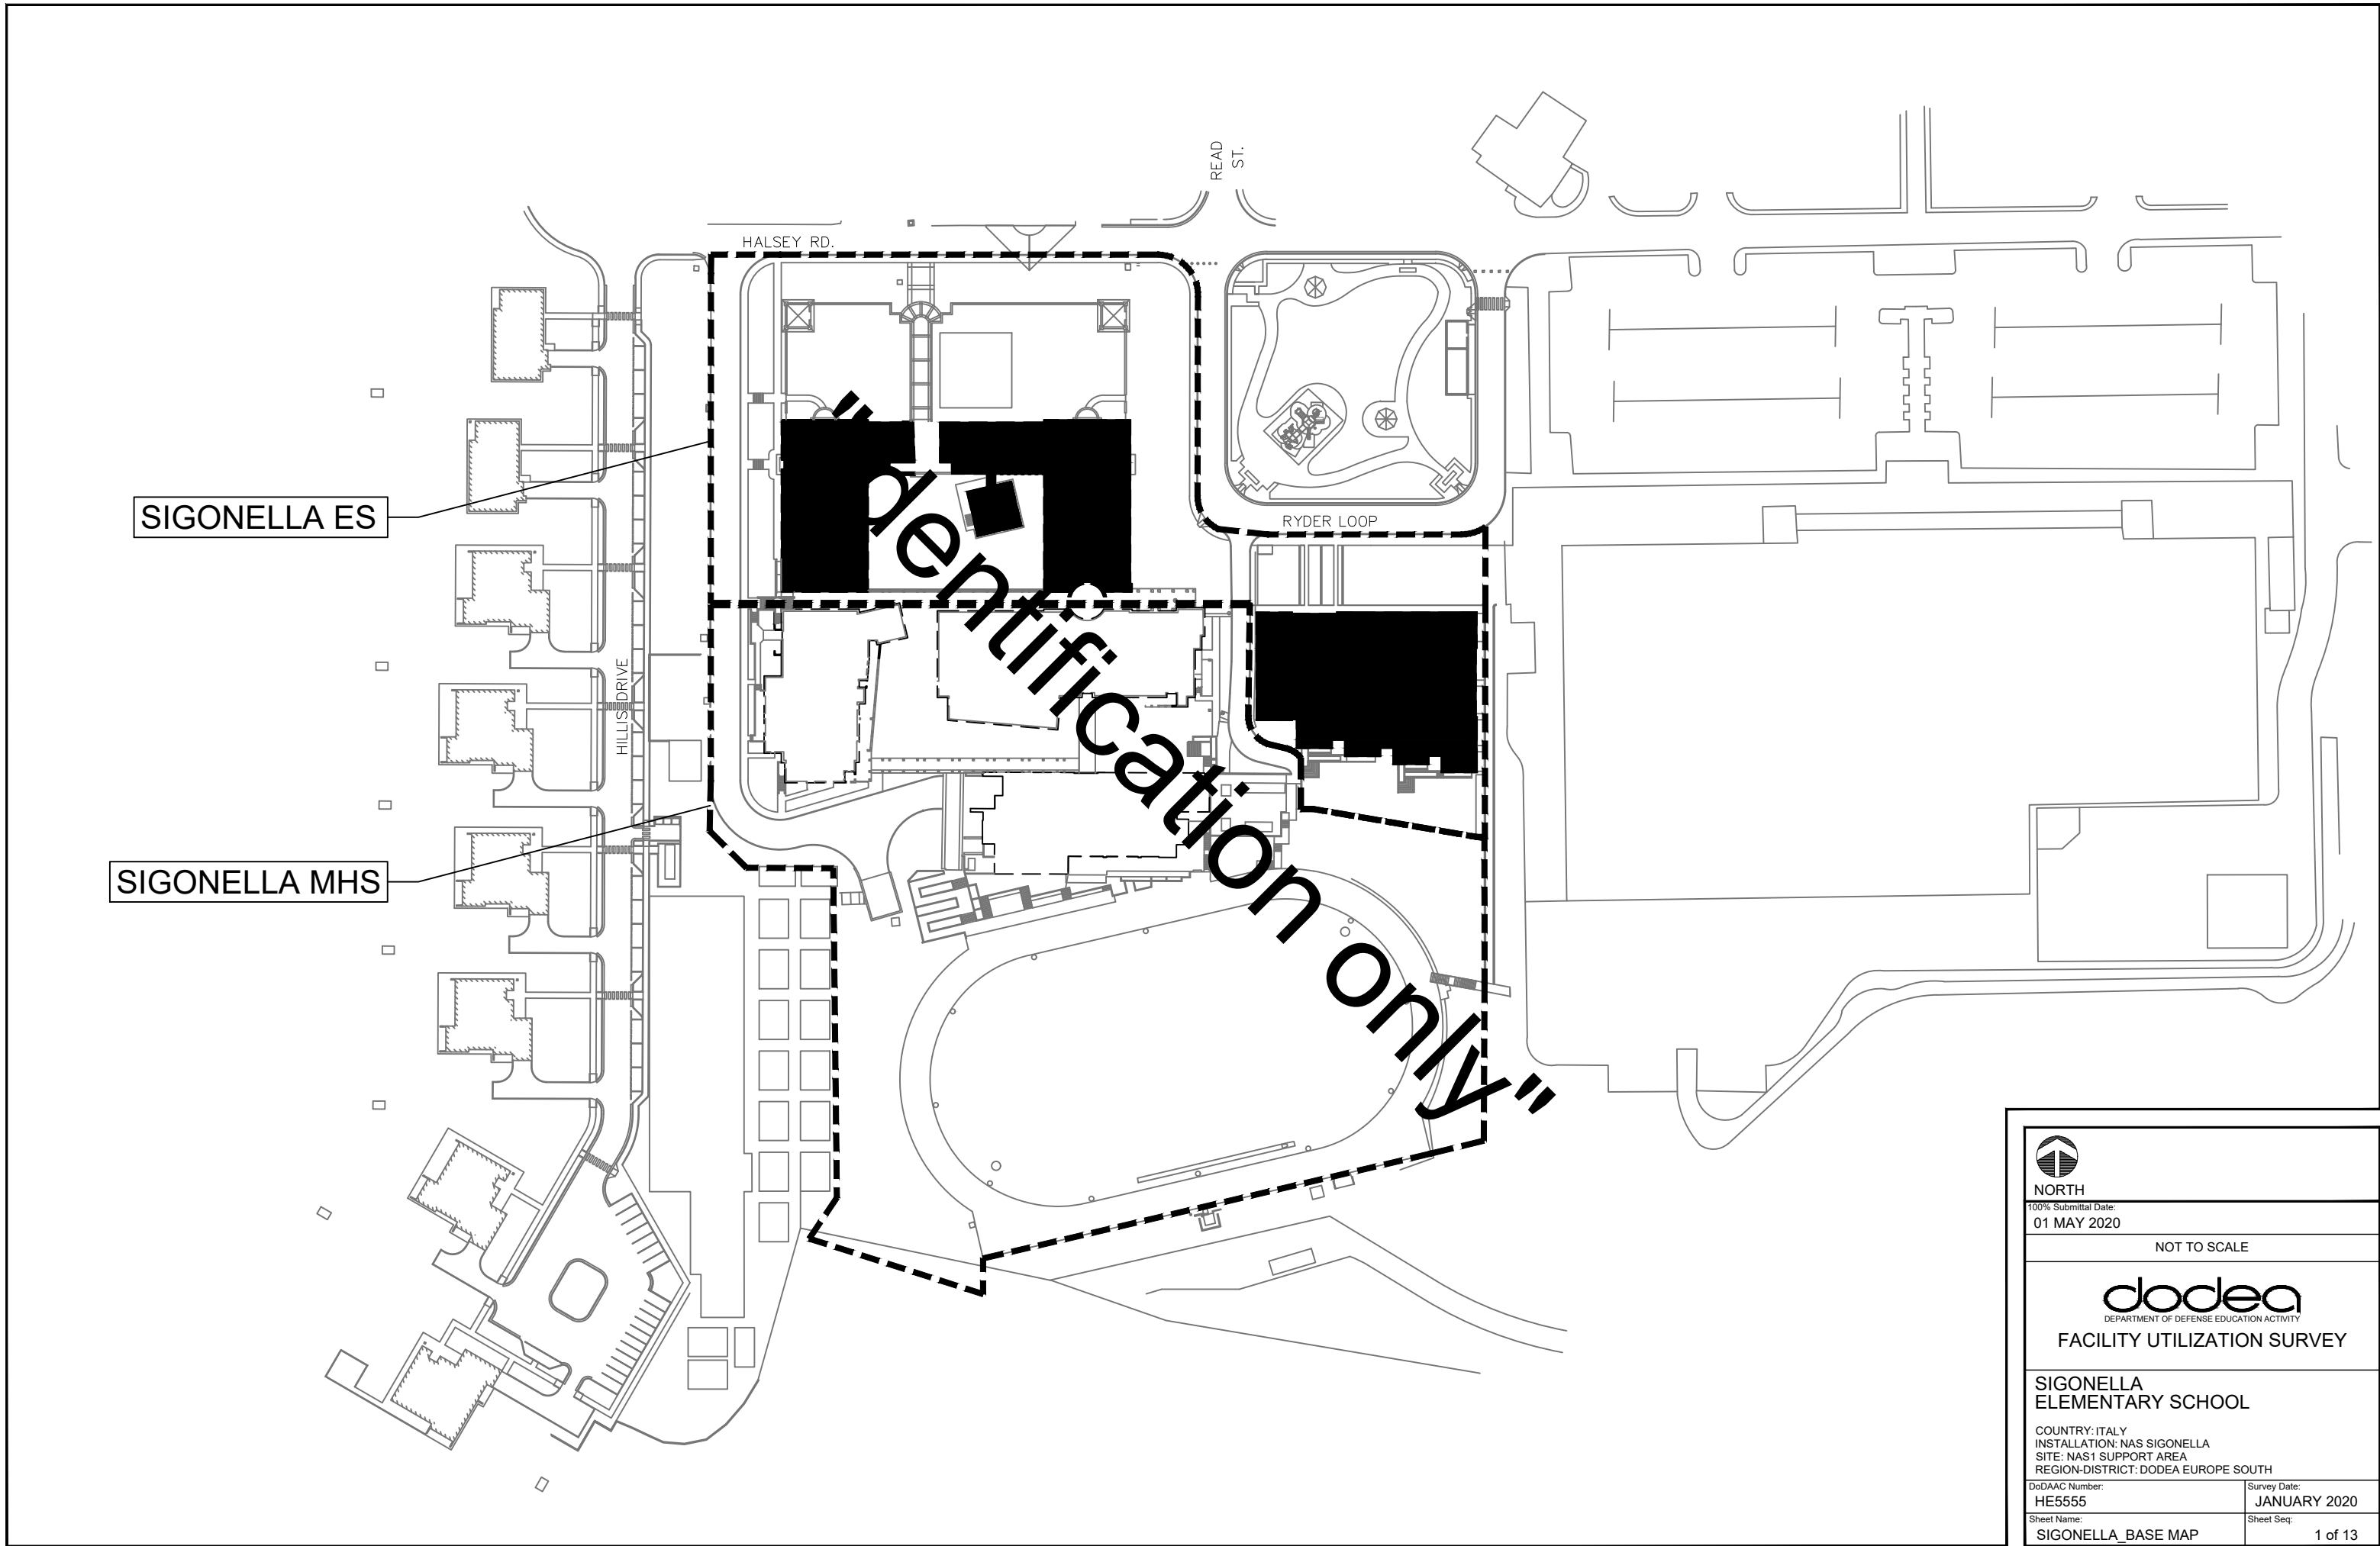


 NORTH	
100% Submittal Date: 01 MAY 2020	
NOT TO SCALE	
 DEPARTMENT OF DEFENSE EDUCATION ACTIVITY FACILITY UTILIZATION SURVEY	
SIGONELLA ELEMENTARY SCHOOL	
COUNTRY: ITALY INSTALLATION: NAS SIGONELLA SITE: NAS1 SUPPORT AREA REGION-DISTRICT: DODEA EUROPE SOUTH	
DoDAAC Number: HE5555	Survey Date: JANUARY 2020
Sheet Name: SIGONELLA_BASE MAP	Sheet Seq: 1 of 13

Sigonella ES
Building 218
Main Building - Floor 1
2008

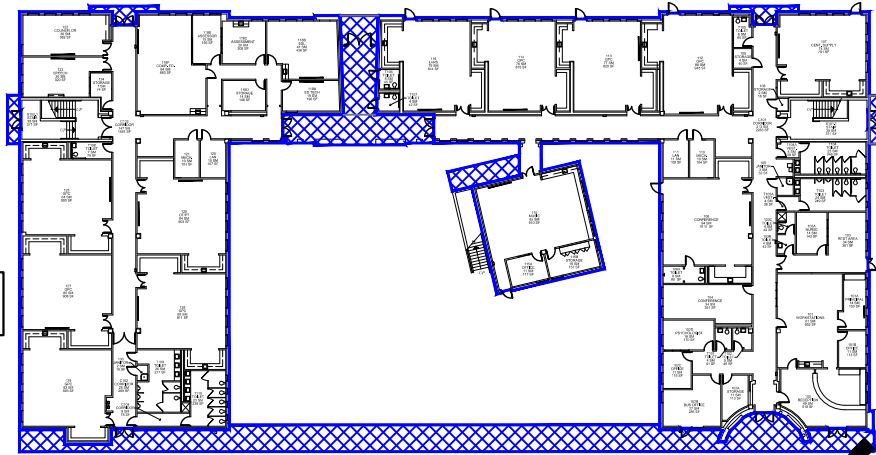


BUILDING 218 - FIRST FLOOR

Sigonella ES
Building 218
Main Building - Floor 2
2008

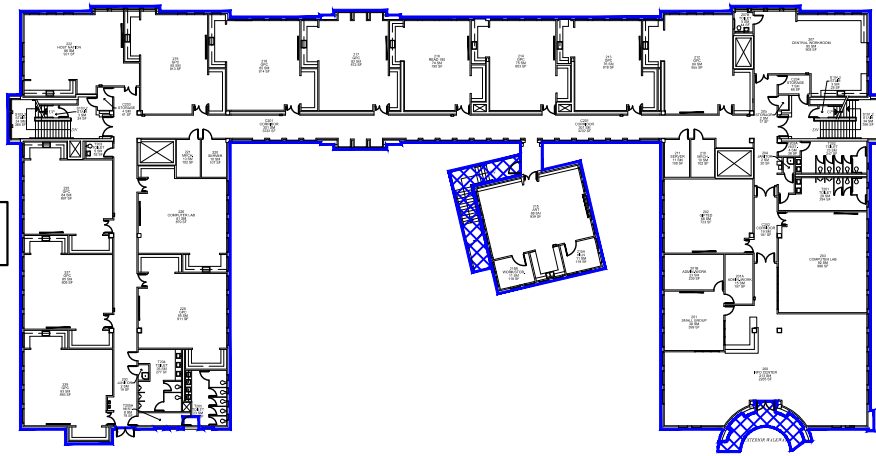


BUILDING 218 - SECOND FLOOR

Sigonella ES
Building 218
Main Building - Floor 3
2008

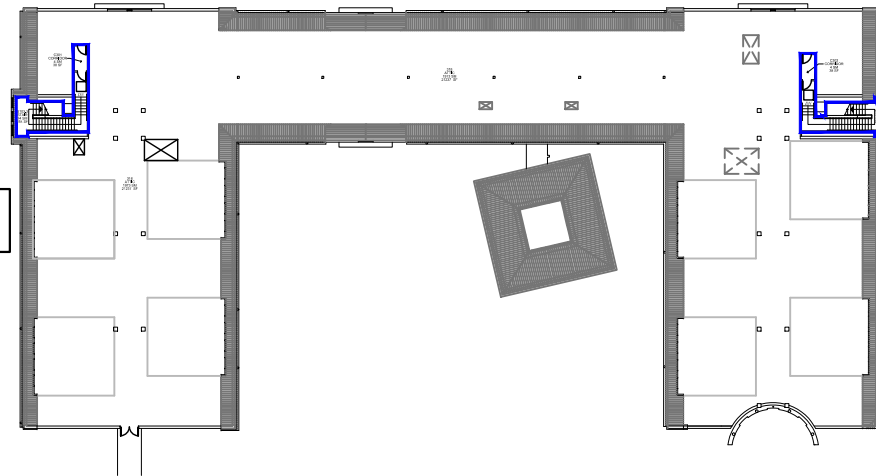

BUILDING 218 - THIRD FLOOR

Sigonella ES
Building 213
Main Building - Floor 1
1999

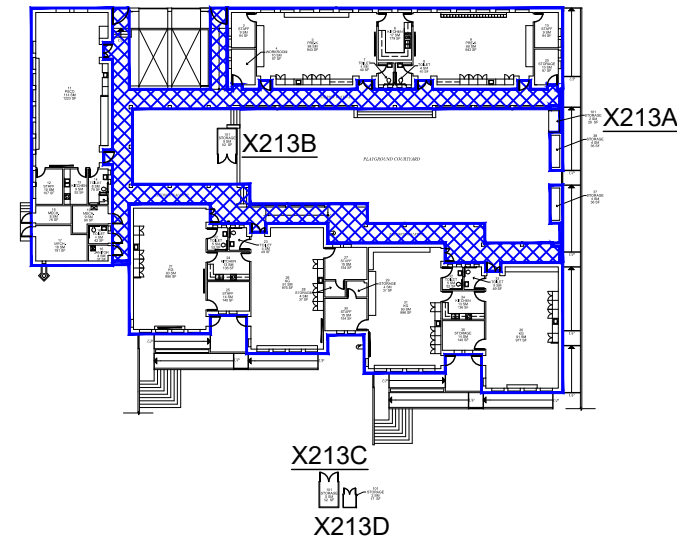

BUILDING 213 - FIRST FLOOR

GSF CALCULATIONS

Building 213	
Floor 1	11,314
Total Area (SF)	11,314
50% Area (SF)	1,478
Gross Area (SF)	12,792

Building 218	
Floor 1	26,297
Floor 2	27,471
Floor 3	716
Total Area (SF)	54,484
50% Area (SF)	2,122
Gross Area (SF)	56,606

NOTE 1: APPROXIMATELY 22% OF BUILDING 211 IS OCCUPIED BY SIGONELLA ES (SHOWN ON SIGONELLA MHS FUS DRAWING).

NOTE 2: GSF CALCULATIONS BASED ON ARMY RPI DoA PAMPHLET 415-28.

DOOR

SLIDING DOOR

ACCORDION PARTITION

STACK OR FOLDING PARTITION

WINDOW/GLAZING

HIGH WINDOW

SKYLIGHT

STOOP/STEP UP

STAIR

RAMP

ACCESS LADDER

COLD STORAGE

AREA CALCULATED @ 50 %

SLOPING ROOF

DRINKING FOUNTAIN

LAVATORY

SINK

TOILET

URINAL

LOCKER

LAN DISTRIBUTION FRAME

VENT HOOD

WALL SHELVING

UPPER CABINET

BASE CABINET

TEACHER CABINET

MATCHLINE

FLAT ROOF

TITLEBLOCK LEGEND

SHEET NAME:

BLDG #_FLOOR # (# IN SERIES)

KEY PLAN

NTS

NORTH

Updated By: AA

FUS Review: MRS

100% Submittal Date: 01 MAY 2020

NOT TO SCALE

dodea

DEPARTMENT OF DEFENSE EDUCATION ACTIVITY

FACILITY UTILIZATION SURVEY

SIGONELLA ELEMENTARY SCHOOL

BUILDING NUMBER: 213, 218, X213A-D

COUNTRY: ITALY

INSTALLATION: NAS SIGONELLA

SITE: NAS1 SUPPORT AREA

REGION-DISTRICT: DODEA EUROPE SOUTH

DoDAAC Number: HE5555

Survey Date: JANUARY 2020

Sheet Name: GSF_1 (1)

Sheet Seq: 4 of 13

213						218					
Floor	Room	Current	Capacity	Area (SF)	Area (SM)	Floor	Room	Current	Capacity	Area (SF)	Area (SM)
1	3	STAFF	OTHER	84 SF	9 SM	1	T119	TOILET	NET - GENERAL	239 SF	23 SM
1	4	WORKROOM	OTHER	87 SF	10 SM	2	209	INFO CENTER	OTHER	2,285 SF	213 SM
1	5	PRE-K	STUDENT - FULL	943 SF	88 SM	2	201	SMALL GROUP	OTHER	399 SF	38 SM
1	6	KITCHEN	OTHER	179 SF	17 SM	2	201A	ADMIN/WORK	OTHER	167 SF	15 SM
1	7	TOILET	NET - GENERAL	46 SF	4 SM	2	201B	ADMIN/WORK	OTHER	239 SF	23 SM
1	8	TOILET	NET - GENERAL	46 SF	4 SM	2	202	GFITED	STUDENT - FULL	723 SF	68 SM
1	9	PRE-K	STUDENT - FULL	943 SF	88 SM	2	203	COMPUTER LAB	STUDENT - FULL	988 SF	92 SM
1	10	STAFF	OTHER	84 SF	9 SM	2	204	JANITOR	NET - GENERAL	20 SF	2 SM
1	11	PSOD	STUDENT - FULL	1,223 SF	114 SM	2	205	STORAGE	OTHER	17 SF	2 SM
1	12	STAFF	OTHER	107 SF	10 SM	2	207	CENTRAL WORKROOM	OTHER	926 SF	85 SM
1	13	KITCHEN	OTHER	82 SF	9 SM	2	207A	TOILET	NET - GENERAL	44 SF	5 SM
1	14	TOILET	NET - GENERAL	76 SF	8 SM	2	210	MECH.	NET - MECH	102 SF	10 SM
1	15	MECH.	NET - MECH	76 SF	8 SM	2	211	SERVER	NET - MECH	108 SF	11 SM
1	16	JANITOR	NET - GENERAL	37 SF	4 SM	2	212	GPC	STUDENT - FULL	955 SF	89 SM
1	17	MECH.	NET - MECH	181 SF	18 SM	2	213	GPC	STUDENT - FULL	818 SF	76 SM
1	18	TOILET	NET - GENERAL	42 SF	4 SM	2	214	GPC	STUDENT - FULL	803 SF	75 SM
1	19	MECH.	NET - MECH	88 SF	9 SM	2	215	ART	STUDENT - FULL	928 SF	88 SM
1	20	STORAGE	OTHER	87 SF	10 SM	2	215A	NLN	OTHER	118 SF	11 SM
1	21	KG	STUDENT - FULL	888 SF	83 SM	2	215B	WORK/STOR.	OTHER	118 SF	11 SM
1	22	TOILET	NET - GENERAL	52 SF	5 SM	2	216	READ/180	STUDENT - FULL	789 SF	74 SM
1	23	TOILET	NET - GENERAL	49 SF	5 SM	2	217	GPC	STUDENT - FULL	872 SF	82 SM
1	24	KITCHEN	OTHER	136 SF	13 SM	2	218	GPC	STUDENT - FULL	914 SF	85 SM
1	25	STAFF	OTHER	143 SF	14 SM	2	219	GPC	STUDENT - FULL	913 SF	85 SM
1	26	KG	STUDENT - FULL	879 SF	91 SM	2	220	SERVER	NET - MECH	107 SF	10 SM
1	27	STAFF	OTHER	154 SF	15 SM	2	221	MECH.	NET - MECH	102 SF	10 SM
1	28	STORAGE	OTHER	37 SF	4 SM	2	222	HOST NATION	STUDENT - FULL	921 SF	86 SM
1	29	STORAGE	OTHER	37 SF	4 SM	2	225	GPC	STUDENT - FULL	887 SF	84 SM
1	30	STAFF	OTHER	154 SF	15 SM	2	226	COMPUTER LAB	STUDENT - FULL	870 SF	81 SM
1	31	KG	STUDENT - FULL	886 SF	83 SM	2	227	GPC	STUDENT - FULL	908 SF	85 SM
1	32	TOILET	NET - GENERAL	52 SF	5 SM	2	228	GPC	STUDENT - FULL	911 SF	85 SM
1	33	TOILET	NET - GENERAL	49 SF	5 SM	2	229	GPC	STUDENT - FULL	883 SF	83 SM
1	34	KITCHEN	OTHER	136 SF	13 SM	2	230	JANITOR	NET - GENERAL	19 SF	2 SM
1	35	STORAGE	OTHER	140 SF	14 SM	2	C201	CORRIDOR	NET - GENERAL	5,232 SF	301 SM
1	36	KG	STUDENT - FULL	977 SF	91 SM	2	C202	CORRIDOR	NET - GENERAL	197 SF	19 SM
1	37	STORAGE	OTHER	36 SF	4 SM	2	C203	STORAGE	OTHER	41 SF	4 SM
1	38	STORAGE	OTHER	36 SF	4 SM	2	C204	STORAGE	OTHER	68 SF	7 SM
218						2	S101.2	STAIR	NET - VERTICAL	356 SF	34 SM
Floor	Room	Current	Capacity	Area (SF)	Area (SM)	2	S102.2	STAIR	NET - VERTICAL	364 SF	34 SM
1	100	RECEPTION	OTHER	518 SF	49 SM	2	S103.2	STAIR	NET - VERTICAL	24 SF	3 SM
1	101	WORKSTATIONS	OTHER	682 SF	61 SM	2	S104.2	STAIR	NET - VERTICAL	26 SF	3 SM
1	101A	PRINCIPAL	OTHER	150 SF	14 SM	2	T201	TOILET	NET - GENERAL	294 SF	28 SM
1	101B	OFFICE	OTHER	113 SF	11 SM	2	T202	TOILET	NET - GENERAL	247 SF	23 SM
1	102A	STORAGE	OTHER	113 SF	11 SM	2	T202A	VEST.	NET - GENERAL	38 SF	4 SM
1	102B	BUS OFFICE	OTHER	288 SF	27 SM	2	T203	TOILET	NET - GENERAL	52 SF	5 SM
1	102C	OFFICE	OTHER	118 SF	11 SM	2	T204	TOILET	NET - GENERAL	277 SF	26 SM
1	102D	PSYCHOLOGIST	OTHER	170 SF	16 SM	2	T205	TOILET	NET - GENERAL	238 SF	23 SM
1	103	REST AREA	OTHER	381 SF	34 SM	2	T205A	VEST.	NET - GENERAL	78 SF	8 SM
1	103A	NURSE	OTHER	142 SF	14 SM	3	C301	CORRIDOR	NET - GENERAL	38 SF	4 SM
1	103B	TOILET	OTHER	42 SF	4 SM	3	C302	CORRIDOR	NET - GENERAL	38 SF	4 SM
1	103C	TOILET	OTHER	42 SF	4 SM	3	S103.3	STAIR	NET - VERTICAL	254 SF	24 SM
1	104	CONFERENCE	OTHER	381 SF	34 SM	3	S104.3	STAIR	NET - VERTICAL	278 SF	26 SM
1	105	JANITOR	NET - GENERAL	52 SF	5 SM						
1	106	CONFERENCE	OTHER	1,070 SF	94 SM						
1	106A	TOILET	NET - GENERAL	86 SF	9 SM						
1	107	CENT. SUPPLY	OTHER	781 SF	74 SM						
1	108	STORAGE	OTHER	16 SF	2 SM						
1	109	STORAGE	OTHER	40 SF	4 SM						
1	110	MECH.	NET - MECH	104 SF	10 SM						
1	111	LAN	NET - MECH	108 SF	11 SM						
1	112	GPC	STUDENT - FULL	849 SF	80 SM						
1	113	GPC	STUDENT - FULL	820 SF	77 SM						
1	114	GPC	STUDENT - FULL	819 SF	76 SM						
1	115	MUSIC	STUDENT - FULL	910 SF	85 SM						
1	115A	OFFICE	OTHER	117 SF	11 SM						
1	115B	STORAGE	OTHER	137 SF	15 SM						
1	116	LABS	STUDENT - FULL	844 SF	79 SM						
1	116A	ED TECH	OTHER	186 SF	19 SM						
1	116B	ESL	STUDENT - HALF	436 SF	41 SM						
1	116C	ASSESSMENT	OTHER	208 SF	20 SM						
1	116D	STORAGE	OTHER	148 SF	14 SM						
1	116E	ASSESSOR	OTHER	156 SF	15 SM						
1	116F	COMP. ED.	STUDENT - FULL	683 SF	64 SM						
1	120	LAN	NET - MECH	107 SF	10 SM						
1	121	MECH.	NET - MECH	104 SF	10 SM						
1	122	COUNSELOR	OTHER	162 SF	16 SM						
1	123	SPEECH	STUDENT - HALF	309 SF	30 SM						
1	124	STORAGE	OTHER	74 SF	7 SM						
1	125	GPC	STUDENT - FULL	900 SF	84 SM						
1	126	OT/PT	STUDENT - FULL	903 SF	84 SM						
1	127	GPC	STUDENT - FULL	908 SF	85 SM						
1	128	GPC	STUDENT - FULL	911 SF	85 SM						
1	129	GPC	STUDENT - FULL	883 SF	83 SM						
1	130	JANITOR	NET - GENERAL	78 SF	7 SM						
1	C101	CORRIDOR	NET - GENERAL	2,283 SF	213 SM						
1	C102	CORRIDOR	NET - GENERAL	289 SF	25 SM						
1	C103	CORRIDOR	NET - GENERAL	1,581 SF	147 SM						
1	C104	CORRIDOR	NET - GENERAL	78 SF	8 SM						
1	S101.1	STAIR	NET - VERTICAL	371 SF	35 SM						
1	S102.1	STAIR	NET - VERTICAL	371 SF	35 SM						
1	T101	TOILET	NET - GENERAL	41 SF	4 SM						
1	T102	TOILET	NET - GENERAL	45 SF	5 SM						
1	T103	TOILET	NET - GENERAL	249 SF	24 SM						
1	T103A	VEST.	NET - GENERAL	36 SF	4 SM						
1	T104	TOILET	NET - GENERAL	248 SF	23 SM						
1	T104A	VEST.	NET - GENERAL	39 SF	4 SM						
1	T105	TOILET	NET - GENERAL	69 SF	6 SM						
1	T106	TOILET	NET - GENERAL	45 SF	5 SM						
1	T107	TOILET	NET - GENERAL	42 SF	4 SM						
1	T108	TOILET	NET - GENERAL	75 SF	7 SM						
1	T109	TOILET	NET - GENERAL	277 SF	26 SM						

"identification only"

DOOR

SLIDING DOOR

ACCORDION PARTITION

STACK OR FOLDING PARTITION

WINDOW/GLAZING

HIGH WINDOW

SKYLIGHT

STOOP/STEP UP

STAIR

RAMP

ACCESS LADDER

COLD STORAGE

AREA CALCULATED @ 50 %

SLOPING ROOF

DRINKING FOUNTAIN

LAVATORY

SINK

TOILET

URINAL

LOCKER

LAN DISTRIBUTION FRAME

VENT HOOD

WALL SHELVING

UPPER CABINET

BASE CABINET

TEACHER CABINET

MATCHLINE

FLAT ROOF

TITLEBLOCK LEGEND

SHEET NAME:

BLDG #_FLOOR # (# IN SERIES)

KEY PLAN

NTS

218

213

X213B

X213A

X213C

X213D

NORTH

Updated By: AA

FUS Review: MRS

100% Submittal Date: 01 MAY 2020

NOT TO SCALE

dodea

DEPARTMENT OF DEFENSE EDUCATION ACTIVITY

FACILITY UTILIZATION SURVEY

SIGONELLA ELEMENTARY SCHOOL

BUILDING NUMBER: 213, 218, X213A-D

COUNTRY: ITALY

INSTALLATION: NAS SIGONELLA

SITE: NAS1 SUPPORT AREA

REGION-DISTRICT: DODEA EUROPE SOUTH


DoDAAC Number: HE5555


Floor: LEVEL 1-3

Survey Date: JANUARY 2020


Sheet Name: SCHEDULES (1)

Sheet Seq: 5 of 13

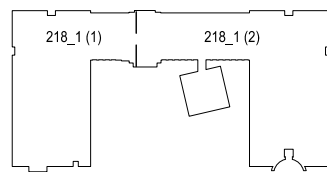

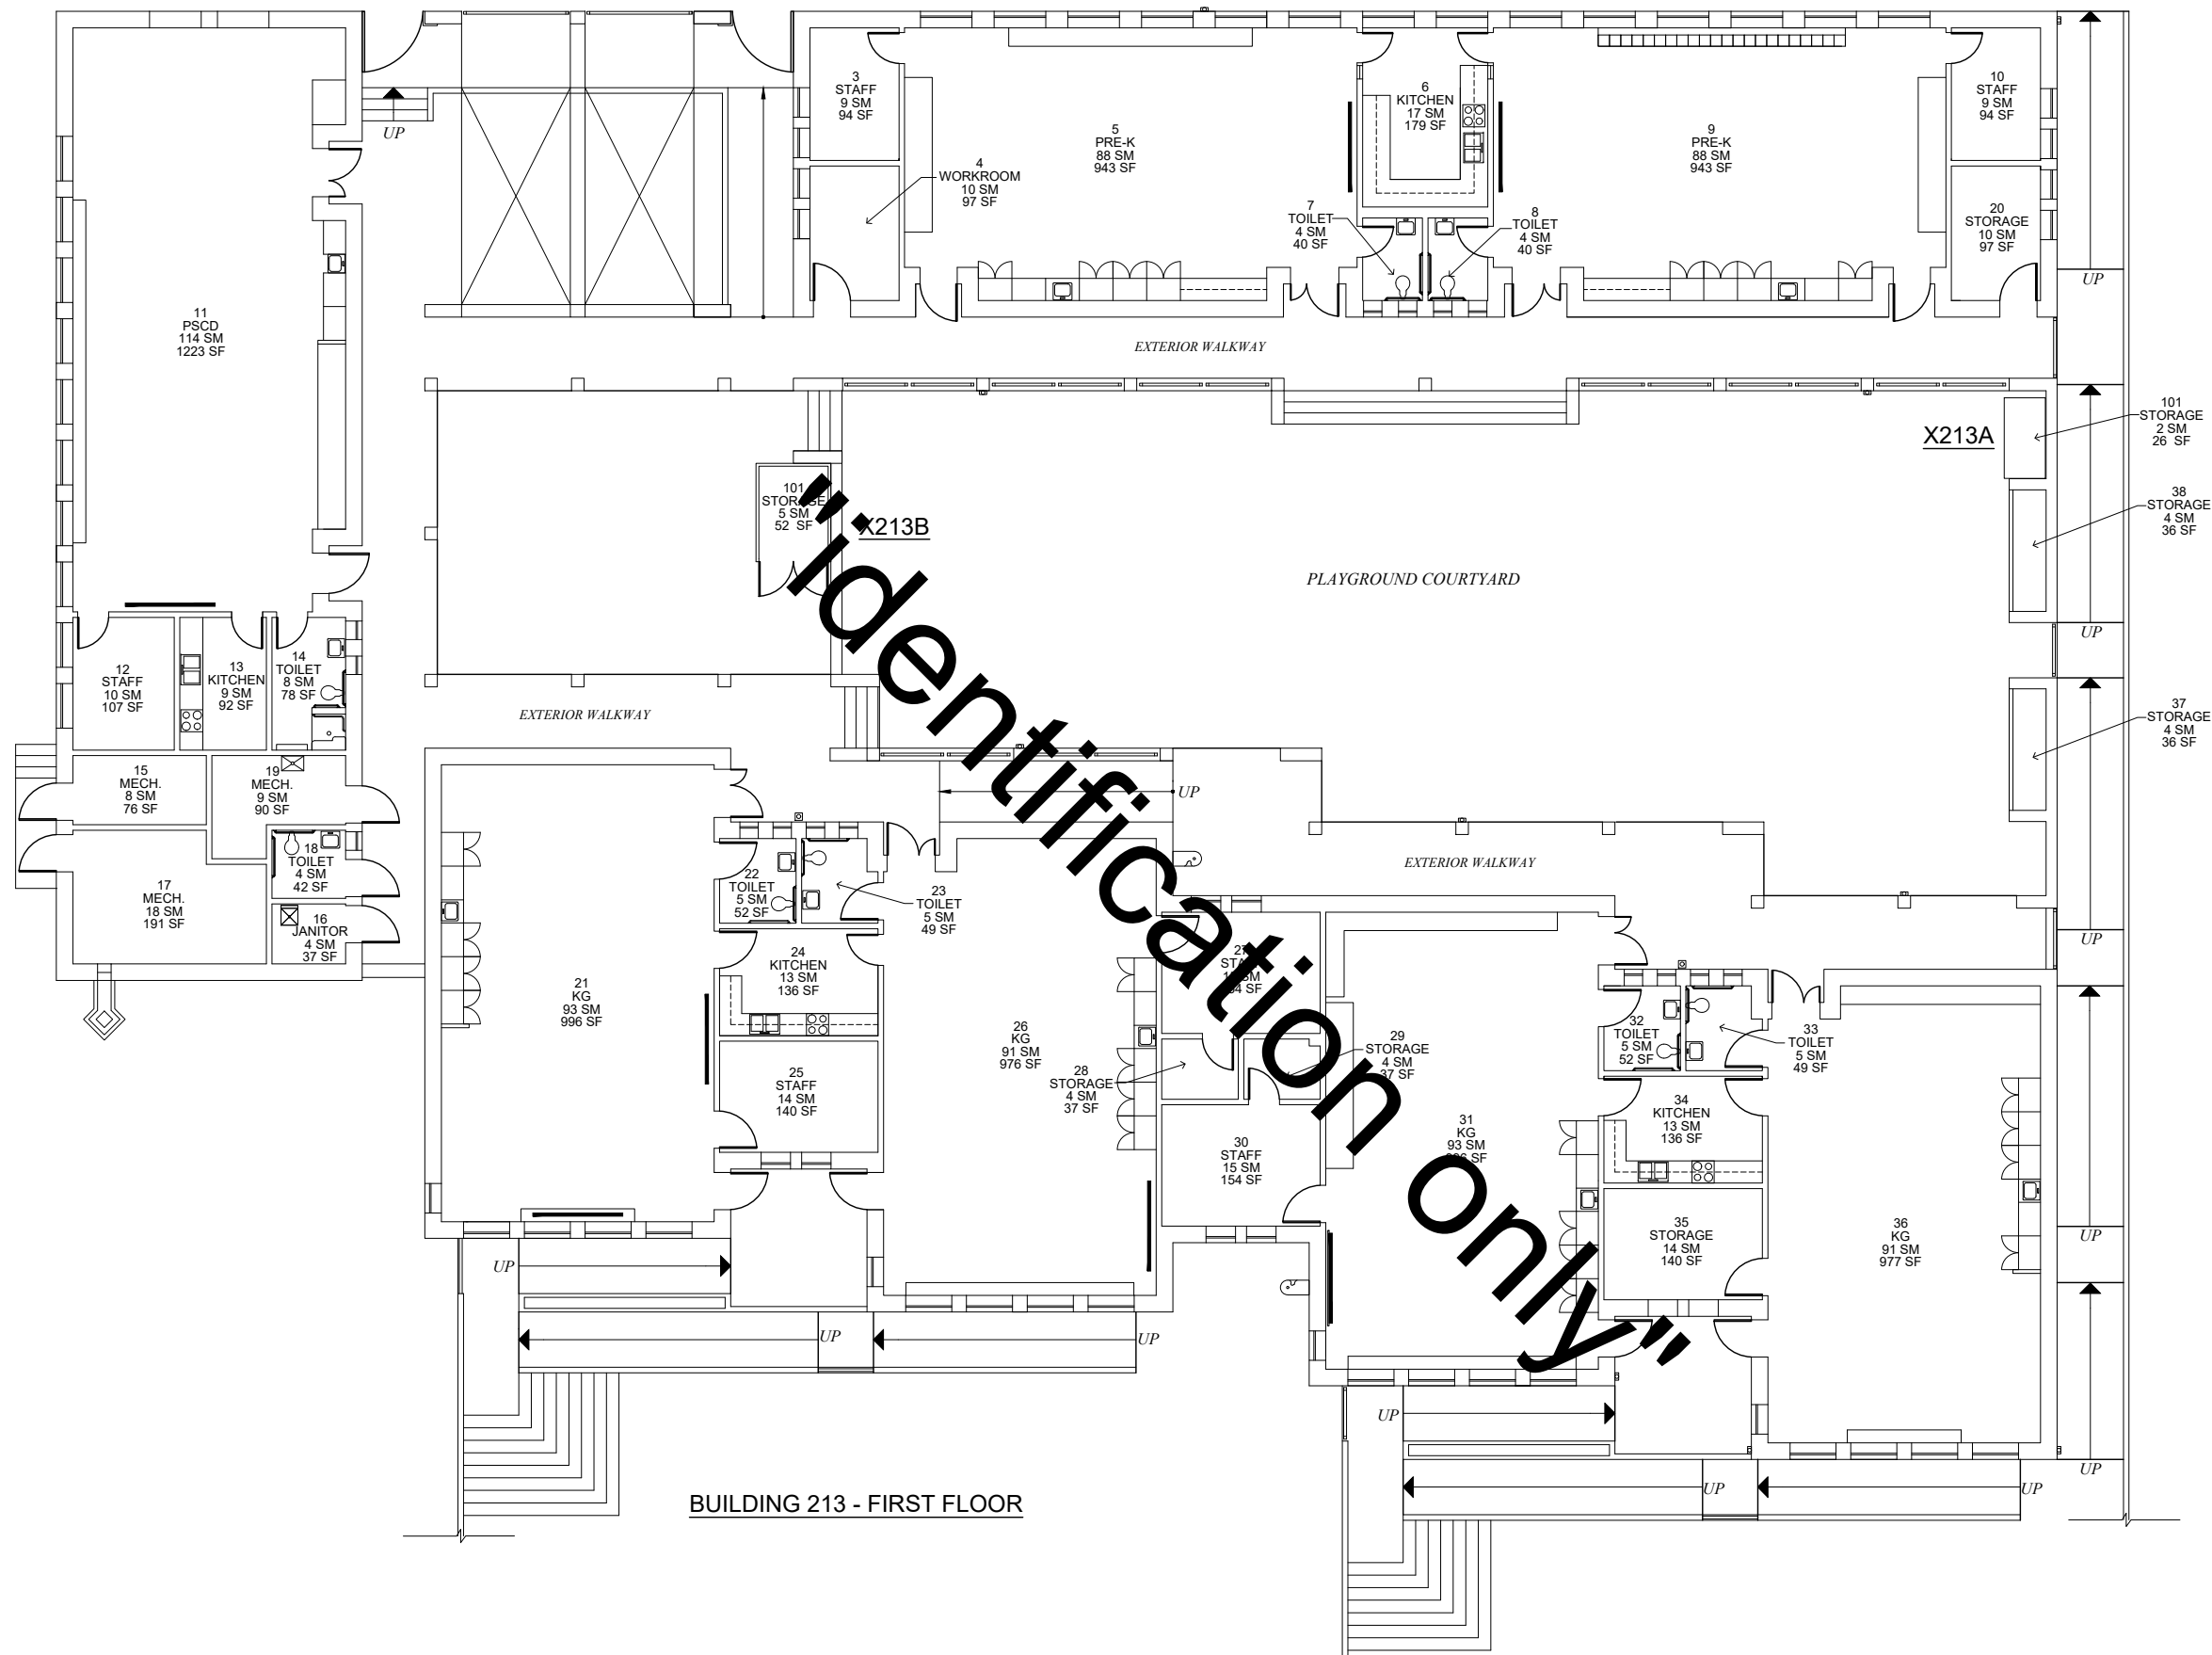

BUILDING 213 - FIRST FLOOR

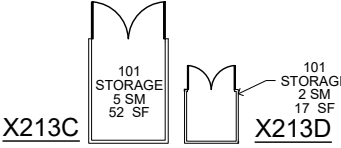

DOOR

SLIDING DOOR

ACCORDION PARTITION

STACK OR FOLDING PARTITION

WINDOW/GLAZING

HIGH WINDOW

SKYLIGHT

STOOP/STEP UP

STAIR

RAMP

ACCESS LADDER

COLD STORAGE

AREA CALCULATED @ 50 %

SLOPING ROOF

DRINKING FOUNTAIN

LAVATORY

SINK

TOILET

URINAL

LOCKER

LAN DISTRIBUTION FRAME

VENT HOOD

WALL SHELVING

UPPER CABINET

BASE CABINET

TEACHER CABINET

MATCHLINE

FLAT ROOF

TITLEBLOCK LEGEND

SHEET NAME:

BLDG # FLOOR # (# IN SERIES)

KEY PLAN

NTS

Updated By: AA

FUS Review: MRS

100% Submittal Date: 01 MAY 2020

0 2 4 8 16 FT

dodea

DEPARTMENT OF DEFENSE EDUCATION ACTIVITY

FACILITY UTILIZATION SURVEY

SIGONELLA ELEMENTARY SCHOOL

BUILDING NUMBER: 213, X213A, X213B, X213C, X213D

COUNTRY: ITALY

INSTALLATION: NAS SIGONELLA

SITE: NAS1 SUPPORT AREA

REGION-DISTRICT: DODEA EUROPE SOUTH


DoDAAC Number: HE5555

Floor: LEVEL 1

Survey Date: JANUARY 2020

Sheet Name: 213_1 (1)

Sheet Seq: 7 of 13

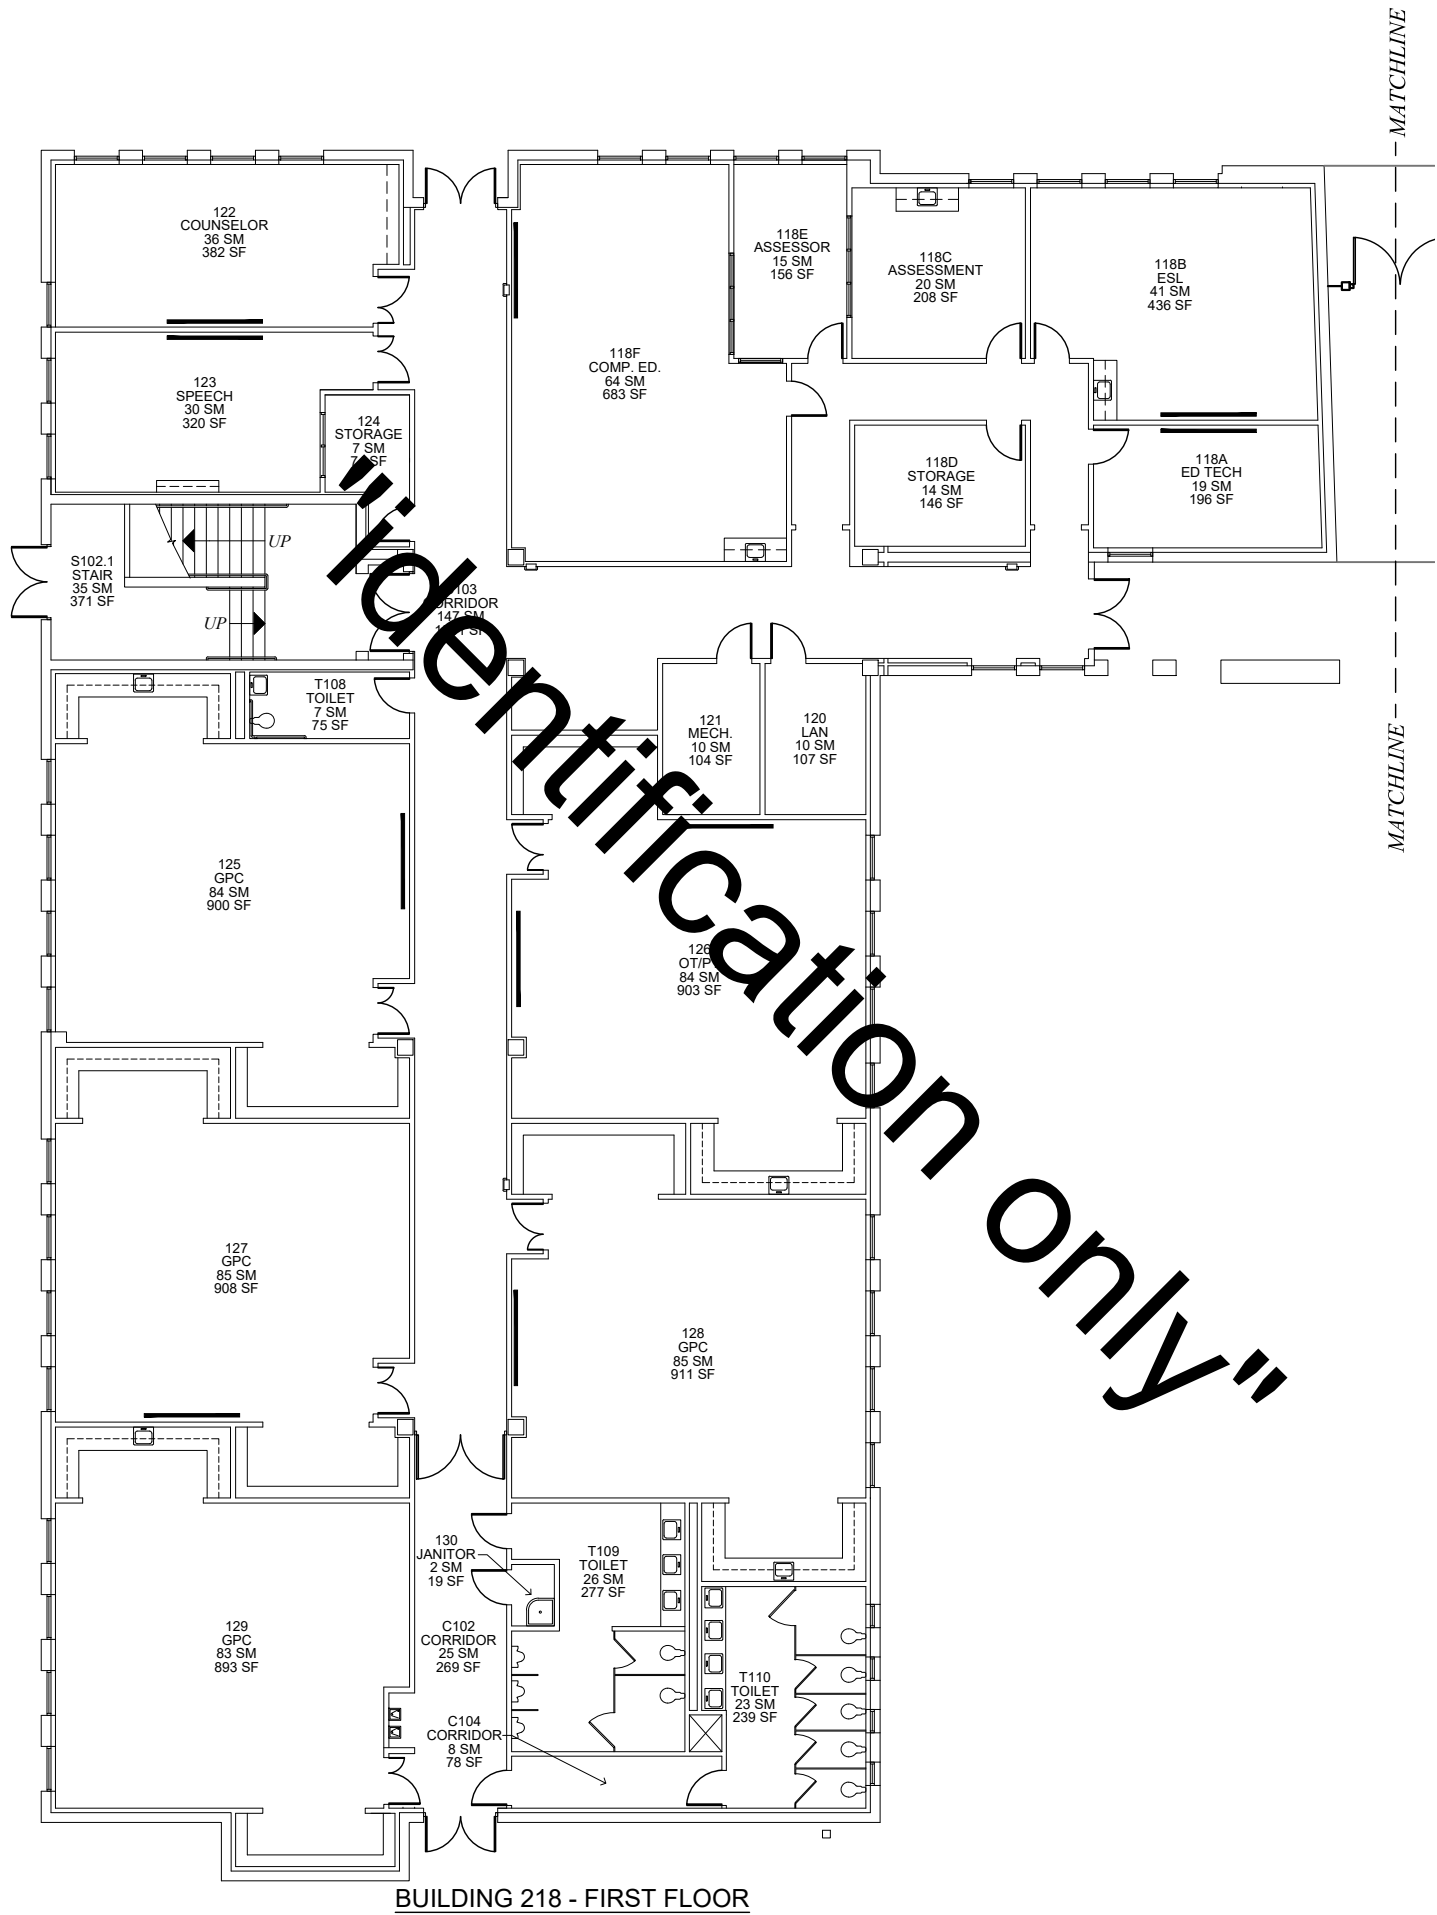

BUILDING 218 - FIRST FLOOR

SYMBOL LEGEND

DOOR	DRINKING FOUNTAIN
SLIDING DOOR	LAVATORY
ACCORDION PARTITION	SINK
STACK OR FOLDING PARTITION	TOILET
WINDOW/GLAZING	URINAL
HIGH WINDOW	LOCKER
SKYLIGHT	LAN DISTRIBUTION FRAME
STOOP/STEP UP	VENT HOOD
STAIR	WALL SHELVING
RAMP	UPPER CABINET
ACCESS LADDER	BASE CABINET
COLD STORAGE	TEACHER CABINET
AREA CALCULATED @ 50 %	MATCHLINE
SLOPING ROOF	FLAT ROOF

TITLEBLOCK LEGEND

SHEET NAME:	BLDG #_FLOOR # (# IN SERIES)

KEY PLAN

NTS

Updated By: AA

FUS Review: MRS

100% Submittal Date: 01 MAY 2020

dodea

DEPARTMENT OF DEFENSE EDUCATION ACTIVITY

FACILITY UTILIZATION SURVEY

SIGONELLA ELEMENTARY SCHOOL

BUILDING NUMBER: 218


COUNTRY: ITALY

INSTALLATION: NAS SIGONELLA

SITE: NAS1 SUPPORT AREA

REGION-DISTRICT: DODEA EUROPE SOUTH

DoDAAC Number: HE5555	Floor: LEVEL 1	Survey Date: JANUARY 2020
Sheet Name: 218_1 (1)	Sheet Seq: 8 of 13	

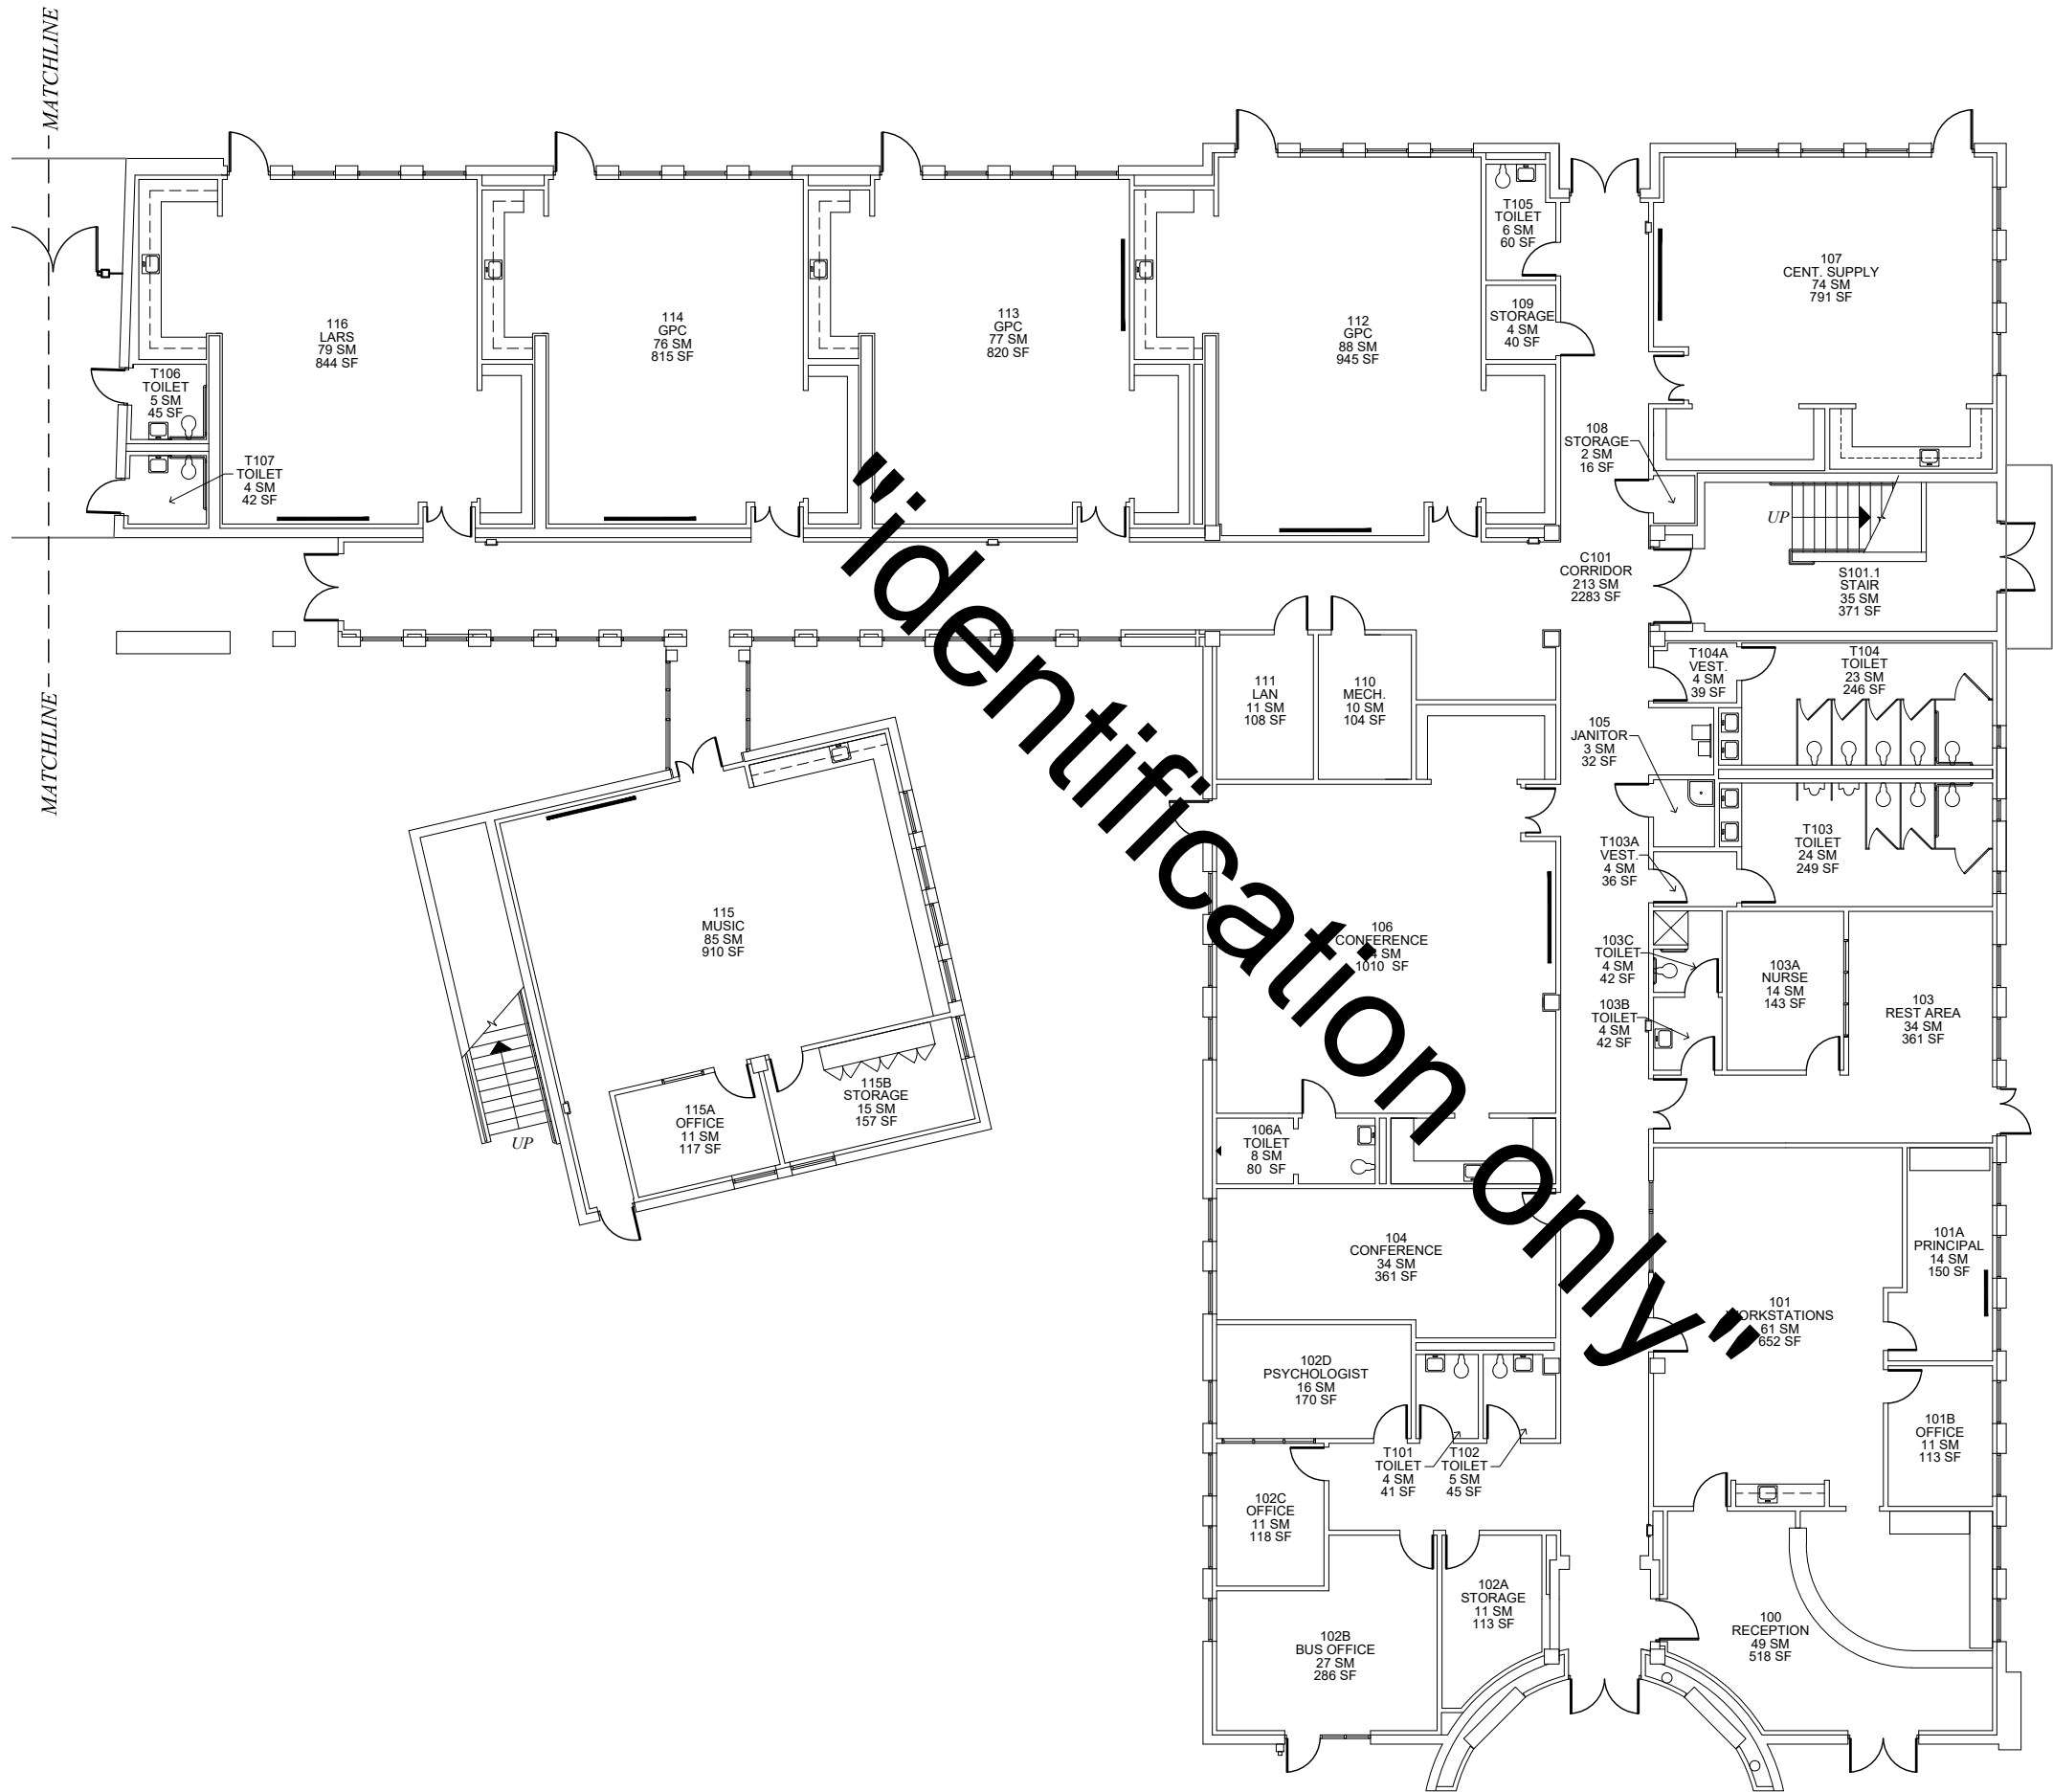

DOOR

SLIDING DOOR

ACCORDION PARTITION

STACK OR FOLDING PARTITION

WINDOW/GLAZING

HIGH WINDOW

SKYLIGHT

STOOP/STEP UP

STAIR

RAMP

ACCESS LADDER

COLD STORAGE

AREA CALCULATED @ 50 %

SLOPING ROOF

DRINKING FOUNTAIN

LAVATORY

SINK

TOILET

URINAL

LOCKER

LAN DISTRIBUTION FRAME

VENT HOOD

WALL SHELVING

UPPER CABINET

BASE CABINET

TEACHER CABINET

MATCHLINE

FLAT ROOF

TITLEBLOCK LEGEND

SHEET NAME:

BLDG #_FLOOR # (# IN SERIES)

KEY PLAN

NTS

218

X213B

X213A

213

X213C

X213D

NORTH

Updated By: AA

FUS Review: MRS

100% Submittal Date: 01 MAY 2020

0

2

4

8

16 FT

dodea

DEPARTMENT OF DEFENSE EDUCATION ACTIVITY

FACILITY UTILIZATION SURVEY

SIGONELLA

ELEMENTARY SCHOOL

BUILDING NUMBER: 218

COUNTRY: ITALY

INSTALLATION: NAS SIGONELLA

SITE: NAS1 SUPPORT AREA

REGION-DISTRICT: DODEA EUROPE SOUTH


DoDAAC Number: HE5555

Floor: LEVEL 1

Survey Date: JANUARY 2020

Sheet Name: 218_1 (2)

Sheet Seq: 9 of 13

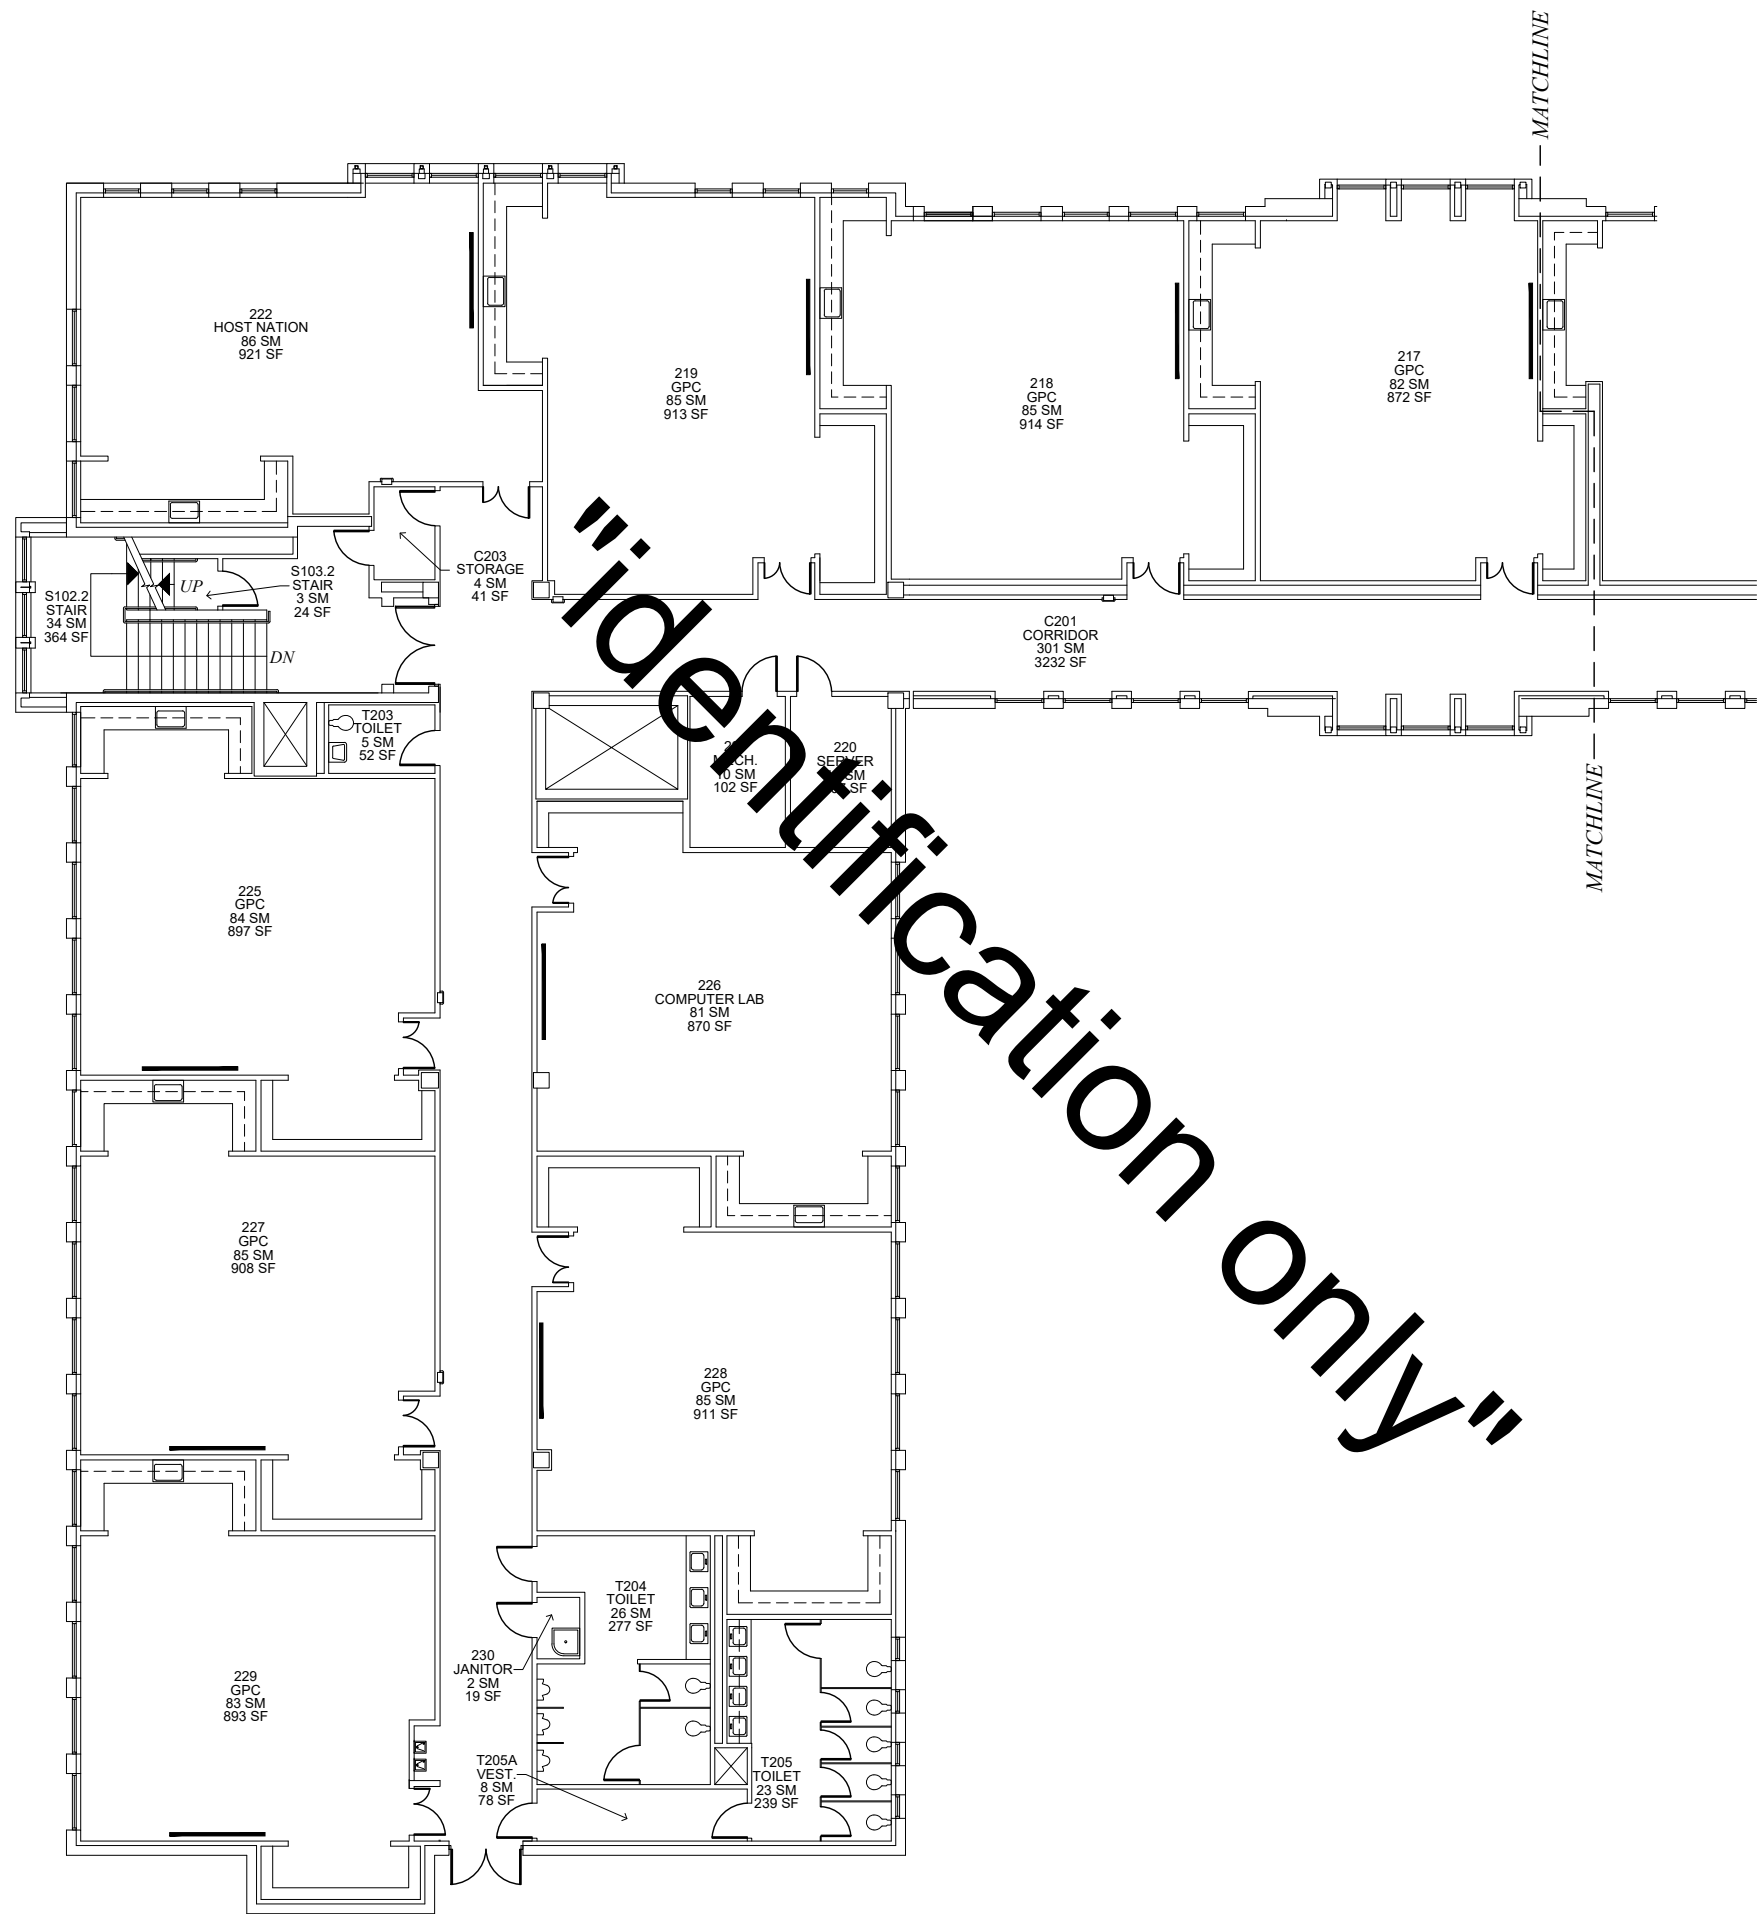

SYMBOL LEGEND

DOOR	DRINKING FOUNTAIN
SLIDING DOOR	LAVATORY
ACCORDION PARTITION	SINK
STACK OR FOLDING PARTITION	TOILET
WINDOW/GLAZING	URINAL
HIGH WINDOW	LOCKER
SKYLIGHT	LAN DISTRIBUTION FRAME
STOOP/STEP UP	VENT HOOD
STAIR	WALL SHELVING
RAMP	UPPER CABINET
ACCESS LADDER	BASE CABINET
COLD STORAGE	TEACHER CABINET
AREA CALCULATED @ 50 %	MATCHLINE
SLOPING ROOF	FLAT ROOF

TITLEBLOCK LEGEND

SHEET NAME:	BLDG #_FLOOR # (# IN SERIES)

KEY PLAN

NTS

Updated By: AA

FUS Review: MRS

100% Submittal Date: 01 MAY 2020

dodea

DEPARTMENT OF DEFENSE EDUCATION ACTIVITY

FACILITY UTILIZATION SURVEY

SIGONELLA ELEMENTARY SCHOOL

BUILDING NUMBER: 218


COUNTRY: ITALY

INSTALLATION: NAS SIGONELLA

SITE: NAS1 SUPPORT AREA


REGION-DISTRICT: DODEA EUROPE SOUTH

DoDAAC Number: HE5555	Floor: LEVEL 2	Survey Date: JANUARY 2020
Sheet Name: 218_2 (1)	Sheet Seq:	10 of 13

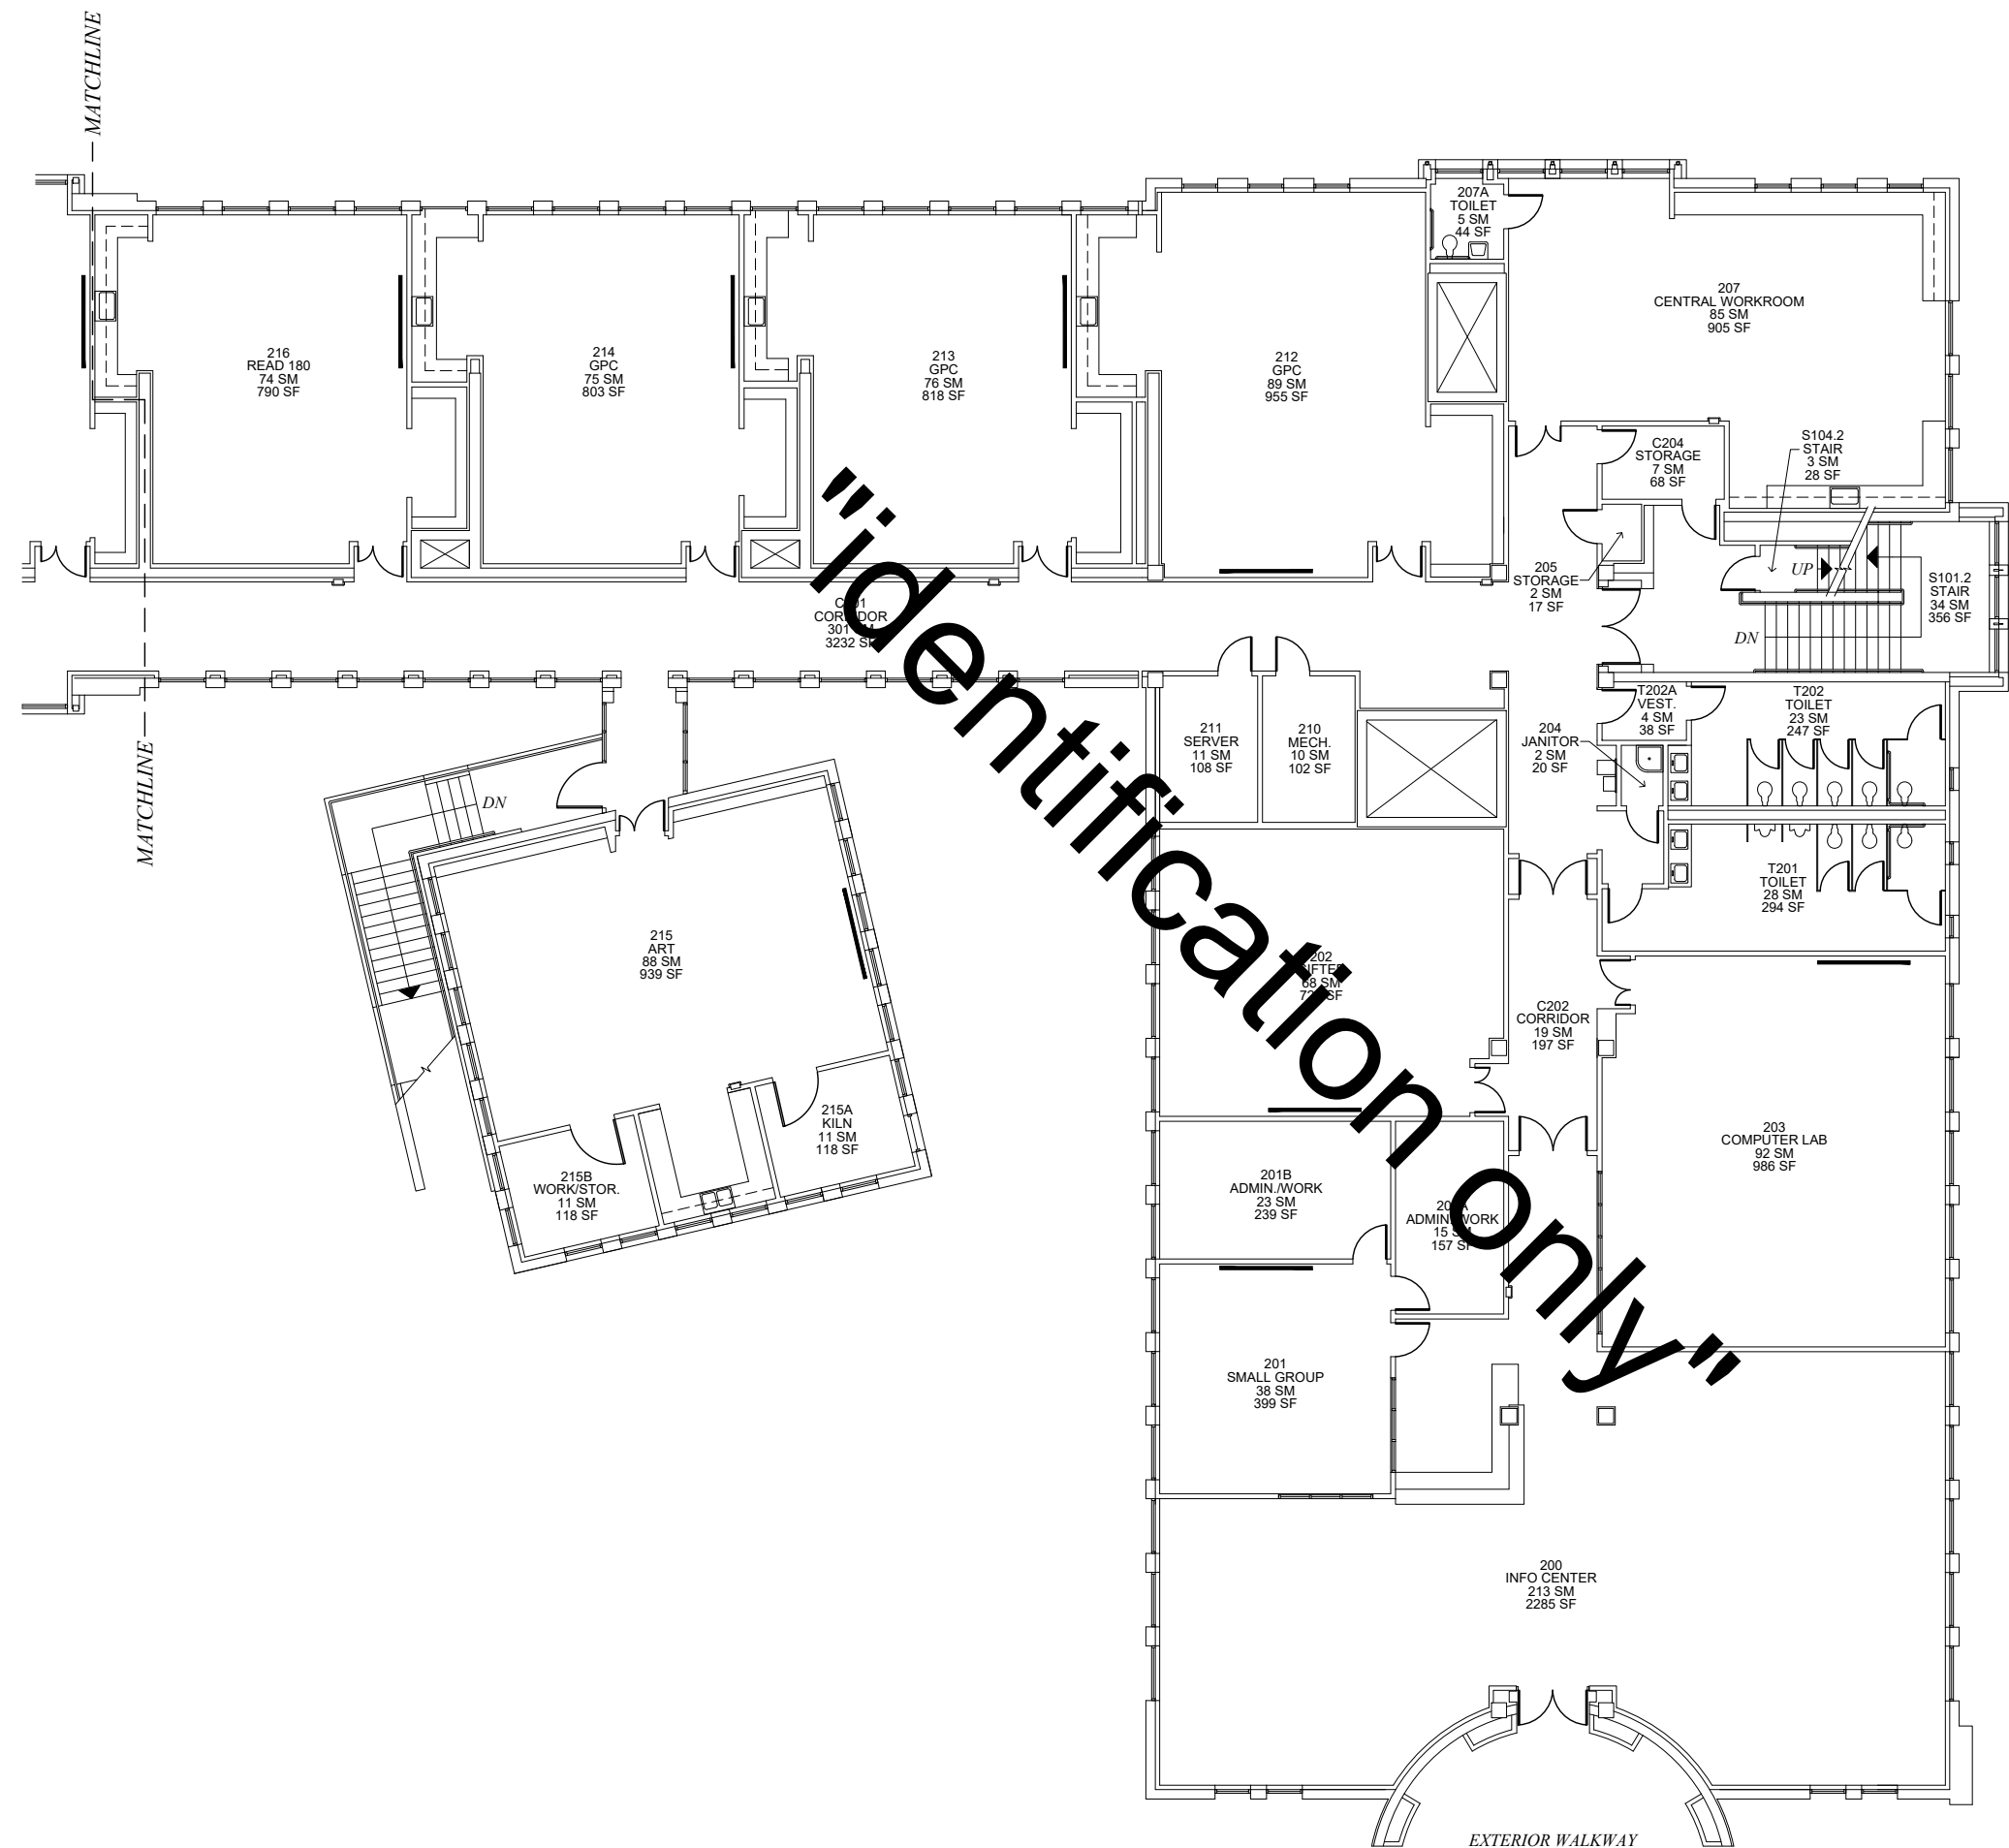

SYMBOL LEGEND	
	DOOR
	DRINKING FOUNTAIN
	SLIDING DOOR
	LAVATORY
	ACCORDION PARTITION
	SINK
	STACK OR FOLDING PARTITION
	TOILET
	WINDOW/GLAZING
	URINAL
	HIGH WINDOW
	LOCKER
	SKYLIGHT
	LAN DISTRIBUTION FRAME
	STOOP/STEP UP
	VENT HOOD
	STAIR
	WALL SHELVING
	RAMP
	UPPER CABINET
	ACCESS LADDER
	BASE CABINET
	COLD STORAGE
	TEACHER CABINET
	AREA CALCULATED @ 50 %
	MATCHLINE
	SLOPING ROOF
	FLAT ROOF

TITLEBLOCK LEGEND	
SHEET NAME:	BLDG # FLOOR # (# IN SERIES)

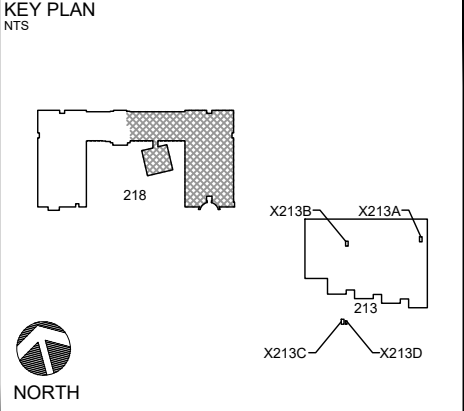


Updated By:	FUS Review:	100% Submittal Date:
AA	MRS	01 MAY 2020

0 2 4 8 16 FT

dodea
DEPARTMENT OF DEFENSE EDUCATION ACTIVITY
FACILITY UTILIZATION SURVEY

**SIGONELLA
ELEMENTARY SCHOOL**
BUILDING NUMBER: 218
COUNTRY: ITALY
INSTALLATION: NAS SIGONELLA
SITE: NAS1 SUPPORT AREA
REGION-DISTRICT: DODEA EUROPE SOUTH

DoDAAC Number:	Floor:	Survey Date:
HE5555	LEVEL 2	JANUARY 2020
Sheet Name:	Sheet Seq:	
218_2 (2)		11 of 13

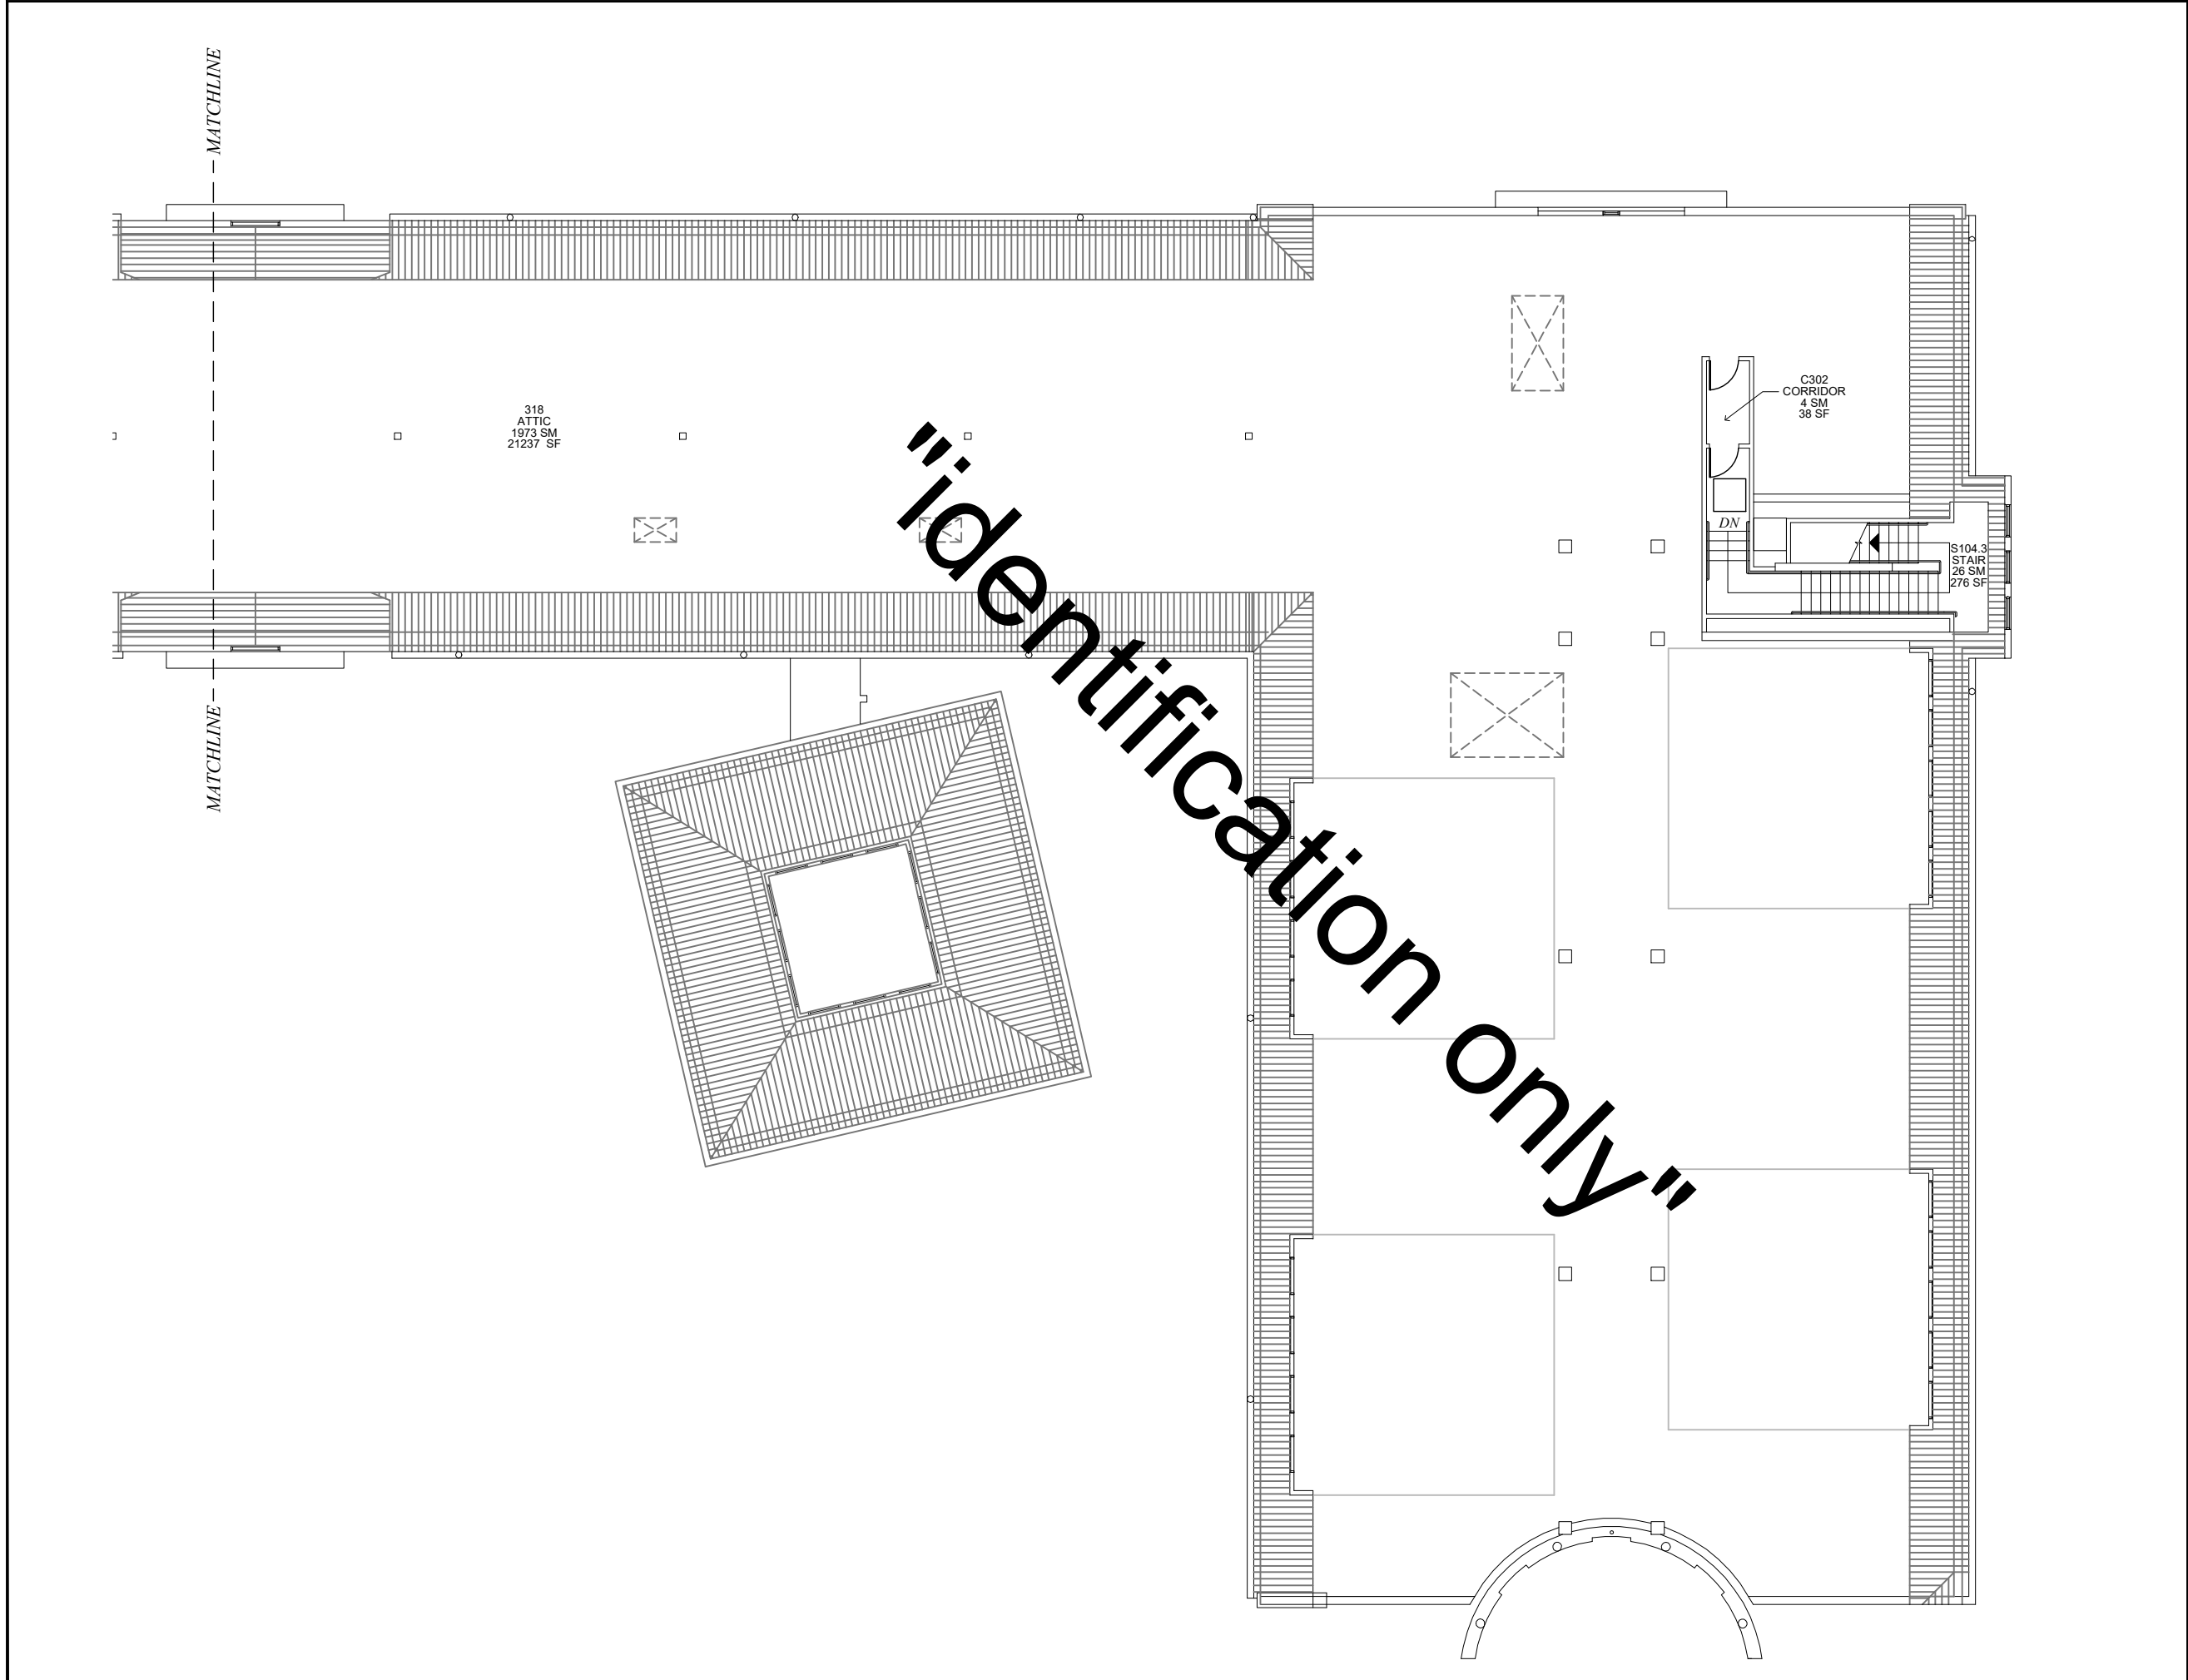

DOOR

SLIDING DOOR

ACCORDION PARTITION

STACK OR FOLDING PARTITION

WINDOW/GLAZING

HIGH WINDOW

SKYLIGHT

STOOP/STEP UP

STAIR

RAMP

ACCESS LADDER

COLD STORAGE

AREA CALCULATED @ 50 %

SLOPING ROOF

DRINKING FOUNTAIN

LAVATORY

SINK

TOILET

URINAL

LOCKER

LAN DISTRIBUTION FRAME

VENT HOOD

WALL SHELVING

UPPER CABINET

BASE CABINET

TEACHER CABINET

MATCHLINE

FLAT ROOF

TITLEBLOCK LEGEND

SHEET NAME:

BLDG #_FLOOR # (# IN SERIES)

KEY PLAN

NTS

218

X213B

X213A

213

X213C

X213D

NORTH

Updated By: AA

FUS Review: MRS

100% Submittal Date: 01 MAY 2020

0

2

4

8

16 FT

dodea

DEPARTMENT OF DEFENSE EDUCATION ACTIVITY

FACILITY UTILIZATION SURVEY

SIGONELLA

ELEMENTARY SCHOOL

BUILDING NUMBER: 218

COUNTRY: ITALY

INSTALLATION: NAS SIGONELLA

SITE: NAS1 SUPPORT AREA

REGION-DISTRICT: DODEA EUROPE SOUTH

DoDAAC Number: HE5555

Floor: LEVEL 3

Survey Date: JANUARY 2020

Sheet Name: 218_3 (2)

Sheet Seq: 13 of 13