


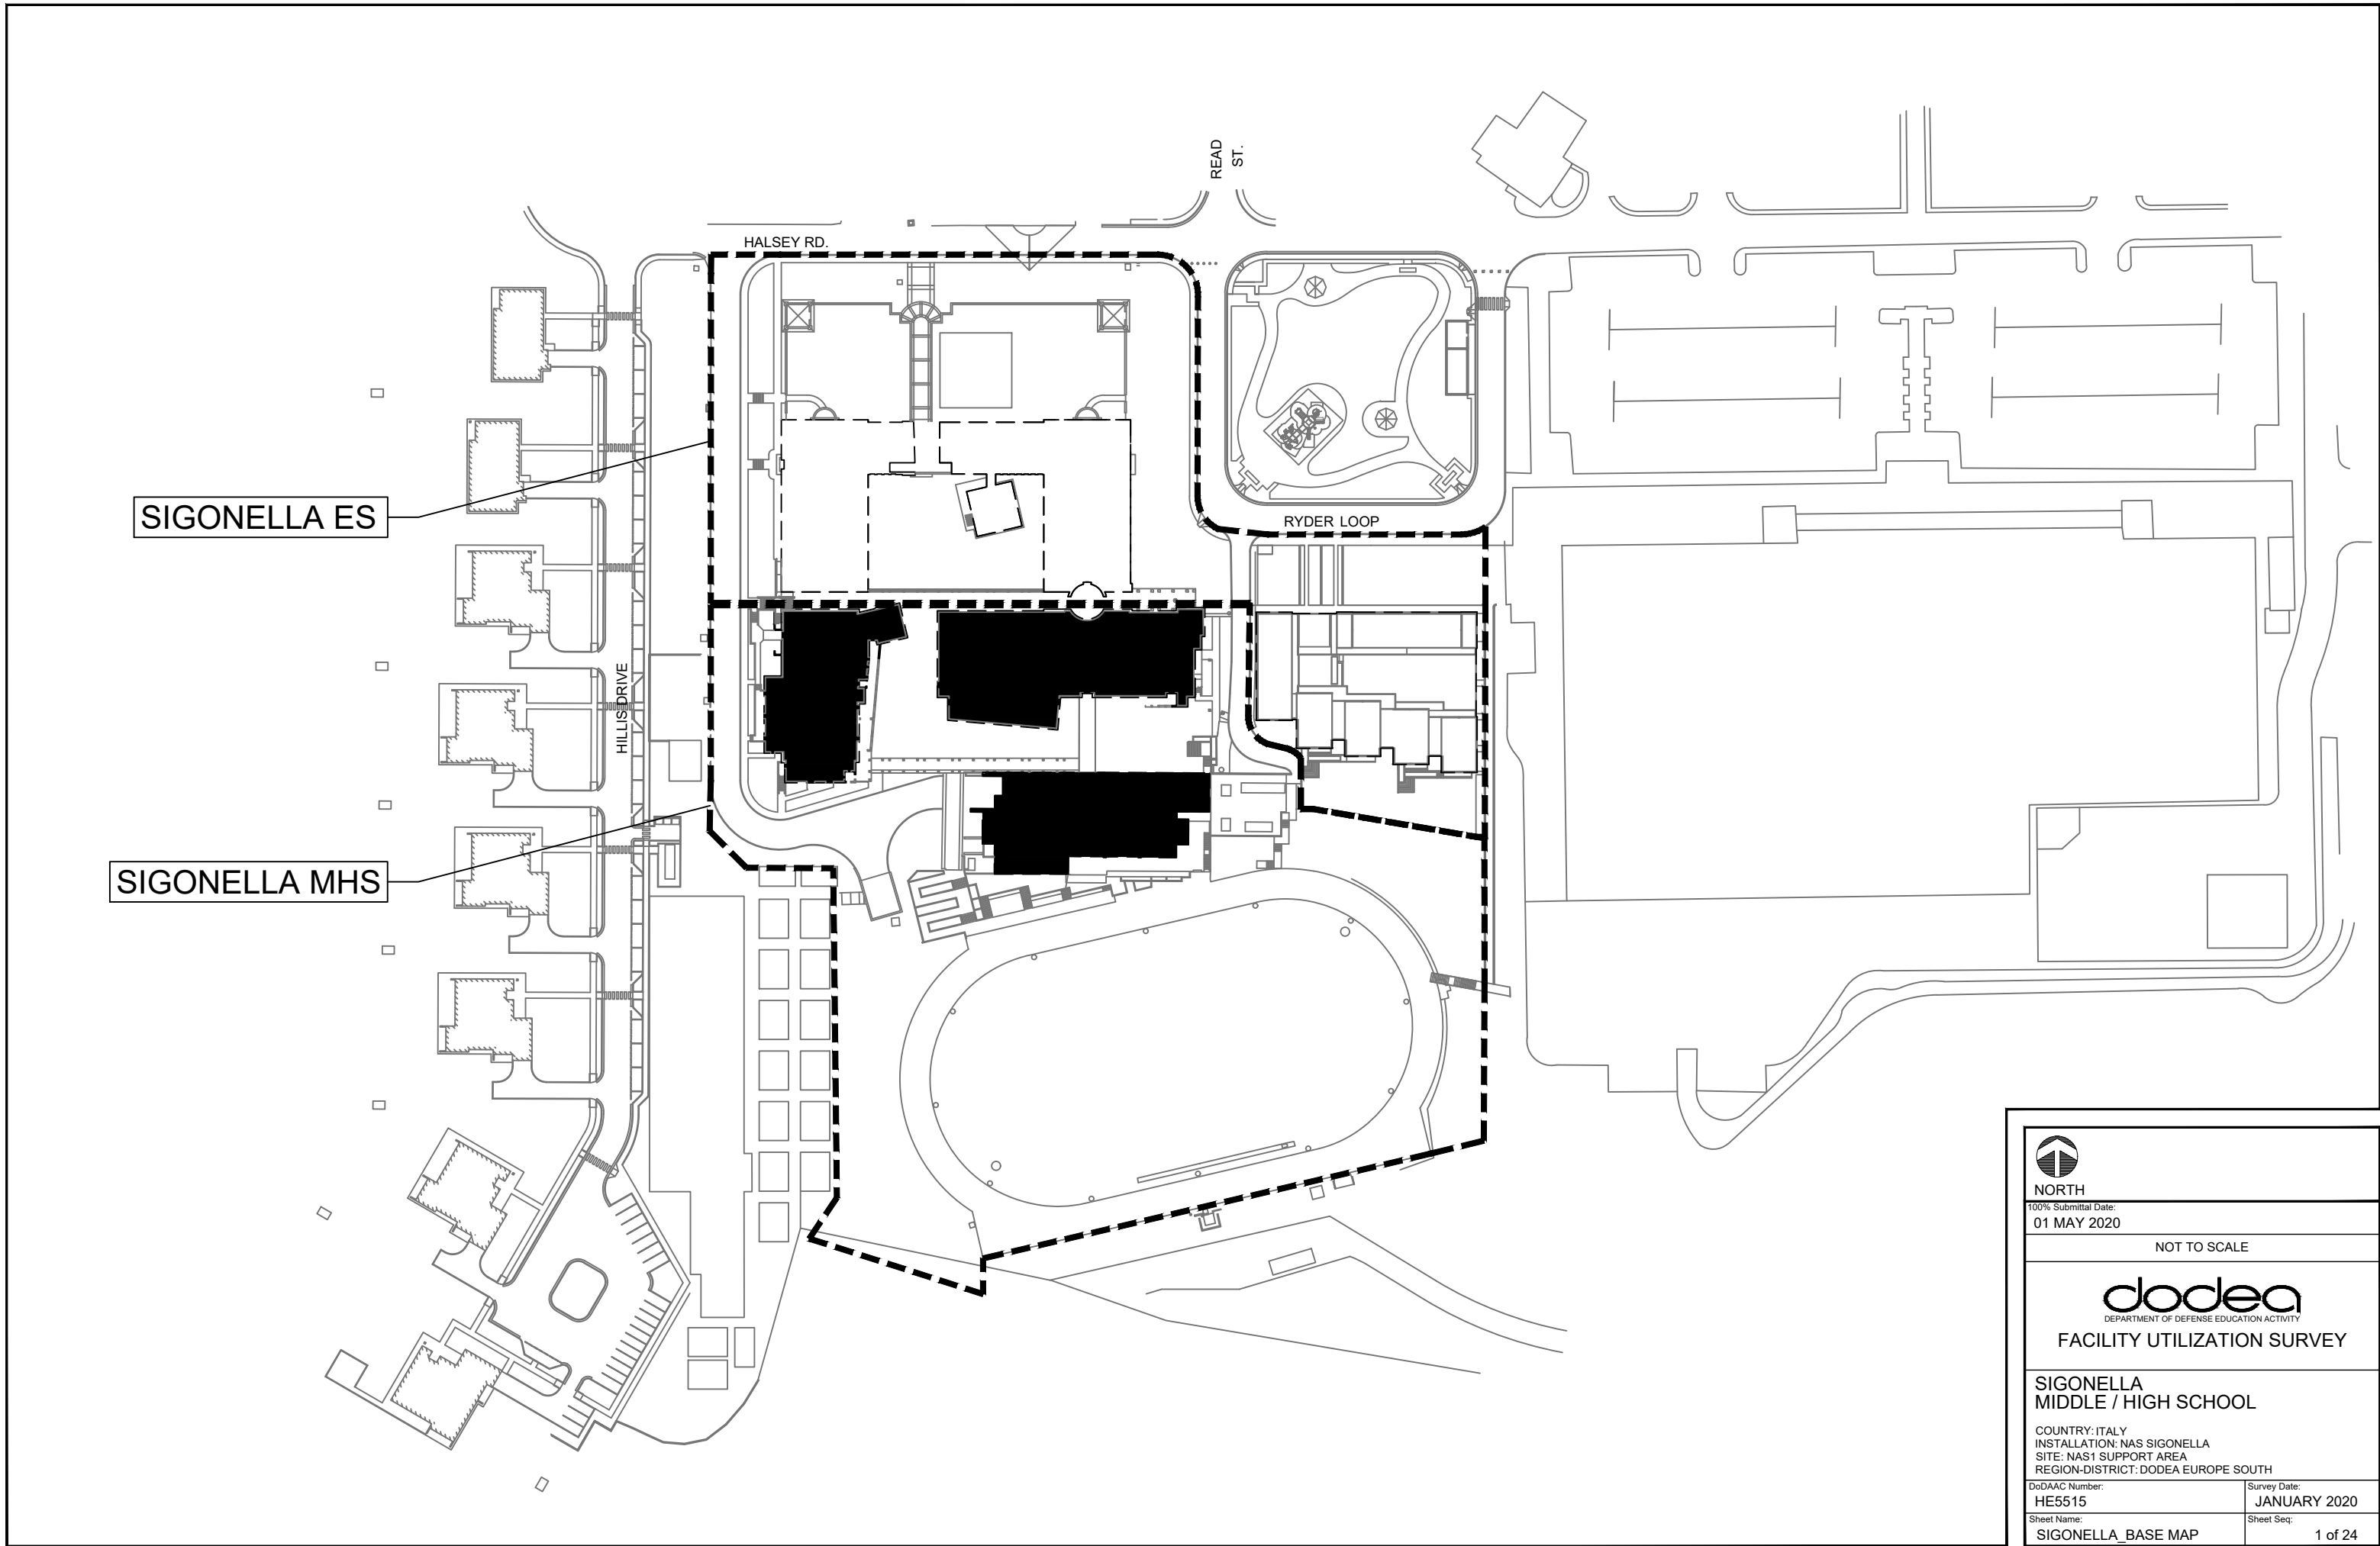


NORTH

100% Submittal Date:
01 MAY 2020





NOT TO SCALE


DEPARTMENT OF DEFENSE EDUCATION ACTIVITY
FACILITY UTILIZATION SURVEY

SIGONELLA
MIDDLE / HIGH SCHOOL

COUNTRY: ITALY
INSTALLATION: NAS SIGONELLA
SITE: NAS1 SUPPORT AREA
REGION-DISTRICT: DODEA EUROPE SOUTH

DoDAAC Number: HE5515	Survey Date: JANUARY 2020
Sheet Name: SIGONELLA_BASE MAP	Sheet Seq: 1 of 24

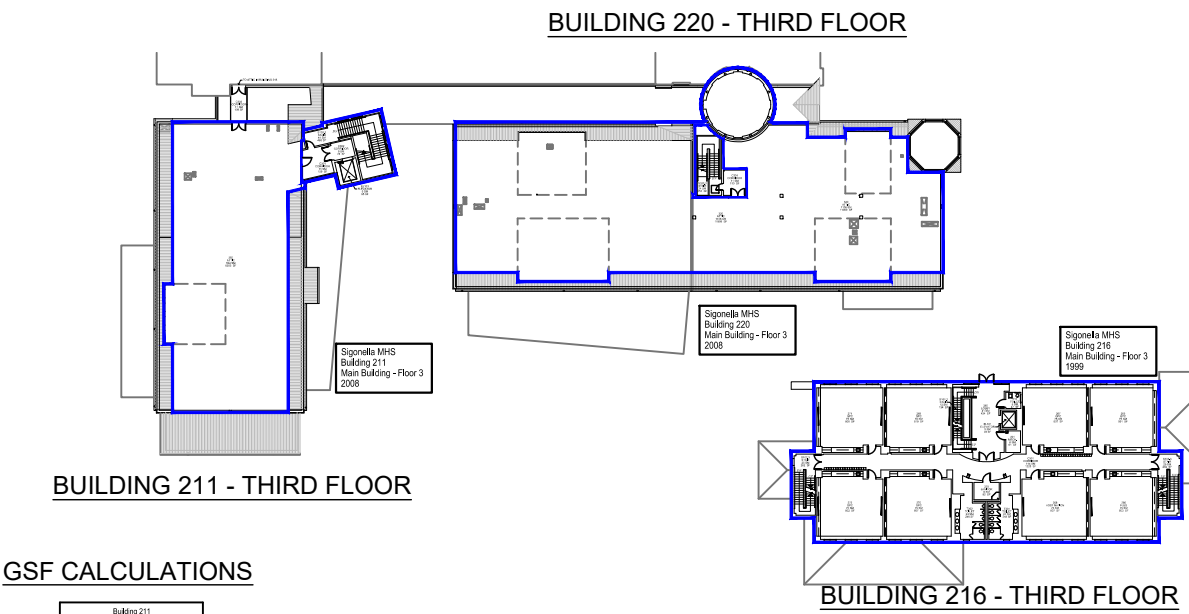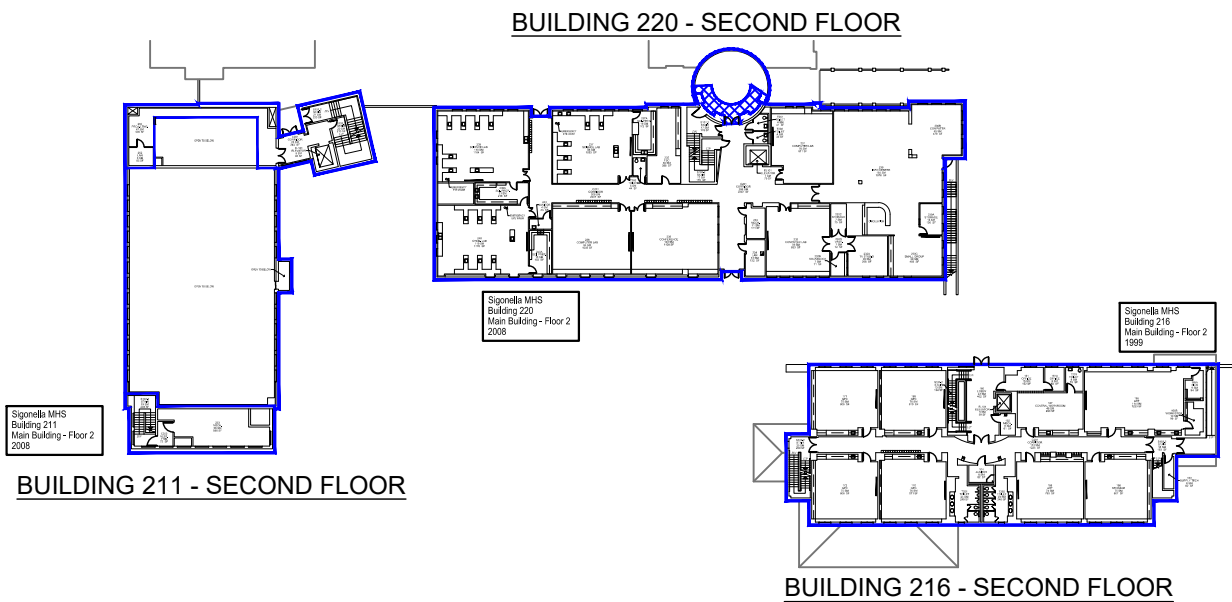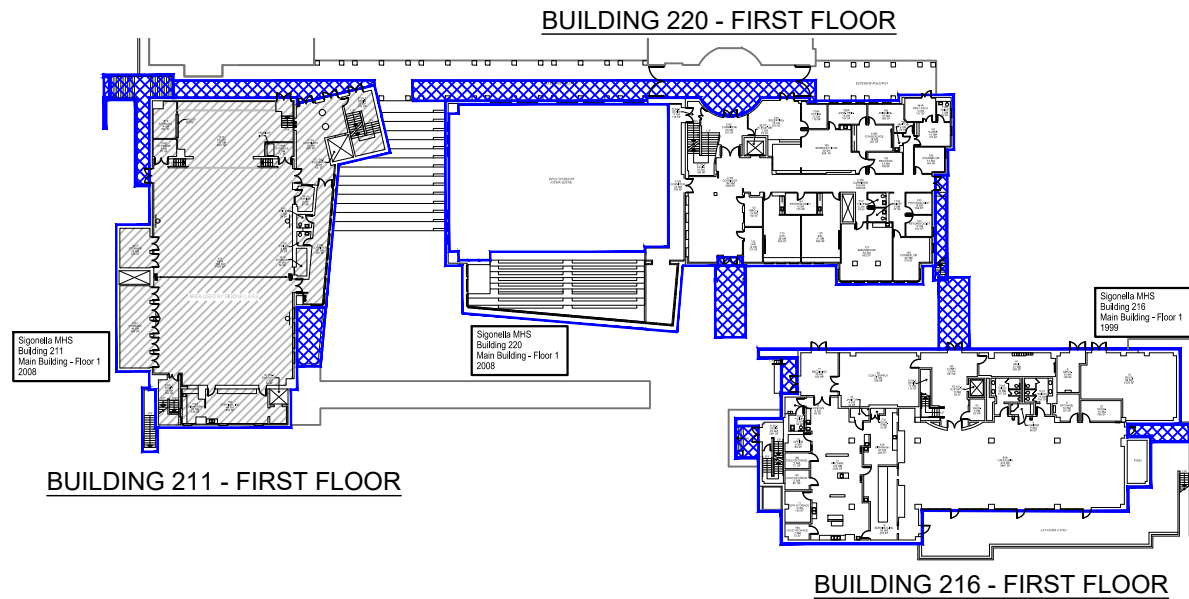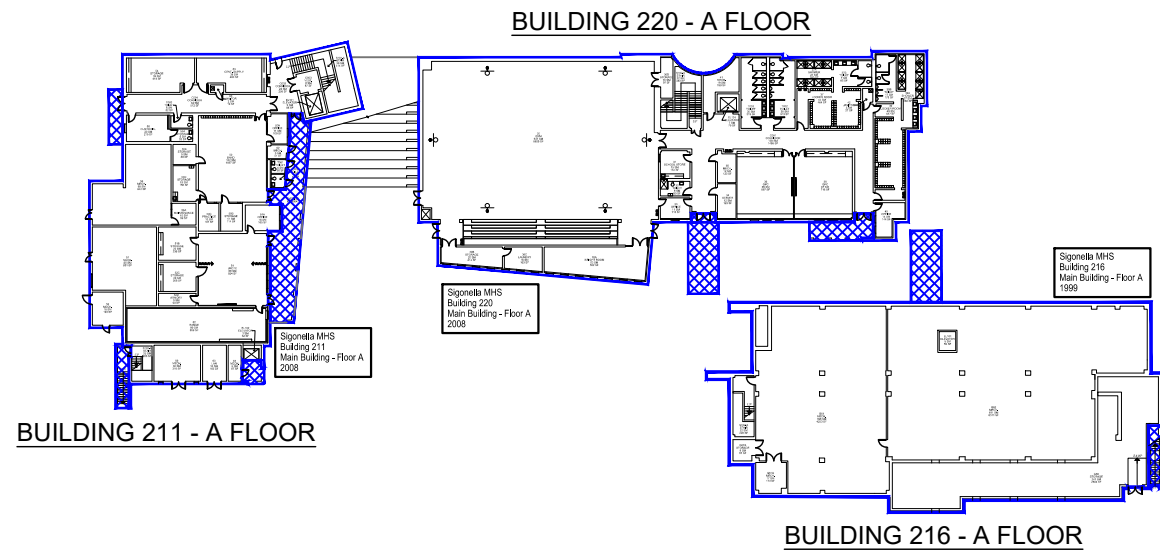


GSF CALCULATIONS

Building 211	
Basement	11,175
Floor 1	11,962
Floor 2	3,232
Floor 3	1,019
Total Area (SF)	27,388
50% Area (SF)	1,362
Gross Area (SF)	28,750

Building 216	
Basement	15,328
Floor 1	12,811
Floor 2	11,933
Floor 3	10,924
Floor 4	10,924
Total Area (SF)	61,920
50% Area (SF)	893
Gross Area (SF)	62,813

Building 220	
Basement	17,449
Floor 1	11,878
Floor 2	16,660
Floor 3	484
Total Area (SF)	45,471
50% Area (SF)	1,591
Gross Area (SF)	46,062

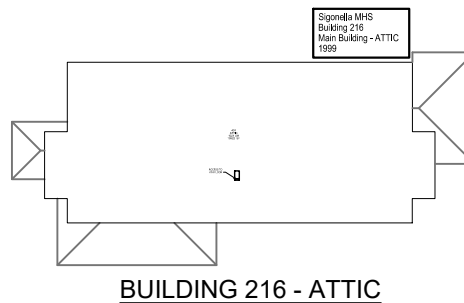

NOTE 1: APPROXIMATELY 22% OF BUILDING 211 IS OCCUPIED BY SIGONELLA ES.

NOTE 2: GSF CALCULATIONS BASED ON ARMY RPI DoA PAMPHLET 415-28.

DOOR

SLIDING DOOR

ACCORDION PARTITION

STACK OR FOLDING PARTITION

WINDOW/GLAZING

HIGH WINDOW

SKYLIGHT

STOOP/STEP UP

STAIR

RAMP

ACCESS LADDER

COLD STORAGE

AREA CALCULATED @ 50 %

SLOPING ROOF

DRINKING FOUNTAIN

LAVATORY

SINK

TOILET

URINAL

LOCKER

LAN DISTRIBUTION FRAME

VENT HOOD

WALL SHELVING

UPPER CABINET

BASE CABINET

TEACHER CABINET

MATCHLINE

FLAT ROOF

TITLEBLOCK LEGEND

SHEET NAME:

BLDG #_FLOOR # (# IN SERIES)

KEY PLAN

NTS

211

220

216

NORTH

Updated By: AA

FUS Review: MRS

100% Submittal Date: 01 MAY 2020

NOT TO SCALE

dodea

DEPARTMENT OF DEFENSE EDUCATION ACTIVITY

FACILITY UTILIZATION SURVEY

SIGONELLA MIDDLE / HIGH SCHOOL

BUILDING NUMBER: 211, 216, 220

COUNTRY: ITALY

INSTALLATION: NAS SIGONELLA

SITE: NAS1 SUPPORT AREA

REGION-DISTRICT: DODEA EUROPE SOUTH

DoDAAC Number: HE5515


Floor: LEVEL A-5

Survey Date: JANUARY 2020

Sheet Name: GSF_1 (1)

Sheet Seq: 4 of 24

211						216						220					
Floor	Room	Current	Capacity	Area (SF)	Area (SM)	Floor	Room	Current	Capacity	Area (SF)	Area (SM)	Floor	Room	Current	Capacity	Area (SF)	Area (SM)
1	151	MPR	OTHER	5,795 SF	530 SM	2	165A	KLN	OTHER	94 SF	9 SM	2	235	TSC	OTHER	386 SF	36 SM
1	151A	OFFICE	OTHER	81 SF	8 SM	2	165B	WORKSTOR.	OTHER	99 SF	10 SM	2	236	CONFERENCE	OTHER	1,198 SF	103 SM
1	151B	STORAGE	OTHER	73 SF	7 SM	2	166	STORAGE	OTHER	807 SF	75 SM	2	237	SCIENCE LAB	STUDENT - FULL	1,053 SF	98 SM
1	151C	STAGE	OTHER	1,297 SF	117 SM	2	167	CENTRAL WORKROOM	OTHER	463 SF	46 SM	2	237A	SCL PREP.	OTHER	172 SF	16 SM
1	151D	STORAGE	OTHER	79 SF	8 SM	2	168	ART	STUDENT - FULL	769 SF	74 SM	2	238	COMPUTER LAB	STUDENT - FULL	1,184 SF	94 SM
1	151E	STORAGE	OTHER	232 SF	22 SM	2	169	GPC	STUDENT - FULL	819 SF	76 SM	2	239	SCIENCE LAB	STUDENT - FULL	1,184 SF	110 SM
1	151F	STORAGE	OTHER	150 SF	14 SM	2	170	GPC	STUDENT - FULL	811 SF	76 SM	2	239A	SCL PREP.	OTHER	216 SF	21 SM
1	151G	STORAGE	OTHER	486 SF	46 SM	2	171	GPC	STUDENT - FULL	806 SF	75 SM	2	240	CHEM LAB	STUDENT - FULL	1,176 SF	110 SM
1	151H	STORAGE	OTHER	56 SF	6 SM	2	172	GPC	STUDENT - FULL	806 SF	75 SM	2	240A	SCL PREP.	OTHER	183 SF	18 SM
1	152	SERVING LINE	OTHER	463 SF	44 SM	2	S101.2	STAIR	NET - VERTICAL	134 SF	13 SM	2	243	JANITOR	NET - GENERAL	43 SF	4 SM
1	152A	DISHWASH	OTHER	130 SF	13 SM	2	S102.2	STAIR	NET - VERTICAL	260 SF	25 SM	2	C201	CORRIDOR	NET - GENERAL	2,207 SF	206 SM
1	C101	CORRIDOR	NET - GENERAL	630 SF	59 SM	2	S103.2	STAIR	NET - VERTICAL	193 SF	18 SM	2	S101.2	STAIR	NET - VERTICAL	178 SF	17 SM
1	C102	CORRIDOR	NET - GENERAL	387 SF	36 SM	2	T201	TOILET	NET - GENERAL	248 SF	24 SM	2	S103.2	STAIR	NET - VERTICAL	179 SF	17 SM
1	EL101.1	ELEVATOR	NET - VERTICAL	95 SF	9 SM	2	T202	TOILET	NET - GENERAL	248 SF	24 SM	2	T201	TOILET	NET - GENERAL	41 SF	4 SM
1	EL102.1	ELEVATOR	NET - VERTICAL	52 SF	5 SM	2	T203	TOILET	NET - GENERAL	79 SF	8 SM	2	T202	TOILET	NET - GENERAL	33 SF	4 SM
1	S101.1	STAIR	NET - VERTICAL	348 SF	33 SM	3	201	MECH.	NET - MECH	61 SF	6 SM	2	T203	TOILET	NET - GENERAL	44 SF	5 SM
1	S102.1	STAIR	NET - VERTICAL	184 SF	18 SM	3	203	JANITOR	NET - GENERAL	82 SF	8 SM	3	C301	CORRIDOR	NET - GENERAL	110 SF	11 SM
1	T101	TOILET	NET - GENERAL	39 SF	4 SM	3	210	TOILET	NET - GENERAL	47 SF	5 SM	3	S103.3	STAIR	NET - VERTICAL	251 SF	24 SM
1	T102	TOILET	NET - GENERAL	37 SF	4 SM	3	260	LOBBY	NET - GENERAL	434 SF	41 SM	G	30	GYM	STUDENT - FULL	8,855 SF	637 SM
2	250	PROLUNTING.	OTHER	505 SF	47 SM	3	265	GPC	STUDENT - FULL	801 SF	75 SM	G	30A	WEIGHT ROOM	STUDENT - HALF	562 SF	53 SM
2	253	MECH.	NET - MECH	586 SF	56 SM	3	266	FILES	STUDENT - FULL	603 SF	75 SM	G	30B	STORAGE	STUDENT - HALF	214 SF	20 SM
2	C201	CORRIDOR	NET - GENERAL	244 SF	23 SM	3	267	GPC	STUDENT - FULL	807 SF	75 SM	G	30C	LAUNDRY	OTHER	163 SF	16 SM
2	C202	VEST.	NET - GENERAL	72 SF	7 SM	3	268	HOST NATION	STUDENT - FULL	807 SF	75 SM	G	30D	STORAGE	STUDENT - HALF	97 SF	10 SM
2	S101.2	STAIR	NET - VERTICAL	229 SF	21 SM	3	269	GPC	STUDENT - FULL	610 SF	76 SM	G	31	SCHOOL STORE	OTHER	154 SF	15 SM
2	S102.2	STAIR	NET - VERTICAL	254 SF	19 SM	3	270	GPC	STUDENT - FULL	807 SF	75 SM	G	32	TOILET	NET - GENERAL	83 SF	8 SM
2	S103.2	STAIR	NET - VERTICAL	219 SF	20 SM	3	271	GPC	STUDENT - FULL	806 SF	75 SM	G	33	OFFICE	OTHER	118 SF	11 SM
3	C301	CORRIDOR	NET - GENERAL	159 SF	15 SM	3	272	GPC	STUDENT - FULL	802 SF	75 SM	G	34	SERVER	NET - MECH	123 SF	12 SM
3	C302	CORRIDOR	NET - GENERAL	78 SF	8 SM	3	C301	CORRIDOR	NET - GENERAL	1,225 SF	114 SM	G	35	MECH.	NET - MECH	123 SF	12 SM
3	C303	CORRIDOR	NET - GENERAL	109 SF	11 SM	3	S101.3	STAIR	NET - VERTICAL	134 SF	13 SM	G	36	GPC	STUDENT - FULL	697 SF	68 SM
3	S103.3	STAIR	NET - VERTICAL	469 SF	44 SM	3	S102.3	STAIR	NET - VERTICAL	262 SF	25 SM	G	37	LOCKER ROOM	OTHER	464 SF	44 SM
G	50	BAND	STUDENT - FULL	1,897 SF	102 SM	3	S103.3	STAIR	NET - VERTICAL	262 SF	25 SM	G	37A	SHOWER	OTHER	280 SF	27 SM
G	50A	OFFICE	OTHER	189 SF	11 SM	3	T301	TOILET	NET - GENERAL	248 SF	24 SM	G	37B	TOILET	OTHER	65 SF	7 SM
G	50B	STORAGE	OTHER	114 SF	11 SM	3	T302	TOILET	NET - GENERAL	246 SF	24 SM	G	38	GPC	STUDENT - FULL	716 SF	67 SM
G	50C	PRACTICE	OTHER	107 SF	10 SM	4	302	MECH.	NET - MECH	61 SF	6 SM	G	39	LOCKER ROOM	OTHER	517 SF	49 SM
G	50D	STORAGE	OTHER	196 SF	15 SM	4	304	JANITOR	NET - GENERAL	82 SF	8 SM	G	39A	SHOWER	OTHER	280 SF	27 SM
G	50E	STORAGE	OTHER	89 SF	9 SM	4	360	LOBBY	NET - GENERAL	442 SF	42 SM	G	39B	TOILET	OTHER	178 SF	17 SM
G	51	JROTC	STUDENT - FULL	664 SF	66 SM	4	361	TOILET	NET - GENERAL	47 SF	5 SM	G	40	OFFICE	OTHER	144 SF	14 SM
G	51A	OFFICE	OTHER	160 SF	16 SM	4	365	STORAGE	OTHER	801 SF	75 SM	G	41	MECH.	NET - MECH	199 SF	19 SM
G	51B	STORAGE	OTHER	236 SF	22 SM	4	366	GPC	STUDENT - FULL	807 SF	75 SM	G	42	JANITOR	NET - GENERAL	27 SF	3 SM
G	52	RANGE	OTHER	869 SF	80 SM	4	367	GPC	STUDENT - FULL	802 SF	75 SM	G	C001	CORRIDOR	NET - GENERAL	1,486 SF	139 SM
G	52C	STORAGE	OTHER	208 SF	20 SM	4	368	GPC	STUDENT - FULL	807 SF	75 SM	G	S102A	STAIR	NET - VERTICAL	340 SF	32 SM
G	52D	ARMORY	OTHER	90 SF	9 SM	4	369	GPC	STUDENT - FULL	805 SF	75 SM	G	T001	TOILET	NET - GENERAL	319 SF	30 SM
G	53	CENT. SUPPLY	OTHER	400 SF	38 SM	4	370	GPC	STUDENT - FULL	812 SF	76 SM	G	T002	TOILET	NET - GENERAL	313 SF	30 SM
G	54	STORAGE	OTHER	414 SF	39 SM	4	371	SCIENCE LAB	STUDENT - FULL	802 SF	75 SM						
G	55	CUSTODIAL	OTHER	215 SF	20 SM	4	372	COMPUTER LAB	STUDENT - FULL	806 SF	75 SM						
G	55A	STORAGE	OTHER	52 SF	5 SM	4	C401	CORRIDOR	NET - GENERAL	1,213 SF	113 SM						
G	56	MECH.	NET - MECH	942 SF	88 SM	4	S101.4	STAIR	NET - VERTICAL	144 SF	14 SM						
G	56A	MAINTENANCE	OTHER	96 SF	10 SM	4	S102.4	STAIR	NET - VERTICAL	261 SF	25 SM						
G	57	MECH.	NET - MECH	861 SF	80 SM	4	S103.4	STAIR	NET - VERTICAL	262 SF	25 SM						
G	58	MECH.	NET - MECH	193 SF	18 SM	4	T401	TOILET	NET - GENERAL	254 SF	24 SM						
G	59	MECH.	NET - MECH	316 SF	30 SM	4	T402	TOILET	NET - GENERAL	254 SF	24 SM						
G	60	LAN	NET - MECH	163 SF	16 SM	A	G60	STORAGE	OTHER	2,684 SF	241 SM						
G	61	MECH.	NET - MECH	67 SF	9 SM	A	G61	MECH.	NET - MECH	4,253 SF	396 SM						
G	62	MECH.	NET - MECH	51 SF	5 SM	A	G61A	MECH.	NET - MECH	173 SF	17 SM						
G	63	JANITOR	NET - GENERAL	19 SF	2 SM	A	G61B	STORAGE	OTHER	81 SF	8 SM						
G	C001	CORRIDOR	NET - GENERAL	572 SF	54 SM	A	G62	MECH.	NET - MECH	6,571 SF	611 SM						
G	C002	CORRIDOR	NET - GENERAL	256 SF	24 SM	A	S102A	STAIR	NET - VERTICAL	228 SF	22 SM						
G	EL102	ELEVATOR	NET - VERTICAL	32 SF	3 SM	220											
G	S101A	STAIR	NET - VERTICAL	414 SF	39 SM	Floor	Room	Current	Capacity	Area (SF)	Area (SM)						
G	S102A	STAIR	NET - VERTICAL	262 SF	25 SM	1	130	RECEPTION	OTHER	379 SF	35 SM						
G	T001	TOILET	NET - GENERAL	39 SF	4 SM	1	130A	OFFICE	OTHER	119 SF	12 SM						
G	T002	TOILET	NET - GENERAL	34 SF	4 SM	1	131	MECH.	NET - MECH	102 SF	10 SM						
G	T003	TOILET	NET - GENERAL	52 SF	5 SM	1	132	LAN	NET - MECH	121 SF	12 SM						
						1	133	GPC	STUDENT - HALF	405 SF	38 SM						
216						220											
Floor	Room	Current	Capacity	Area (SF)	Area (SM)	1	134	PSYCHOLOGIST	OTHER	125 SF	12 SM						
1	5	JANITOR	NET - GENERAL	48 SF	5 SM	1	135	ESL	STUDENT - HALF	434 SF	41 SM						
1	8	STORAGE	OTHER	122 SF	12 SM	1	136	WORKSTATIONS	OTHER	628 SF	59 SM						
1	9	MECH.	NET - MECH	188 SF	18 SM	1	136A	ASST. PRIN.	OTHER	154 SF	15 SM						
1	10	MECH.	NET - MECH	1,029 SF	96 SM	1	136B	CONFERENCE	OTHER	202 SF	19 SM						
1	12	SERVING LINE	OTHER	418 SF	39 SM	1	137	BREAKROOM	OTHER	552 SF	52 SM						
1	12A	DISHWASH	OTHER	289 SF	27 SM	1	138	RECORDS	OTHER	138 SF	13 SM						
1	13	KITCHEN	OTHER	1,380 SF	129 SM	1	139	COUNSELOR	OTHER	144 SF	14 SM						
1	14	DRY STORAGE	OTHER	148 SF	14 SM	1	141	NURSE	OTHER	161 SF	15 SM						
1	14A	COLD STORAGE	OTHER	72 SF	7 SM	1	141A	REST AREA	OTHER	137 SF	13 SM						
1	14B	COLD STORAGE	OTHER	72 SF	7 SM	1	142	PRINCIPAL	OTHER	168 SF	16 SM						
1	14C	COLD STORAGE	OTHER	86 SF	9 SM												

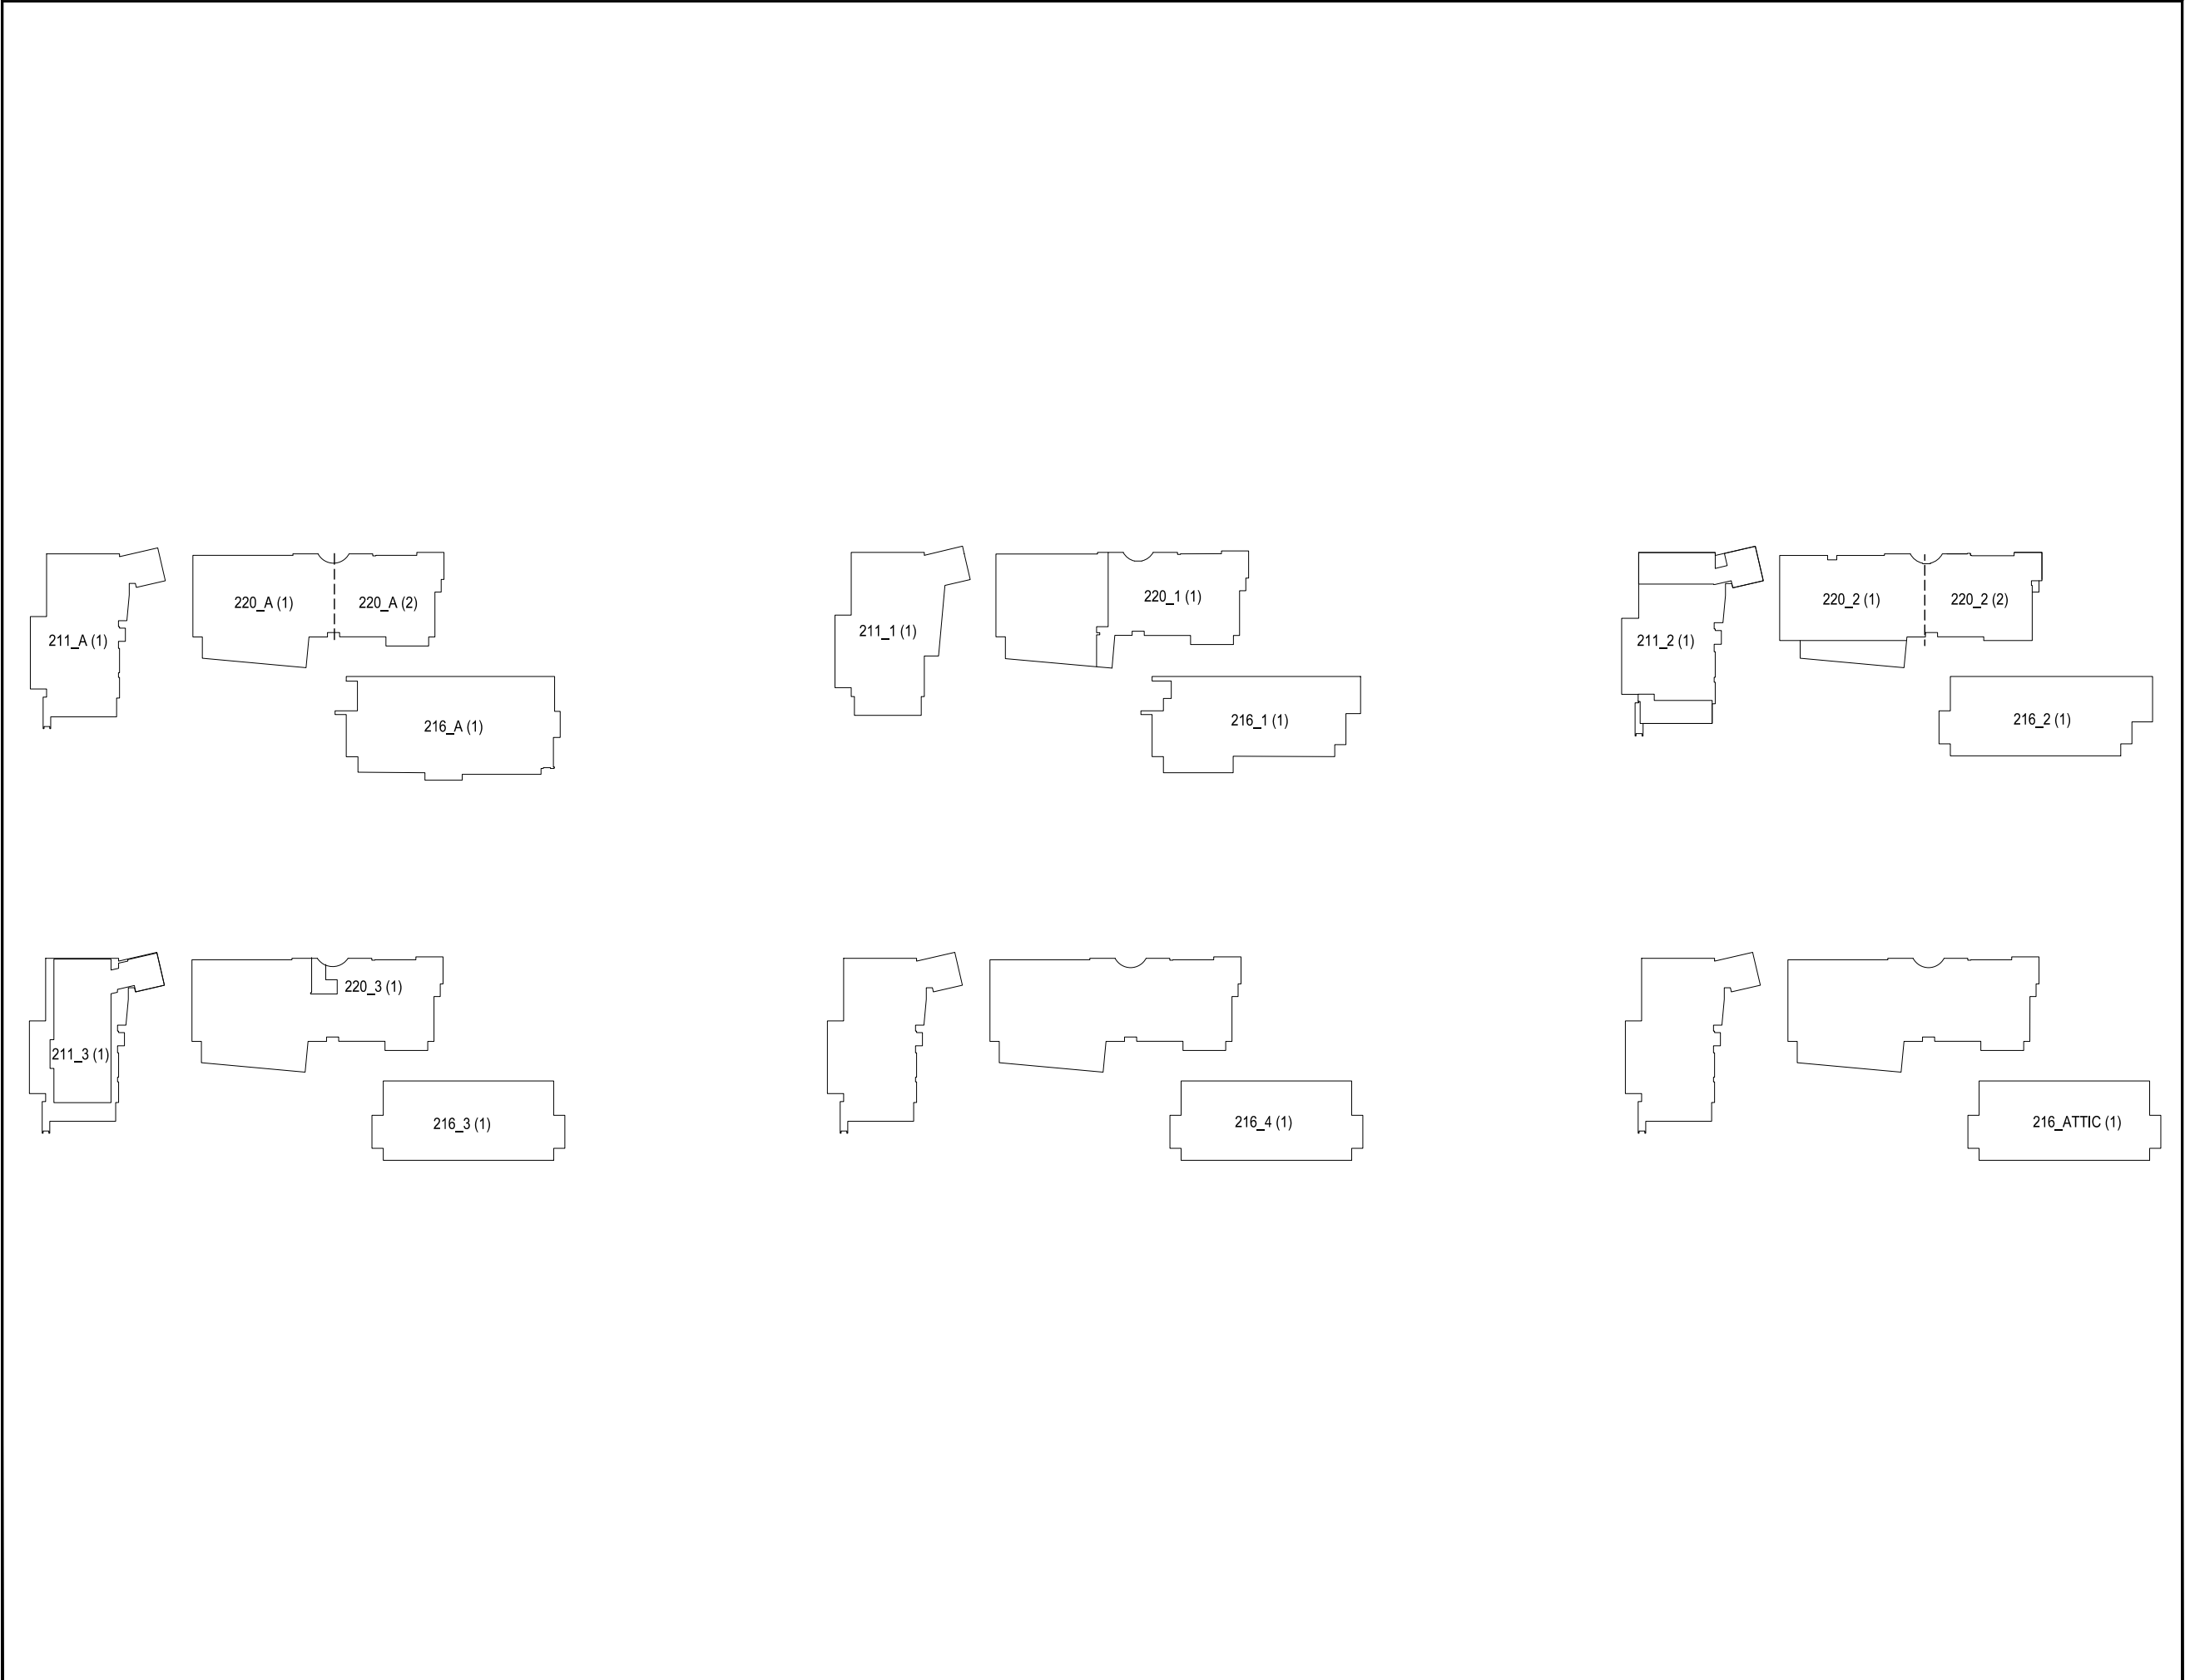

SYMBOL LEGEND

DOOR	DRINKING FOUNTAIN
SLIDING DOOR	LAVATORY
ACCORDION PARTITION	SINK
STACK OR FOLDING PARTITION	TOILET
WINDOW/GLAZING	URINAL
HIGH WINDOW	LOCKER
SKYLIGHT	LAN DISTRIBUTION FRAME
STOOP/STEP UP	VENT HOOD
STAIR	WALL SHELVING
RAMP	UPPER CABINET
ACCESS LADDER	BASE CABINET
COLD STORAGE	TEACHER CABINET
AREA CALCULATED @ 50 %	MATCHLINE
SLOPING ROOF	FLAT ROOF

TITLEBLOCK LEGEND

SHEET NAME:	BLDG #_ FLOOR # (# IN SERIES)

KEY PLAN

NTS

NORTH

Updated By:	FUS Review:	100% Submittal Date:
AA	MRS	01 MAY 2020


NOT TO SCALE

dodeca
DEPARTMENT OF DEFENSE EDUCATION ACTIVITY
FACILITY UTILIZATION SURVEY

SIGONELLA
MIDDLE / HIGH SCHOOL


BUILDING NUMBER: 211, 216, 220
COUNTRY: ITALY
INSTALLATION: NAS SIGONELLA
SITE: NAS1 SUPPORT AREA
REGION-DISTRICT: DODEA EUROPE SOUTH

DoDAAC Number:	Floor:	Survey Date:
HE5515	LEVEL A-5	JANUARY 2020
Sheet Name:		Sheet Seq:
KEY PLAN		6 of 24

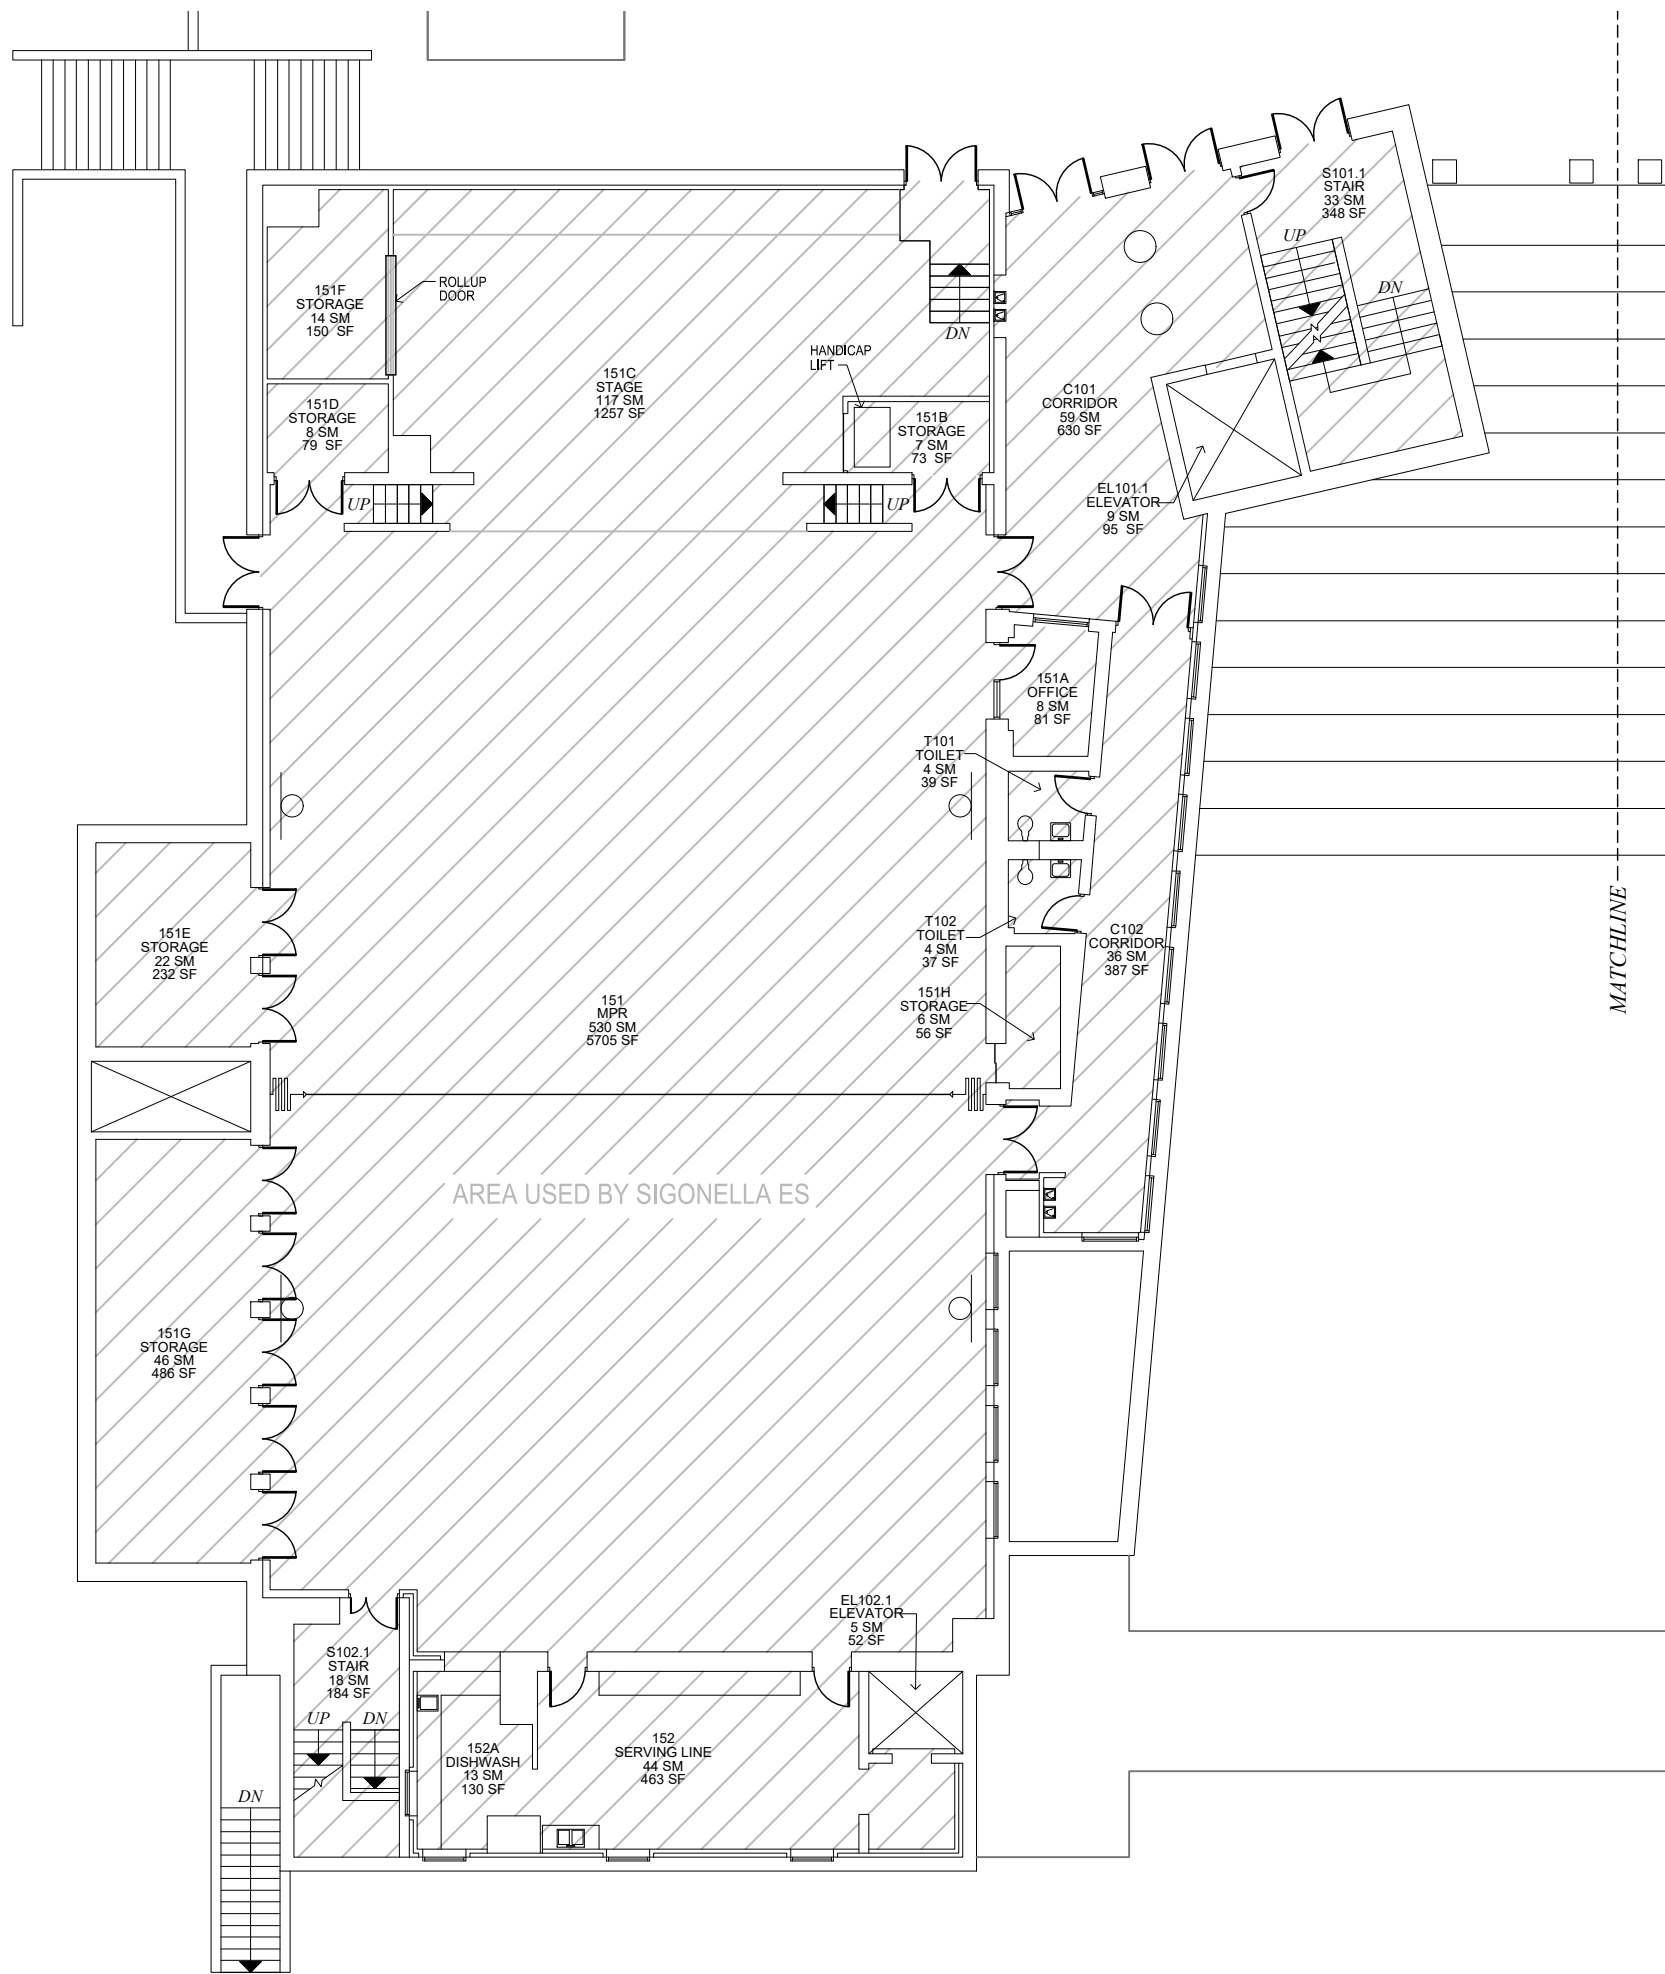

SYMBOL LEGEND	
	DOOR
	DRINKING FOUNTAIN
	SLIDING DOOR
	LAVATORY
	ACCORDION PARTITION
	SINK
	STACK OR FOLDING PARTITION
	TOILET
	WINDOW/GLAZING
	URINAL
	HIGH WINDOW
	LOCKER
	SKYLIGHT
	LAN DISTRIBUTION FRAME
	STOOP/STEP UP
	VENT HOOD
	STAIR
	WALL SHELVING
	RAMP
	UPPER CABINET
	ACCESS LADDER
	BASE CABINET
	COLD STORAGE
	TEACHER CABINET
	AREA CALCULATED @ 50 %
	MATCHLINE
	SLOPING ROOF
	FLAT ROOF


TITLEBLOCK LEGEND	
SHEET NAME:	BLDG #_FLOOR # (# IN SERIES)

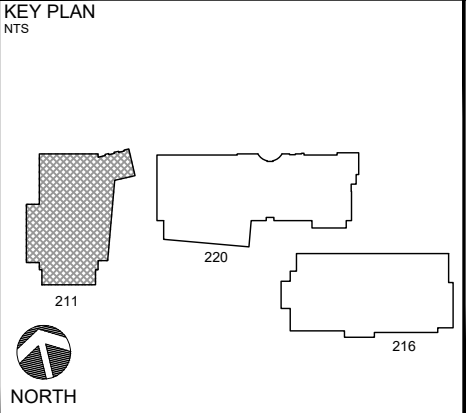

Updated By:	FUS Review:	100% Submittal Date:
AA	MRS	01 MAY 2020
0 2 4 8 16 FT		

dodea
DEPARTMENT OF DEFENSE EDUCATION ACTIVITY
FACILITY UTILIZATION SURVEY

SIGONELLA MIDDLE / HIGH SCHOOL		
BUILDING NUMBER: 211		
COUNTRY: ITALY		
INSTALLATION: NAS SIGONELLA		
SITE: NAS1 SUPPORT AREA		
REGION-DISTRICT: DODEA EUROPE SOUTH		
DoDAAC Number:	Floor:	Survey Date:
HE5515	LEVEL 1	JANUARY 2020
Sheet Name:	Sheet Seq:	
211_1 (1)	8 of 24	

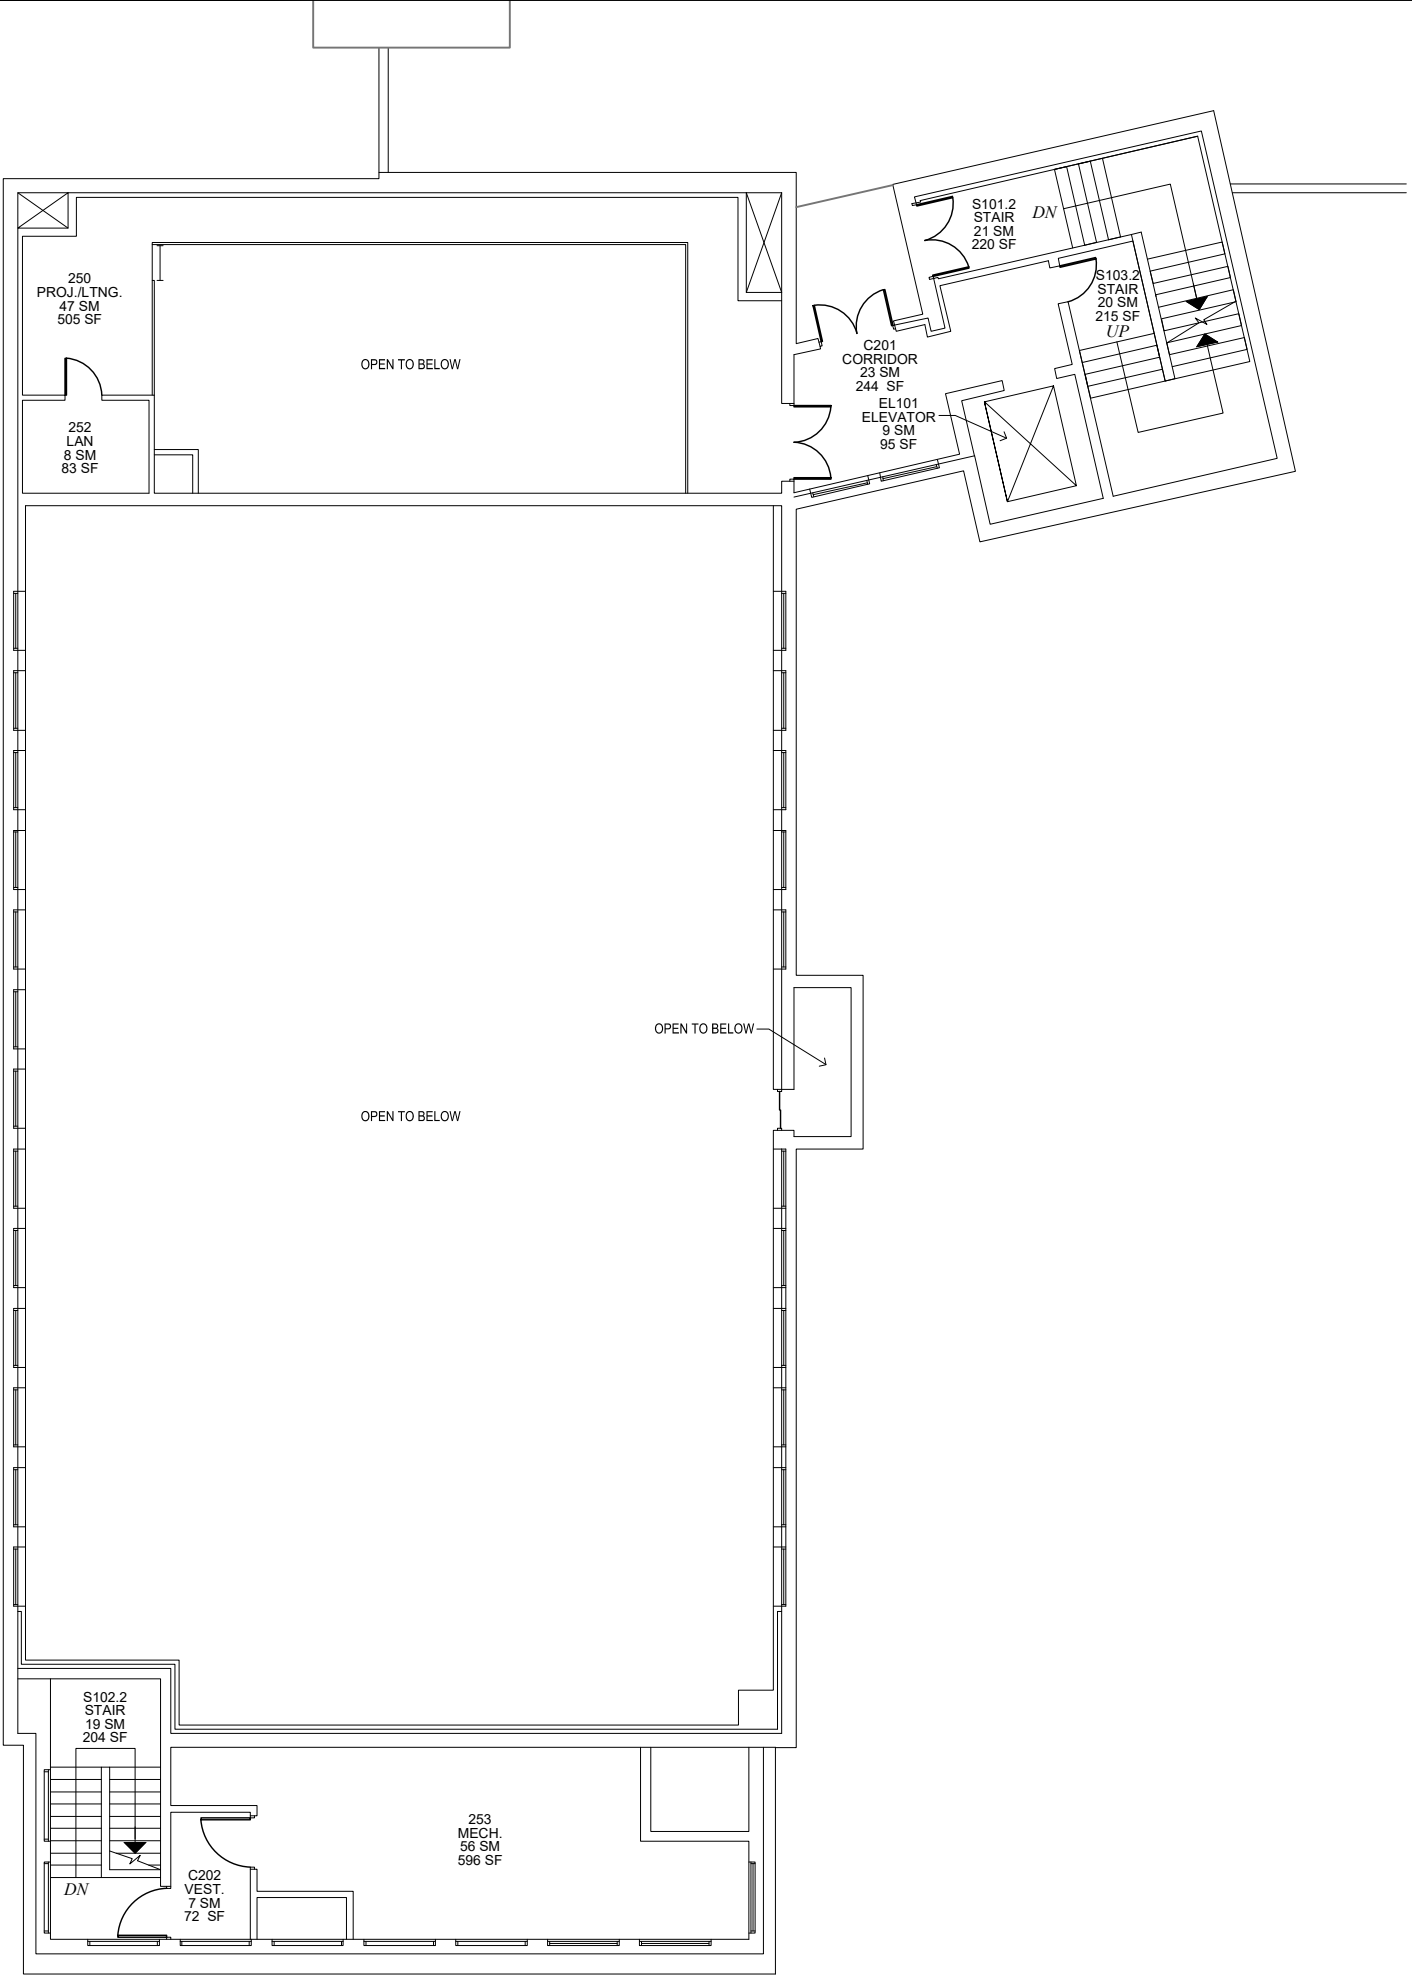

SYMBOL LEGEND

DOOR	DRINKING FOUNTAIN
SLIDING DOOR	LAVATORY
ACCORDION PARTITION	SINK
STACK OR FOLDING PARTITION	TOILET
WINDOW/GLAZING	URINAL
HIGH WINDOW	LOCKER
SKYLIGHT	LAN DISTRIBUTION FRAME
STOOP/STEP UP	VENT HOOD
STAIR	WALL SHELVING
RAMP	UPPER CABINET
ACCESS LADDER	BASE CABINET
COLD STORAGE	TEACHER CABINET
AREA CALCULATED @ 50 %	MATCHLINE
SLOPING ROOF	FLAT ROOF

TITLEBLOCK LEGEND

SHEET NAME:	BLDG #_FLOOR # (# IN SERIES)

KEY PLAN

NTS

Updated By: AA

FUS Review: MRS

100% Submittal Date: 01 MAY 2020

dodea

DEPARTMENT OF DEFENSE EDUCATION ACTIVITY

FACILITY UTILIZATION SURVEY

SIGONELLA

MIDDLE / HIGH SCHOOL

BUILDING NUMBER: 211


COUNTRY: ITALY

INSTALLATION: NAS SIGONELLA

SITE: NAS1 SUPPORT AREA


REGION-DISTRICT: DODEA EUROPE SOUTH

DoDAAC Number: HE5515	Floor: LEVEL 2	Survey Date: JANUARY 2020
Sheet Name: 211_2 (1)		Sheet Seq: 9 of 24

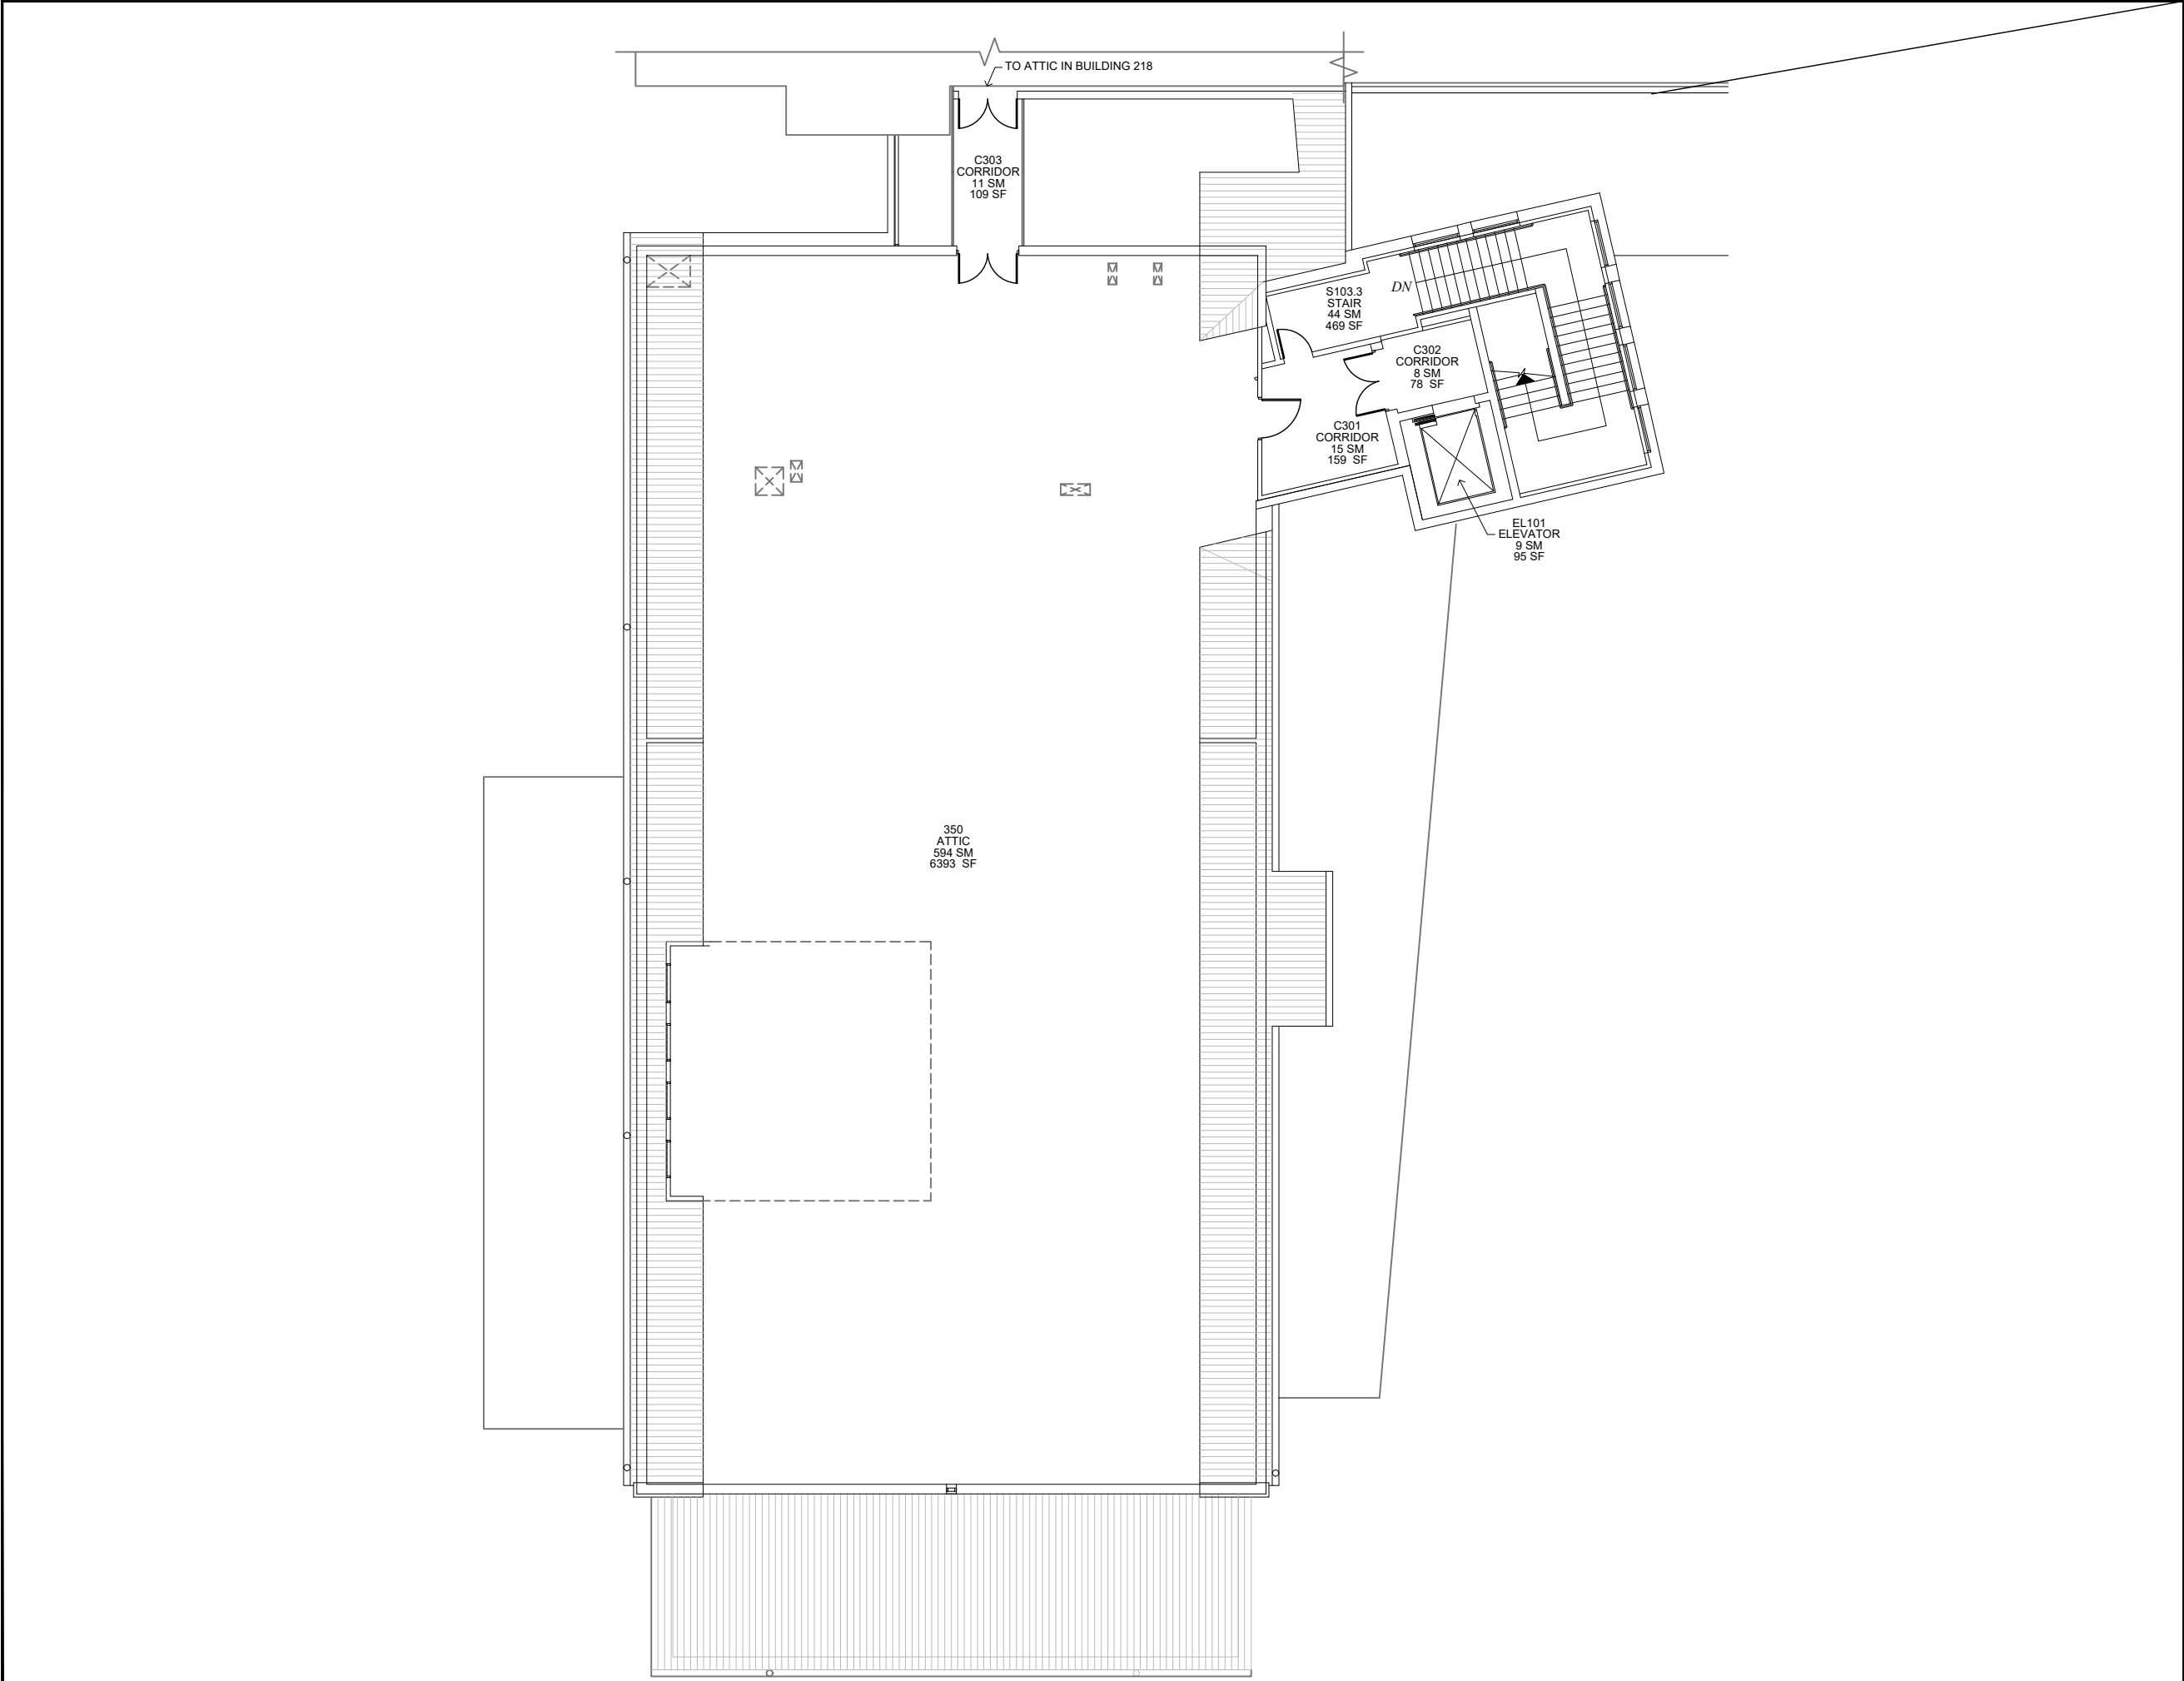

SYMBOL LEGEND	
	DOOR
	DRINKING FOUNTAIN
	SLIDING DOOR
	LAVATORY
	ACCORDION PARTITION
	SINK
	STACK OR FOLDING PARTITION
	TOILET
	WINDOW/GLAZING
	URINAL
	HIGH WINDOW
	LOCKER
	SKYLIGHT
	LAN DISTRIBUTION FRAME
	STOOP/STEP UP
	VENT HOOD
	STAIR
	WALL SHELVING
	RAMP
	UPPER CABINET
	ACCESS LADDER
	BASE CABINET
	COLD STORAGE
	TEACHER CABINET
	AREA CALCULATED @ 50 %
	MATCHLINE
	SLOPING ROOF
	FLAT ROOF

TITLEBLOCK LEGEND	
SHEET NAME:	BLDG #_FLOOR # (# IN SERIES)

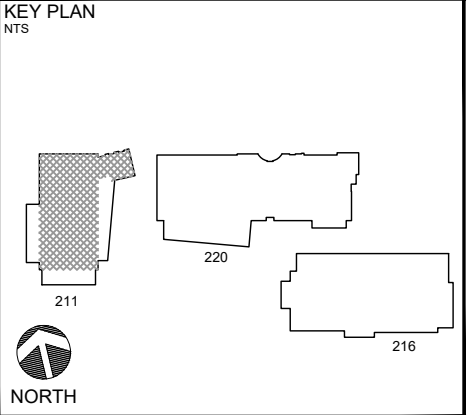

Updated By:	FUS Review:	100% Submittal Date:
AA	MRS	01 MAY 2020
0 2 4 8 16 FT		


DEPARTMENT OF DEFENSE EDUCATION ACTIVITY

FACILITY UTILIZATION SURVEY

SIGONELLA
MIDDLE / HIGH SCHOOL

BUILDING NUMBER: 211
COUNTRY: ITALY
INSTALLATION: NAS SIGONELLA
SITE: NAS1 SUPPORT AREA
REGION-DISTRICT: DODEA EUROPE SOUTH

DoDAAC Number: HE5515	Floor: LEVEL 3	Survey Date: JANUARY 2020
Sheet Name: 211_3 (1)	Sheet Seq: 10 of 24	

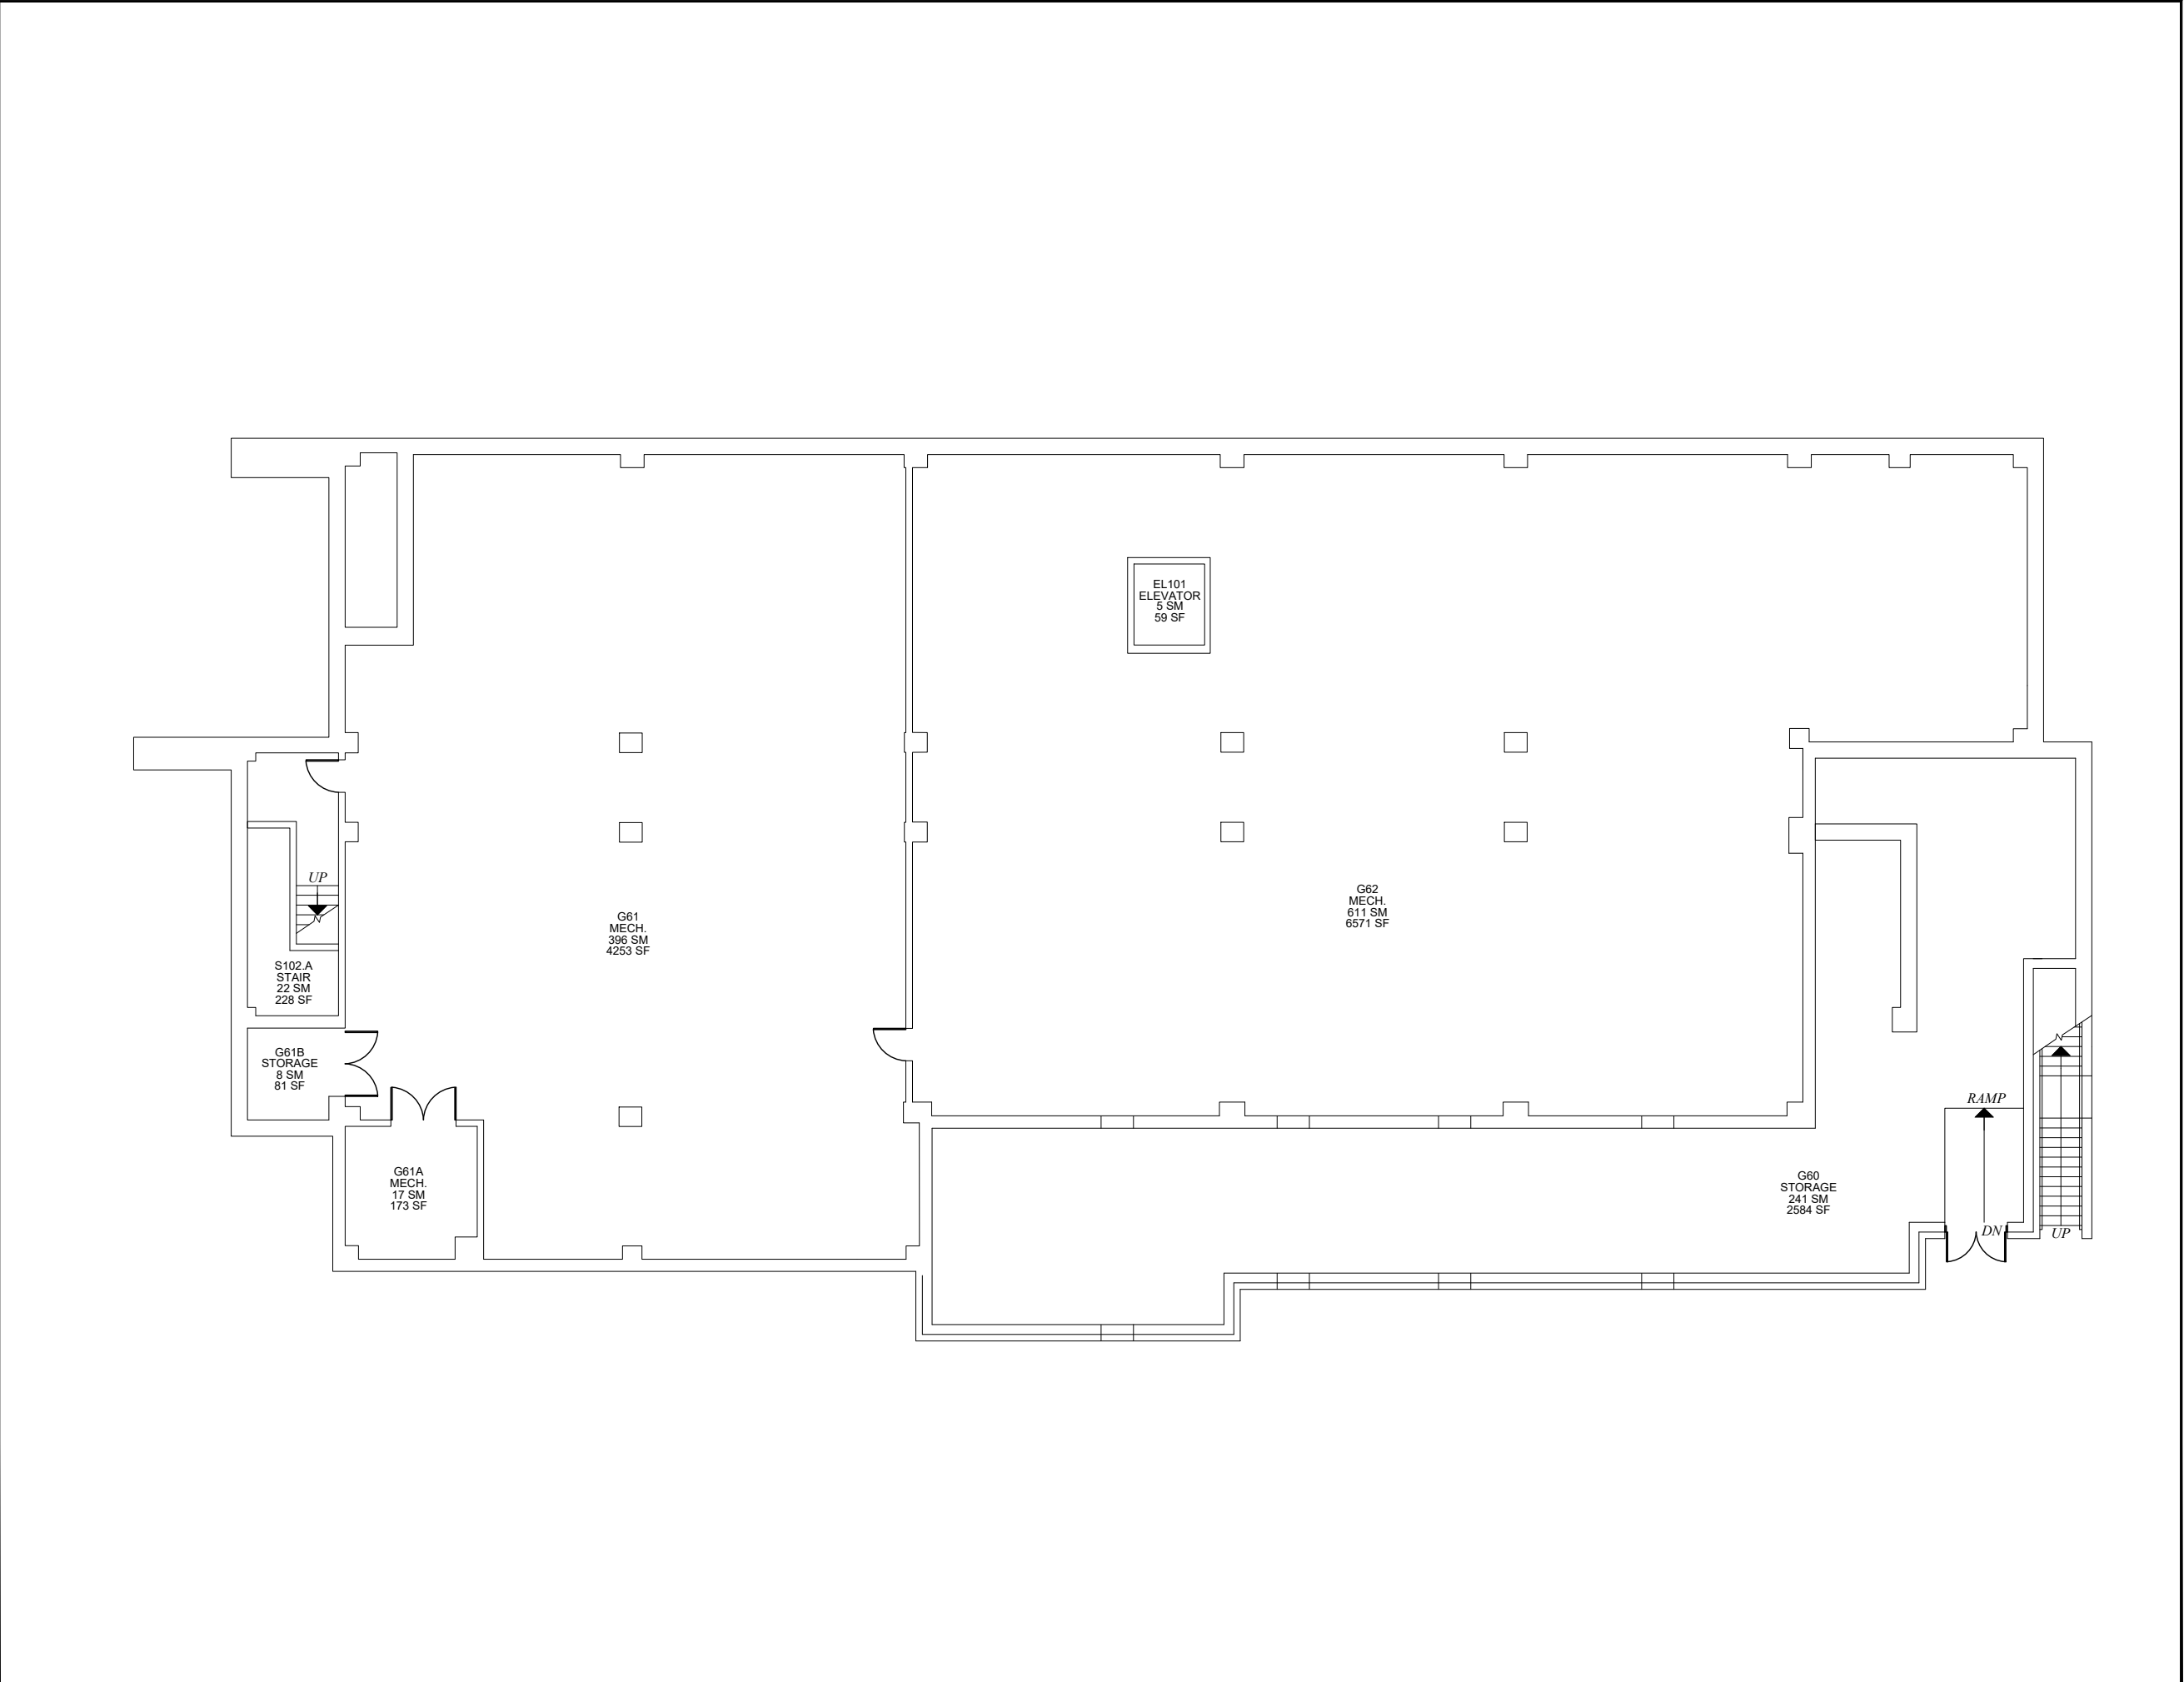

SYMBOL LEGEND

DOOR	DRINKING FOUNTAIN
SLIDING DOOR	LAVATORY
ACCORDION PARTITION	SINK
STACK OR FOLDING PARTITION	TOILET
WINDOW/GLAZING	URINAL
HIGH WINDOW	LOCKER
SKYLIGHT	LAN DISTRIBUTION FRAME
STOOP/STEP UP	VENT HOOD
STAIR	WALL SHELVING
RAMP	UPPER CABINET
ACCESS LADDER	BASE CABINET
COLD STORAGE	TEACHER CABINET
AREA CALCULATED @ 50 %	MATCHLINE
SLOPING ROOF	FLAT ROOF

TITLEBLOCK LEGEND

SHEET NAME:	BLDG #_FLOOR # (# IN SERIES)

KEY PLAN

NTS

NORTH

Updated By:	FUS Review:	100% Submittal Date:
AA	MRS	01 MAY 2020

0

2

4

8

16

FT

dodea

DEPARTMENT OF DEFENSE EDUCATION ACTIVITY

FACILITY UTILIZATION SURVEY

SIGONELLA

MIDDLE / HIGH SCHOOL

BUILDING NUMBER: 216


COUNTRY: ITALY

INSTALLATION: NAS SIGONELLA

SITE: NAS1 SUPPORT AREA


REGION-DISTRICT: DODEA EUROPE SOUTH

DoDAAC Number:	Floor:	Survey Date:
HE5515	LEVEL A	JANUARY 2020
Sheet Name:	Sheet Seq:	
216_A (1)	11 of 24	

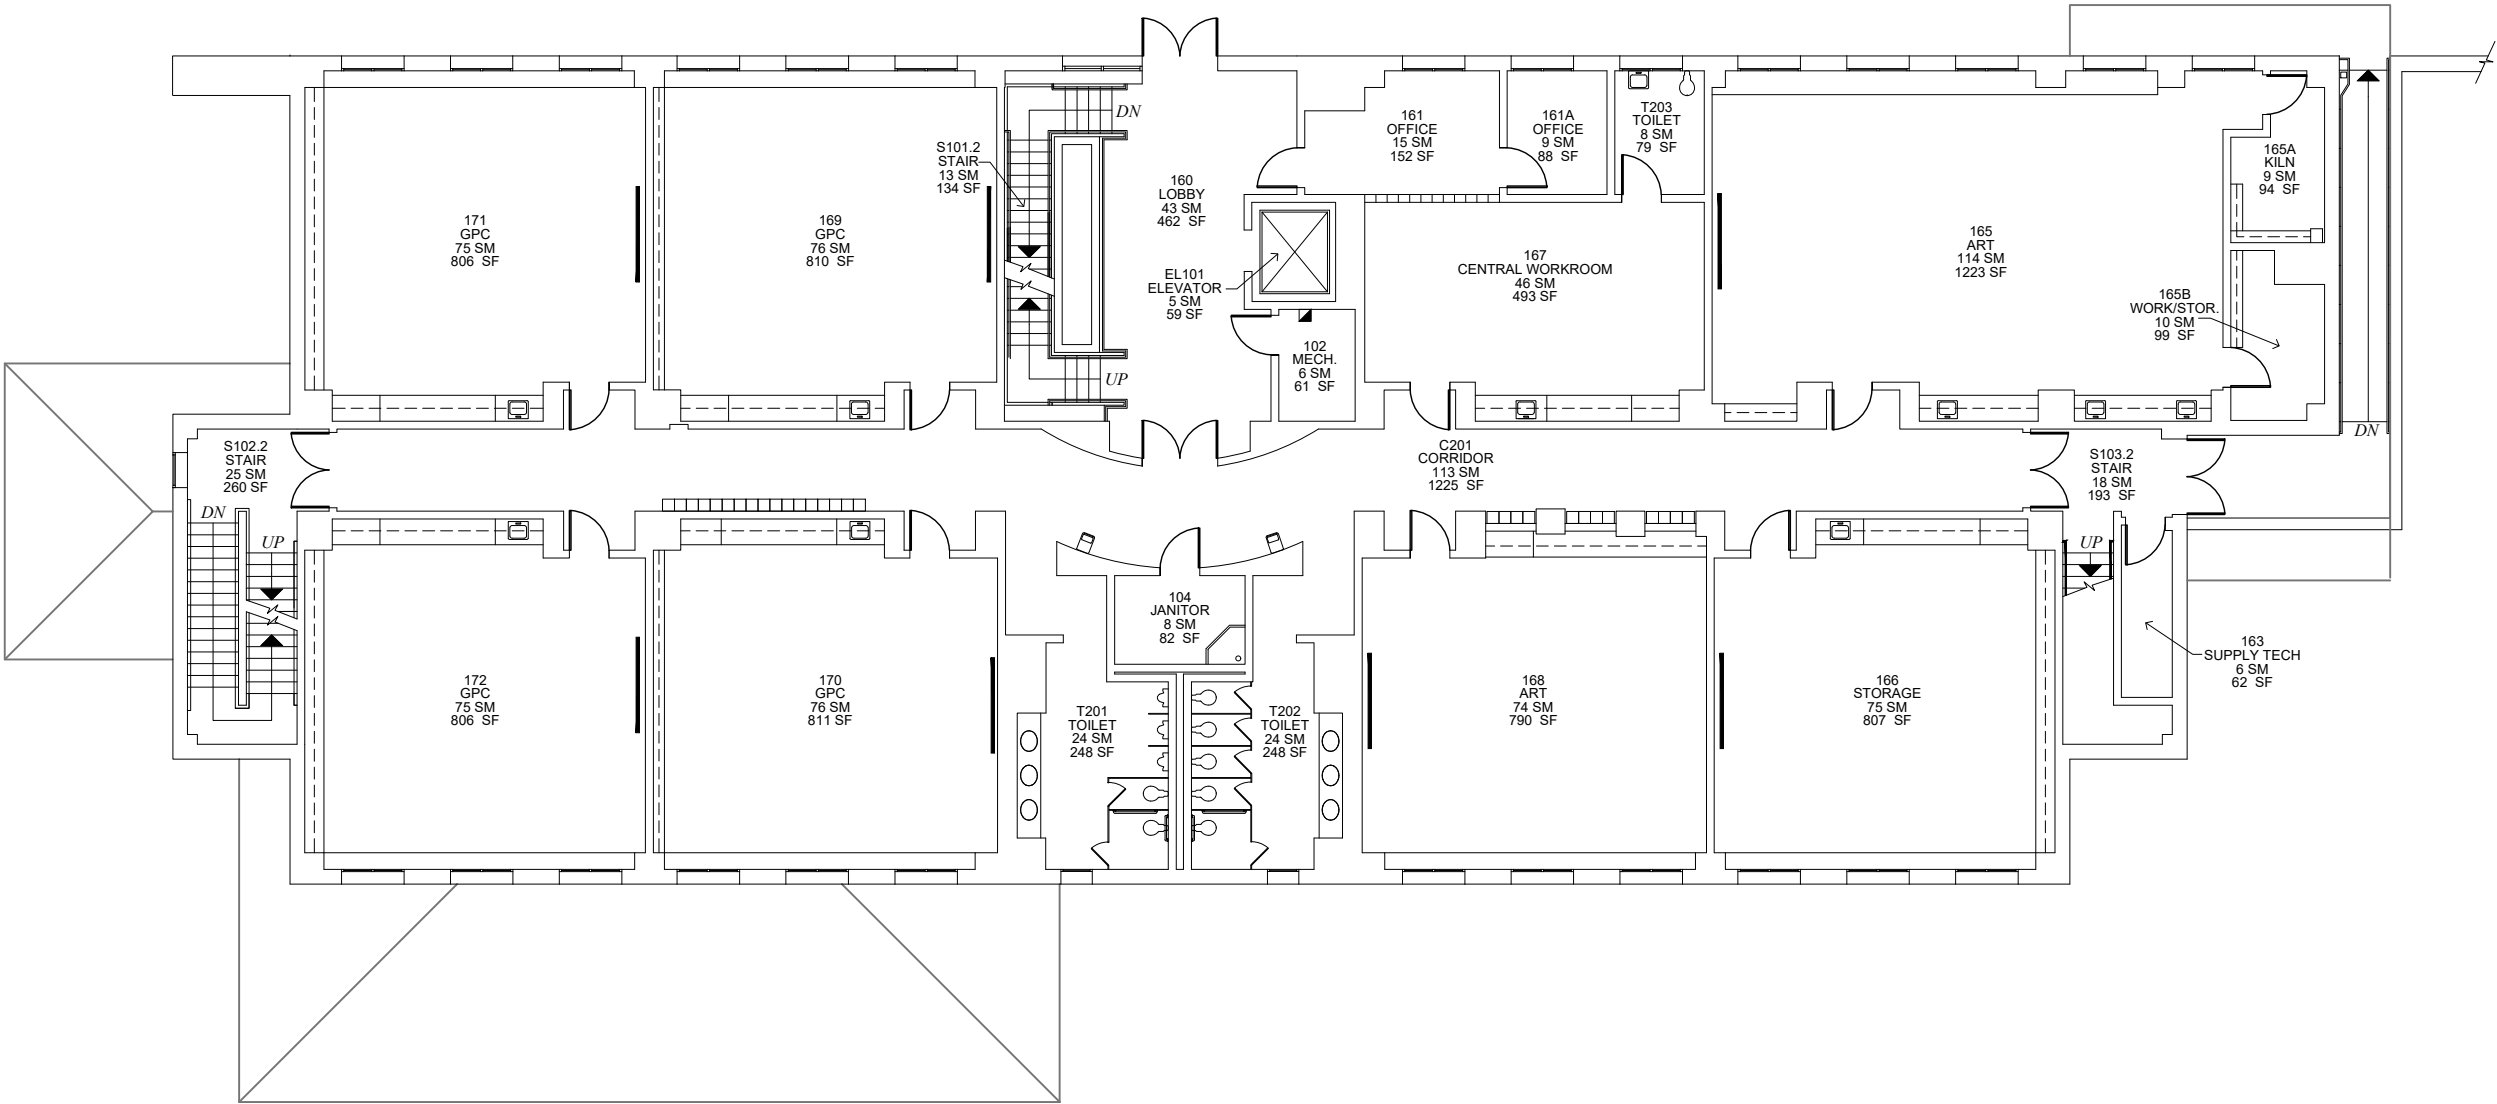

SYMBOL LEGEND	
	DOOR
	DRINKING FOUNTAIN
	SLIDING DOOR
	LAVATORY
	ACCORDION PARTITION
	SINK
	STACK OR FOLDING PARTITION
	TOILET
	WINDOW/GLAZING
	URINAL
	HIGH WINDOW
	LOCKER
	SKYLIGHT
	LAN DISTRIBUTION FRAME
	STOOP/STEP UP
	VENT HOOD
	STAIR
	WALL SHELVING
	RAMP
	UPPER CABINET
	ACCESS LADDER
	BASE CABINET
	COLD STORAGE
	TEACHER CABINET
	AREA CALCULATED @ 50 %
	MATCHLINE
	SLOPING ROOF
	FLAT ROOF


TITLEBLOCK LEGEND	
SHEET NAME:	BLDG #_FLOOR # (# IN SERIES)

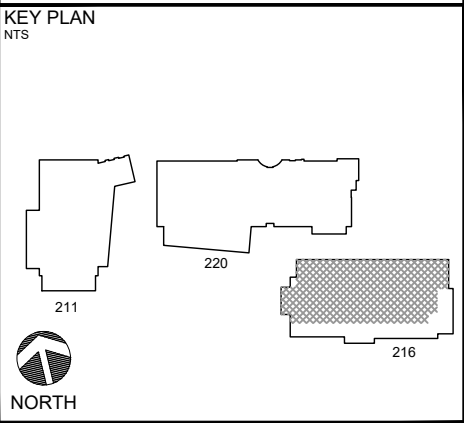

Updated By:	FUS Review:	100% Submittal Date:
AA	MRS	01 MAY 2020
0 2 4 8 16 FT		

dodea
DEPARTMENT OF DEFENSE EDUCATION ACTIVITY
FACILITY UTILIZATION SURVEY

SIGONELLA MIDDLE / HIGH SCHOOL BUILDING NUMBER: 216 COUNTRY: ITALY INSTALLATION: NAS SIGONELLA SITE: NAS1 SUPPORT AREA REGION-DISTRICT: DODEA EUROPE SOUTH		
DoDAAC Number: HE5515	Floor: LEVEL 2	Survey Date: JANUARY 2020
Sheet Name: 216_2 (1)	Sheet Seq: 13 of 24	

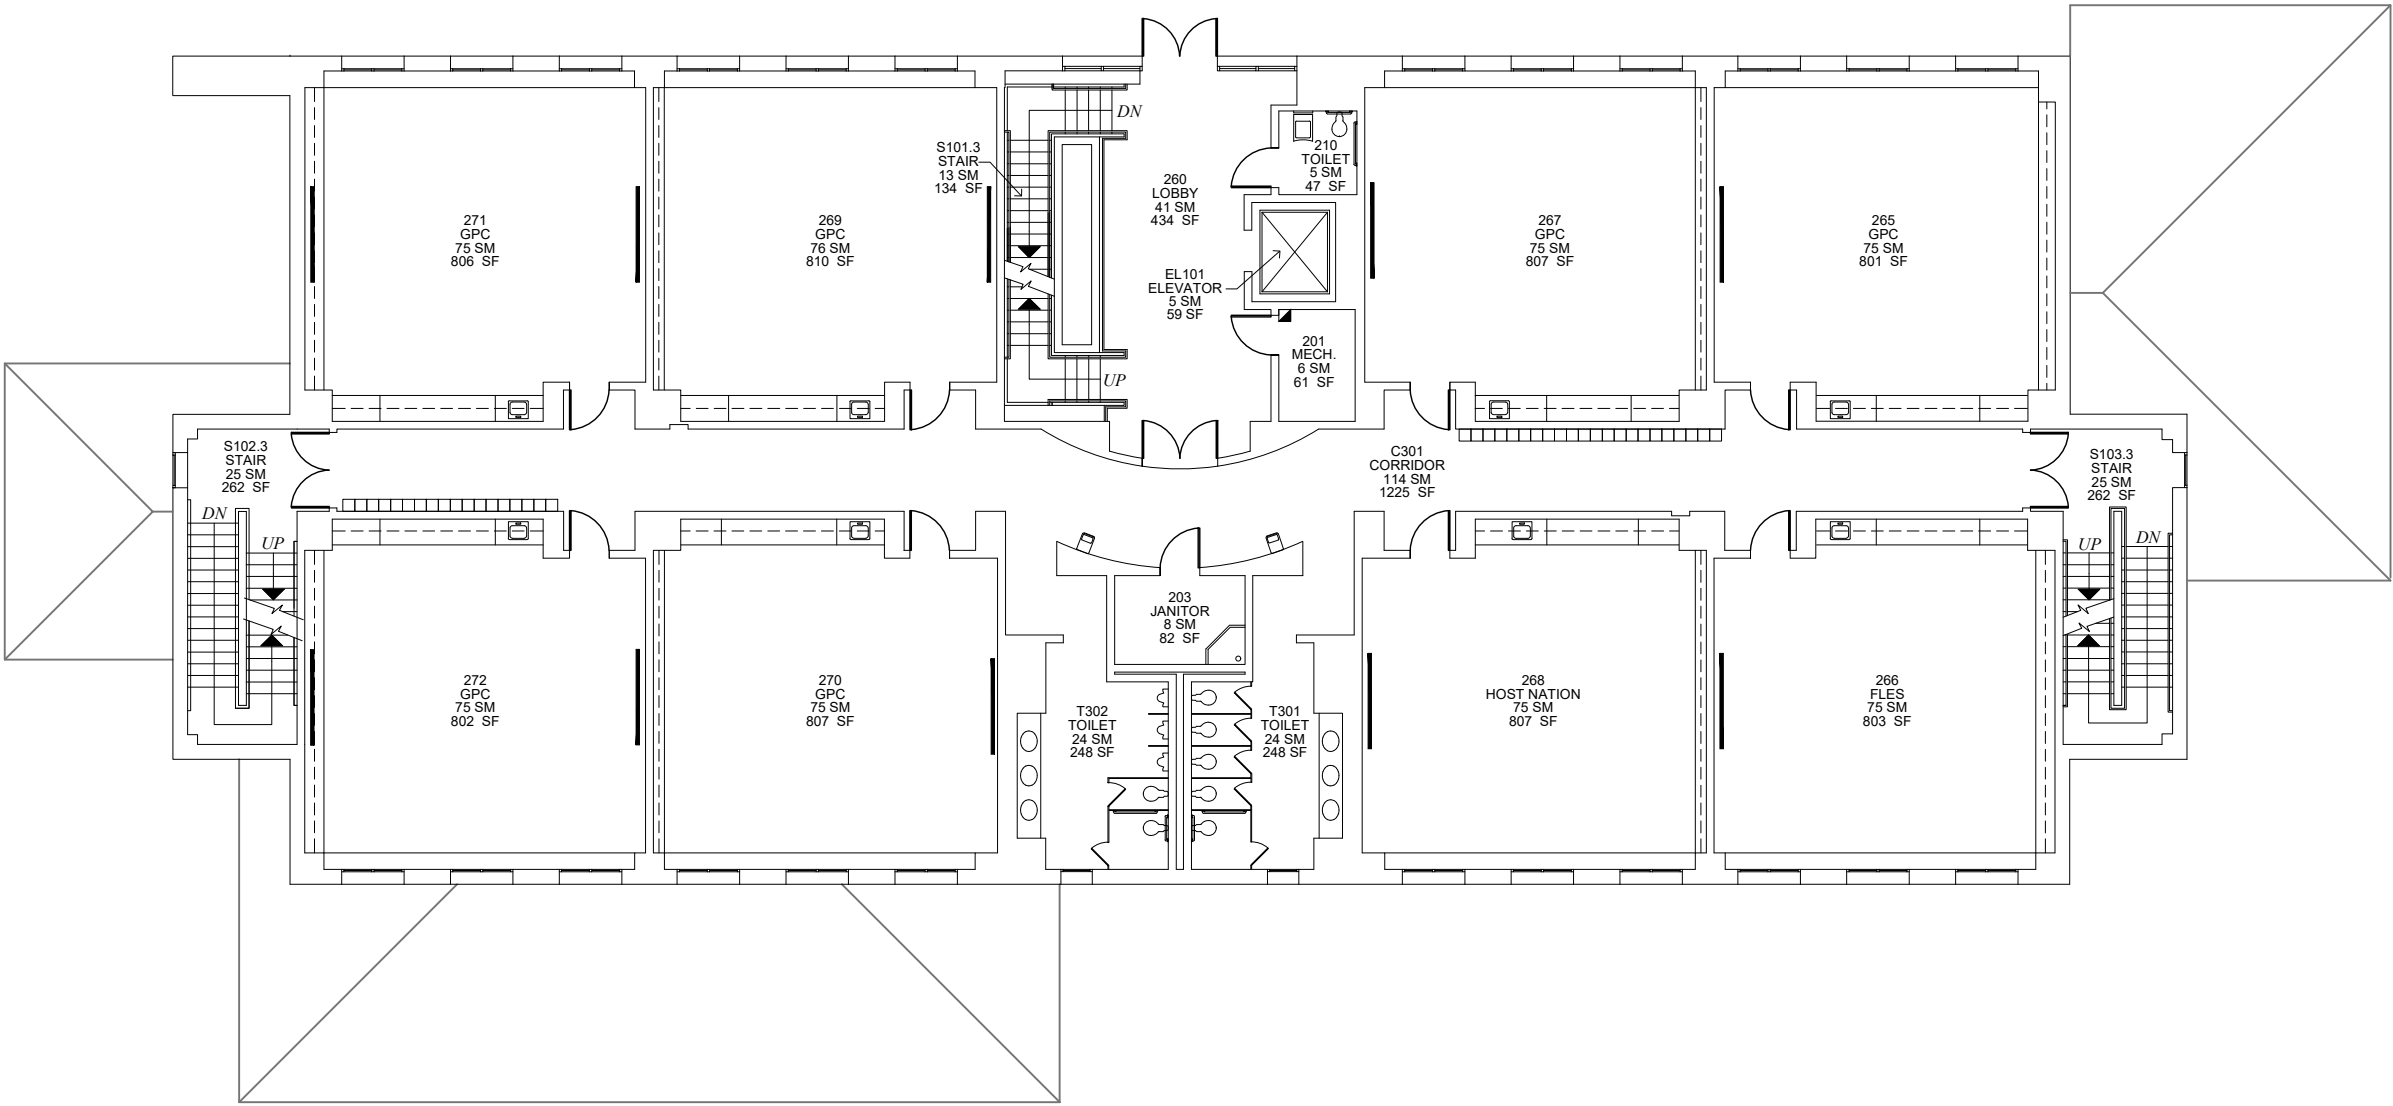

DOOR

SLIDING DOOR

ACCORDION PARTITION

STACK OR FOLDING PARTITION

WINDOW/GLAZING

HIGH WINDOW

SKYLIGHT

STOOP/STEP UP

STAIR

RAMP

ACCESS LADDER

COLD STORAGE

AREA CALCULATED @ 50 %

SLOPING ROOF

DRINKING FOUNTAIN

LAVATORY

SINK

TOILET

URINAL

LOCKER

LAN DISTRIBUTION FRAME

VENT HOOD

WALL SHELVING

UPPER CABINET

BASE CABINET

TEACHER CABINET

MATCHLINE

FLAT ROOF

TITLEBLOCK LEGEND

SHEET NAME:

BLDG #_FLOOR # (# IN SERIES)

KEY PLAN

NTS

211

220

216

NORTH

0 2 4 8 16 FT

Updated By: AA

FUS Review: MRS

100% Submittal Date: 01 MAY 2020

0 2 4 8 16 FT

dodea

DEPARTMENT OF DEFENSE EDUCATION ACTIVITY

FACILITY UTILIZATION SURVEY

SIGONELLA

MIDDLE / HIGH SCHOOL

BUILDING NUMBER: 216

COUNTRY: ITALY

INSTALLATION: NAS SIGONELLA

SITE: NAS1 SUPPORT AREA

REGION-DISTRICT: DODEA EUROPE SOUTH


DoDAAC Number: HE5515

Floor: LEVEL 3

Survey Date: JANUARY 2020


Sheet Name: 216_3 (1)

Sheet Seq: 14 of 24

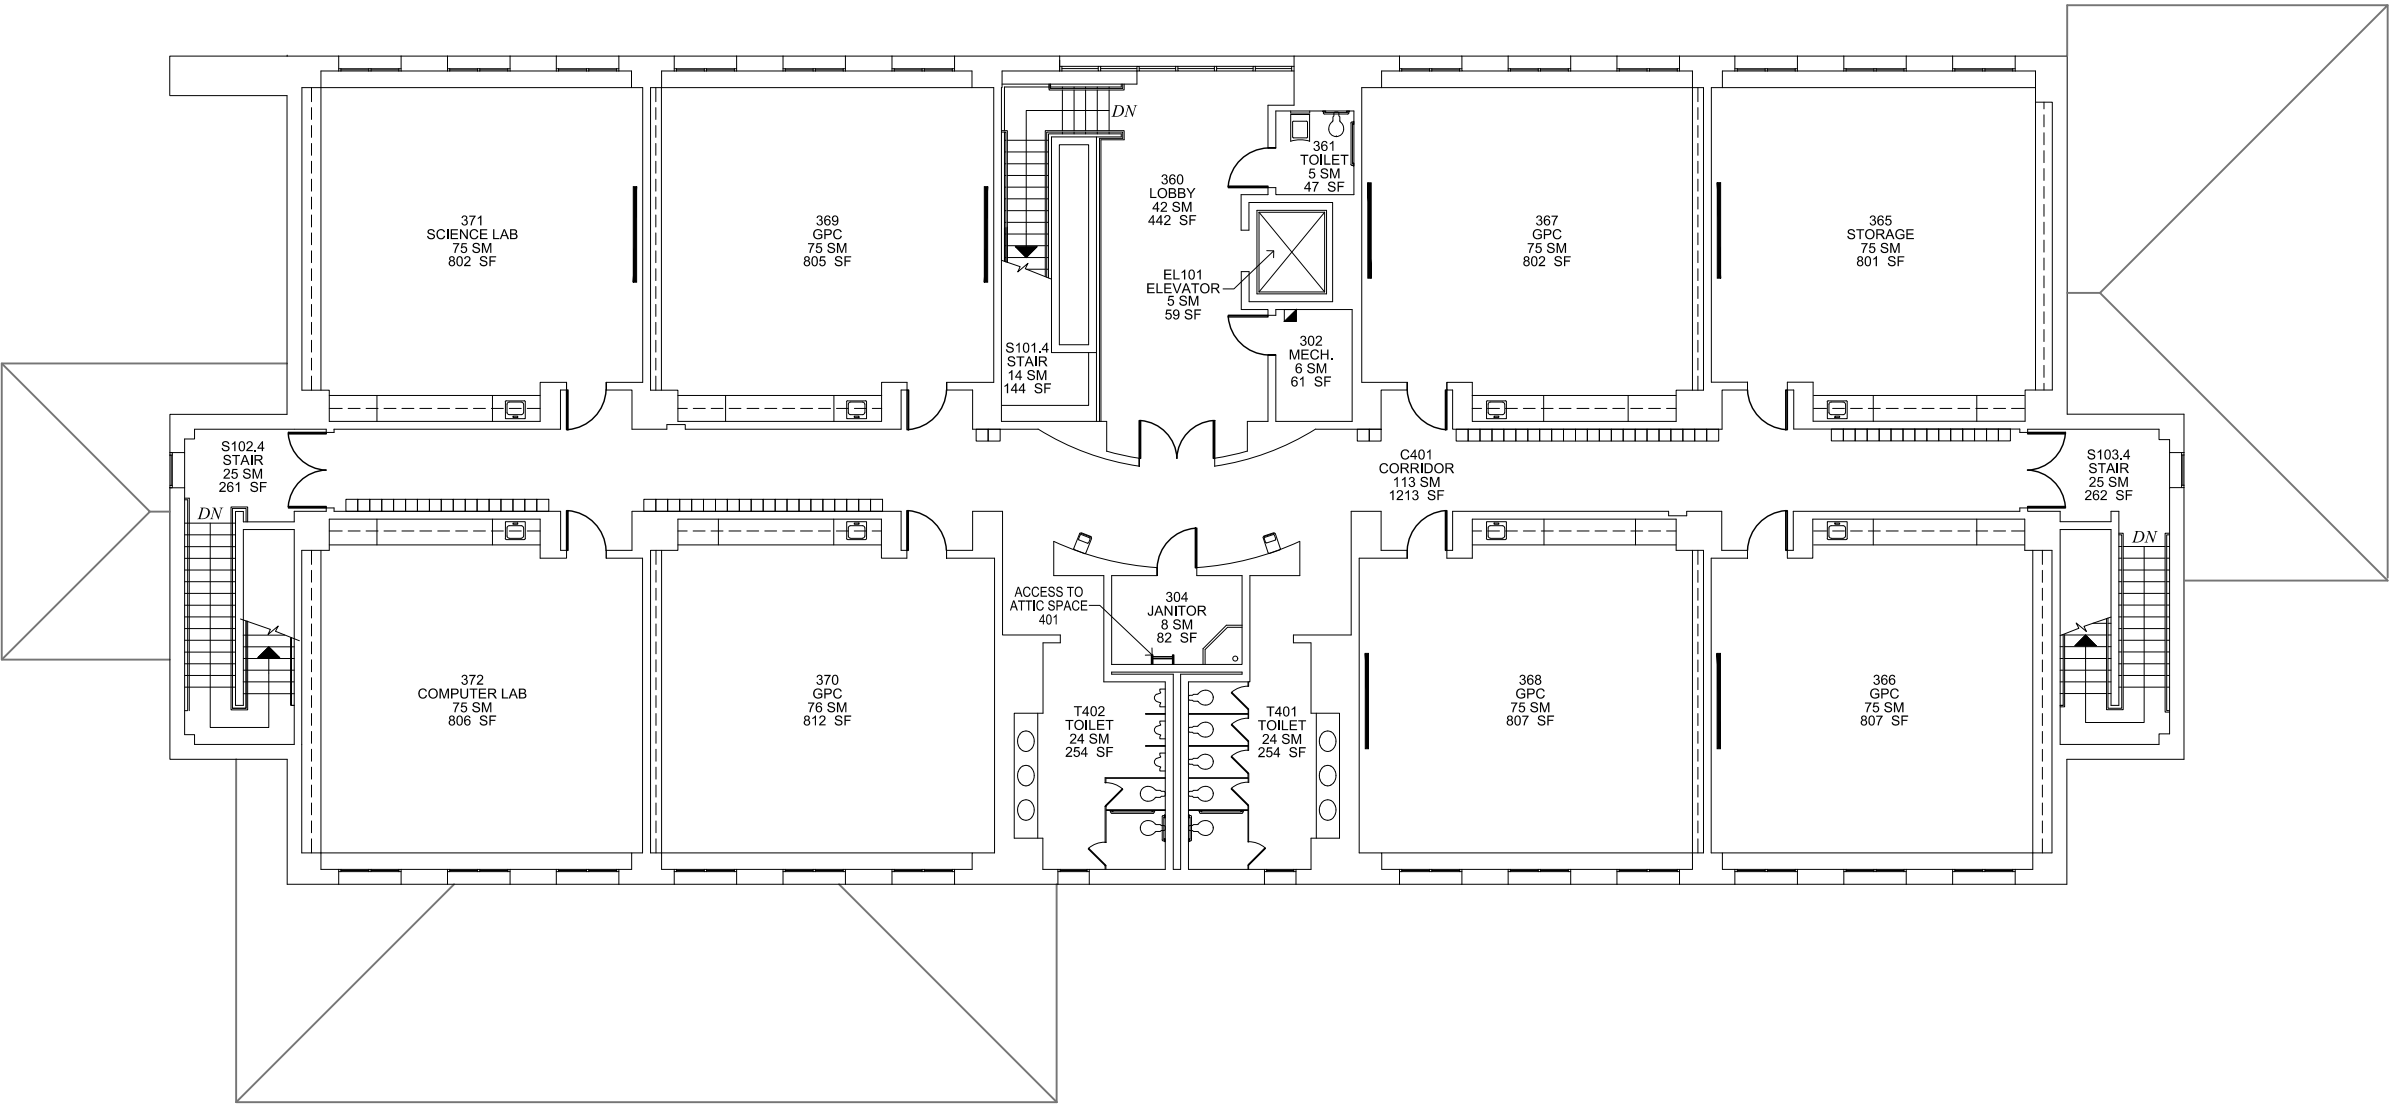

SYMBOL LEGEND	
	DOOR
	DRINKING FOUNTAIN
	SLIDING DOOR
	LAVATORY
	ACCORDION PARTITION
	SINK
	STACK OR FOLDING PARTITION
	TOILET
	WINDOW/GLAZING
	URINAL
	HIGH WINDOW
	LOCKER
	SKYLIGHT
	LAN DISTRIBUTION FRAME
	STOOP/STEP UP
	VENT HOOD
	STAIR
	WALL SHELVING
	RAMP
	UPPER CABINET
	ACCESS LADDER
	BASE CABINET
	COLD STORAGE
	TEACHER CABINET
	AREA CALCULATED @ 50 %
	MATCHLINE
	SLOPING ROOF
	FLAT ROOF


TITLEBLOCK LEGEND	
SHEET NAME:	BLDG #_FLOOR # (# IN SERIES)

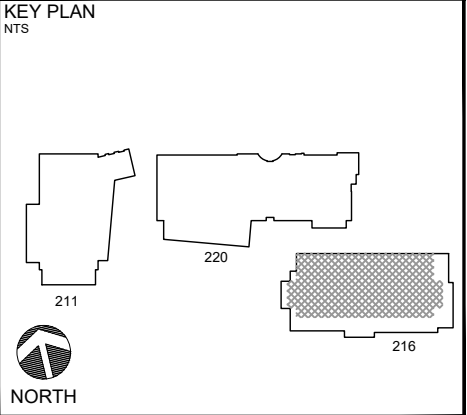

Updated By: AA	FUS Review: MRS	100% Submittal Date: 01 MAY 2020
0 2 4 8 16 FT		

DEPARTMENT OF DEFENSE EDUCATION ACTIVITY
FACILITY UTILIZATION SURVEY

SIGONELLA MIDDLE / HIGH SCHOOL		
BUILDING NUMBER: 216		
COUNTRY: ITALY		
INSTALLATION: NAS SIGONELLA		
SITE: NAS1 SUPPORT AREA		
REGION-DISTRICT: DODEA EUROPE SOUTH		
DoDAAC Number: HE5515	Floor: LEVEL 4	Survey Date: JANUARY 2020
Sheet Name: 216_4 (1)	Sheet Seq: 15 of 24	

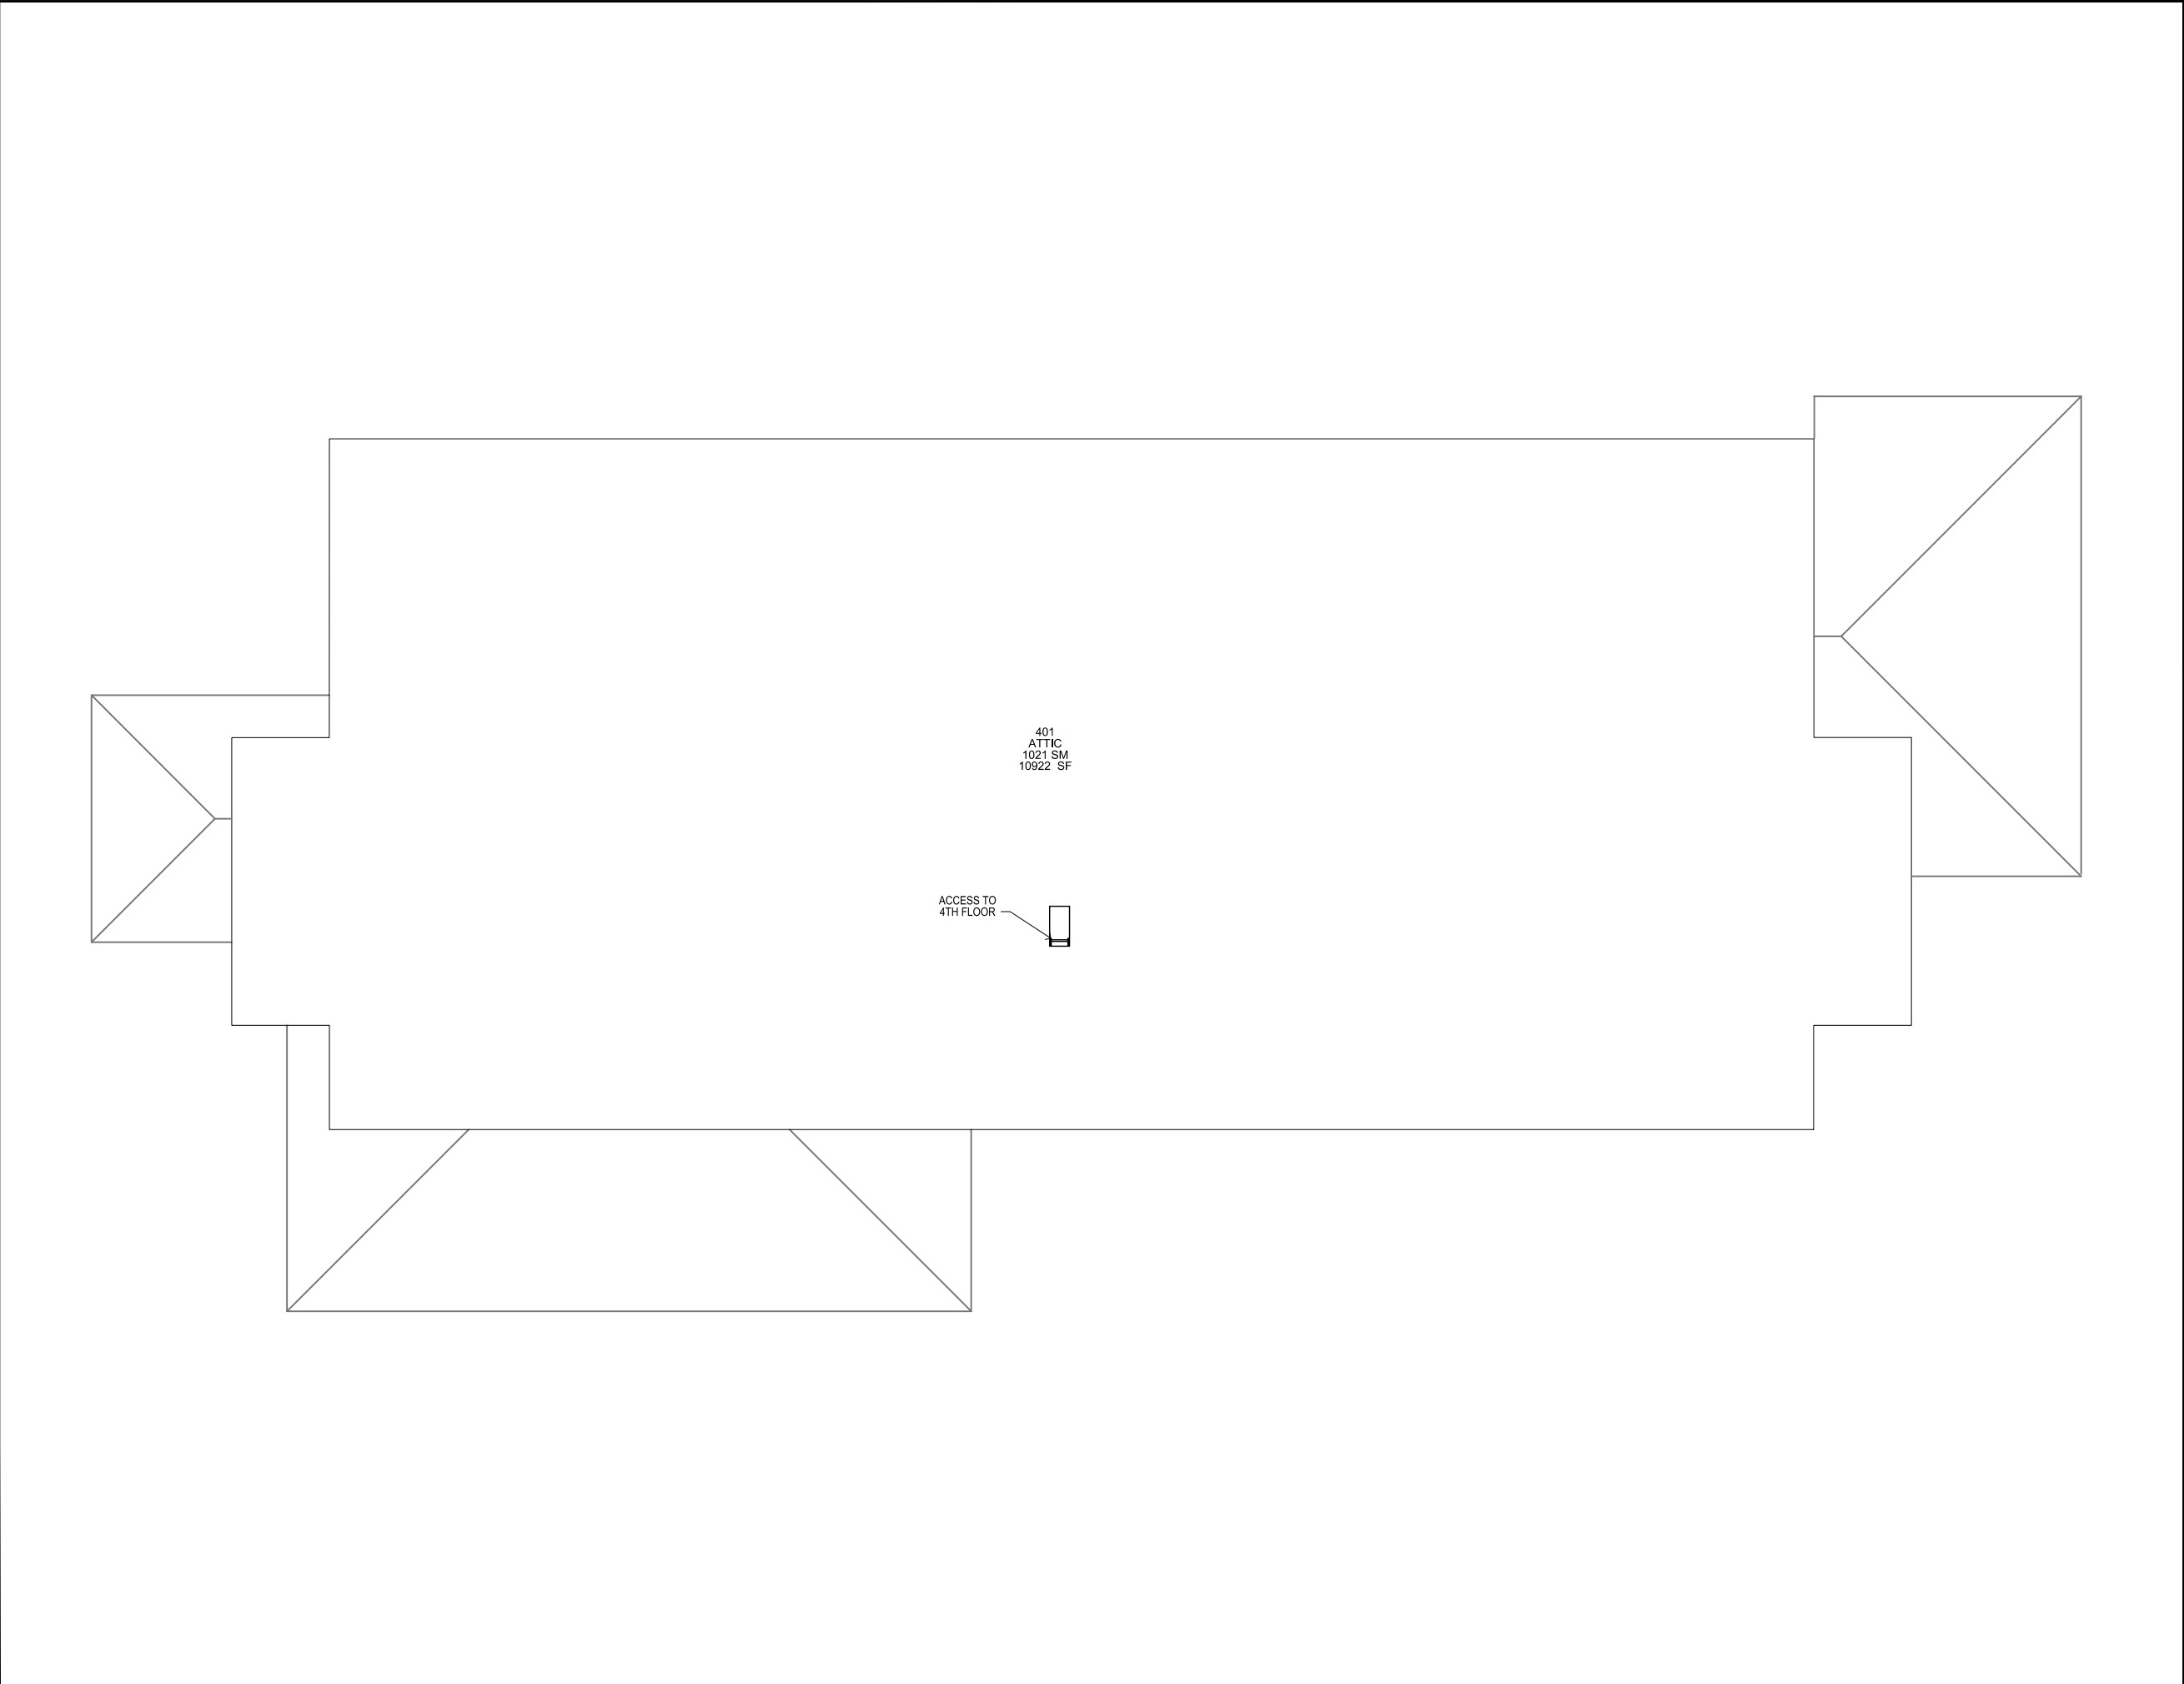

SYMBOL LEGEND

	DOOR		DRINKING FOUNTAIN
	SLIDING DOOR		LAVATORY
	ACCORDION PARTITION		SINK
	STACK OR FOLDING PARTITION		TOILET
	WINDOW/GLAZING		URINAL
	HIGH WINDOW		LOCKER
	SKYLIGHT		LAN DISTRIBUTION FRAME
	STOOP/STEP UP		VENT HOOD
	STAIR		WALL SHELVING
	RAMP		UPPER CABINET
	ACCESS LADDER		BASE CABINET
	COLD STORAGE		TEACHER CABINET
	AREA CALCULATED @ 50 %		MATCHLINE
	SLOPING ROOF		FLAT ROOF

TITLEBLOCK LEGEND

SHEET NAME:	BLDG #_FLOOR # (# IN SERIES)

KEY PLAN

NTS

NORTH

Updated By:	FUS Review:	100% Submittal Date:
AA	MRS	01 MAY 2020

0

2

4

8

16

FT

DEPARTMENT OF DEFENSE EDUCATION ACTIVITY

FACILITY UTILIZATION SURVEY

SIGONELLA

MIDDLE / HIGH SCHOOL

BUILDING NUMBER: 216

COUNTRY: ITALY


INSTALLATION: NAS SIGONELLA

SITE: NAS1 SUPPORT AREA

REGION-DISTRICT: DODEA EUROPE SOUTH


DoDAAC Number:	Floor:	Survey Date:
HE5515	LEVEL 5	JANUARY 2020

Sheet Name:	Sheet Seq:
216_ATTIC (1)	16 of 24

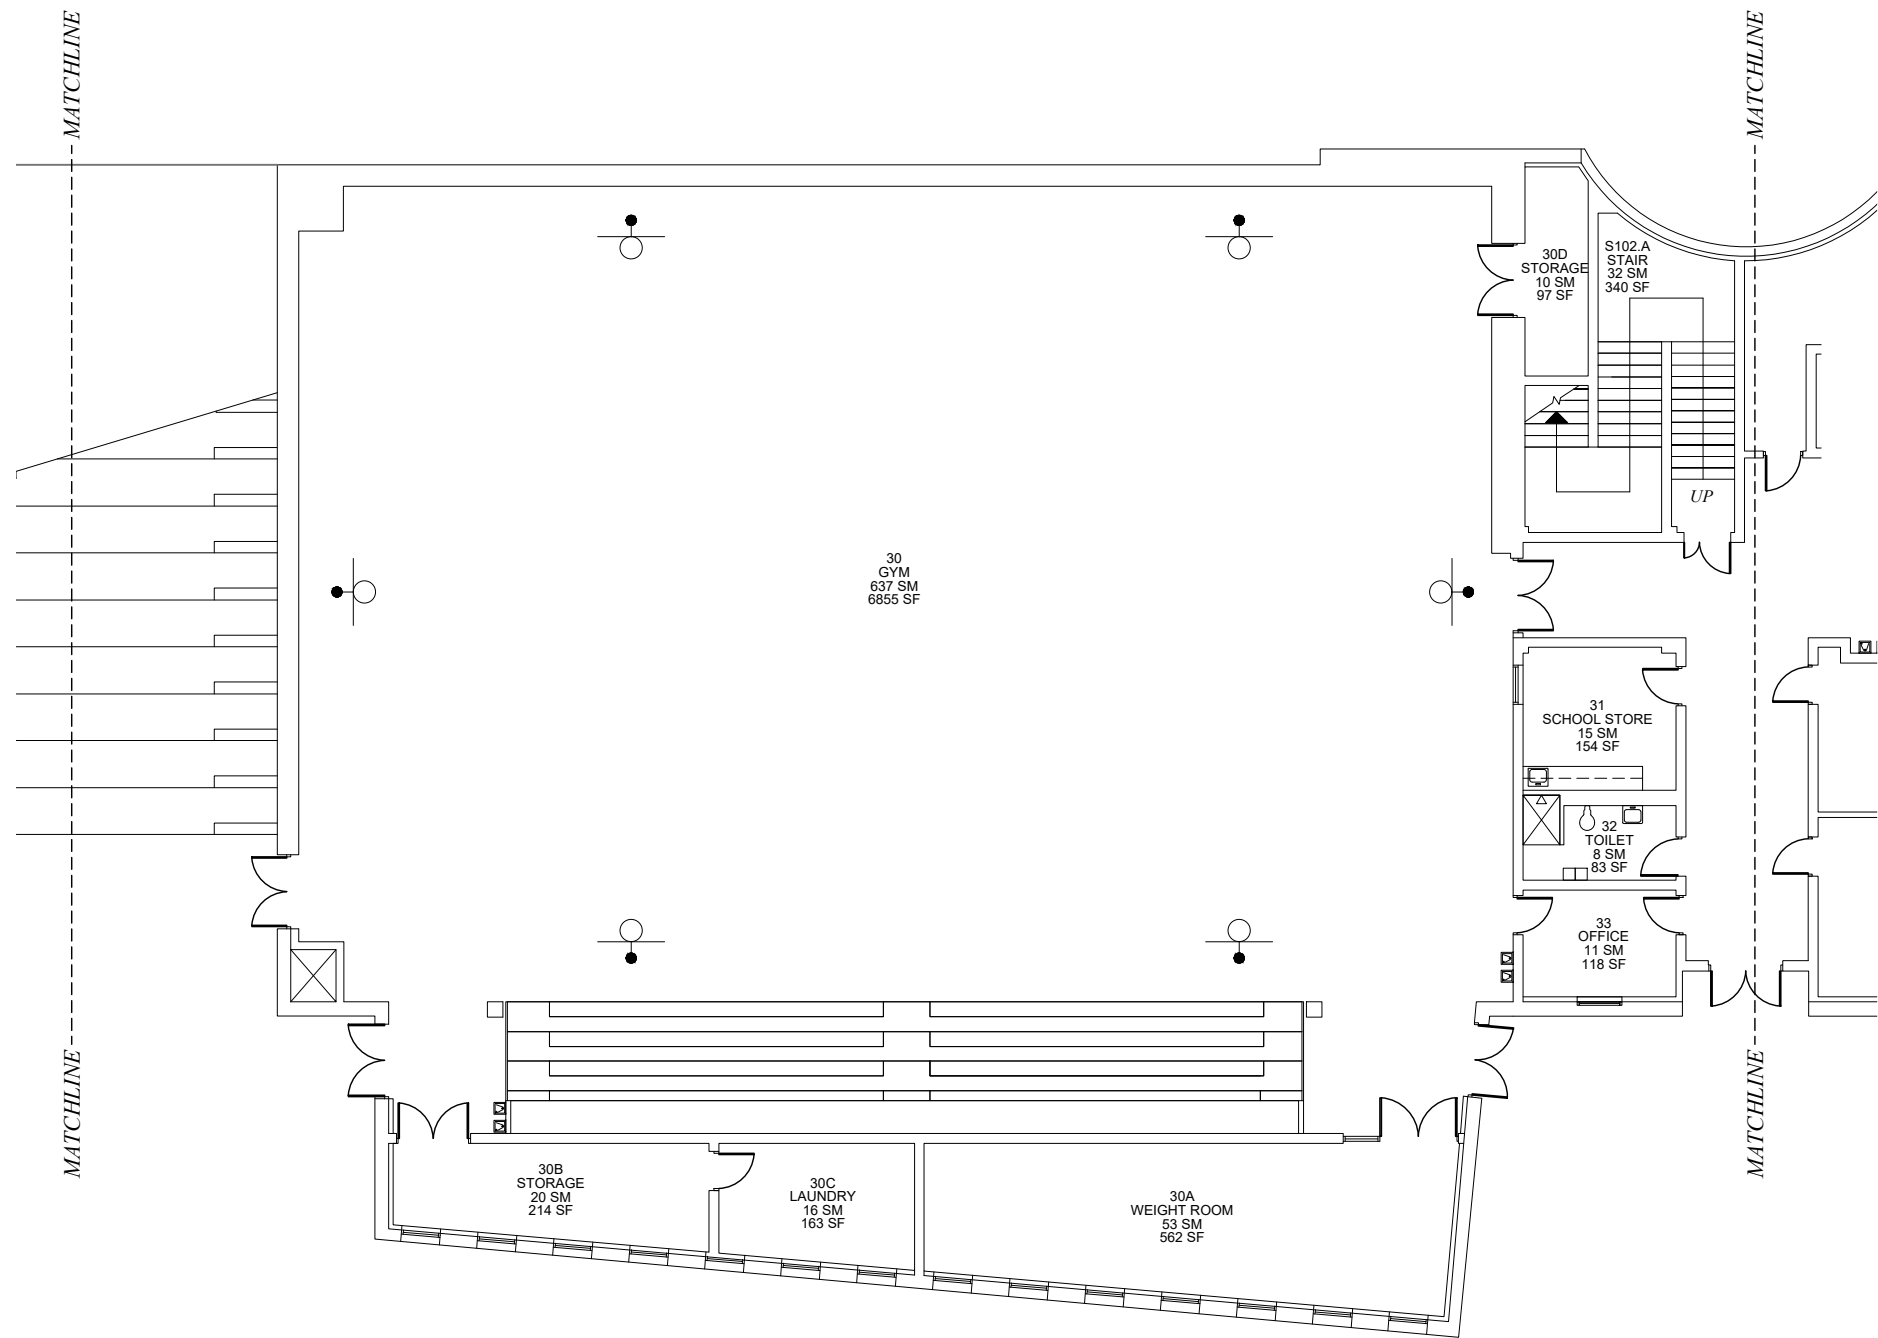

SYMBOL LEGEND	
	DOOR
	DRINKING FOUNTAIN
	SLIDING DOOR
	LAVATORY
	ACCORDION PARTITION
	SINK
	STACK OR FOLDING PARTITION
	TOILET
	WINDOW/GLAZING
	URINAL
	HIGH WINDOW
	LOCKER
	SKYLIGHT
	LAN DISTRIBUTION FRAME
	STOOP/STEP UP
	VENT HOOD
	STAIR
	WALL SHELVING
	RAMP
	UPPER CABINET
	ACCESS LADDER
	BASE CABINET
	COLD STORAGE
	TEACHER CABINET
	AREA CALCULATED @ 50 %
	MATCHLINE
	SLOPING ROOF
	FLAT ROOF

TITLEBLOCK LEGEND	
SHEET NAME:	BLDG #_FLOOR # (# IN SERIES)

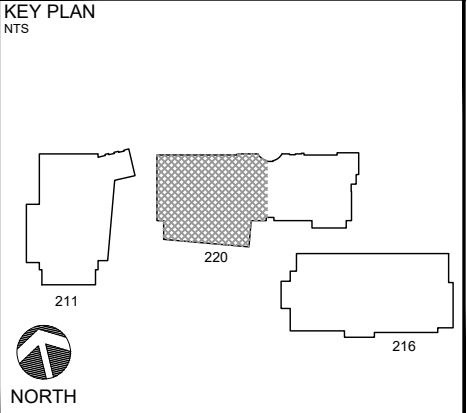


Updated By:	FUS Review:	100% Submittal Date:
AA	MRS	01 MAY 2020
0 2 4 8 16 FT		

dodea
DEPARTMENT OF DEFENSE EDUCATION ACTIVITY
FACILITY UTILIZATION SURVEY


**SIGONELLA
MIDDLE / HIGH SCHOOL**
BUILDING NUMBER: 220
COUNTRY: ITALY
INSTALLATION: NAS SIGONELLA
SITE: NAS1 SUPPORT AREA
REGION-DISTRICT: DODEA EUROPE SOUTH

DoDAAC Number:	Floor:	Survey Date:
HE5515	LEVEL A	JANUARY 2020
Sheet Name:	Sheet Seq:	
220_A (1)	17 of 24	

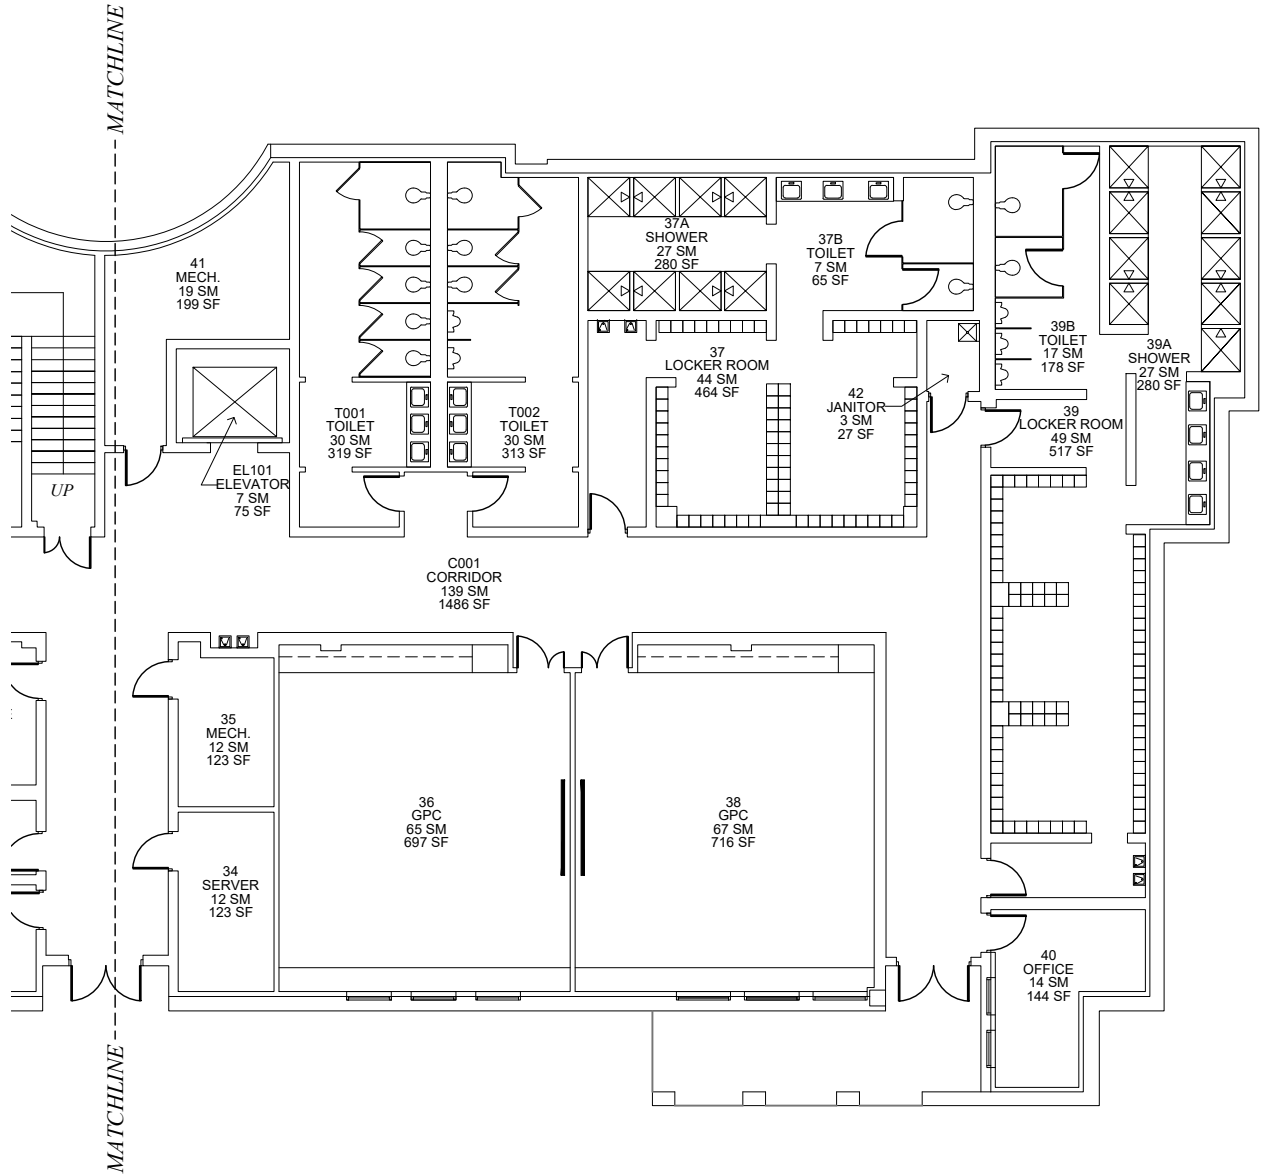


SYMBOL LEGEND	
	DOOR
	SLIDING DOOR
	ACCORDION PARTITION
	STACK OR FOLDING PARTITION
	WINDOW/GLAZING
	HIGH WINDOW
	SKYLIGHT
	STOOP/STEP UP
	STAIR
	RAMP
	ACCESS LADDER
	COLD STORAGE
	AREA CALCULATED @ 50 %
	SLOPING ROOF
	DRINKING FOUNTAIN
	LAVATORY
	SINK
	TOILET
	URINAL
	LOCKER
	LAN DISTRIBUTION FRAME
	VENT HOOD
	WALL SHELVING
	UPPER CABINET
	BASE CABINET
	TEACHER CABINET
	MATCHLINE

TITLEBLOCK LEGEND	
SHEET NAME:	BLDG #_FLOOR # (# IN SERIES)

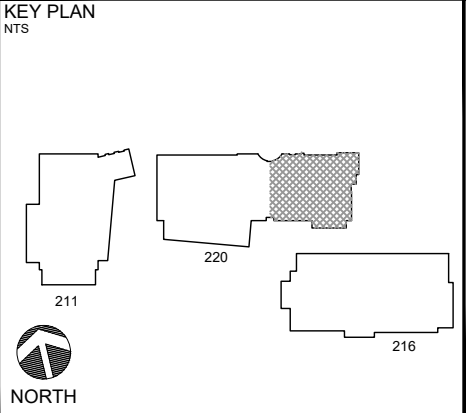


Updated By:	FUS Review:	100% Submittal Date:
AA	MRS	01 MAY 2020
0 2 4 8 16 FT		
 DEPARTMENT OF DEFENSE EDUCATION ACTIVITY		
FACILITY UTILIZATION SURVEY		
SIGONELLA MIDDLE / HIGH SCHOOL BUILDING NUMBER: 220 COUNTRY: ITALY INSTALLATION: NAS SIGONELLA SITE: NAS1 SUPPORT AREA REGION-DISTRICT: DODEA EUROPE SOUTH		
DoDAAC Number:	Floor:	Survey Date:
HE5515	LEVEL A	JANUARY 2020
Sheet Name:	Sheet Seq:	
220_A (2)	18 of 24	

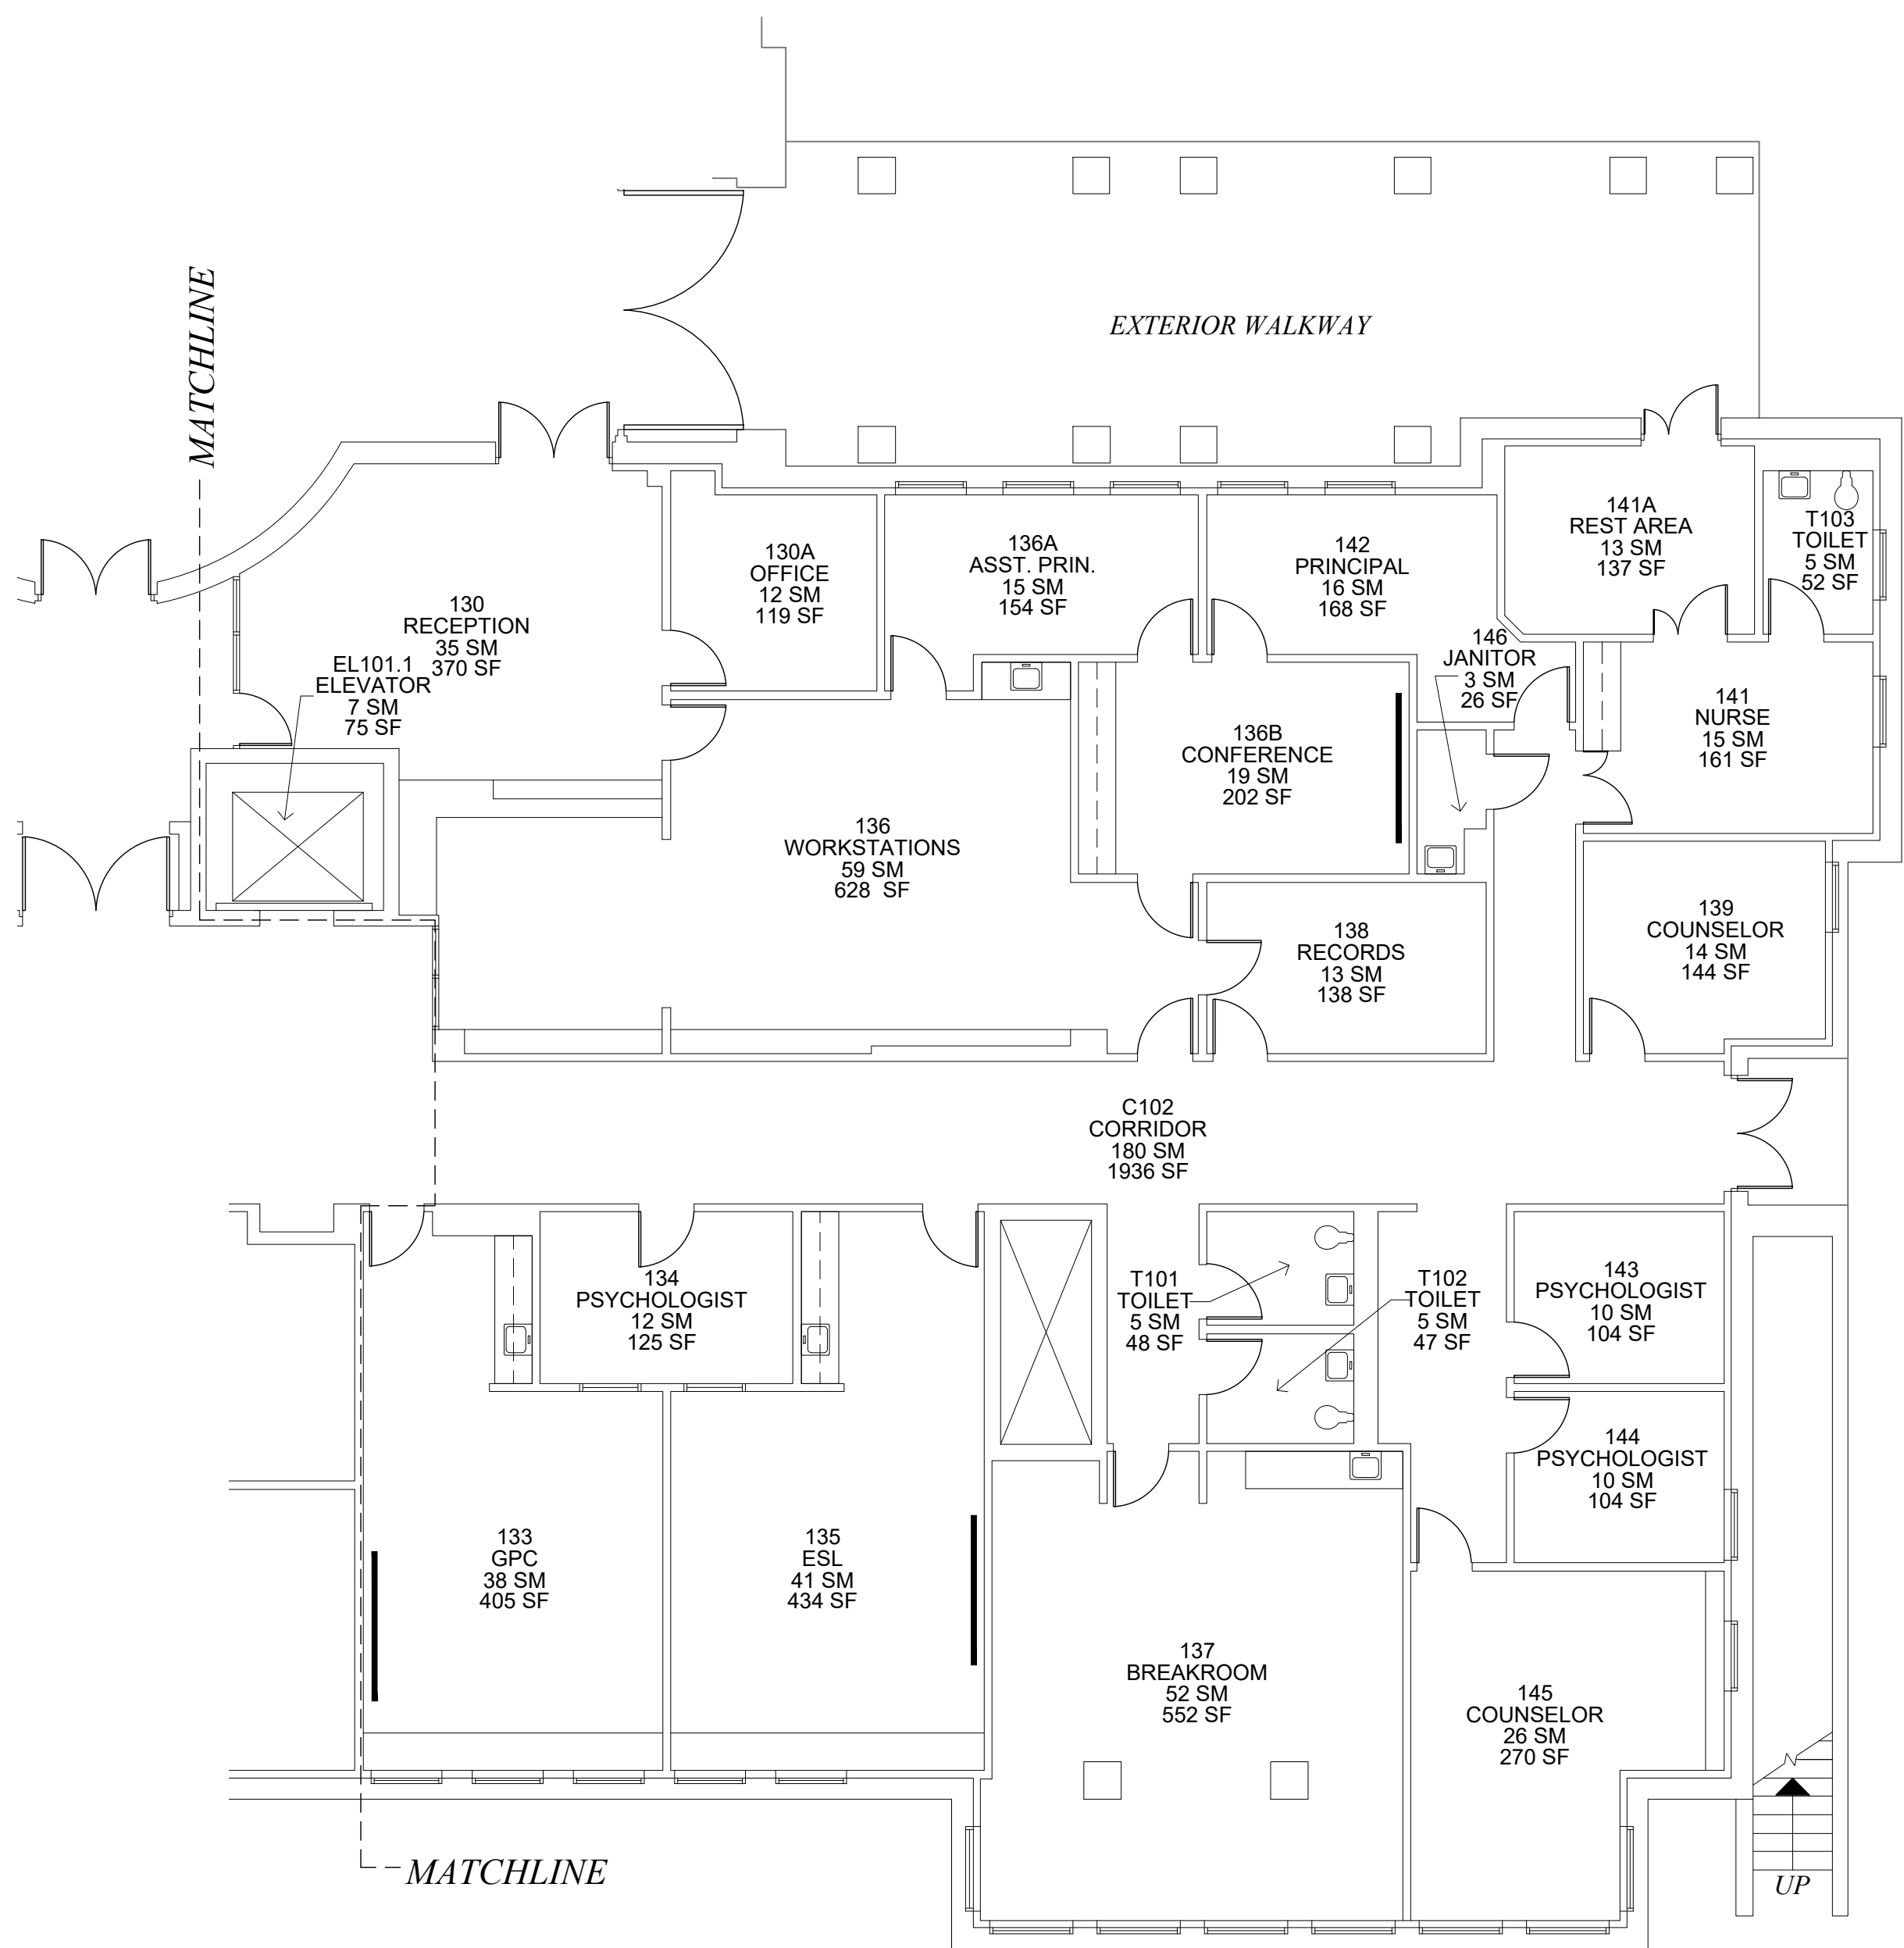

SYMBOL LEGEND	
	DOOR
	DRINKING FOUNTAIN
	SLIDING DOOR
	LAVATORY
	ACCORDION PARTITION
	SINK
	STACK OR FOLDING PARTITION
	TOILET
	WINDOW/GLAZING
	URINAL
	HIGH WINDOW
	LOCKER
	SKYLIGHT
	LAN DISTRIBUTION FRAME
	STOOP/STEP UP
	VENT HOOD
	STAIR
	WALL SHELVING
	RAMP
	UPPER CABINET
	ACCESS LADDER
	BASE CABINET
	COLD STORAGE
	TEACHER CABINET
	AREA CALCULATED @ 50 %
	MATCHLINE
	SLOPING ROOF
	FLAT ROOF

TITLEBLOCK LEGEND	
SHEET NAME:	BLDG #_FLOOR # (# IN SERIES)

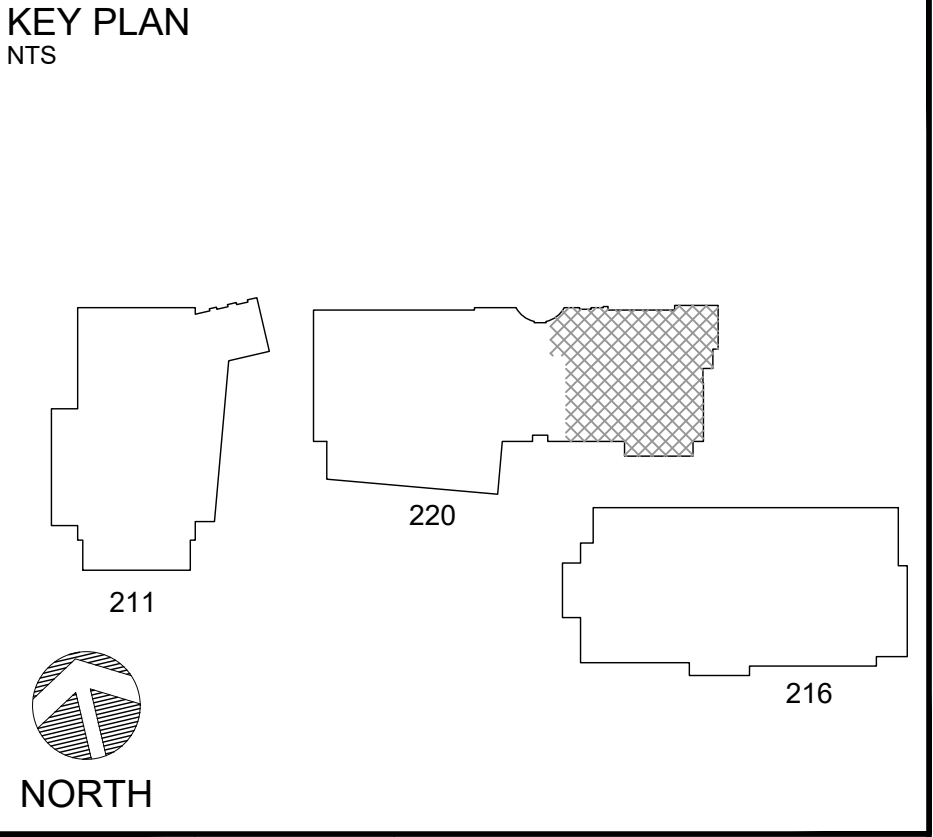


Updated By:	FUS Review:	100% Submittal Date:
AA	MRS	01 MAY 2020

0 2 4 8 16 FT


dodea
DEPARTMENT OF DEFENSE EDUCATION ACTIVITY
FACILITY UTILIZATION SURVEY

SIGONELLA MIDDLE / HIGH SCHOOL		
BUILDING NUMBER: 220		
COUNTRY: ITALY		
INSTALLATION: NAS SIGONELLA		
SITE: NAS1 SUPPORT AREA		
REGION-DISTRICT: DODEA EUROPE SOUTH		
DoDAAC Number:	Floor:	Survey Date:
HE5515	LEVEL 1	JANUARY 2020
Sheet Name:	Sheet Seq:	
220_1 (1)		19 of 24

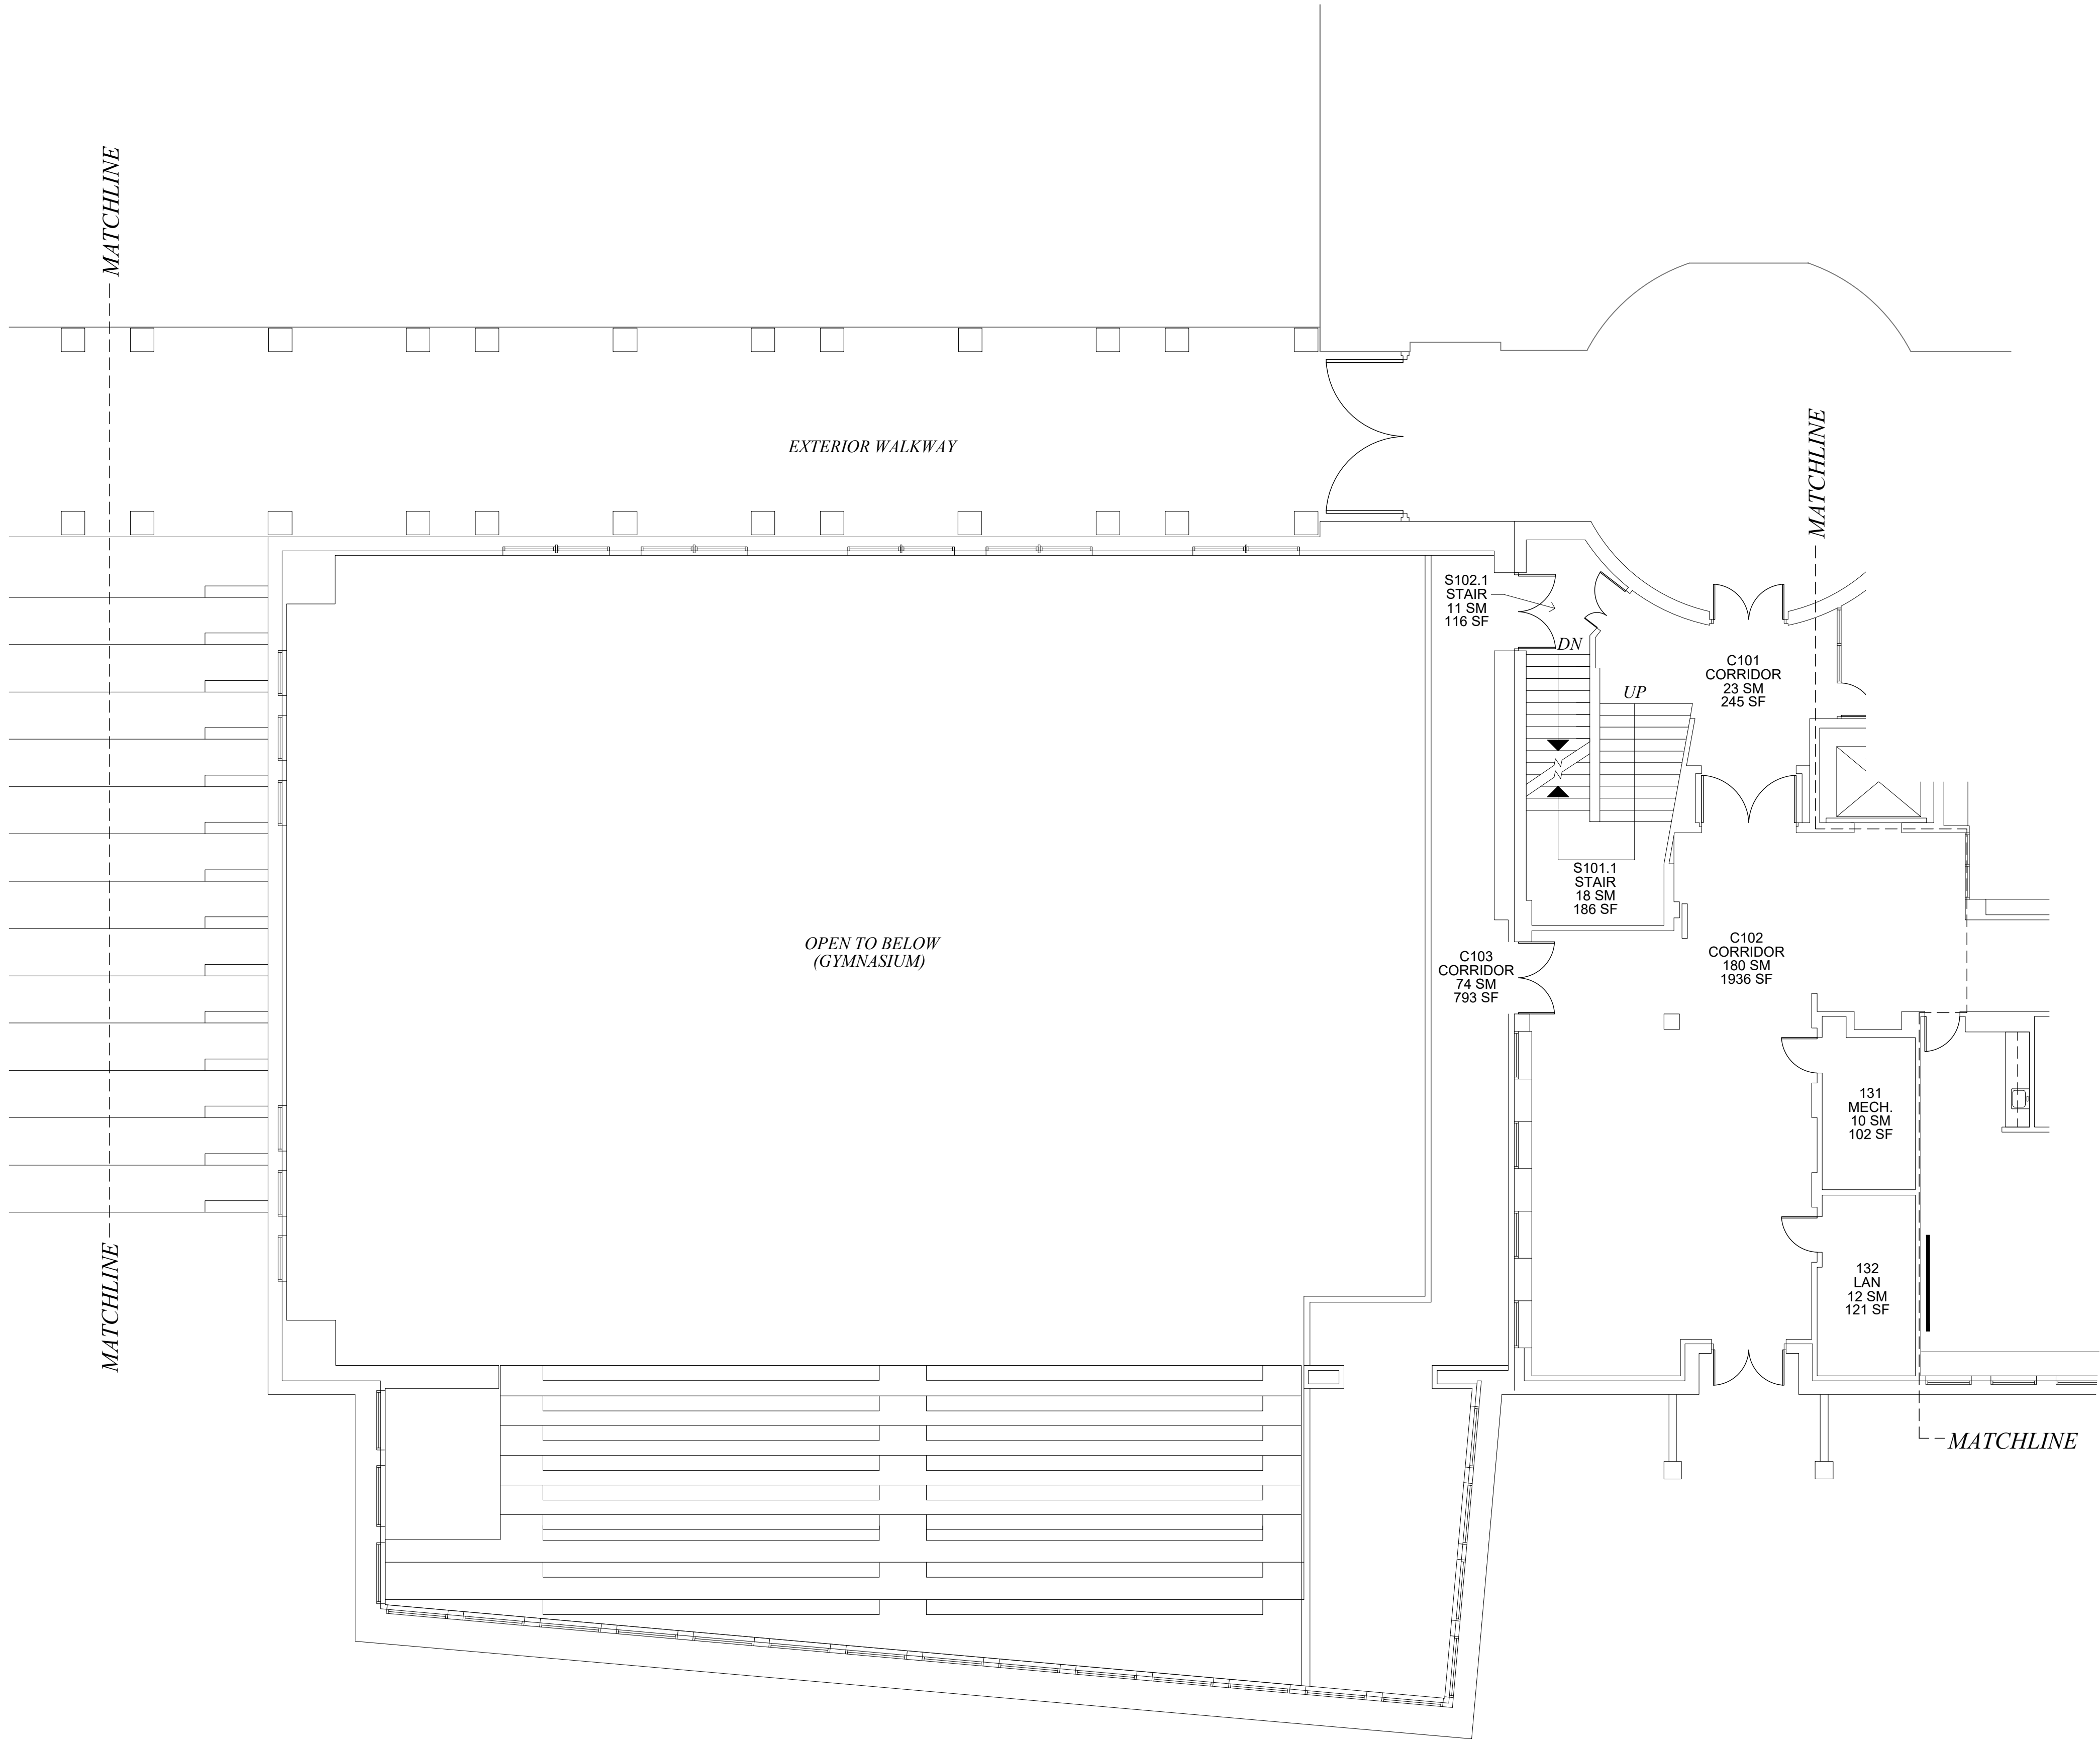

SYMBOL LEGEND			
	DOOR		DRINKING FOUNTAIN
	SLIDING DOOR		LAVATORY
	ACCORDION PARTITION		SINK
	STACK OR FOLDING PARTITION		TOILET
	WINDOW/GLAZING		URINAL
	HIGH WINDOW		LOCKER
	SKYLIGHT		LAN DISTRIBUTION FRAME
	STOOP/STEP UP		VENT HOOD
	STAIR		WALL SHELVING
	RAMP		UPPER CABINET
	ACCESS LADDER		BASE CABINET
	COLD STORAGE		TEACHER CABINET
	AREA CALCULATED @ 50 %		MATCHLINE
	SLOPING ROOF		FLAT ROOF

TITLEBLOCK LEGEND	
SHEET NAME:	BLDG #_FLOOR # (# IN SERIES)

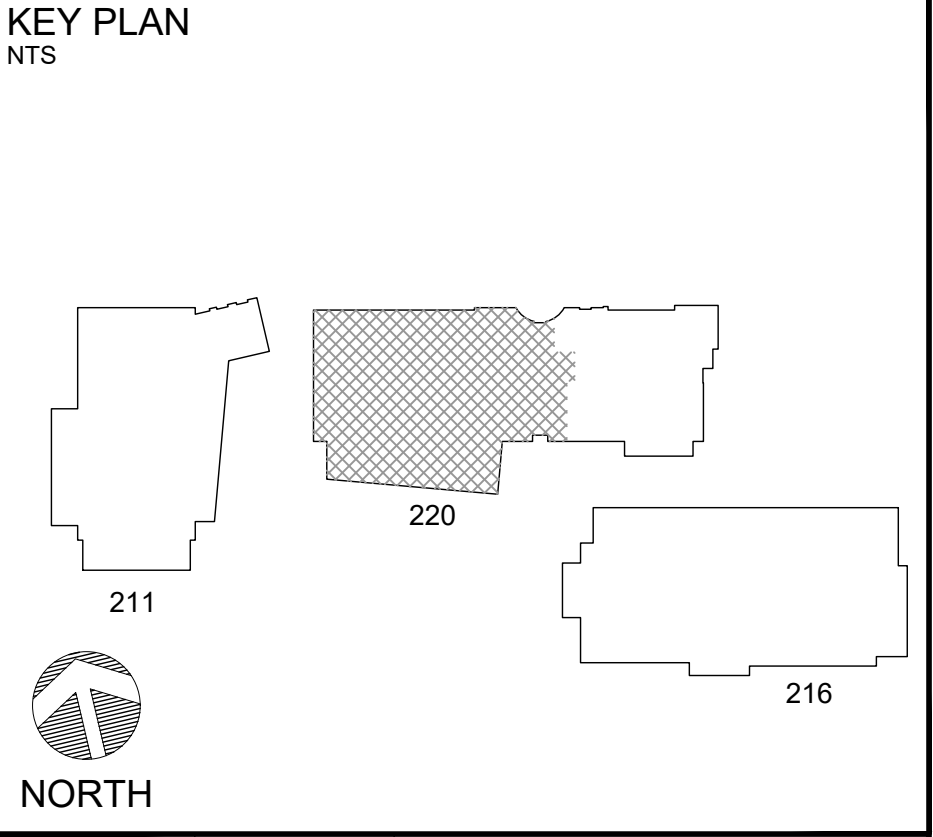


Updated By:	FUS Review:	100% Submittal Date:
AA	MRS	01 MAY 2020
0 2 4 8 16 FT		

DEPARTMENT OF DEFENSE EDUCATION ACTIVITY


FACILITY UTILIZATION SURVEY

SIGONELLA MIDDLE / HIGH SCHOOL		
BUILDING NUMBER: 220		
COUNTRY: ITALY		
INSTALLATION: NAS SIGONELLA		
SITE: NAS1 SUPPORT AREA		
REGION-DISTRICT: DODEA EUROPE SOUTH		
DoDAAC Number:	Floor:	Survey Date:
HE5515	LEVEL 1	JANUARY 2020
Sheet Name:	Sheet Seq:	
220_1 (2)		20 of 24

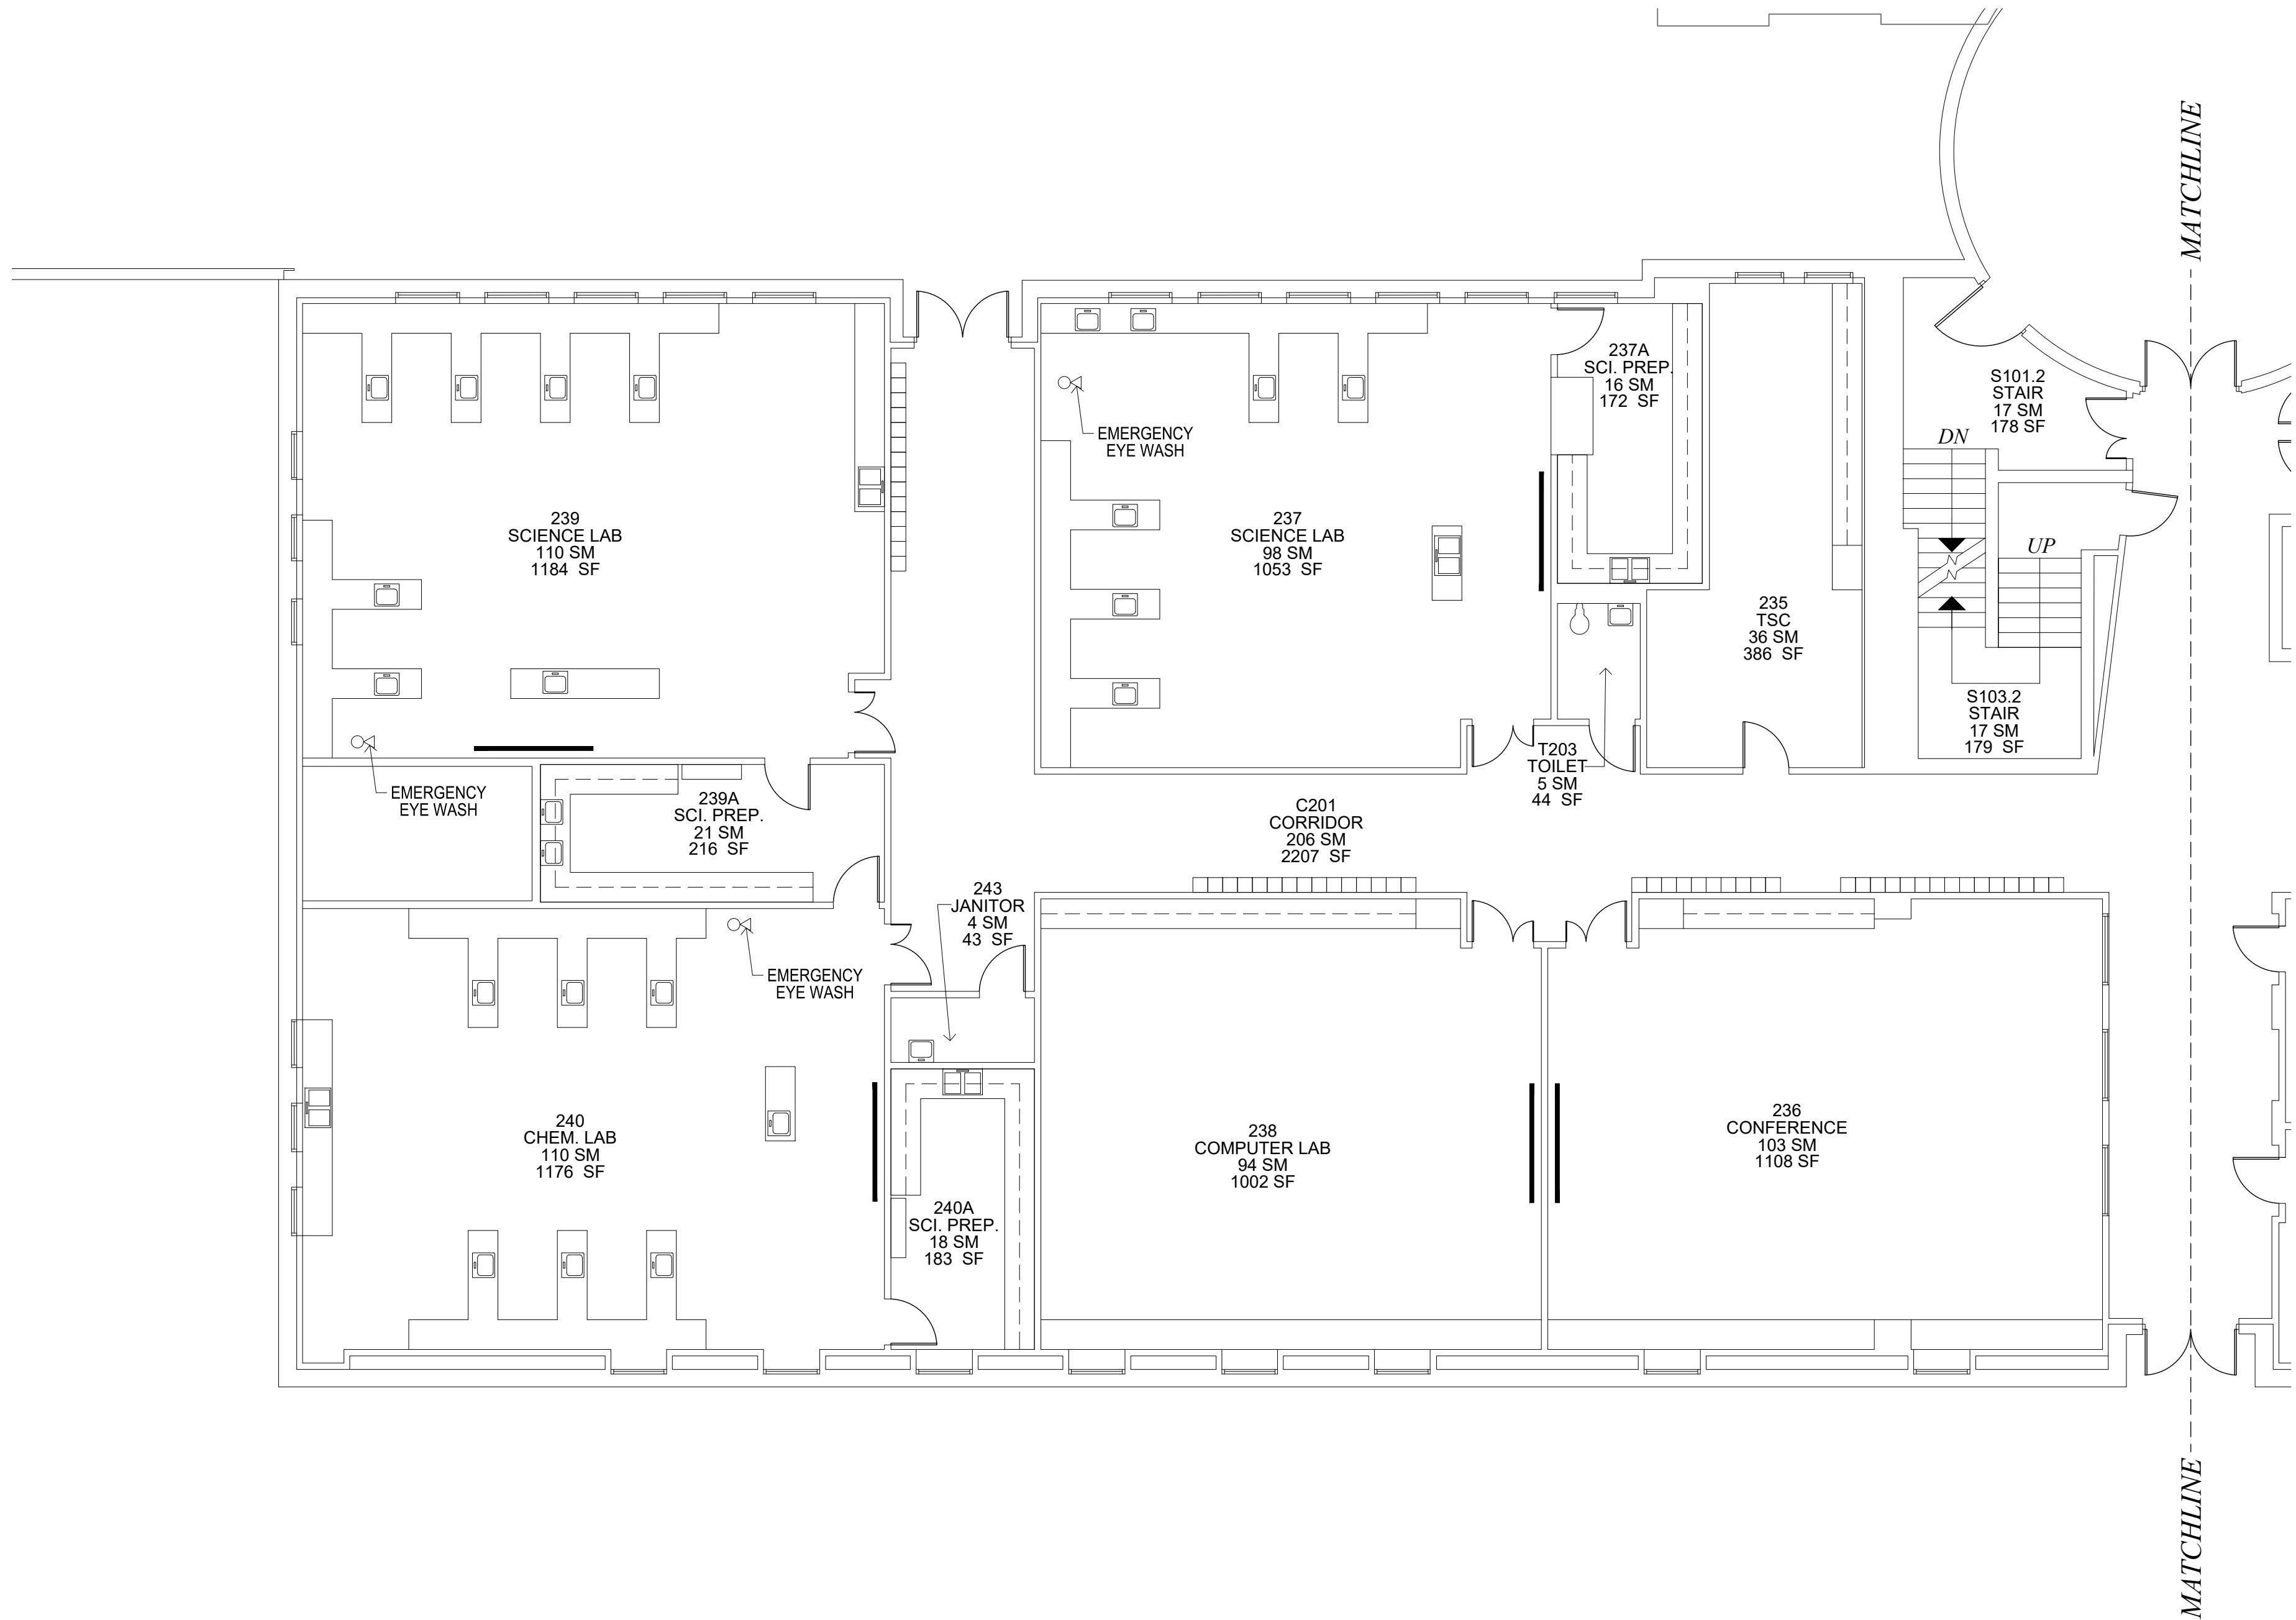

SYMBOL LEGEND			
	DOOR		DRINKING FOUNTAIN
	SLIDING DOOR		LAVATORY
	ACCORDION PARTITION		SINK
	STACK OR FOLDING PARTITION		TOILET
	WINDOW/GLAZING		URINAL
	HIGH WINDOW		LOCKER
	SKYLIGHT		LAN DISTRIBUTION FRAME
	STOOP/STEP UP		VENT HOOD
	STAIR		WALL SHELVING
	RAMP		UPPER CABINET
	ACCESS LADDER		BASE CABINET
	COLD STORAGE		TEACHER CABINET
	AREA CALCULATED @ 50 %		MATCHLINE
	SLOPING ROOF		FLAT ROOF

TITLEBLOCK LEGEND	
SHEET NAME:	BLDG #_FLOOR # (# IN SERIES)

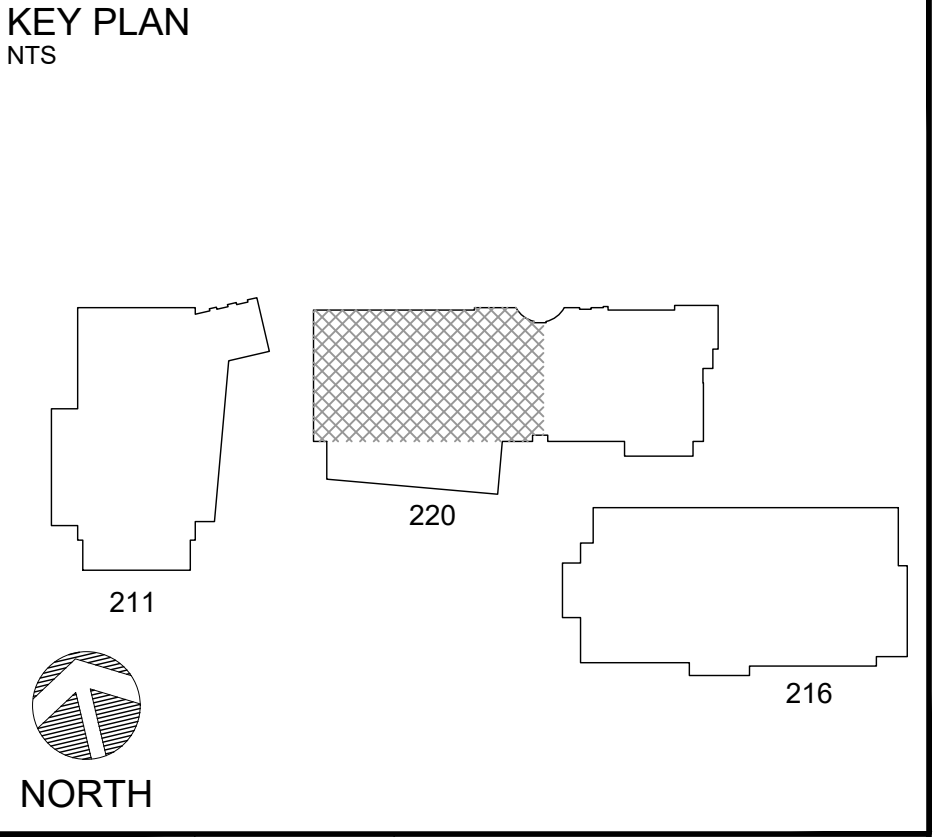


Updated By:	FUS Review:	100% Submittal Date:
AA	MRS	01 MAY 2020



DEPARTMENT OF DEFENSE EDUCATION ACTIVITY

FACILITY UTILIZATION SURVEY

SIGONELLA MIDDLE / HIGH SCHOOL		
BUILDING NUMBER: 220		
COUNTRY: ITALY		
INSTALLATION: NAS SIGONELLA		
SITE: NAS1 SUPPORT AREA		
REGION-DISTRICT: DODEA EUROPE SOUTH		
DoDAAC Number:	Floor:	Survey Date:
HE5515	LEVEL 2	JANUARY 2020
Sheet Name:	Sheet Seq:	
220_2 (1)		21 of 24

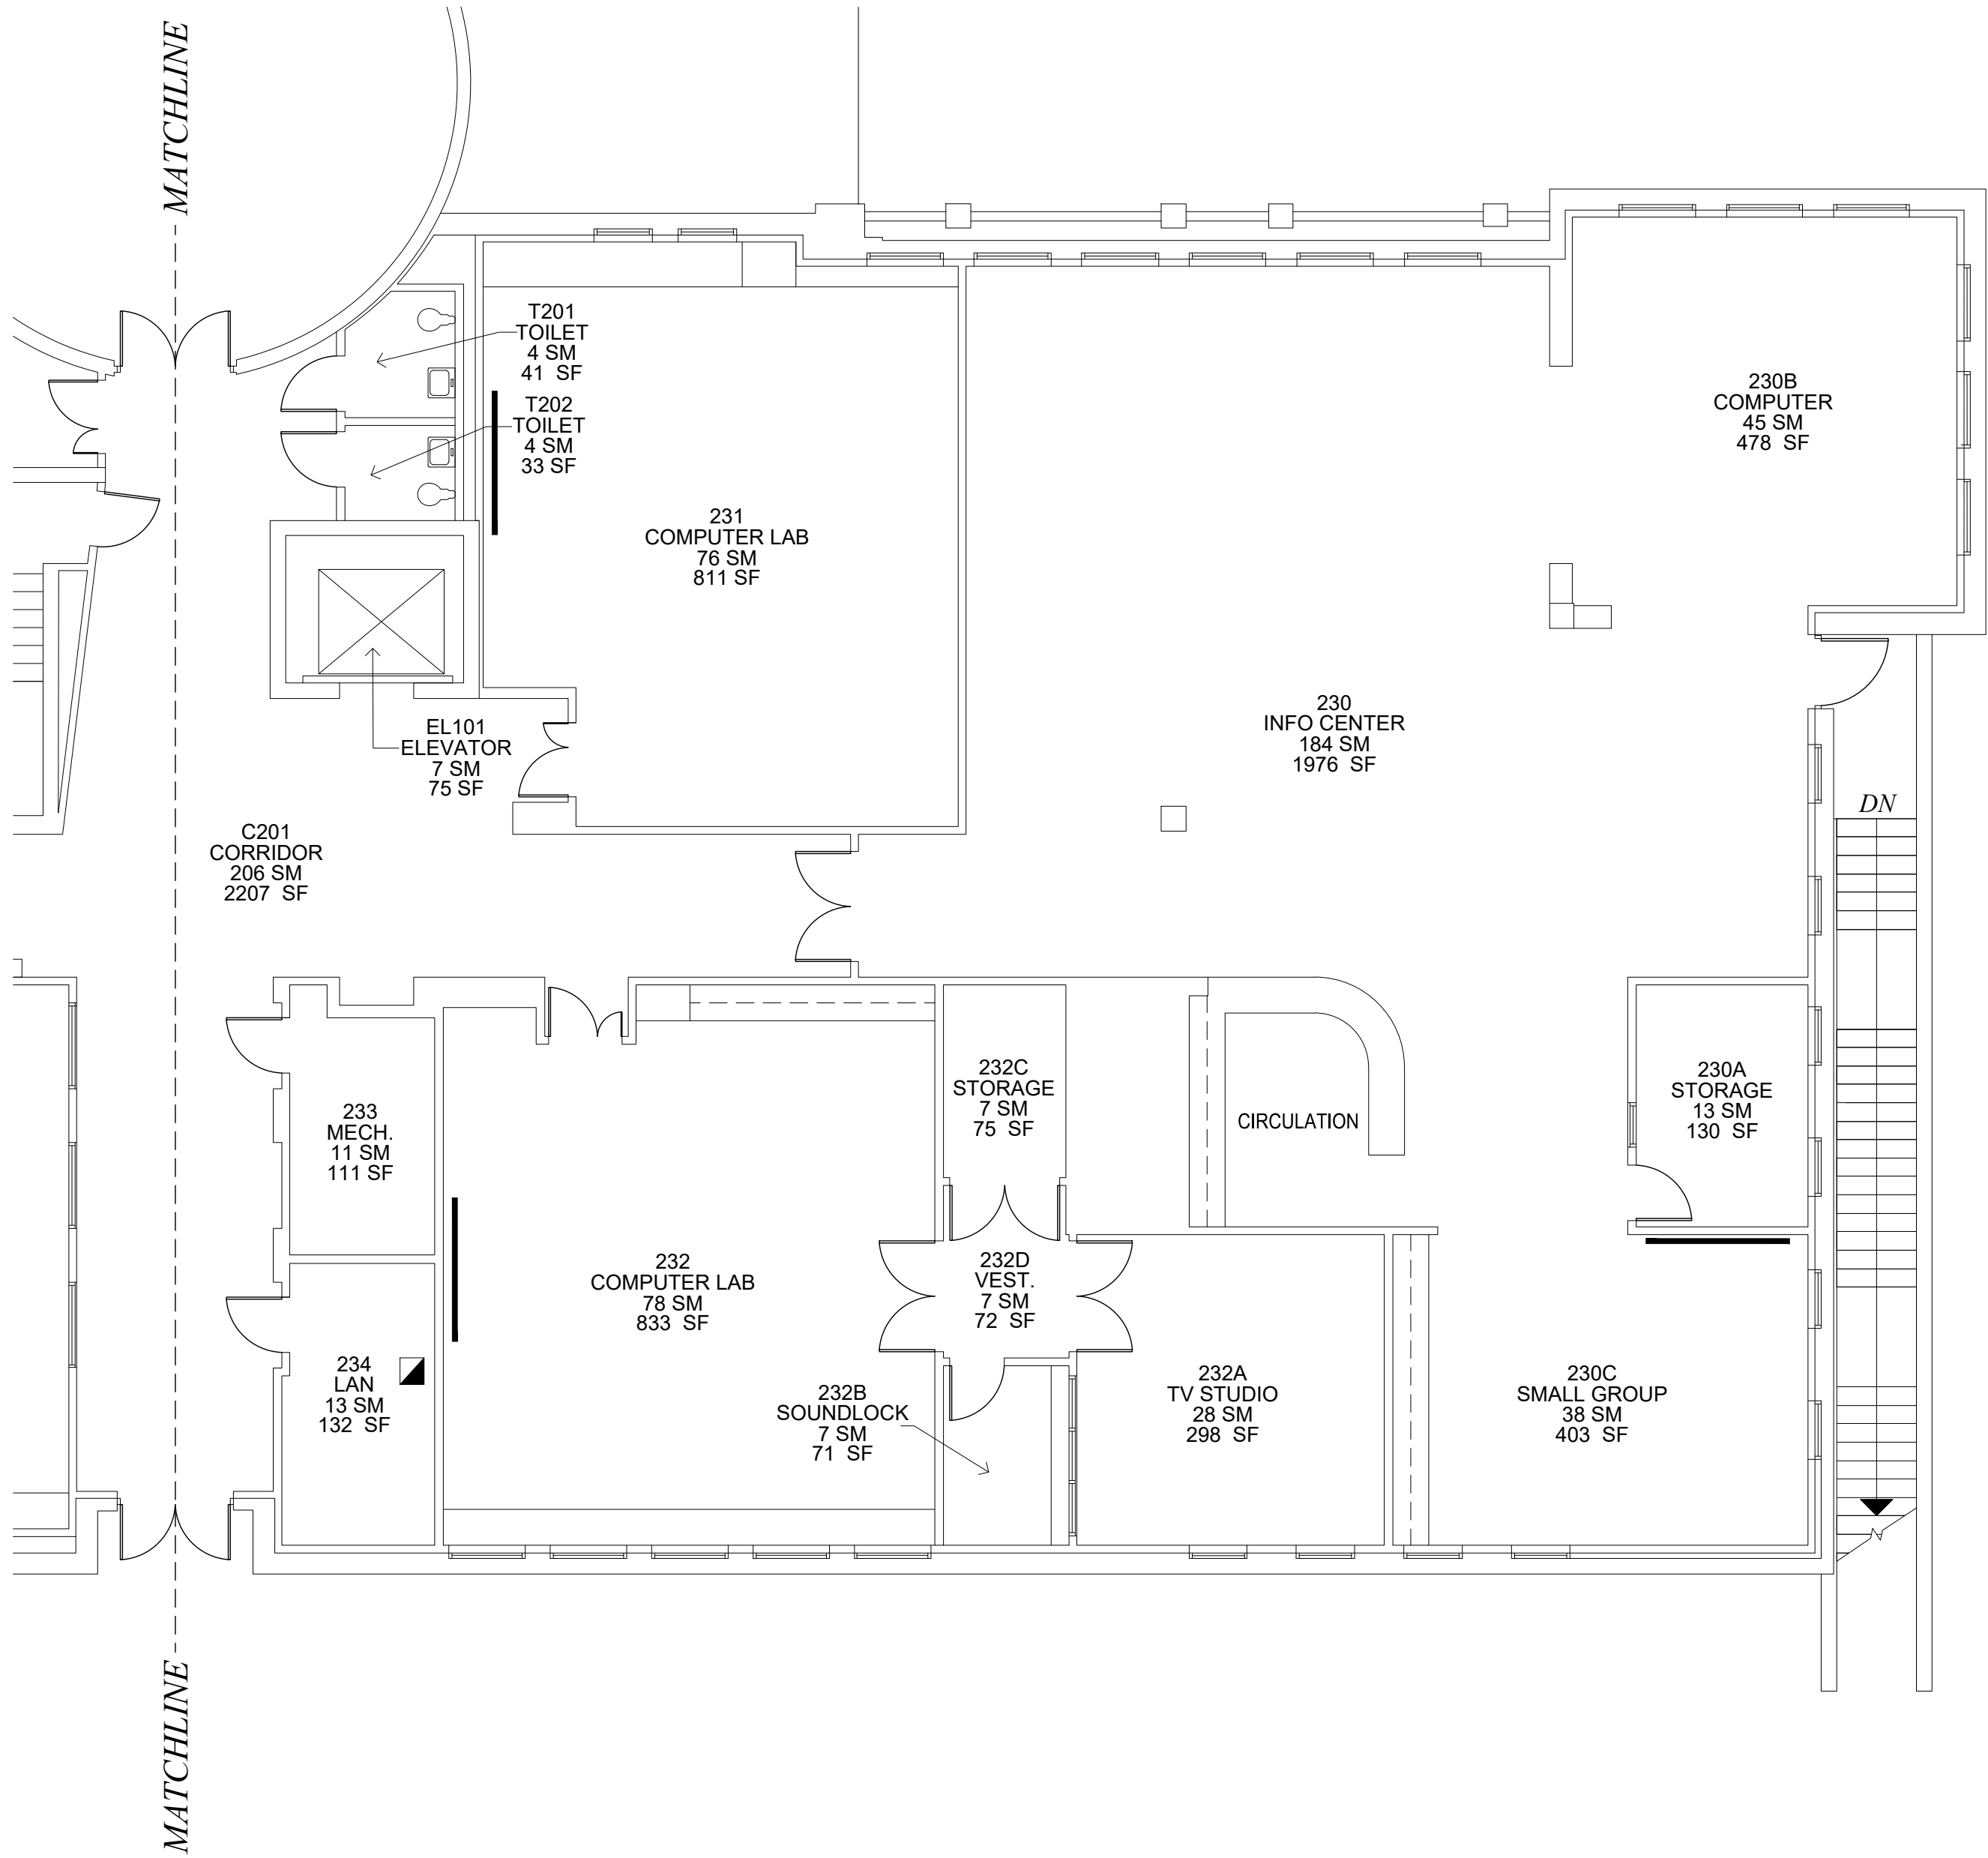

SYMBOL LEGEND	
	DOOR
	DRINKING FOUNTAIN
	SLIDING DOOR
	LAVATORY
	ACCORDION PARTITION
	SINK
	STACK OR FOLDING PARTITION
	TOILET
	WINDOW/GLAZING
	URINAL
	HIGH WINDOW
	LOCKER
	SKYLIGHT
	LAN DISTRIBUTION FRAME
	STOOP/STEP UP
	VENT HOOD
	STAIR
	WALL SHELVING
	RAMP
	UPPER CABINET
	ACCESS LADDER
	BASE CABINET
	COLD STORAGE
	TEACHER CABINET
	AREA CALCULATED @ 50 %
	MATCHLINE
	SLOPING ROOF
	FLAT ROOF

TITLEBLOCK LEGEND	
SHEET NAME:	BLDG #_FLOOR # (# IN SERIES)

KEY PLAN
NTS


Updated By:	FUS Review:	100% Submittal Date:
AA	MRS	01 MAY 2020

FACILITY UTILIZATION SURVEY

SIGONELLA
MIDDLE / HIGH SCHOOL


BUILDING NUMBER: 220
COUNTRY: ITALY
INSTALLATION: NAS SIGONELLA
SITE: NAS1 SUPPORT AREA
REGION-DISTRICT: DODEA EUROPE SOUTH

DoDAAC Number:	Floor:	Survey Date:
HE5515	LEVEL 2	JANUARY 2020
Sheet Name:	Sheet Seq:	
220_2 (2)	22 of 24	

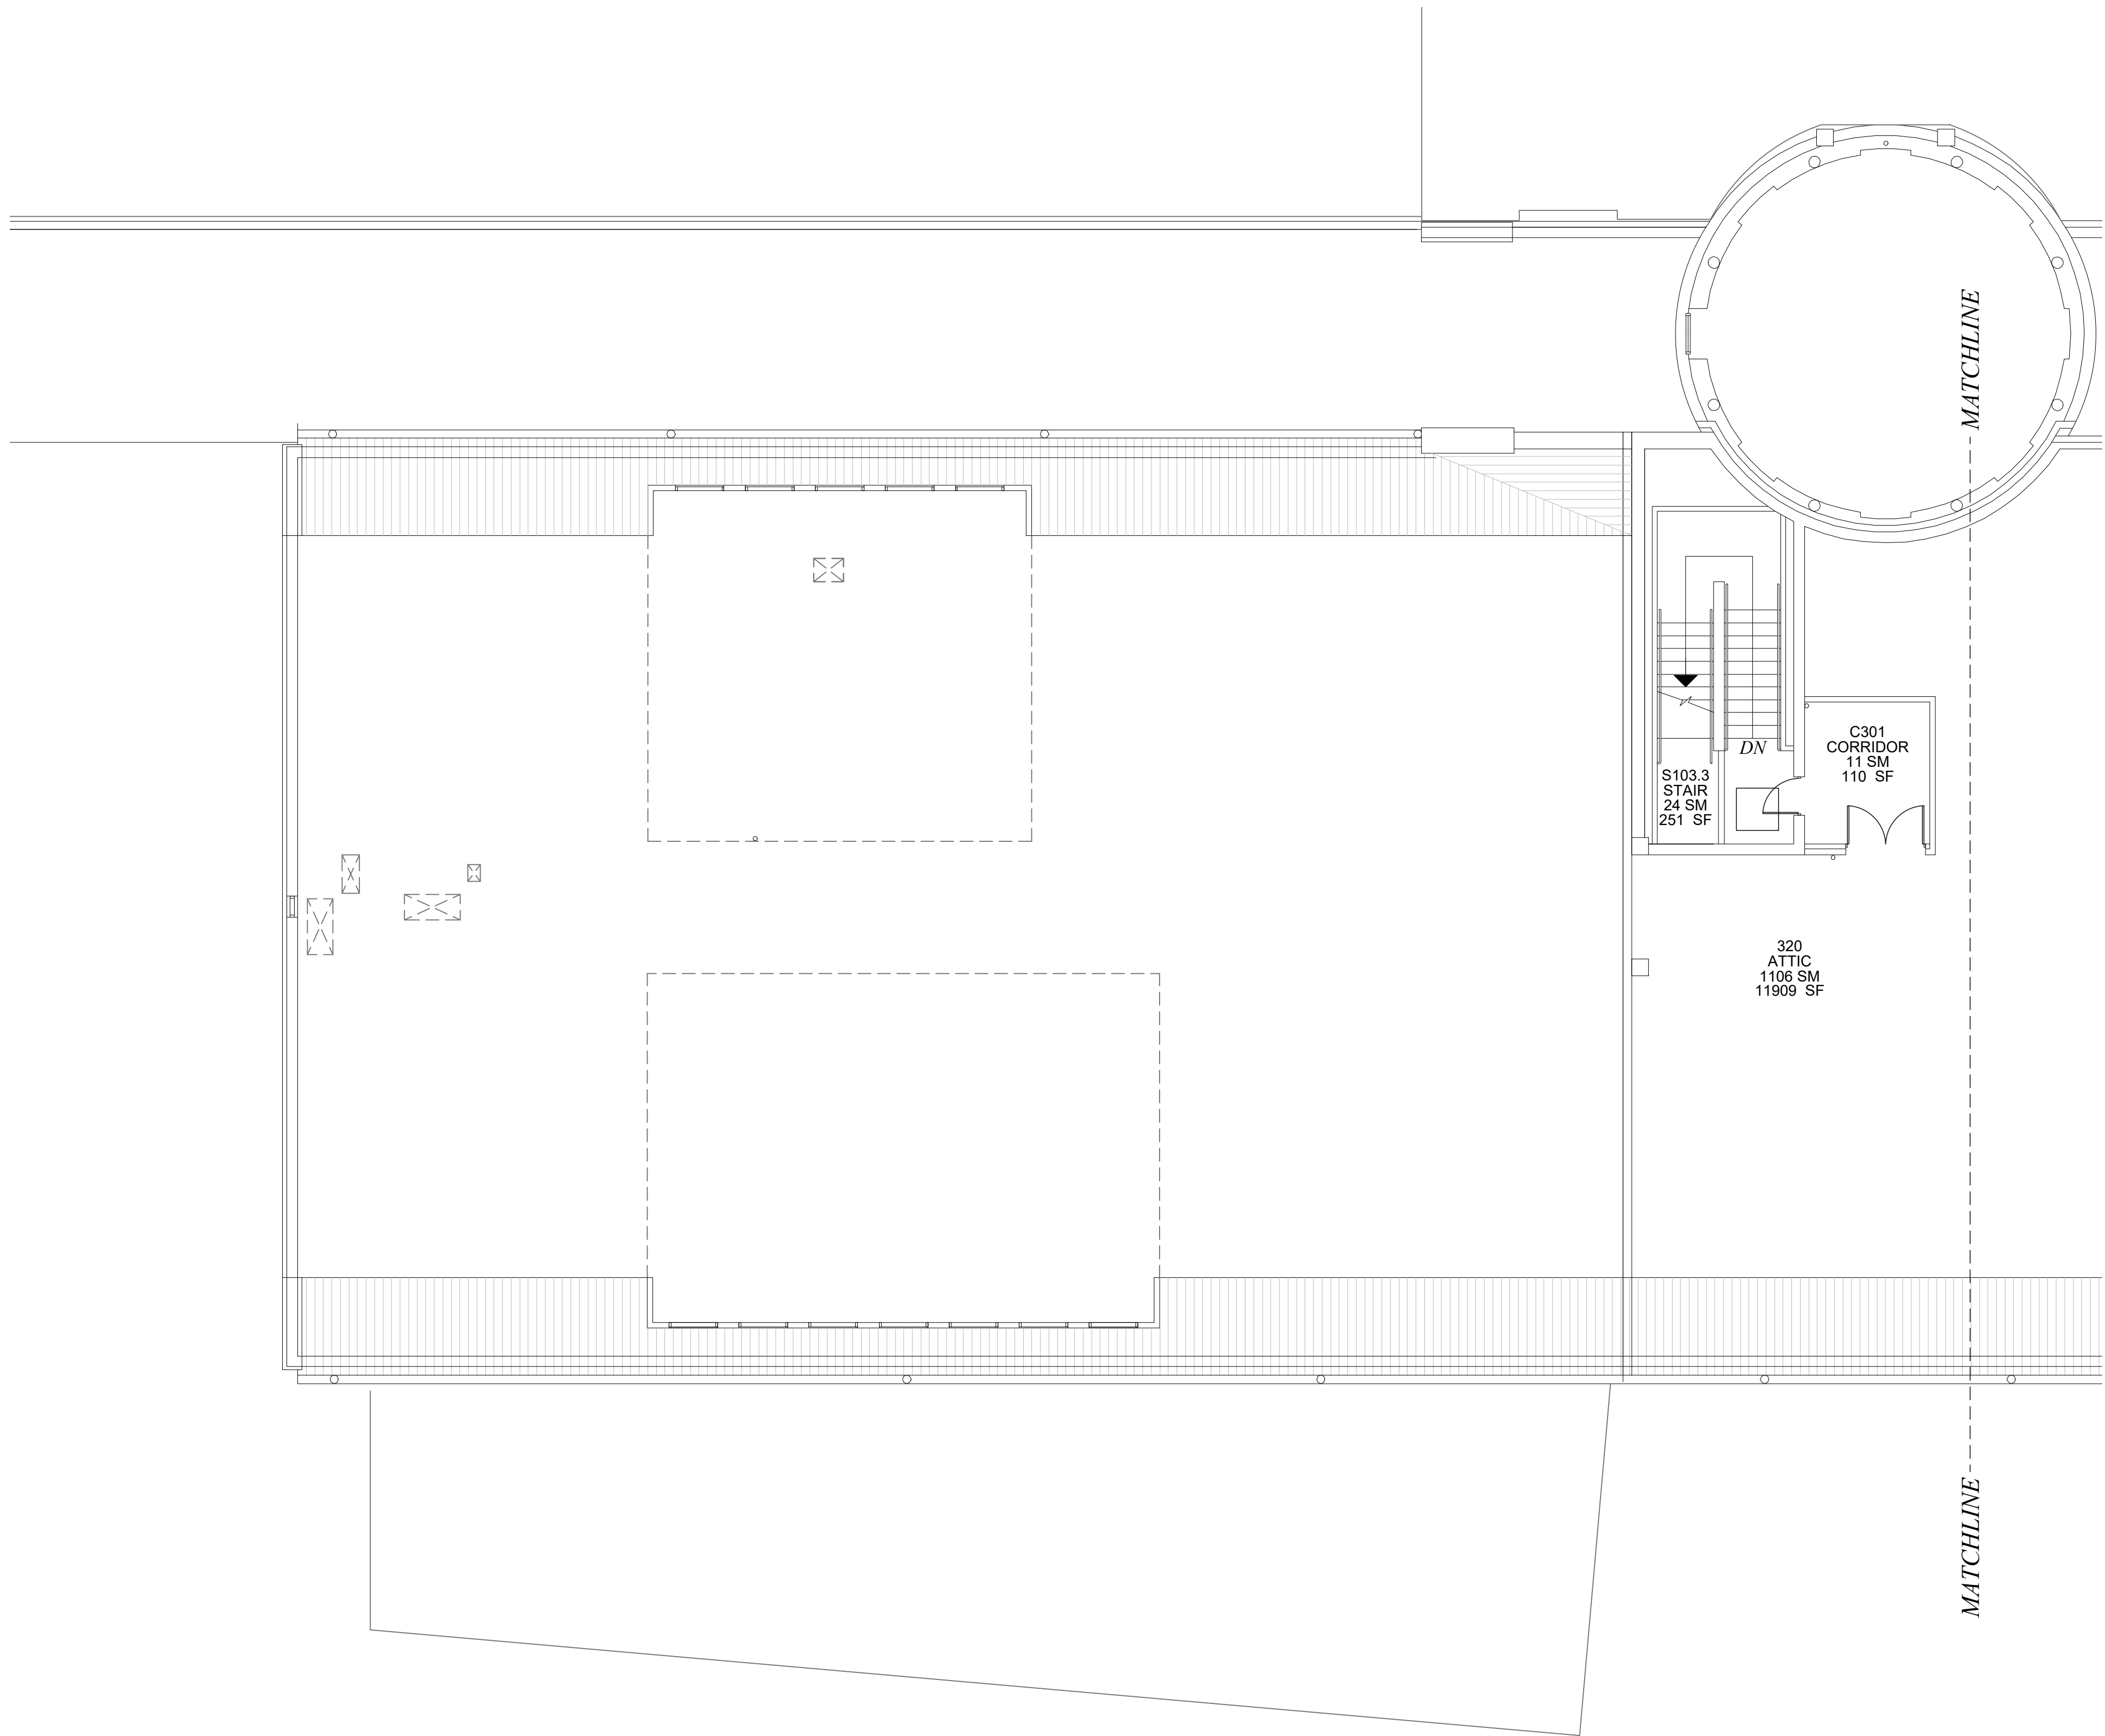

SYMBOL LEGEND	
	DOOR
	DRINKING FOUNTAIN
	SLIDING DOOR
	LAVATORY
	ACCORDION PARTITION
	SINK
	STACK OR FOLDING PARTITION
	TOILET
	WINDOW/GLAZING
	URINAL
	HIGH WINDOW
	LOCKER
	SKYLIGHT
	LAN DISTRIBUTION FRAME
	STOOP/STEP UP
	VENT HOOD
	STAIR
	WALL SHELVING
	RAMP
	UPPER CABINET
	ACCESS LADDER
	BASE CABINET
	COLD STORAGE
	TEACHER CABINET
	AREA CALCULATED @ 50 %
	MATCHLINE
	SLOPING ROOF
	FLAT ROOF

TITLEBLOCK LEGEND	
SHEET NAME:	BLDG #_FLOOR # (# IN SERIES)

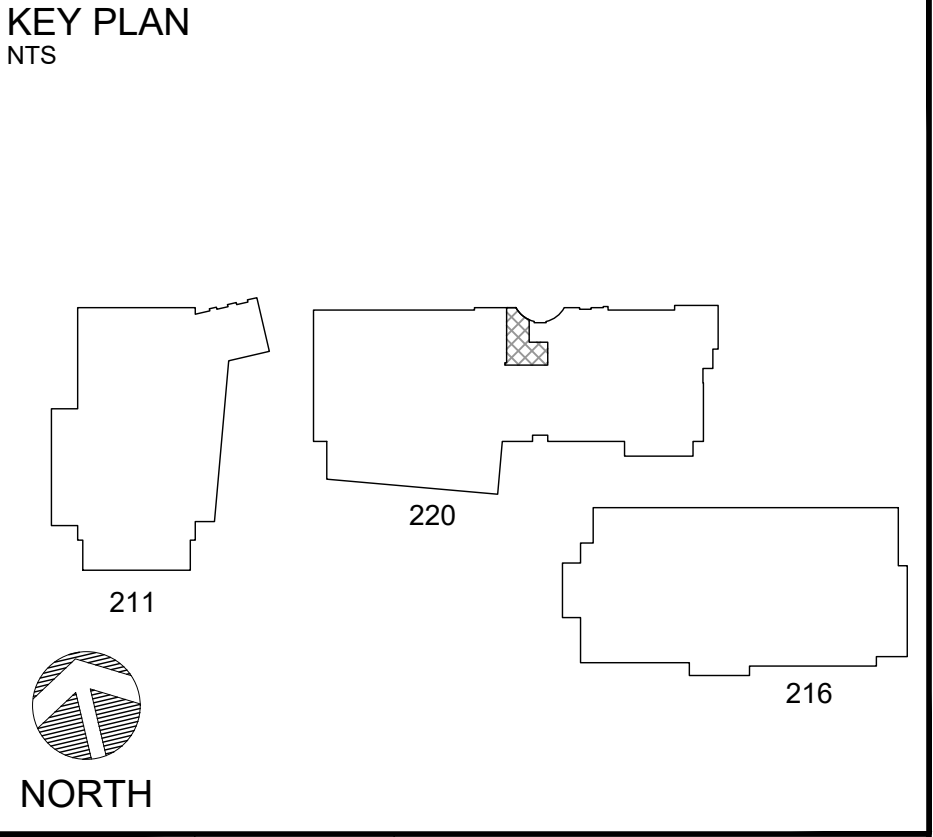


Updated By:	FUS Review:	100% Submittal Date:
AA	MRS	01 MAY 2020
0 2 4 8 16 FT		



DEPARTMENT OF DEFENSE EDUCATION ACTIVITY


FACILITY UTILIZATION SURVEY

SIGONELLA MIDDLE / HIGH SCHOOL		
BUILDING NUMBER: 220		
COUNTRY: ITALY		
INSTALLATION: NAS SIGONELLA		
SITE: NAS1 SUPPORT AREA		
REGION-DISTRICT: DODEA EUROPE SOUTH		
DoDAAC Number:	Floor:	Survey Date:
HE5515	LEVEL 3	JANUARY 2020
Sheet Name:	Sheet Seq:	
220_3 (1)	23 of 24	

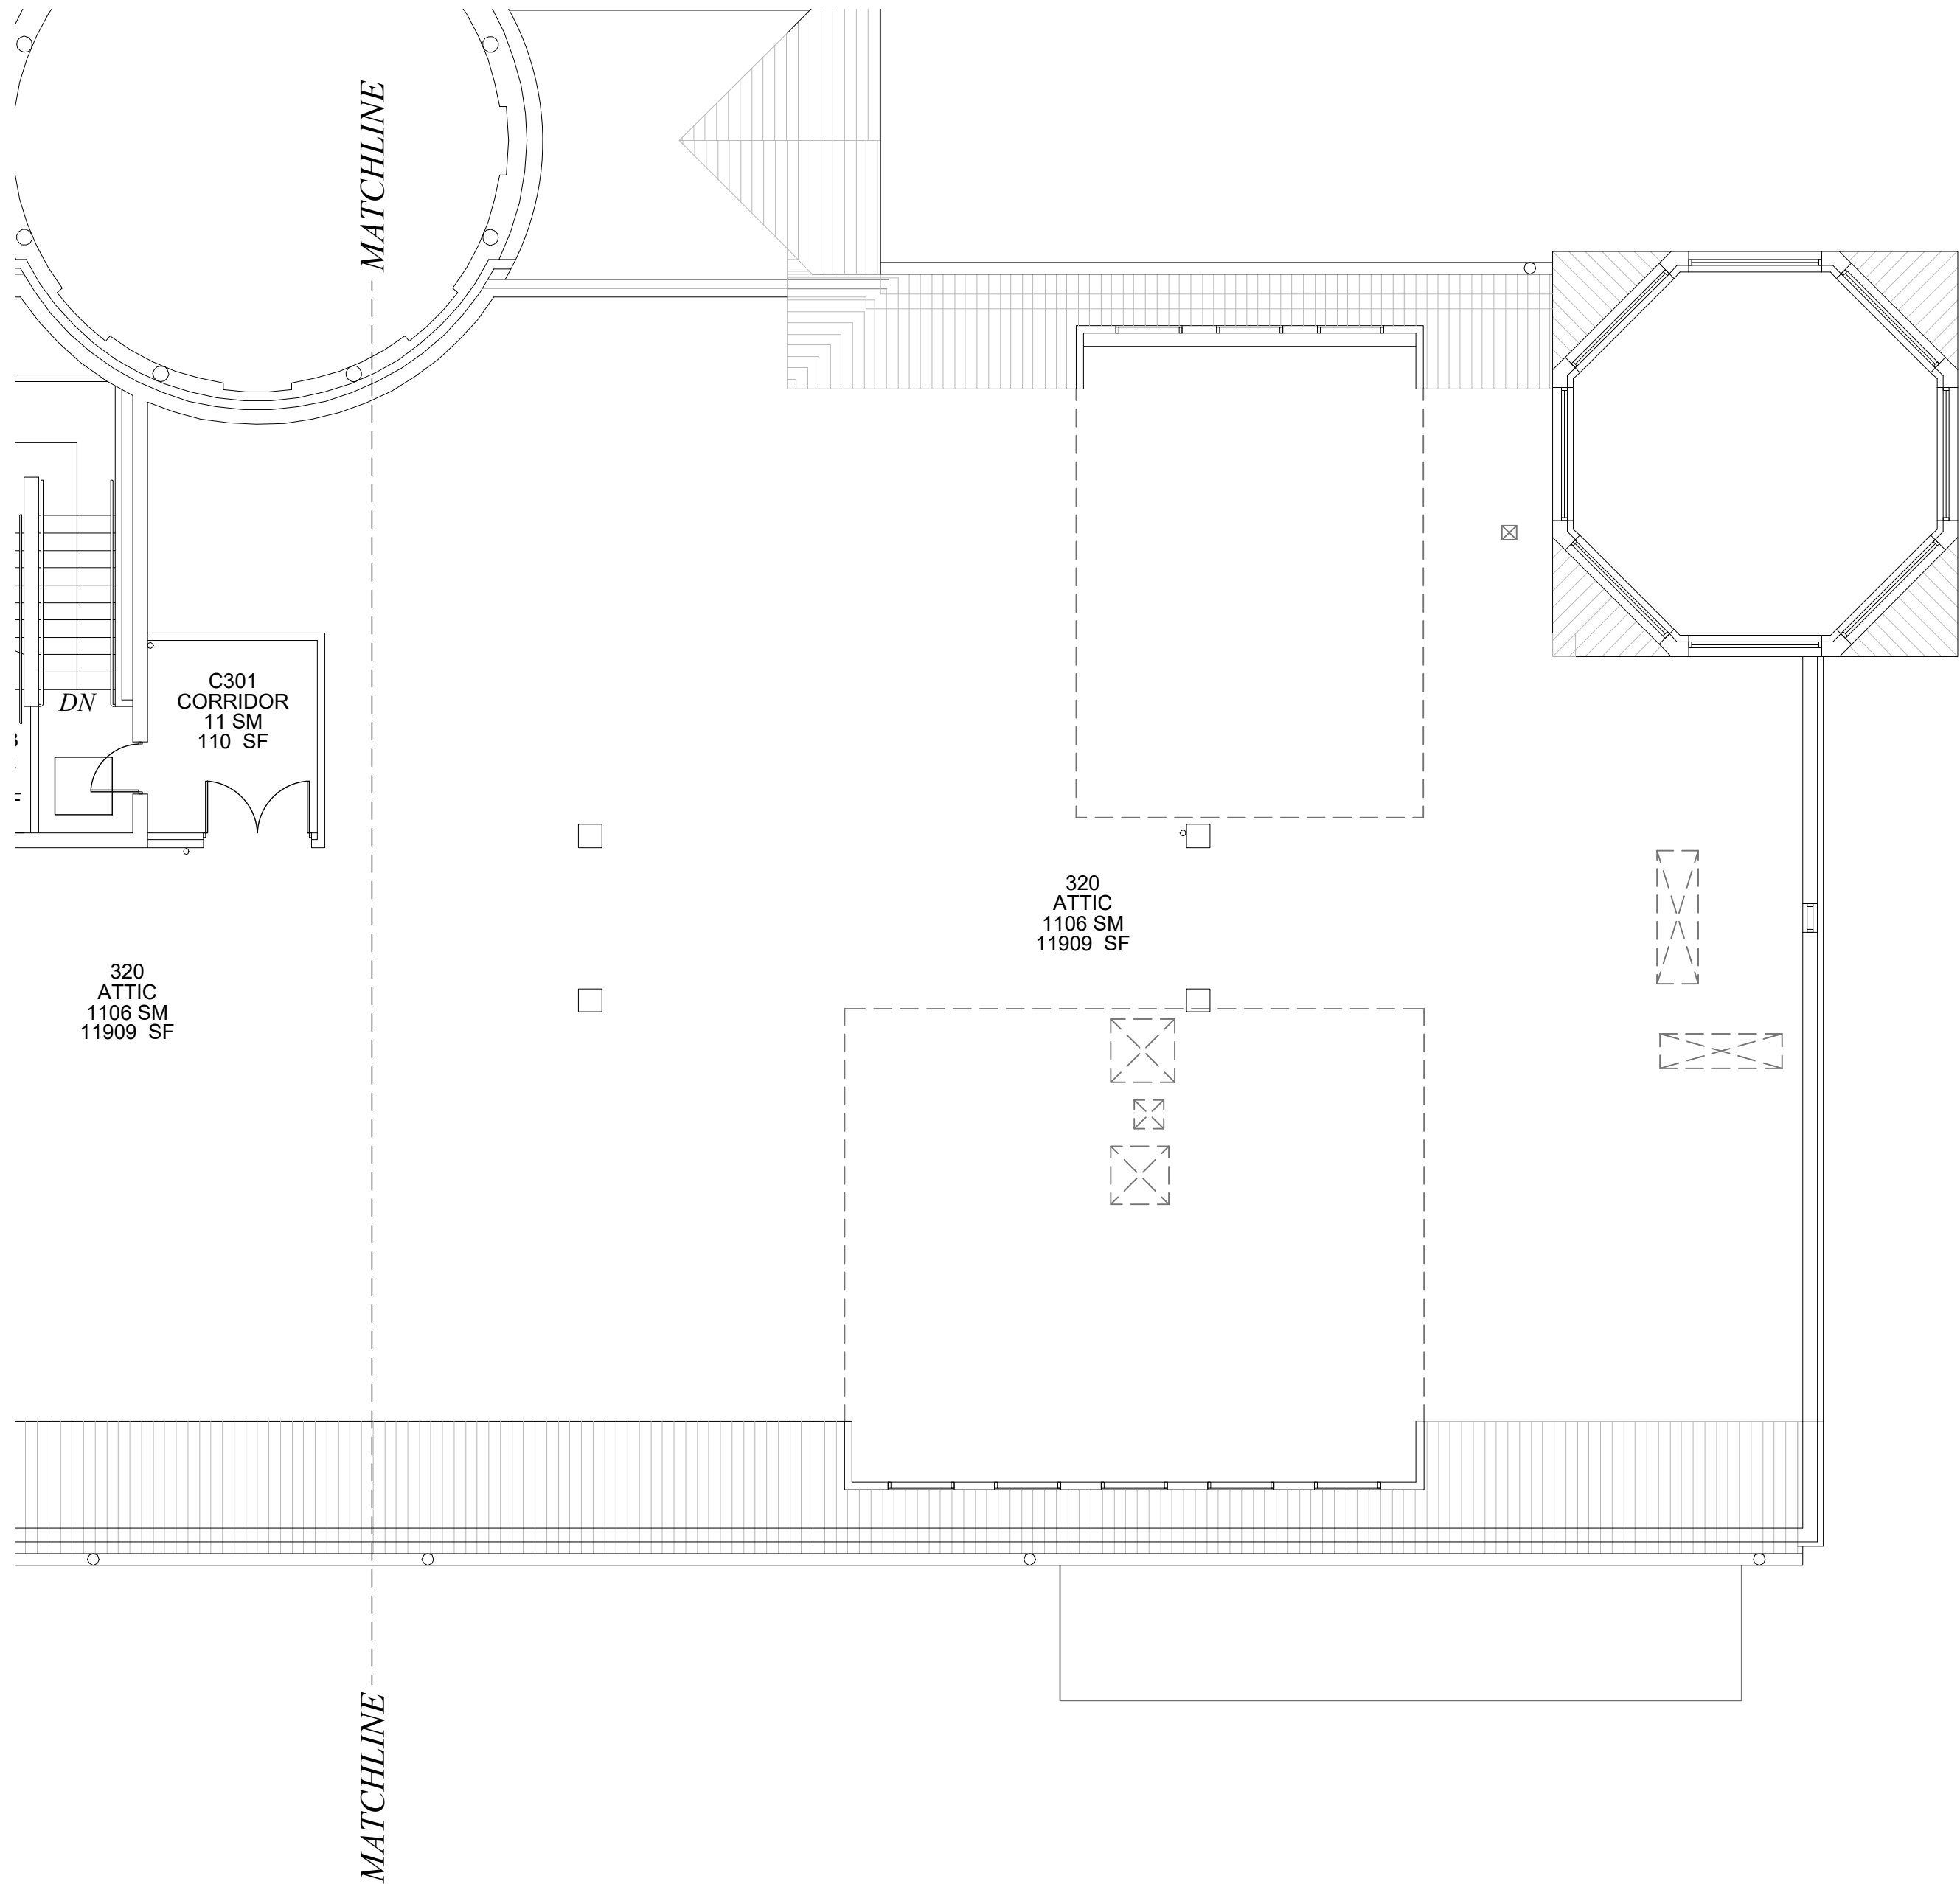

SYMBOL LEGEND			
	DOOR		DRINKING FOUNTAIN
	SLIDING DOOR		LAVATORY
	ACCORDION PARTITION		SINK
	STACK OR FOLDING PARTITION		TOILET
	WINDOW/GLAZING		URINAL
	HIGH WINDOW		LOCKER
	SKYLIGHT		LAN DISTRIBUTION FRAME
	STOOP/STEP UP		VENT HOOD
	STAIR		WALL SHELVING
	RAMP		UPPER CABINET
	ACCESS LADDER		BASE CABINET
	COLD STORAGE		TEACHER CABINET
	AREA CALCULATED @ 50 %		MATCHLINE
	SLOPING ROOF		FLAT ROOF

TITLEBLOCK LEGEND	
SHEET NAME:	BLDG #_FLOOR # (# IN SERIES)

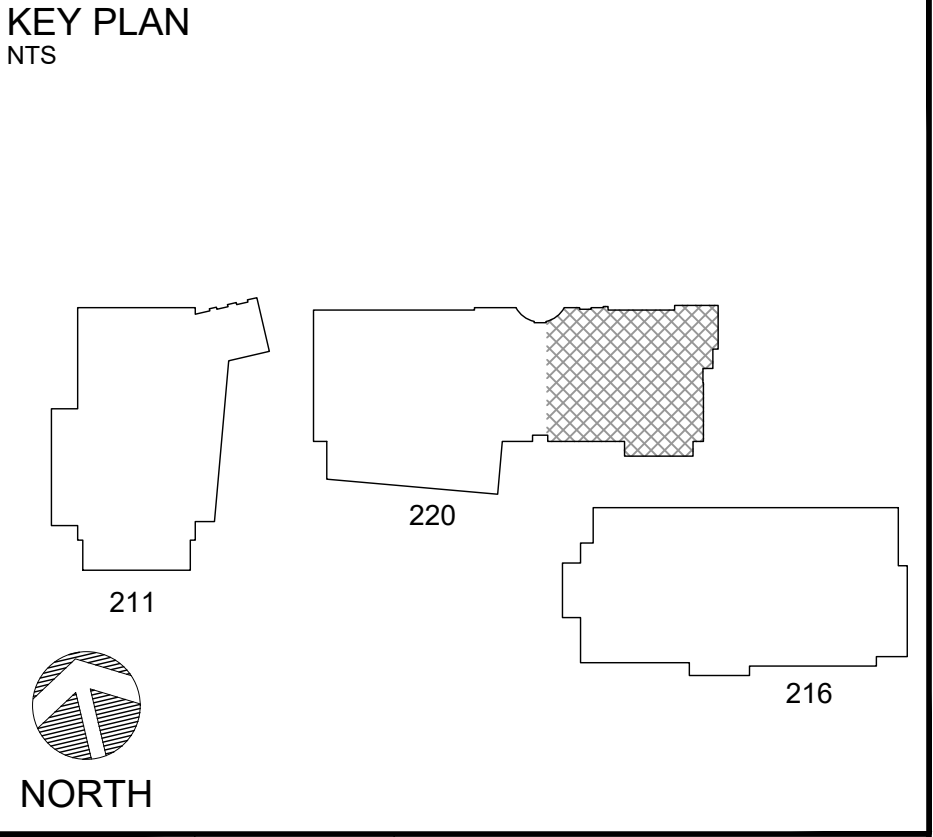

Updated By:	FUS Review:	100% Submittal Date:
AA	MRS	01 MAY 2020
0 2 4 8 16 FT		



DEPARTMENT OF DEFENSE EDUCATION ACTIVITY

FACILITY UTILIZATION SURVEY

SIGONELLA MIDDLE / HIGH SCHOOL		
BUILDING NUMBER: 220		
COUNTRY: ITALY		
INSTALLATION: NAS SIGONELLA		
SITE: NAS1 SUPPORT AREA		
REGION-DISTRICT: DODEA EUROPE SOUTH		
DoDAAC Number:	Floor:	Survey Date:
HE5515	LEVEL 3	JANUARY 2020
Sheet Name:	Sheet Seq:	
220_3 (2)		24 of 24