



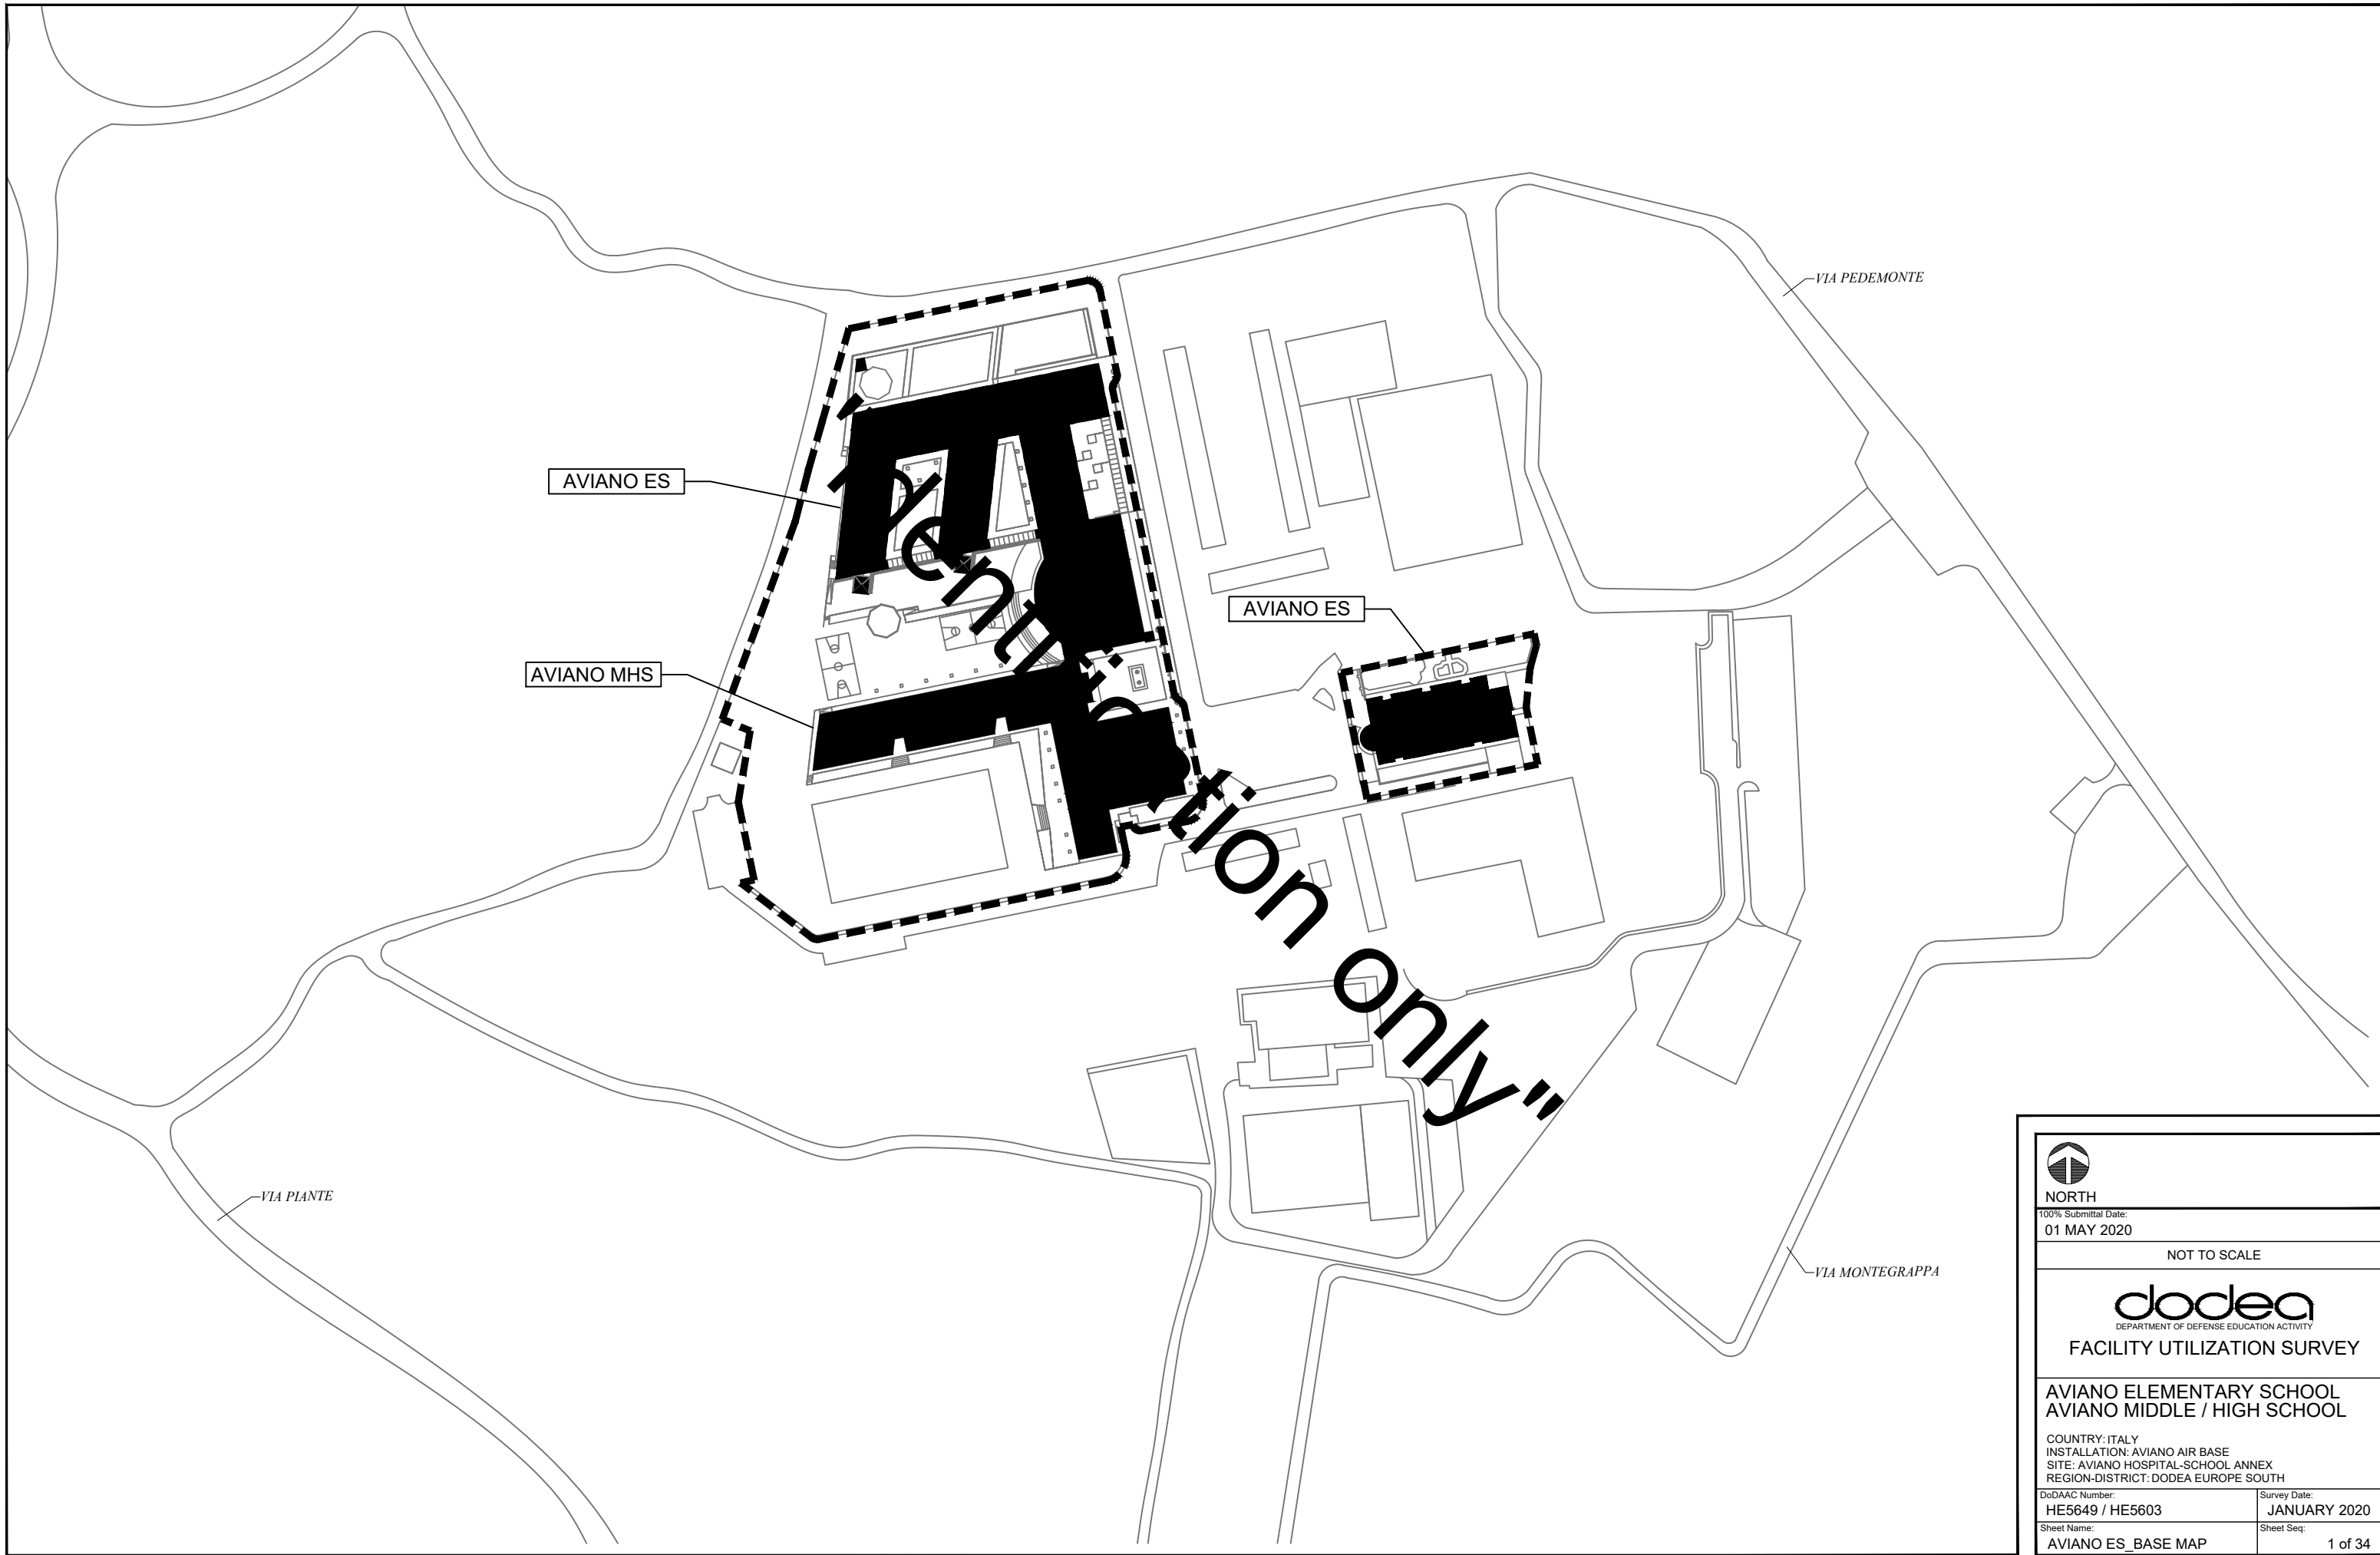

 NORTH	
100% Submittal Date: 01 MAY 2020	
NOT TO SCALE	
 DEPARTMENT OF DEFENSE EDUCATION ACTIVITY FACILITY UTILIZATION SURVEY	
AVIANO ELEMENTARY SCHOOL AVIANO MIDDLE / HIGH SCHOOL	
COUNTRY: ITALY INSTALLATION: AVIANO AIR BASE SITE: AVIANO HOSPITAL-SCHOOL ANNEX REGION-DISTRICT: DODEA EUROPE SOUTH	
DoDAAC Number: HE5649 / HE5603	Survey Date: JANUARY 2020
Sheet Name: AVIANO ES_BASE MAP	Sheet Seq: 1 of 34

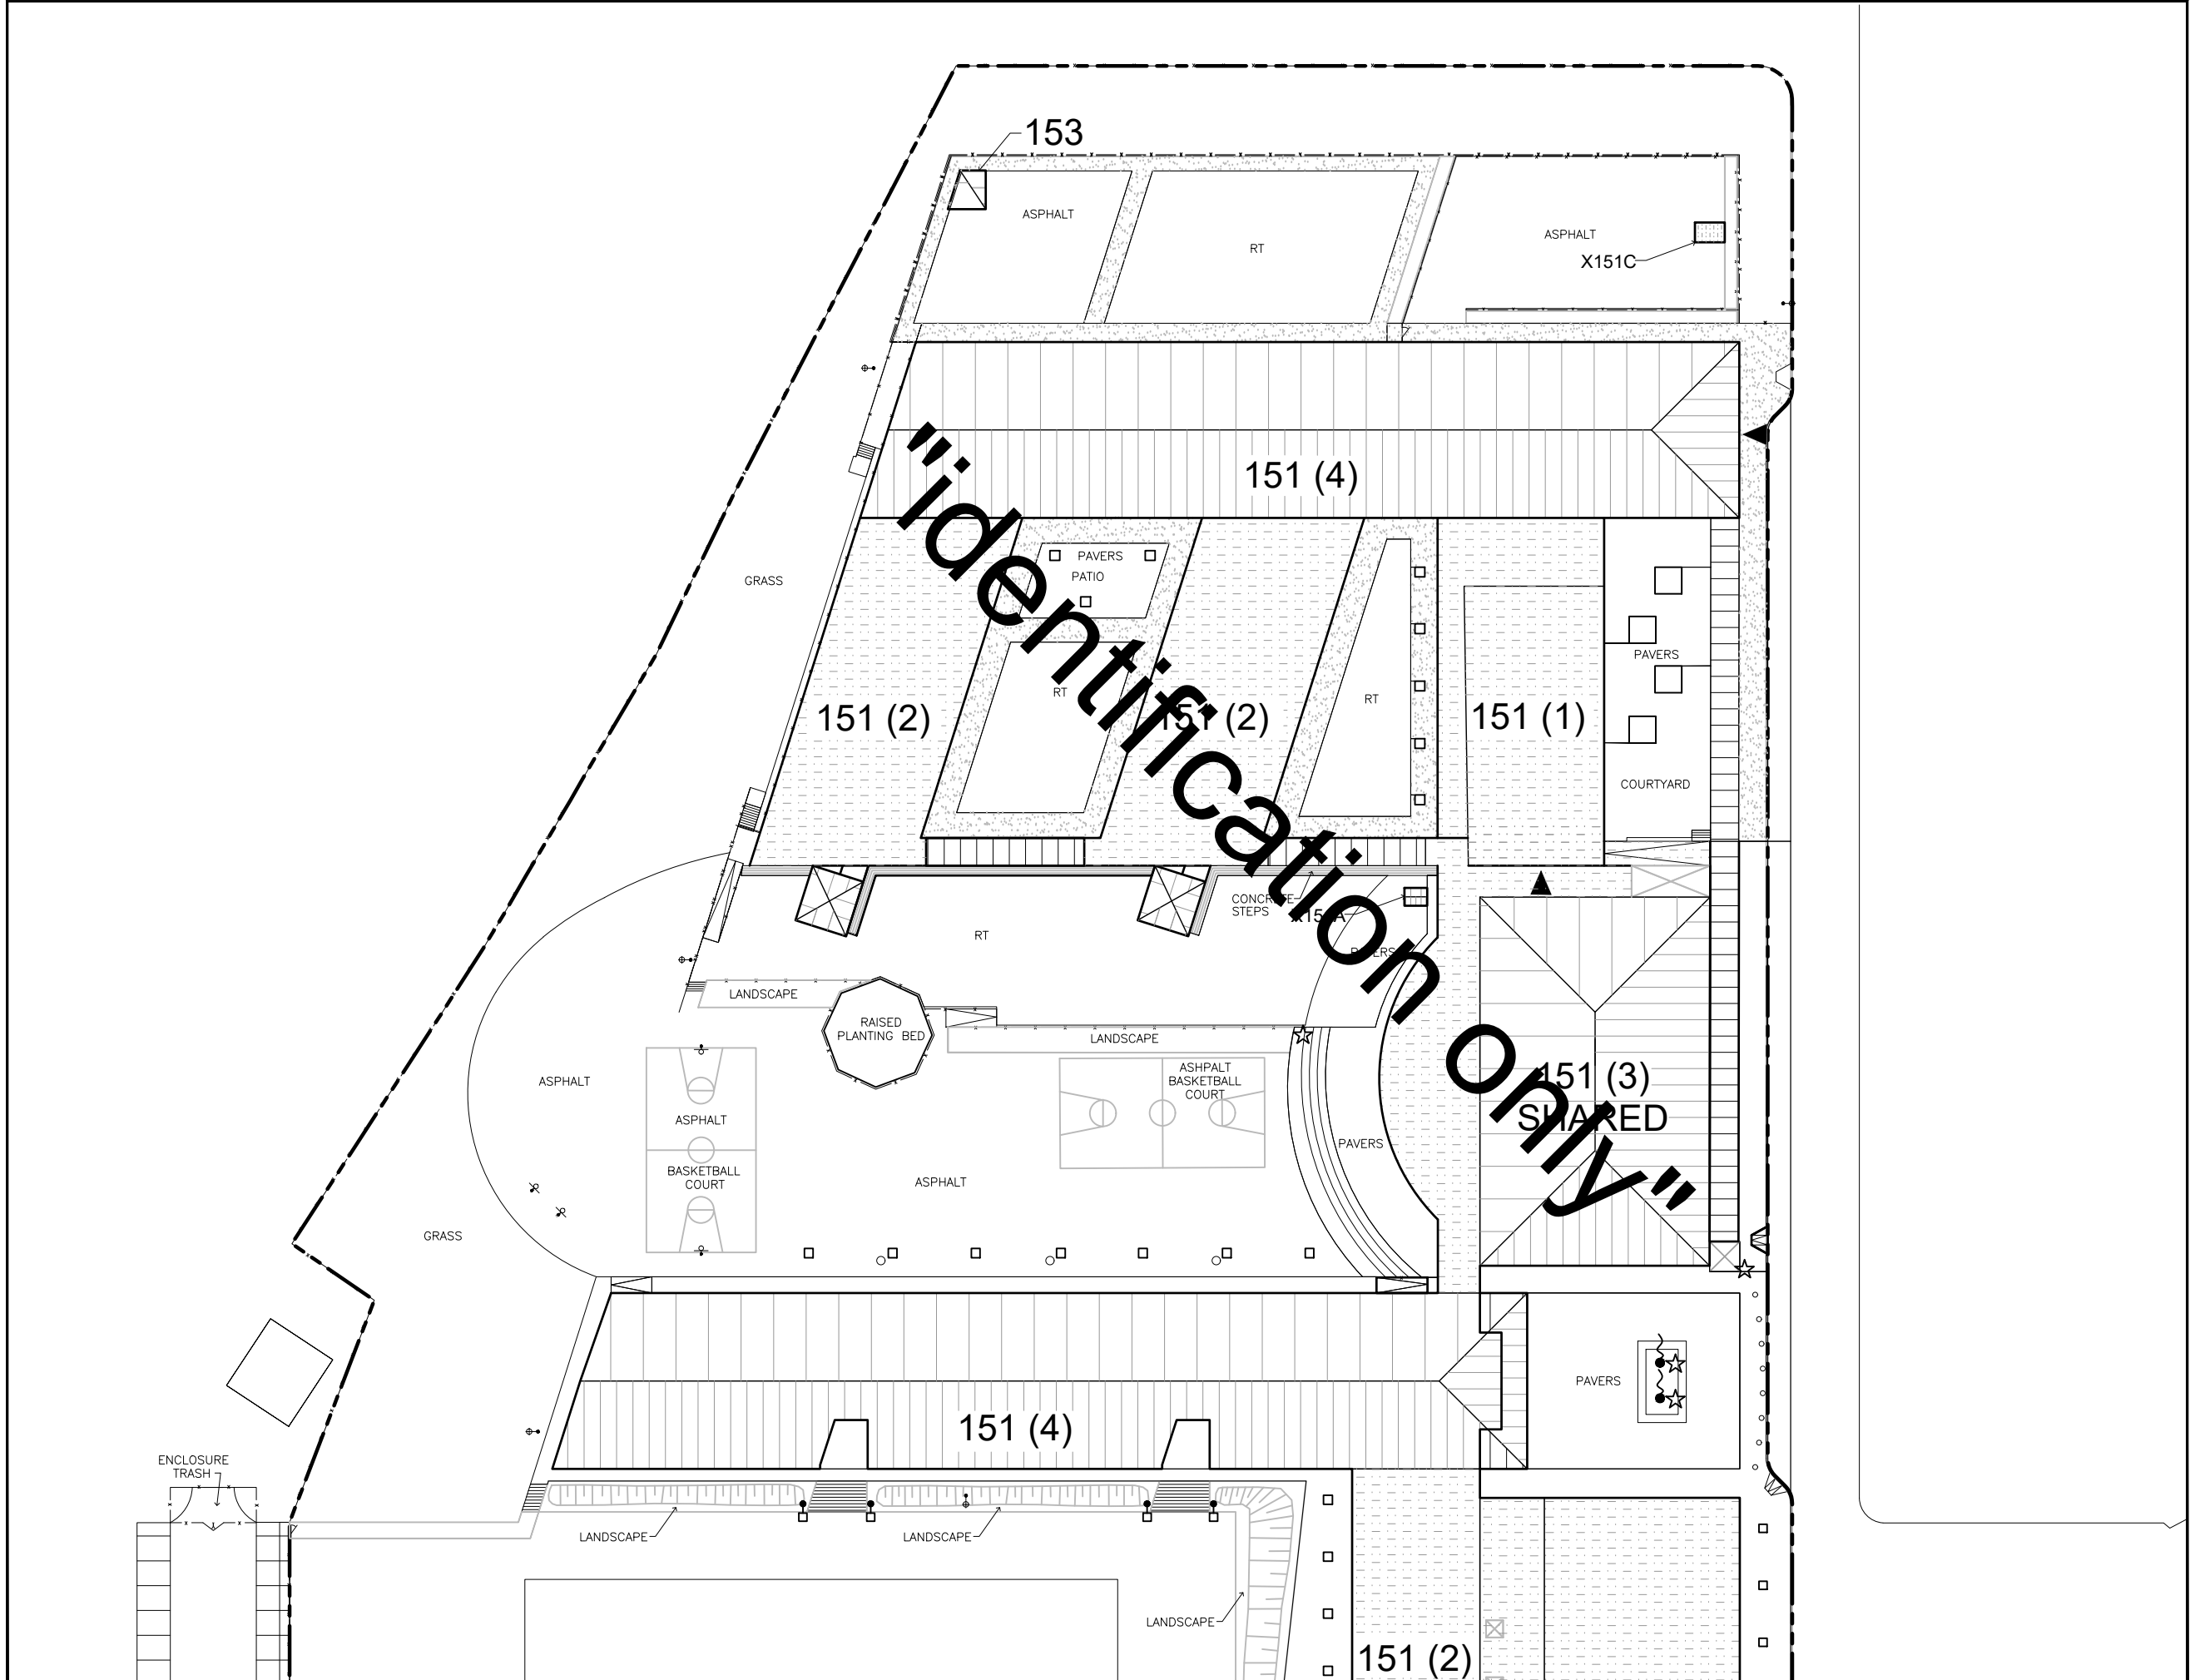

BASKETBALL GOAL

STADIUM LIGHT

SIGN

FOOTBALL GOAL

BASEBALL BACKSTOP

PARKING AREA

FLAT ROOF

SLOPE

COVERED WALKWAY

SLOPING ROOF

AREA LIGHT

FLAG POLE

MONUMENT

SOCCER GOAL

MAIN ENTRY

CONCRETE

PLAYGROUND

FIRE HYDRANT

PROPERTY LINE

(APPROX. 36,574 SM)

(APPROX. 9.05 AC)

FENCE LINE

LEGEND

PLAYGROUND SURFACING

WC - WOOD CHIPS PR - POURED RUBBER M - MULCH

SRT - SHREDDED RUBBER TIRES S - SAND

PG - PEA GRAVEL RT - RUBBER TILES

BUILDING LABEL

BLDG # (# OF FLOORS)

KEY PLAN

NTS

NORTH

Updated By: SPF

FUS Review: MRS

100% Submittal Date: 01 MAY 2020

0

16

32

64 FT

dodea

DEPARTMENT OF DEFENSE EDUCATION ACTIVITY

FACILITY UTILIZATION SURVEY

AVIANO ELEMENTARY SCHOOL

AVIANO MIDDLE / HIGH SCHOOL

COUNTRY: ITALY

INSTALLATION: AVIANO AIR BASE

SITE: AVIANO HOSPITAL-SCHOOL ANNEX


REGION-DISTRICT: DODEA EUROPE SOUTH

DoDAAC Number: HE5649 / HE5603

Survey Date: JANUARY 2020

Sheet Name: AVIANO EMHS SITE 32ND (1)


Sheet Seq: 3 of 34

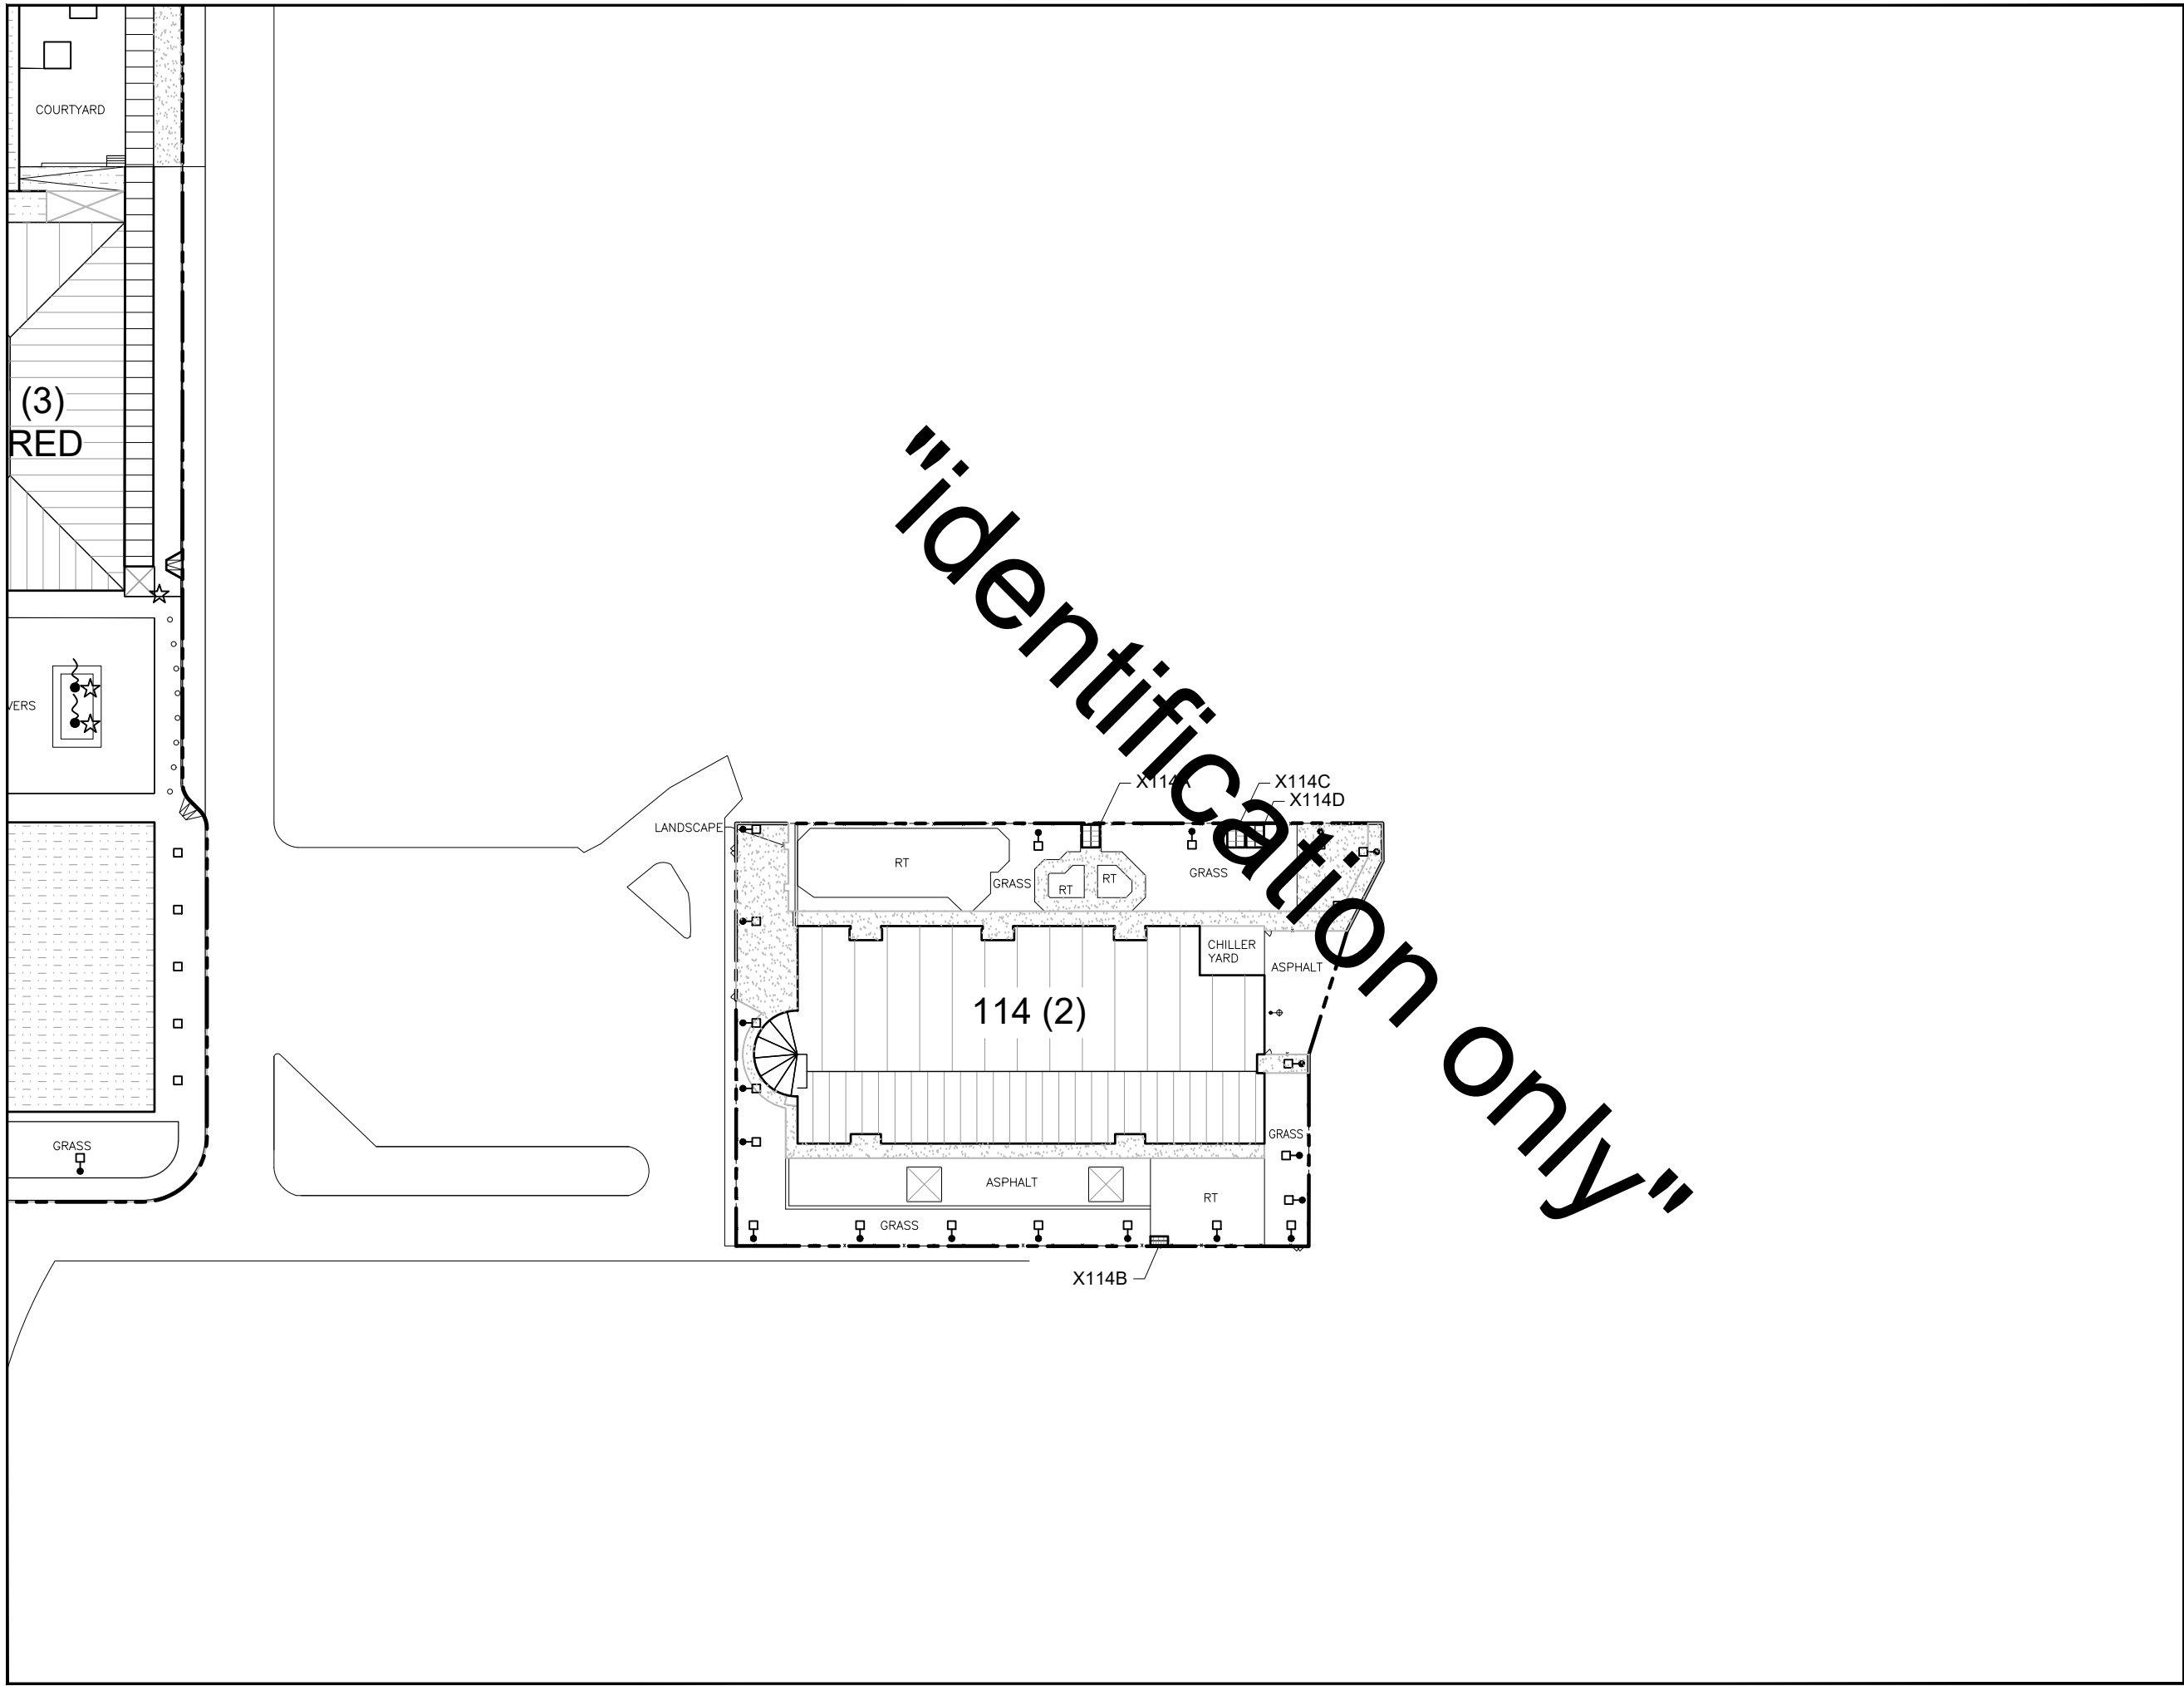

SYMBOL LEGEND	
	BASKETBALL GOAL
	AREA LIGHT
	STADIUM LIGHT
	FLAG POLE
	SIGN
	MONUMENT
	FOOTBALL GOAL
	SOCCER GOAL
	BASEBALL BACKSTOP
	MAIN ENTRY
	PARKING AREA
	CONCRETE
	FLAT ROOF
	PLAYGROUND
	SLOPE
	FIRE HYDRANT
	COVERED WALKWAY
	SLOPING ROOF
	PROPERTY LINE (APPROX. 36,574 SM) (APPROX. 9.05 AC)
	FENCE LINE

LEGEND	
PLAYGROUND SURFACING	
WC - WOOD CHIPS	PR - POURED RUBBER
M - MULCH	
SRT - SHREDDED RUBBER TIRES	S - SAND
PG - PEA GRAVEL	RT - RUBBER TILES

BUILDING LABEL	BLDG #_(# OF FLOORS)
----------------	----------------------

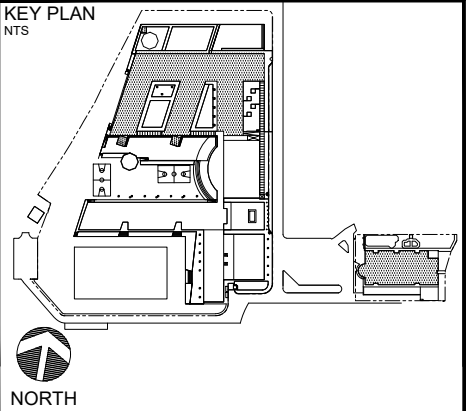

Updated By:	FUS Review:	100% Submittal Date:
SPF	MRS	01 MAY 2020

0 16 32 64 FT

DEPARTMENT OF DEFENSE EDUCATION ACTIVITY
FACILITY UTILIZATION SURVEY

AVIANO ELEMENTARY SCHOOL
AVIANO MIDDLE / HIGH SCHOOL


COUNTRY: ITALY
INSTALLATION: AVIANO AIR BASE
SITE: AVIANO HOSPITAL-SCHOOL ANNEX
REGION-DISTRICT: DODEA EUROPE SOUTH

DoDAAC Number:
HE5649 / HE5603

Survey Date:
JANUARY 2020

Sheet Name:
AVIANO EMHS SITE 32ND (3)

Sheet Seq:
5 of 34

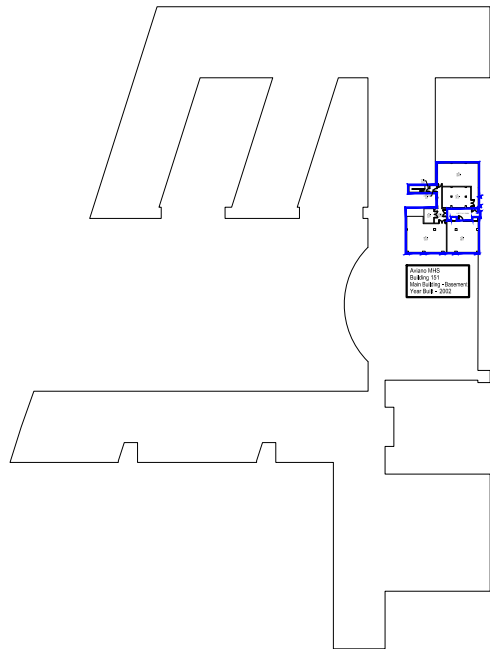


BUILDING 151 - BASEMENT FLOOR

GSF CALCULATIONS


Building 114	
Floor 1	15,136
Floor 2	4,595
Total Area (SF)	19,731
50% Area (SF)	9,865
Gross Area (SF)	20,046

Building 151	
Basement	5,183
Floor 1	113,883
Floor 2	77,258
Floor 3	47,800
Floor 4	26,405
Total Area (SF)	270,529
50% Area (SF)	135,264
Gross Area (SF)	275,854


Building 153	
Floor 1	203
Total Area (SF)	203
50% Area (SF)	0
Gross Area (SF)	203

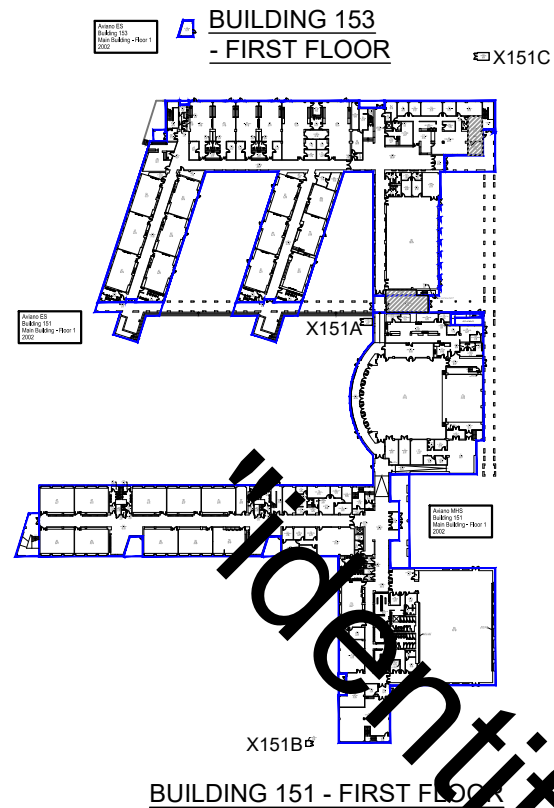


BUILDING 151 - FIRST FLOOR

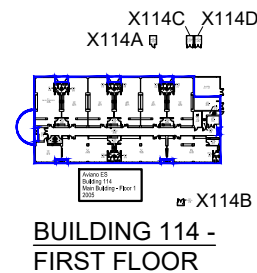


BUILDING 114 - FIRST FLOOR

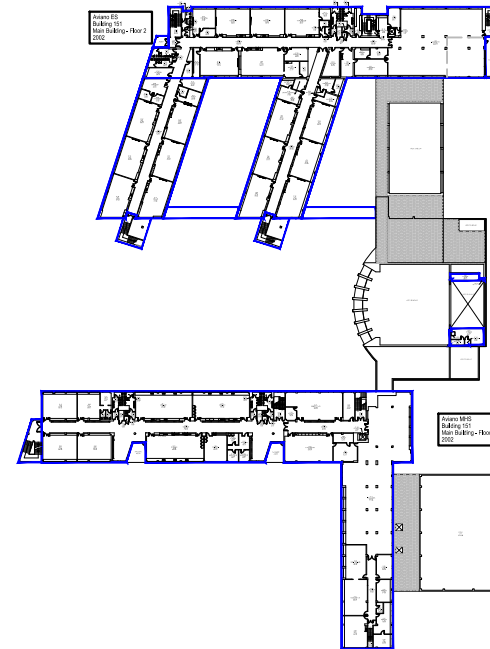


BUILDING 151 - SECOND FLOOR

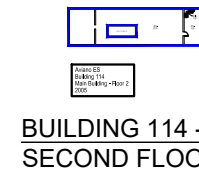

BUILDING 114 - SECOND FLOOR

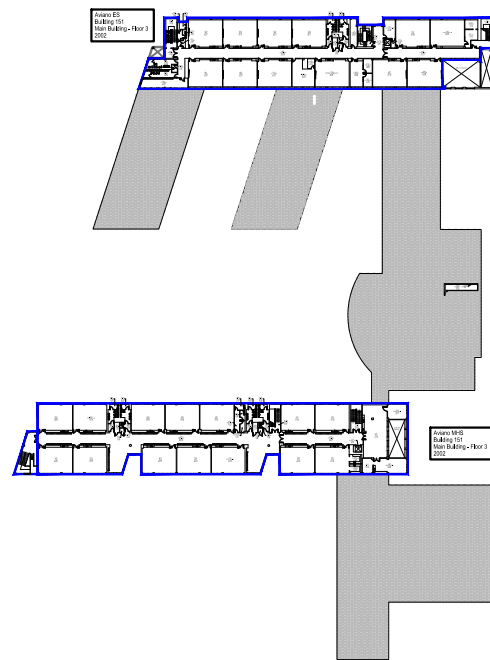

BUILDING 151 - THIRD FLOOR

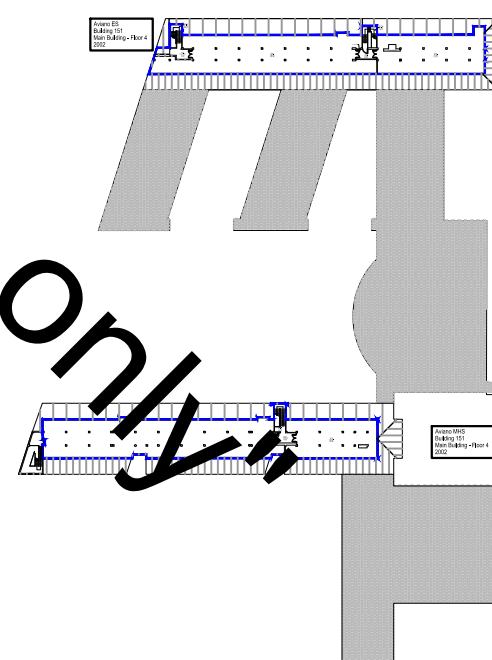

BUILDING 151 - FOURTH FLOOR

NOTE 1: APPROXIMATELY 44% OF BUILDING 151 IS OCCUPIED BY AVIANO ES.
NOTE 2: APPROXIMATELY 1% OF BUILDING 151 IS OCCUPIED BY DODEA EUROPE SOUTH DSO.
NOTE 3: GSF CALCULATIONS BASED ON ARMY RPI DoA PAMPHLET 415-28.

DOOR

SLIDING DOOR

ACCORDION PARTITION

STACK OR FOLDING PARTITION

WINDOW/GLAZING

HIGH WINDOW

SKYLIGHT

STOOP/STEP UP

STAIR

RAMP

ACCESS LADDER

COLD STORAGE

AREA CALCULATED @ 50 %

SLOPING ROOF

DRINKING FOUNTAIN

LAVATORY

SINK

TOILET

URINAL

LOCKER

LAN DISTRIBUTION FRAME

VENT HOOD

WALL SHELVING

UPPER CABINET

BASE CABINET

TEACHER CABINET

MATCHLINE

FLAT ROOF

TITLEBLOCK LEGEND

SHEET NAME:

BLDG #_FLOOR # (# IN SERIES)

KEY PLAN

NTS

153

151

114

151C

151A

114D

114C

114A

114B

151B

NORTH

Updated By:

FUS Review:

100% Submittal Date:

SPF

MRS

01 MAY 2020

NOT TO SCALE

dodea

DEPARTMENT OF DEFENSE EDUCATION ACTIVITY

FACILITY UTILIZATION SURVEY

AVIANO ELEMENTARY SCHOOL

AVIANO MIDDLE / HIGH SCHOOL

BUILDING NUMBER: 114, 151, 153, X114A-D, X151A-C

COUNTRY: ITALY

INSTALLATION: AVIANO AIR BASE

SITE: AVIANO HOSPITAL-SCHOOL ANNEX

REGION-DISTRICT: DODEA EUROPE SOUTH

DoDAAC Number:

Floor:

Survey Date:

HE5649 / HE5603

LEVEL 1-4


JANUARY 2020

Sheet Name:


Sheet Seq:

GSF 1 (1)


6 of 34

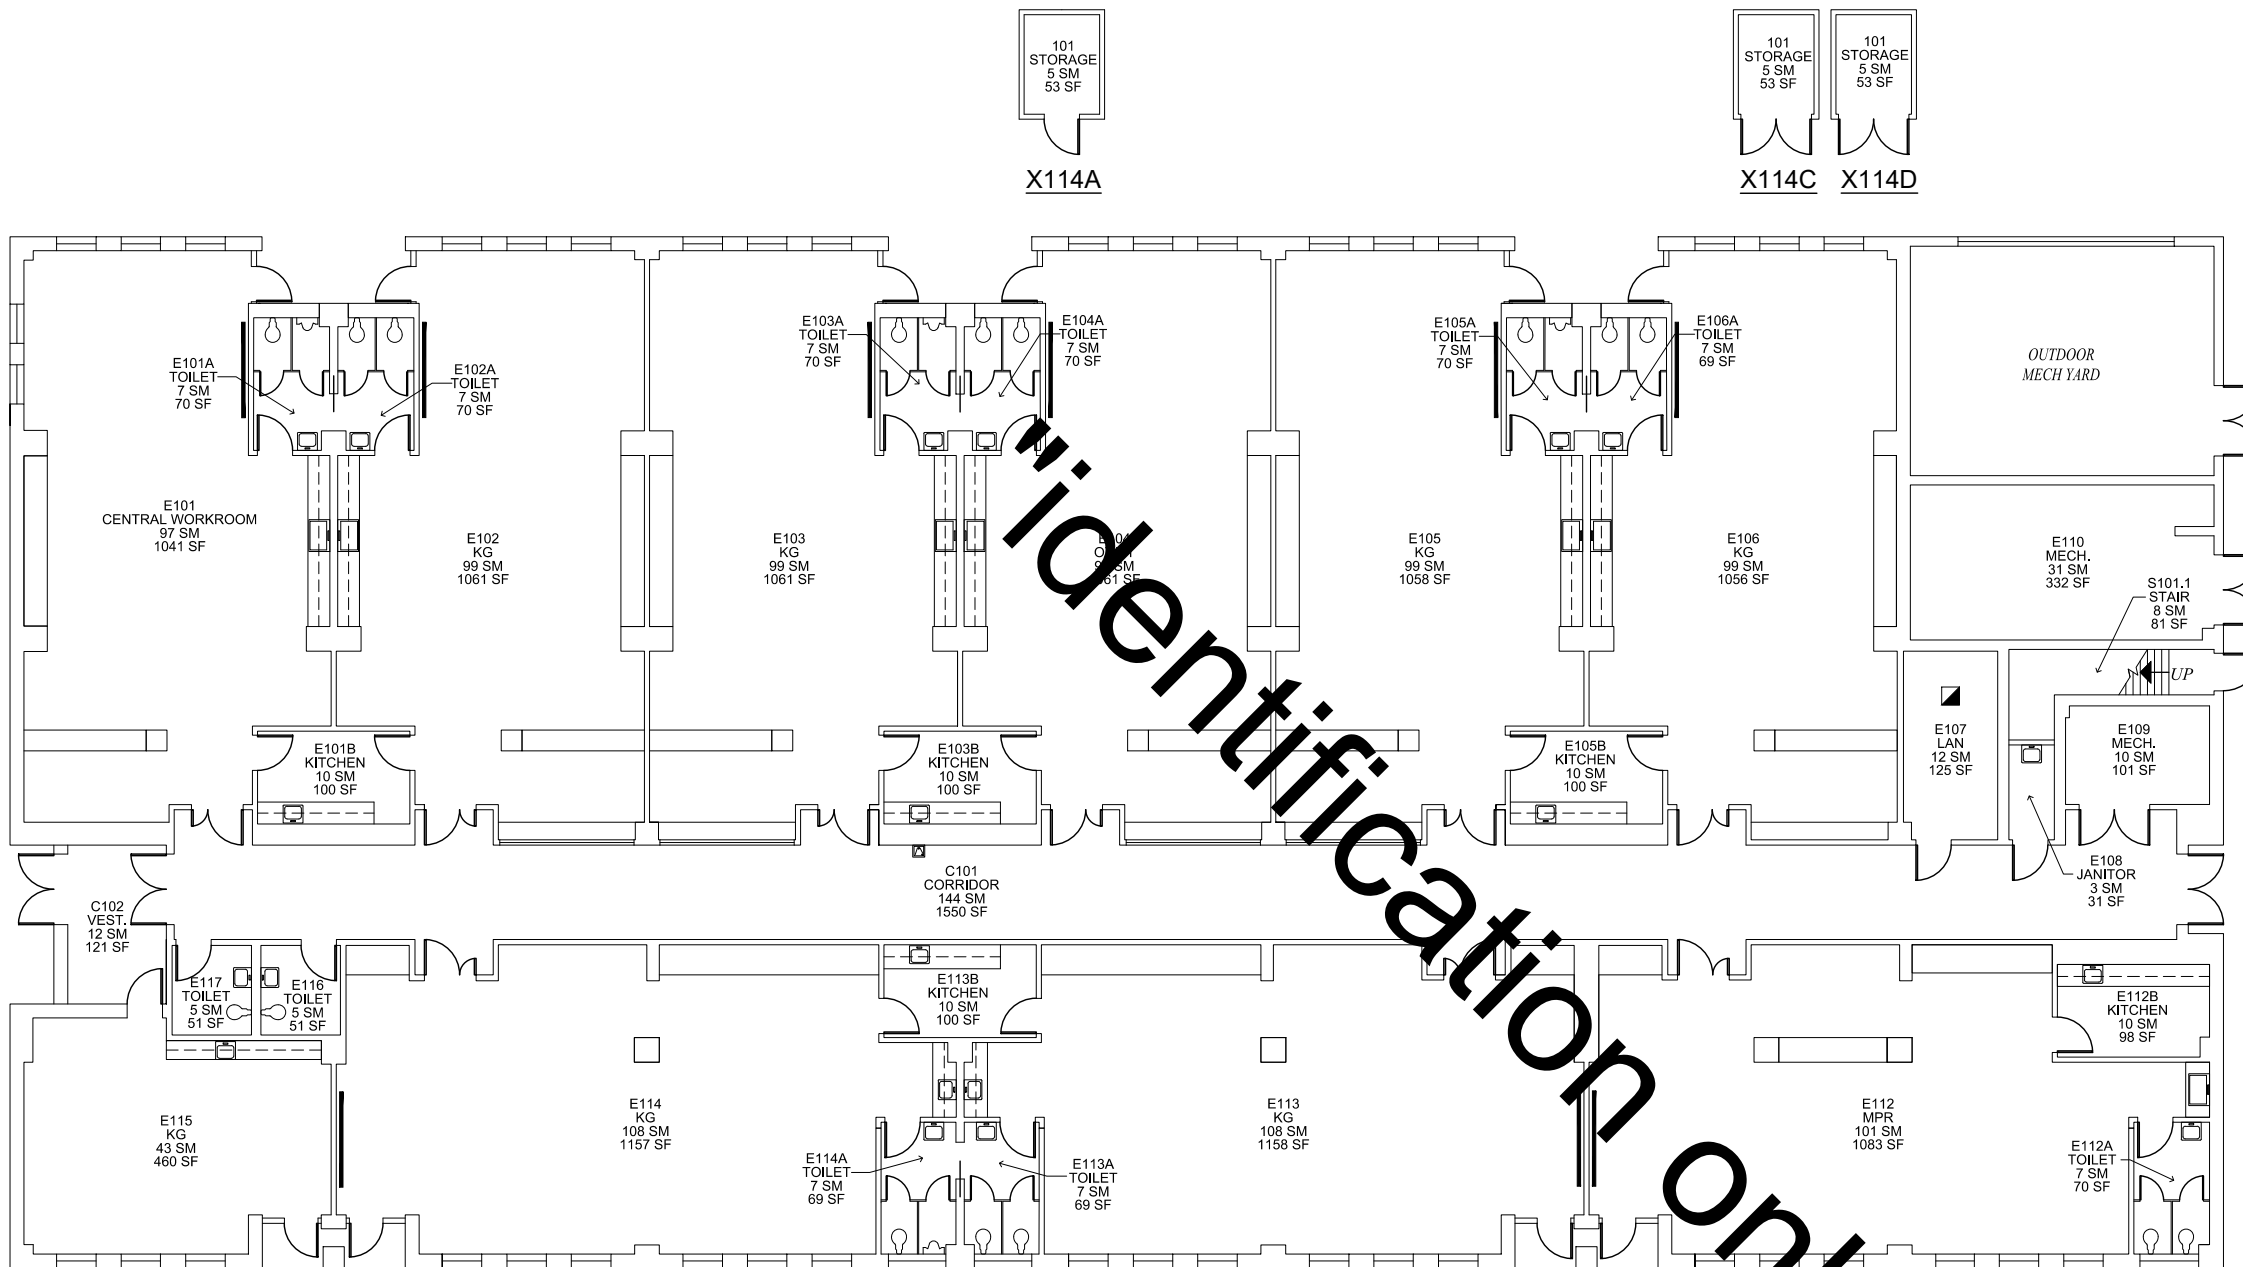

BUILDING 114 - FIRST FLOOR

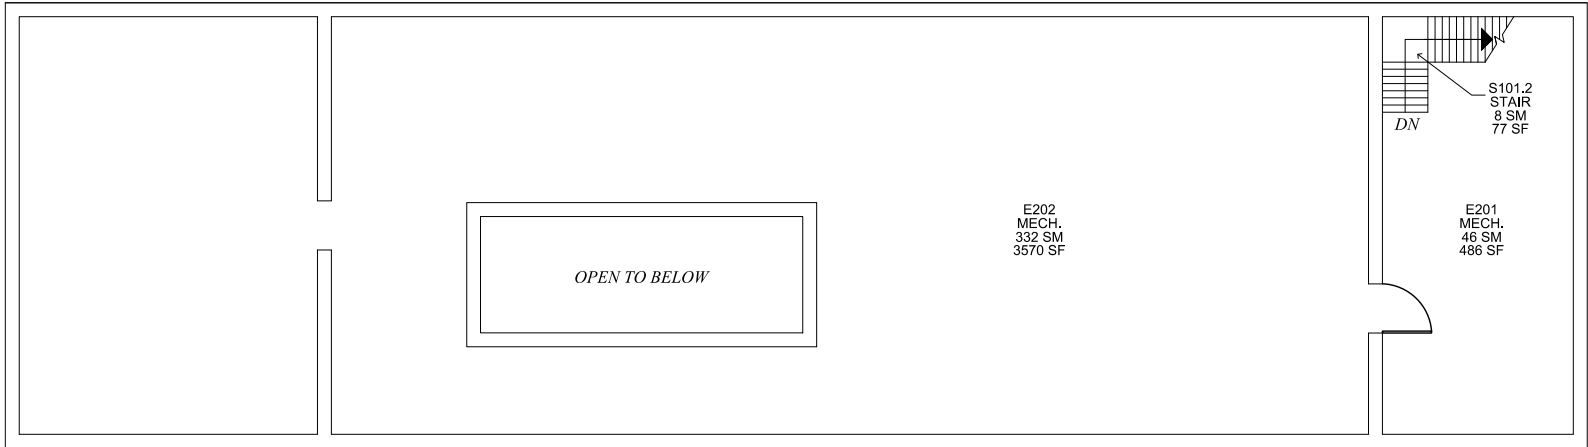

BUILDING 114 - SECOND FLOOR

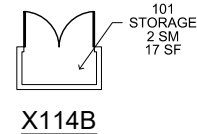

DOOR

SLIDING DOOR

ACCORDION PARTITION

STACK OR FOLDING PARTITION

WINDOW/GLAZING

HIGH WINDOW

SKYLIGHT

STOOP/STEP UP

STAIR

RAMP

ACCESS LADDER

COLD STORAGE

AREA CALCULATED @ 50 %

SLOPING ROOF

DRINKING FOUNTAIN

LAVATORY

SINK

TOILET

URINAL

LOCKER

LAN DISTRIBUTION FRAME

VENT HOOD

WALL SHELVING

UPPER CABINET

BASE CABINET

TEACHER CABINET

MATCHLINE

FLAT ROOF

TITLEBLOCK LEGEND

SHEET NAME:

BLDG #_FLOOR # (# IN SERIES)

KEY PLAN

NTS

153

X151C

X151A

151

X114D

X114C

X114A

114

X114B

X151B

NORTH

Updated By: SPF

FUS Review: MRS

100% Submittal Date: 01 MAY 2020

0 2 4 8 16 FT

dodea

DEPARTMENT OF DEFENSE EDUCATION ACTIVITY

FACILITY UTILIZATION SURVEY

AVIANO ELEMENTARY SCHOOL

AVIANO MIDDLE / HIGH SCHOOL

BUILDING NUMBER: 114, X114A-D

COUNTRY: ITALY

INSTALLATION: AVIANO AIR BASE

SITE: AVIANO HOSPITAL-SCHOOL ANNEX

REGION-DISTRICT: DODEA EUROPE SOUTH


DoDAAC Number: HE5649 / HE5603

Floor: LEVEL 1-2

Survey Date: JANUARY 2020

Sheet Name: 114_1 (1)

Sheet Seq: 9 of 34

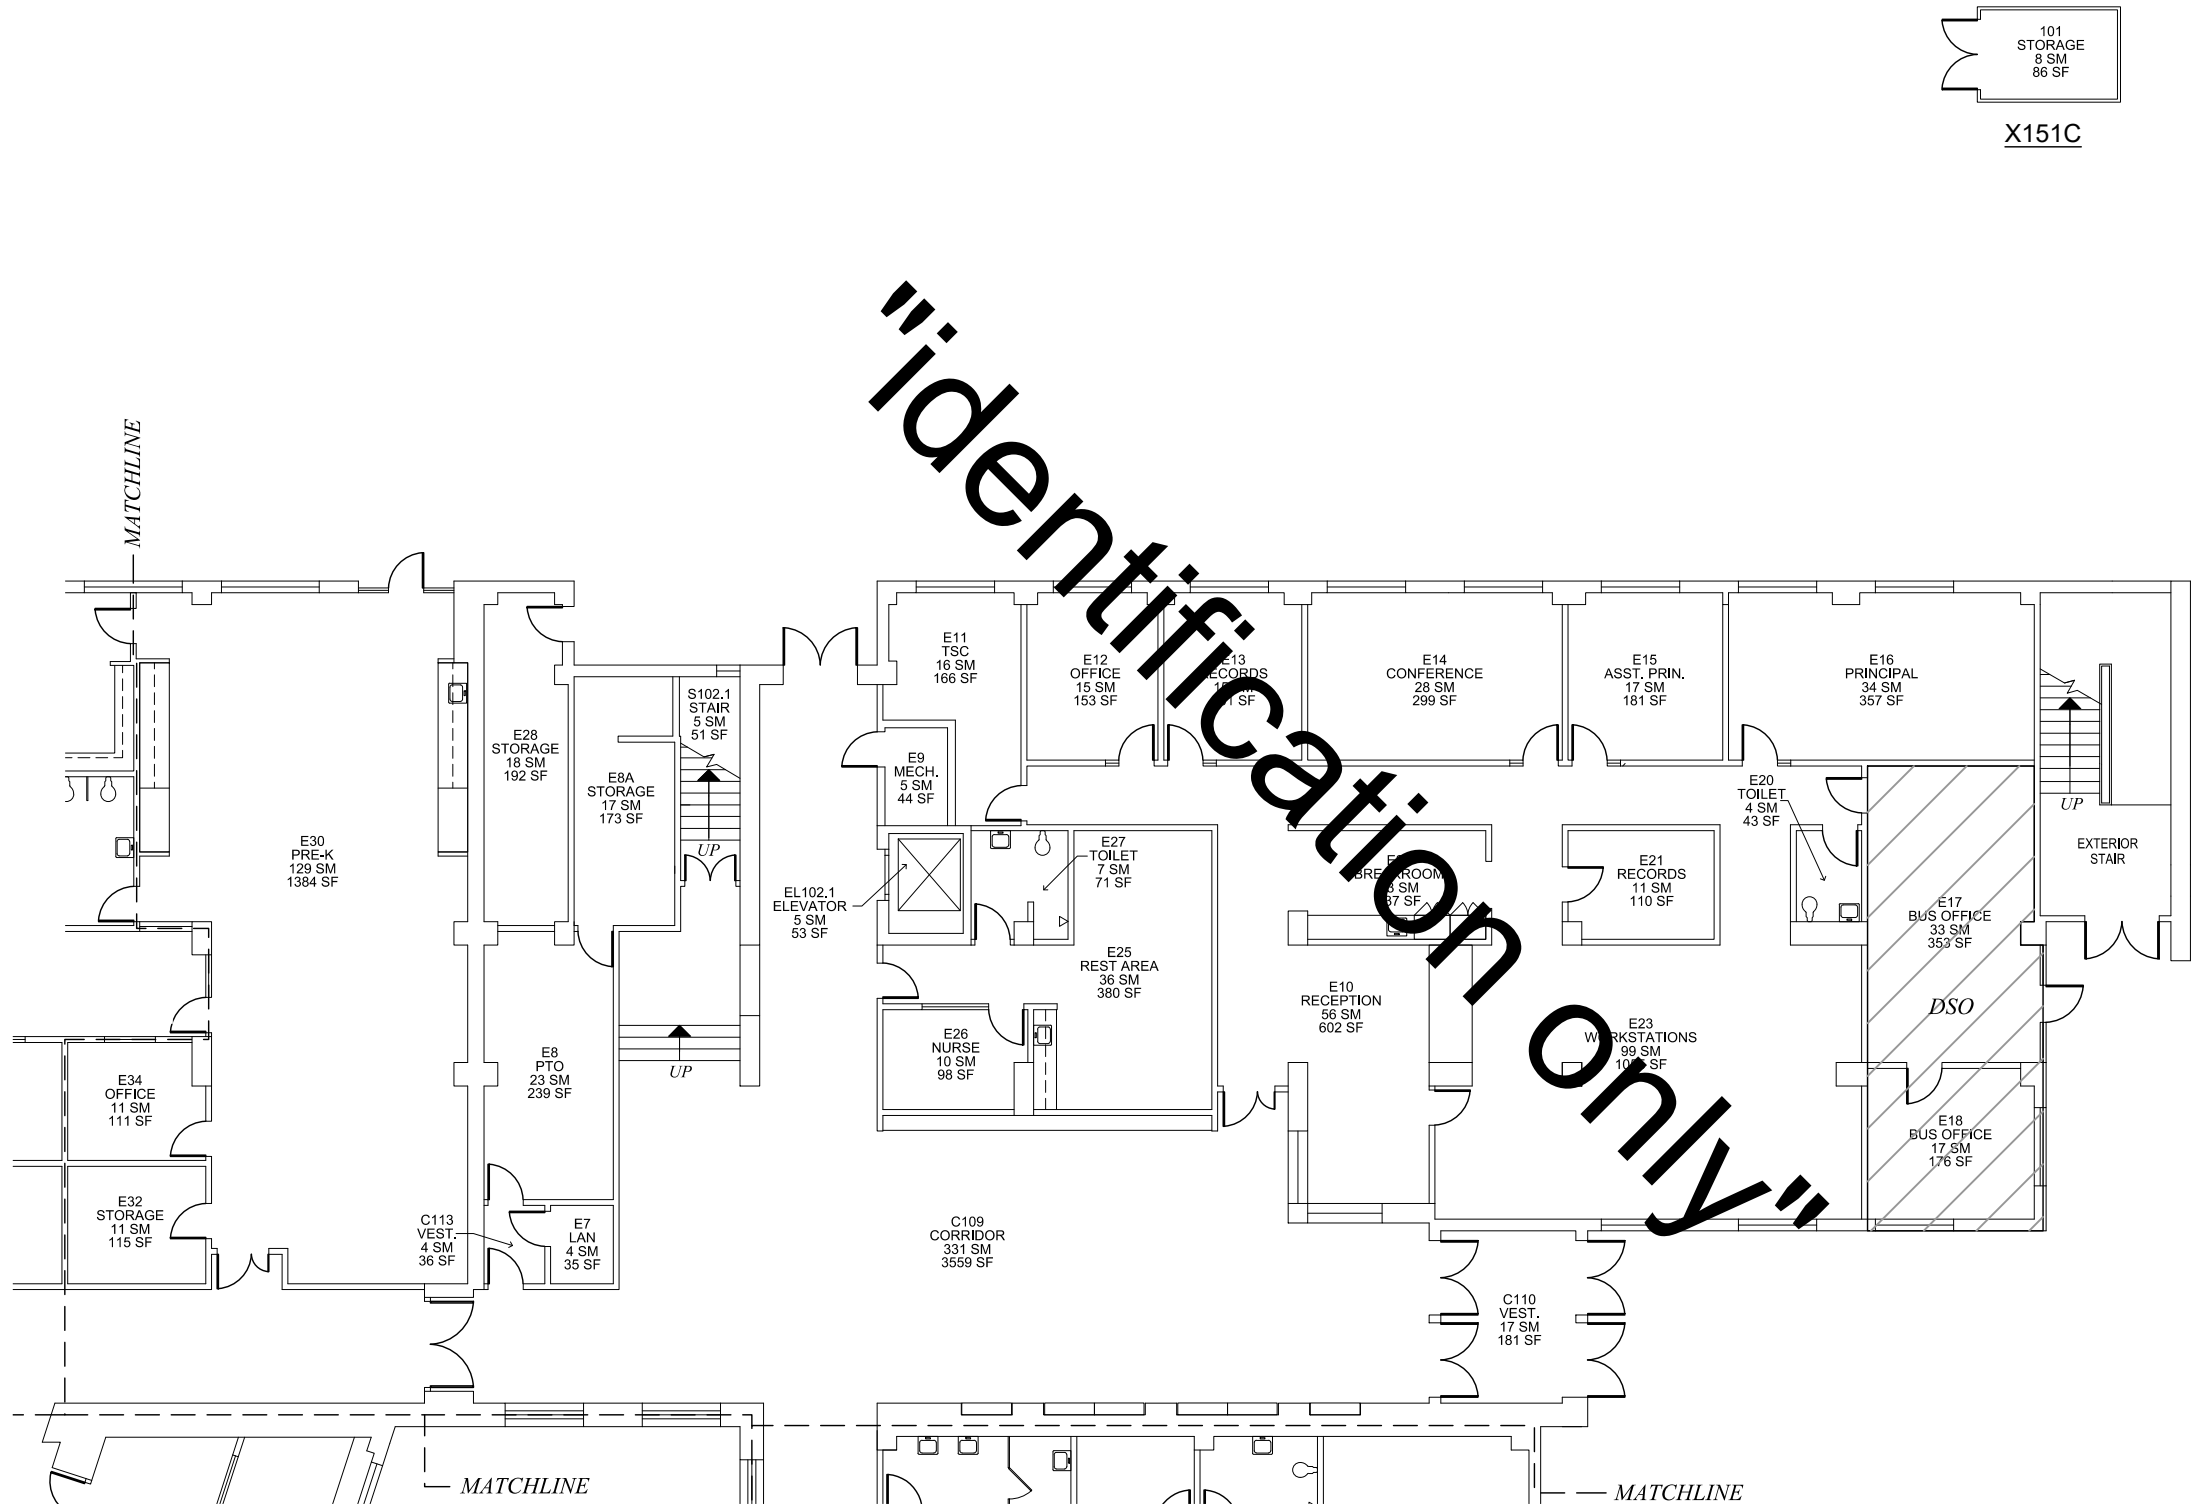

BUILDING 151 - FIRST FLOOR

DOOR

SLIDING DOOR

ACCORDION PARTITION

STACK OR FOLDING PARTITION

WINDOW/GLAZING

HIGH WINDOW

SKYLIGHT

STOOP/STEP UP

STAIR

RAMP

ACCESS LADDER

COLD STORAGE

AREA CALCULATED @ 50 %

SLOPING ROOF

DRINKING FOUNTAIN

LAVATORY

SINK

TOILET

URINAL

LOCKER

LAN DISTRIBUTION FRAME

VENT HOOD

WALL SHELVING

UPPER CABINET

BASE CABINET

TEACHER CABINET

MATCHLINE

FLAT ROOF

TITLEBLOCK LEGEND

SHEET NAME:

BLDG #_FLOOR # (# IN SERIES)

KEY PLAN

NTS

153

X151C

X151A

151

X114D

X114C

X114A

114

X151B

X114B

NORTH

Updated By:

SPF

FUS Review:

MRS

100% Submittal Date:

01 MAY 2020

0

2

4

8

16

FT

dodea

DEPARTMENT OF DEFENSE EDUCATION ACTIVITY

FACILITY UTILIZATION SURVEY

AVIANO ELEMENTARY SCHOOL

AVIANO MIDDLE / HIGH SCHOOL

BUILDING NUMBER: 151, X151C

COUNTRY: ITALY

INSTALLATION: AVIANO AIR BASE

SITE: AVIANO HOSPITAL-SCHOOL ANNEX

REGION-DISTRICT: DODEA EUROPE SOUTH

DoDAAC Number:

HE5649 / HE5603

Floor:

LEVEL 1

Survey Date:


JANUARY 2020

Sheet Name:

151_1 (1)


Sheet Seq:

11 of 34

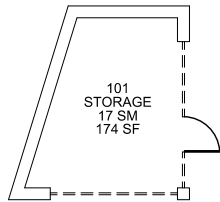

BUILDING 153 - FIRST FLOOR

"identification only"

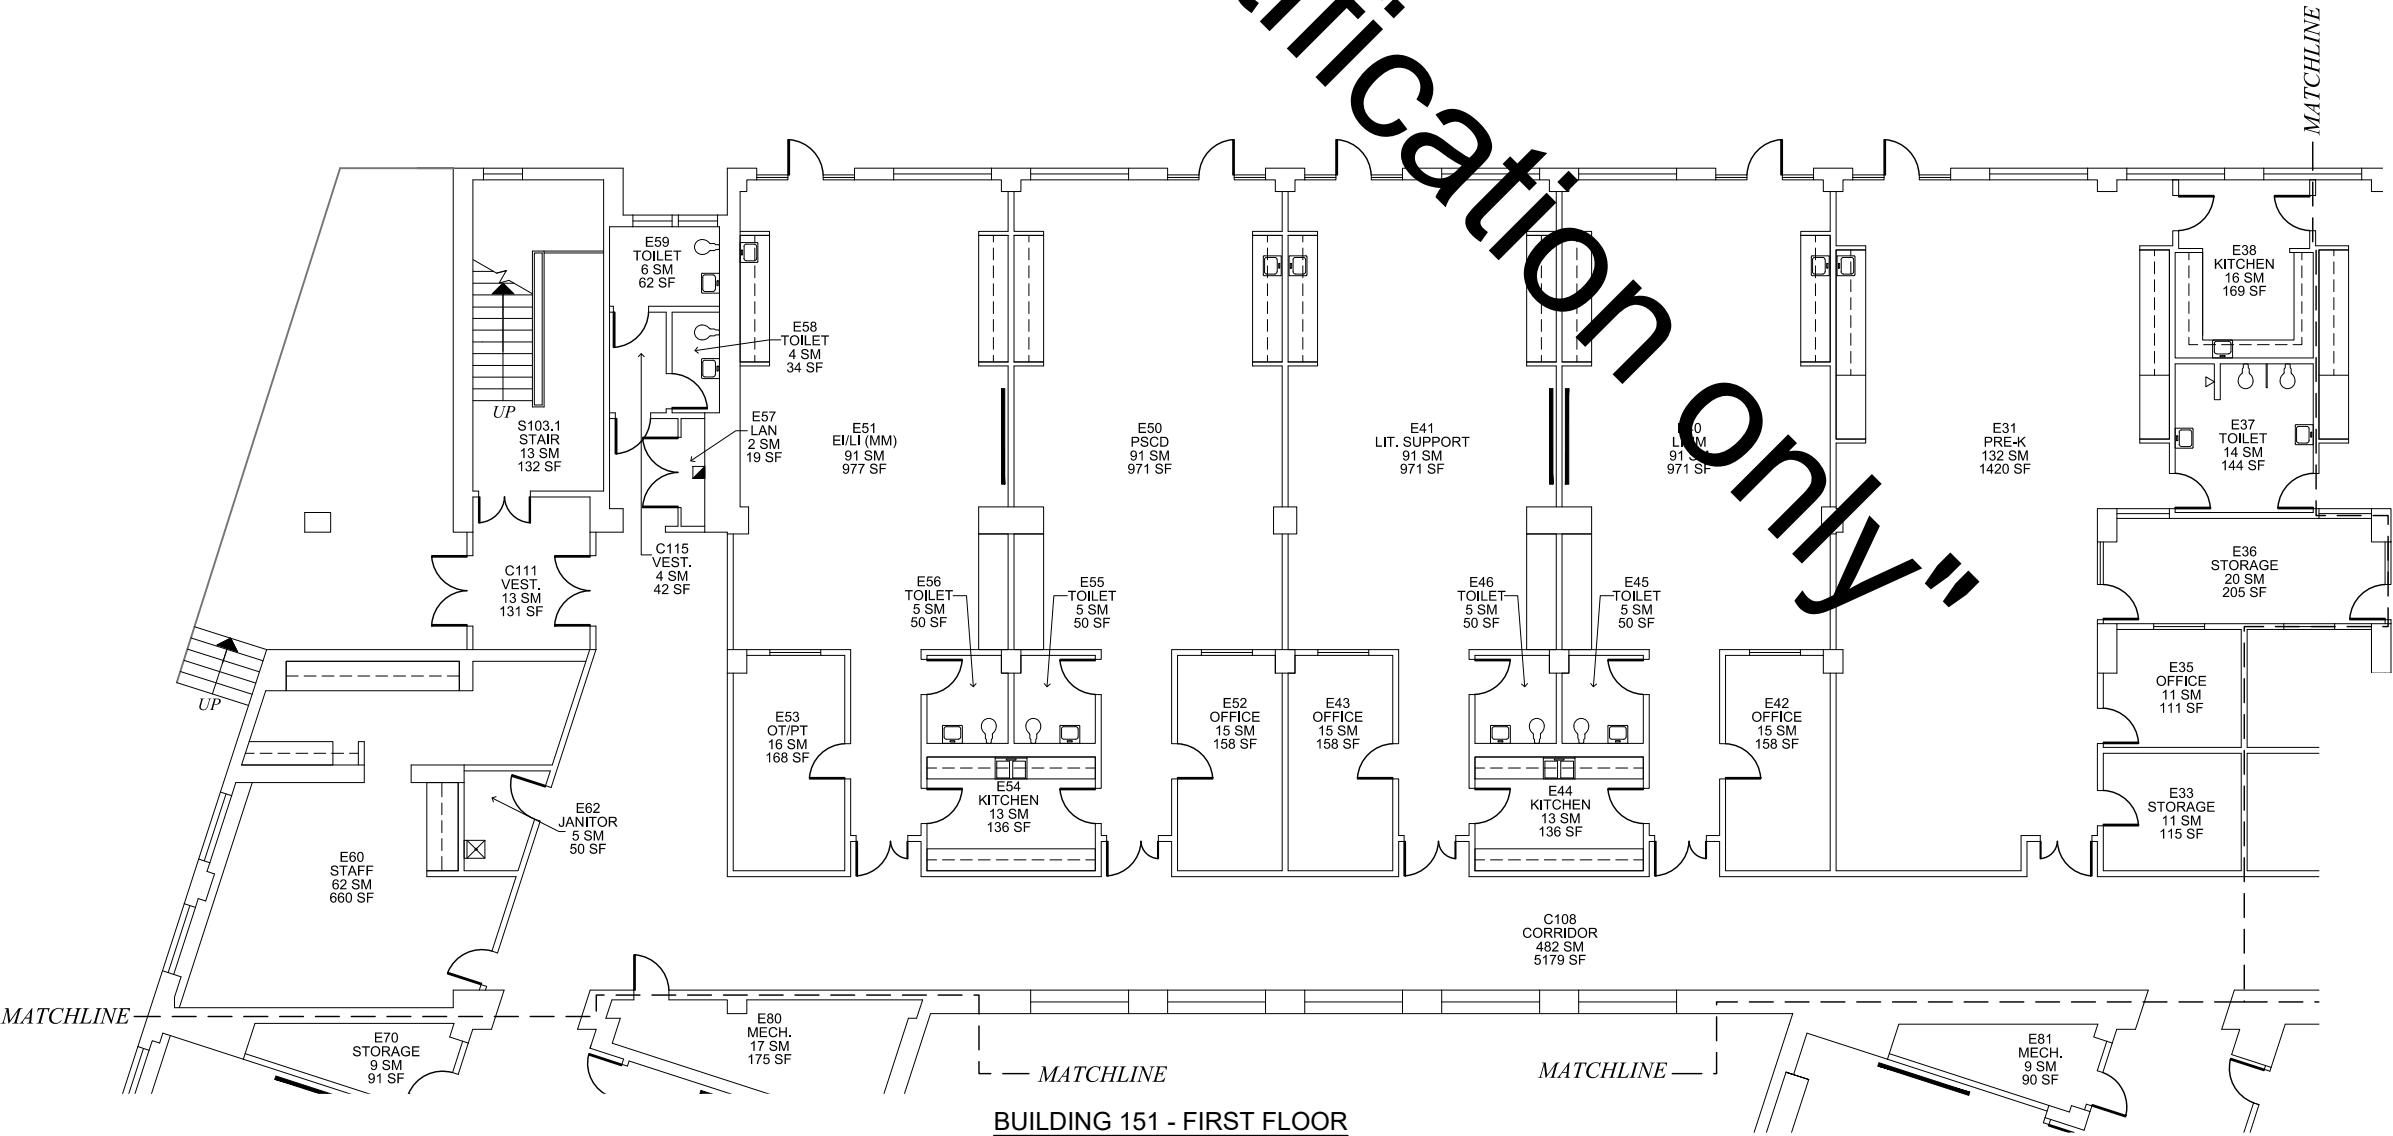

BUILDING 151 - FIRST FLOOR

SYMBOL LEGEND

DOOR	DRINKING FOUNTAIN
SLIDING DOOR	LAVATORY
ACCORDION PARTITION	SINK
STACK OR FOLDING PARTITION	TOILET
WINDOW/GLAZING	URINAL
HIGH WINDOW	LOCKER
SKYLIGHT	LAN DISTRIBUTION FRAME
STOOP/STEP UP	VENT HOOD
STAIR	WALL SHELVING
RAMP	UPPER CABINET
ACCESS LADDER	BASE CABINET
COLD STORAGE	TEACHER CABINET
AREA CALCULATED @ 50 %	MATCHLINE
SLOPING ROOF	FLAT ROOF

TITLEBLOCK LEGEND

SHEET NAME:	BLDG #_FLOOR # (# IN SERIES)
-------------	------------------------------

KEY PLAN

Updated By: SPF

FUS Review: MRS

100% Submittal Date: 01 MAY 2020

0 2 4 8 16 FT

dodeca

DEPARTMENT OF DEFENSE EDUCATION ACTIVITY

FACILITY UTILIZATION SURVEY

AVIANO ELEMENTARY SCHOOL

AVIANO MIDDLE / HIGH SCHOOL

BUILDING NUMBER: 151, 153

COUNTRY: ITALY

INSTALLATION: AVIANO AIR BASE

SITE: AVIANO HOSPITAL-SCHOOL ANNEX

REGION-DISTRICT: DODEA EUROPE SOUTH


DoDAAC Number: HE5649 / HE5603



Floor: LEVEL 1


Survey Date: JANUARY 2020

Sheet Name: 151_1 (2)

Sheet Seq: 12 of 34

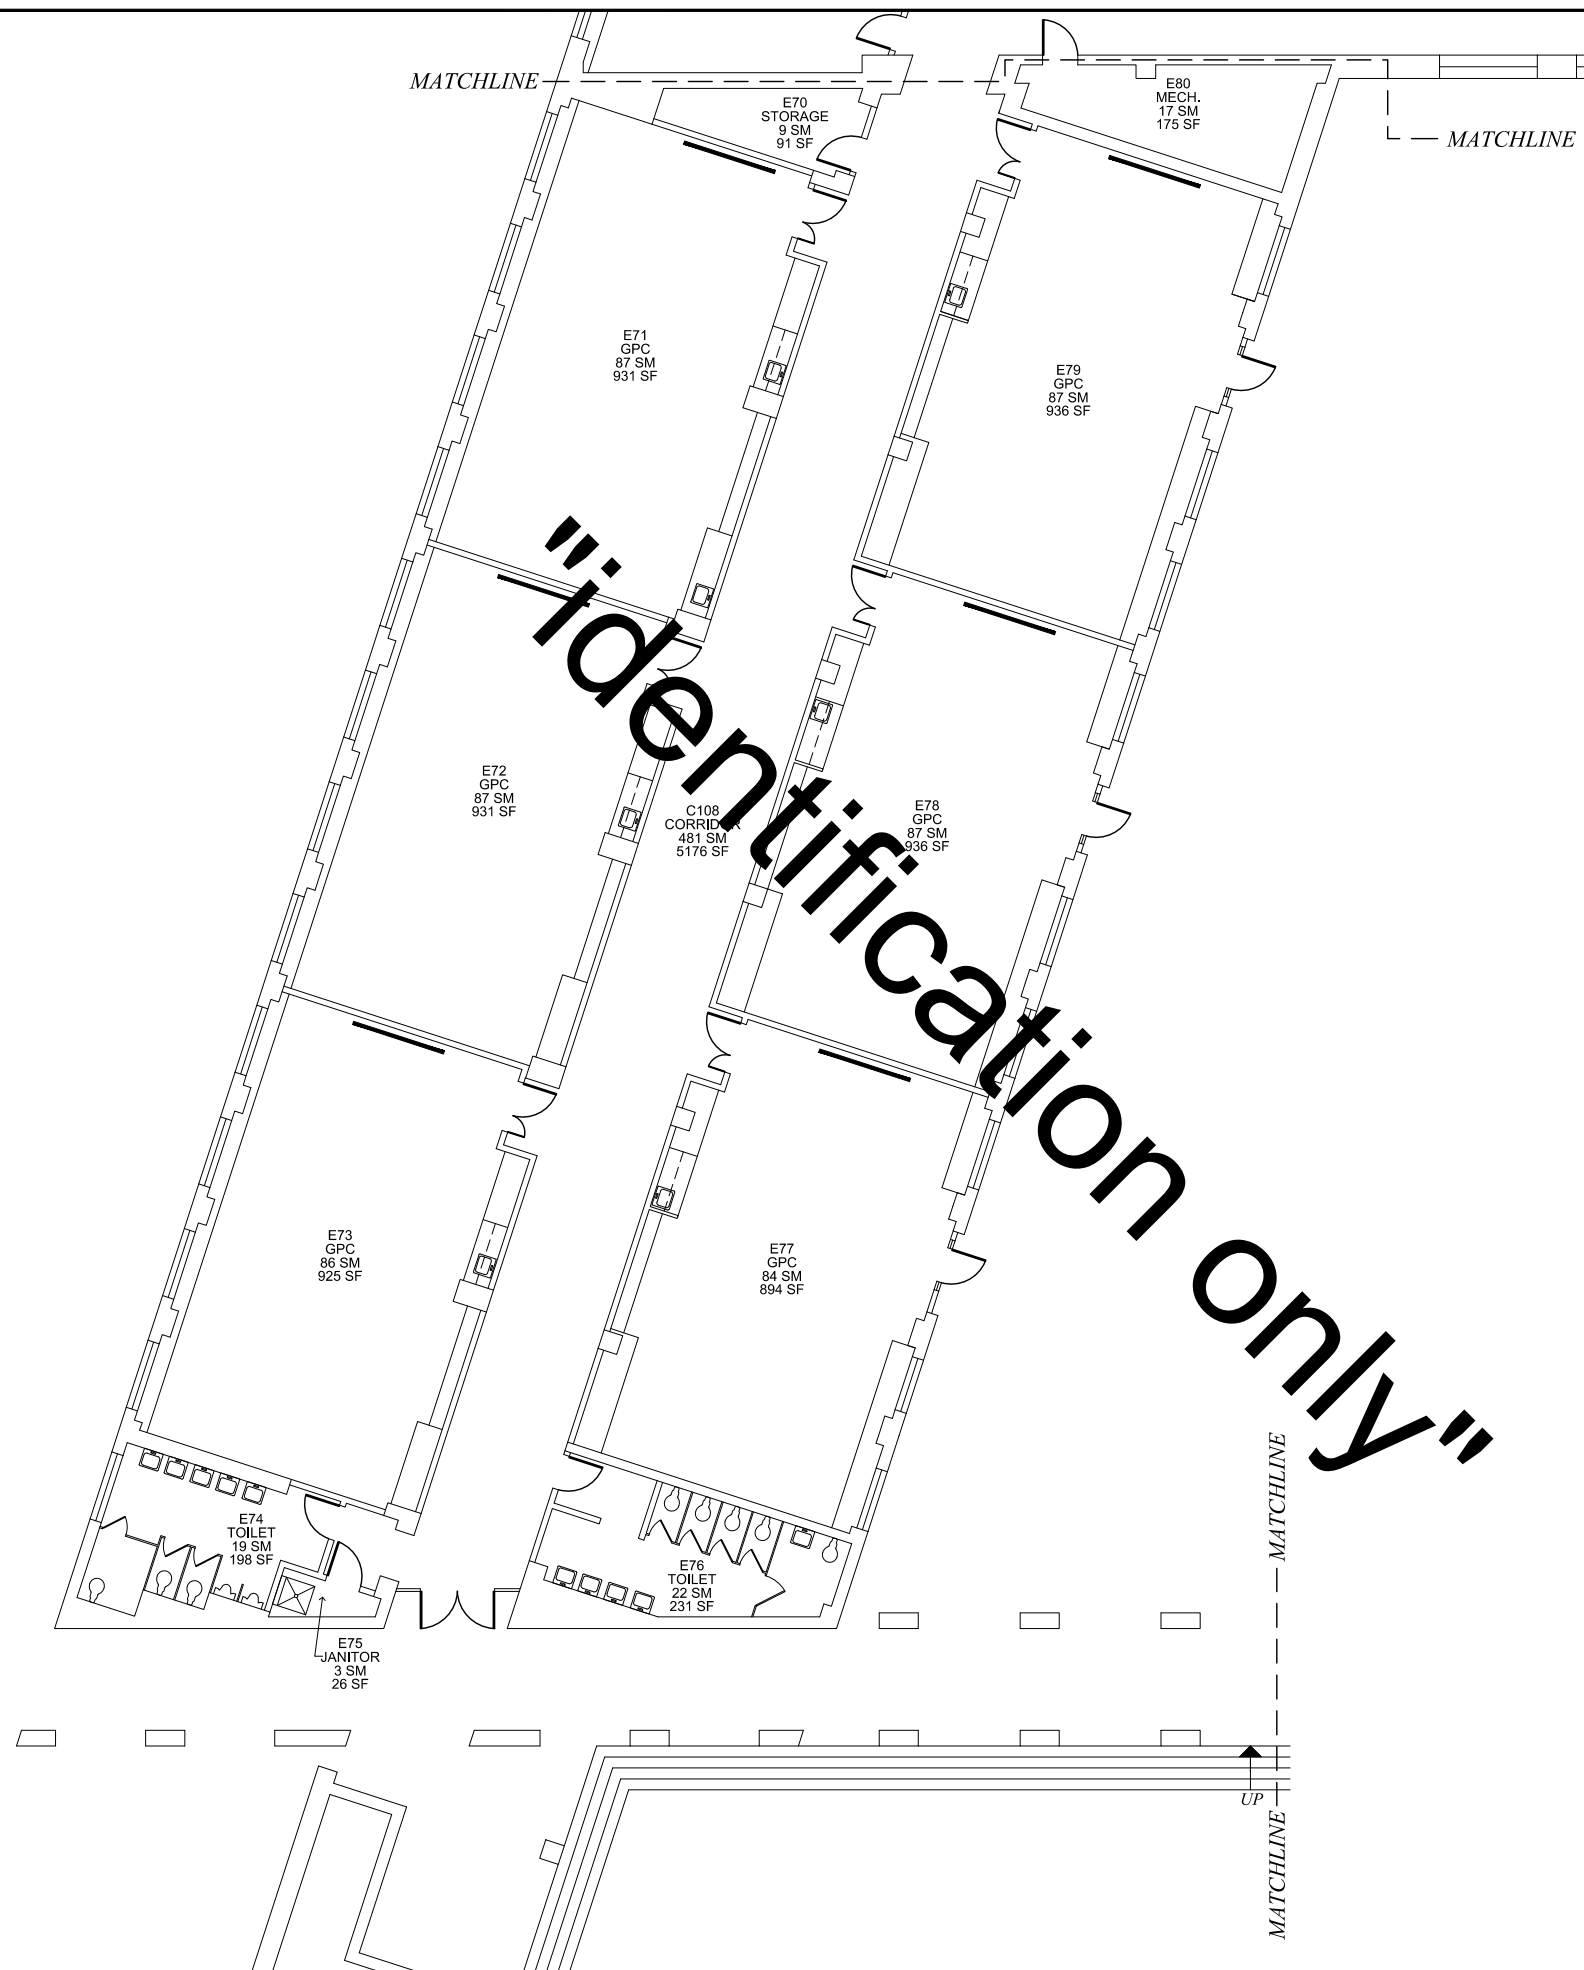


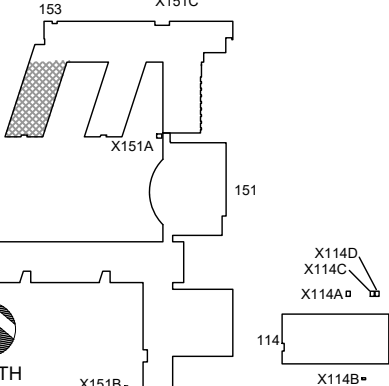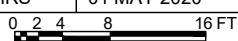SYMBOL LEGEND	
 DOOR	 DRINKING FOUNTAIN
 SLIDING DOOR	 LAVATORY
 ACCORDION PARTITION	 SINK
 STACK OR FOLDING PARTITION	 TOILET
 WINDOW/GLAZING	 URINAL
 HIGH WINDOW	 LOCKER
 SKYLIGHT	 LAN DISTRIBUTION FRAME
 STOOP/STEP UP	 VENT HOOD
 STAIR	 WALL SHELVING
 RAMP	 UPPER CABINET
 ACCESS LADDER	 BASE CABINET
 COLD STORAGE	 TEACHER CABINET
 AREA CALCULATED @ 50 %	 MATCHLINE
 SLOPING ROOF	 FLAT ROOF
TITLEBLOCK LEGEND	
SHEET NAME:	BLDG # FLOOR # (# IN SERIES)
KEY PLAN    NORTH	
Updated By: SPF	FUS Review: MRS
100% Submittal Date: 01 MAY 2020	
	
 DEPARTMENT OF DEFENSE EDUCATION ACTIVITY	
FACILITY UTILIZATION SURVEY	
AVIANO ELEMENTARY SCHOOL AVIANO MIDDLE / HIGH SCHOOL BUILDING NUMBER: 151 COUNTRY: ITALY INSTALLATION: AVIANO AIR BASE SITE: AVIANO HOSPITAL-SCHOOL ANNEX REGION-DISTRICT: DODEA EUROPE SOUTH	
DodaAC Number: HE5649 / HE5603	Floor: LEVEL 1
Survey Date: JANUARY 2020	
Sheet Name: 151_1 (3)	Sheet Seq: 13 of 34

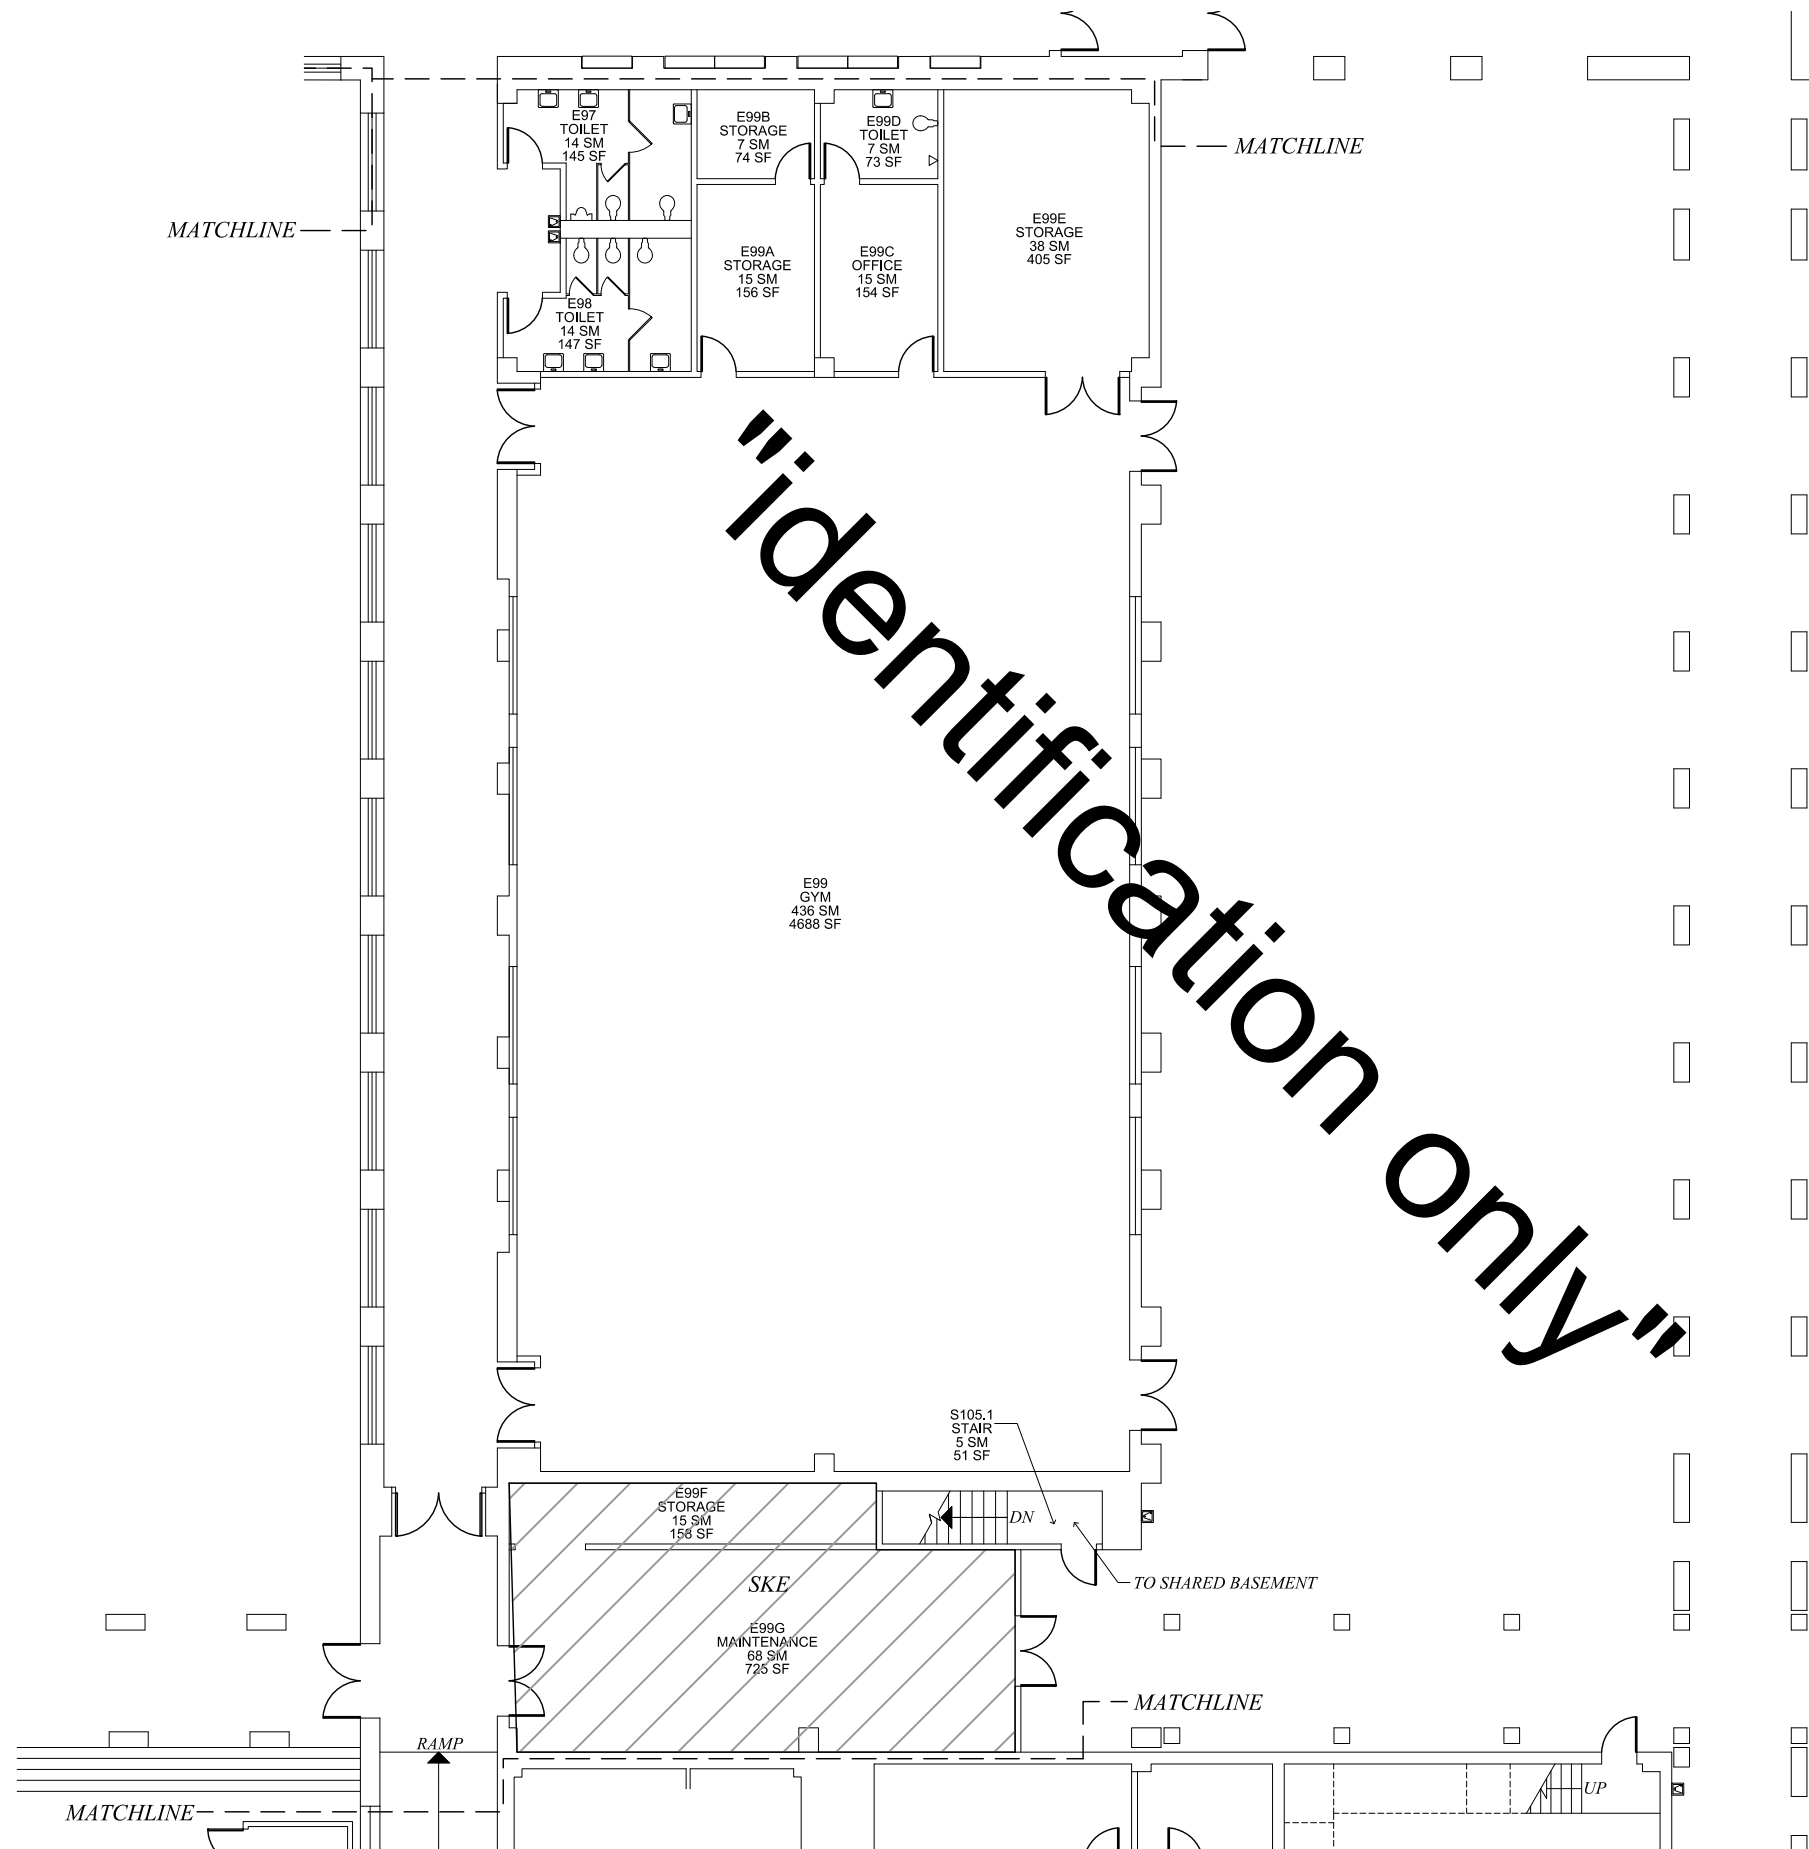

SYMBOL LEGEND	
	DOOR
	DRINKING FOUNTAIN
	SLIDING DOOR
	LAVATORY
	ACCORDION PARTITION
	SINK
	STACK OR FOLDING PARTITION
	TOILET
	WINDOW/GLAZING
	URINAL
	HIGH WINDOW
	LOCKER
	SKYLIGHT
	LAN DISTRIBUTION FRAME
	STOOP/STEP UP
	VENT HOOD
	STAIR
	WALL SHELVING
	RAMP
	UPPER CABINET
	ACCESS LADDER
	BASE CABINET
	COLD STORAGE
	TEACHER CABINET
	AREA CALCULATED @ 50 %
	MATCHLINE
	SLOPING ROOF
	FLAT ROOF

TITLEBLOCK LEGEND	
SHEET NAME:	BLDG #_FLOOR # (# IN SERIES)

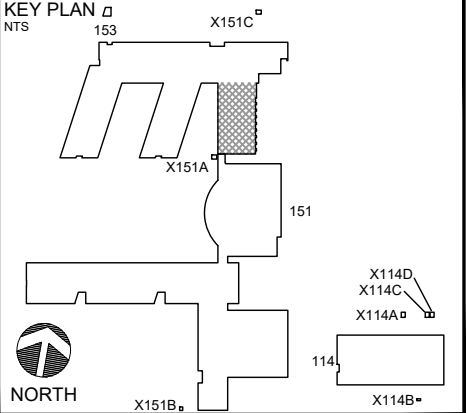


Updated By:	FUS Review:	100% Submittal Date:
SPF	MRS	01 MAY 2020
0 2 4 8 16 FT		

DEPARTMENT OF DEFENSE EDUCATION ACTIVITY
FACILITY UTILIZATION SURVEY


AVIANO ELEMENTARY SCHOOL
AVIANO MIDDLE / HIGH SCHOOL
BUILDING NUMBER: 151
COUNTRY: ITALY
INSTALLATION: AVIANO AIR BASE
SITE: AVIANO HOSPITAL-SCHOOL ANNEX
REGION-DISTRICT: DODEA EUROPE SOUTH

DoDAAC Number:	Floor:	Survey Date:
HE5649 / HE5603	LEVEL 1	JANUARY 2020
Sheet Name:	Sheet Seq:	
151_1 (5)	15 of 34	

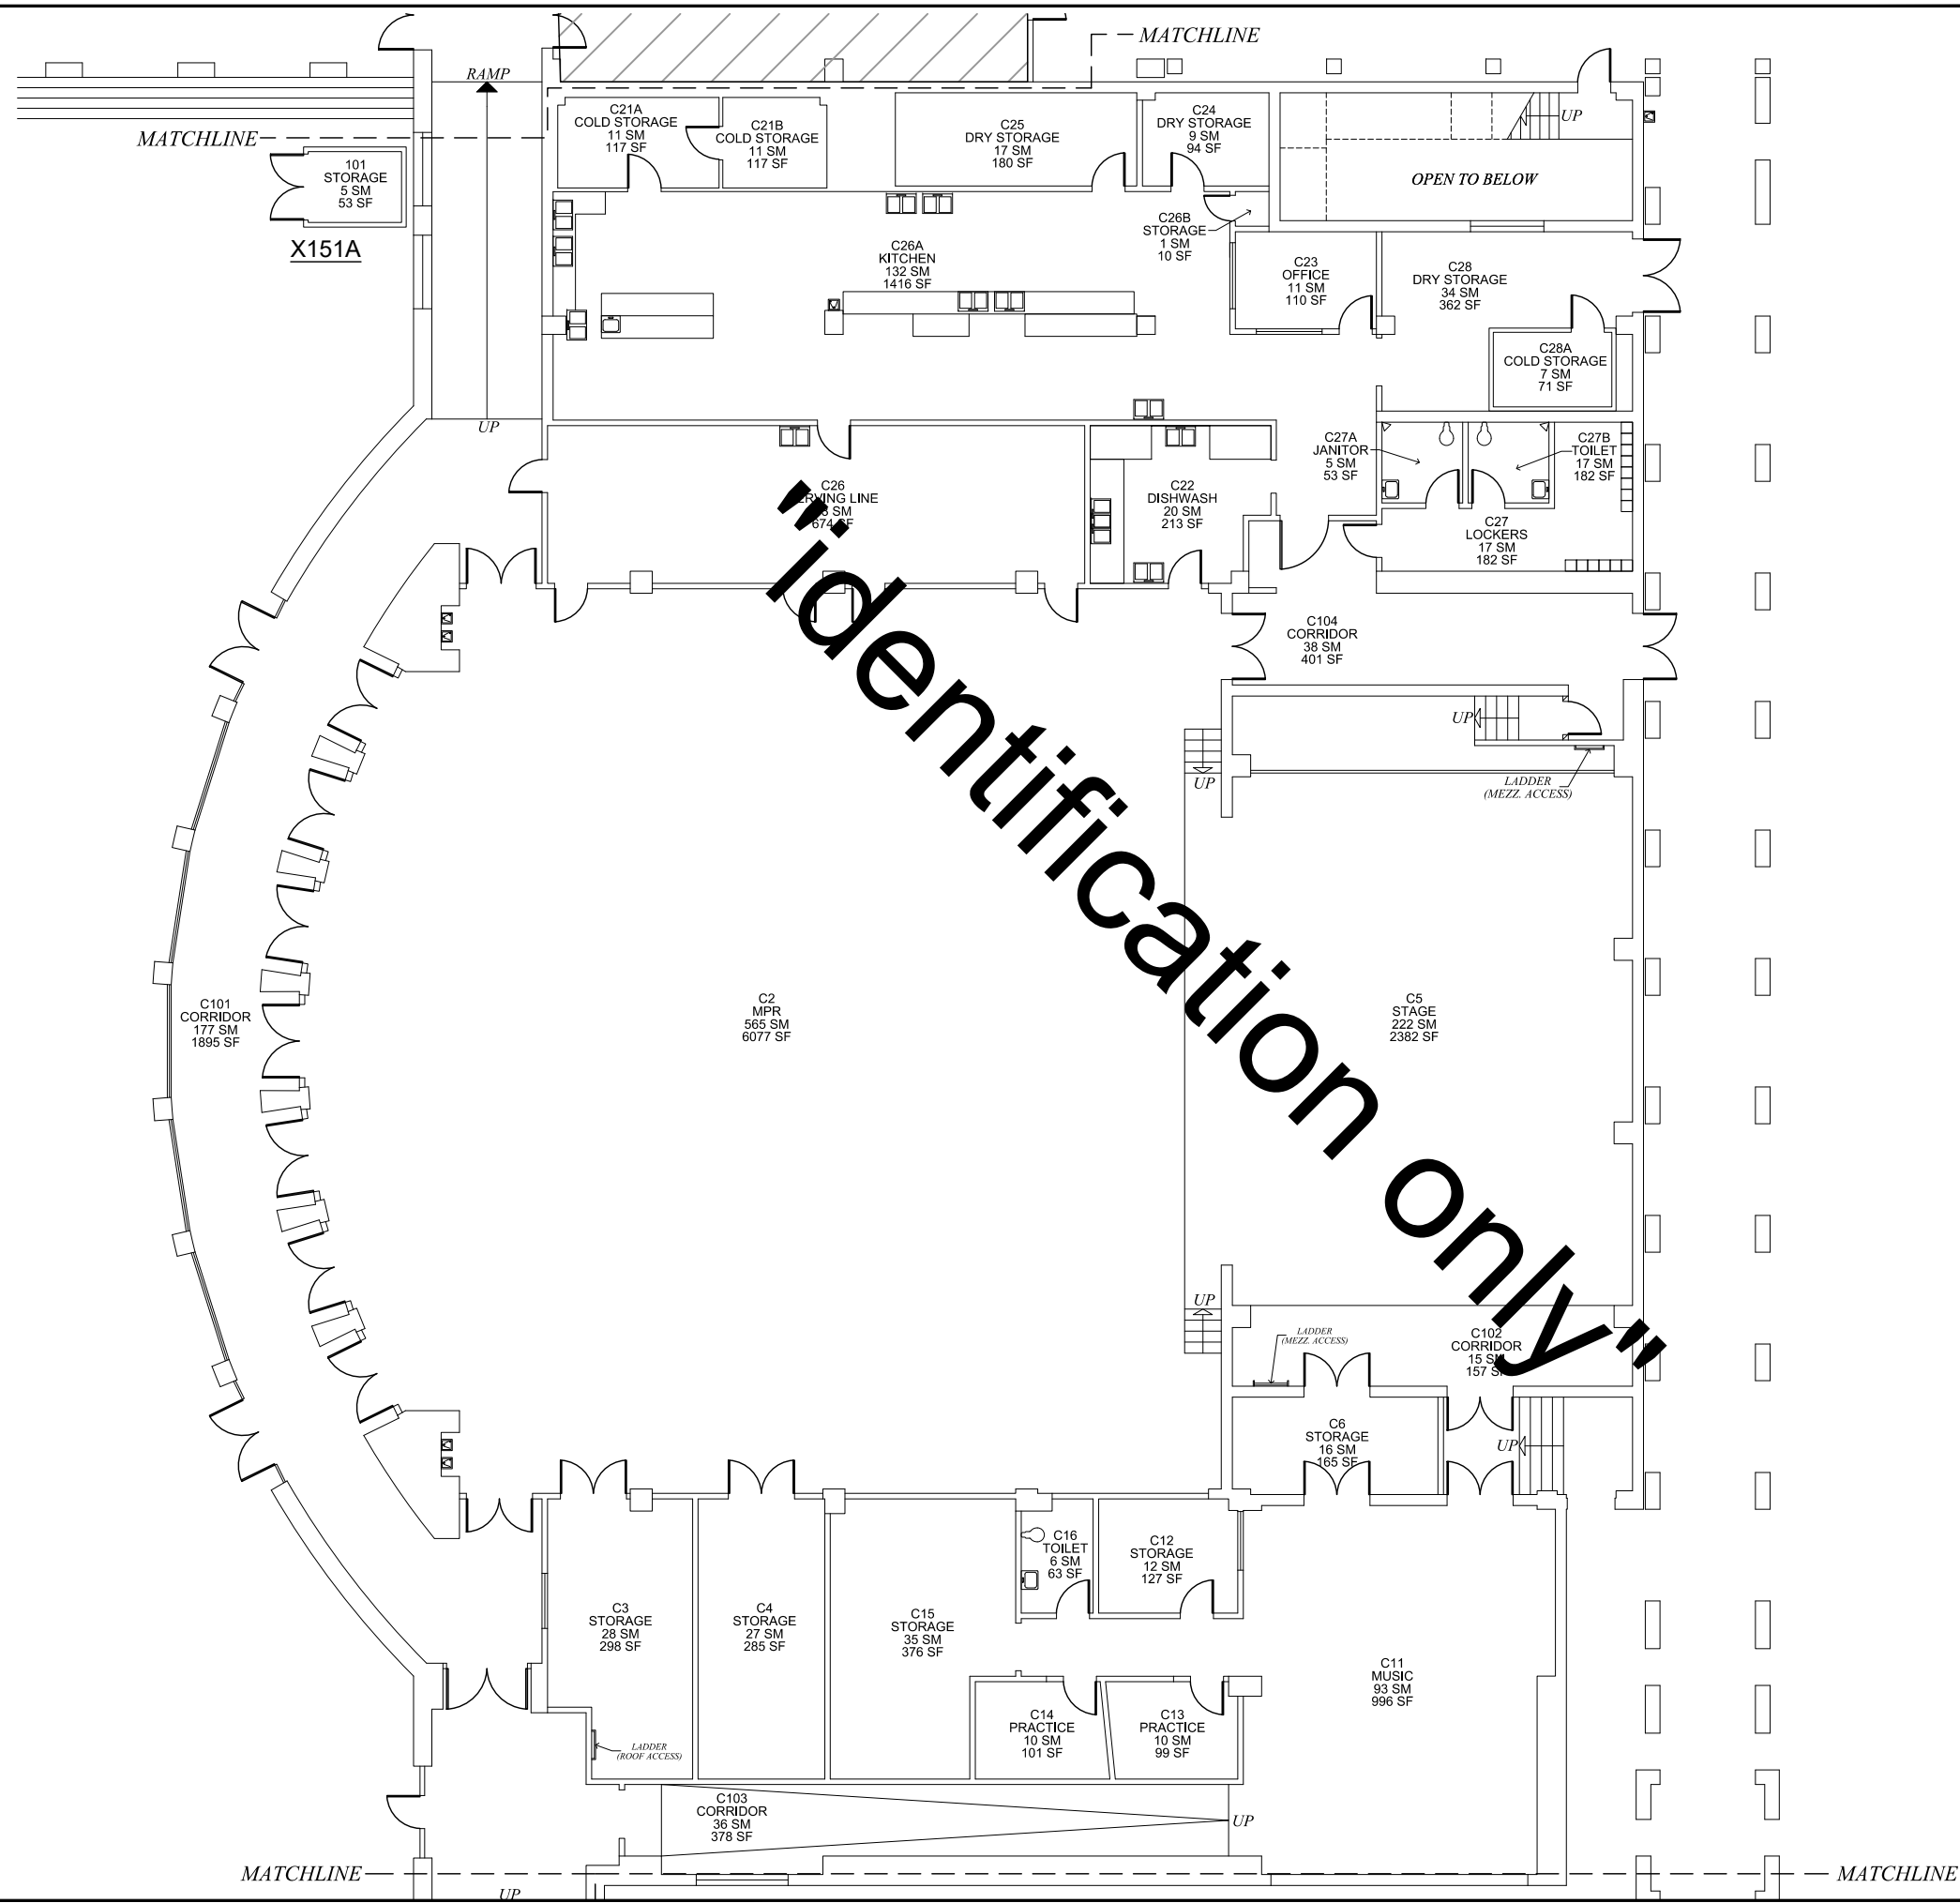

SYMBOL LEGEND	
	DOOR
	DRINKING FOUNTAIN
	SLIDING DOOR
	LAVATORY
	ACCORDION PARTITION
	SINK
	STACK OR FOLDING PARTITION
	TOILET
	WINDOW/GLAZING
	URINAL
	HIGH WINDOW
	LOCKER
	SKYLIGHT
	LAN DISTRIBUTION FRAME
	STOOP/STEP UP
	VENT HOOD
	STAIR
	WALL SHELVING
	RAMP
	UPPER CABINET
	ACCESS LADDER
	BASE CABINET
	COLD STORAGE
	TEACHER CABINET
	AREA CALCULATED @ 50 %
	MATCHLINE
	SLOPING ROOF
	FLAT ROOF

TITLEBLOCK LEGEND	
SHEET NAME:	BLDG #_FLOOR # (# IN SERIES)

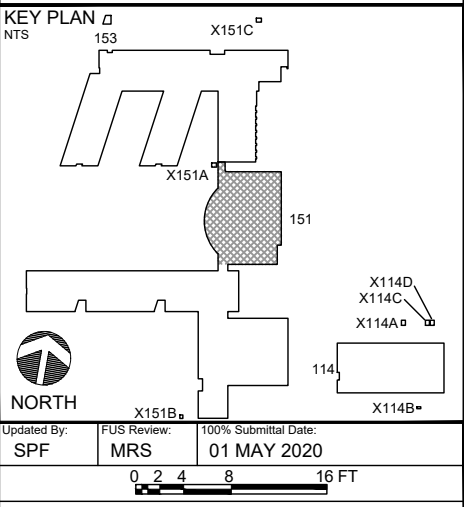


DEPARTMENT OF DEFENSE EDUCATION ACTIVITY

FACILITY UTILIZATION SURVEY

AVIANO ELEMENTARY SCHOOL
AVIANO MIDDLE / HIGH SCHOOL

BUILDING NUMBER: 151, X151A
COUNTRY: ITALY
INSTALLATION: AVIANO AIR BASE
SITE: AVIANO HOSPITAL-SCHOOL ANNEX
REGION-DISTRICT: DODEA EUROPE SOUTH

DoDAAC Number: HE5649 / HE5603	Floor: LEVEL 1	Survey Date: JANUARY 2020
Sheet Name: 151_1 (6)	Sheet Seq:	16 of 34

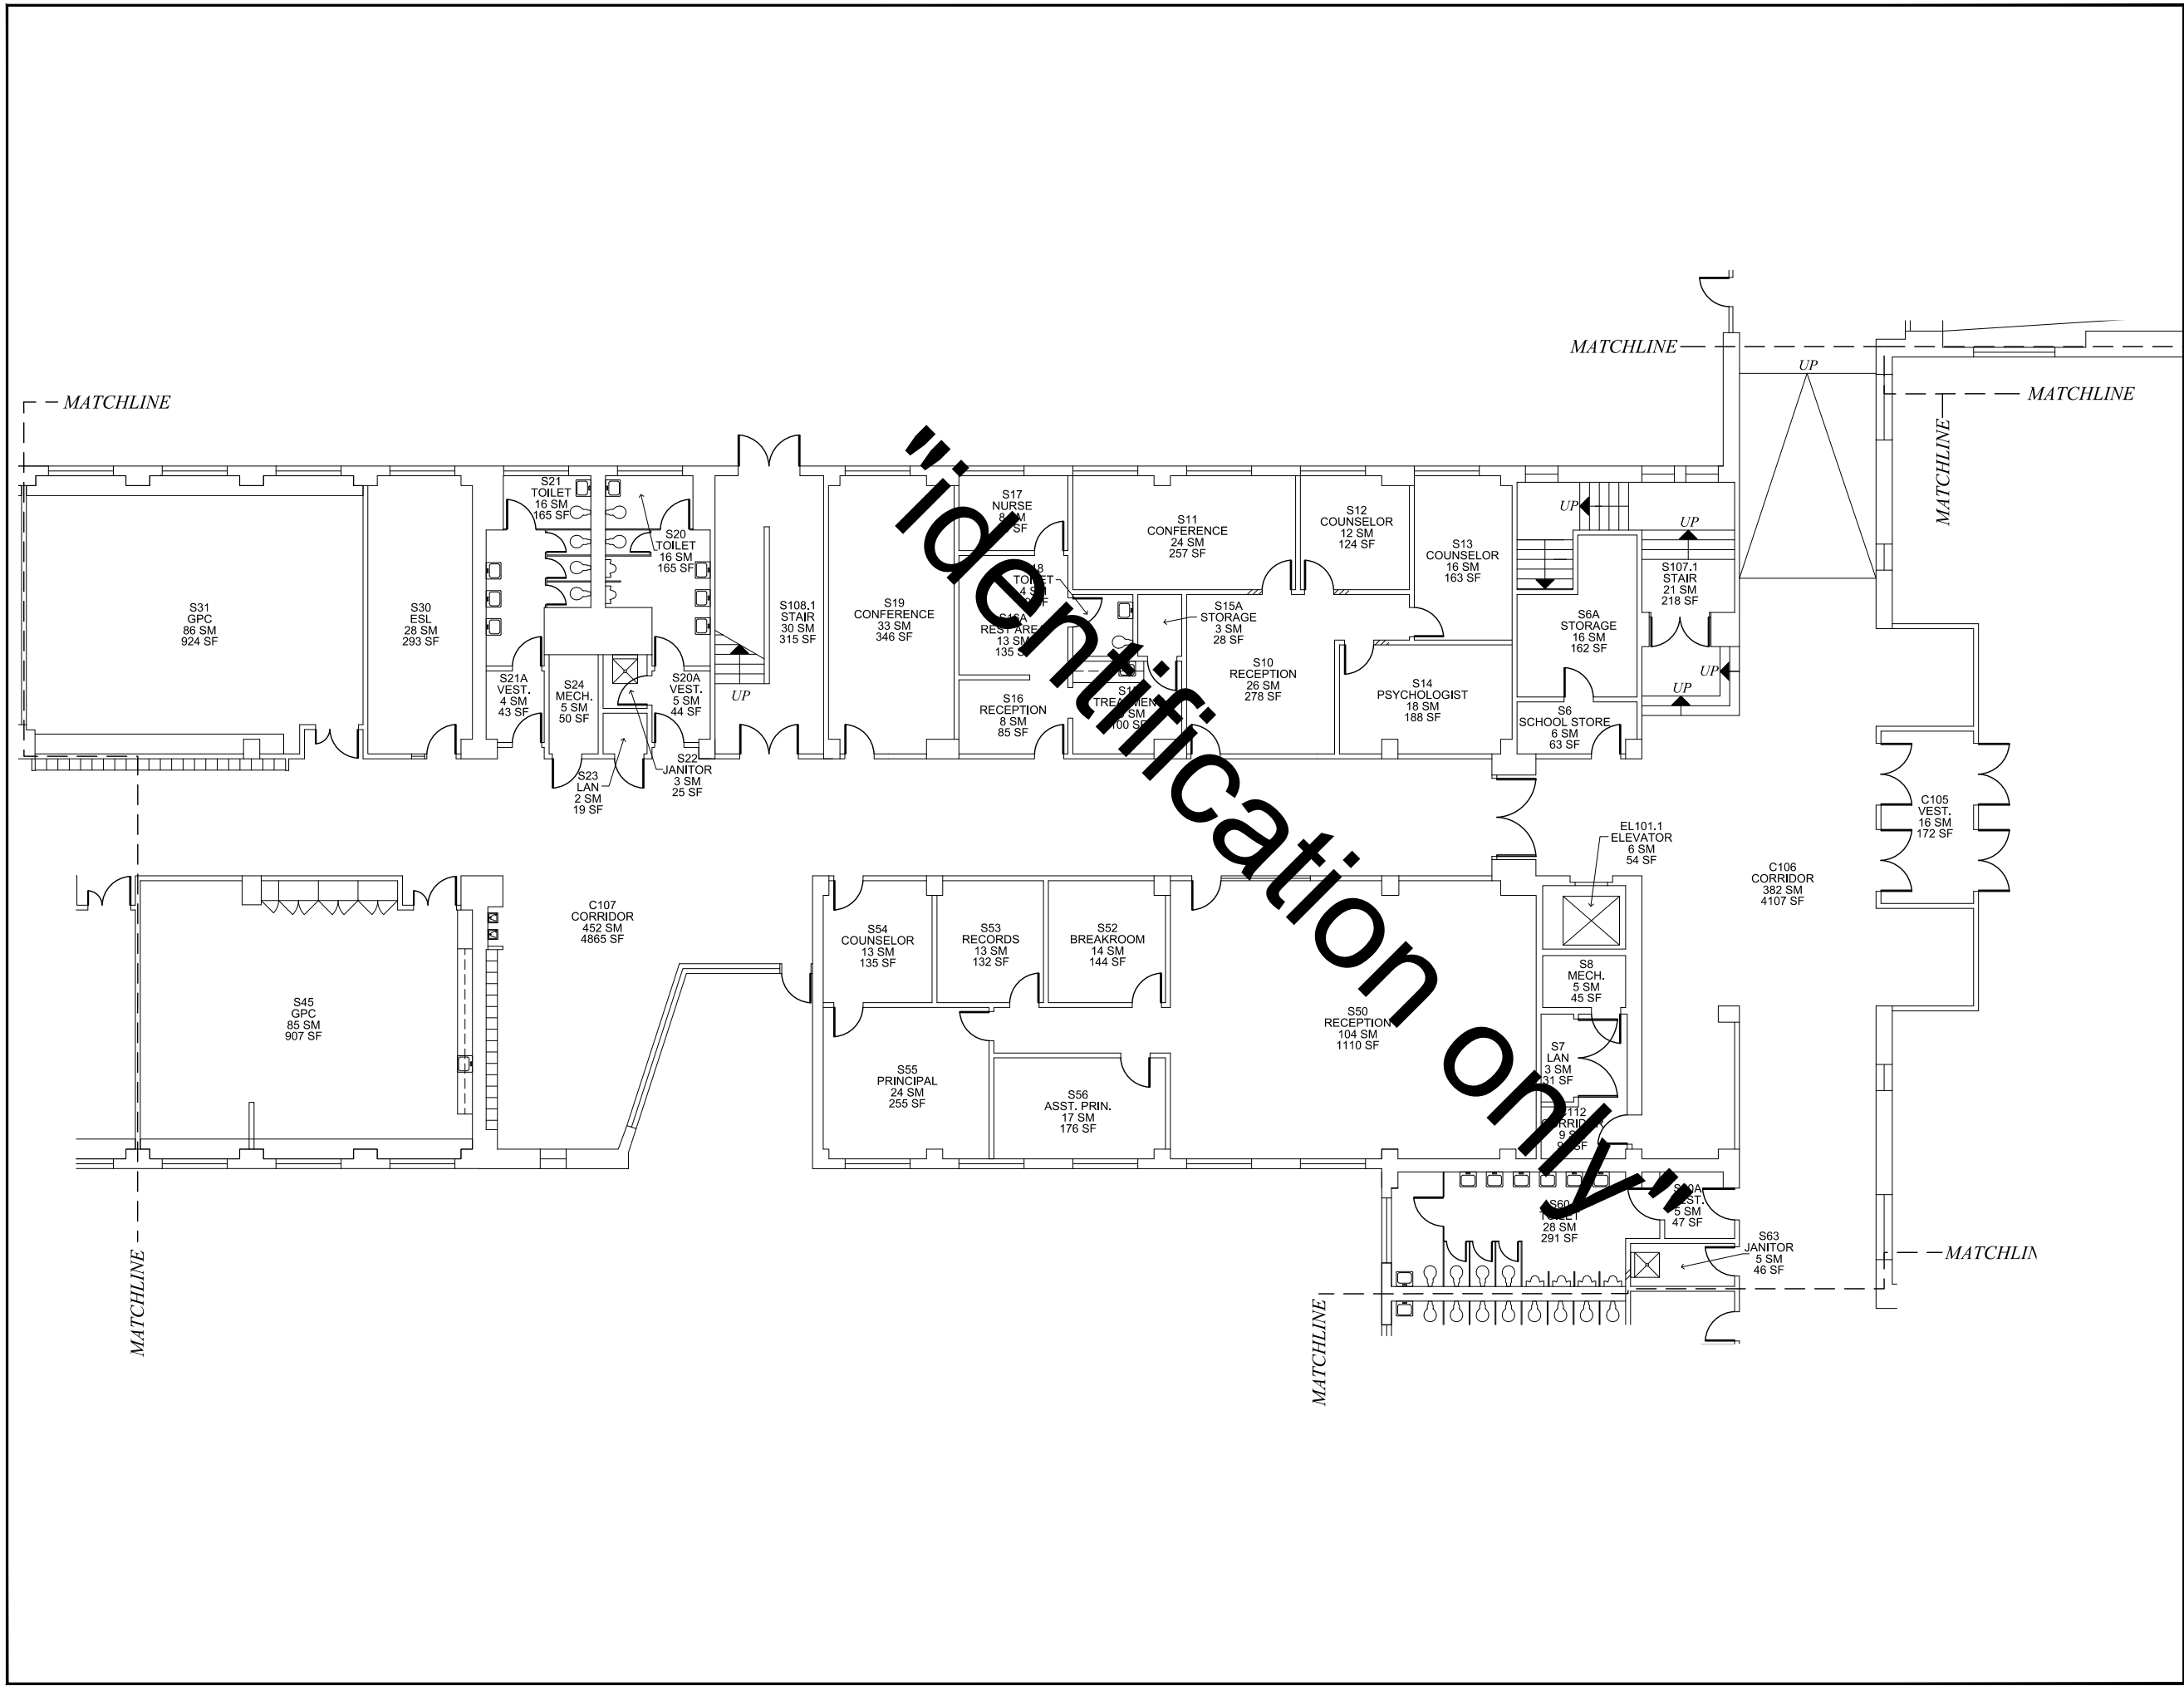

DOOR

SLIDING DOOR

ACCORDION PARTITION

STACK OR FOLDING PARTITION

WINDOW/GLAZING

HIGH WINDOW

SKYLIGHT

STOOP/STEP UP

STAIR

RAMP

ACCESS LADDER

COLD STORAGE

AREA CALCULATED @ 50 %

SLOPING ROOF

DRINKING FOUNTAIN

LAVATORY

SINK

TOILET

URINAL

LOCKER

LAN DISTRIBUTION FRAME

VENT HOOD

WALL SHELVING

UPPER CABINET

BASE CABINET

TEACHER CABINET

MATCHLINE

FLAT ROOF

TITLEBLOCK LEGEND

SHEET NAME:

BLDG #_FLOOR # (# IN SERIES)

KEY PLAN

NTS

153

X151C

X151A

151

X114D

X114C

X114A

114

X151B

X114B

NORTH

Updated By: SPF

FUS Review: MRS

100% Submittal Date: 01 MAY 2020

0 2 4 8 16 FT

dodea

DEPARTMENT OF DEFENSE EDUCATION ACTIVITY

FACILITY UTILIZATION SURVEY

AVIANO ELEMENTARY SCHOOL

AVIANO MIDDLE / HIGH SCHOOL

BUILDING NUMBER: 151

COUNTRY: ITALY

INSTALLATION: AVIANO AIR BASE

SITE: AVIANO HOSPITAL-SCHOOL ANNEX

REGION-DISTRICT: DODEA EUROPE SOUTH


DoDAAC Number: HE5649 / HE5603

Floor: LEVEL 1

Survey Date: JANUARY 2020


Sheet Name: 151_1 (7)

Sheet Seq: 17 of 34

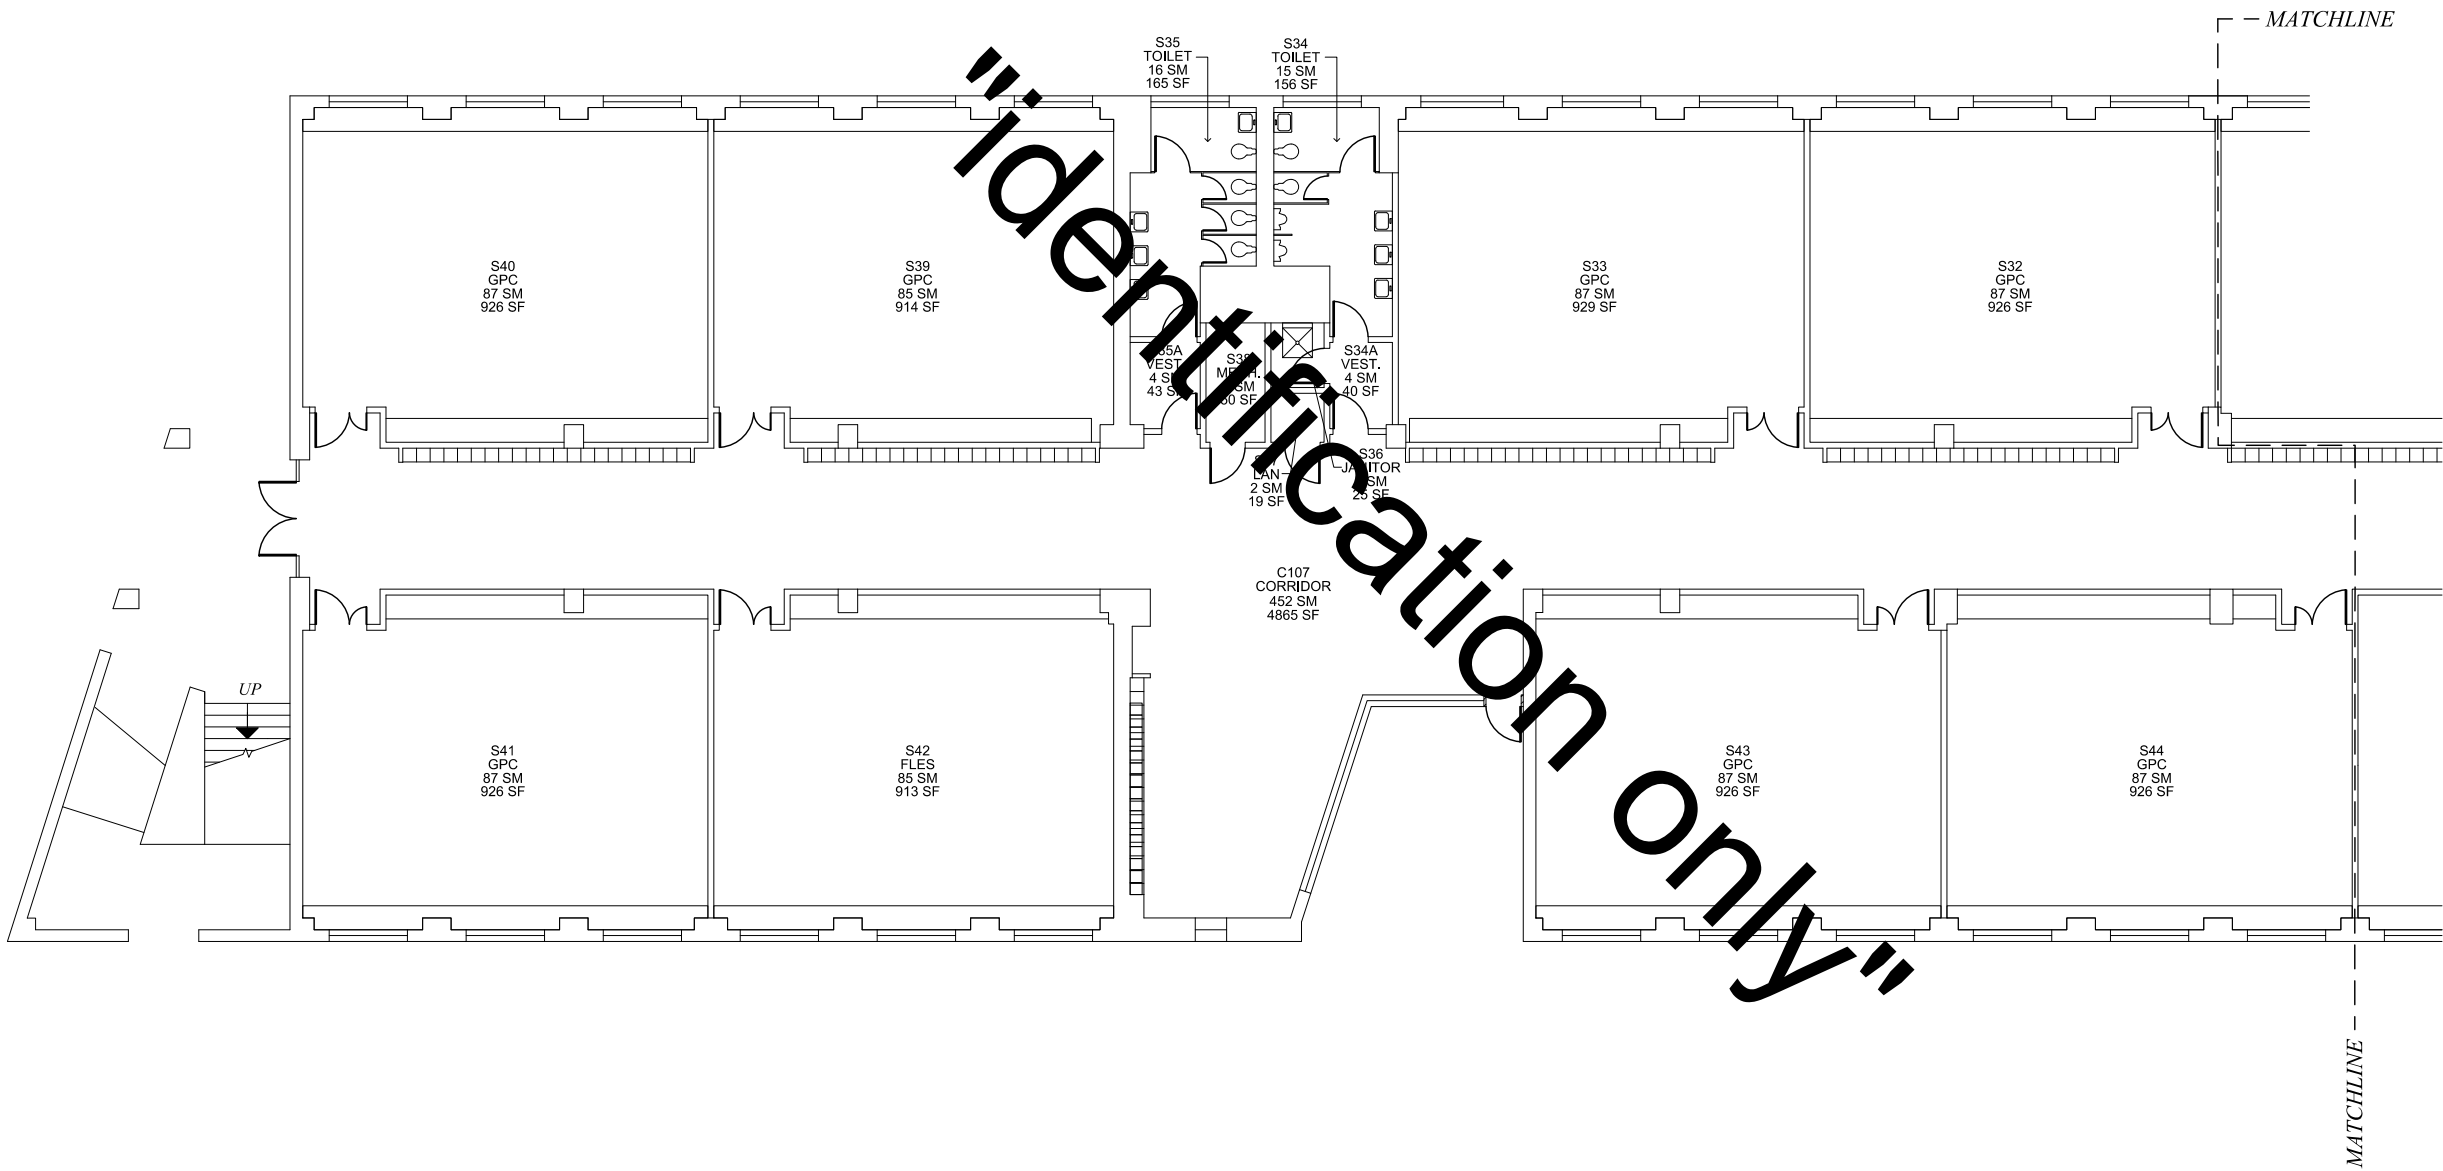


SYMBOL LEGEND	
	DOOR
	DRINKING FOUNTAIN
	SLIDING DOOR
	LAVATORY
	ACCORDION PARTITION
	SINK
	STACK OR FOLDING PARTITION
	TOILET
	WINDOW/GLAZING
	URINAL
	HIGH WINDOW
	LOCKER
	SKYLIGHT
	LAN DISTRIBUTION FRAME
	STOOP/STEP UP
	VENT HOOD
	STAIR
	WALL SHELVING
	RAMP
	UPPER CABINET
	ACCESS LADDER
	BASE CABINET
	COLD STORAGE
	TEACHER CABINET
	AREA CALCULATED @ 50 %
	MATCHLINE
	SLOPING ROOF
	FLAT ROOF

TITLEBLOCK LEGEND	
SHEET NAME:	BLDG #_ FLOOR # (# IN SERIES)

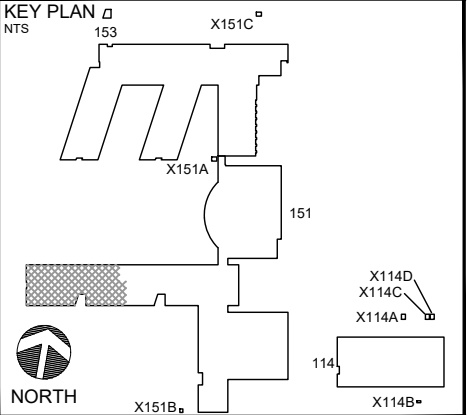

Updated By: SPF	FUS Review: MRS	100% Submittal Date: 01 MAY 2020
0 2 4 8 16 FT		
DEPARTMENT OF DEFENSE EDUCATION ACTIVITY FACILITY UTILIZATION SURVEY		
AVIANO ELEMENTARY SCHOOL AVIANO MIDDLE / HIGH SCHOOL BUILDING NUMBER: 151 COUNTRY: ITALY INSTALLATION: AVIANO AIR BASE SITE: AVIANO HOSPITAL-SCHOOL ANNEX REGION-DISTRICT: DODEA EUROPE SOUTH		
DoDAAC Number: HE5649 / HE5603	Floor: LEVEL 1	Survey Date: JANUARY 2020
Sheet Name: 151_1 (8)		Sheet Seq: 18 of 34

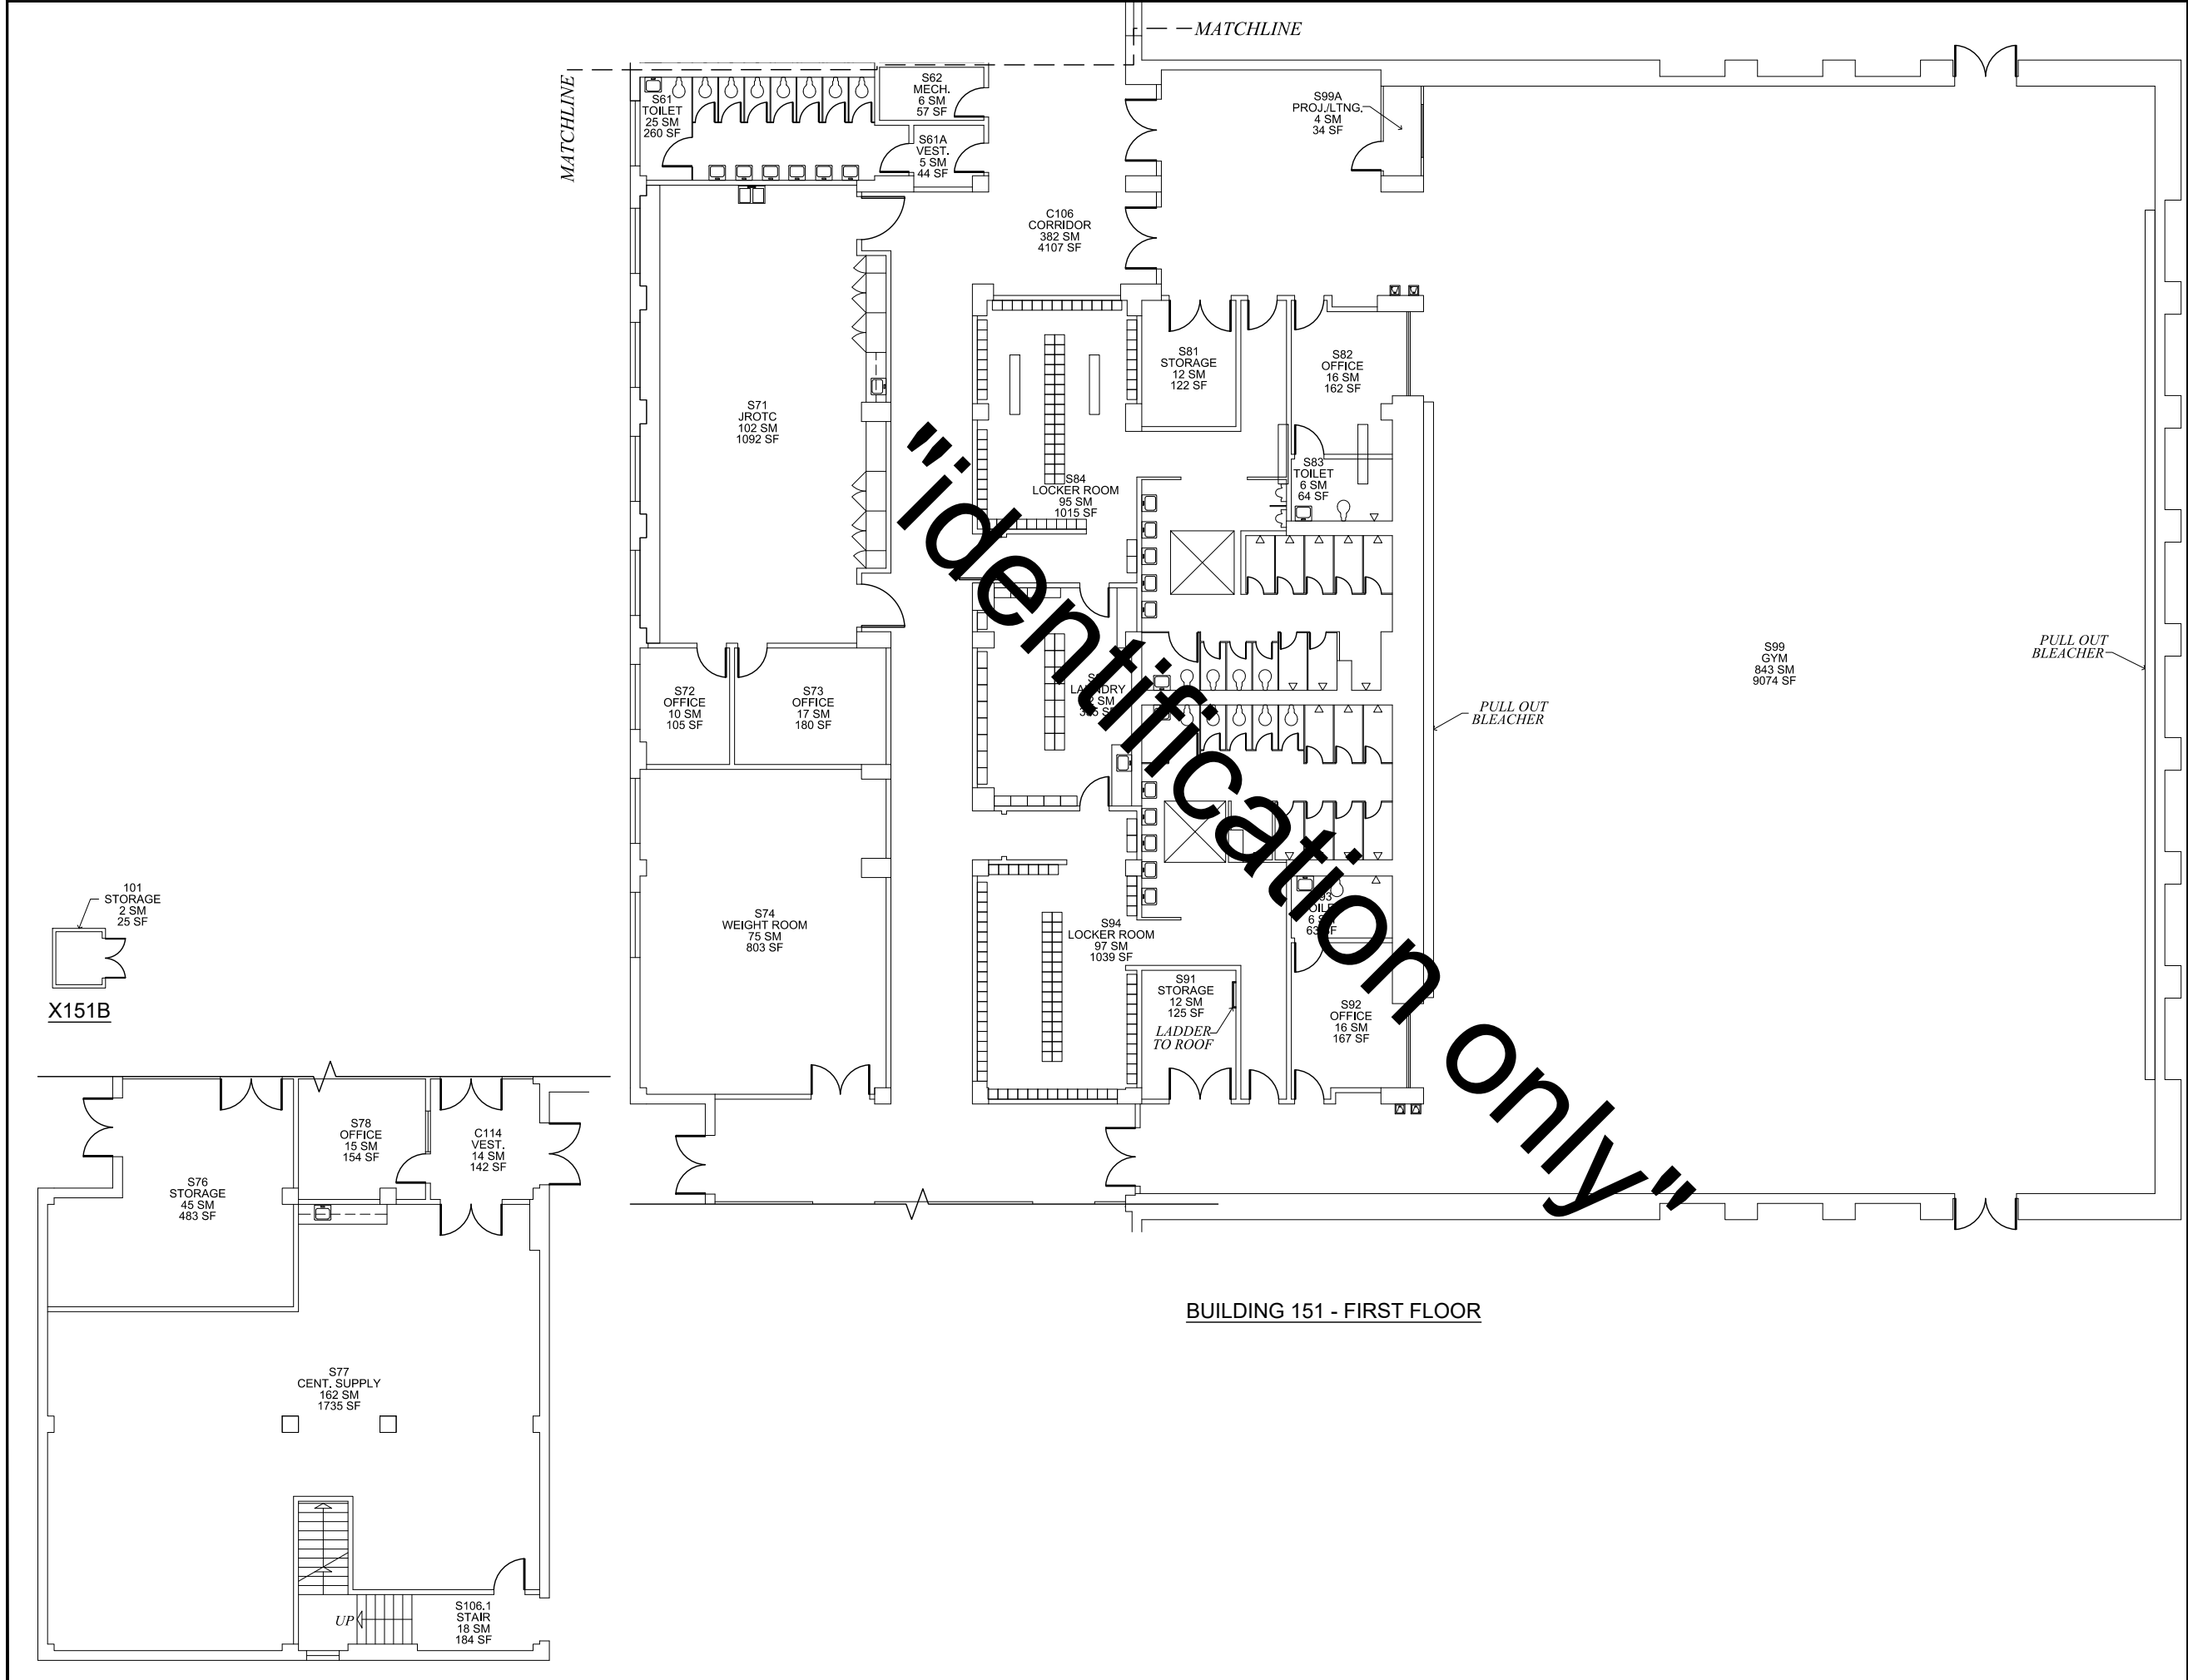

BUILDING 151 - FIRST FLOOR

DOOR

SLIDING DOOR

ACCORDION PARTITION

STACK OR FOLDING PARTITION

WINDOW/GLAZING

HIGH WINDOW

SKYLIGHT

STOOP/STEP UP

STAIR

RAMP

ACCESS LADDER

COLD STORAGE

AREA CALCULATED @ 50 %

SLOPING ROOF

DRINKING FOUNTAIN

LAVATORY

SINK

TOILET

URINAL

LOCKER

LAN DISTRIBUTION FRAME

VENT HOOD

WALL SHELVING

UPPER CABINET

BASE CABINET

TEACHER CABINET

MATCHLINE

FLAT ROOF

TITLEBLOCK LEGEND

SHEET NAME:

BLDG #_FLOOR # (# IN SERIES)

KEY PLAN

NTS

153

X151C

X151A

151

X114D

X114C

X114A

114

X151B

X114B

NORTH

Updated By: SPF

FUS Review: MRS

100% Submittal Date: 01 MAY 2020

0 2 4 8 16 FT

dodea

DEPARTMENT OF DEFENSE EDUCATION ACTIVITY

FACILITY UTILIZATION SURVEY

AVIANO ELEMENTARY SCHOOL

AVIANO MIDDLE / HIGH SCHOOL

BUILDING NUMBER: 151, X151B

COUNTRY: ITALY

INSTALLATION: AVIANO AIR BASE

SITE: AVIANO HOSPITAL-SCHOOL ANNEX

REGION-DISTRICT: DODEA EUROPE SOUTH


DoDAAC Number: HE5649 / HE5603

Floor: LEVEL 1

Survey Date: JANUARY 2020

Sheet Name: 151_1 (9)

Sheet Seq: 19 of 34

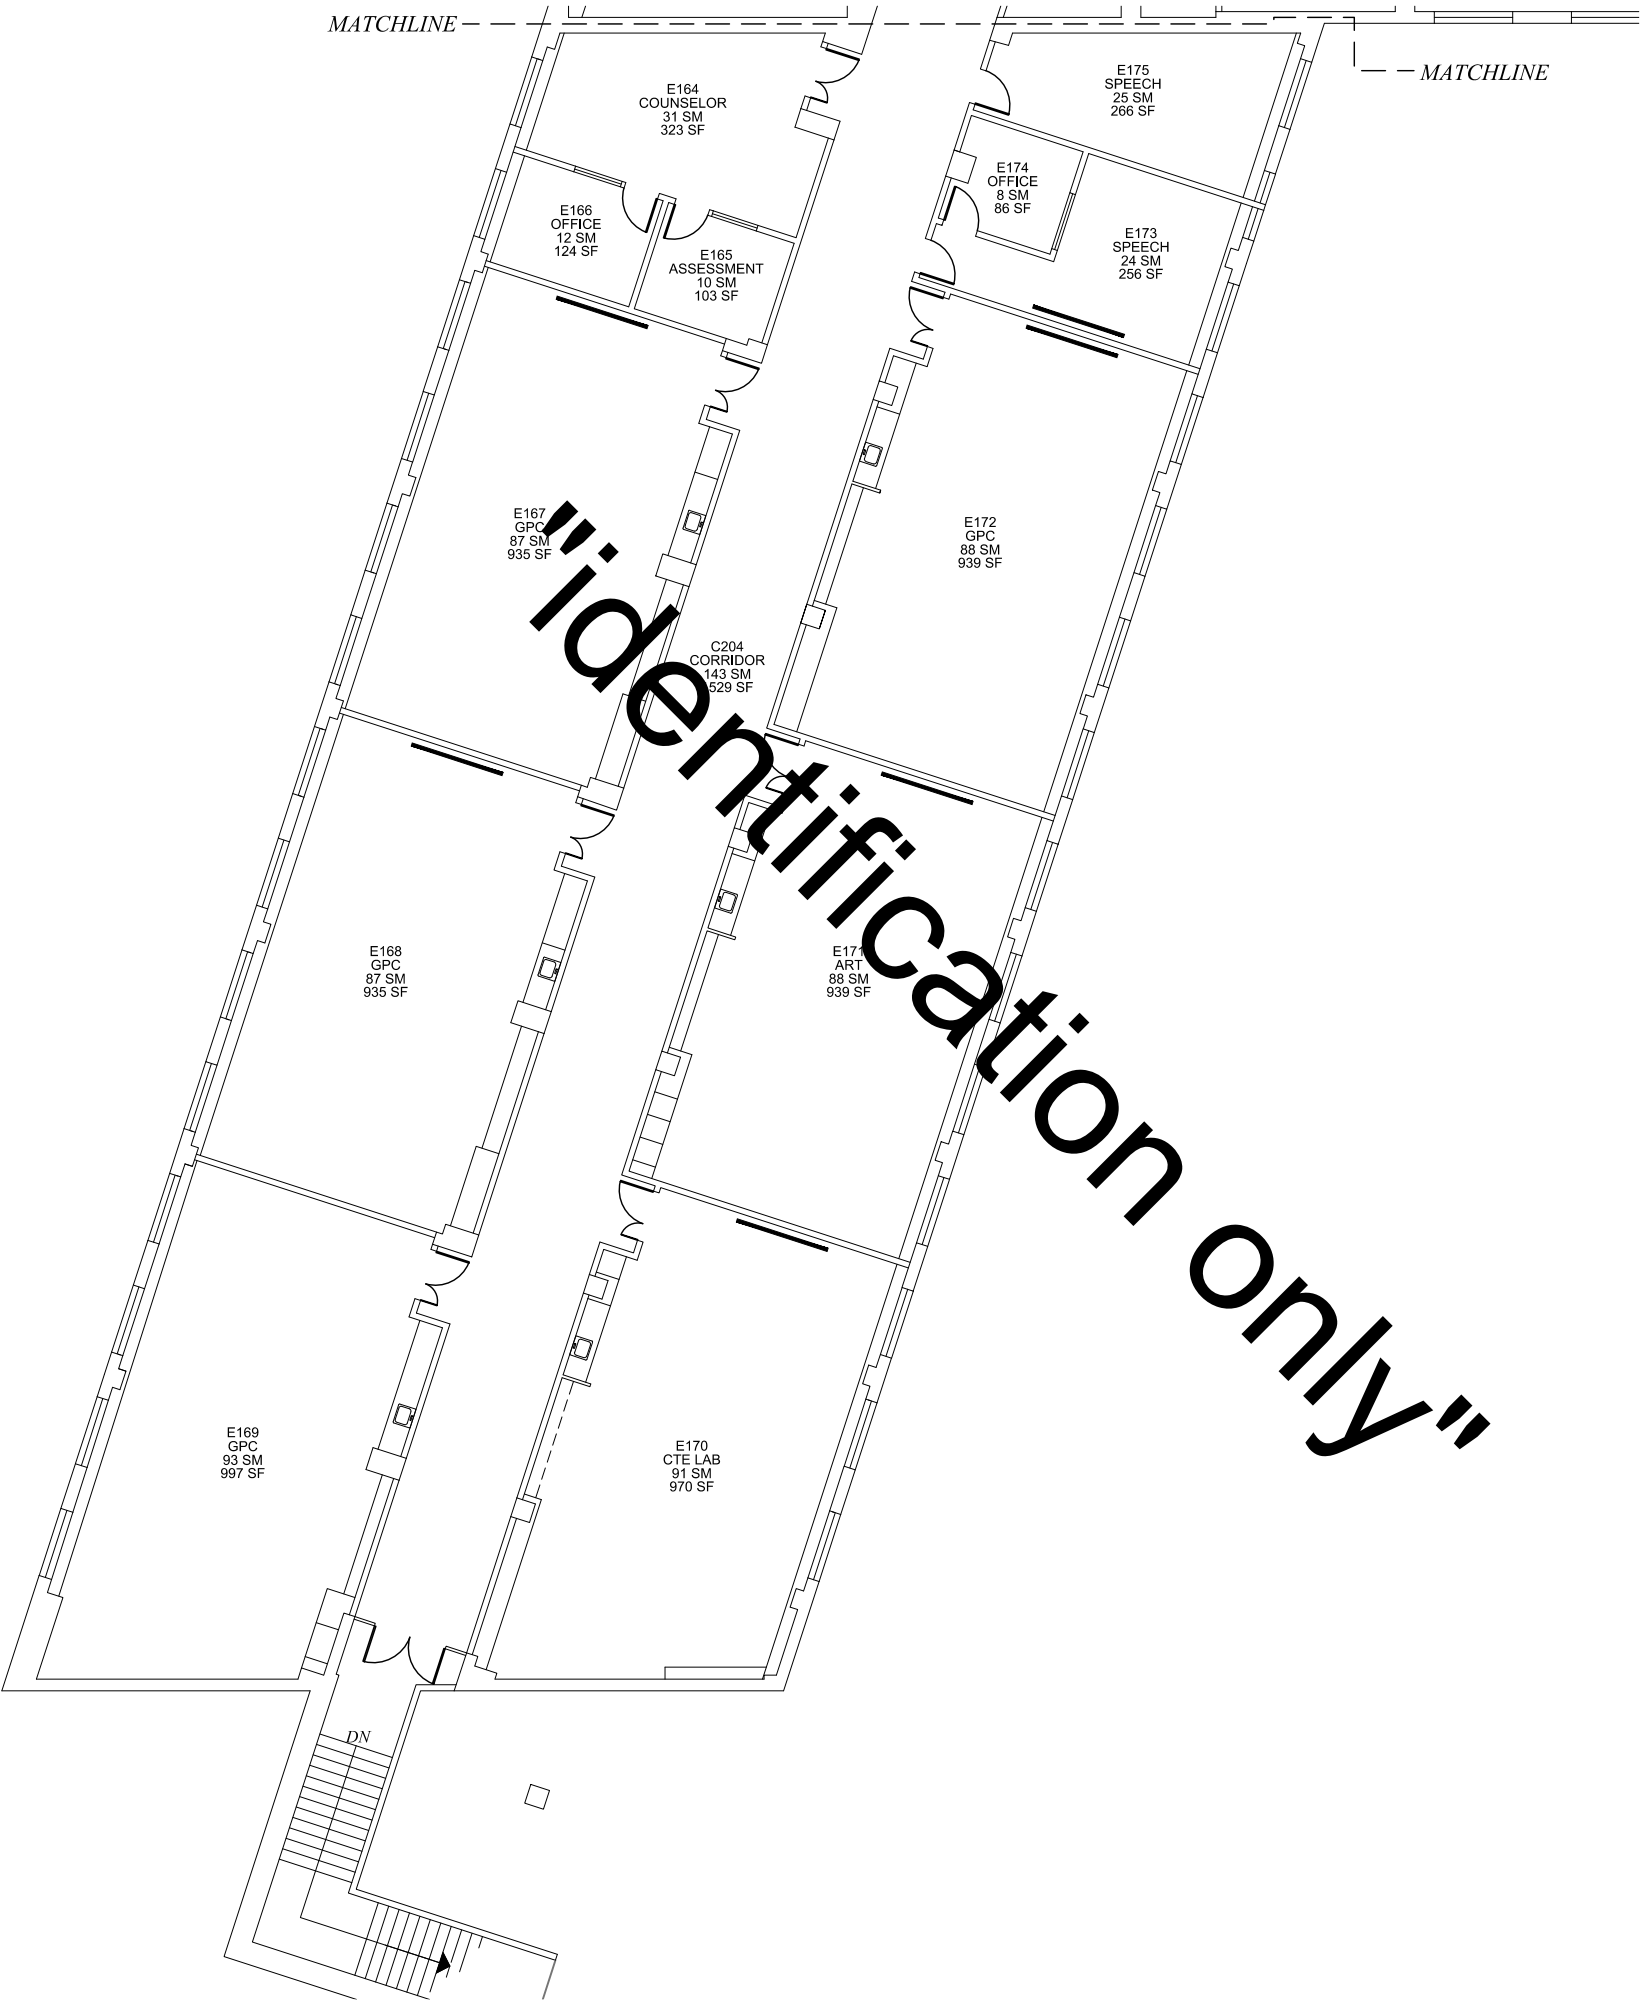

DOOR

DRINKING FOUNTAIN

SLIDING DOOR

LAVATORY

ACCORDION PARTITION

SINK

STACK OR FOLDING PARTITION

TOILET

WINDOW/GLAZING

URINAL

HIGH WINDOW

LOCKER

SKYLIGHT

LAN DISTRIBUTION FRAME

STOOP/STEP UP

VENT HOOD

STAIR

WALL SHELVING

RAMP

UPPER CABINET

ACCESS LADDER

BASE CABINET

COLD STORAGE

TEACHER CABINET

AREA CALCULATED @ 50 %

MATCHLINE

SLOPING ROOF

FLAT ROOF


TITLEBLOCK LEGEND

SHEET NAME:

BLDG #_FLOOR # (# IN SERIES)

KEY PLAN

NTS

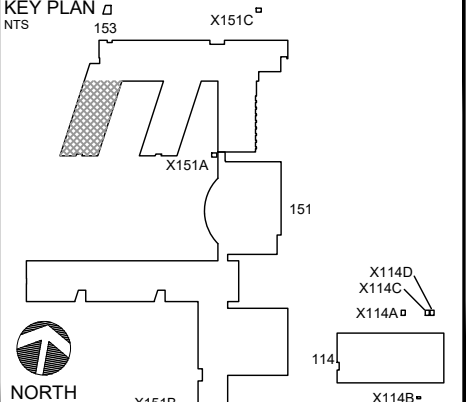

Updated By: SPF

FUS Review: MRS

100% Submittal Date: 01 MAY 2020

0 2 4 8 16 FT

dodea

DEPARTMENT OF DEFENSE EDUCATION ACTIVITY

FACILITY UTILIZATION SURVEY

AVIANO ELEMENTARY SCHOOL

AVIANO MIDDLE / HIGH SCHOOL

BUILDING NUMBER: 151

COUNTRY: ITALY

INSTALLATION: AVIANO AIR BASE

SITE: AVIANO HOSPITAL-SCHOOL ANNEX

REGION-DISTRICT: DODEA EUROPE SOUTH


DoDAAC Number: HE5649 / HE5603

Floor: LEVEL 2

Survey Date: JANUARY 2020

Sheet Name: 151_2 (1)

Sheet Seq: 20 of 34

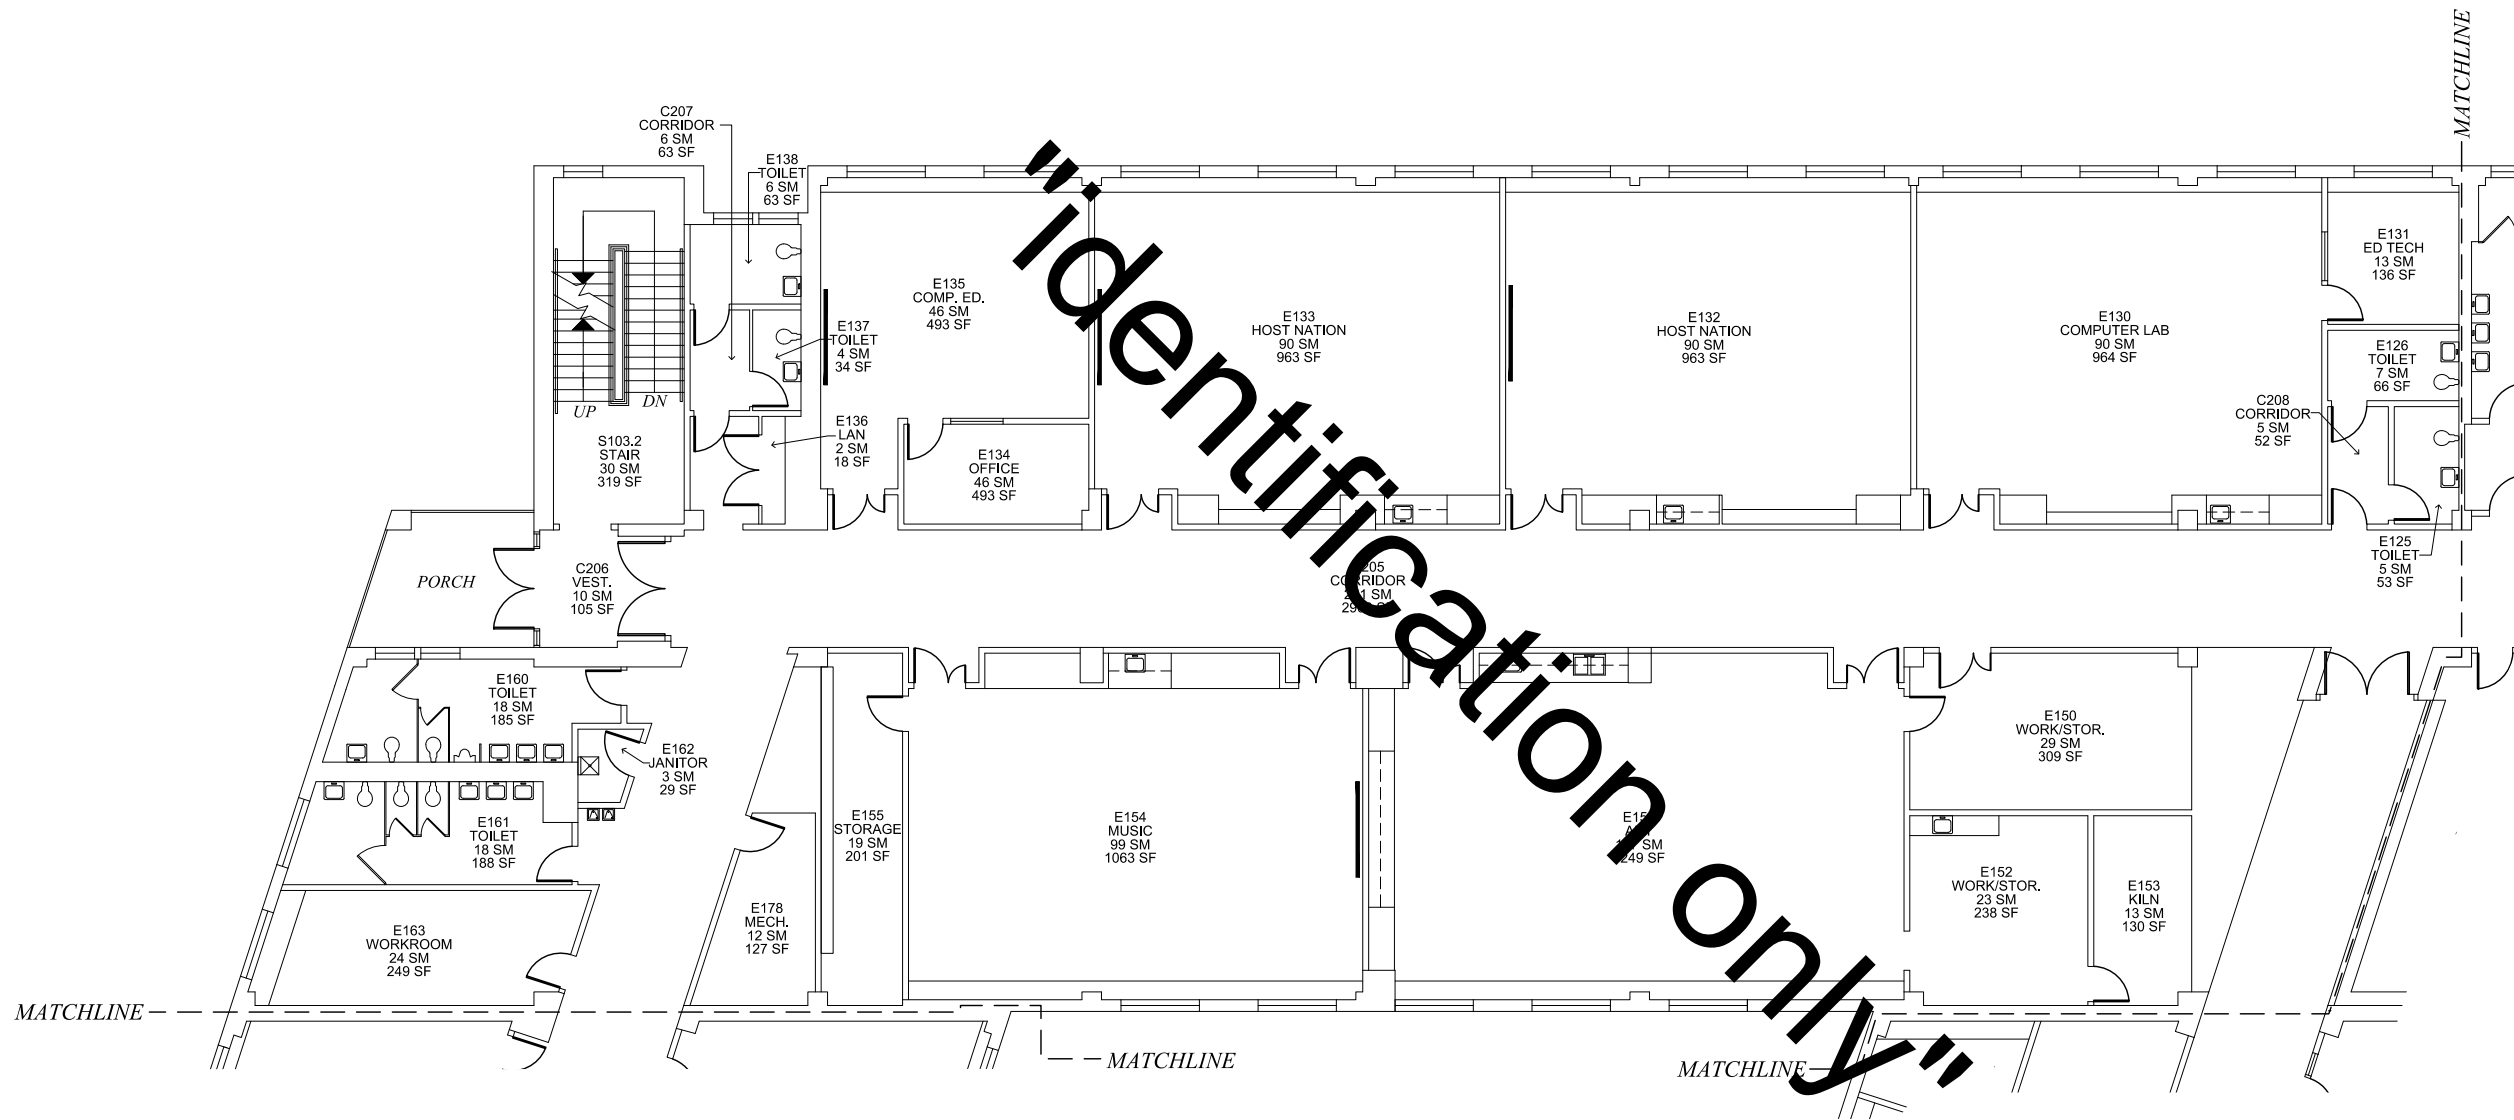

DOOR

SLIDING DOOR

ACCORDION PARTITION

STACK OR FOLDING PARTITION

WINDOW/GLAZING

HIGH WINDOW

SKYLIGHT

STOOP/STEP UP

STAIR

RAMP

ACCESS LADDER

COLD STORAGE

AREA CALCULATED @ 50 %

SLOPING ROOF

DRINKING FOUNTAIN

LAVATORY

SINK

TOILET

URINAL

LOCKER

LAN DISTRIBUTION FRAME

VENT HOOD

WALL SHELVING

UPPER CABINET

BASE CABINET

TEACHER CABINET

MATCHLINE

FLAT ROOF

TITLEBLOCK LEGEND

SHEET NAME:

BLDG #, FLOOR # (# IN SERIES)

KEY PLAN

NTS

153

X151C

X151A

151

X114D

X114C

X114A

114

X151B

X114B

NORTH

Updated By: SPF

FUS Review: MRS

100% Submittal Date: 01 MAY 2020

0 2 4 8 16 FT

dodea

DEPARTMENT OF DEFENSE EDUCATION ACTIVITY

FACILITY UTILIZATION SURVEY

AVIANO ELEMENTARY SCHOOL

AVIANO MIDDLE / HIGH SCHOOL

BUILDING NUMBER: 151

COUNTRY: ITALY

INSTALLATION: AVIANO AIR BASE

SITE: AVIANO HOSPITAL-SCHOOL ANNEX

REGION-DISTRICT: DODEA EUROPE SOUTH


DoDAAC Number: HE5649 / HE5603

Floor: LEVEL 2

Survey Date: JANUARY 2020

Sheet Name: 151_2 (2)

Sheet Seq: 21 of 34

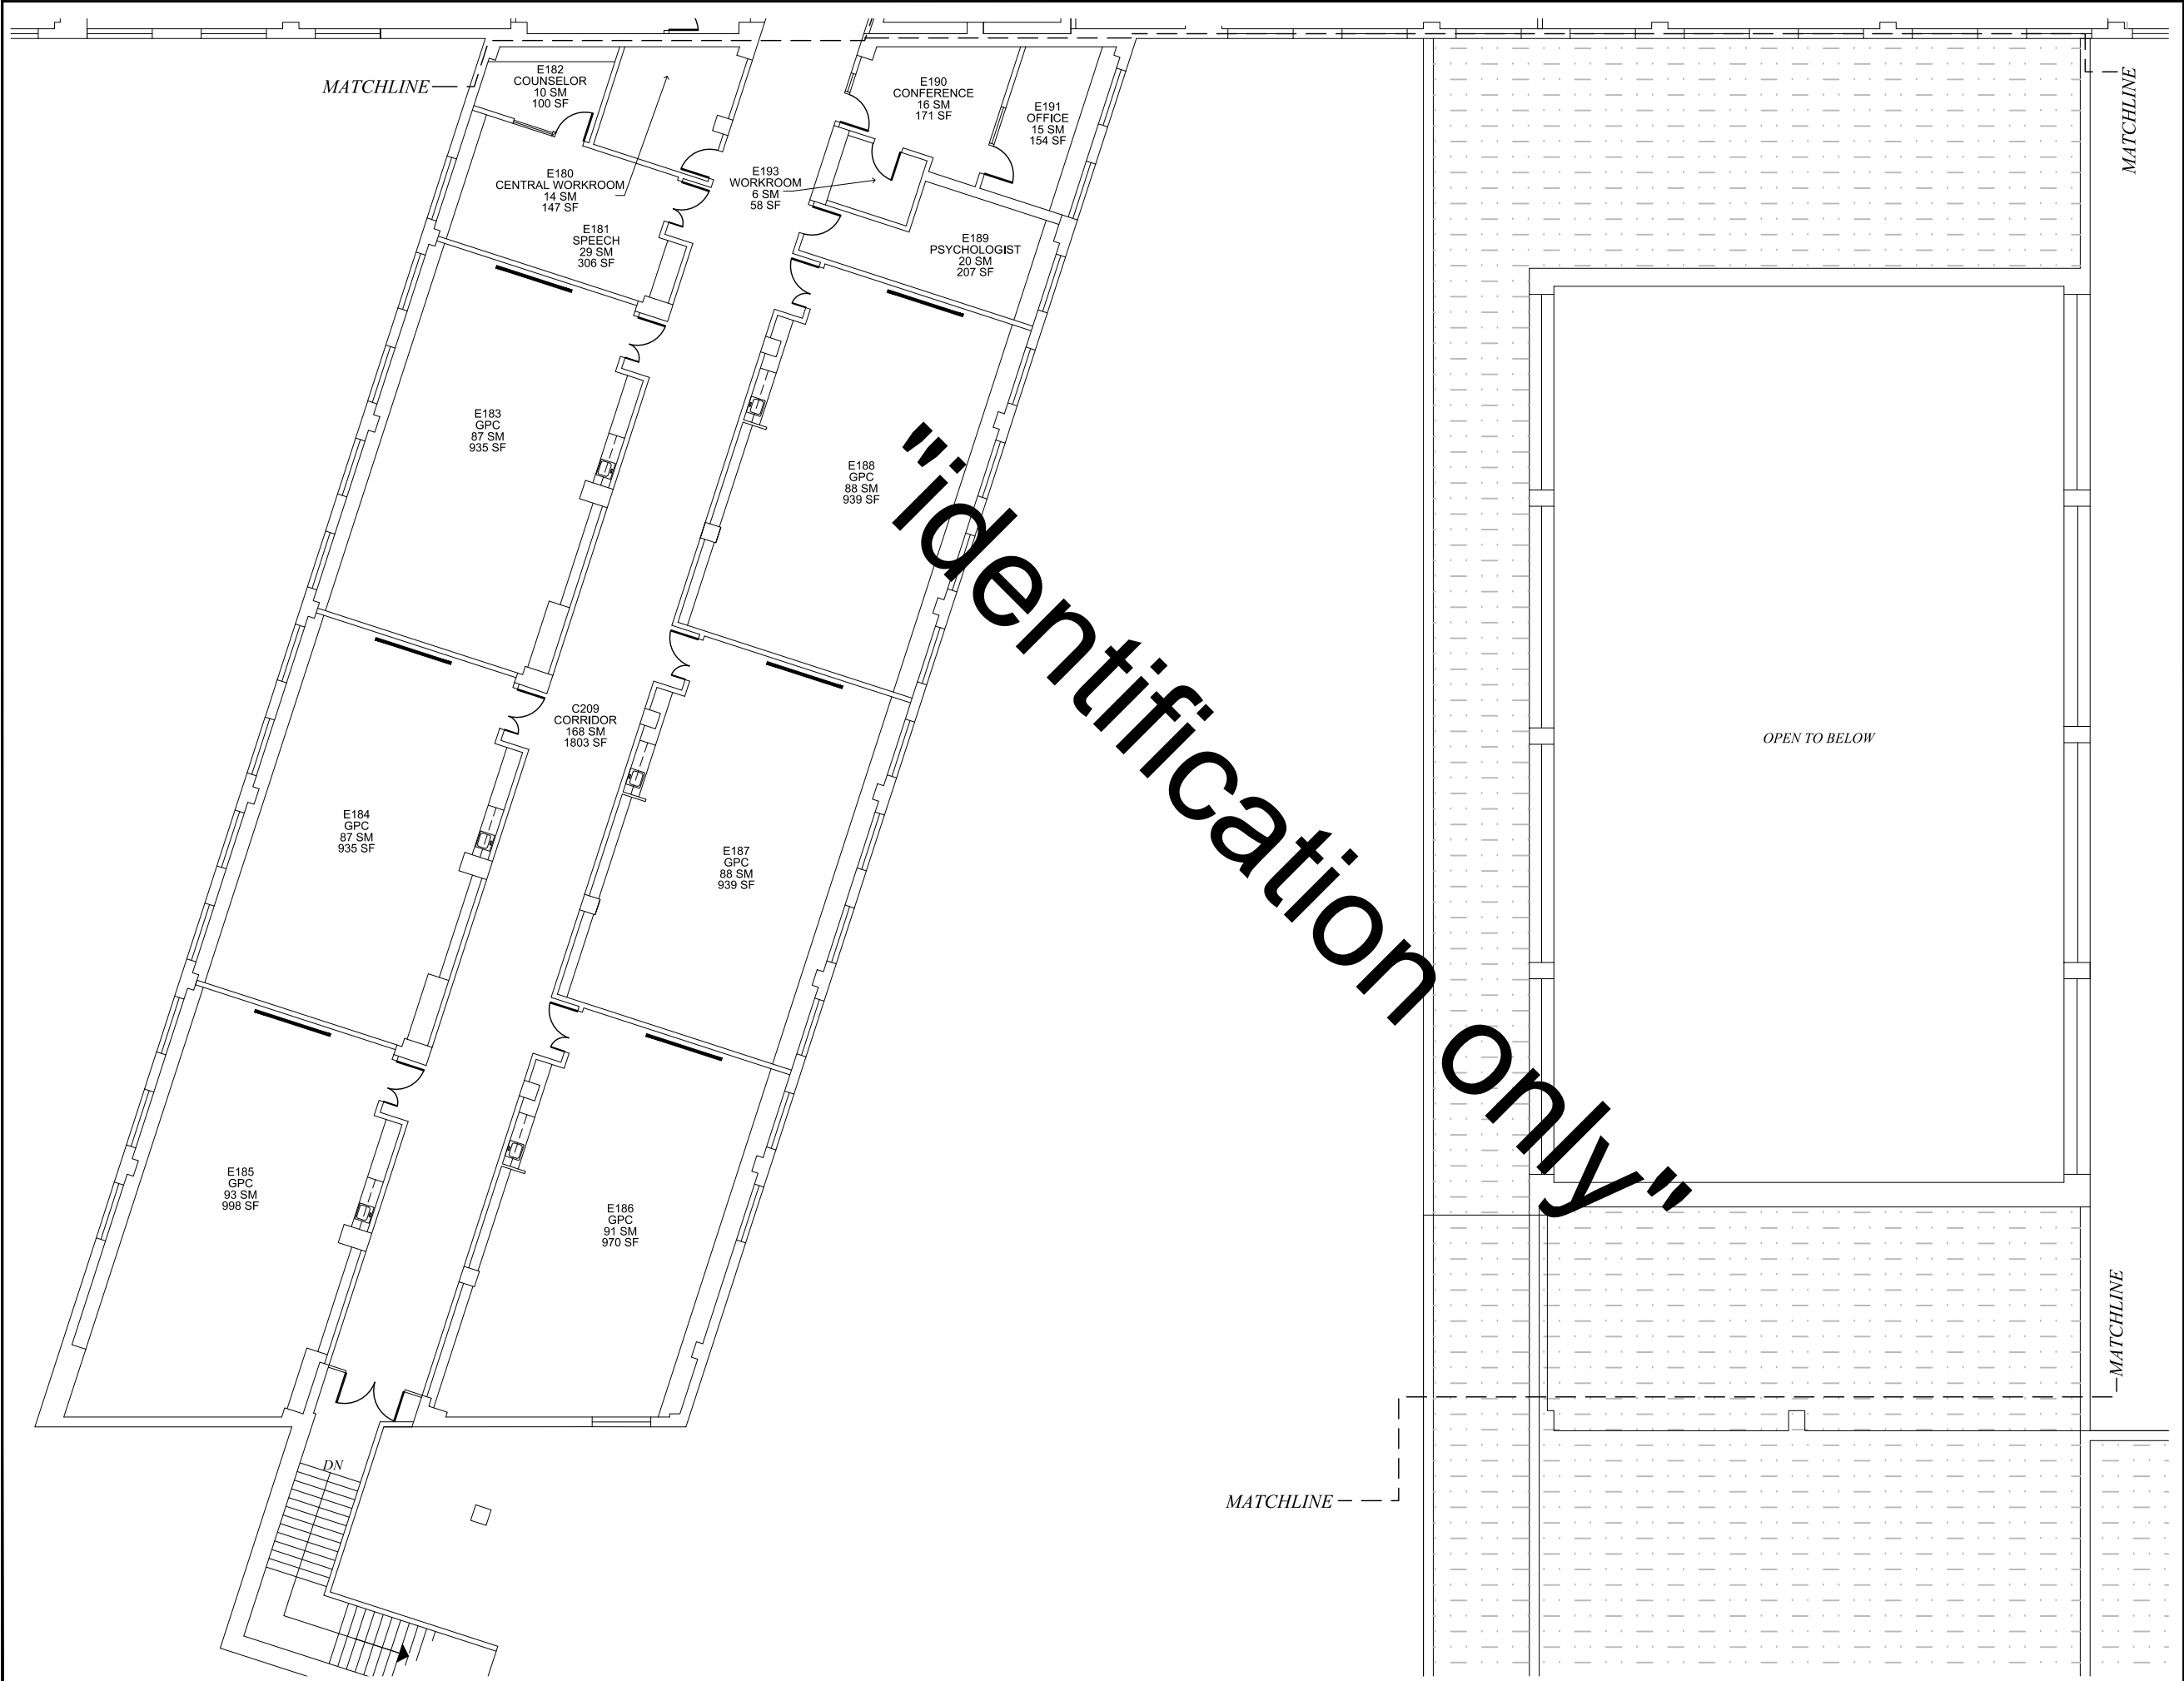

DOOR

SLIDING DOOR

ACCORDION PARTITION

STACK OR FOLDING PARTITION

WINDOW/GLAZING

HIGH WINDOW

SKYLIGHT

STOOP/STEP UP

STAIR

RAMP

ACCESS LADDER

COLD STORAGE

AREA CALCULATED @ 50 %

SLOPING ROOF

DRINKING FOUNTAIN

LAVATORY

SINK

TOILET

URINAL

LOCKER

LAN DISTRIBUTION FRAME

VENT HOOD

WALL SHELVING

UPPER CABINET

BASE CABINET

TEACHER CABINET

MATCHLINE

FLAT ROOF

TITLEBLOCK LEGEND

SHEET NAME:

BLDG #_FLOOR # (# IN SERIES)

KEY PLAN

NTS

153

X151C

X151A

151

X114D

X114C

X114A

114

X114B

NORTH

Updated By: SPF

FUS Review: MRS

100% Submittal Date: 01 MAY 2020

0 2 4 8 16 FT

dodea

DEPARTMENT OF DEFENSE EDUCATION ACTIVITY

FACILITY UTILIZATION SURVEY

AVIANO ELEMENTARY SCHOOL

AVIANO MIDDLE / HIGH SCHOOL

BUILDING NUMBER: 151

COUNTRY: ITALY

INSTALLATION: AVIANO AIR BASE

SITE: AVIANO HOSPITAL-SCHOOL ANNEX

REGION-DISTRICT: DODEA EUROPE SOUTH


DoDAAC Number: HE5649 / HE5603

Floor: LEVEL 2

Survey Date: JANUARY 2020

Sheet Name: 151_2 (3)

Sheet Seq: 22 of 34

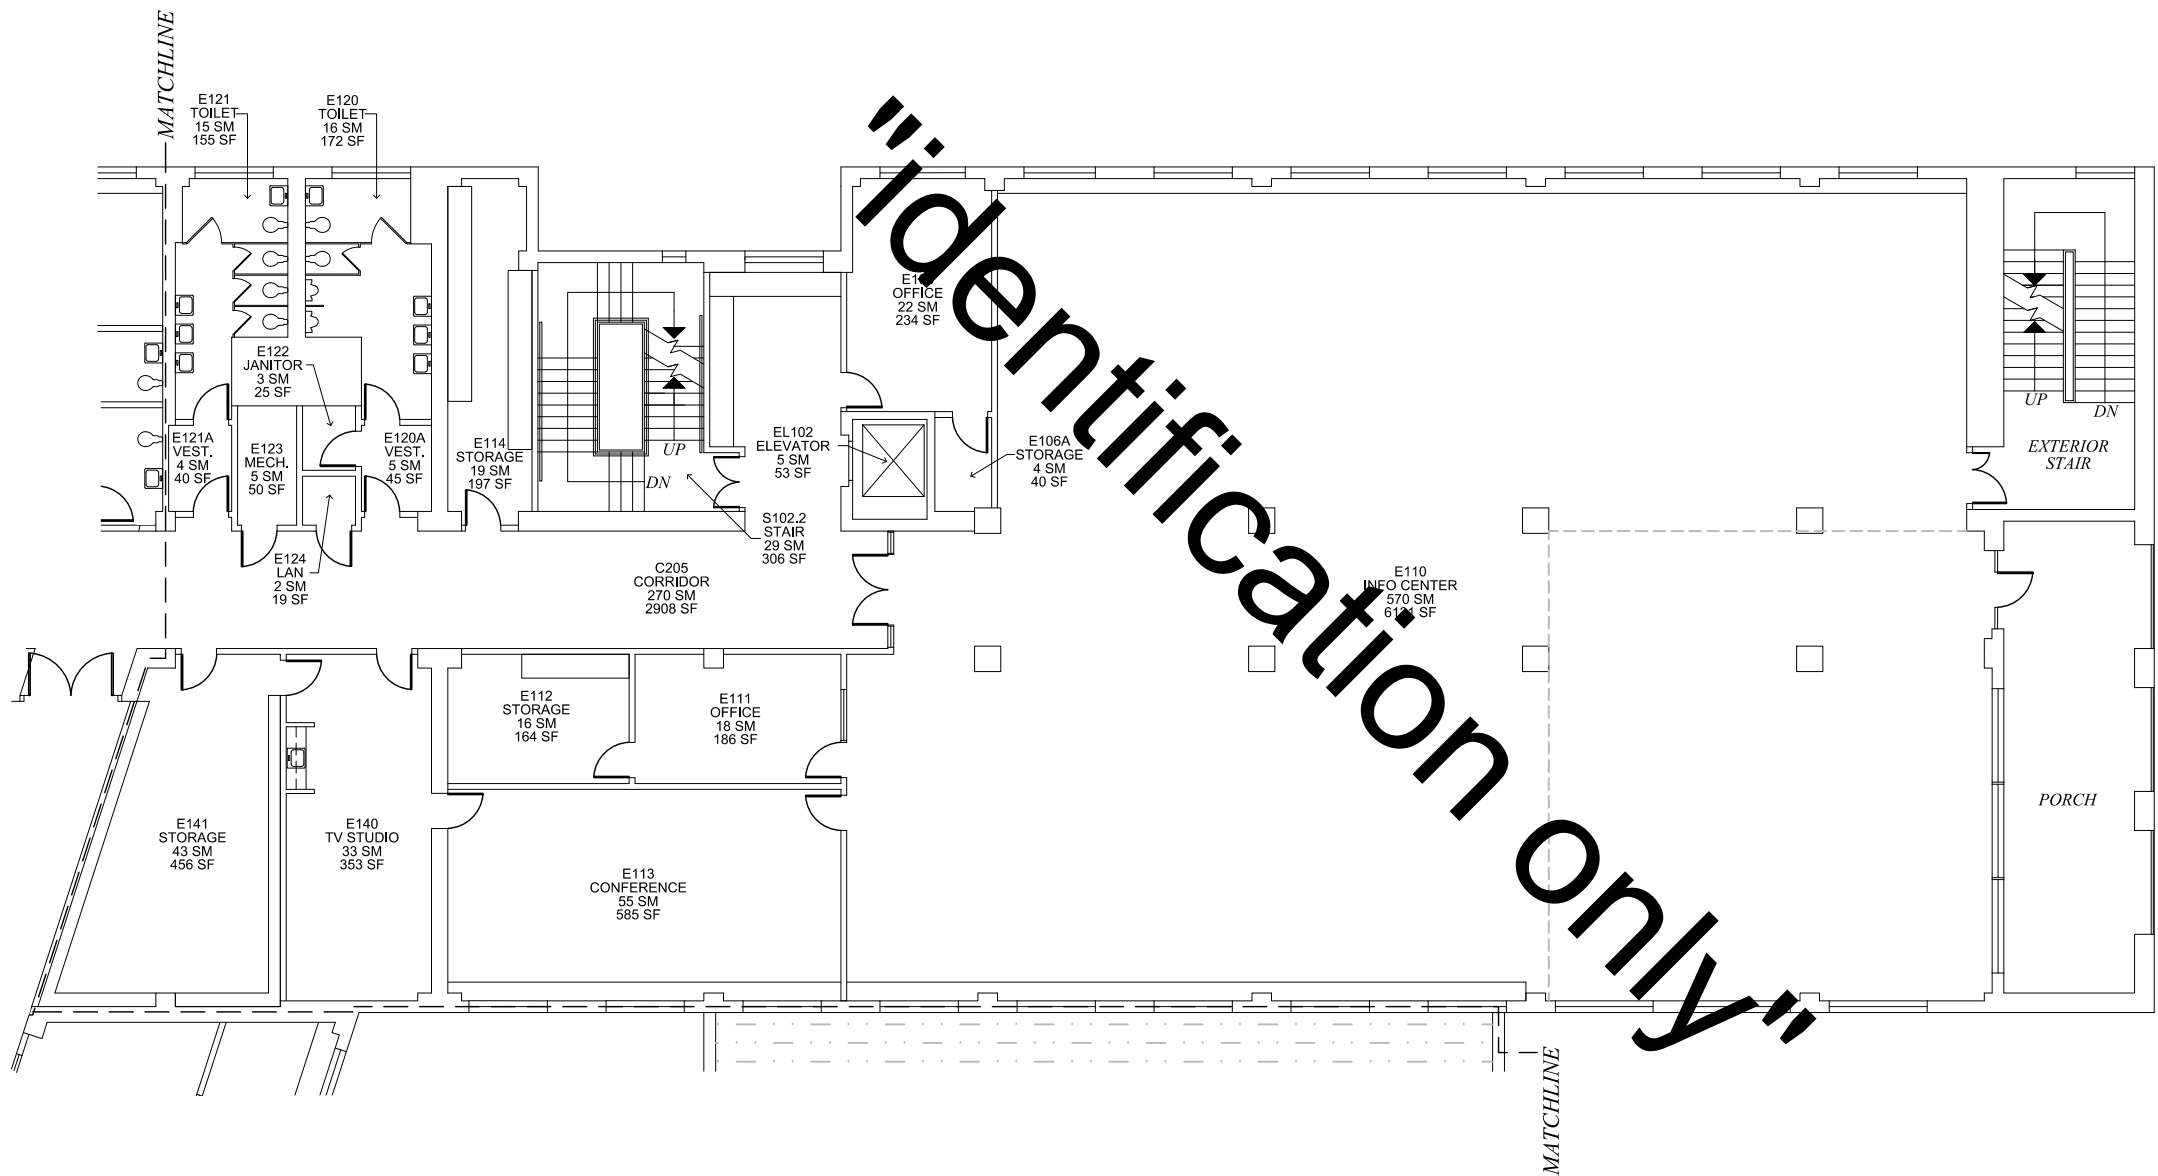

SYMBOL LEGEND	
DOOR	DRINKING FOUNTAIN
SLIDING DOOR	LAVATORY
ACCORDION PARTITION	SINK
STACK OR FOLDING PARTITION	TOILET
WINDOW/GLAZING	URINAL
HIGH WINDOW	LOCKER
SKYLIGHT	LAN DISTRIBUTION FRAME
STOOP/STEP UP	VENT HOOD
STAIR	WALL SHELVING
RAMP	UPPER CABINET
ACCESS LADDER	BASE CABINET
COLD STORAGE	TEACHER CABINET
AREA CALCULATED @ 50 %	MATCHLINE
SLOPING ROOF	FLAT ROOF

TITLEBLOCK LEGEND	
SHEET NAME:	BLDG #_FLOOR # (# IN SERIES)

KEY PLAN

Updated By: SPF

FUS Review: MRS

100% Submittal Date: 01 MAY 2020


0 2 4 8 16 FT

dodea
DEPARTMENT OF DEFENSE EDUCATION ACTIVITY

FACILITY UTILIZATION SURVEY

AVIANO ELEMENTARY SCHOOL
AVIANO MIDDLE / HIGH SCHOOL
BUILDING NUMBER: 151
COUNTRY: ITALY
INSTALLATION: AVIANO AIR BASE
SITE: AVIANO HOSPITAL-SCHOOL ANNEX
REGION-DISTRICT: DODEA EUROPE SOUTH


DoDAAC Number: HE5649 / HE5603	Floor: LEVEL 2	Survey Date: JANUARY 2020
Sheet Name: 151_2 (4)		Sheet Seq: 23 of 34

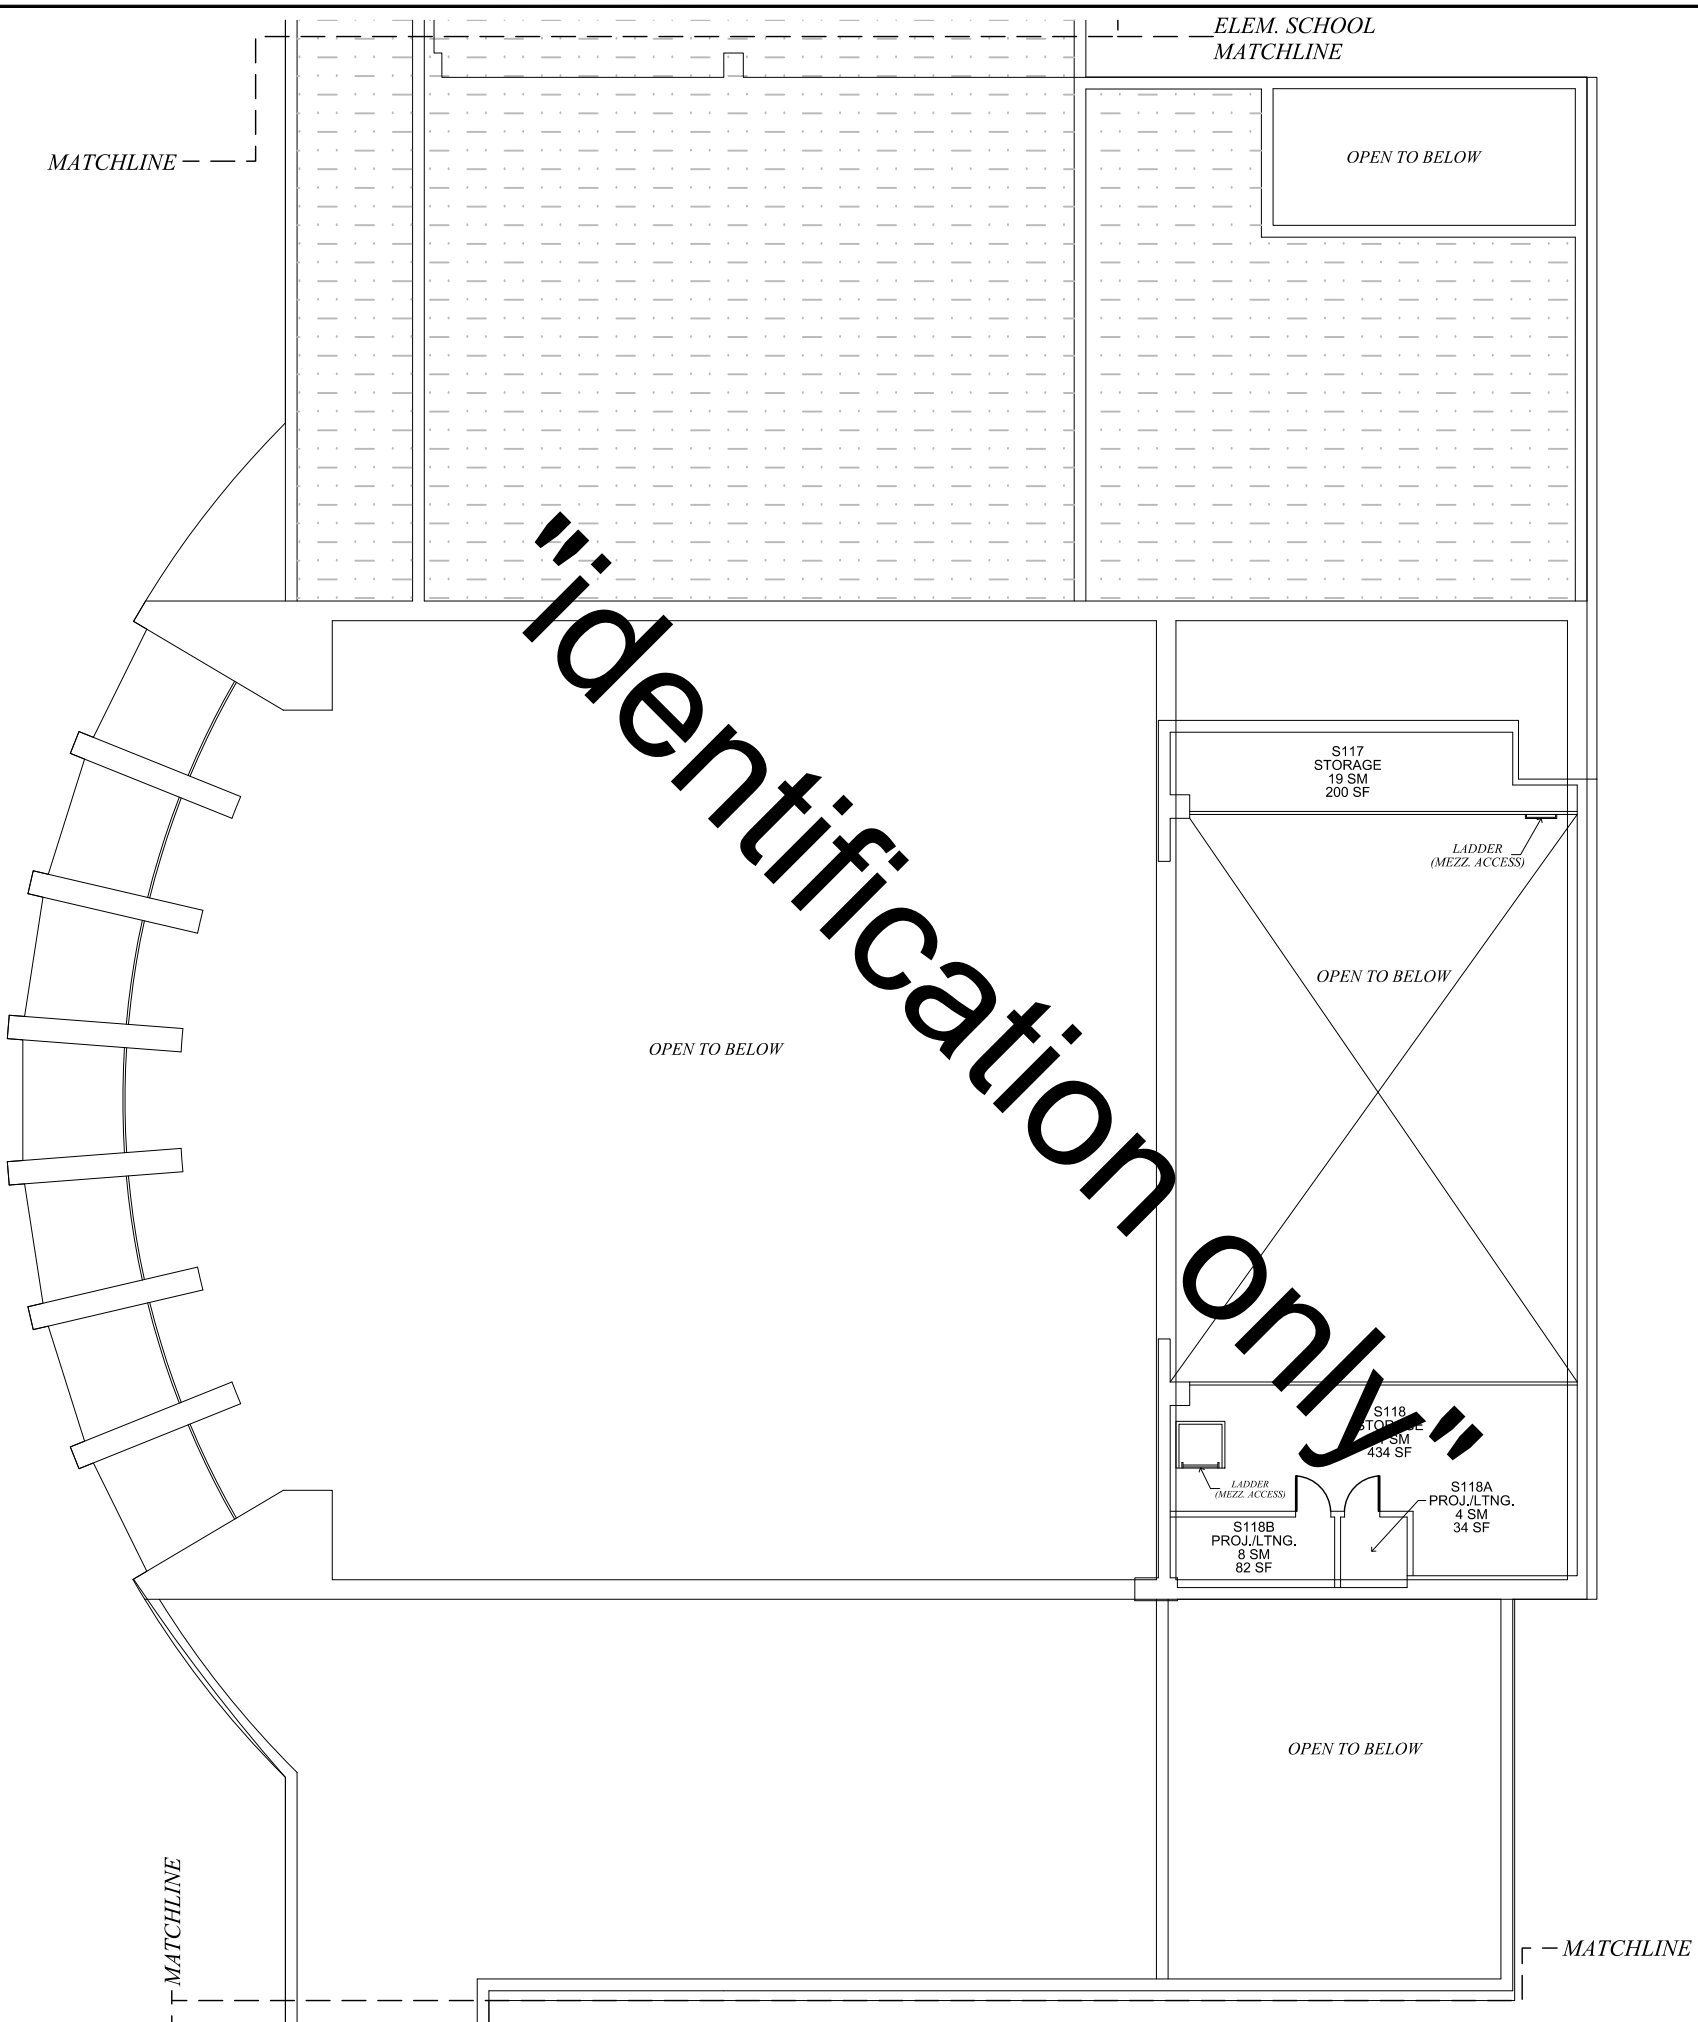

SYMBOL LEGEND			
	DOOR		DRINKING FOUNTAIN
	SLIDING DOOR		LAVATORY
	ACCORDION PARTITION		SINK
	STACK OR FOLDING PARTITION		TOILET
	WINDOW/GLAZING		URINAL
	HIGH WINDOW		LOCKER
	SKYLIGHT		LAN DISTRIBUTION FRAME
	STOOP/STEP UP		VENT HOOD
	STAIR		WALL SHELVING
	RAMP		UPPER CABINET
	ACCESS LADDER		BASE CABINET
	COLD STORAGE		TEACHER CABINET
	AREA CALCULATED @ 50 %		MATCHLINE
	SLOPING ROOF		FLAT ROOF

TITLEBLOCK LEGEND	
SHEET NAME:	BLDG #_FLOOR # (# IN SERIES)

KEY PLAN

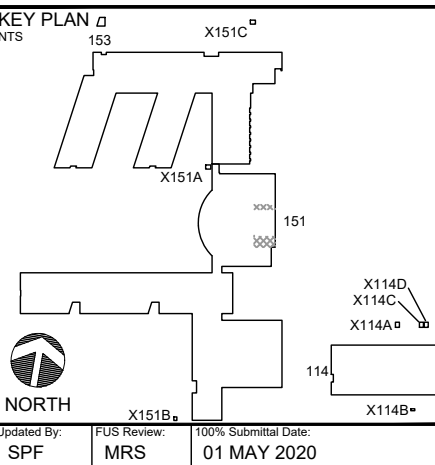

NTS

153

X151C

X151A

151

X114D

X114C

X114A

114L

X114B

X151B

NORTH

Updated By: **SPF** FUS Review: **MRS** 100% Submittal Date: **01 MAY 2020**

0 2 4 8 16 FT



DEPARTMENT OF DEFENSE EDUCATION ACTIVITY

FACILITY UTILIZATION SURVEY

AVIANO ELEMENTARY SCHOOL

AVIANO MIDDLE / HIGH SCHOOL

BUILDING NUMBER: 151


COUNTRY: ITALY

INSTALLATION: AVIANO AIR BASE

SITE: AVIANO HOSPITAL-SCHOOL ANNEX

REGION-DISTRICT: DODEA EUROPE SOUTH

DoDAAC Number: HE5649 / HE5603	Floor: LEVEL 2	Survey Date: JANUARY 2020
Sheet Name: 151_2 (5)		Sheet Seq: 24 of 34

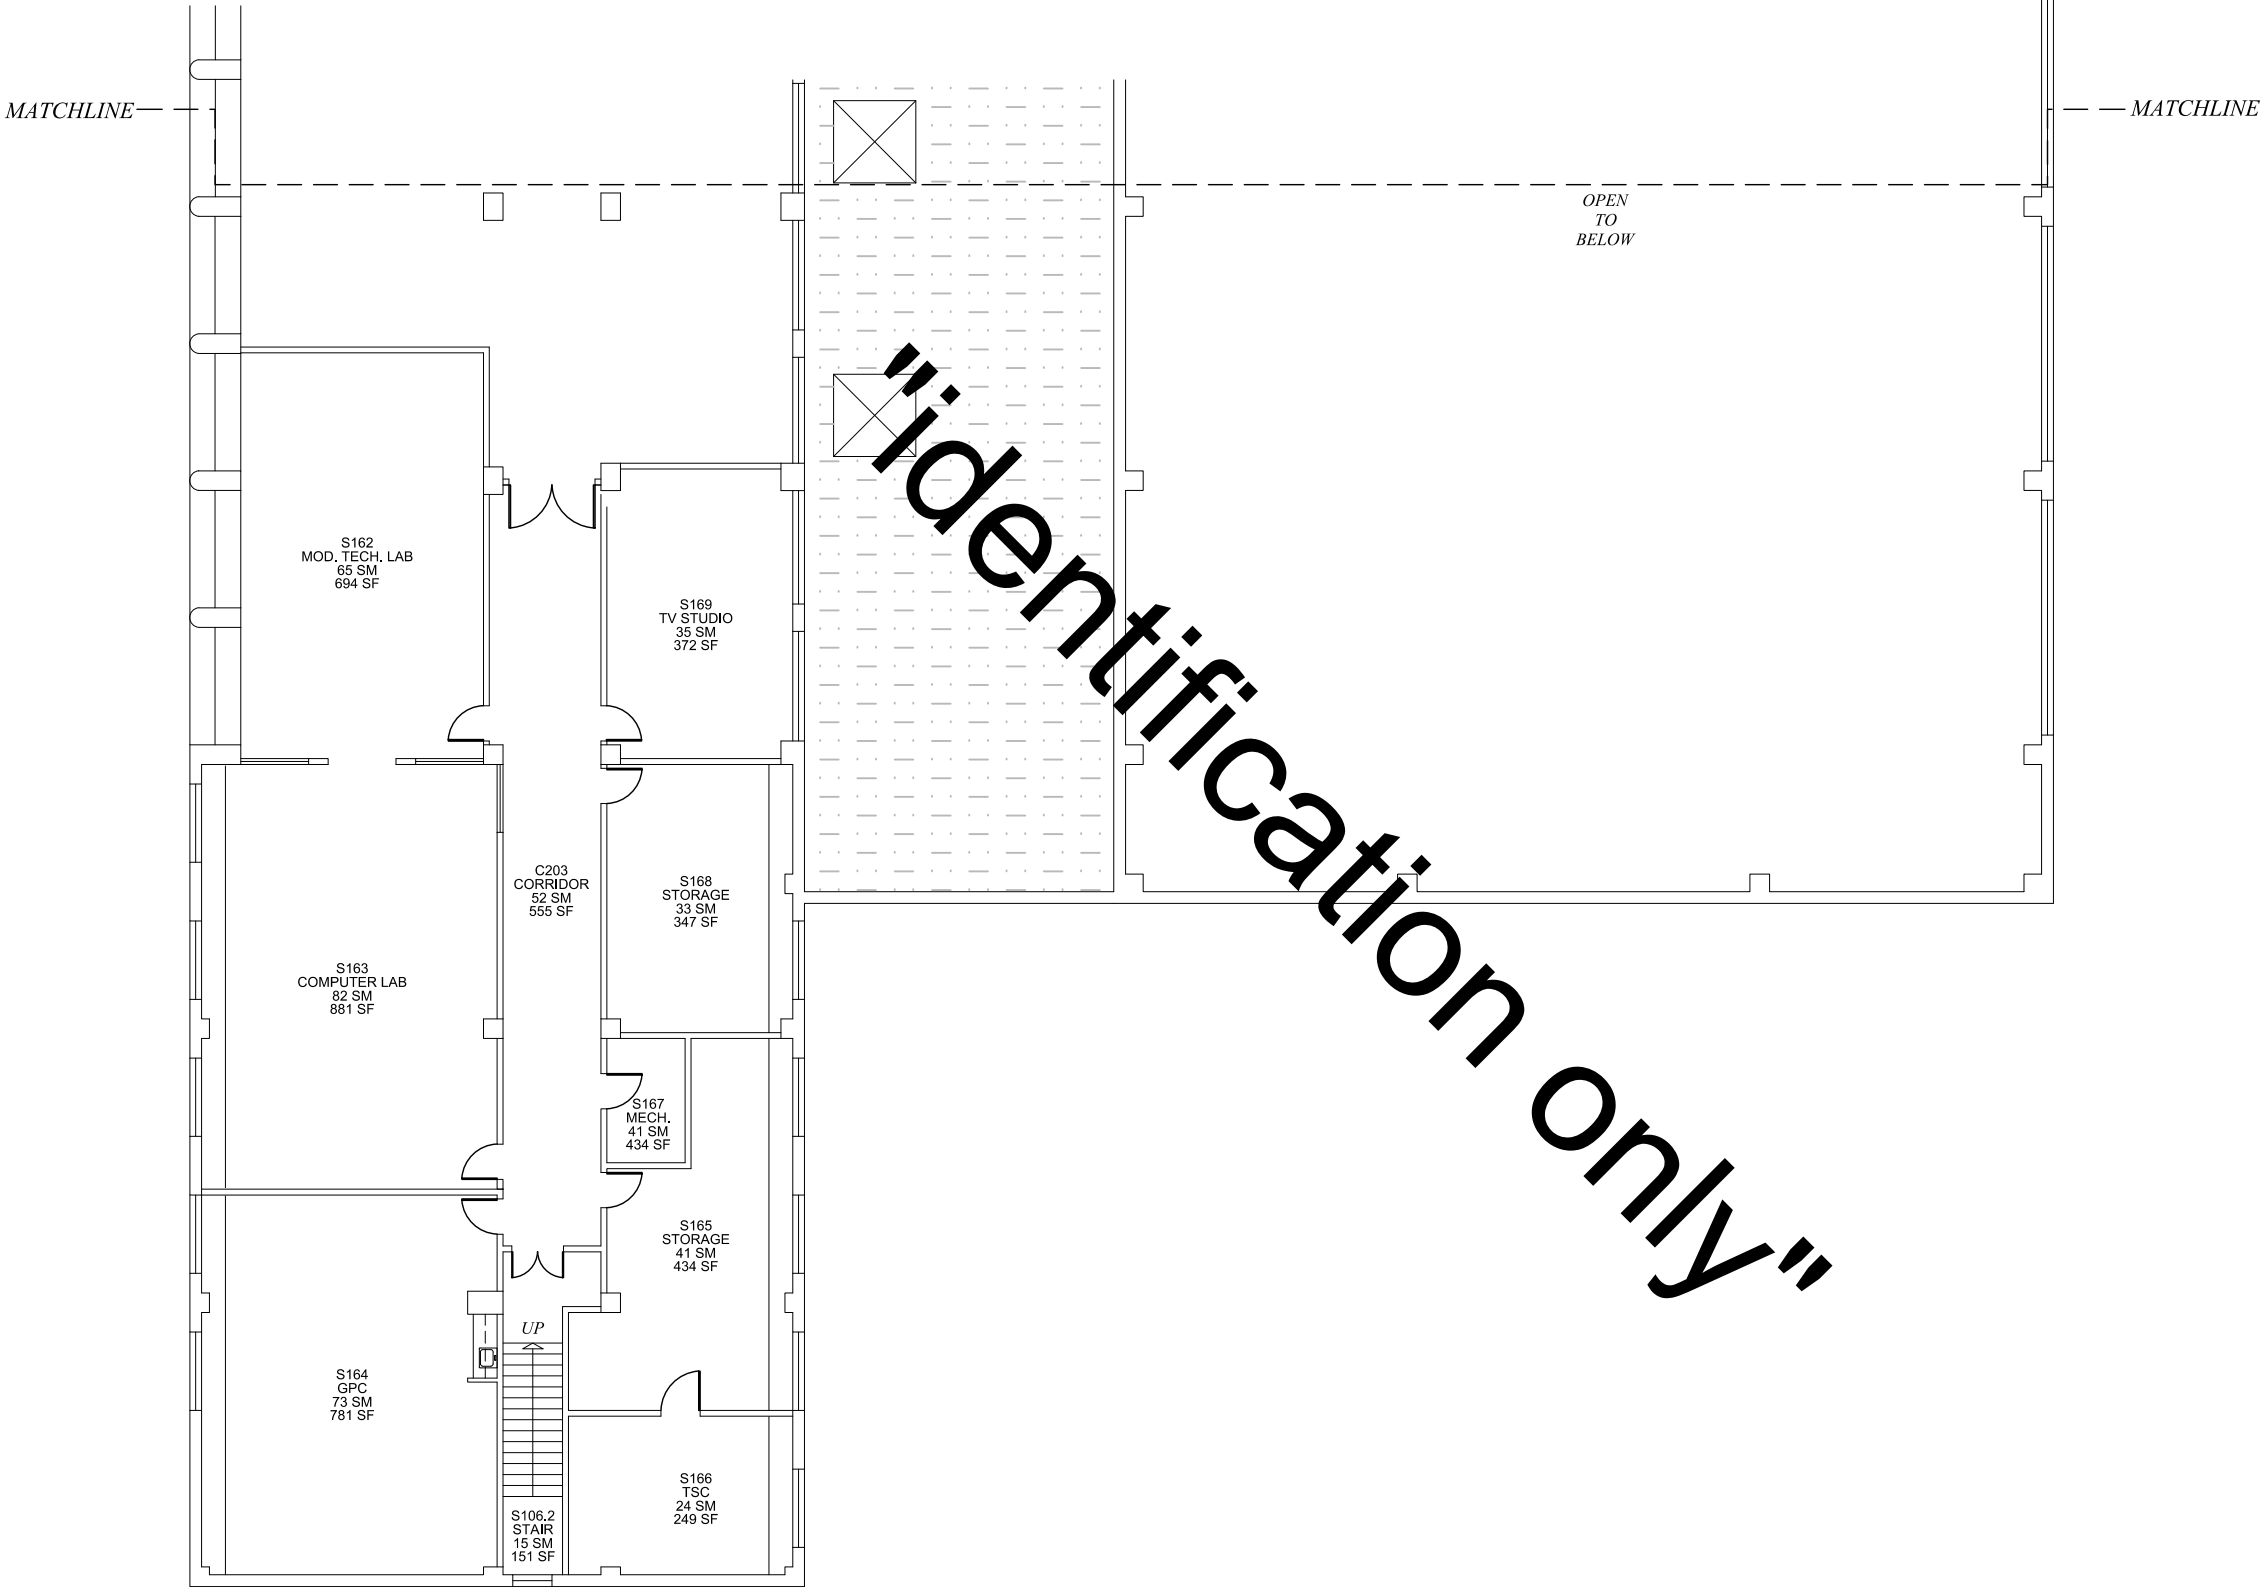

SYMBOL LEGEND

DOOR	DRINKING FOUNTAIN
SLIDING DOOR	LAVATORY
ACCORDION PARTITION	SINK
STACK OR FOLDING PARTITION	TOILET
WINDOW/GLAZING	URINAL
HIGH WINDOW	LOCKER
SKYLIGHT	LAN DISTRIBUTION FRAME
STOOP/STEP UP	VENT HOOD
STAIR	WALL SHELVING
RAMP	UPPER CABINET
ACCESS LADDER	BASE CABINET
COLD STORAGE	TEACHER CABINET
AREA CALCULATED @ 50 %	MATCHLINE
SLOPING ROOF	FLAT ROOF

TITLEBLOCK LEGEND

SHEET NAME:	BLDG #_FLOOR # (# IN SERIES)

KEY PLAN

NTS

Updated By:

FUS Review:

100% Submittal Date:

SPF

MRS

01 MAY 2020

0

2

4

8

16 FT

dodea

DEPARTMENT OF DEFENSE EDUCATION ACTIVITY

FACILITY UTILIZATION SURVEY

AVIANO ELEMENTARY SCHOOL

AVIANO MIDDLE / HIGH SCHOOL

BUILDING NUMBER: 151

COUNTRY: ITALY

INSTALLATION: AVIANO AIR BASE

SITE: AVIANO HOSPITAL-SCHOOL ANNEX

REGION-DISTRICT: DODEA EUROPE SOUTH

DoDAAC Number:

Floor:

Survey Date:

HE5649 / HE5603

LEVEL 2


JANUARY 2020

Sheet Name:

Sheet Seq:

151_2 (7)

26 of 34

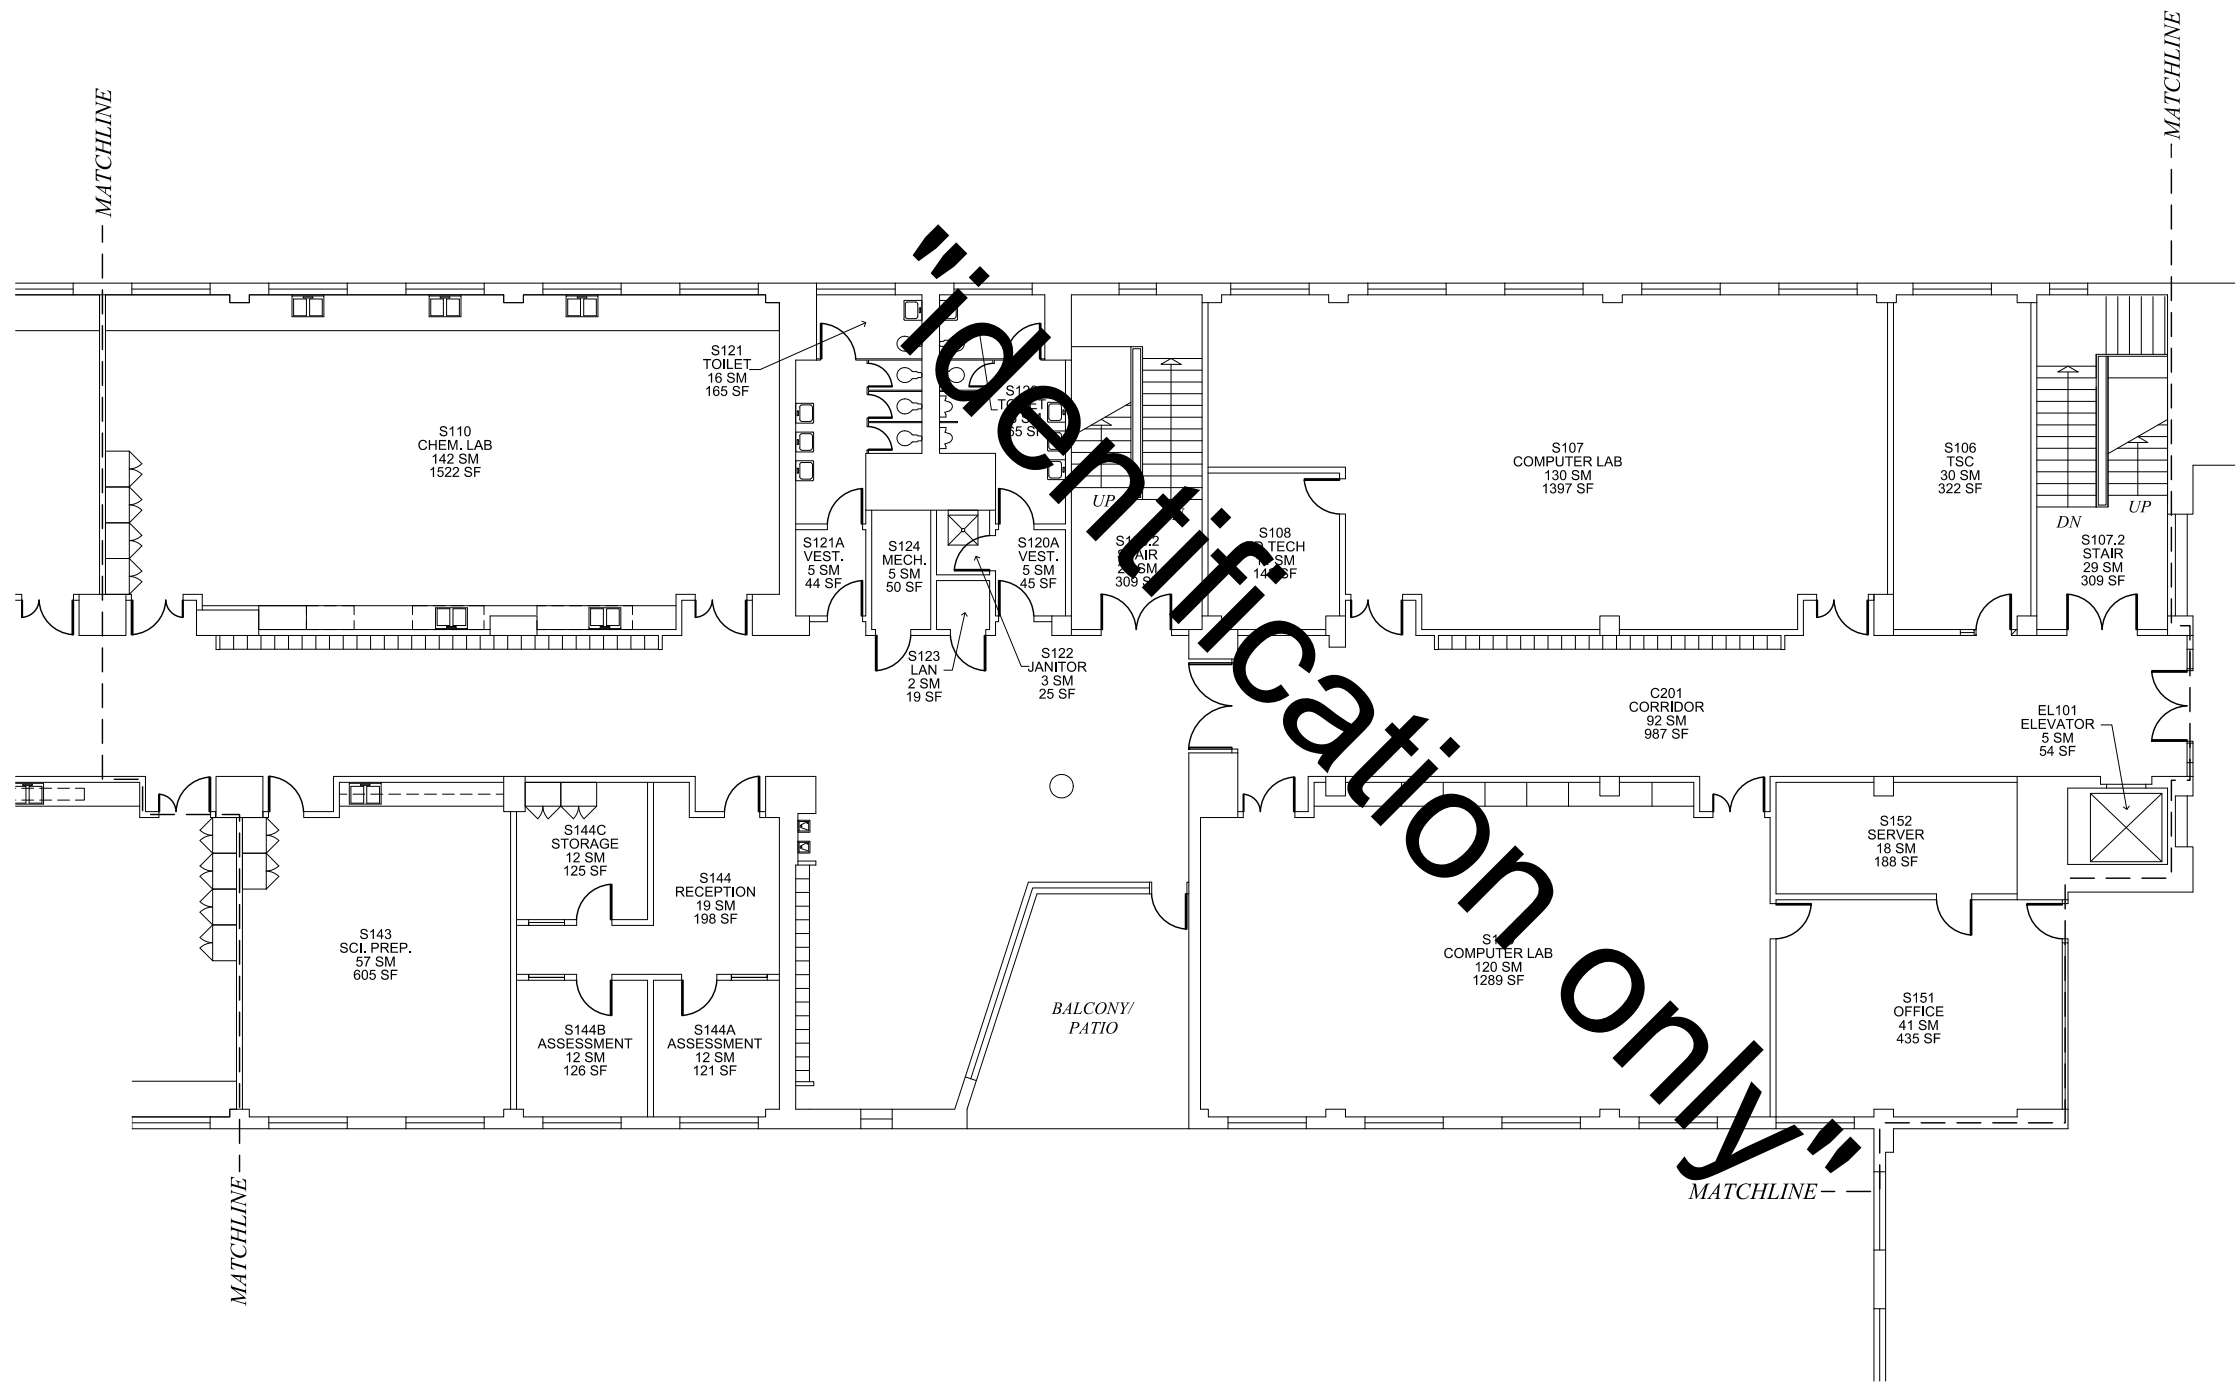

DOOR

SLIDING DOOR

ACCORDION PARTITION

STACK OR FOLDING PARTITION

WINDOW/GLAZING

HIGH WINDOW

SKYLIGHT

STOOP/STEP UP

STAIR

RAMP

ACCESS LADDER

COLD STORAGE

AREA CALCULATED @ 50 %

SLOPING ROOF

DRINKING FOUNTAIN

LAVATORY

SINK

TOILET

URINAL

LOCKER

LAN DISTRIBUTION FRAME

VENT HOOD

WALL SHELVING

UPPER CABINET

BASE CABINET

TEACHER CABINET

MATCHLINE

FLAT ROOF

TITLEBLOCK LEGEND

SHEET NAME:

BLDG # FLOOR # (# IN SERIES)

KEY PLAN

NTS

153

X151C

X151A

151

X114D

X114C

X114A

114

X114B

X151B

NORTH

Updated By: SPF

FUS Review: MRS

100% Submittal Date: 01 MAY 2020

0 2 4 8 16 FT

dodea

DEPARTMENT OF DEFENSE EDUCATION ACTIVITY

FACILITY UTILIZATION SURVEY

AVIANO ELEMENTARY SCHOOL

AVIANO MIDDLE / HIGH SCHOOL

BUILDING NUMBER: 151

COUNTRY: ITALY

INSTALLATION: AVIANO AIR BASE

SITE: AVIANO HOSPITAL-SCHOOL ANNEX

REGION-DISTRICT: DODEA EUROPE SOUTH


DoDAAC Number: HE5649 / HE5603

Floor: LEVEL 2

Survey Date: JANUARY 2020

Sheet Name: 151_2 (8)

Sheet Seq: 27 of 34

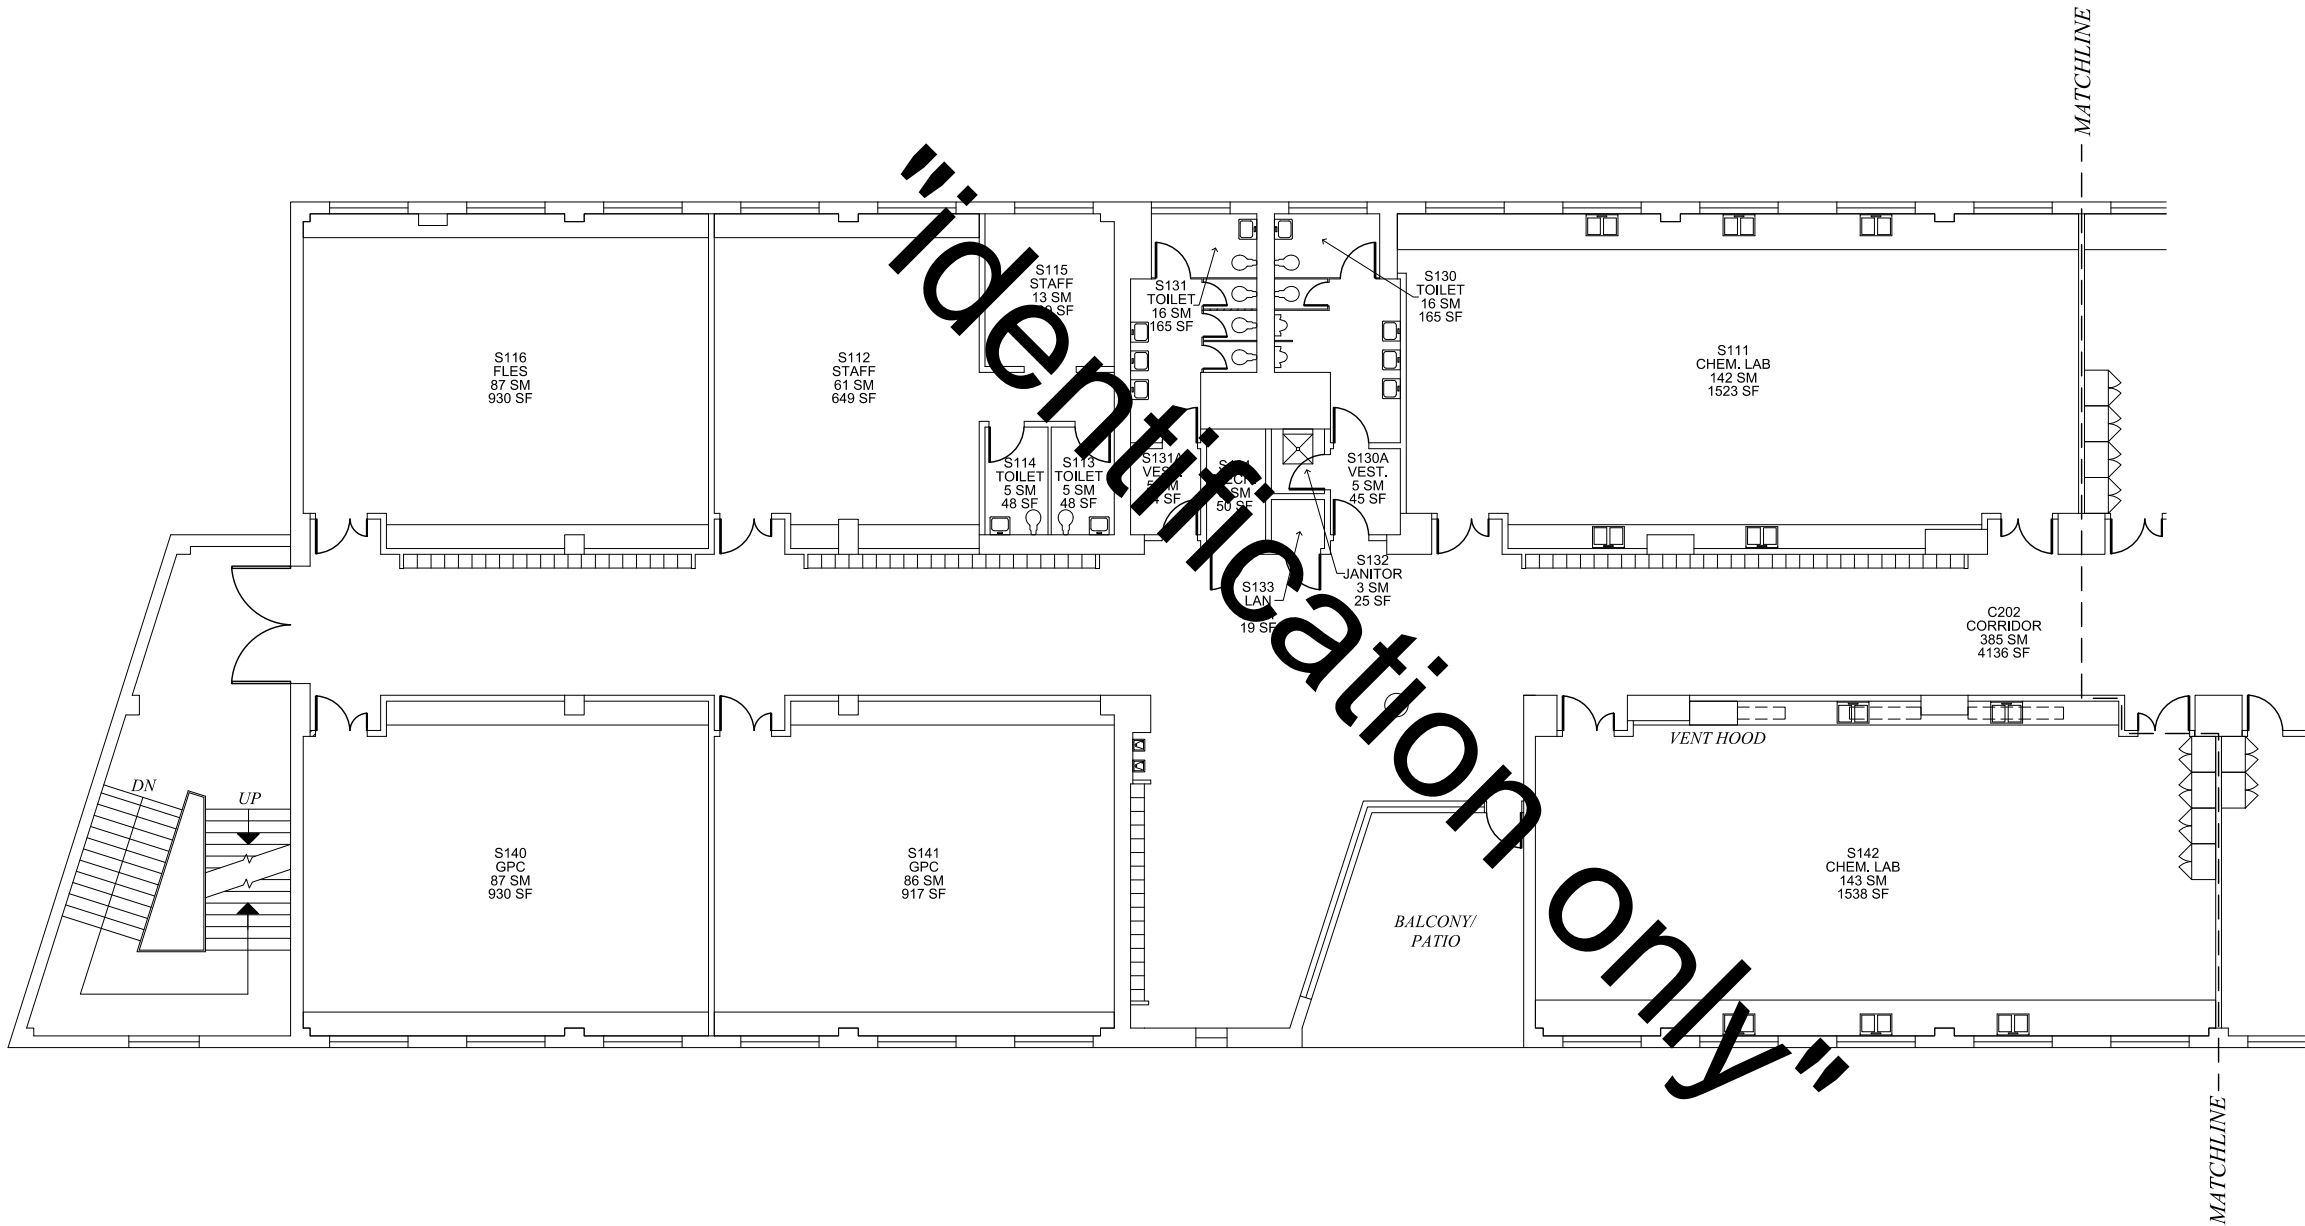

DOOR

SLIDING DOOR

ACCORDION PARTITION

STACK OR FOLDING PARTITION

WINDOW/GLAZING

HIGH WINDOW

SKYLIGHT

STOOP/STEP UP

STAIR

RAMP

ACCESS LADDER

COLD STORAGE

AREA CALCULATED @ 50 %

SLOPING ROOF

DRINKING FOUNTAIN

LAVATORY

SINK

TOILET

URINAL

LOCKER

LAN DISTRIBUTION FRAME

VENT HOOD

WALL SHELVING

UPPER CABINET

BASE CABINET

TEACHER CABINET

MATCHLINE

FLAT ROOF

TITLEBLOCK LEGEND

SHEET NAME:

BLDG #_FLOOR # (# IN SERIES)

KEY PLAN

NTS

153

X151C

X151A

151

X114D

X114C

X114A

114

X114B

X151B

NORTH

Updated By:SPF

FUS Review:MRS

100% Submittal Date:01 MAY 2020

0

2

4

8

16 FT

dodea

DEPARTMENT OF DEFENSE EDUCATION ACTIVITY

FACILITY UTILIZATION SURVEY

AVIANO ELEMENTARY SCHOOL

AVIANO MIDDLE / HIGH SCHOOL

BUILDING NUMBER: 151

COUNTRY: ITALY

INSTALLATION: AVIANO AIR BASE

SITE: AVIANO HOSPITAL-SCHOOL ANNEX

REGION-DISTRICT: DODEA EUROPE SOUTH


DoDAAC Number:HE5649 / HE5603

Floor:LEVEL 2

Survey Date:JANUARY 2020

Sheet Name:151_2 (9)

Sheet Seq:28 of 34

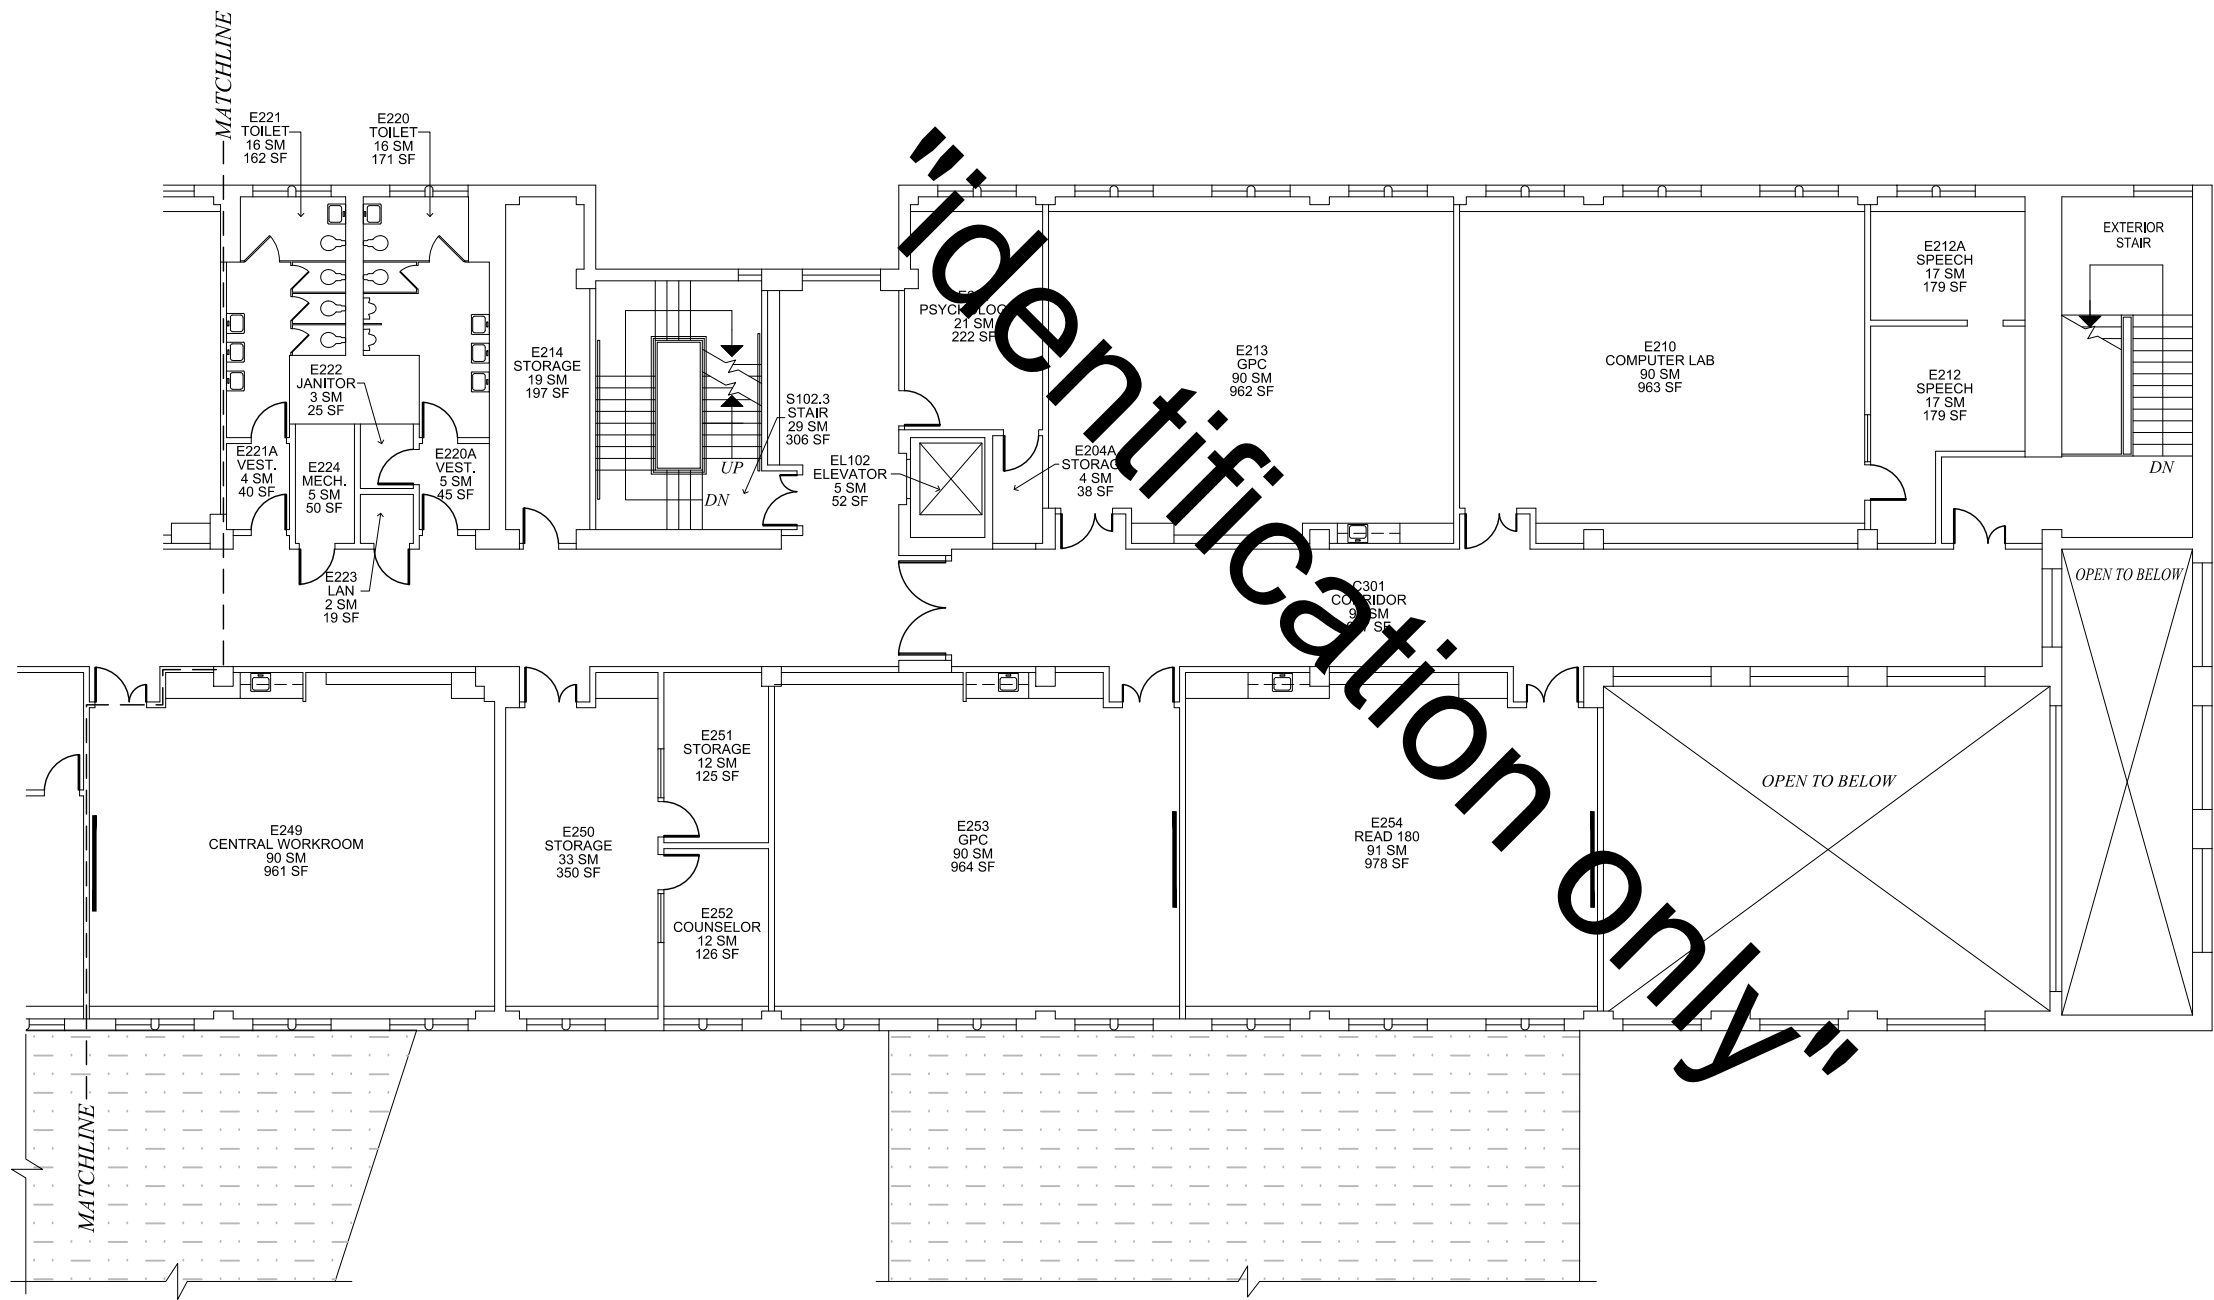

DOOR

SLIDING DOOR

ACCORDION PARTITION

STACK OR FOLDING PARTITION

WINDOW/GLAZING

HIGH WINDOW

SKYLIGHT

STOOP/STEP UP

STAIR

RAMP

ACCESS LADDER

COLD STORAGE

AREA CALCULATED @ 50 %

SLOPING ROOF

DRINKING FOUNTAIN

LAVATORY

SINK

TOILET

URINAL

LOCKER

LAN DISTRIBUTION FRAME

VENT HOOD

WALL SHELVING

UPPER CABINET

BASE CABINET

TEACHER CABINET

MATCHLINE

FLAT ROOF

TITLEBLOCK LEGEND

SHEET NAME:

BLDG #_FLOOR # (# IN SERIES)

KEY PLAN

NTS

153

X151C

X151A

151

X114D

X114C

X114A

114

X114B

X151B

NORTH

Updated By: SPF

FUS Review: MRS

100% Submittal Date: 01 MAY 2020

0 2 4 8 16 FT

dodea

DEPARTMENT OF DEFENSE EDUCATION ACTIVITY

FACILITY UTILIZATION SURVEY

AVIANO ELEMENTARY SCHOOL

AVIANO MIDDLE / HIGH SCHOOL

BUILDING NUMBER: 151

COUNTRY: ITALY

INSTALLATION: AVIANO AIR BASE

SITE: AVIANO HOSPITAL-SCHOOL ANNEX

REGION-DISTRICT: DODEA EUROPE SOUTH


DoDAAC Number: HE5649 / HE5603

Floor: LEVEL 3

Survey Date: JANUARY 2020

Sheet Name: 151_3 (1)

Sheet Seq: 29 of 34

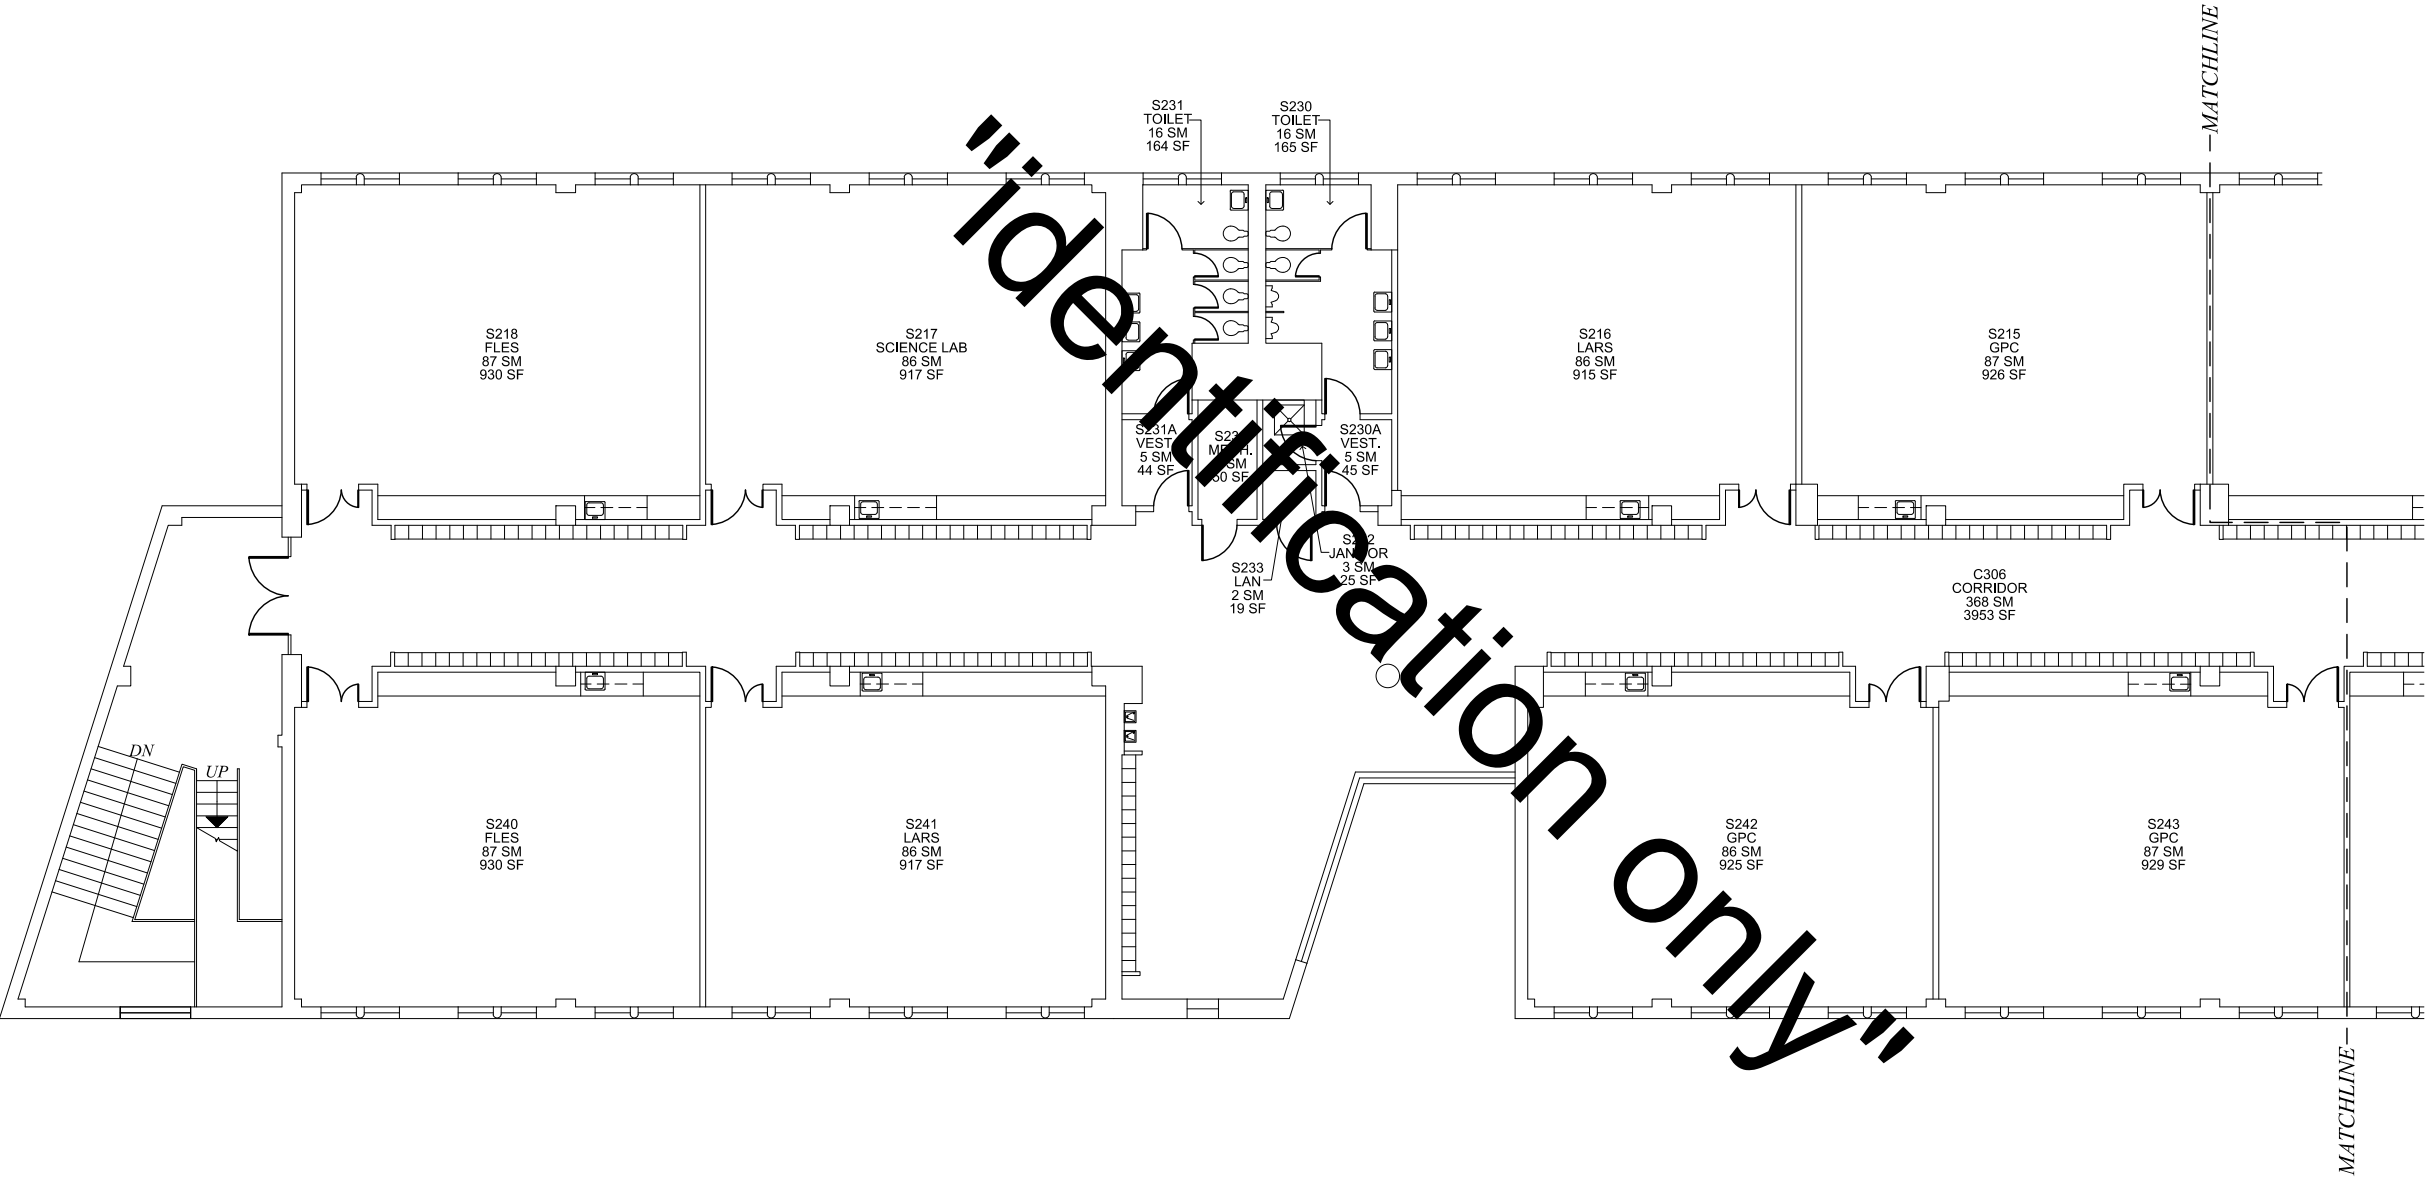

SYMBOL LEGEND

DOOR	DRINKING FOUNTAIN
SLIDING DOOR	LAVATORY
ACCORDION PARTITION	SINK
STACK OR FOLDING PARTITION	TOILET
WINDOW/GLAZING	URINAL
HIGH WINDOW	LOCKER
SKYLIGHT	LAN DISTRIBUTION FRAME
STOOP/STEP UP	VENT HOOD
STAIR	WALL SHELVING
RAMP	UPPER CABINET
ACCESS LADDER	BASE CABINET
COLD STORAGE	TEACHER CABINET
AREA CALCULATED @ 50 %	MATCHLINE
SLOPING ROOF	FLAT ROOF

TITLEBLOCK LEGEND

SHEET NAME:	BLDG #_ FLOOR # (# IN SERIES)


KEY PLAN

Updated By: SPF	FUS Review: MRS	100% Submittal Date: 01 MAY 2020
-----------------	-----------------	----------------------------------


dodeca
DEPARTMENT OF DEFENSE EDUCATION ACTIVITY
FACILITY UTILIZATION SURVEY

AVIANO ELEMENTARY SCHOOL
AVIANO MIDDLE / HIGH SCHOOL
BUILDING NUMBER: 151
COUNTRY: ITALY
INSTALLATION: AVIANO AIR BASE
SITE: AVIANO HOSPITAL-SCHOOL ANNEX
REGION-DISTRICT: DODEA EUROPE SOUTH

DoDAAC Number: HE5649 / HE5603	Floor: LEVEL 3	Survey Date: JANUARY 2020
Sheet Name: 151_3 (4)	Sheet Seq: 32 of 34	

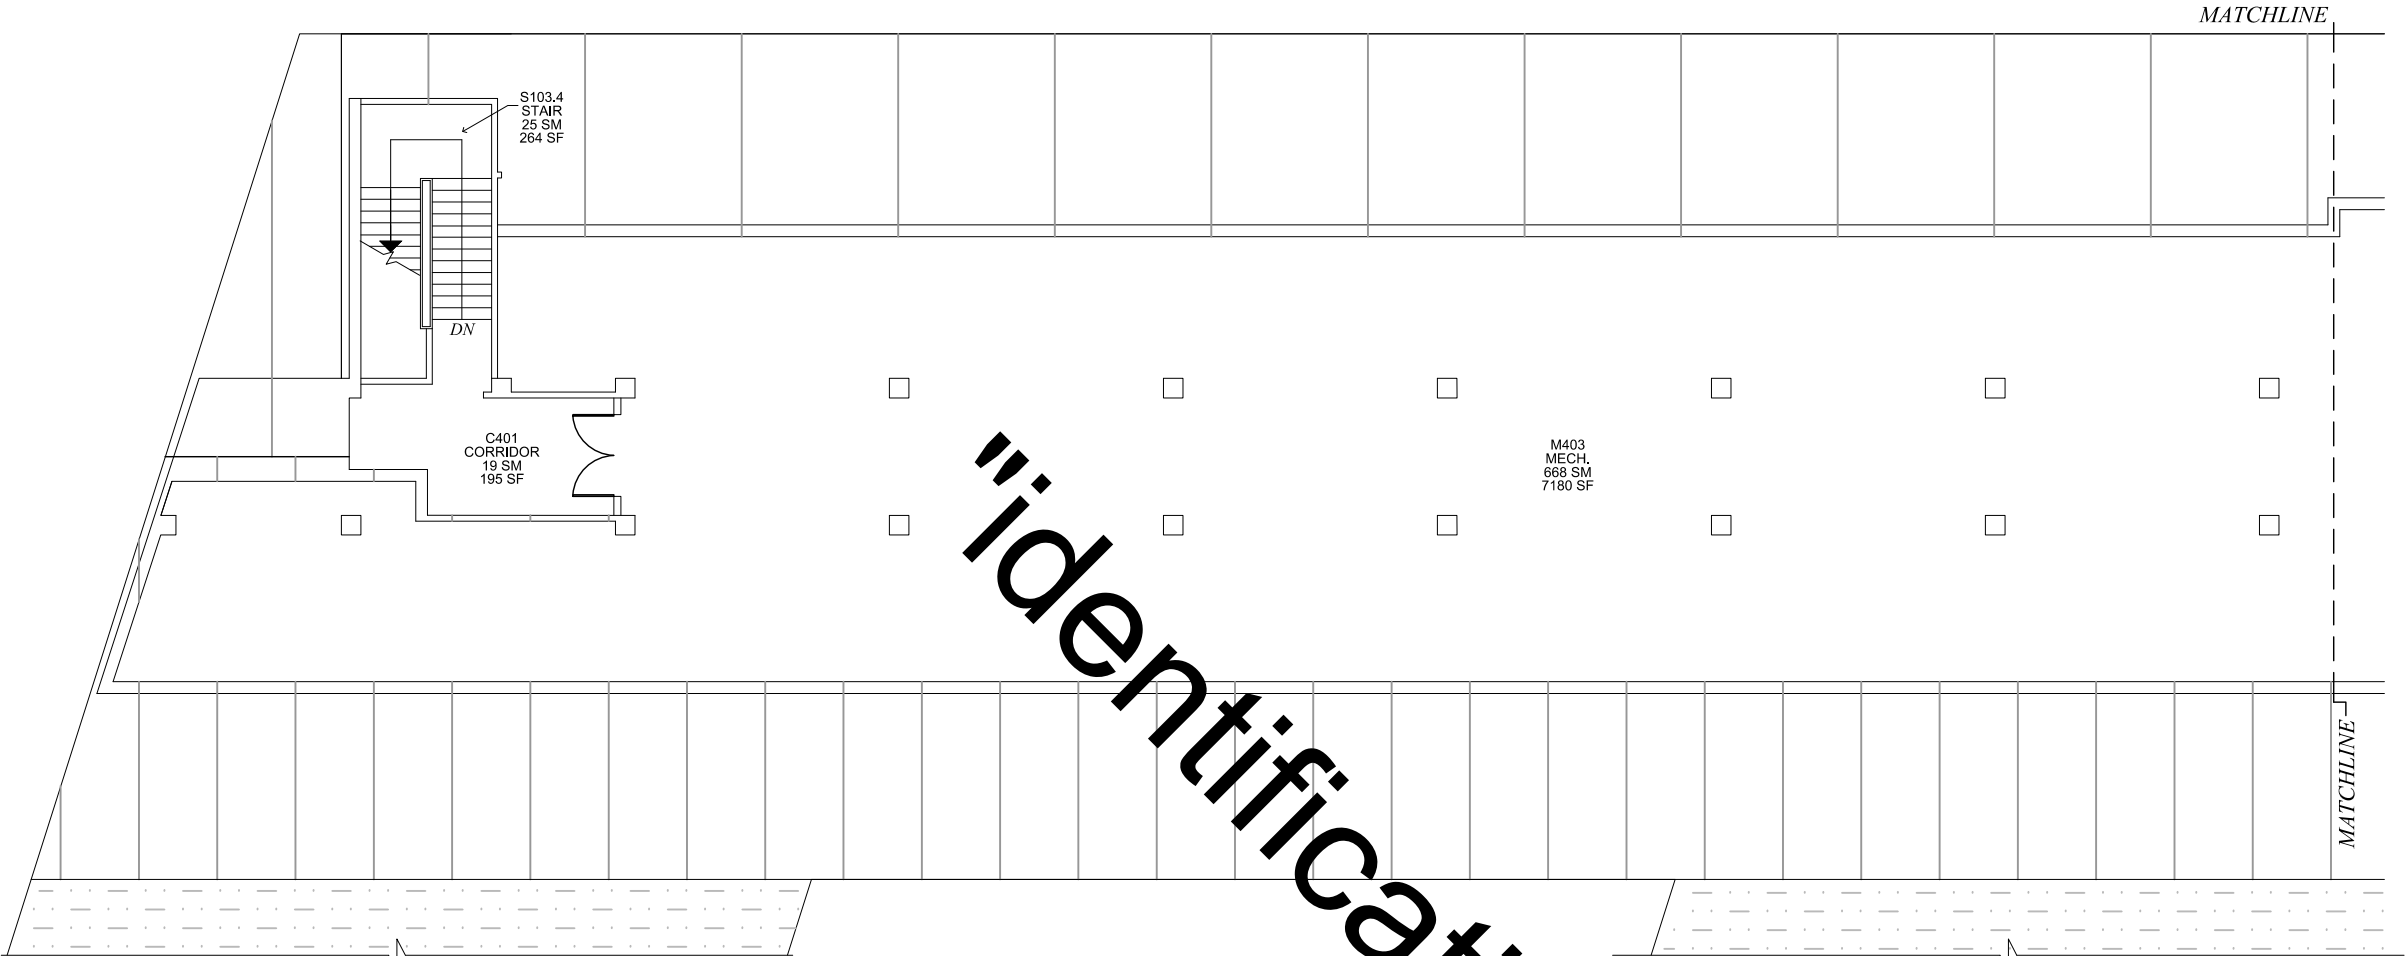


BUILDING 151 - FOURTH FLOOR

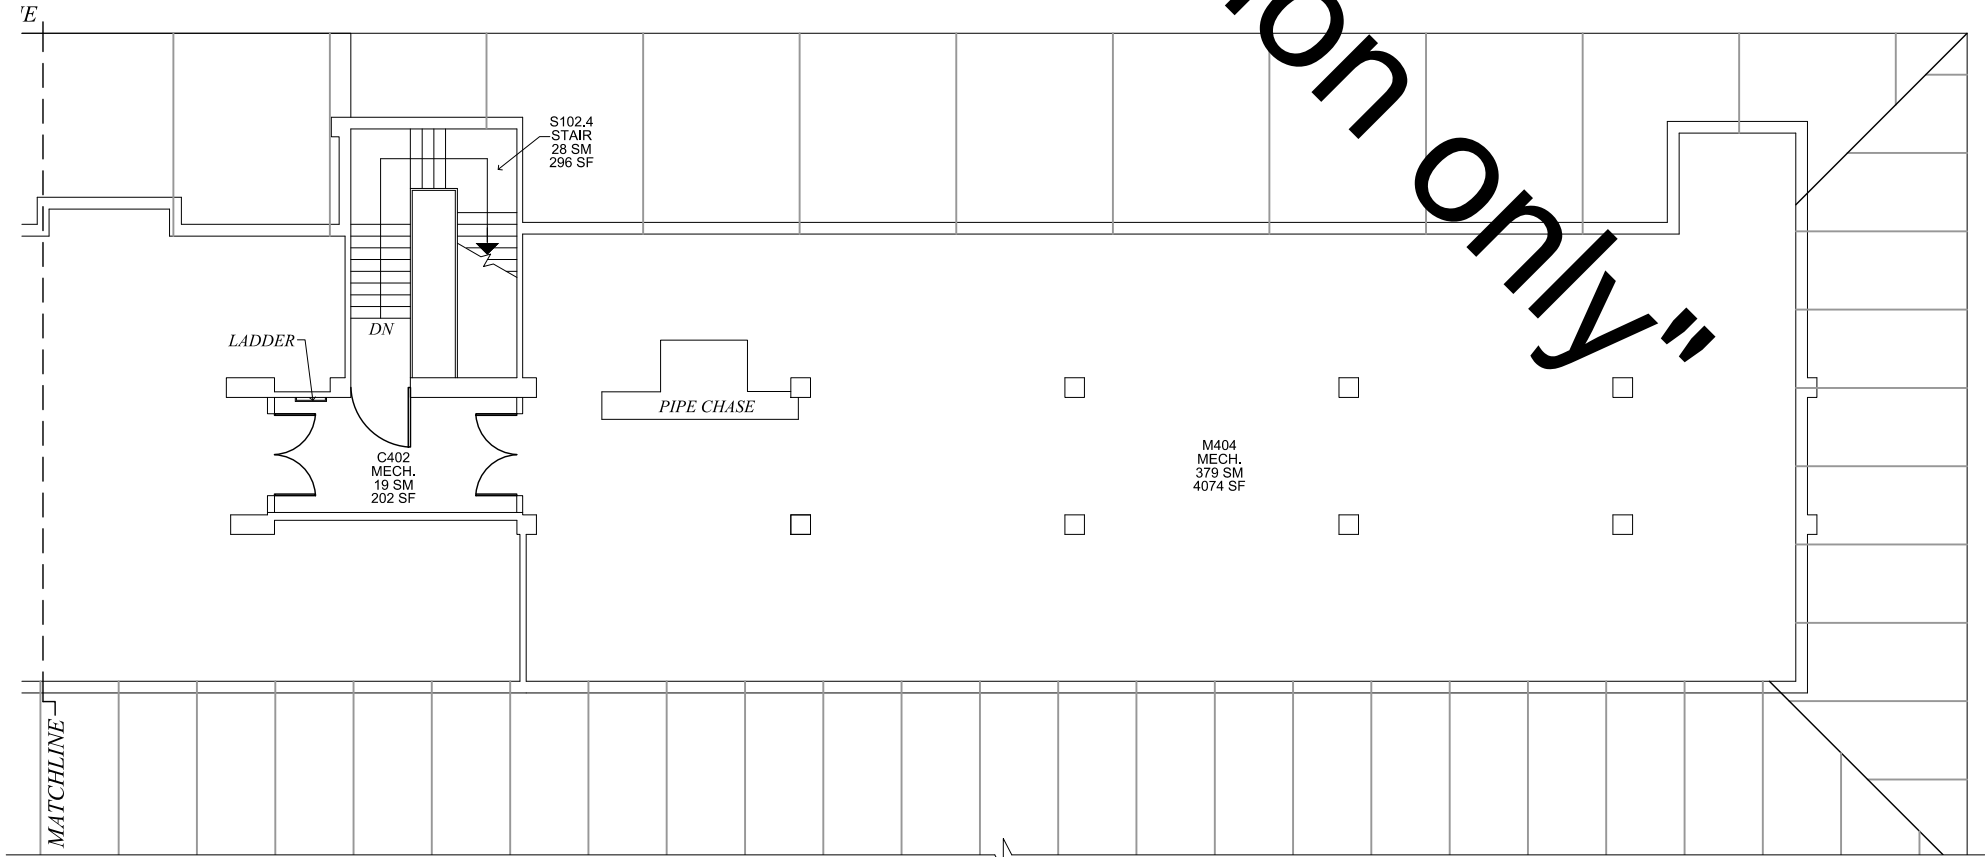

BUILDING 151 - FOURTH FLOOR

SYMBOL LEGEND	
DOOR	DRINKING FOUNTAIN
SLIDING DOOR	LAVATORY
ACCORDION PARTITION	SINK
STACK OR FOLDING PARTITION	TOILET
WINDOW/GLAZING	URINAL
HIGH WINDOW	LOCKER
SKYLIGHT	LAN DISTRIBUTION FRAME
STOOP/STEP UP	VENT HOOD
STAIR	WALL SHELVING
RAMP	UPPER CABINET
ACCESS LADDER	BASE CABINET
COLD STORAGE	TEACHER CABINET
AREA CALCULATED @ 50 %	MATCHLINE
SLOPING ROOF	FLAT ROOF

TITLEBLOCK LEGEND	
SHEET NAME:	BLDG #_FLOOR # (# IN SERIES)

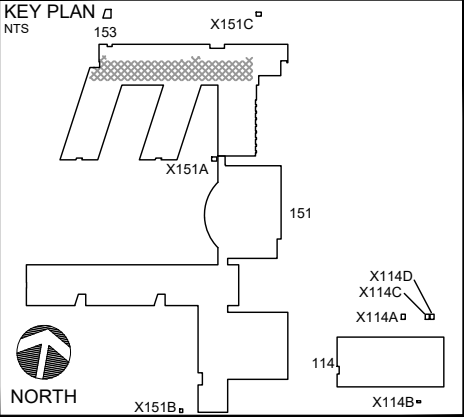

Updated By:	FUS Review:	100% Submittal Date:
SPF	MRS	01 MAY 2020
0 2 4 8 16 FT		

dodea
DEPARTMENT OF DEFENSE EDUCATION ACTIVITY
FACILITY UTILIZATION SURVEY

AVIANO ELEMENTARY SCHOOL
AVIANO MIDDLE / HIGH SCHOOL
BUILDING NUMBER: 151
COUNTRY: ITALY
INSTALLATION: AVIANO AIR BASE
SITE: AVIANO HOSPITAL-SCHOOL ANNEX
REGION-DISTRICT: DODEA EUROPE SOUTH

DoDAAC Number:	Floor:	Survey Date:
HE5649 / HE5603	LEVEL 4	JANUARY 2020
Sheet Name:	Sheet Seq:	
151_4 (1)	33 of 34	

