




NORTH

100% Submittal Date:
01 MAY 2020

NOT TO SCALE

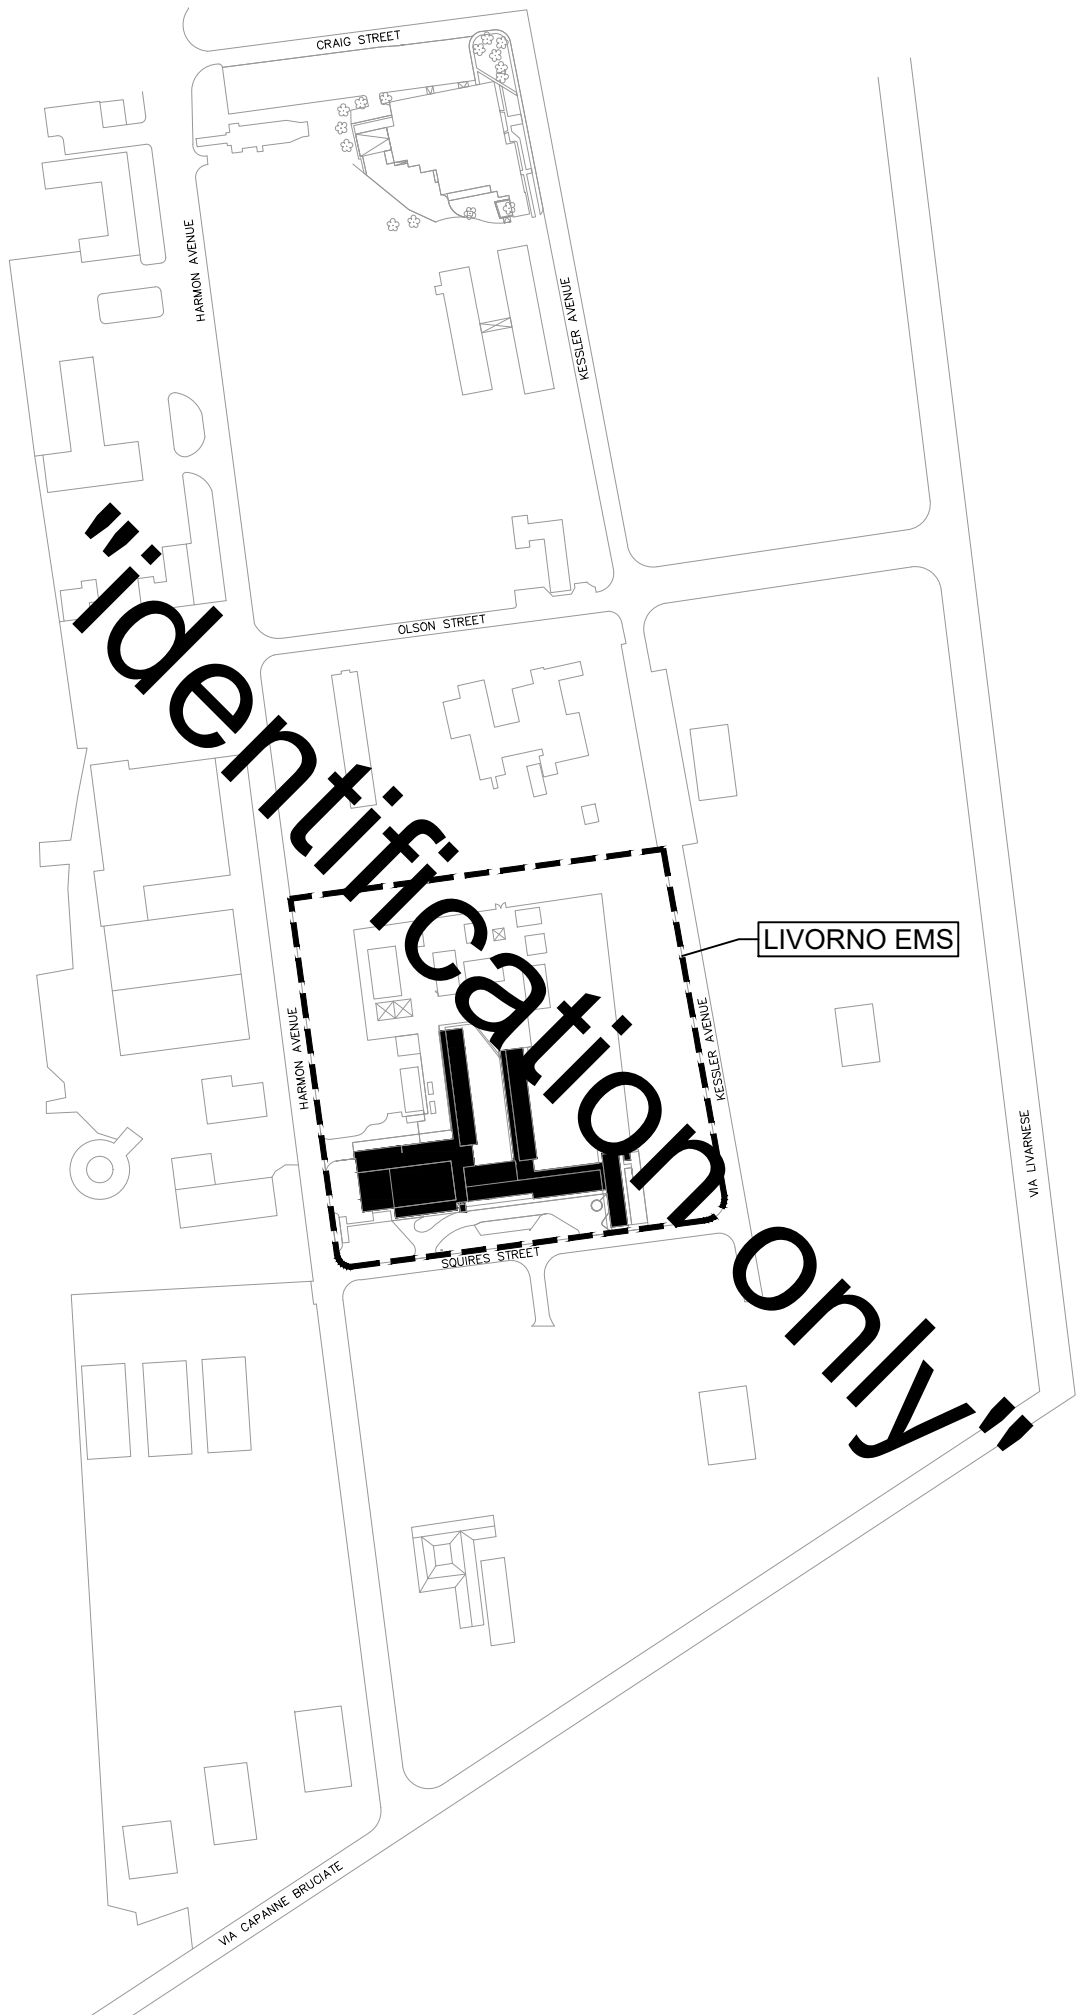



FACILITY UTILIZATION SURVEY

LIVORNO
ELEMENTARY / MIDDLE SCHOOL

COUNTRY: ITALY
INSTALLATION: US ARMY GARRISON ITALY
SITE: CAMP DARBY
REGION-DISTRICT: DODEA EUROPE SOUTH

DoDAAC Number: HE5408	Survey Date: JANUARY 2020
Sheet Name: LIVORNO_BASE MAP	Sheet Seq: 1 of 9

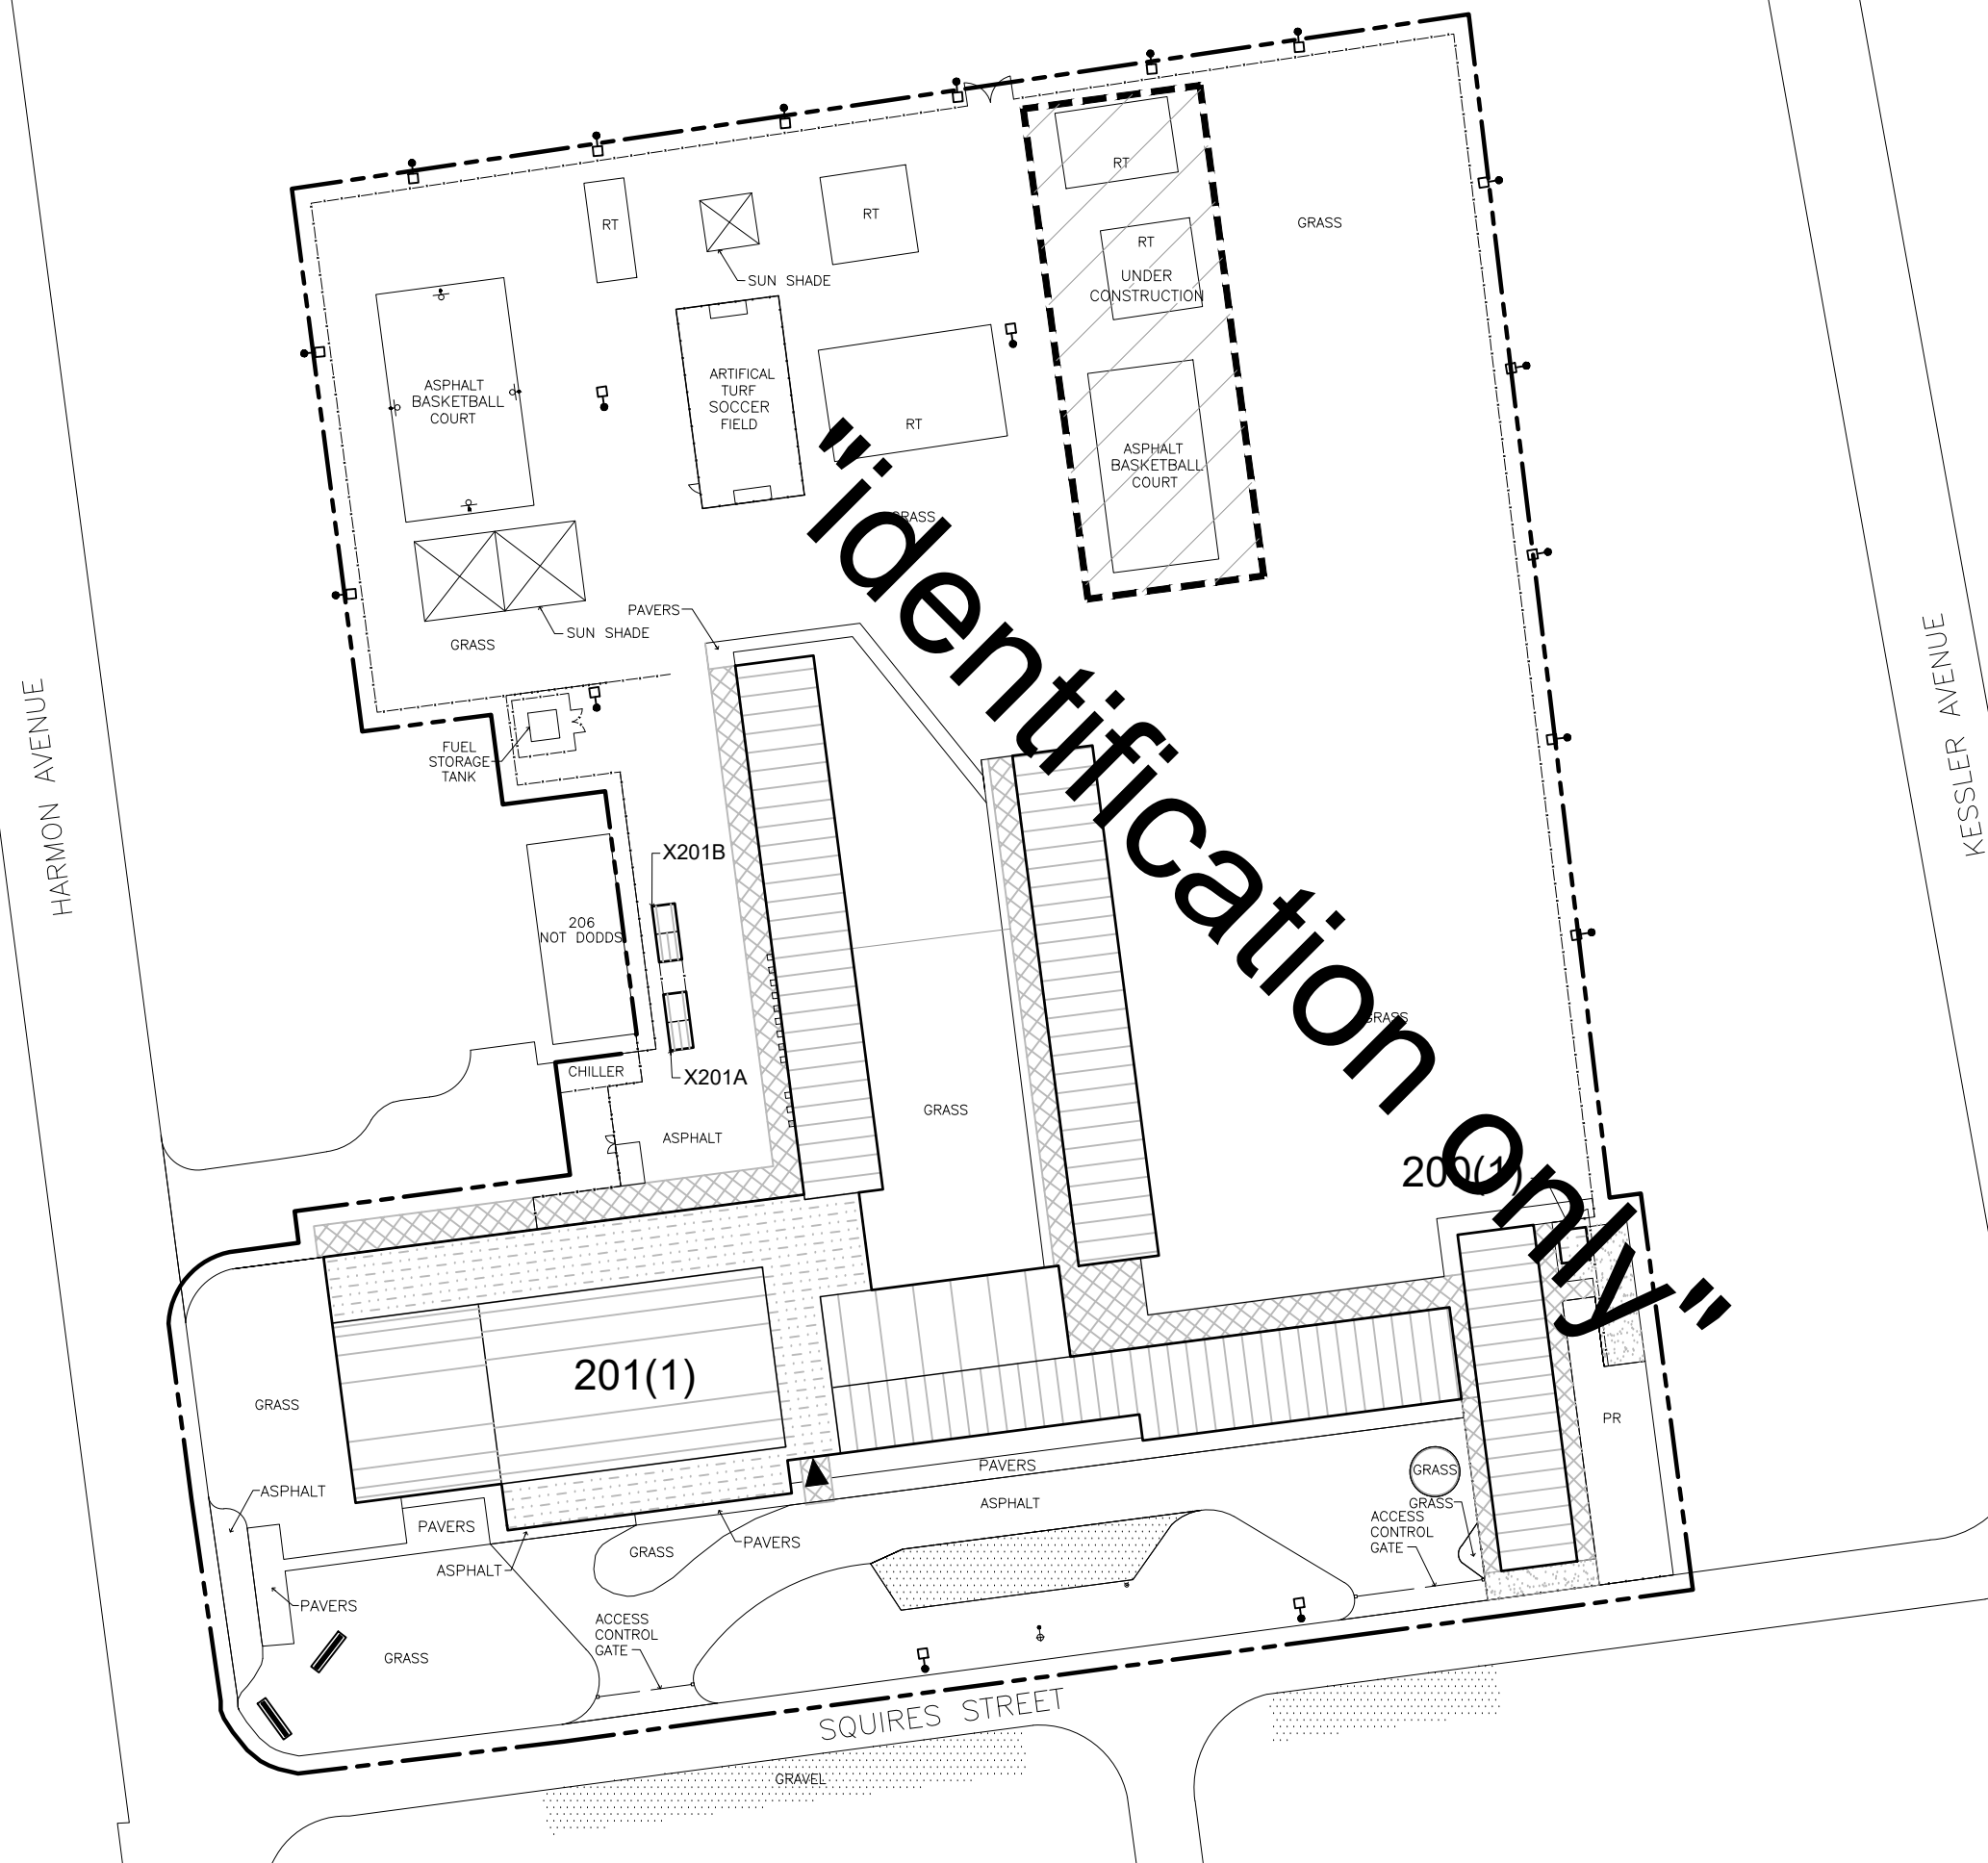

 SYMBOL LEGEND	
	BASKETBALL GOAL
	STADIUM LIGHT
	SIGN
	FOOTBALL GOAL
	BASEBALL BACKSTOP
	PARKING AREA
	FLAT ROOF
	SLOPE
	COVERED WALKWAY
	SLOPING ROOF
	PROPERTY LINE (APPROX. 21,788 SM) (APPROX. 5.38 AC)
	FENCE LINE
LEGEND	
PLAYGROUND SURFACING	
WC - WOOD CHIPS PR - POURED RUBBER M - MULCH	
SRT - SHREDDED RUBBER TIRES S - SAND	
PG - PEA GRAVEL RT - RUBBER TILES	
BUILDING LABEL	BLDG #_ (# OF FLOORS)

GSF CALCULATIONS

Building 200	
Floor 1	96
Total Area (SF)	96
50% Area (SF)	0
Gross Area (SF)	96

Building 201	
Floor 1	38,242
Mezzanine	367
Total Area (SF)	38,609
50% Area (SF)	4,777
Gross Area (SF)	43,386

BUILDING X201B - FIRST FLOOR

BUILDING X201A - FIRST FLOOR

BUILDING 201 - MEZZININE

BUILDING 201 - FIRST FLOOR


BUILDING 201 - MEZZININE

BUILDING 200
(STORAGE)
- FIRST FLOOR
- 96 GSF

NOTE 1: APPROXIMATELY 3% OF BUILDING 201 IS IDENTIFIED AS PARTIAL- USE, OCCUPIED BY CHILD AND YOUTH SERVICES (CYS).
NOTE 2: GSF CALCULATIONS BASED ON ARMY RPI DoA PAMPHLET 415-28.


SYMBOL LEGEND	
	DOOR
	DRINKING FOUNTAIN
	SLIDING DOOR
	LAVATORY
	ACCORDION PARTITION
	SINK
	STACK OR FOLDING PARTITION
	TOILET
	WINDOW/GLAZING
	URINAL
	HIGH WINDOW
	LOCKER
	SKYLIGHT
	LAN DISTRIBUTION FRAME
	STOOP/STEP UP
	VENT HOOD
	STAIR
	WALL SHELVING
	RAMP
	UPPER CABINET
	ACCESS LADDER
	BASE CABINET
	COLD STORAGE
	TEACHER CABINET
	AREA CALCULATED @ 50 %
	MATCHLINE
	SLOPING ROOF
	FLAT ROOF


TITLEBLOCK LEGEND	
SHEET NAME:	BLDG #_FLOOR # (# IN SERIES)

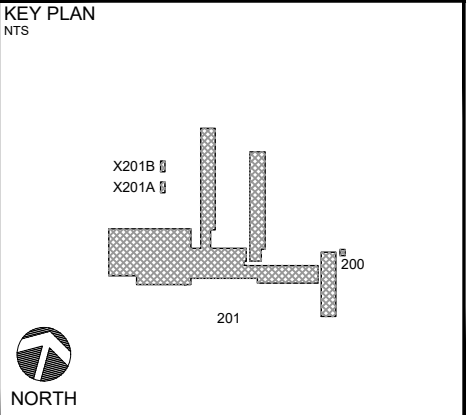

Updated By: SPF	FUS Review: MRS	100% Submittal Date: 01 MAY 2020
NOT TO SCALE		
 DEPARTMENT OF DEFENSE EDUCATION ACTIVITY FACILITY UTILIZATION SURVEY		
LIVORNO ELEMENTARY / MIDDLE SCHOOL BUILDING NUMBER: 200, 201, X201A, X201B COUNTRY: ITALY INSTALLATION: US ARMY GARRISON ITALY SITE: CAMP DARBY REGION-DISTRICT: DODEA EUROPE SOUTH		
DoDAAC Number: HE5408	Floor: LEVEL 1	Survey Date: JANUARY 2020
Sheet Name: GSF_1 (1)	Sheet Seq:	3 of 9

200				Capacity	Area (SF)	Area (SM)
Floor	Room	Current				
1	101	STORAGE		OTHER	79 SF	8 SM
201						
Floor	Room	Current		Capacity	Area (SF)	Area (SM)
1	100	NURSE		OTHER	132 SF	13 SM
1	100A	REST AREA		OTHER	111 SF	11 SM
1	100B	TOILET		OTHER	64 SF	6 SM
1	A01	TSC		OTHER	219 SF	21 SM
1	A01A	STORAGE		OTHER	35 SF	4 SM
1	A02	CONFERENCE		OTHER	410 SF	39 SM
1	A02A	STORAGE		OTHER	43 SF	4 SM
1	A03	RECEPTION		OTHER	264 SF	27 SM
1	A03A	RECORDS		OTHER	47 SF	5 SM
1	A04	PRINCIPAL		OTHER	480 SF	45 SM
1	A05	STORAGE	STUDENT - HALF		267 SF	20 SM
1	A05A	CENT. SUPPLY		OTHER	959 SF	52 SM
1	A06	BUS OFFICE		OTHER	284 SF	27 SM
1	A06A	STAFF		OTHER	30 SF	3 SM
1	C01	STAFF		OTHER	725 SF	68 SM
1	C02	GPC	STUDENT - FULL		726 SF	68 SM
1	C03	GPC	STUDENT - FULL		721 SF	67 SM
1	C04	SCIENCE LAB	STUDENT - FULL		748 SF	70 SM
1	C05	GPC	STUDENT - FULL		723 SF	68 SM
1	C06	MUSIC	STUDENT - FULL		1,471 SF	137 SM
1	C08	CENTRAL WORKROOM		OTHER	577 SF	54 SM
1	C08A	TOILET	NET - GENERAL		64 SF	6 SM
1	C09	GPC	STUDENT - FULL		943 SF	88 SM
1	C10	GPC	STUDENT - FULL		936 SF	87 SM
1	C11	STORAGE	OTHER		642 SF	60 SM
1	C11A	KLEN	OTHER		280 SF	27 SM
1	C12	MOD. TECH. LAB	STUDENT - HALF		377 SF	36 SM
1	C13A	MOD. TECH. LAB	STUDENT - HALF		351 SF	33 SM
1	C14	INFO CENTER	OTHER		2,582 SF	239 SM
1	C14A	ADMIN.WORK	OTHER		78 SF	8 SM
1	C15	COMPUTER LAB	STUDENT - FULL		673 SF	63 SM
1	C16	ASSESSMENT	OTHER		677 SF	63 SM
1	C101	CORRIDOR	NET - GENERAL		238 SF	23 SM
1	C102	CORRIDOR	NET - GENERAL		132 SF	12 SM
1	C103	CORRIDOR	NET - GENERAL		74 SF	7 SM
1	C105	CORRIDOR	NET - GENERAL		1,777 SF	166 SM
1	J101	JANITOR	NET - GENERAL		38 SF	4 SM
1	K01	KG	STUDENT - FULL		1,089 SF	102 SM
1	K01A	WORKROOM	OTHER		68 SF	7 SM
1	K01B	TOILET	NET - GENERAL		23 SF	3 SM
1	K01C	KITCHEN	OTHER		211 SF	20 SM
1	K02	KG	STUDENT - FULL		1,070 SF	101 SM
1	K02A	WORKROOM	OTHER		75 SF	7 SM
1	K02B	TOILET	NET - GENERAL		22 SF	3 SM
1	K11	DSHAWASH	OTHER		256 SF	28 SM
1	K12	KITCHEN	OTHER		887 SF	83 SM
1	K12A	DRY STORAGE	OTHER		229 SF	22 SM
1	M03	GYM	STUDENT - FULL		4,983 SF	463 SM
1	M03A	STAGE	OTHER		767 SF	74 SM
1	M04	CAFETERIA	OTHER		3,004 SF	285 SM
1	M101	MECH.	NET - MECH		555 SF	52 SM
1	M102	MECH.	NET - MECH		89 SF	9 SM
1	M103	MECH.	NET - MECH		81 SF	8 SM
1	S01	STORAGE	OTHER		58 SF	6 SM
1	S02	STORAGE	OTHER		75 SF	7 SM
1	S03	STORAGE	OTHER		87 SF	9 SM
1	S04	STORAGE	OTHER		40 SF	4 SM
1	S05	STORAGE	OTHER		88 SF	9 SM
1	S06	JANITOR	NET - GENERAL		64 SF	6 SM
1	S07	LAN	NET - MECH		172 SF	16 SM
1	S08	LAN	NET - MECH		93 SF	9 SM
1	ST1	STORAGE	STUDENT - HALF		93 SF	9 SM
1	T01	TOILET	NET - GENERAL		242 SF	23 SM
1	T01A	SHOWER	OTHER		10 SF	1 SM
1	T01B	TOILET	NET - GENERAL		41 SF	4 SM
1	T02	TOILET	NET - GENERAL		241 SF	23 SM
1	T02A	SHOWER	OTHER		10 SF	1 SM
1	T02B	TOILET	NET - GENERAL		41 SF	4 SM
1	T03	TOILET	NET - GENERAL		163 SF	16 SM
1	T04	TOILET	NET - GENERAL		147 SF	14 SM
1	T05	TOILET	NET - GENERAL		40 SF	4 SM
1	T06	JANITOR	NET - GENERAL		102 SF	10 SM
1	T108	TOILET	NET - GENERAL		95 SF	9 SM
1	T109	TOILET	NET - GENERAL		38 SF	4 SM
2	118A	STORAGE	OTHER		168 SF	16 SM
2	118B	STORAGE	OTHER		168 SF	16 SM

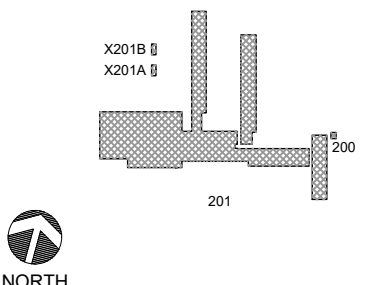SYMBOL LEGEND		
	DOOR	 DRINKING FOUNTAIN
	SLIDING DOOR	 LAVATORY
	ACCORDION PARTITION	 SINK
	STACK OR FOLDING PARTITION	 TOILET
	WINDOW/GLAZING	 URINAL
	HIGH WINDOW	 LOCKER
	SKYLIGHT	 LAN DISTRIBUTION FRAME
	STOOP/STEP UP	 VENT HOOD
	STAIR	 WALL SHELVING
	RAMP	 UPPER CABINET
	ACCESS LADDER	 BASE CABINET
	COLD STORAGE	 TEACHER CABINET
	AREA CALCULATED @ 50 %	 MATCHLINE
	SLOPING ROOF	 FLAT ROOF
TITLEBLOCK LEGEND		
SHEET NAME:		BLDG #, FLOOR # (# IN SERIES)
KEY PLAN		
NTS		
		
Updated By: SPF	FUS Review: MRS	100% Submittal Date: 01 MAY 2020
NOT TO SCALE		
 DEPARTMENT OF DEFENSE EDUCATION ACTIVITY FACILITY UTILIZATION SURVEY		
LIVORNO ELEMENTARY / MIDDLE SCHOOL BUILDING NUMBER: 200, 201, X201A, X201B COUNTRY: ITALY INSTALLATION: US ARMY GARRISON ITALY SITE: CAMP DARBY REGION-DISTRICT: DODEA EUROPE SOUTH		
DoDAAC Number: HE5408	Floor: LEVEL 1	Survey Date: JANUARY 2020
Sheet Name: SCHEDULES (1)		Sheet Seq: 4 of 9

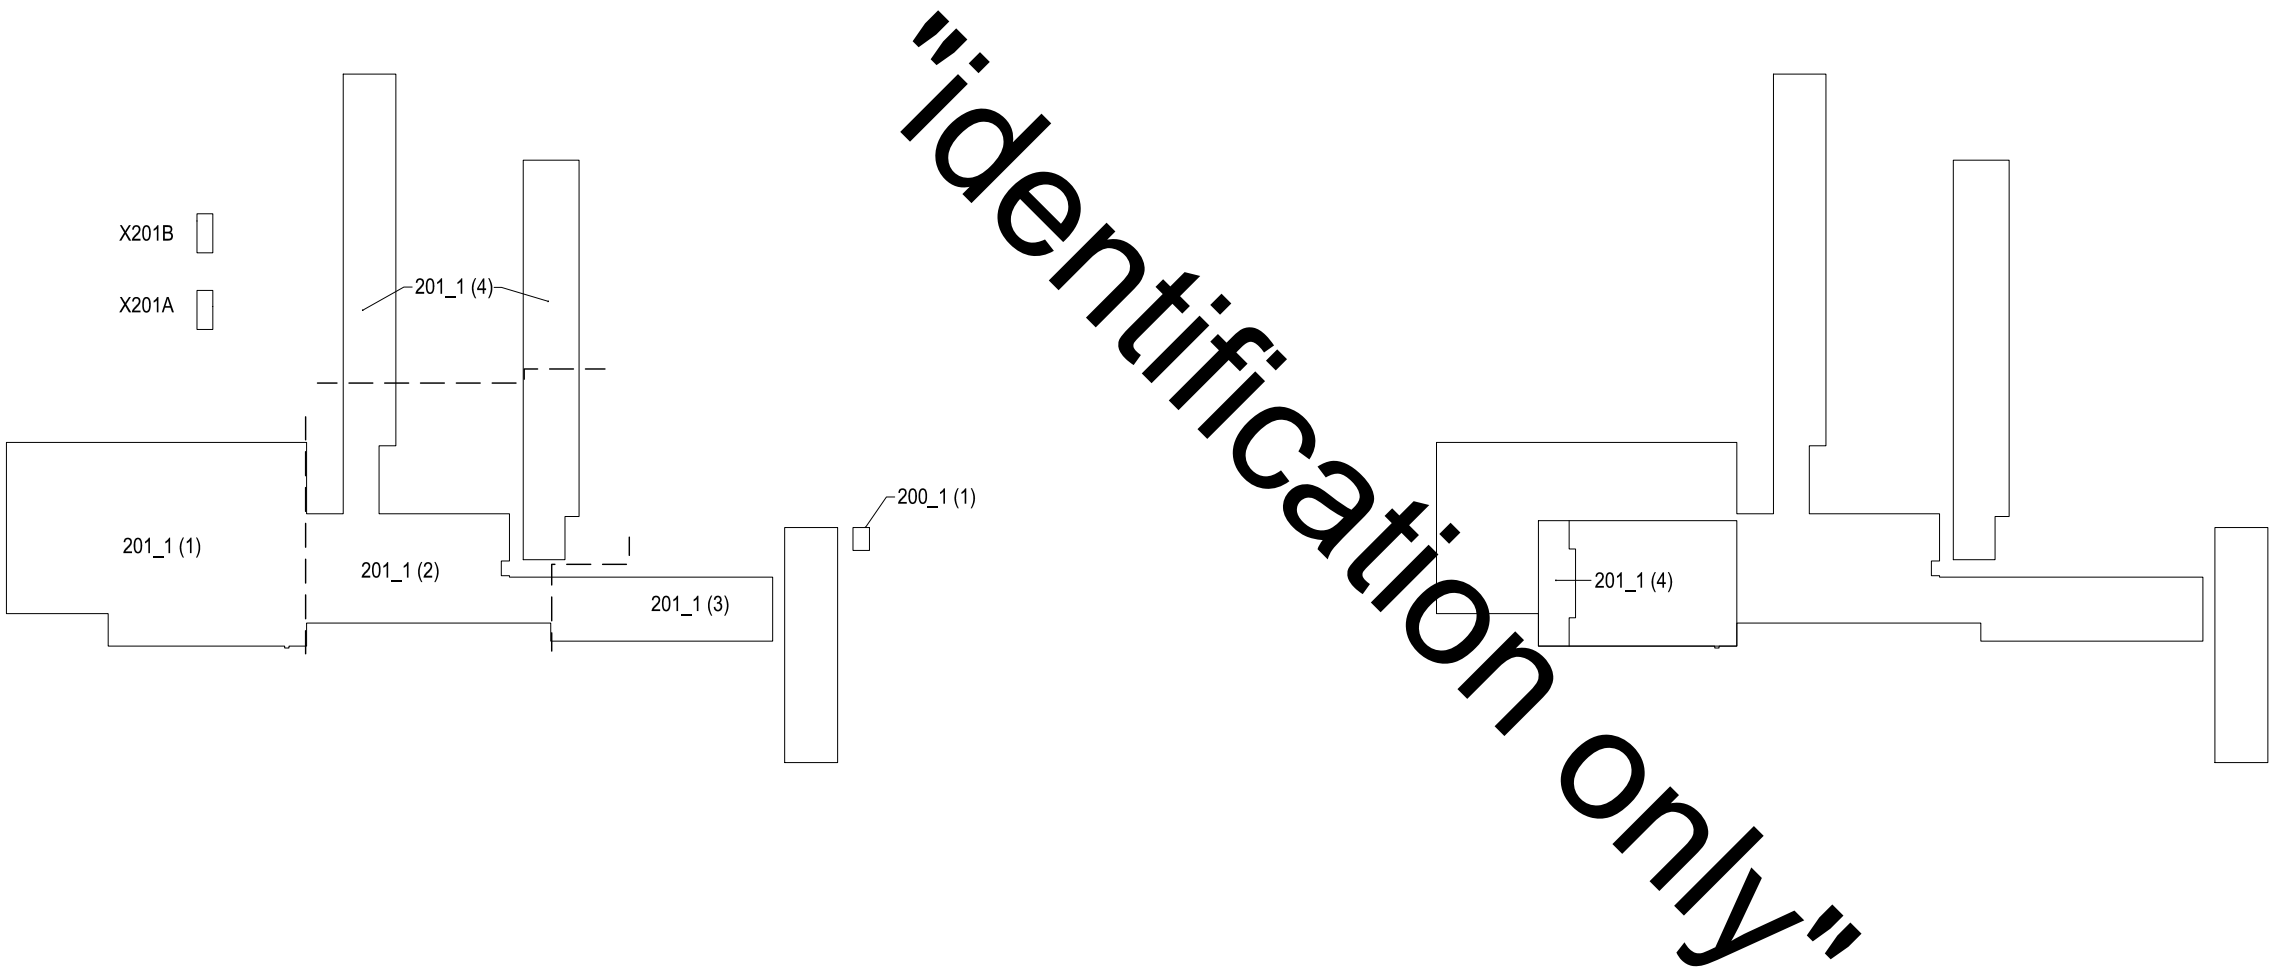

DOOR

SLIDING DOOR

ACCORDION PARTITION

STACK OR FOLDING PARTITION

WINDOW/GLAZING

HIGH WINDOW

SKYLIGHT

STOOP/STEP UP

STAIR

RAMP

ACCESS LADDER

COLD STORAGE

AREA CALCULATED @ 50 %

SLOPING ROOF

DRINKING FOUNTAIN

LAVATORY

SINK

TOILET

URINAL

LOCKER

LAN DISTRIBUTION FRAME

VENT HOOD

WALL SHELVING

UPPER CABINET

BASE CABINET

TEACHER CABINET

MATCHLINE

FLAT ROOF

TITLEBLOCK LEGEND

SHEET NAME:

BLDG #_ FLOOR # (# IN SERIES)

KEY PLAN

NTS

X201B

X201A

200

201

NORTH

Updated By:

FUS Review:

100% Submittal Date:

SPF

MRS

01 MAY 2020

NOT TO SCALE

dodea

DEPARTMENT OF DEFENSE EDUCATION ACTIVITY

FACILITY UTILIZATION SURVEY

LIVORNO

ELEMENTARY / MIDDLE SCHOOL

BUILDING NUMBER: 200, 201, X201A, X201B

COUNTRY: ITALY

INSTALLATION: US ARMY GARRISON ITALY

SITE: CAMP DARBY

REGION-DISTRICT: DODEA EUROPE SOUTH

DoDAAC Number:

HE5408

Floor:

LEVEL 1

Survey Date:


JANUARY 2020

Sheet Name:

KEY PLAN


Sheet Seq:

5 of 9

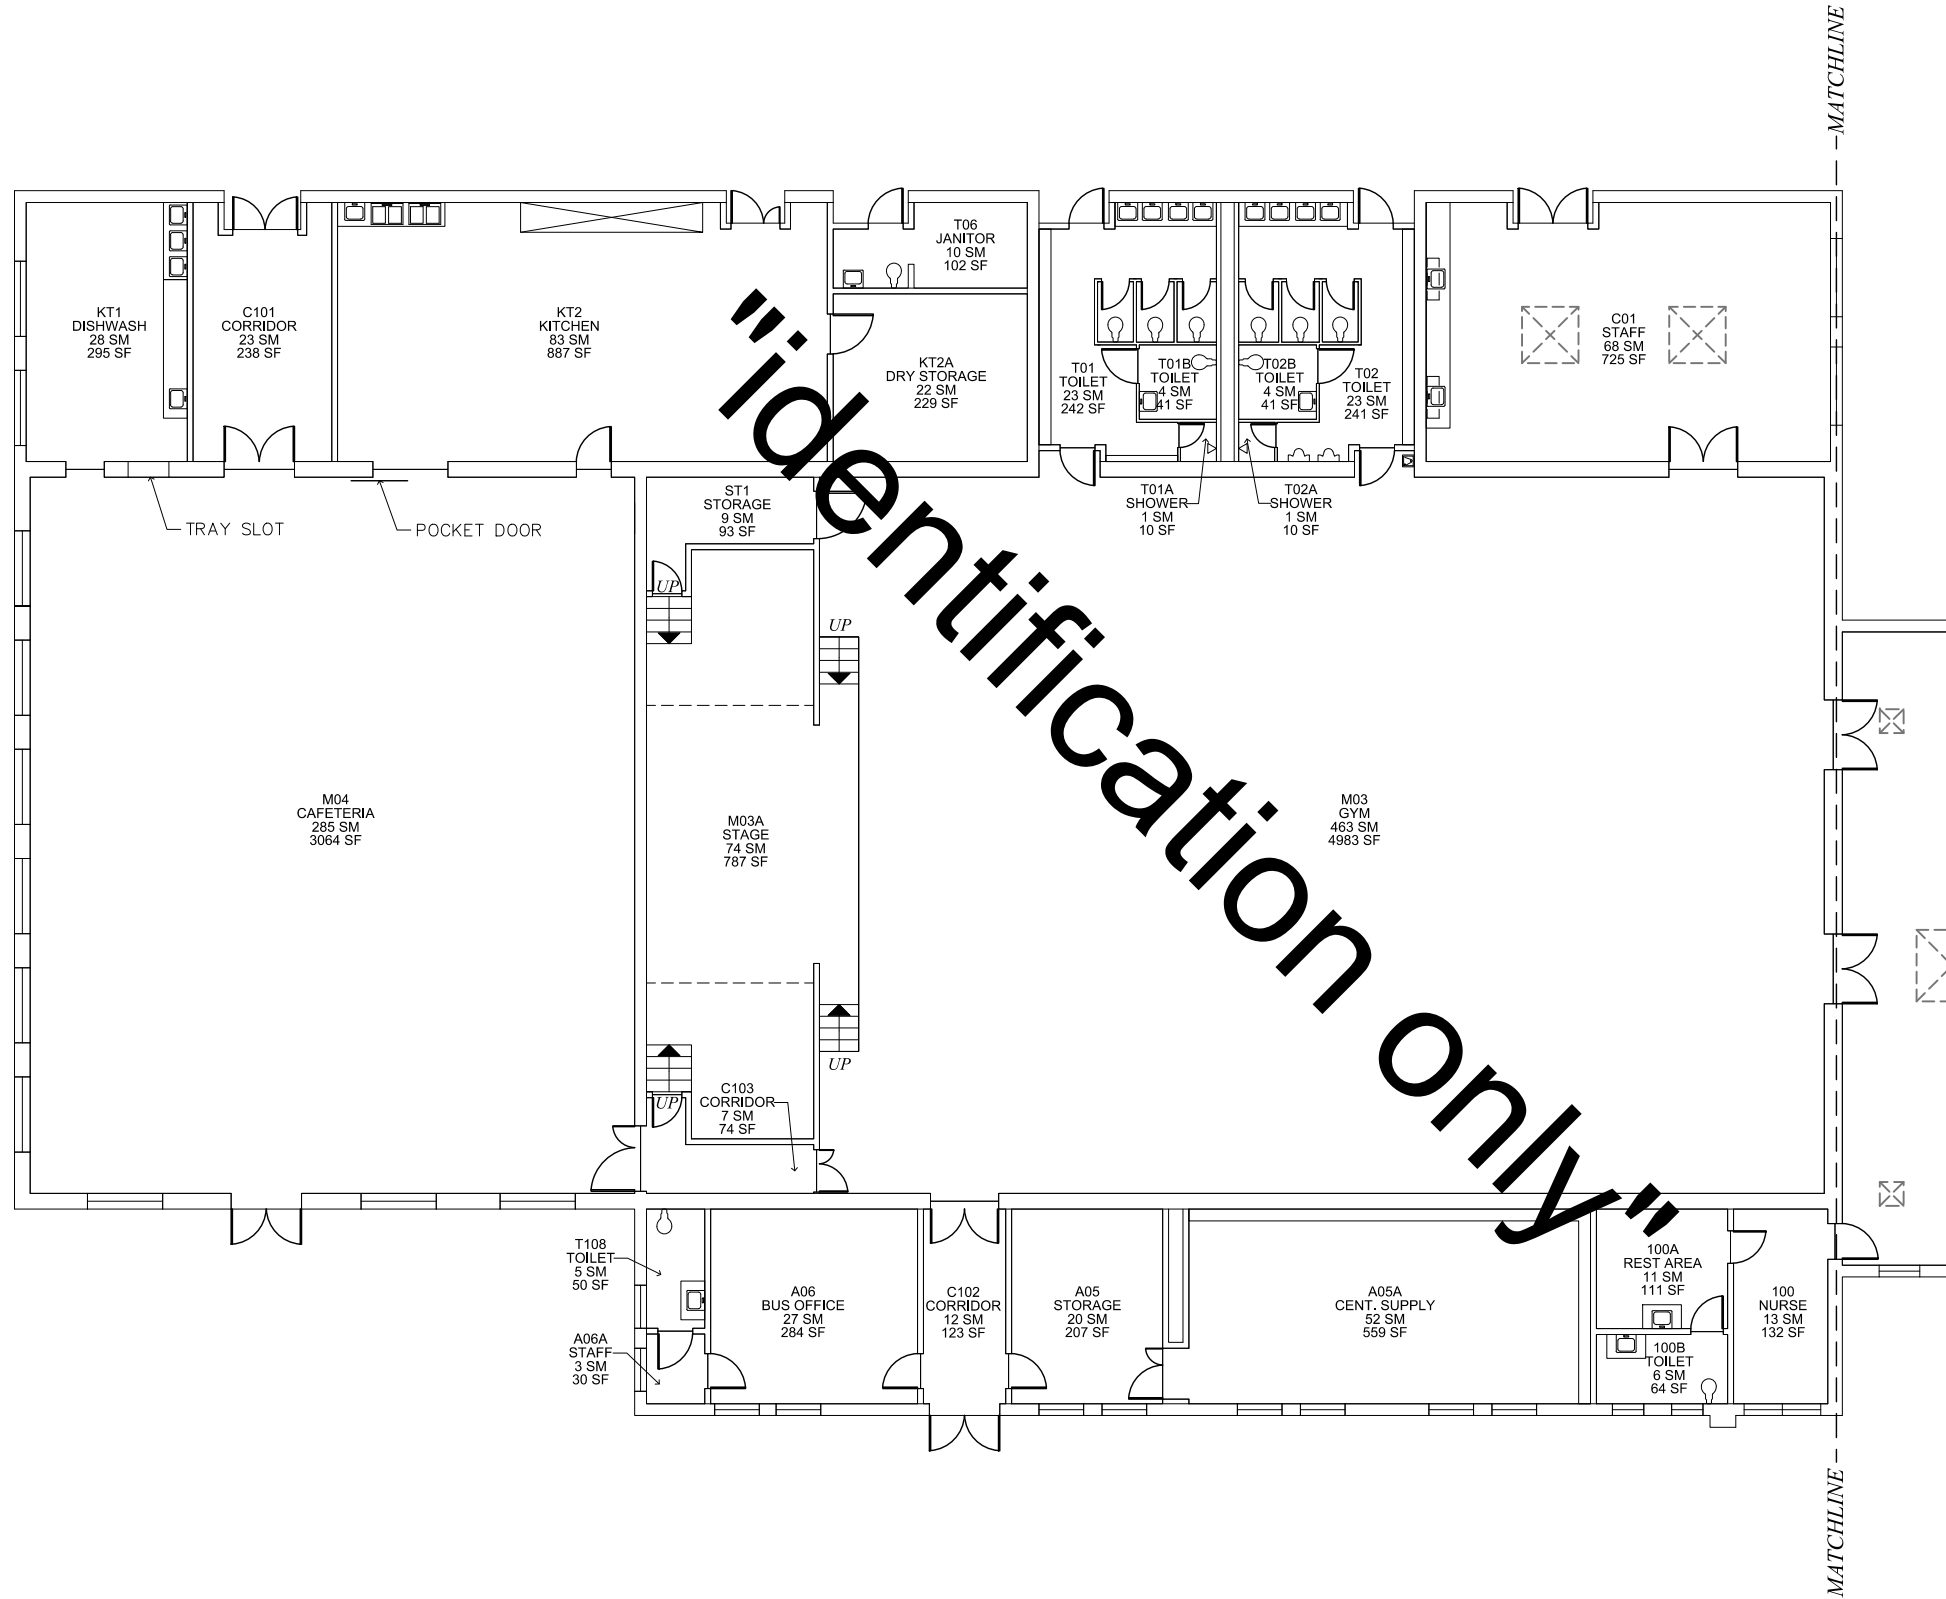

SYMBOL LEGEND	
	DOOR
	DRINKING FOUNTAIN
	SLIDING DOOR
	LAVATORY
	ACCORDION PARTITION
	SINK
	STACK OR FOLDING PARTITION
	TOILET
	WINDOW/GLAZING
	URINAL
	HIGH WINDOW
	LOCKER
	SKYLIGHT
	LAN DISTRIBUTION FRAME
	STOOP/STEP UP
	VENT HOOD
	STAIR
	WALL SHELVING
	RAMP
	UPPER CABINET
	ACCESS LADDER
	BASE CABINET
	COLD STORAGE
	TEACHER CABINET
	AREA CALCULATED @ 50 %
	MATCHLINE
	SLOPING ROOF
	FLAT ROOF

TITLEBLOCK LEGEND	
SHEET NAME:	BLDG #_FLOOR # (# IN SERIES)

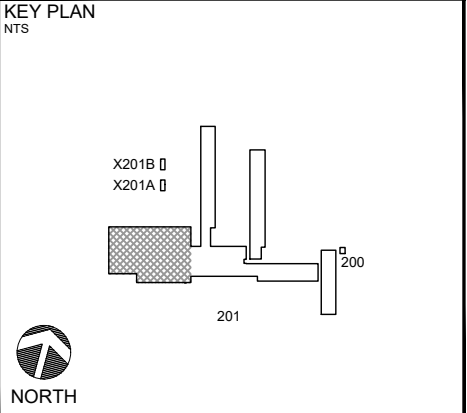

Updated By:	FUS Review:	100% Submittal Date:
SPF	MRS	01 MAY 2020


0 2 4 8 16 FT

DEPARTMENT OF DEFENSE EDUCATION ACTIVITY

FACILITY UTILIZATION SURVEY


LIVORNO
ELEMENTARY / MIDDLE SCHOOL
BUILDING NUMBER: 201
COUNTRY: ITALY
INSTALLATION: US ARMY GARRISON ITALY
SITE: CAMP DARBY
REGION-DISTRICT: DODEA EUROPE SOUTH

DoDAAC Number:	Floor:	Survey Date:
HE5408	LEVEL 1	JANUARY 2020
Sheet Name:	Sheet Seq:	
201_1 (1)	6 of 9	

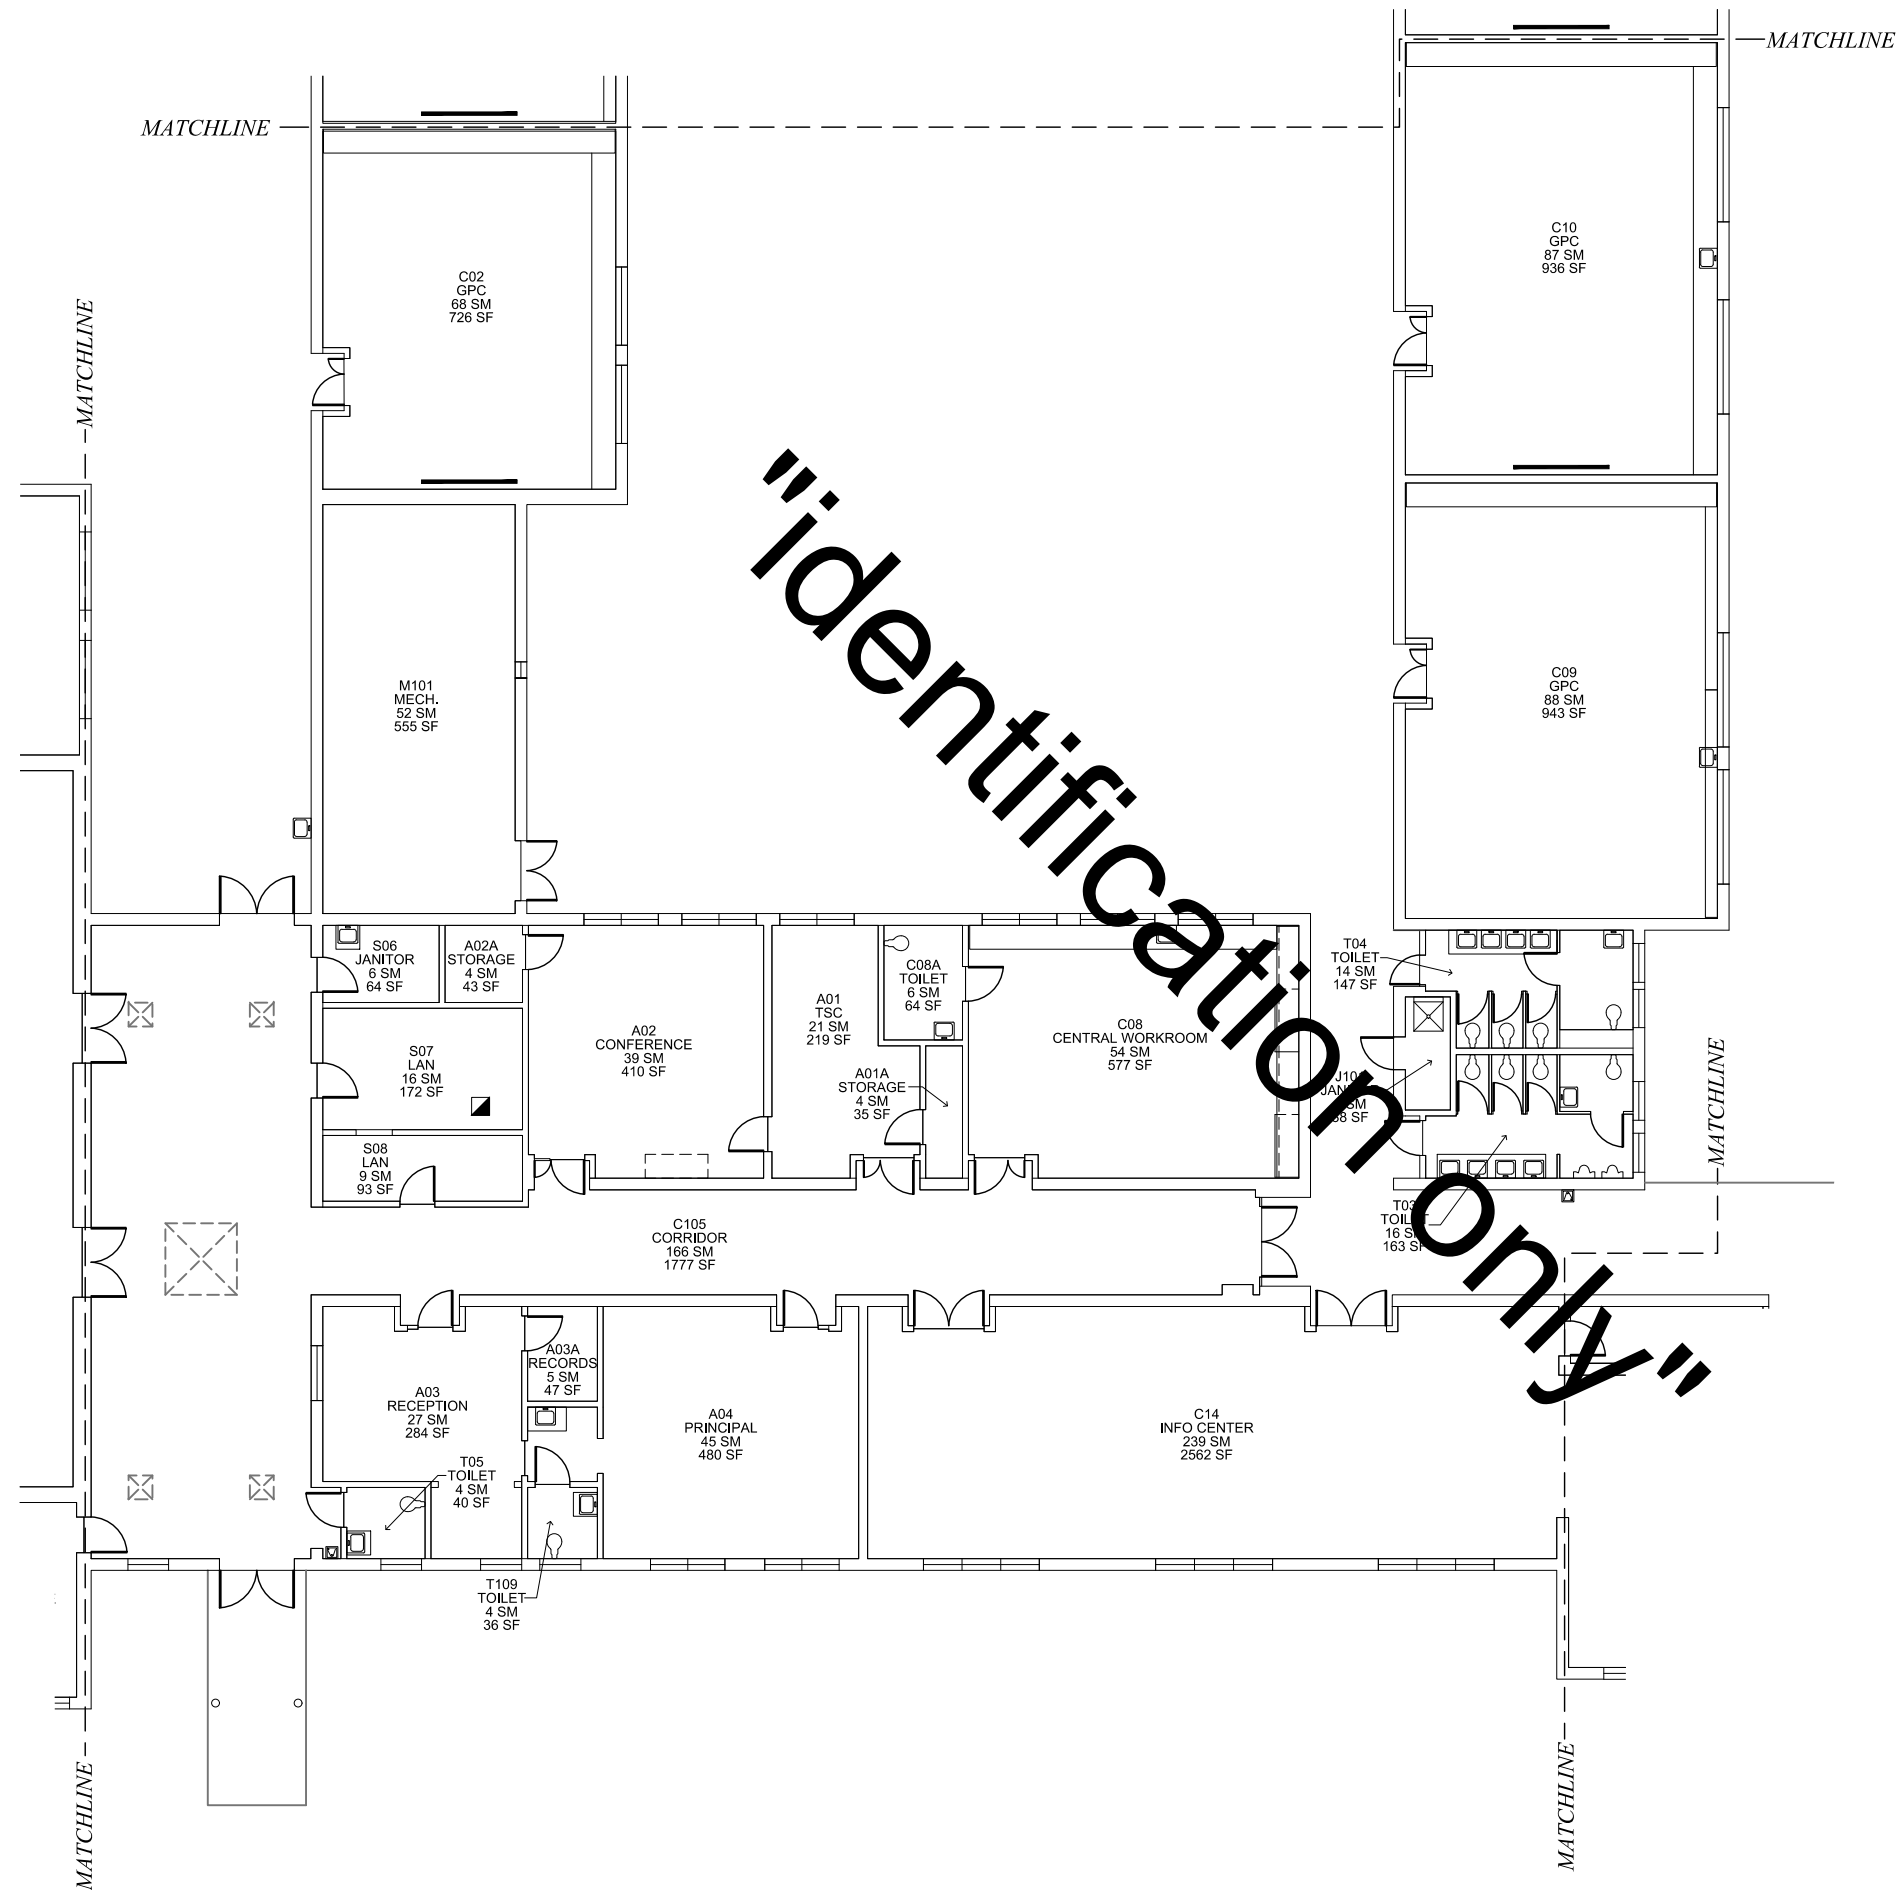

SYMBOL LEGEND	
DOOR	DRINKING FOUNTAIN
SLIDING DOOR	LAVATORY
ACCORDION PARTITION	SINK
STACK OR FOLDING PARTITION	TOILET
WINDOW/GLAZING	URINAL
HIGH WINDOW	LOCKER
SKYLIGHT	LAN DISTRIBUTION FRAME
STOOP/STEP UP	VENT HOOD
STAIR	WALL SHELVING
RAMP	UPPER CABINET
ACCESS LADDER	BASE CABINET
COLD STORAGE	TEACHER CABINET
AREA CALCULATED @ 50 %	MATCHLINE
SLOPING ROOF	FLAT ROOF

TITLEBLOCK LEGEND	
SHEET NAME:	BLDG #_FLOOR # (# IN SERIES)

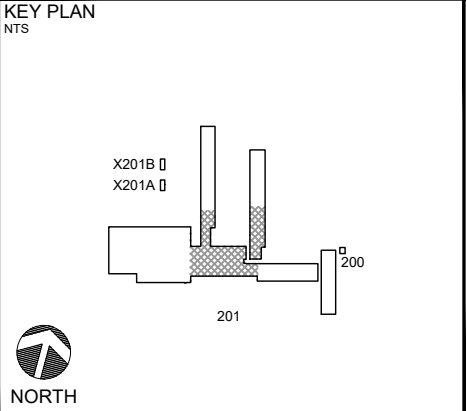



Updated By: SPF	FUS Review: MRS	100% Submittal Date: 01 MAY 2020
0 2 4 8 16 FT		




dodea
DEPARTMENT OF DEFENSE EDUCATION ACTIVITY
FACILITY UTILIZATION SURVEY


LIVORNO
ELEMENTARY / MIDDLE SCHOOL
BUILDING NUMBER: 201
COUNTRY: ITALY
INSTALLATION: US ARMY GARRISON ITALY
SITE: CAMP DARBY
REGION-DISTRICT: DODEA EUROPE SOUTH

DoDAAC Number: HE5408	Floor: LEVEL 1	Survey Date: JANUARY 2020
Sheet Name: 201_1 (2)	Sheet Seq: 7 of 9	

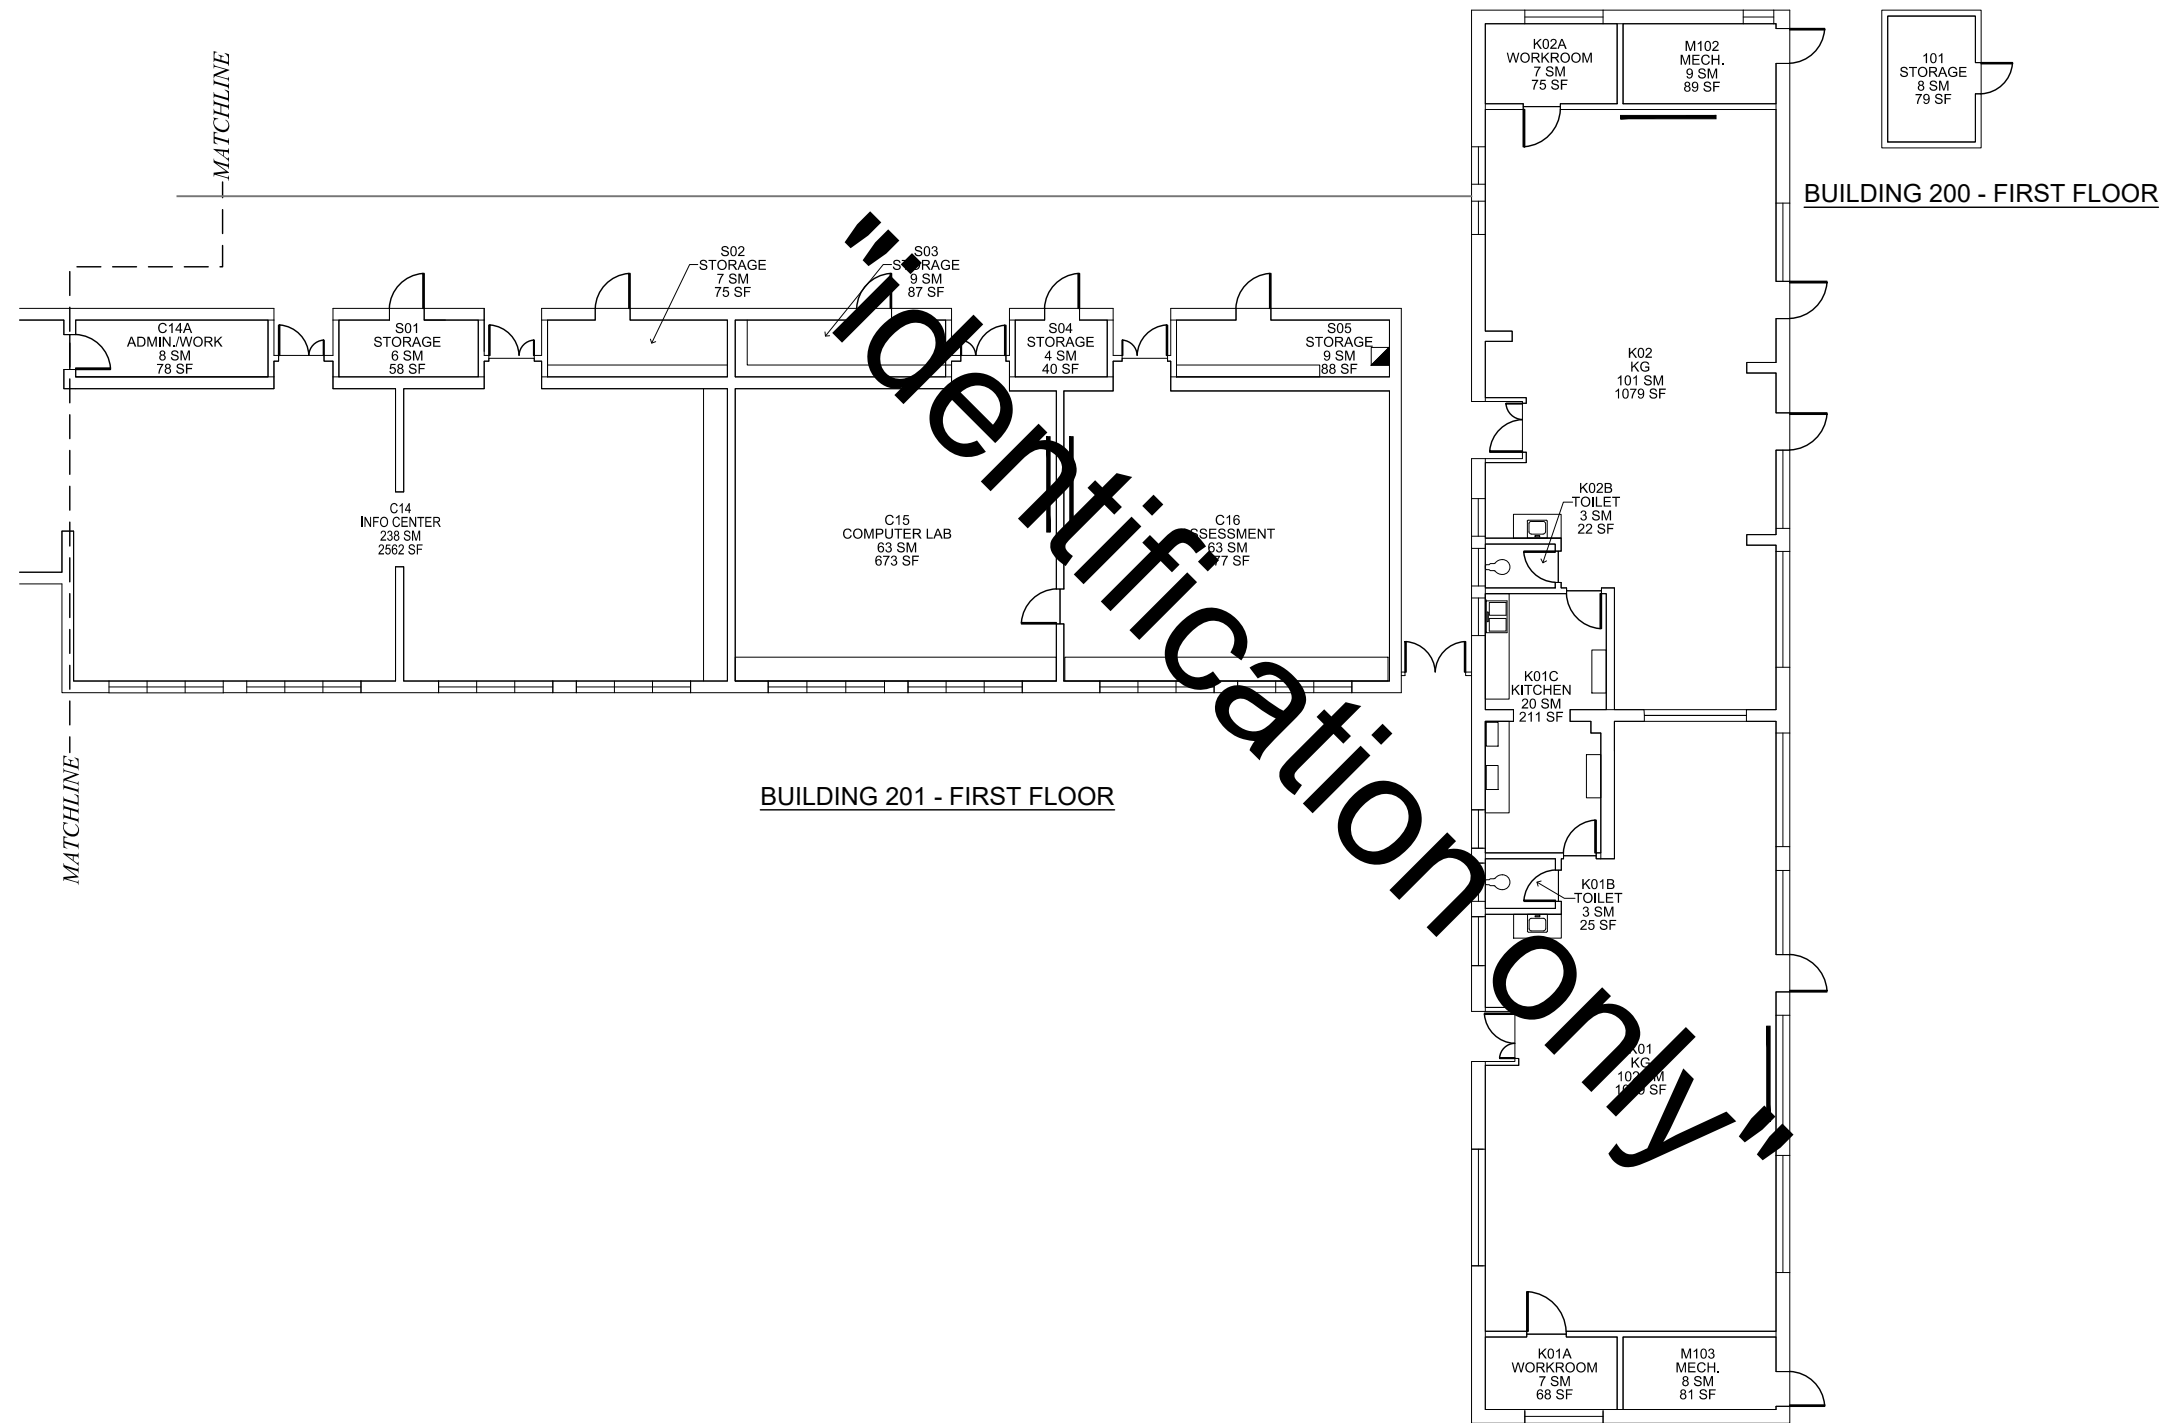

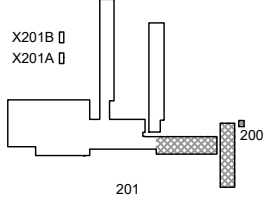SYMBOL LEGEND			
	DOOR		DRINKING FOUNTAIN
	SLIDING DOOR		LAVATORY
	ACCORDION PARTITION		SINK
	STACK OR FOLDING PARTITION		TOILET
	WINDOW/GLAZING		URINAL
	HIGH WINDOW		LOCKER
	SKYLIGHT		LAN DISTRIBUTION FRAME
	STOOP/STEP UP		VENT HOOD
	STAIR		WALL SHELVING
	RAMP		UPPER CABINET
	ACCESS LADDER		BASE CABINET
	COLD STORAGE		TEACHER CABINET
	AREA CALCULATED @ 50 %		MATCHLINE
	SLOPING ROOF		FLAT ROOF
TITLEBLOCK LEGEND			
SHEET NAME:		BLDG #_FLOOR # (# IN SERIES)	
KEY PLAN			
NTS			
			
			
NORTH			
Updated By:		FUS Review:	100% Submittal Date:
SPF		MRS	01 MAY 2020
			
			
FACILITY UTILIZATION SURVEY			
LIVORNO			
ELEMENTARY / MIDDLE SCHOOL			
BUILDING NUMBER: 200, 201			
COUNTRY: ITALY			
INSTALLATION: US ARMY GARRISON ITALY			
SITE: CAMP DARBY			
REGION-DISTRICT: DODEA EUROPE SOUTH			
DoDAAC Number:		Floor:	Survey Date:
HE5408		LEVEL 1	JANUARY 2020
Sheet Name:			Sheet Seq:
201_1 (3)			8 of 9

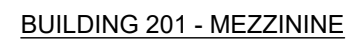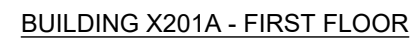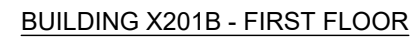

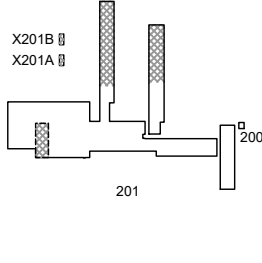SYMBOL LEGEND		
	DOOR	 DRINKING FOUNTAIN
	SLIDING DOOR	 LAVATORY
	ACCORDION PARTITION	 SINK
	STACK OR FOLDING PARTITION	 TOILET
	WINDOW/GLAZING	 URINAL
	HIGH WINDOW	 LOCKER
	SKYLIGHT	 LAN DISTRIBUTION FRAME
	STOOP/STEP UP	 VENT HOOD
	STAIR	 WALL SHELVING
	RAMP	 UPPER CABINET
	ACCESS LADDER	 BASE CABINET
	COLD STORAGE	 TEACHER CABINET
	AREA CALCULATED @ 50 %	 MATCHLINE
	SLOPING ROOF	 FLAT ROOF
TITLEBLOCK LEGEND		
SHEET NAME:		BLDG #, FLOOR # (# IN SERIES)
KEY PLAN		
NTS		
		
Updated By:	FUS Review:	100% Submittal Date:
SPF	MRS	01 MAY 2020
		
 DEPARTMENT OF DEFENSE EDUCATION ACTIVITY FACILITY UTILIZATION SURVEY		
LIVORNO ELEMENTARY / MIDDLE SCHOOL BUILDING NUMBER: 201, X201A, X201B COUNTRY: ITALY INSTALLATION: US ARMY GARRISON ITALY SITE: CAMP DARBY REGION-DISTRICT: DODEA EUROPE SOUTH		
DoDAAC Number:	Floor:	Survey Date:
HE5408	LEVEL 1	JANUARY 2020
Sheet Name:		Sheet Seq:
201_1 (4)		9 of 9