



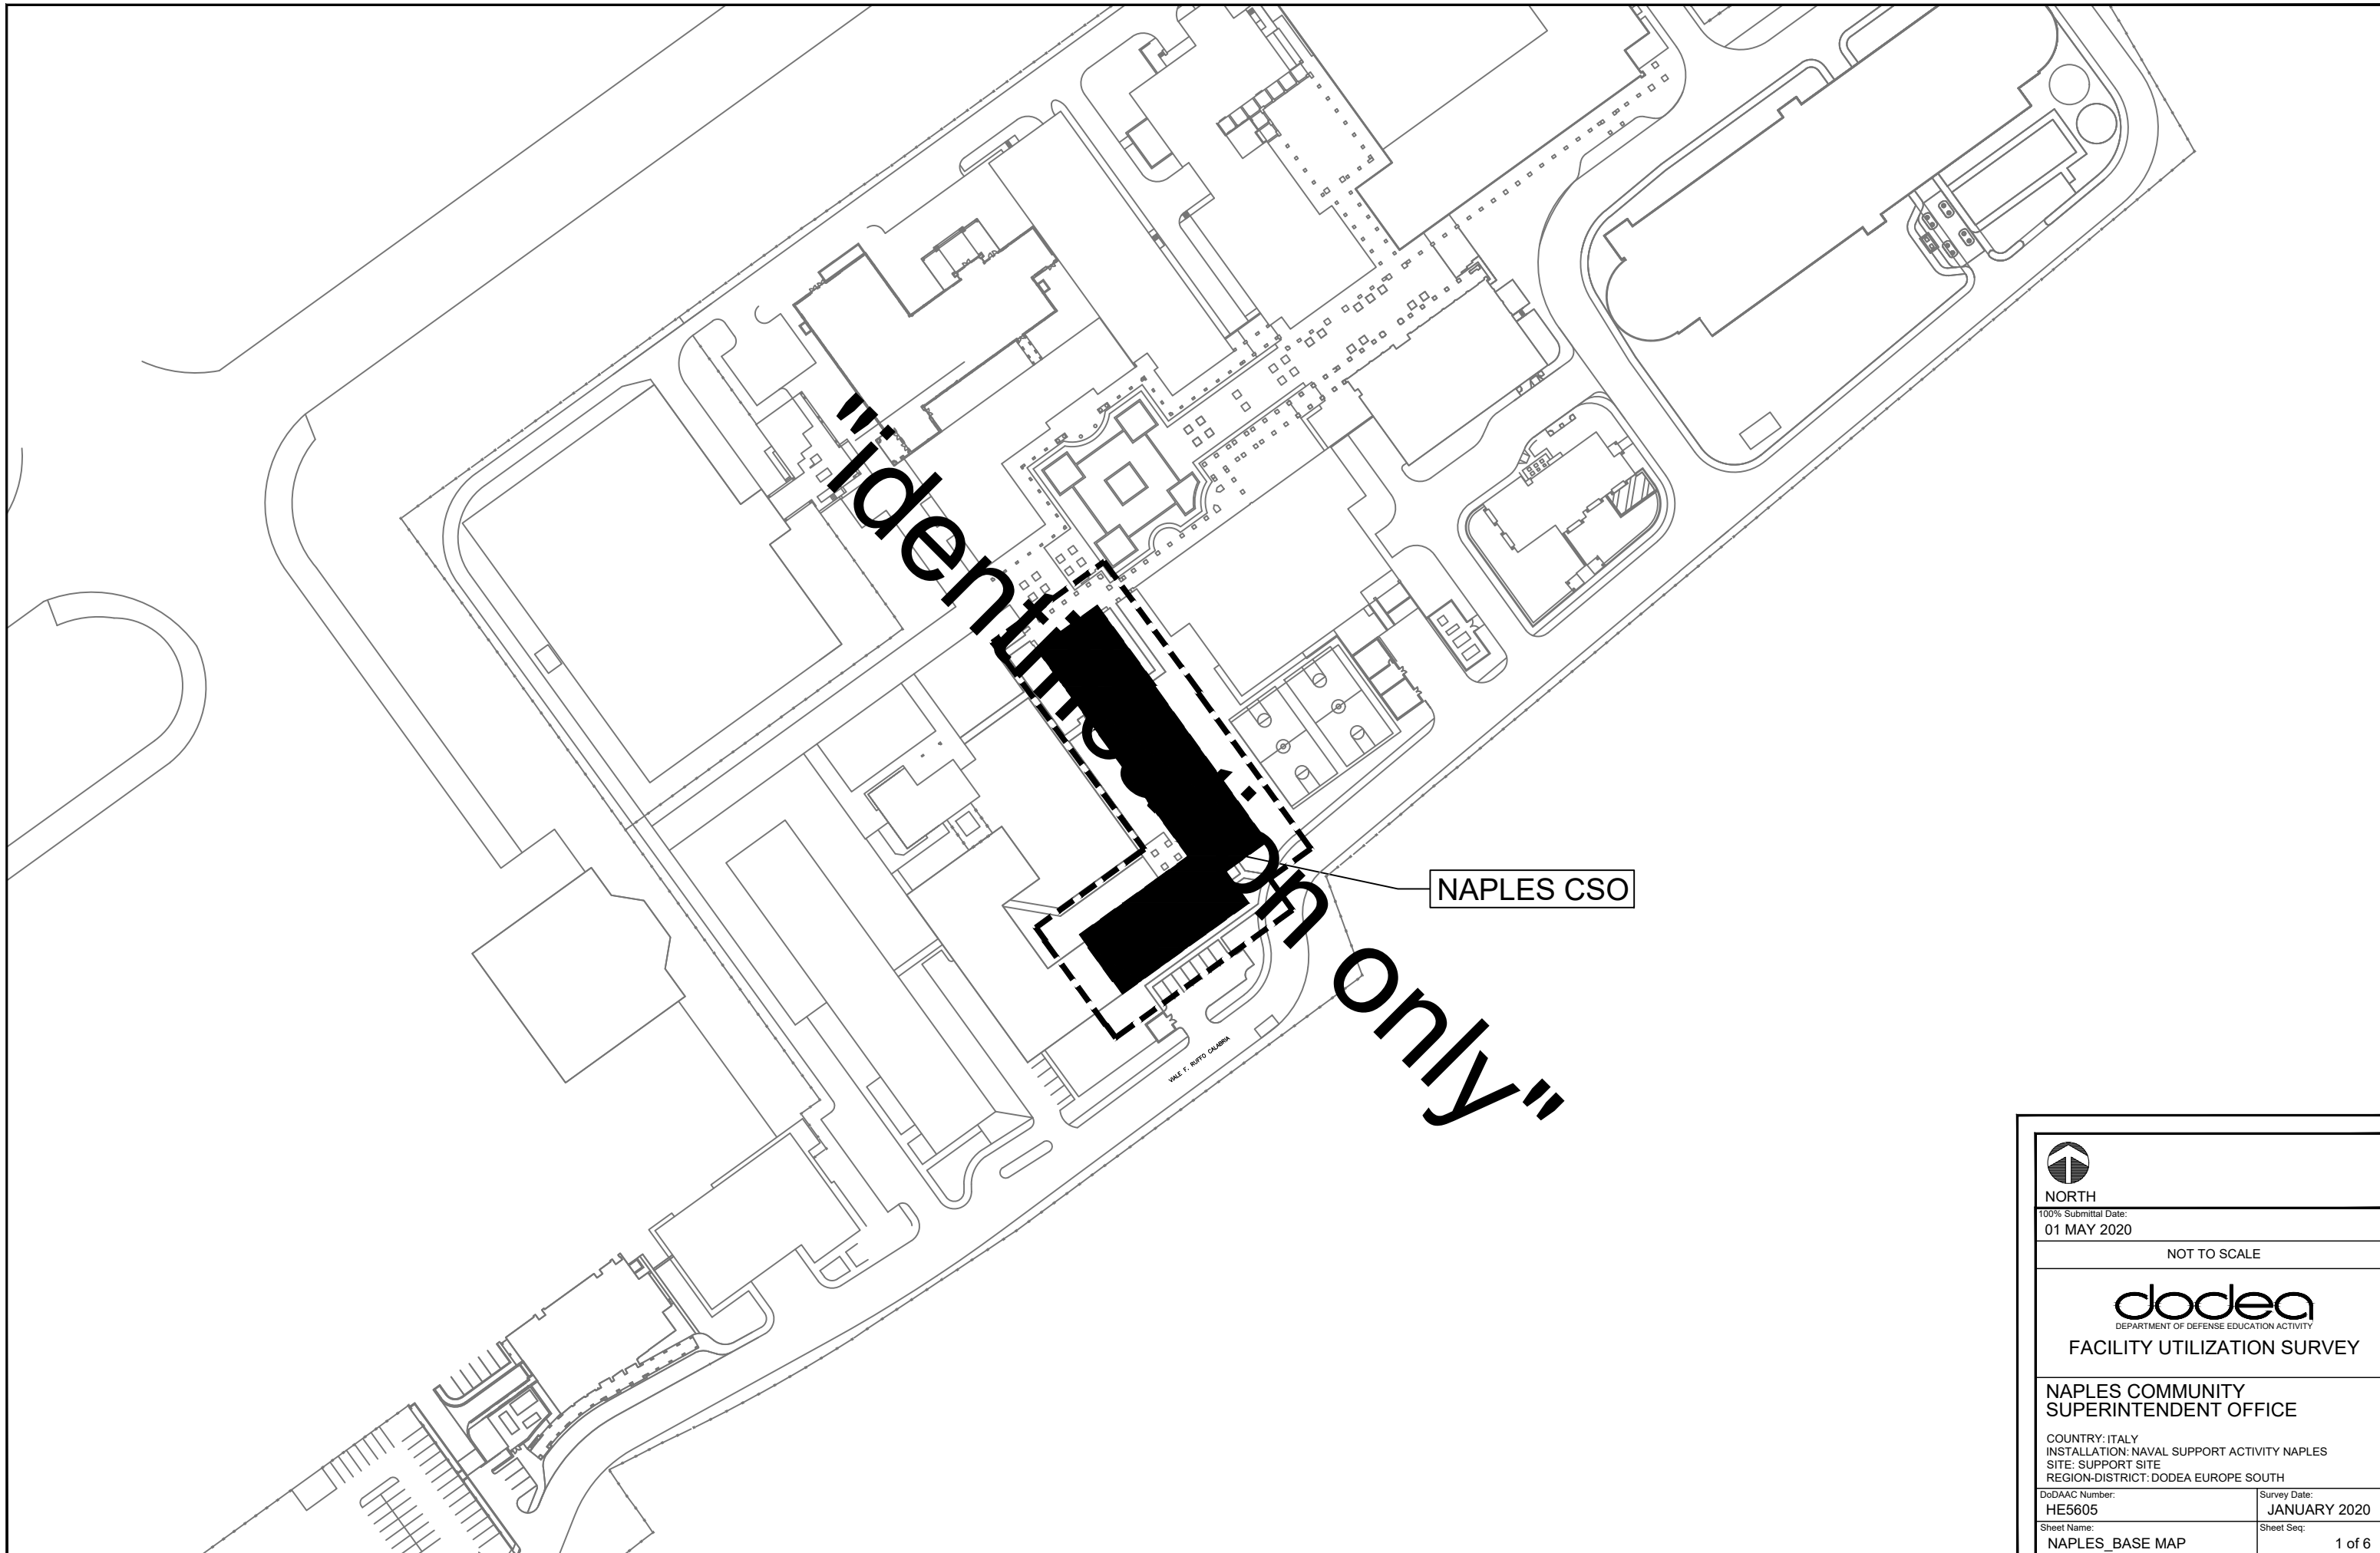

 NORTH	
100% Submittal Date: 01 MAY 2020	
NOT TO SCALE	
 DEPARTMENT OF DEFENSE EDUCATION ACTIVITY FACILITY UTILIZATION SURVEY	
NAPLES COMMUNITY SUPERINTENDENT OFFICE	
COUNTRY: ITALY INSTALLATION: NAVAL SUPPORT ACTIVITY NAPLES SITE: SUPPORT SITE REGION-DISTRICT: DODEA EUROPE SOUTH	
DoDAAC Number: HE5605	Survey Date: JANUARY 2020
Sheet Name: NAPLES_BASE MAP	Sheet Seq: 1 of 6

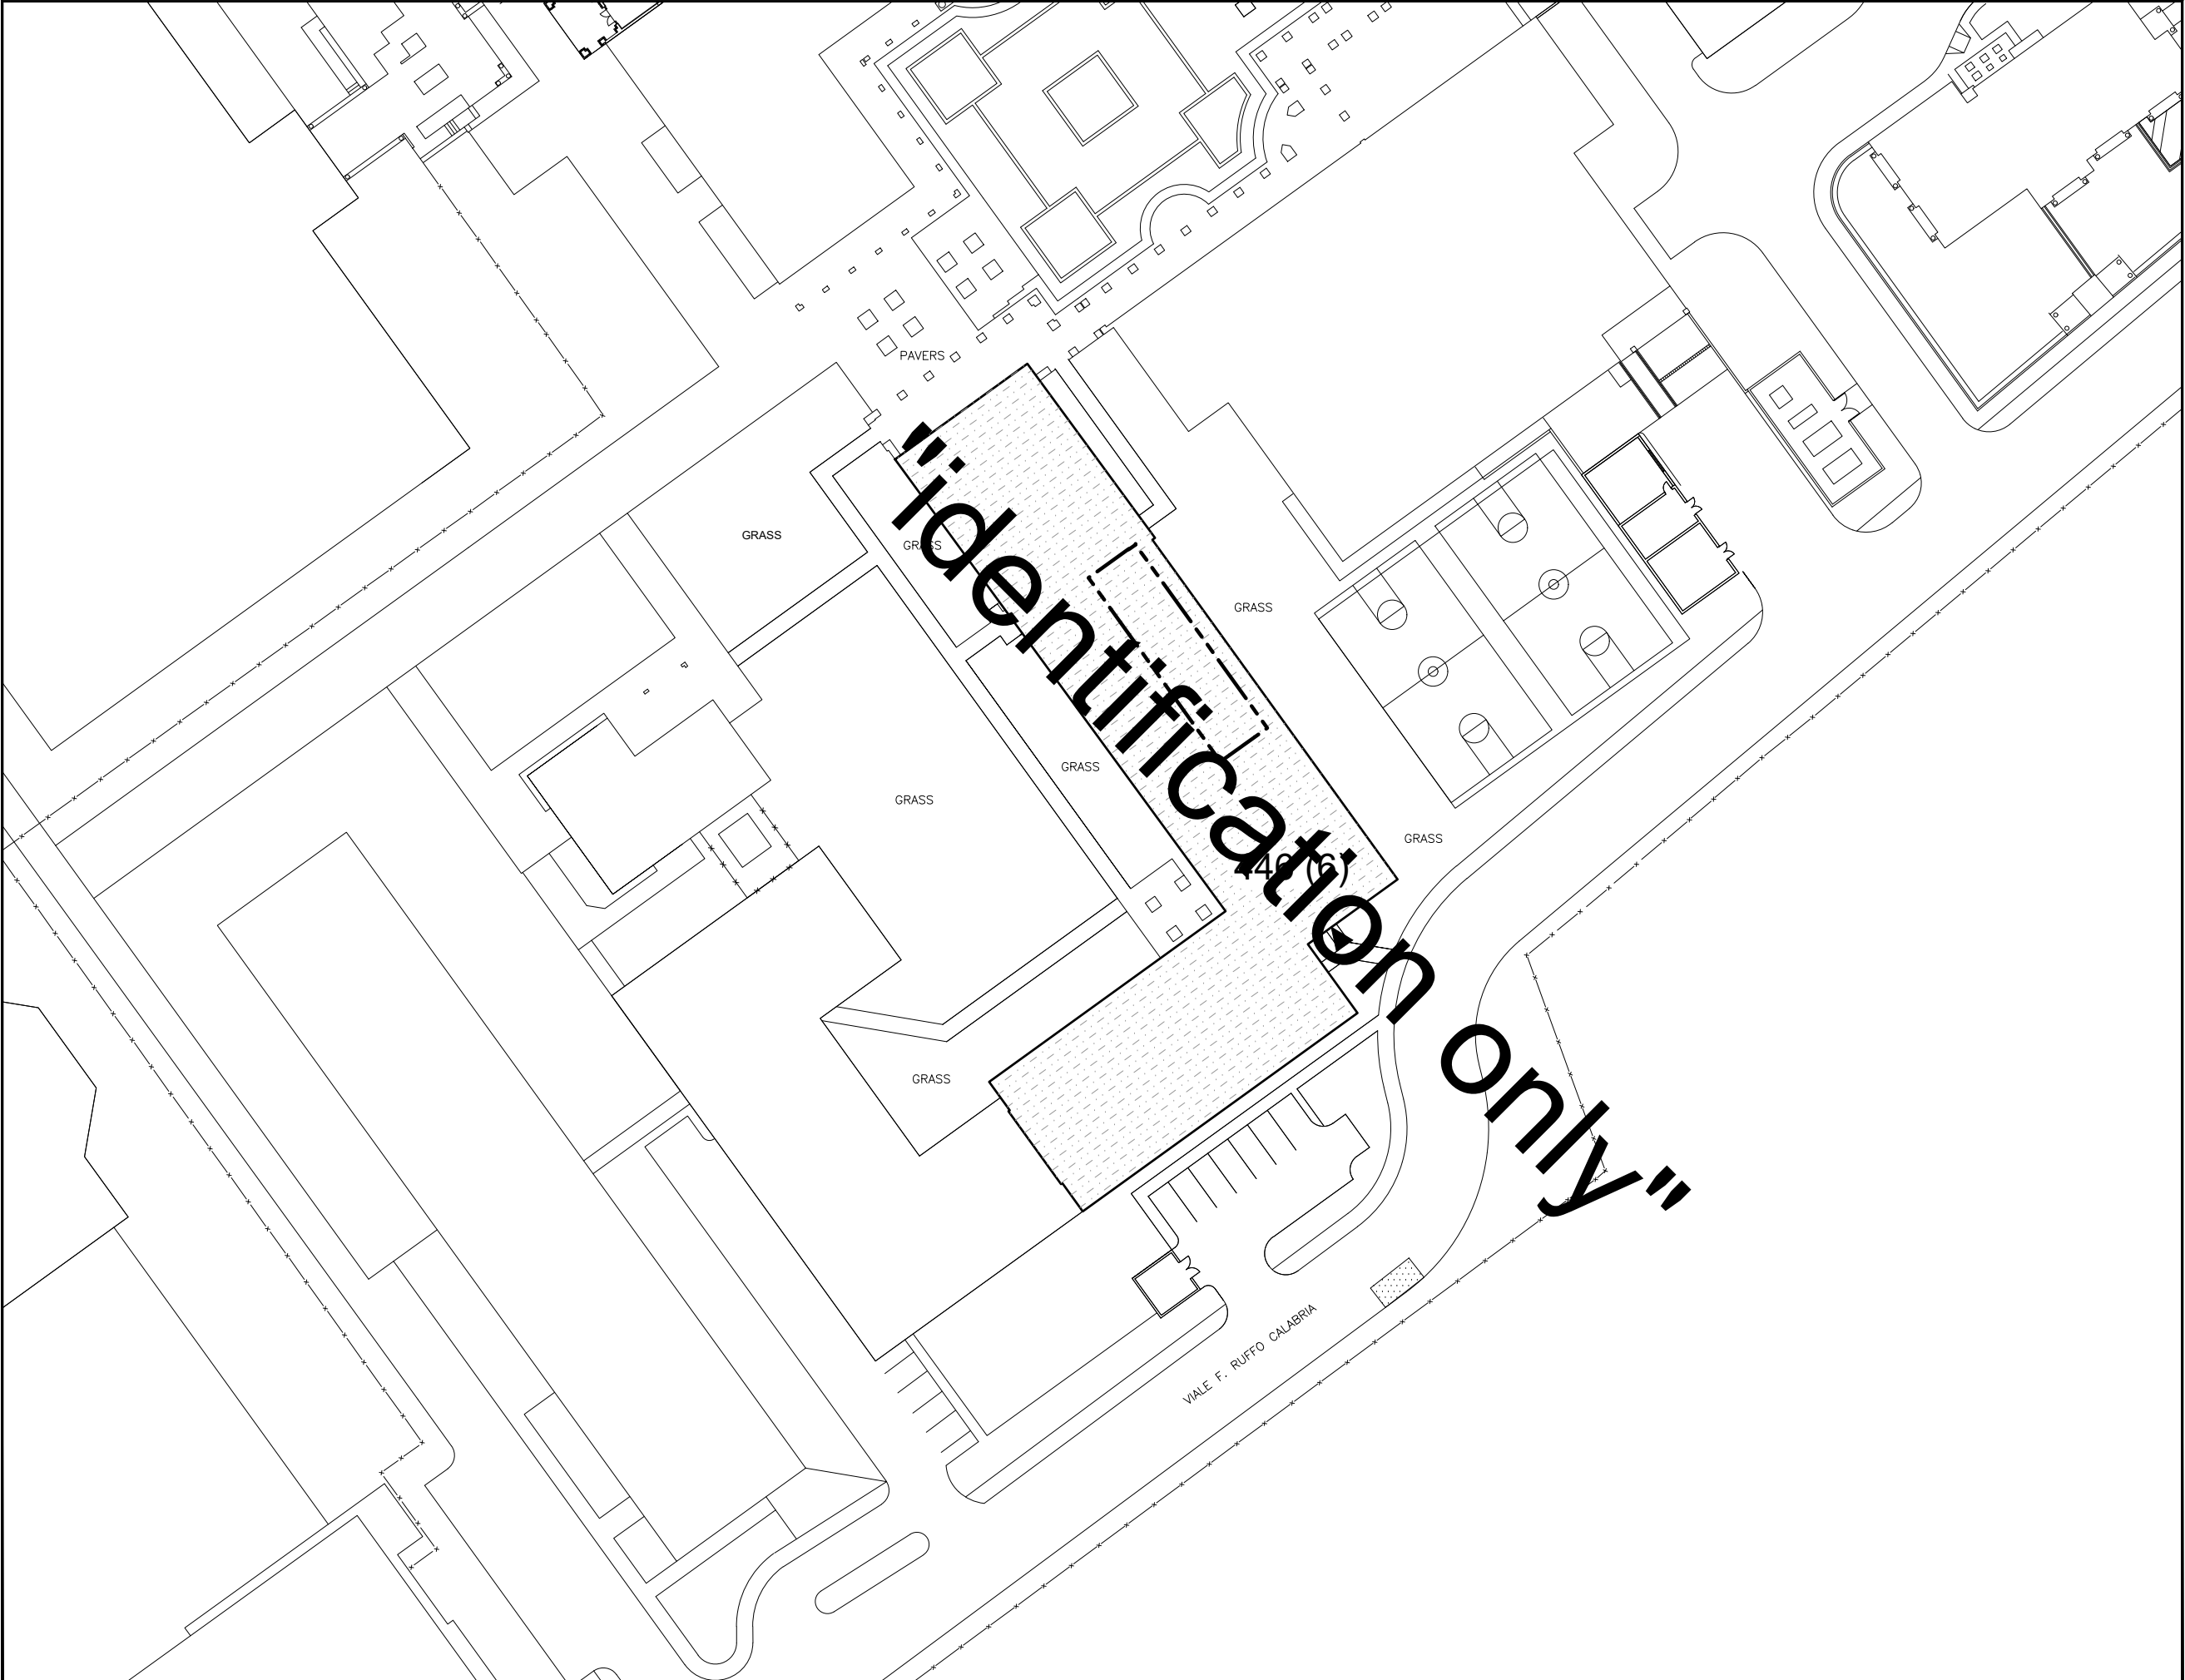


SYMBOL LEGEND	
	BASKETBALL GOAL
	STADIUM LIGHT
	SIGN
	FOOTBALL GOAL
	BASEBALL BACKSTOP
	PARKING AREA
	FLAT ROOF
	SLOPE
	COVERED WALKWAY
	SLOPING ROOF
	AREA LIGHT
	FLAG POLE
	MONUMENT
	SOCCER GOAL
	MAIN ENTRY
	CONCRETE
	PLAYGROUND
	FIRE HYDRANT
PROPERTY LINE (APPROX. 196 SM) (APPROX. 0.05 AC)	
FENCE LINE	

LEGEND	
PLAYGROUND SURFACING	
WC - WOOD CHIPS PR - POURED RUBBER M - MULCH	
SRT - SHREDDED RUBBER TIRES S - SAND	
PG - PEA GRAVEL RT - RUBBER TILES	
BUILDING LABEL	BLDG #_(# OF FLOORS)

KEY PLAN
NTS

Updated By: AA	FUS Review: MRS	100% Submittal Date: 01 MAY 2020
NOT TO SCALE		
 DEPARTMENT OF DEFENSE EDUCATION ACTIVITY FACILITY UTILIZATION SURVEY		
NAPLES COMMUNITY SUPERINTENDENT OFFICE		
COUNTRY: ITALY INSTALLATION: NAVAL SUPPORT ACTIVITY NAPLES SITE: SUPPORT SITE REGION-DISTRICT: DODEA EUROPE SOUTH		
DoDAAC Number: HE5605		Survey Date: JANUARY 2020
Sheet Name: NAPLES CSO OVERALL		Sheet Seq: 2 of 6

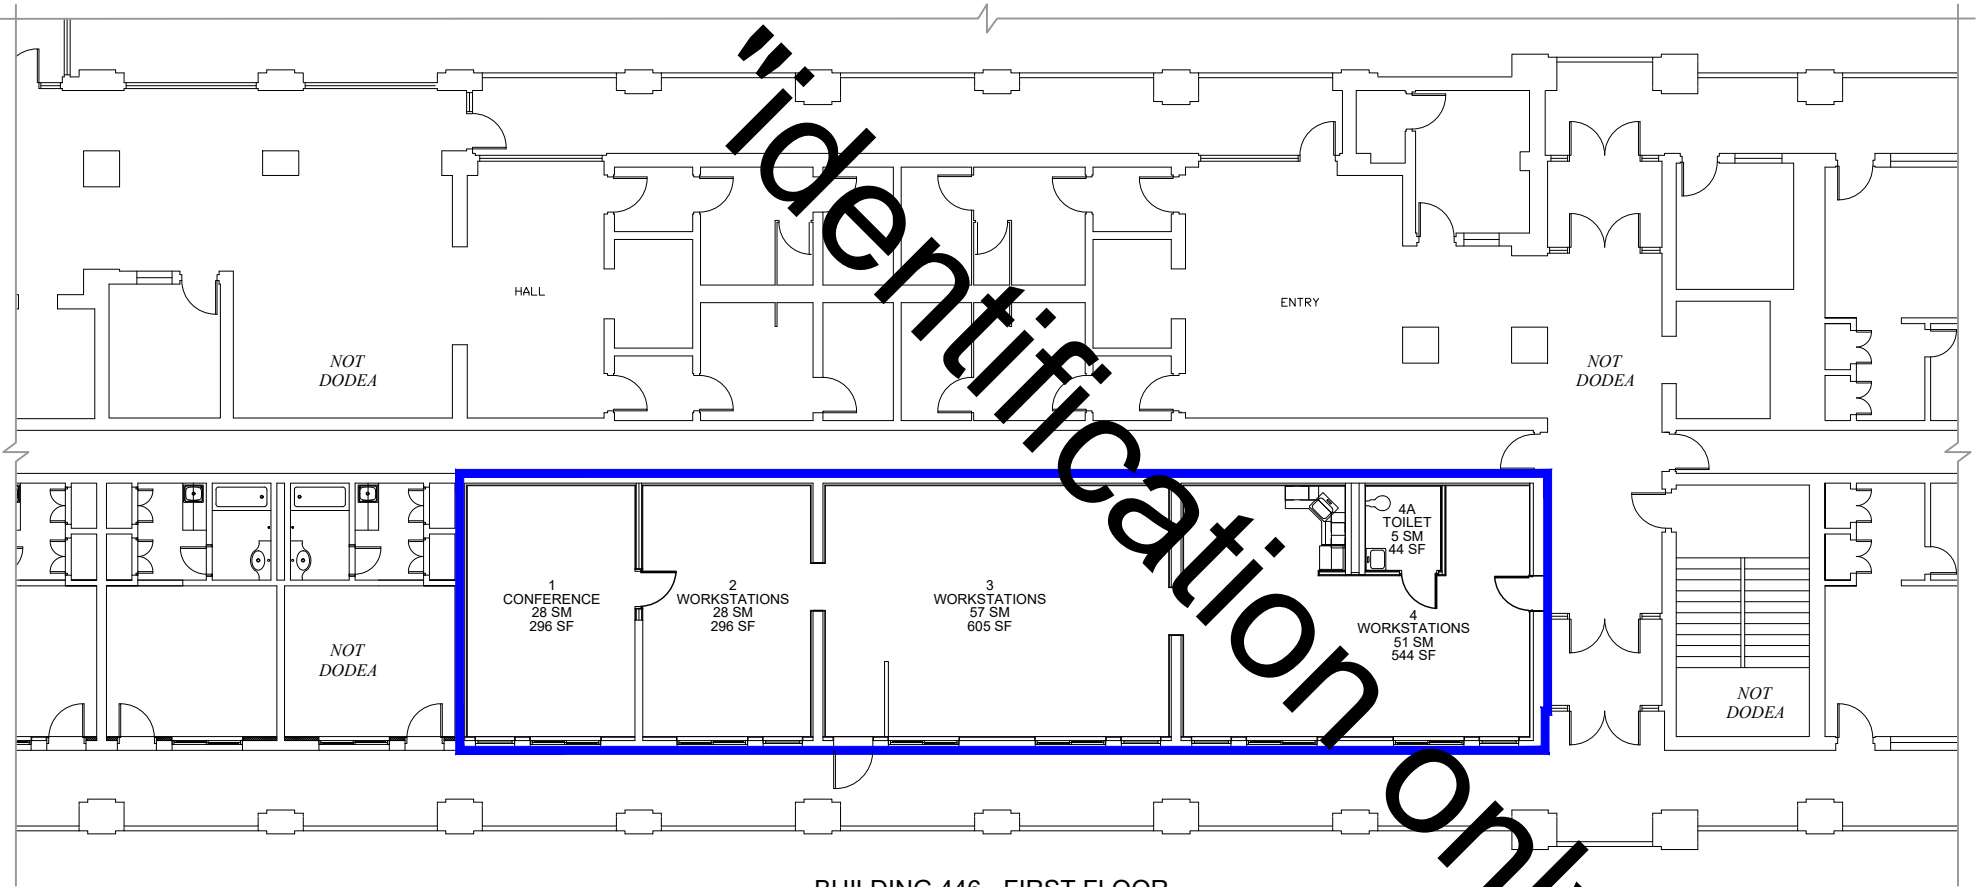


BUILDING 446 - FIRST FLOOR

GSF CALCULATIONS

Building 446	
Floor 1	2,115
Total Area (SF)	2,115
50% Area (SF)	0
Gross Area (SF)	2,115

SYMBOL LEGEND	
DOOR	DRINKING FOUNTAIN
SLIDING DOOR	LAVATORY
ACCORDION PARTITION	SINK
STACK OR FOLDING PARTITION	TOILET
WINDOW/GLAZING	URINAL
HIGH WINDOW	LOCKER
SKYLIGHT	LAN DISTRIBUTION FRAME
STOOP/STEP UP	VENT HOOD
STAIR	WALL SHELVING
RAMP	UPPER CABINET
ACCESS LADDER	BASE CABINET
COLD STORAGE	TEACHER CABINET
AREA CALCULATED @ 50 %	MATCHLINE
SLOPING ROOF	FLAT ROOF

TITLEBLOCK LEGEND	
SHEET NAME:	BLDG #_FLOOR # (# IN SERIES)

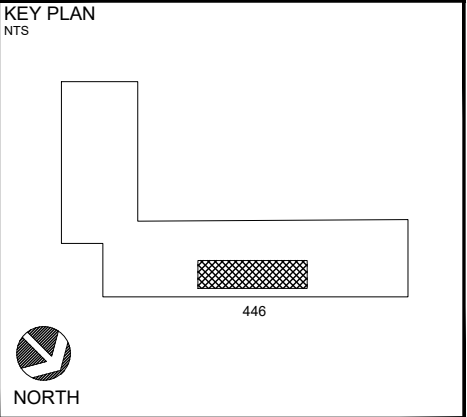

Updated By:	FUS Review:	100% Submittal Date:
AA	MRS	01 MAY 2020
0 2 4 8 16 FT		

dodea
DEPARTMENT OF DEFENSE EDUCATION ACTIVITY
FACILITY UTILIZATION SURVEY

NAPLES COMMUNITY
SUPERINTENDENT OFFICE
BUILDING NUMBER: 446
COUNTRY: ITALY
INSTALLATION: NAVAL SUPPORT ACTIVITY NAPLES
SITE: SUPPORT SITE
REGION-DISTRICT: DODEA EUROPE SOUTH

DoDAAC Number:	Floor:	Survey Date:
HE5605	LEVEL 1	JANUARY 2020
Sheet Name:	Sheet Seq:	
GSF_1 (1)	3 of 6	

NOTE 1: BUILDING 446 IS A PARTIAL-USE FACILITY, AND DODEA UTILIZES 2,115 SF (APPROXIMATELY 2%) OF THE LARGER INSTALLATION BUILDING.


NOTE 1: GSF CALCULATIONS BASED ON ARMY RPI DoA PAMPHLET 415-28.

446					
Floor	Room	Current	Capacity	Area (SF)	Area (SM)
1	1	CONFERENCE	OTHER	296 SF	28 SM
1	2	WORKSTATIONS	OTHER	296 SF	28 SM
1	3	WORKSTATIONS	OTHER	605 SF	57 SM
1	4	WORKSTATIONS	OTHER	544 SF	51 SM
1	4A	TOILET	NET - GENERAL	44 SF	5 SM

"identification only"

SYMBOL LEGEND		
	DOOR	 DRINKING FOUNTAIN
	SLIDING DOOR	 LAVATORY
	ACCORDION PARTITION	 SINK
	STACK OR FOLDING PARTITION	 TOILET
	WINDOW/GLAZING	 URINAL
	HIGH WINDOW	 LOCKER
	SKYLIGHT	 LAN DISTRIBUTION FRAME
	STOOP/STEP UP	 VENT HOOD
	STAIR	 WALL SHELVING
	RAMP	 UPPER CABINET
	ACCESS LADDER	 BASE CABINET
	COLD STORAGE	 TEACHER CABINET
	AREA CALCULATED @ 50 %	 MATCHLINE
	SLOPING ROOF	 FLAT ROOF

TITLEBLOCK LEGEND	
SHEET NAME:	BLDG #_ FLOOR # (# IN SERIES)

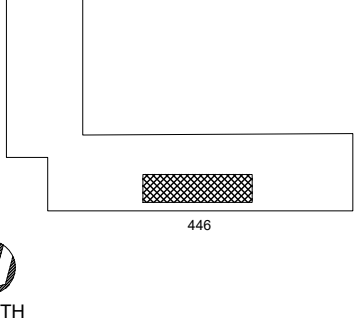KEY PLAN		
NTS		
		
Updated By: FUS Review: 100% Submittal Date: AA MRS 01 MAY 2020		
NOT TO SCALE		
 DEPARTMENT OF DEFENSE EDUCATION ACTIVITY		
FACILITY UTILIZATION SURVEY		
NAPLES COMMUNITY SUPERINTENDENT OFFICE BUILDING NUMBER: 446 COUNTRY: ITALY INSTALLATION: NAVAL SUPPORT ACTIVITY NAPLES SITE: SUPPORT SITE REGION-DISTRICT: DODEA EUROPE SOUTH		
DoDAAC Number: HE5605	Floor: LEVEL 1	Survey Date: JANUARY 2020
Sheet Name: SCHEDULES (1)		Sheet Seq: 4 of 6

TITLEBLOCK LEGEND	
<i>SHEET NAME:</i>	<i>BLDG #_FLOOR # (# IN SERIES)</i>

KEY PLAN
NTS

446

NORTH


Updated By: AA	FUS Review: MRS	100% Submittal Date: 01 MAY 2020
-------------------	--------------------	-------------------------------------

NOT TO SCALE

dodeca
DEPARTMENT OF DEFENSE EDUCATION ACTIVITY
FACILITY UTILIZATION SURVEY


**NAPLES COMMUNITY
SUPERINTENDENT OFFICE**
BUILDING NUMBER: 446
COUNTRY: ITALY
INSTALLATION: NAVAL SUPPORT ACTIVITY NAPLES
SITE: SUPPORT SITE
REGION-DISTRICT: DODEA EUROPE SOUTH

DoDAAC Number: HE5605	Floor: LEVEL 1	Survey Date: JANUARY 2020
Sheet Name: SCHEDULES (1)		Sheet Seq: 4 of 6

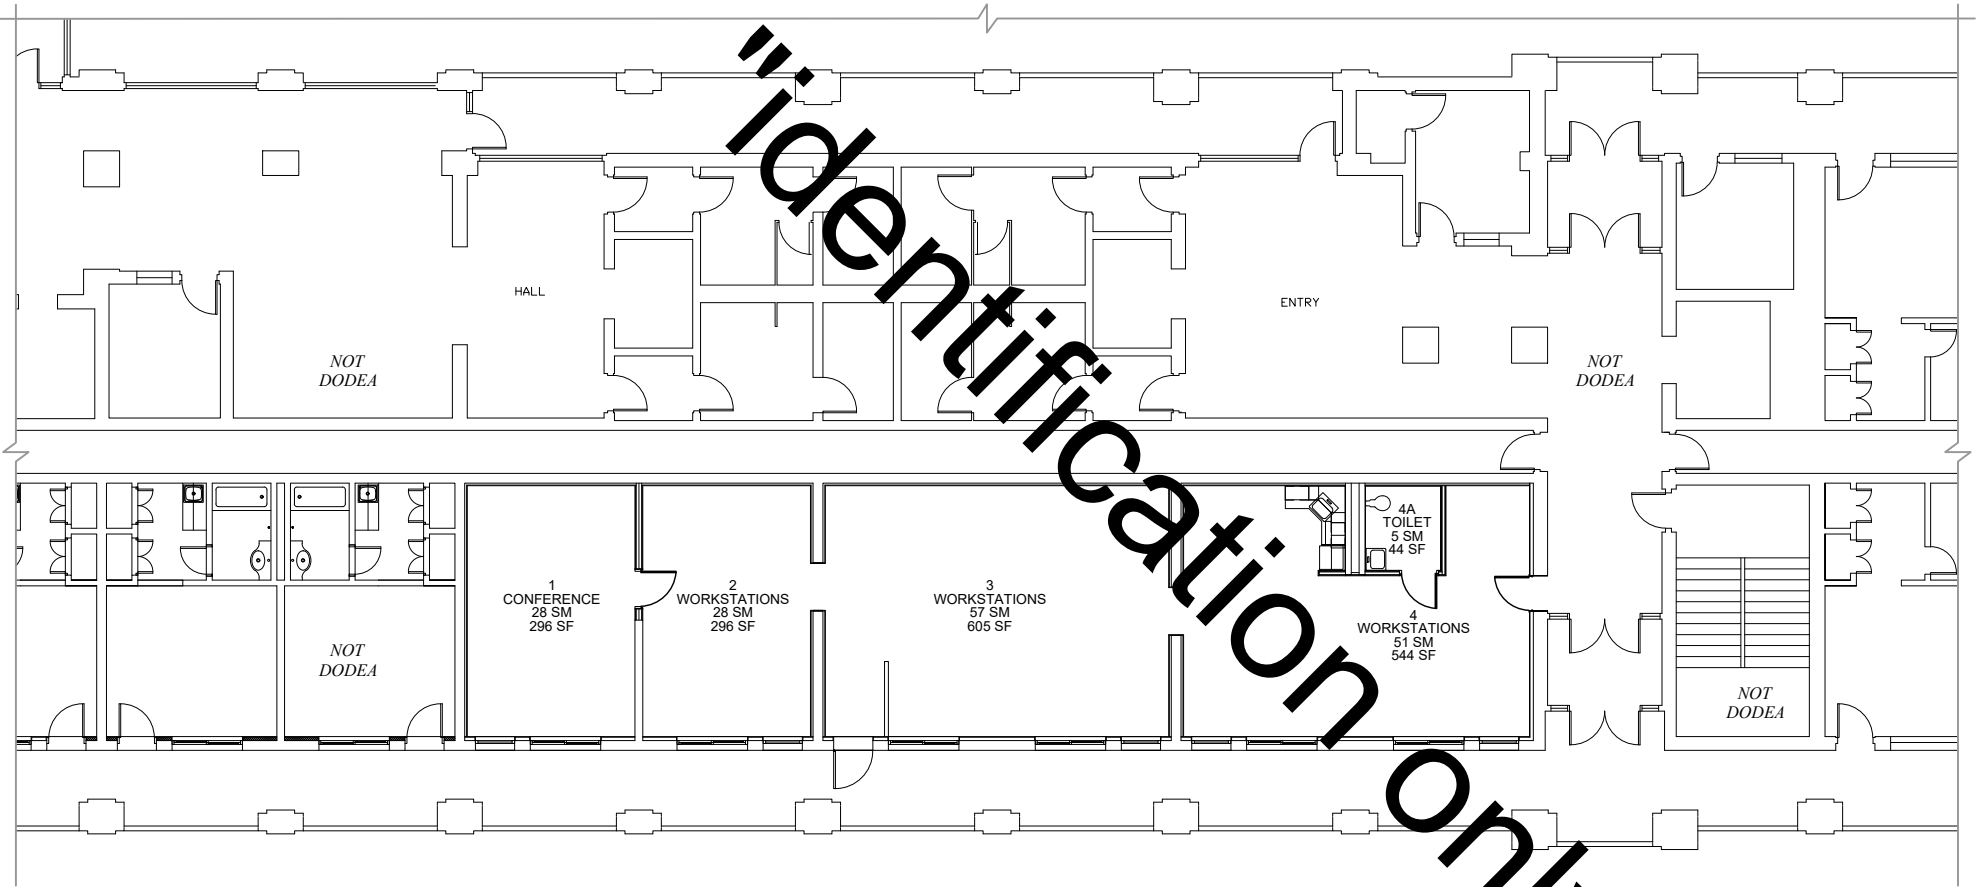

SYMBOL LEGEND	
	DOOR
	DRINKING FOUNTAIN
	SLIDING DOOR
	LAVATORY
	ACCORDION PARTITION
	SINK
	STACK OR FOLDING PARTITION
	TOILET
	WINDOW/GLAZING
	URINAL
	HIGH WINDOW
	LOCKER
	SKYLIGHT
	LAN DISTRIBUTION FRAME
	STOOP/STEP UP
	VENT HOOD
	STAIR
	WALL SHELVING
	RAMP
	UPPER CABINET
	ACCESS LADDER
	BASE CABINET
	COLD STORAGE
	TEACHER CABINET
	AREA CALCULATED @ 50 %
	MATCHLINE
	SLOPING ROOF
	FLAT ROOF

TITLEBLOCK LEGEND	
SHEET NAME:	BLDG #_FLOOR # (# IN SERIES)

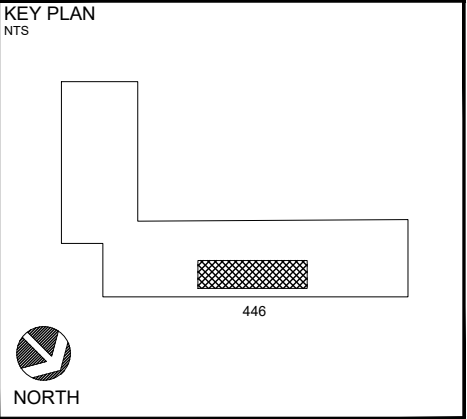

Updated By:	FUS Review:	100% Submittal Date:
AA	MRS	01 MAY 2020

DEPARTMENT OF DEFENSE EDUCATION ACTIVITY

FACILITY UTILIZATION SURVEY

NAPLES COMMUNITY SUPERINTENDENT OFFICE		
BUILDING NUMBER: 446		
COUNTRY: ITALY		
INSTALLATION: NAVAL SUPPORT ACTIVITY NAPLES		
SITE: SUPPORT SITE		
REGION-DISTRICT: DODEA EUROPE SOUTH		
DoDAAC Number:	Floor:	Survey Date:
HE5605	LEVEL 1	JANUARY 2020
Sheet Name:	Sheet Seq:	
446_1 (1)	6 of 6	