



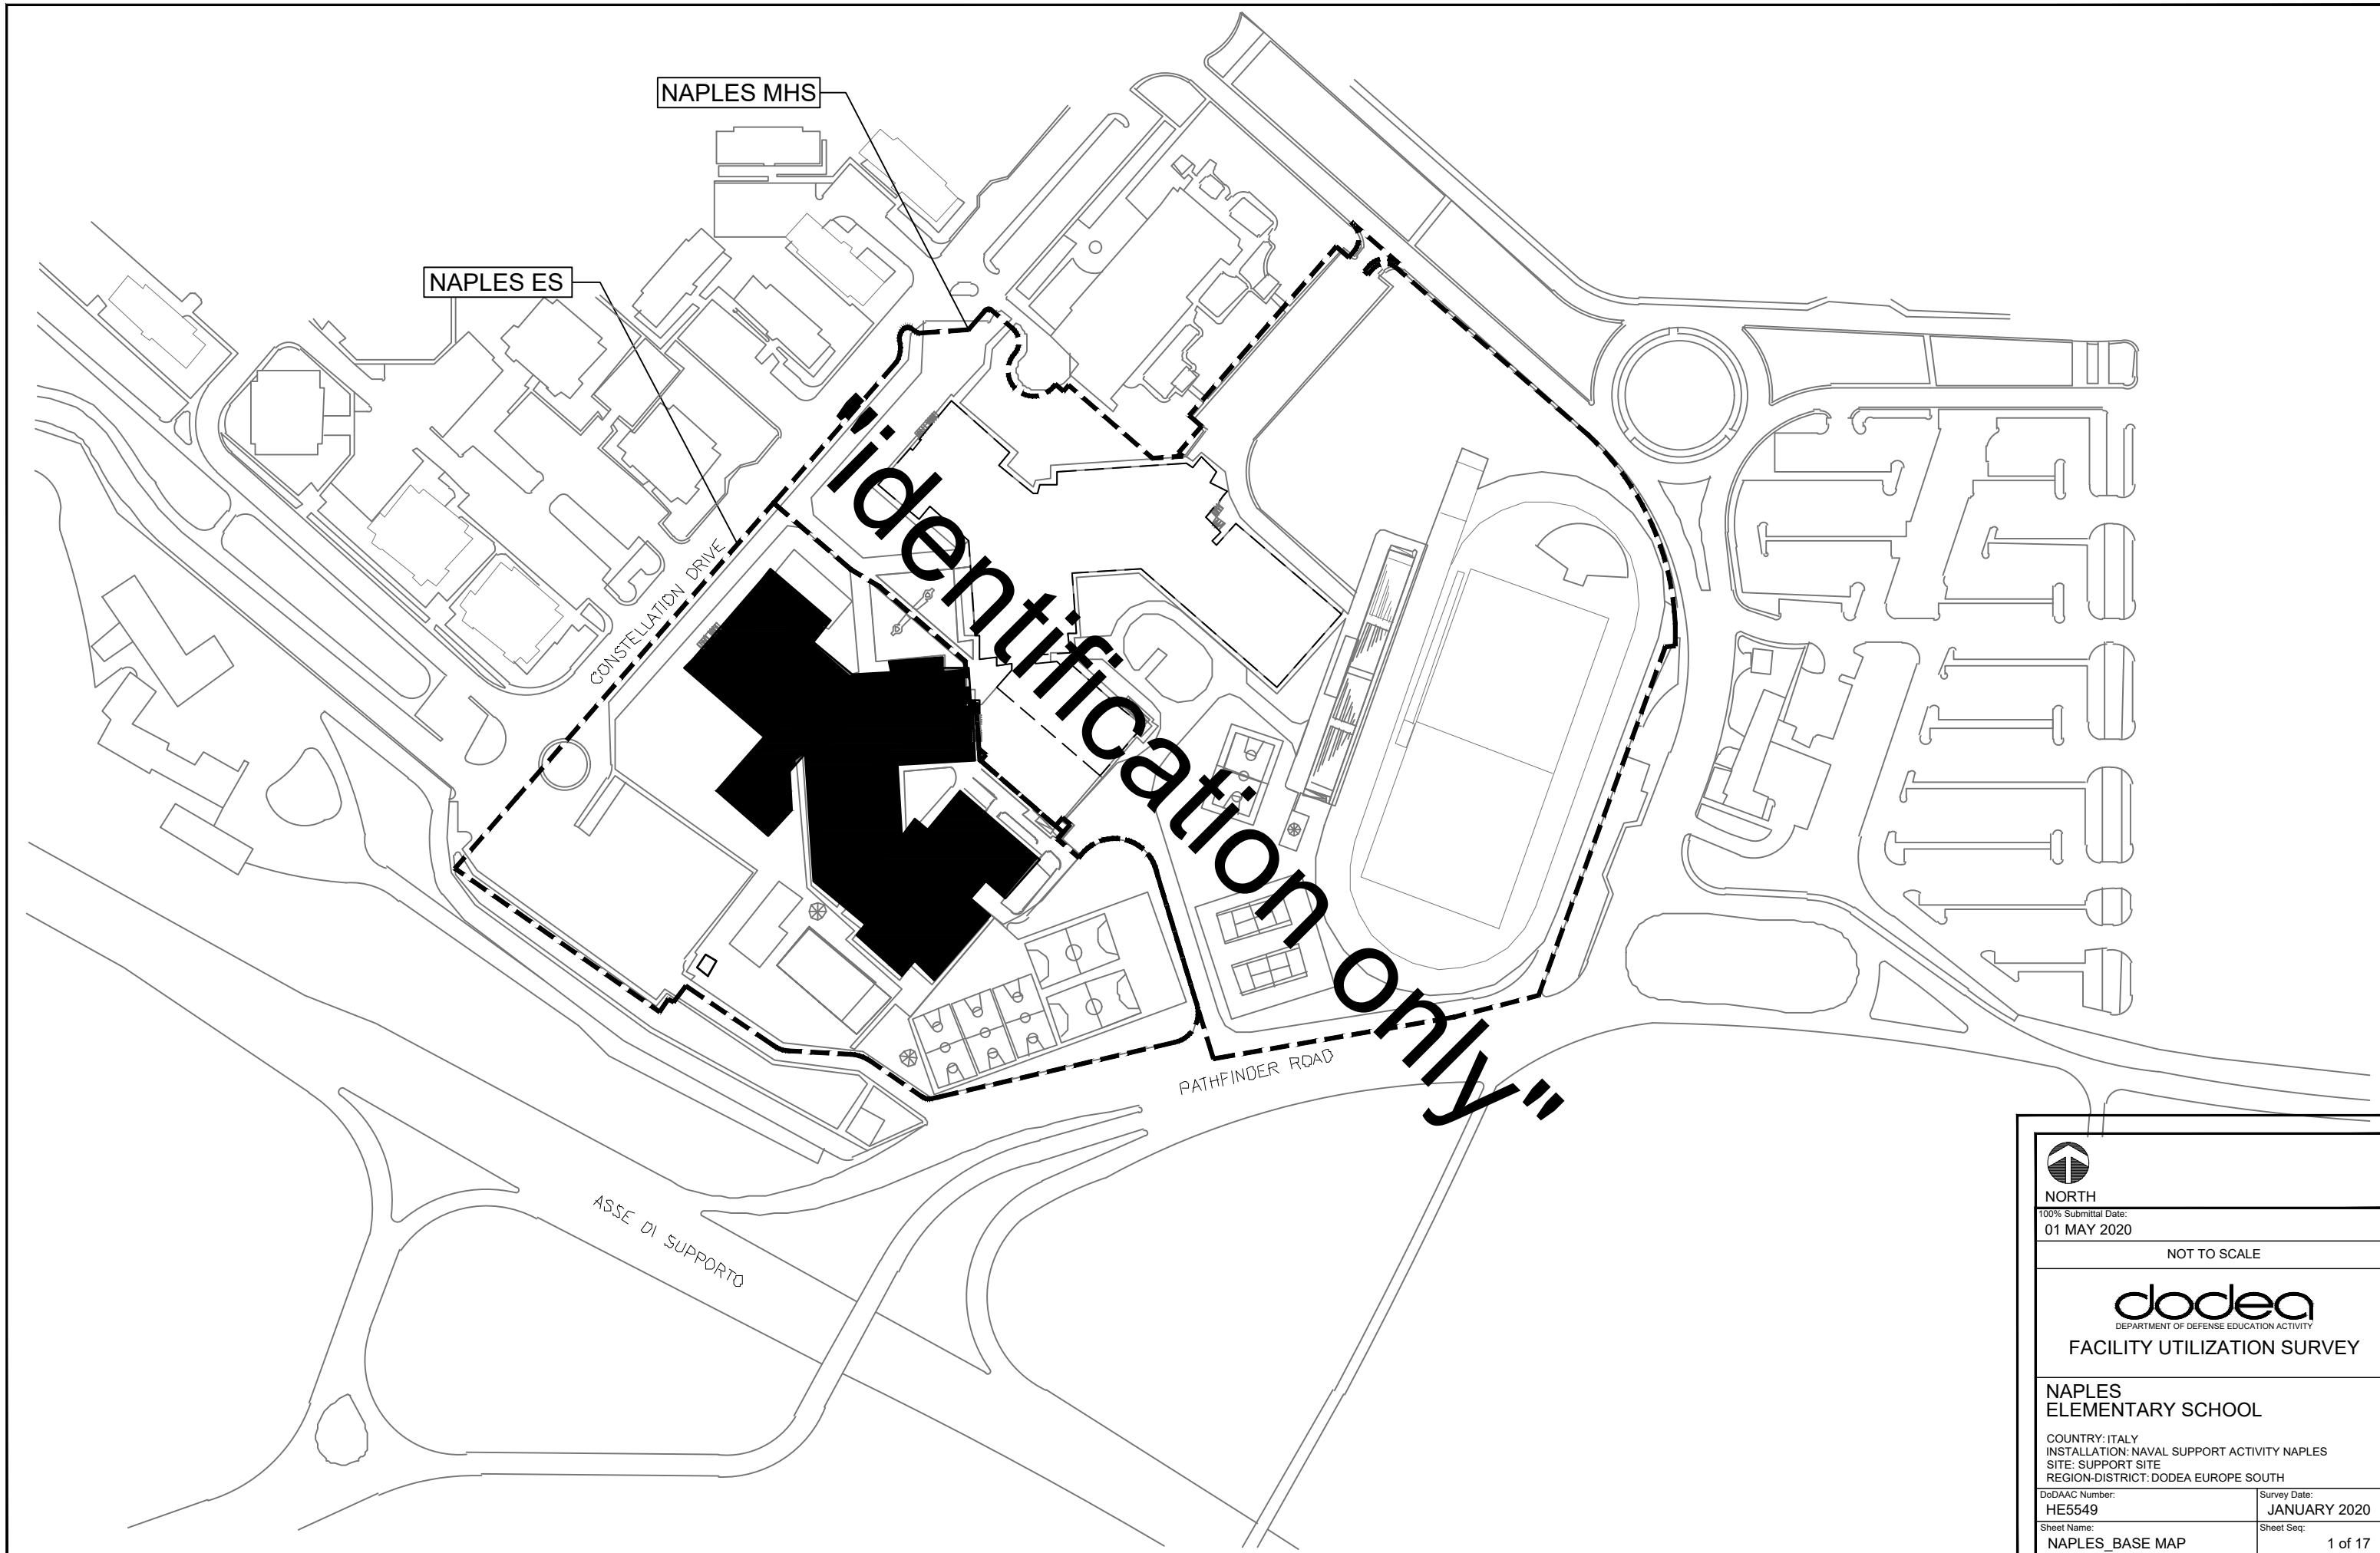

 NORTH	
100% Submittal Date: 01 MAY 2020	
NOT TO SCALE	
 DEPARTMENT OF DEFENSE EDUCATION ACTIVITY FACILITY UTILIZATION SURVEY	
NAPLES ELEMENTARY SCHOOL	
COUNTRY: ITALY INSTALLATION: NAVAL SUPPORT ACTIVITY NAPLES SITE: SUPPORT SITE REGION-DISTRICT: DODEA EUROPE SOUTH	
DoDAAC Number: HE5549	Survey Date: JANUARY 2020
Sheet Name: NAPLES_BASE MAP	Sheet Seq: 1 of 17

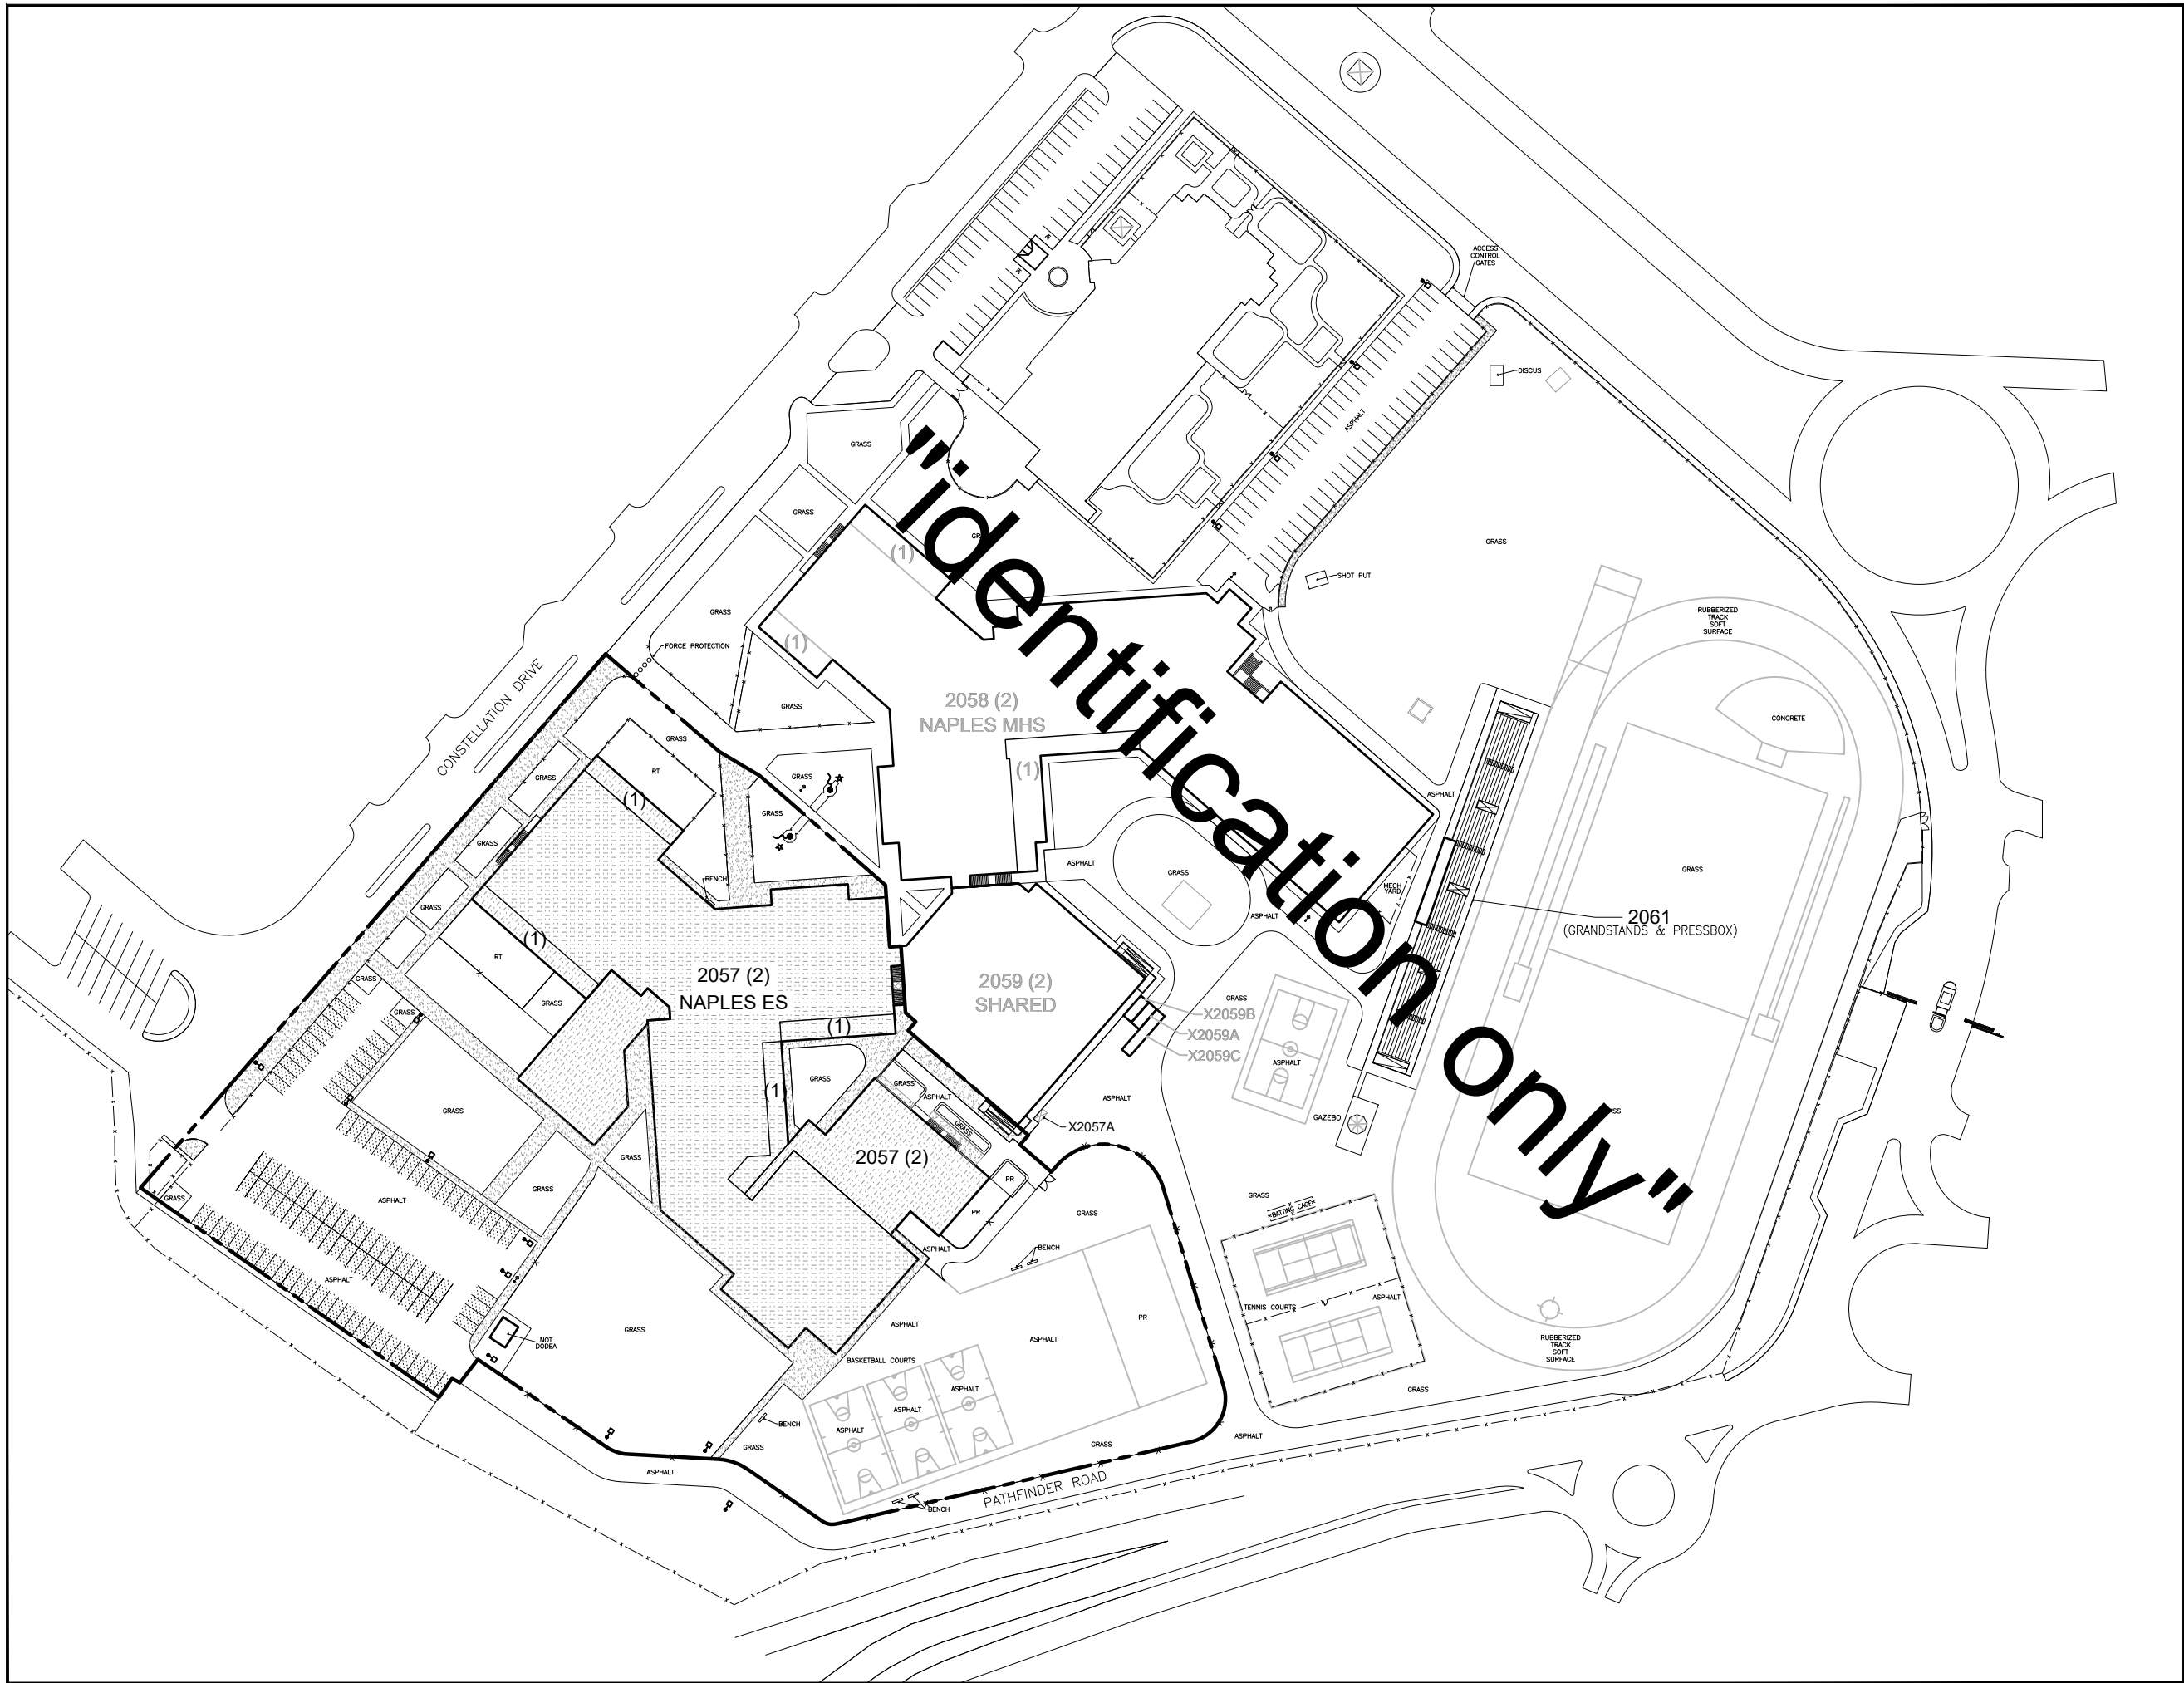


SYMBOL LEGEND	
	BASKETBALL GOAL
	STADIUM LIGHT
	SIGN
	FOOTBALL GOAL
	BASEBALL BACKSTOP
	PARKING AREA
	FLAT ROOF
	SLOPE
	COVERED WALKWAY
	SLOPING ROOF
	AREA LIGHT
	FLAG POLE
	MONUMENT
	SOCCER GOAL
	MAIN ENTRY
	CONCRETE
	PLAYGROUND
	FIRE HYDRANT
PROPERTY LINE (APPROX. 26,294 SM) (APPROX. 6.50 AC)	
FENCE LINE	

LEGEND	
PLAYGROUND SURFACING	
WC - WOOD CHIPS	PR - POURED RUBBER M - MULCH
SRT - SHREDDED RUBBER TIRES	S - SAND
PG - PEA GRAVEL	RT - RUBBER TILES

BUILDING LABEL	BLDG #_(# OF FLOORS)
----------------	----------------------

KEY PLAN
NTS

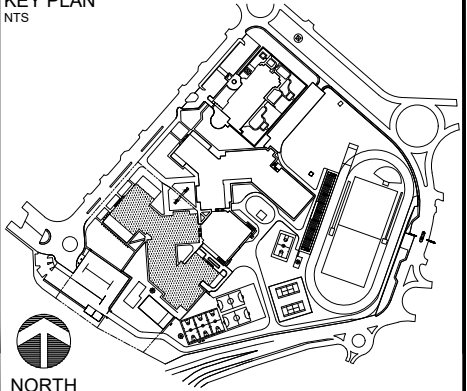

Updated By: AA	FUS Review: MRS	100% Submittal Date: 01 MAY 2020
-------------------	--------------------	-------------------------------------

NOT TO SCALE

DEPARTMENT OF DEFENSE EDUCATION ACTIVITY
FACILITY UTILIZATION SURVEY

NAPLES
ELEMENTARY SCHOOL


COUNTRY: ITALY
INSTALLATION: NAVAL SUPPORT ACTIVITY NAPLES
SITE: SUPPORT SITE
REGION-DISTRICT: DODEA EUROPE SOUTH

DoDAAC Number:
HE5549

Survey Date:
JANUARY 2020

Sheet Name:
NAPLES ES_OVERALL

Sheet Seq:
2 of 17

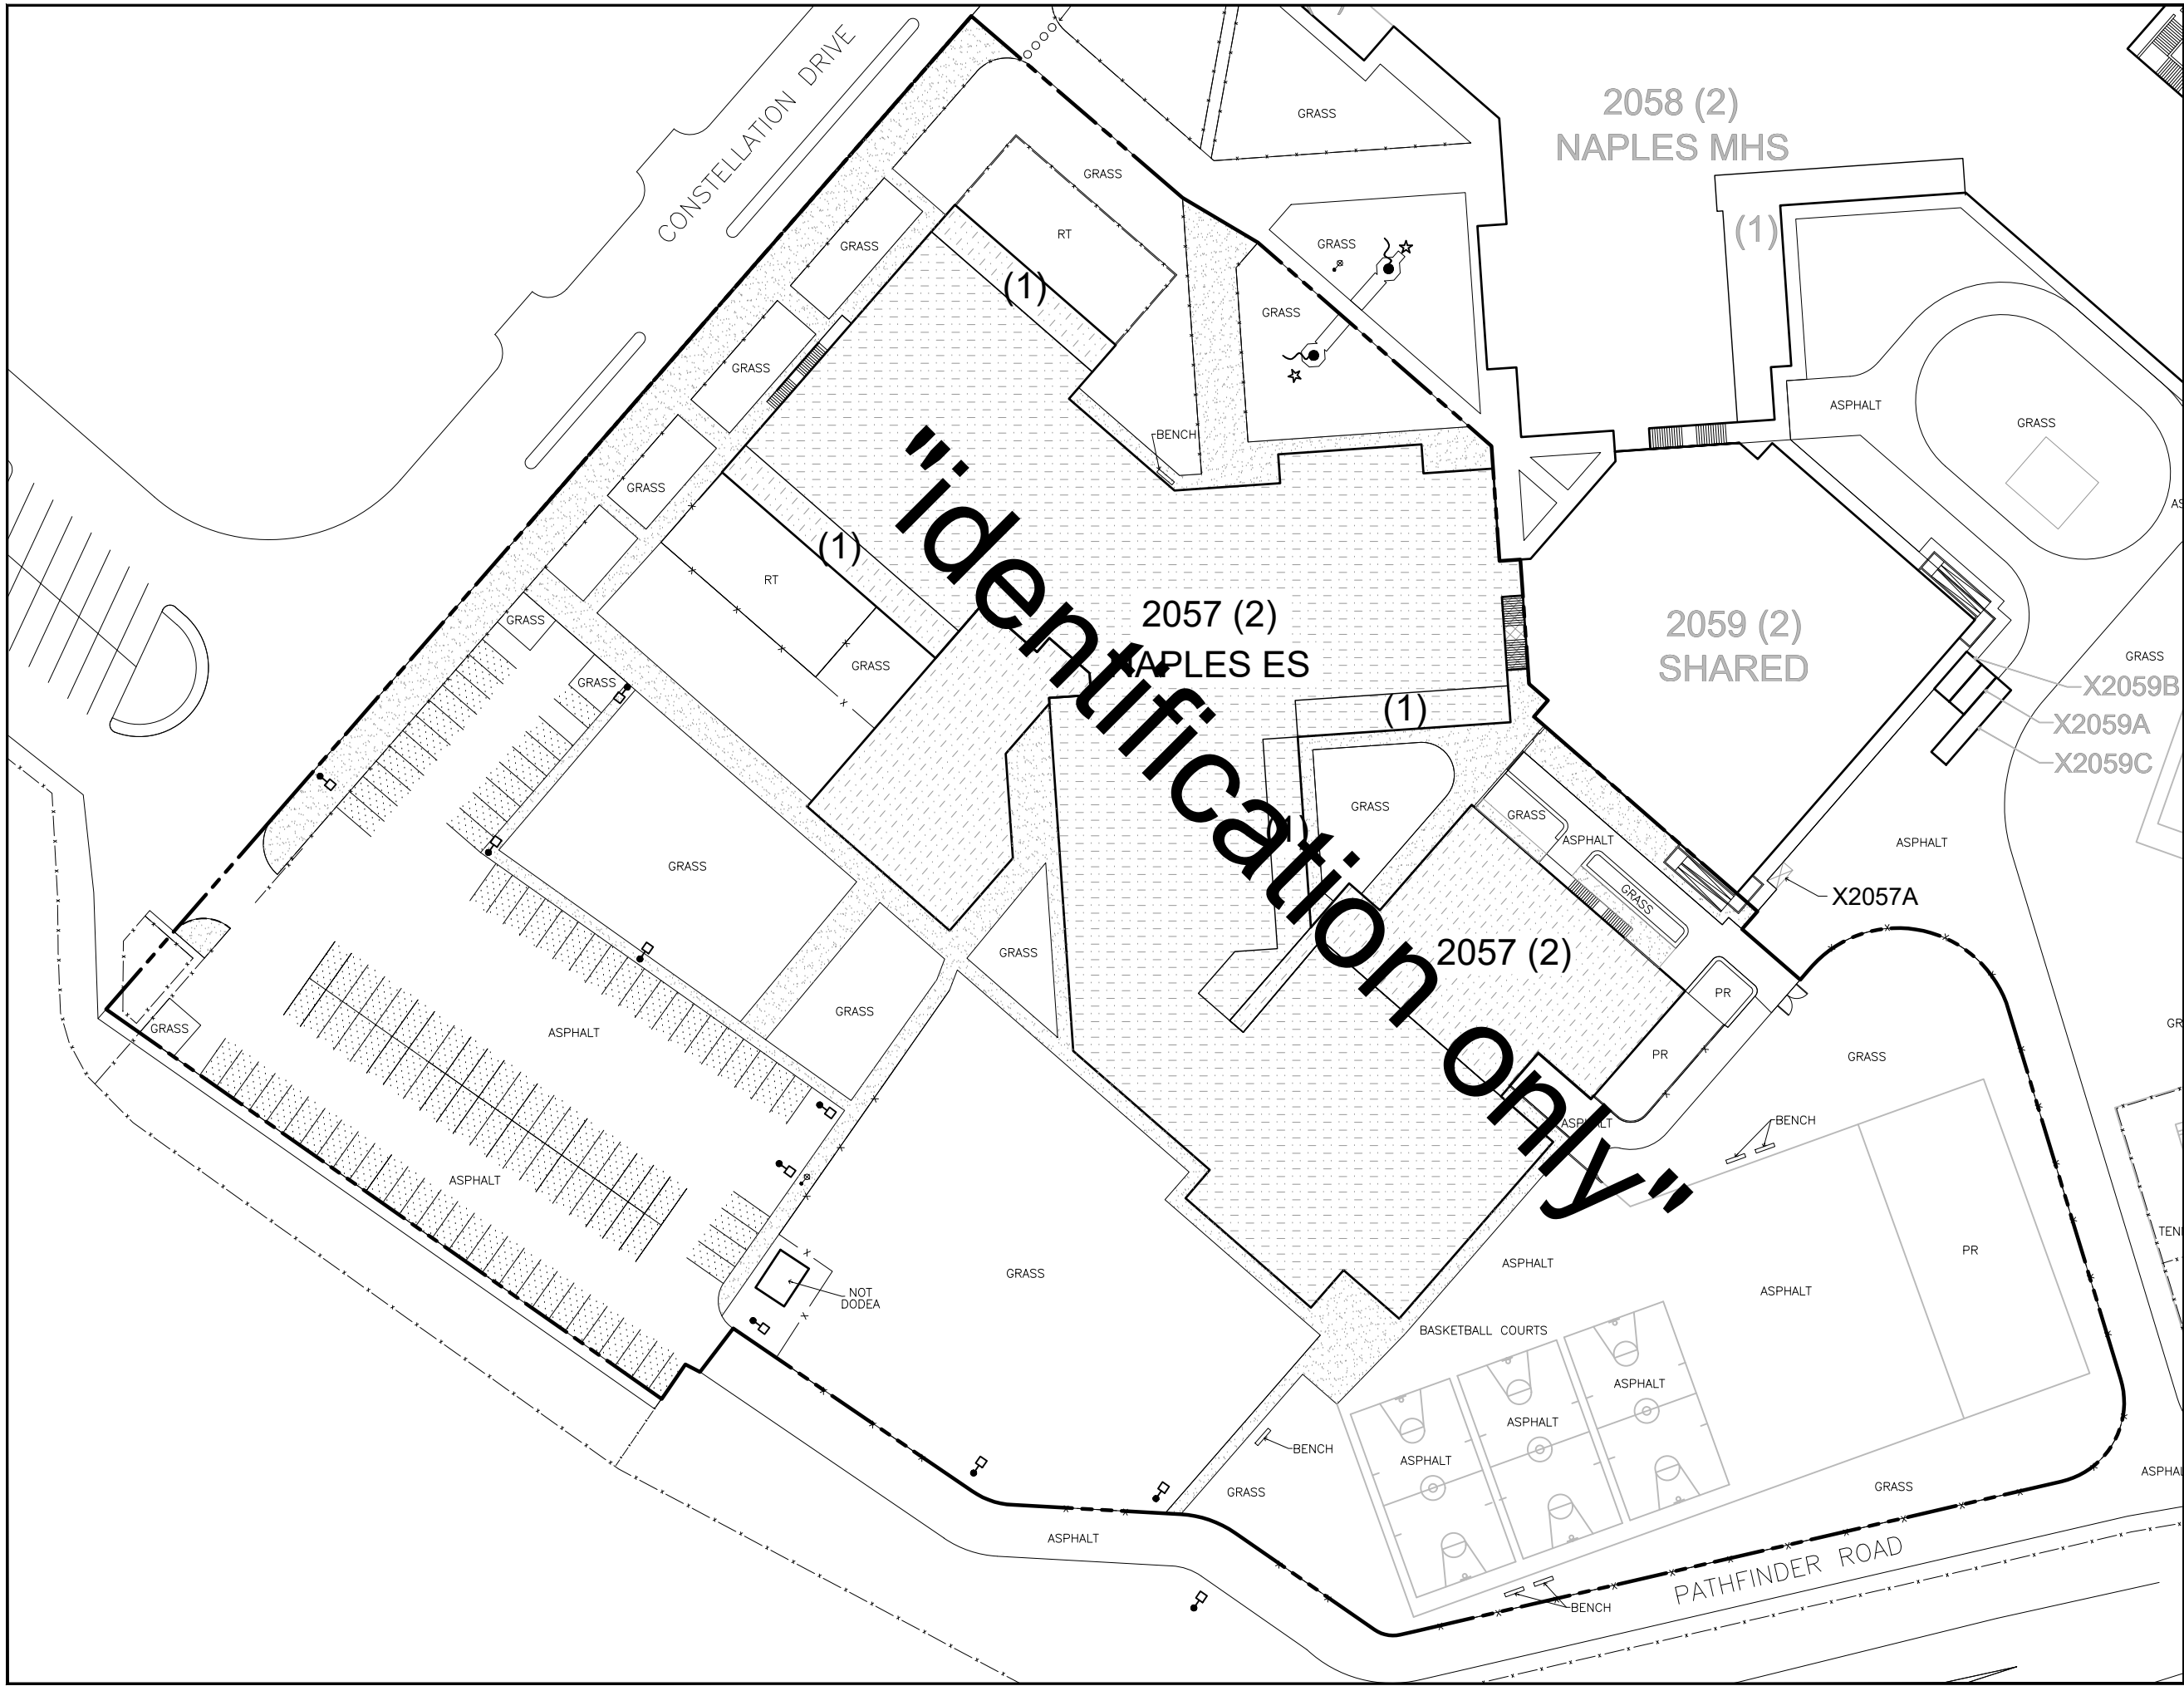


SYMBOL LEGEND	
	BASKETBALL GOAL
	STADIUM LIGHT
	SIGN
	FOOTBALL GOAL
	BASEBALL BACKSTOP
	PARKING AREA
	FLAT ROOF
	SLOPE
	COVERED WALKWAY
	SLOPING ROOF
	AREA LIGHT
	FLAG POLE
	MONUMENT
	SOCCER GOAL
	MAIN ENTRY
	CONCRETE
	PLAYGROUND
	FIRE HYDRANT
PROPERTY LINE (APPROX. 26,294 SM) (APPROX. 6.50 AC)	
FENCE LINE	

LEGEND	
PLAYGROUND SURFACING	
WC - WOOD CHIPS	PR - POURED RUBBER M - MULCH
SRT - SHREDDED RUBBER TIRES	S - SAND
PG - PEA GRAVEL	RT - RUBBER TILES

BUILDING LABEL	BLDG # (# OF FLOORS)
----------------	----------------------

	X2059B
	X2059A
	X2059C
	X2057A

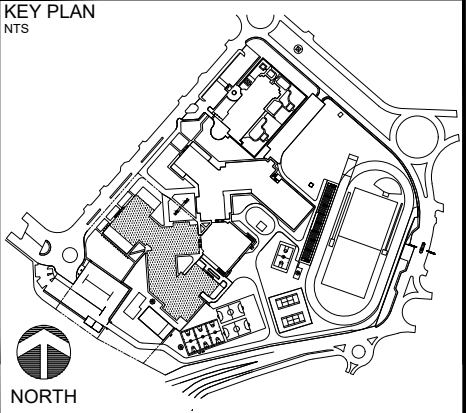


Updated By:	FUS Review:	100% Submittal Date:
AA	MRS	01 MAY 2020

DEPARTMENT OF DEFENSE EDUCATION ACTIVITY

FACILITY UTILIZATION SURVEY

NAPLES ELEMENTARY SCHOOL	
COUNTRY: ITALY INSTALLATION: NAVAL SUPPORT ACTIVITY NAPLES SITE: SUPPORT SITE REGION-DISTRICT: DODEA EUROPE SOUTH	
DoDAAC Number: HE5549	Survey Date: JANUARY 2020
Sheet Name: NAPLES ES 32ND SC (1)	Sheet Seq: 3 of 17

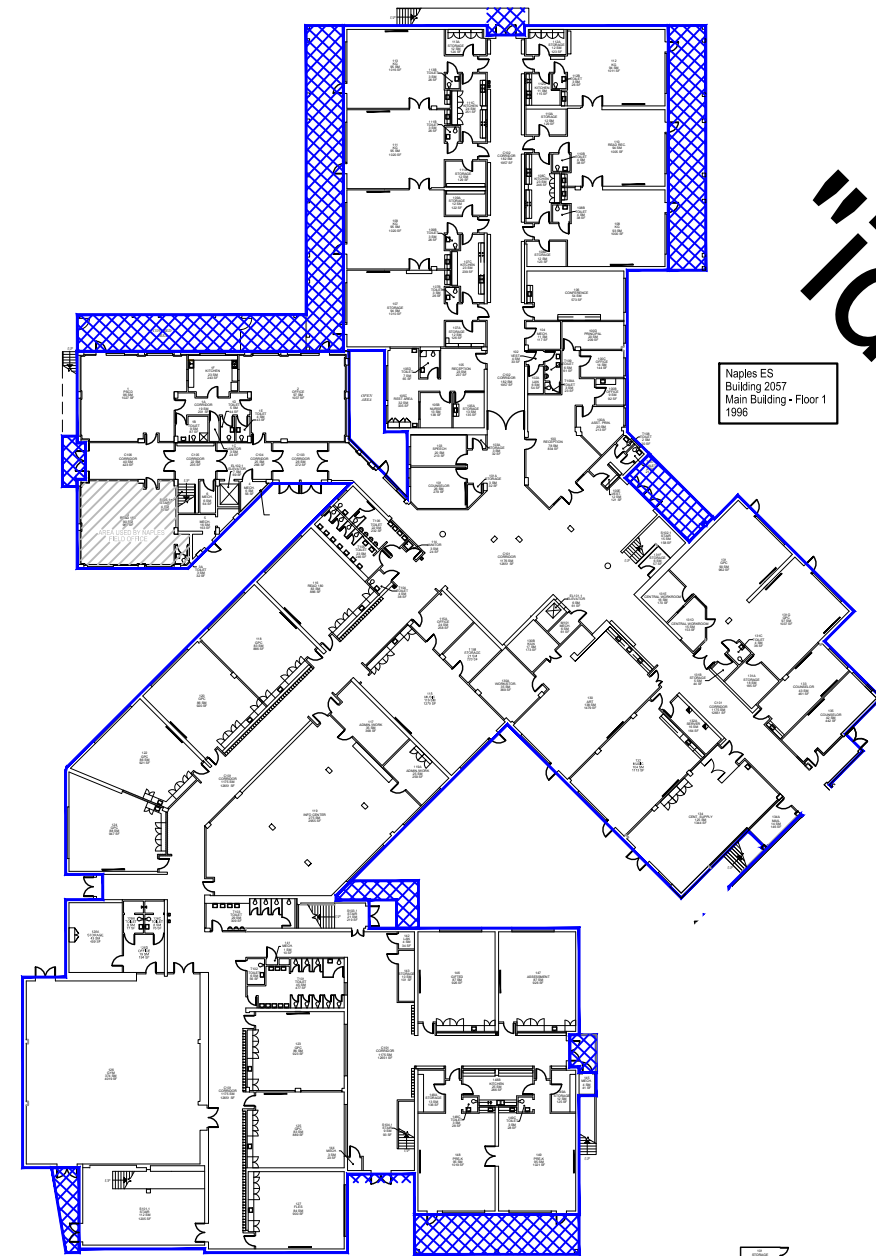


BUILDING 2057 - FIRST FLOOR

X2057A

GSF CALCULATIONS

Building 2057	
Floor 1	73,032
Floor 2	98,553
Total Area (SF)	131,585
50% Area (SF)	3,883
Gross Area (SF)	135,268

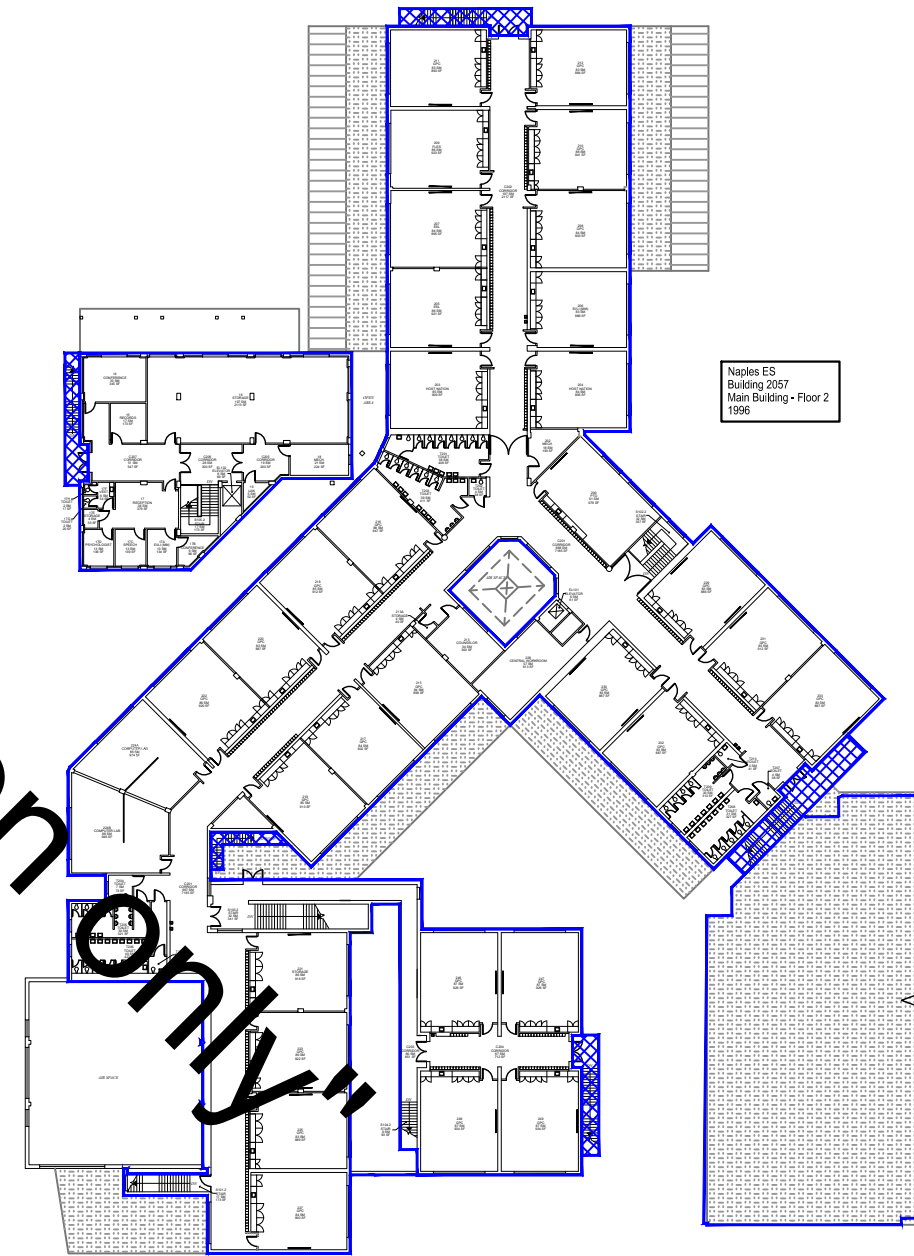

BUILDING 2057 - SECOND FLOOR

NOTE 1: APPROXIMATELY 1% OF BUILDING 2057 IS OCCUPIED BY THE EUROPE SOUTH NAPLES FOFC.
NOTE 2: APPROXIMATELY 50% OF BUILDING 2059 (MPR) IS UTILIZED BY NAPLES ELEMENTARY SCHOOL ASSIGNED TO NAPLES MIDDLE /HIGH SCHOOL .
NOTE 3: GSF CALCULATIONS BASED ON ARMY RPI DoA PAMPHLET 415-28.

DOOR

SLIDING DOOR

ACCORDION PARTITION

STACK OR FOLDING PARTITION

WINDOW/GLAZING

HIGH WINDOW

SKYLIGHT

STOOP/STEP UP

STAIR

RAMP

ACCESS LADDER

COLD STORAGE

AREA CALCULATED @ 50 %

SLOPING ROOF

DRINKING FOUNTAIN

LAVATORY

SINK

TOILET

URINAL

LOCKER

LAN DISTRIBUTION FRAME

VENT HOOD

WALL SHELVING

UPPER CABINET

BASE CABINET

TEACHER CABINET

MATCHLINE

FLAT ROOF

TITLEBLOCK LEGEND

SHEET NAME:

BLDG #_FLOOR # (# IN SERIES)

KEY PLAN

NTS

NORTH

Updated By: AA

FUS Review: MRS

100% Submittal Date: 01 MAY 2020

NOT TO SCALE

dodea

DEPARTMENT OF DEFENSE EDUCATION ACTIVITY

FACILITY UTILIZATION SURVEY

NAPLES ELEMENTARY SCHOOL

BUILDING NUMBER: 2057, X2057A

COUNTRY: ITALY

INSTALLATION: NAVAL SUPPORT ACTIVITY NAPLES

SITE: SUPPORT SITE

REGION-DISTRICT: DODEA EUROPE SOUTH

DoDAAC Number: HE5549 / HE5605



Floor: LEVEL 1, 2

Survey Date: JANUARY 2020

Sheet Name: GSF_1 (1)

Sheet Seq: 4 of 17

2057						2057						2057					
Floor	Room	Current	Capacity	Area (SF)	Area (SM)	Floor	Room	Current	Capacity	Area (SF)	Area (SM)	Floor	Room	Current	Capacity	Area (SF)	Area (SM)
1	1	PSCD	STUDENT - FULL	1,027 SF	96 SM	1	147	ASSESSMENT	OTHER	906 SF	87 SM	2	T206	TOILET	NET - GENERAL	427 SF	40 SM
1	1A	CORRIDOR	NET - GENERAL	201 SF	19 SM	1	148	PRE-K	STUDENT - FULL	1,019 SF	95 SM	2	T206A	TOILET	NET - GENERAL	39 SF	4 SM
1	1B	TOILET	NET - GENERAL	87 SF	9 SM	1	148A	STORAGE	OTHER	136 SF	13 SM	2	T207	TOILET	NET - GENERAL	38 SF	4 SM
1	1C	JANITOR	NET - GENERAL	24 SF	3 SM	1	148B	KITCHEN	OTHER	266 SF	25 SM	2	T208	TOILET	NET - GENERAL	327 SF	31 SM
1	1D	TOILET	NET - GENERAL	44 SF	5 SM	1	148C	TOILET	NET - GENERAL	28 SF	3 SM	2	T209	TOILET	NET - GENERAL	313 SF	30 SM
1	1E	TOILET	NET - GENERAL	43 SF	4 SM	1	149	PRE-K	STUDENT - FULL	1,021 SF	95 SM	2	T210	TOILET	NET - GENERAL	41 SF	4 SM
1	1F	KITCHEN	OTHER	243 SF	23 SM	1	149A	STORAGE	OTHER	125 SF	12 SM						
1	2	OFFICE	OTHER	1,037 SF	97 SM	1	149C	TOILET	NET - GENERAL	28 SF	3 SM						
1	3	READ 180	STUDENT - FULL	967 SF	90 SM	1	C101	CORRIDOR	NET - GENERAL	12,651 SF	1,176 SM						
1	3A	TOILET	NET - GENERAL	32 SF	3 SM	1	C102	CORRIDOR	NET - GENERAL	1,957 SF	182 SM						
1	4	MECH.	NET - MECH	56 SF	6 SM	1	C103	CORRIDOR	NET - GENERAL	272 SF	26 SM						
1	5	MECH.	NET - MECH	163 SF	16 SM	1	C104	CORRIDOR	NET - GENERAL	268 SF	25 SM						
1	6	MECH.	NET - MECH	64 SF	6 SM	1	C105	CORRIDOR	NET - GENERAL	235 SF	22 SM						
1	100	RECEPTION	OTHER	834 SF	78 SM	1	C106	CORRIDOR	NET - GENERAL	423 SF	40 SM						
1	100A	ASST.PRNL	OTHER	213 SF	20 SM	1	EL101.1	ELEVATOR	NET - VERTICAL	61 SF	6 SM						
1	100B	OFFICE	OTHER	92 SF	9 SM	1	EL102.1	ELEVATOR	NET - VERTICAL	69 SF	7 SM						
1	100C	OFFICE	OTHER	144 SF	14 SM	1	M101	MECH.	NET - MECH	61 SF	6 SM						
1	100D	PRINCIPAL	OTHER	209 SF	20 SM	1	S101.1	STAIR	NET - VERTICAL	1,205 SF	112 SM						
1	100E	VEST.	NET - GENERAL	121 SF	12 SM	1	S102.1	STAIR	NET - VERTICAL	158 SF	15 SM						
1	101	COUNSELOR	OTHER	279 SF	26 SM	1	S103.1	STAIR	NET - VERTICAL	219 SF	21 SM						
1	101A	STORAGE	OTHER	32 SF	3 SM	1	S104.1	STAIR	NET - VERTICAL	93 SF	9 SM						
1	102	VEST.	NET - GENERAL	33 SF	4 SM	1	S105.1	STAIR	NET - VERTICAL	36 SF	4 SM						
1	102A	LAN	NET - MECH	54 SF	6 SM	1	T101	TOILET	NET - GENERAL	477 SF	45 SM						
1	103	SPEECH	STUDENT - HALF	213 SF	20 SM	1	T102	TOILET	NET - GENERAL	96 SF	9 SM						
1	103A	STORAGE	OTHER	32 SF	3 SM	1	T103	TOILET	NET - GENERAL	309 SF	29 SM						
1	104	MECH.	NET - MECH	117 SF	11 SM	1	T104	TOILET	NET - GENERAL	38 SF	4 SM						
1	105	RECEPTION	OTHER	237 SF	23 SM	1	T105	TOILET	NET - GENERAL	246 SF	23 SM						
1	105A	STORAGE	OTHER	135 SF	13 SM	1	T106	TOILET	NET - GENERAL	232 SF	22 SM						
1	106B	NURSE	OTHER	138 SF	13 SM	1	T107	TOILET	NET - GENERAL	21 SF	2 SM						
1	106C	REST AREA	OTHER	335 SF	32 SM	1	T108	TOILET	NET - GENERAL	20 SF	2 SM						
1	106D	TOILET	OTHER	65 SF	7 SM	1	T109	TOILET	NET - GENERAL	61 SF	6 SM						
1	106	CONFERENCE	OTHER	573 SF	54 SM	1	T109A	TOILET	NET - GENERAL	23 SF	3 SM						
1	107	STORAGE	OTHER	1,010 SF	94 SM	2	14	CONFERENCE	OTHER	345 SF	33 SM						
1	107A	STORAGE	OTHER	130 SF	12 SM	2	15	RECORDS	OTHER	173 SF	17 SM						
1	107B	TOILET	NET - GENERAL	26 SF	3 SM	2	16	STORAGE	OTHER	2,113 SF	197 SM						
1	107C	KITCHEN	OTHER	239 SF	23 SM	2	17	RECEPTION	OTHER	379 SF	36 SM						
1	108	KG	STUDENT - FULL	1,000 SF	93 SM	2	17A	BLU (NM)	STUDENT - HALF	134 SF	13 SM						
1	108A	STORAGE	OTHER	123 SF	12 SM	2	17B	CONFERENCE	OTHER	96 SF	9 SM						
1	108B	TOILET	NET - GENERAL	39 SF	4 SM	2	17C	SPEECH	STUDENT - HALF	139 SF	13 SM						
1	108C	KITCHEN	OTHER	246 SF	23 SM	2	17D	PSYCHOLOGIST	OTHER	136 SF	13 SM						
1	109	KG	STUDENT - FULL	1,020 SF	95 SM	2	17E	STORAGE	OTHER	33 SF	4 SM						
1	109A	STORAGE	OTHER	122 SF	12 SM	2	17F	VEST.	NET - GENERAL	54 SF	6 SM						
1	109B	TOILET	NET - GENERAL	28 SF	3 SM	2	17G	TOILET	NET - GENERAL	20 SF	2 SM						
1	110	READ REC.	STUDENT - FULL	1,005 SF	94 SM	2	17H	TOILET	NET - GENERAL	17 SF	2 SM						
1	110A	STORAGE	OTHER	129 SF	12 SM	2	18	MECH.	NET - MECH	224 SF	21 SM						
1	110B	TOILET	NET - GENERAL	38 SF	4 SM	2	19	LAN	NET - MECH	52 SF	5 SM						
1	111	KG	STUDENT - FULL	1,020 SF	95 SM	2	200	PTO	OTHER	979 SF	91 SM						
1	111A	STORAGE	OTHER	129 SF	12 SM	2	202	MECH.	NET - MECH	163 SF	16 SM						
1	111B	TOILET	NET - GENERAL	26 SF	3 SM	2	203	HOST NATION	STUDENT - FULL	909 SF	85 SM						
1	111C	KITCHEN	OTHER	251 SF	24 SM	2	204	HOST NATION	STUDENT - FULL	895 SF	84 SM						
1	112	KG	STUDENT - FULL	1,011 SF	94 SM	2	205	ESL	STUDENT - FULL	921 SF	86 SM						
1	112A	STORAGE	OTHER	123 SF	12 SM	2	206	BLU (NM)	STUDENT - FULL	886 SF	83 SM						
1	112B	TOILET	NET - GENERAL	28 SF	3 SM	2	207	ESL	STUDENT - FULL	895 SF	84 SM						
1	112C	KITCHEN	OTHER	115 SF	11 SM	2	208	GPC	STUDENT - FULL	903 SF	84 SM						
1	113	KG	STUDENT - FULL	1,016 SF	95 SM	2	209	FLES	STUDENT - FULL	923 SF	86 SM						
1	113A	STORAGE	OTHER	134 SF	12 SM	2	210	GPC	STUDENT - FULL	941 SF	88 SM						
1	113B	TOILET	NET - GENERAL	28 SF	3 SM	2	211	GPC	STUDENT - FULL	893 SF	83 SM						
1	114	JANITOR	NET - GENERAL	24 SF	3 SM	2	212	GPC	STUDENT - FULL	884 SF	83 SM						
1	115	MUSIC	STUDENT - FULL	1,275 SF	119 SM	2	213	COUNSELOR	OTHER	363 SF	34 SM						
1	115A	OFFICE	OTHER	259 SF	24 SM	2	213A	STORAGE	OTHER	40 SF	4 SM						
1	115B	STORAGE	OTHER	228 SF	21 SM	2	215	GPC	STUDENT - FULL	899 SF	84 SM						
1	116	READ 180	STUDENT - FULL	888 SF	83 SM	2	216	GPC	STUDENT - FULL	947 SF	88 SM						
1	117	ADMIN/WORK	OTHER	369 SF	35 SM	2	217	GPC	STUDENT - FULL	902 SF	84 SM						
1	118	GPC	STUDENT - FULL	886 SF	83 SM	2	218	GPC	STUDENT - FULL	912 SF	85 SM						
1	119	INFO CENTER	OTHER	2,895 SF	275 SM	2	219	GPC	STUDENT - FULL	910 SF	85 SM						
1	119A	ADMIN/WORK	OTHER	259 SF	25 SM	2	220	GPC	STUDENT - FULL	887 SF	83 SM						
1	120	GPC	STUDENT - FULL	920 SF	86 SM	2	221	STORAGE	OTHER	918 SF	86 SM						
1	122	GPC	STUDENT - FULL	921 SF	86 SM	2	222	GPC	STUDENT - FULL	928 SF	86 SM						
1	123	GPC	STUDENT - FULL	923 SF	86 SM	2	223	GPC	STUDENT - FULL	922 SF	86 SM						
1	124	GPC	STUDENT - FULL	947 SF	88 SM	2	224A	COMPUTER LAB	STUDENT - FULL	924 SF	86 SM						
1	125	GPC	STUDENT - FULL	889 SF	83 SM	2	224B	COMPUTER LAB	STUDENT - FULL	949 SF	88 SM						
1	126	GYM	STUDENT - FULL	4,019 SF	374 SM	2	225	GPC	STUDENT - FULL	888 SF	83 SM						
1	126A	STORAGE	STUDENT - HALF	439 SF	43 SM	2	227	GPC	STUDENT - FULL	900 SF	84 SM						
1	126B	TOILET	NET - GENERAL	77 SF	8 SM	2	228	CENTRAL WORKROOM	OTHER	613 SF	57 SM						
1	126C	TOILET	NET - GENERAL	16 SF	2 SM	2	229	GPC	STUDENT - FULL	896 SF	83 SM						
1	126D	OFFICE	OTHER	194 SF	19 SM	2	230	GPC	STUDENT - FULL	887 SF	83 SM						
1	127	FLES	STUDENT - FULL	960 SF	84 SM	2	231	GPC	STUDENT - FULL	912 SF	85 SM						
1	130	ART	STUDENT - FULL	1,479 SF	138 SM	2	232	GPC	STUDENT - FULL	887 SF	83 SM						
1	130A	WORKSTOR.	OTHER	369 SF	35 SM	2	233	GPC	STUDENT - FULL	887 SF	83 SM						
1	130B	KLN	OTHER	173 SF	17 SM	2	246	GPC	STUDENT - FULL	926 SF	87 SM						
1	131	GPC	STUDENT - FULL	962 SF	90 SM	2	247	GPC	STUDENT - FULL	926 SF	87 SM						
1	131A	STORAGE	OTHER	182 SF	18 SM	2	248	GPC	STUDENT - FULL	934 SF	87 SM						
1	131B	STORAGE	OTHER	44 SF	5 SM	2	249	GPC	STUDENT - FULL	994 SF	87 SM						
1	131C	TOILET	NET - GENERAL	36 SF	4 SM	2	C201	CORRIDOR	NET - GENERAL	7,185 SF	669 SM						
1	131D	CENTRAL WORKROOM	OTHER	163 SF	15 SM	2	C202	CORRIDOR	NET - GENERAL	2,117 SF	197 SM						
1	131E	CENTRAL WORKROOM	OTHER	170 SF	16 SM	2	C203	CORRIDOR	NET - GENERAL	851 SF	80 SM						
1	131F	STORAGE	OTHER	57 SF	6 SM	2	C204	CORRIDOR	NET - GENERAL	712 SF	67 SM						
1	131G	GPC	STUDENT - FULL	1,037 SF	97 SM	2	C205	CORRIDOR	NET - GENERAL	200 SF	19 SM						
1	132	MUSIC	STUDENT - FULL	1,113 SF	104 SM	2	C206	CORRIDOR	NET - GENERAL	309 SF	28 SM						
1	132A	SERVER	NET - MECH	164 SF	16 SM	2	C207	CORRIDOR	NET - GENERAL	547 SF	51 SM						
1	133	COUNSELOR	OTHER	481 SF	43 SM	2	S101.2	STAIR	NET - VERTICAL	173 SF	17 SM						
1	134	CENT. SUPPLY	OTHER	1,344 SF	125 SM	2	S102.2	STAIR	NET - VERTICAL	337 SF	32 SM						
1	134A	MAIL	OTHER	146 SF	14 SM	2	S103.2	STAIR	NET - VERTICAL	341 SF	32 SM						
1	135	COUNSELOR	OTHER	442 SF	42 SM	2	S104.2	STAIR	NET - VERTICAL	93 SF	9 SM						
1	141	MECH.	NET - MECH	19 SF	1 SM	2	S105.2	STAIR	NET - VERTICAL	173 SF	17 SM						
1	142	LAN	NET - MECH	34 SF	4 SM	2	T201	TOILET	NET - GENERAL	408 SF	38 SM						
1	143	STORAGE	OTHER	181 SF	10 SM	2	T202	TOILET	NET - GENERAL	38 SF	4 SM						
1	144	MECH.	NET - MECH	23 SF	3 SM	2	T203	TOILET	NET - GENERAL	411 SF	39 SM						
1	145	MECH.	NET - MECH	41 SF	4 SM	2	T204	TOILET	NET - GENERAL	73 SF	7 SM						
1	146	OFFED	STUDENT														

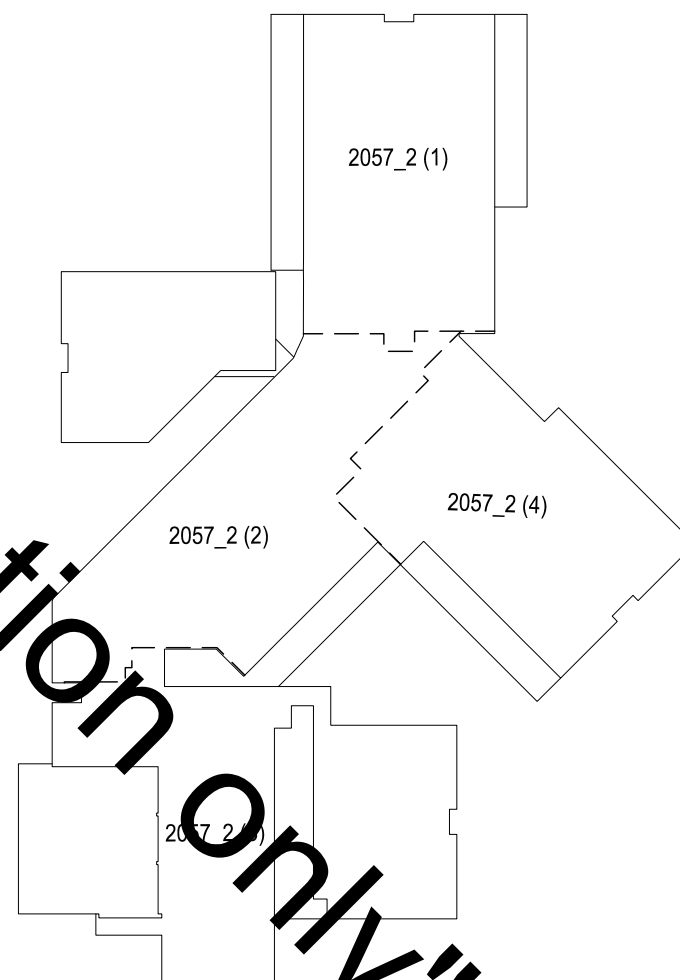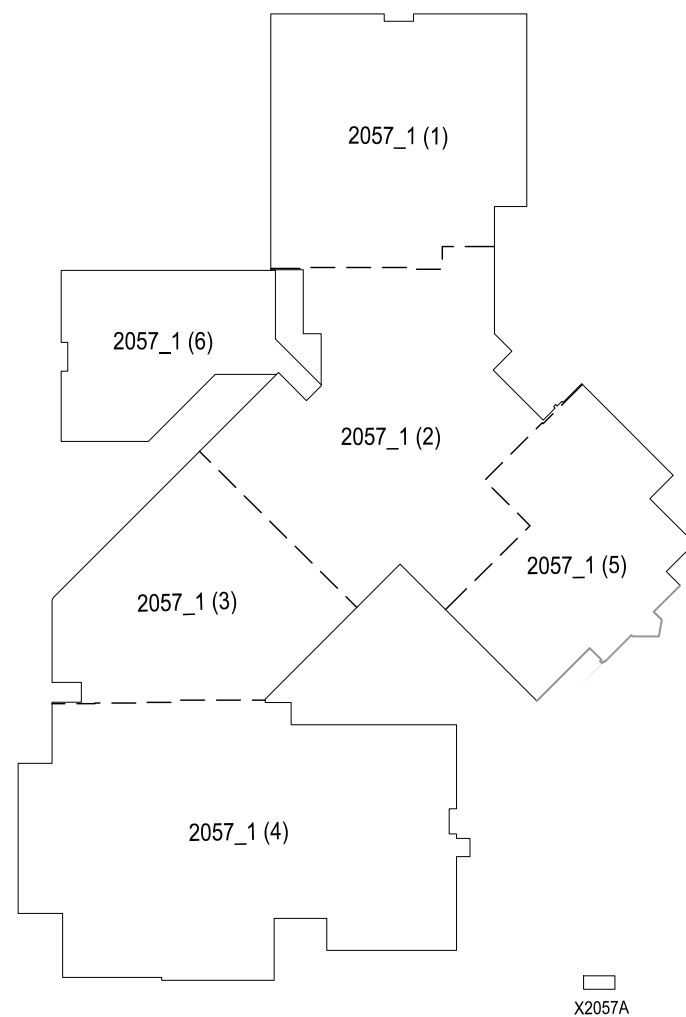

2057_2 (1)

2057_2 (2)

2057_2 (3)

2057_2 (4)

2057_2 (5)

2057_2 (6)

2057_2 (7)

2057_2 (8)

2057_2 (9)

2057_2 (10)

2057_2 (11)

2057_2 (12)

2057_2 (13)

2057_2 (14)

2057_2 (15)

2057_2 (16)

2057_2 (17)

2057_2 (18)

2057_2 (19)

2057_2 (20)

2057_2 (21)

2057_2 (22)

2057_2 (23)

2057_2 (24)

2057_2 (25)

2057_2 (26)

2057_2 (27)

2057_2 (28)

2057_2 (29)

2057_2 (30)

2057_2 (31)

2057_2 (32)

2057_2 (33)

2057_2 (34)

2057_2 (35)

2057_2 (36)

2057_2 (37)

2057_2 (38)

2057_2 (39)

2057_2 (40)

2057_2 (41)

2057_2 (42)

2057_2 (43)

2057_2 (44)

2057_2 (45)

2057_2 (46)

2057_2 (47)

2057_2 (48)

2057_2 (49)

2057_2 (50)

2057_2 (51)

2057_2 (52)

2057_2 (53)

2057_2 (54)

2057_2 (55)

2057_2 (56)

2057_2 (57)

2057_2 (58)

2057_2 (59)

2057_2 (60)

2057_2 (61)

2057_2 (62)

2057_2 (63)

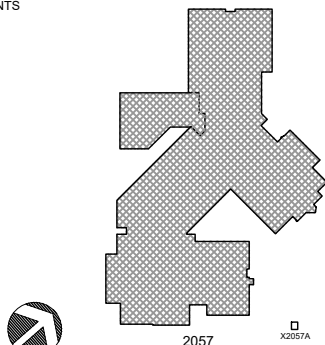SYMBOL LEGEND		
	DOOR	 DRINKING FOUNTAIN
	SLIDING DOOR	 LAVATORY
	ACCORDION PARTITION	 SINK
	STACK OR FOLDING PARTITION	 TOILET
	WINDOW/GLAZING	 URINAL
	HIGH WINDOW	 LOCKER
	SKYLIGHT	 LAN DISTRIBUTION FRAME
	STOOP/STEP UP	 VENT HOOD
	STAIR	 WALL SHELVING
	RAMP	 UPPER CABINET
	ACCESS LADDER	 BASE CABINET
	COLD STORAGE	 TEACHER CABINET
	AREA CALCULATED @ 50 %	 MATCHLINE
	SLOPING ROOF	 FLAT ROOF
TITLEBLOCK LEGEND		
SHEET NAME:		BLDG #_FLOOR # (# IN SERIES)
KEY PLAN		
		
Updated By: FUS Review: 100% Submittal Date: AA MRS 01 MAY 2020		
NOT TO SCALE		
 DEPARTMENT OF DEFENSE EDUCATION ACTIVITY		
FACILITY UTILIZATION SURVEY		
NAPLES ELEMENTARY SCHOOL BUILDING NUMBER: 2057, X2057A COUNTRY: ITALY INSTALLATION: NAVAL SUPPORT ACTIVITY NAPLES SITE: SUPPORT SITE REGION-DISTRICT: DODEA EUROPE SOUTH		
DoDAAC Number:	Floor:	Survey Date:
HE5549 / HE5605	LEVEL 1, 2	JANUARY 2020
Sheet Name:		Sheet Seq:
KEY PLAN		6 of 17

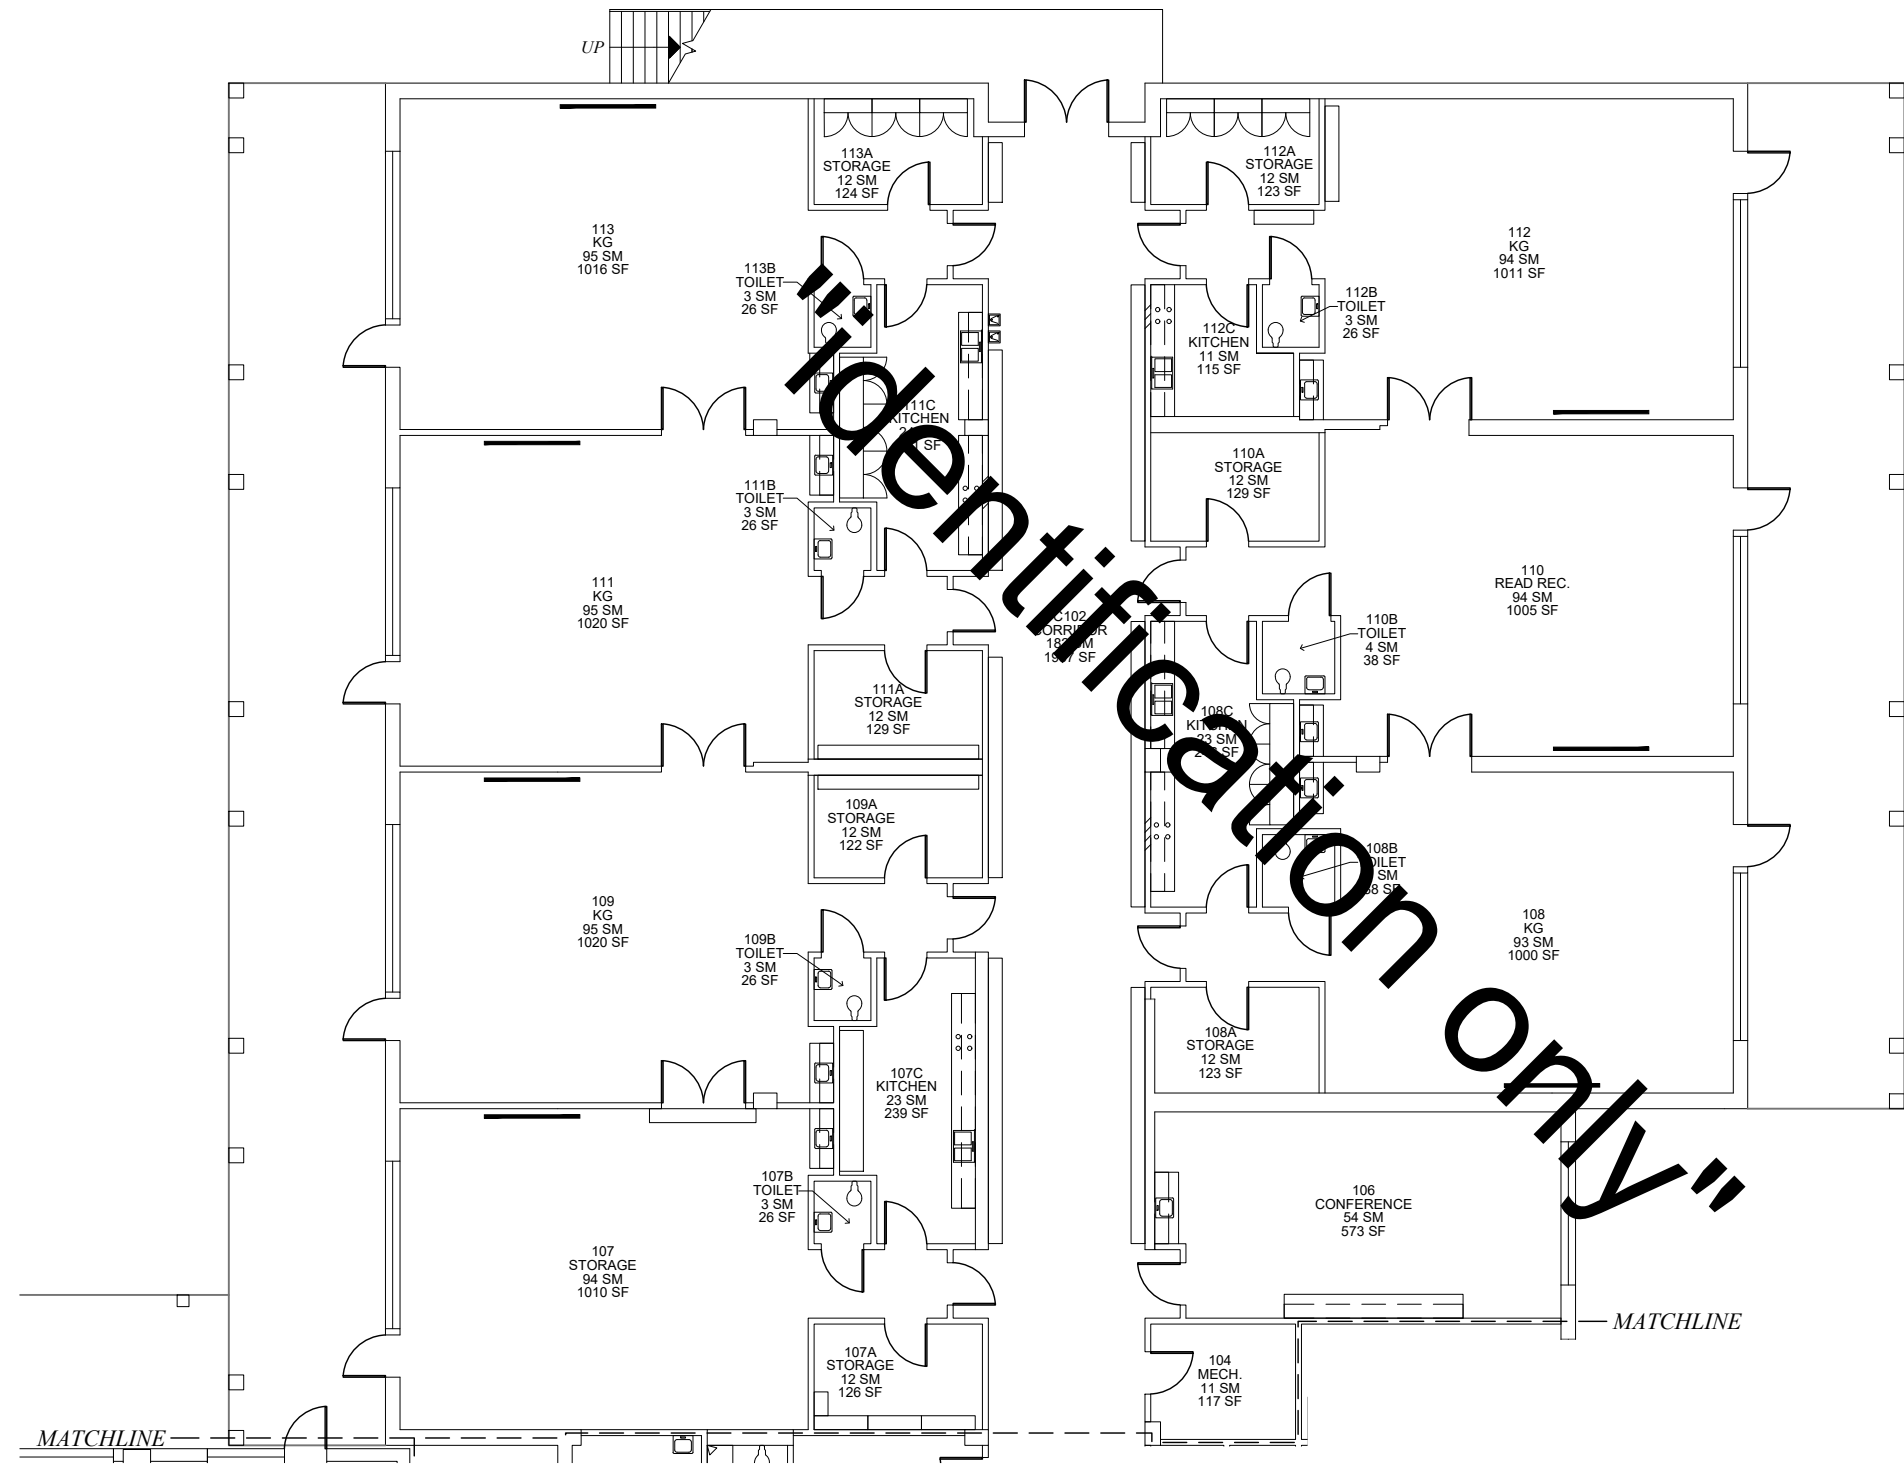


SYMBOL LEGEND	
	DOOR
	DRINKING FOUNTAIN
	SLIDING DOOR
	LAVATORY
	ACCORDION PARTITION
	SINK
	STACK OR FOLDING PARTITION
	TOILET
	WINDOW/GLAZING
	URINAL
	HIGH WINDOW
	LOCKER
	SKYLIGHT
	LAN DISTRIBUTION FRAME
	STOOP/STEP UP
	VENT HOOD
	STAIR
	WALL SHELVING
	RAMP
	UPPER CABINET
	ACCESS LADDER
	BASE CABINET
	COLD STORAGE
	TEACHER CABINET
	AREA CALCULATED @ 50 %
	MATCHLINE
	SLOPING ROOF
	FLAT ROOF

TITLEBLOCK LEGEND	
SHEET NAME:	BLDG #_FLOOR # (# IN SERIES)

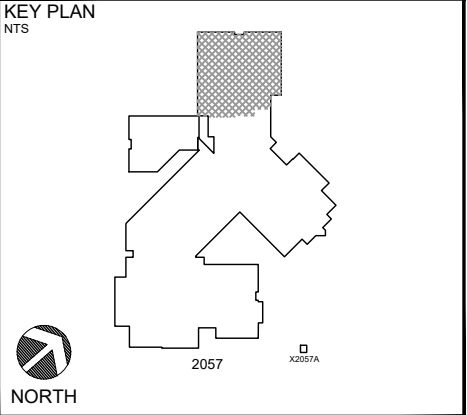

Updated By:	FUS Review:	100% Submittal Date:
AA	MRS	01 MAY 2020
0 2 4 8 16 FT		
DEPARTMENT OF DEFENSE EDUCATION ACTIVITY		
FACILITY UTILIZATION SURVEY		
NAPLES ELEMENTARY SCHOOL		
BUILDING NUMBER: 2057		
COUNTRY: ITALY		
INSTALLATION: NAVAL SUPPORT ACTIVITY NAPLES		
SITE: SUPPORT SITE		
REGION-DISTRICT: DODEA EUROPE SOUTH		
DoDAAC Number:	Floor:	Survey Date:
HE5549 / HE5605	LEVEL 1	JANUARY 2020
Sheet Name:	Sheet Seq:	
2057_1 (1)	7 of 17	

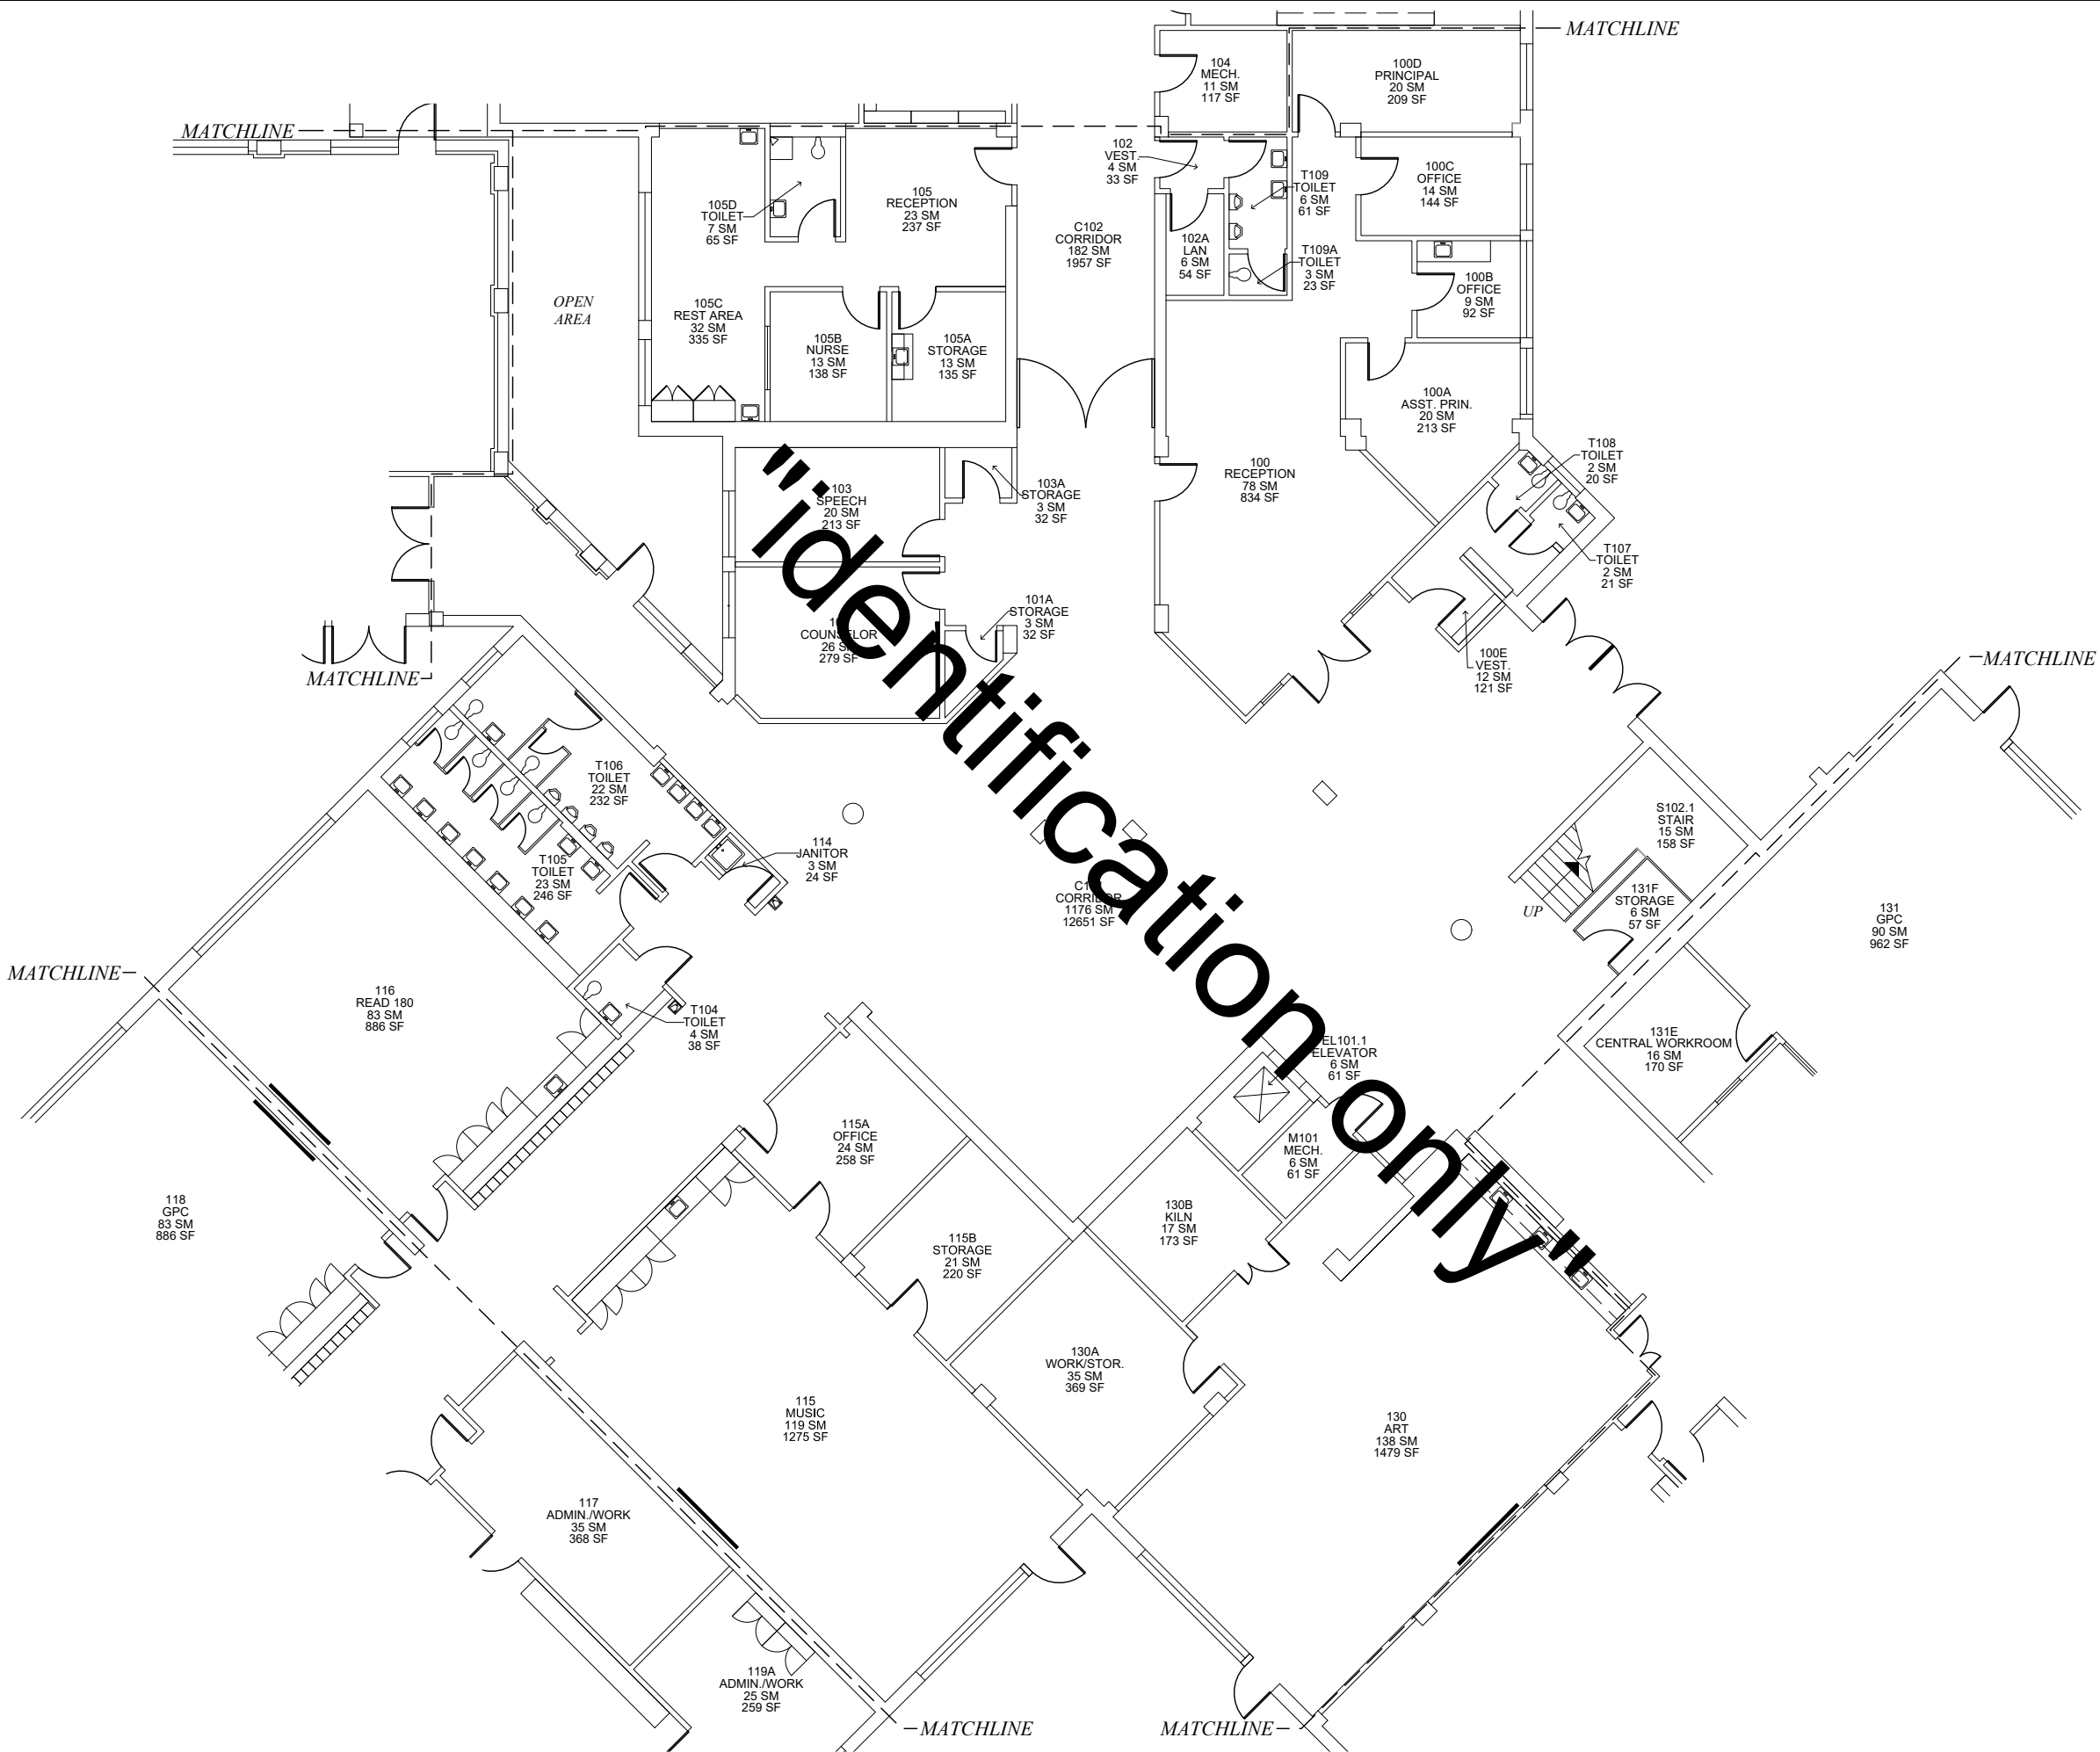

DOOR

SLIDING DOOR

ACCORDION PARTITION

STACK OR FOLDING PARTITION

WINDOW/GLAZING

HIGH WINDOW

SKYLIGHT

STOOP/STEP UP

STAIR

RAMP

ACCESS LADDER

COLD STORAGE

AREA CALCULATED @ 50 %

SLOPING ROOF

DRINKING FOUNTAIN

LAVATORY

SINK

TOILET

URINAL

LOCKER

LAN DISTRIBUTION FRAME

VENT HOOD

WALL SHELVING

UPPER CABINET

BASE CABINET

TEACHER CABINET

MATCHLINE

FLAT ROOF

TITLEBLOCK LEGEND

SHEET NAME:

BLDG #_FLOOR # (# IN SERIES)

KEY PLAN

NTS

NORTH

2057

X2057A

Updated By: AA

FUS Review: MRS

100% Submittal Date: 01 MAY 2020

0

2

4

8

16

FT

dodea

DEPARTMENT OF DEFENSE EDUCATION ACTIVITY

FACILITY UTILIZATION SURVEY

NAPLES

ELEMENTARY SCHOOL

BUILDING NUMBER: 2057

COUNTRY: ITALY

INSTALLATION: NAVAL SUPPORT ACTIVITY NAPLES

SITE: SUPPORT SITE

REGION-DISTRICT: DODEA EUROPE SOUTH


DoDAAC Number: HE5549 / HE5605

Floor: LEVEL 1

Survey Date: JANUARY 2020


Sheet Name: 2057_1 (2)

Sheet Seq: 8 of 17

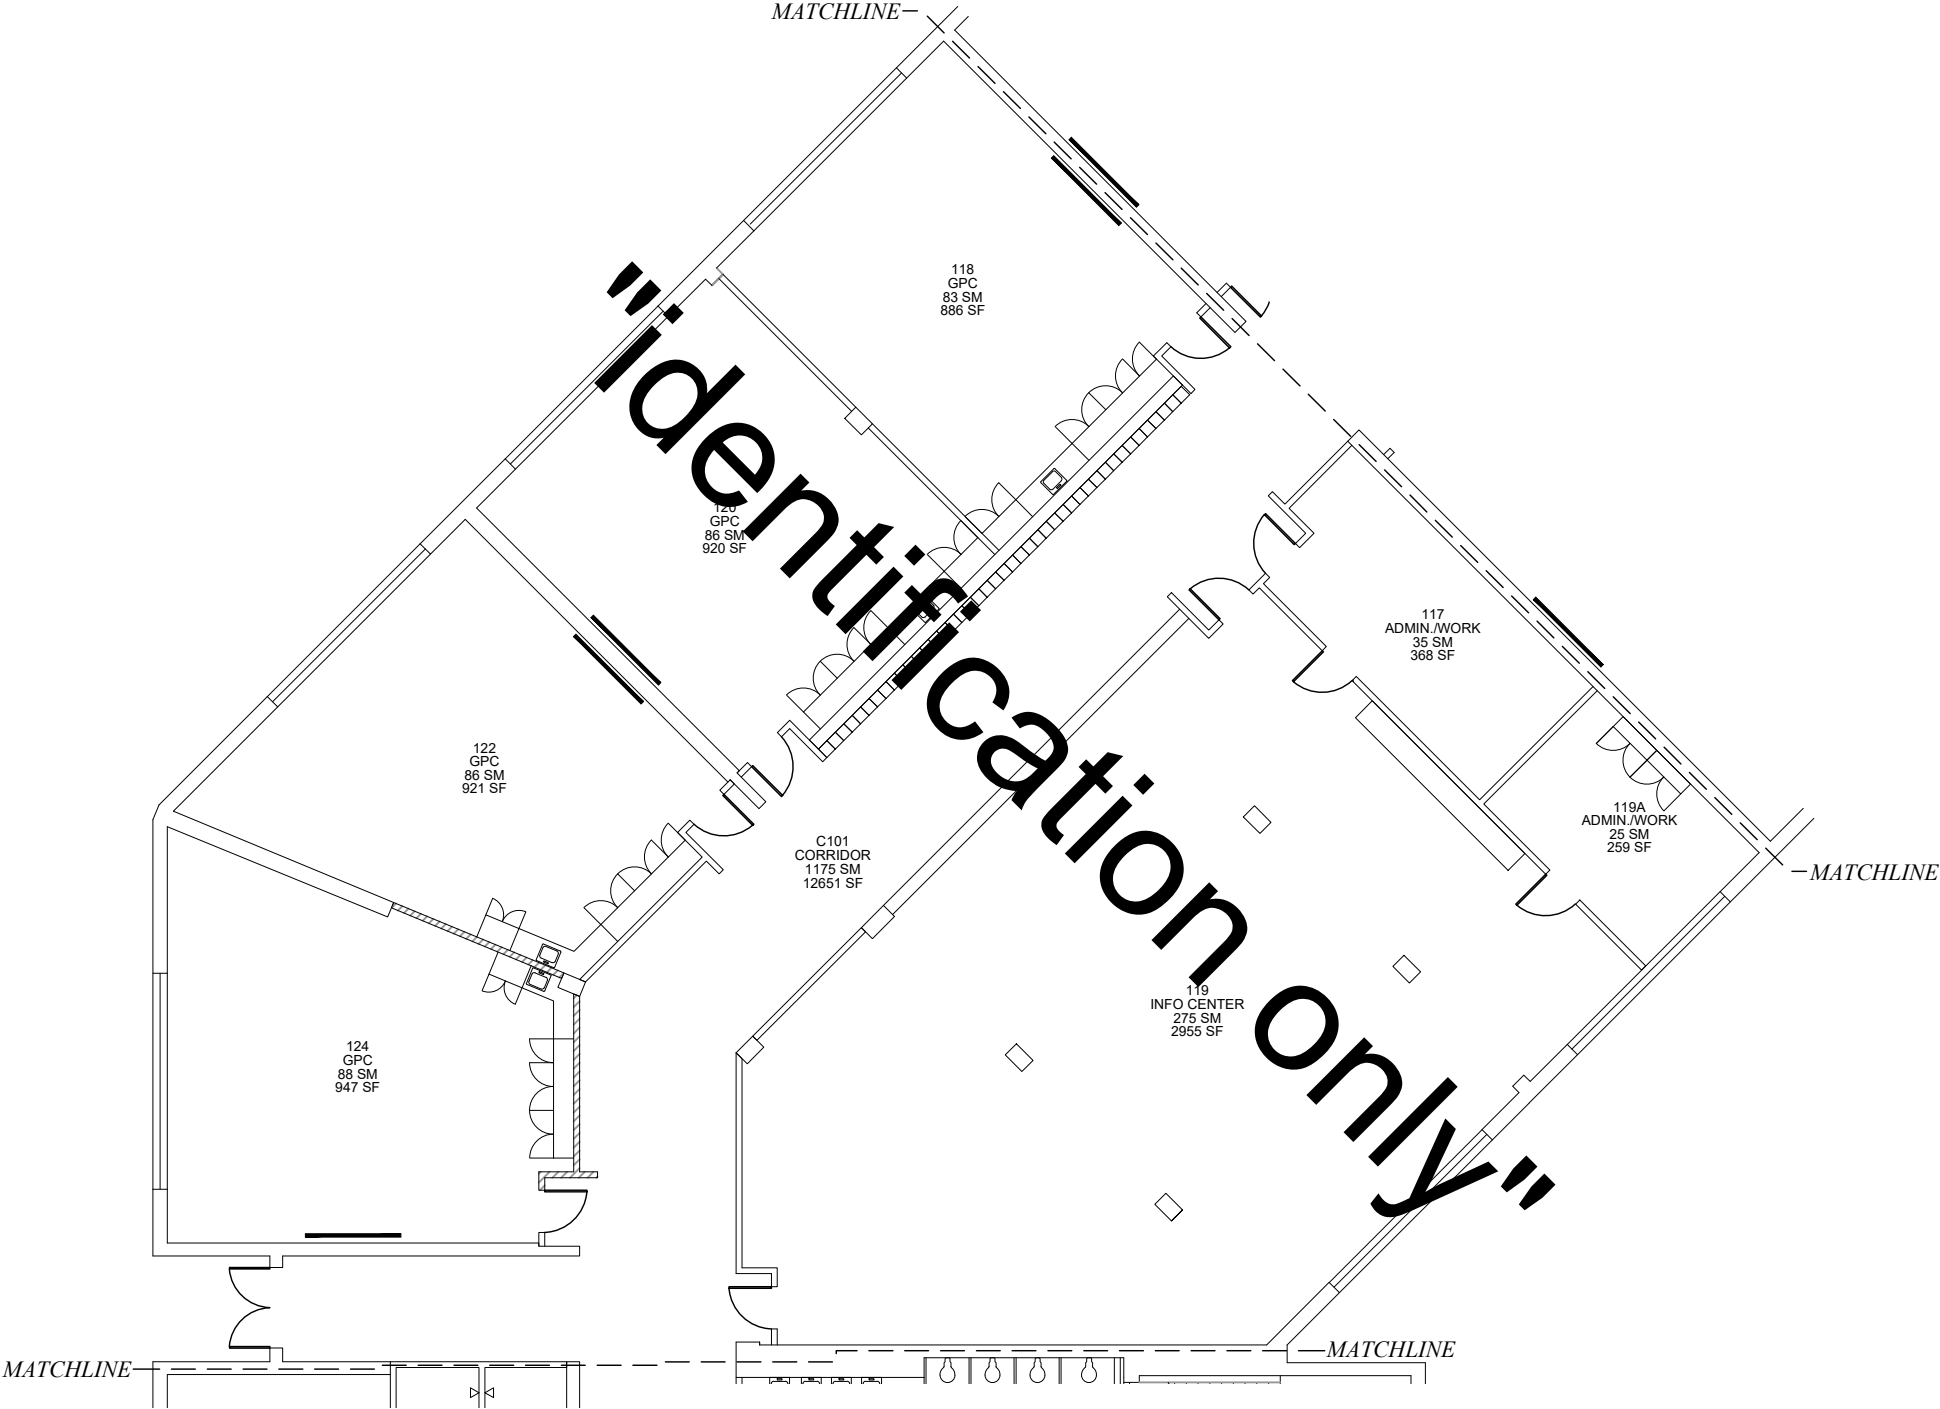

SYMBOL LEGEND	
	DOOR
	DRINKING FOUNTAIN
	SLIDING DOOR
	LAVATORY
	ACCORDION PARTITION
	SINK
	STACK OR FOLDING PARTITION
	TOILET
	WINDOW/GLAZING
	URINAL
	HIGH WINDOW
	LOCKER
	SKYLIGHT
	LAN DISTRIBUTION FRAME
	STOOP/STEP UP
	VENT HOOD
	STAIR
	WALL SHELVING
	RAMP
	UPPER CABINET
	ACCESS LADDER
	BASE CABINET
	COLD STORAGE
	TEACHER CABINET
	AREA CALCULATED @ 50 %
	MATCHLINE
	SLOPING ROOF
	FLAT ROOF

TITLEBLOCK LEGEND	
SHEET NAME:	BLDG #_FLOOR # (# IN SERIES)

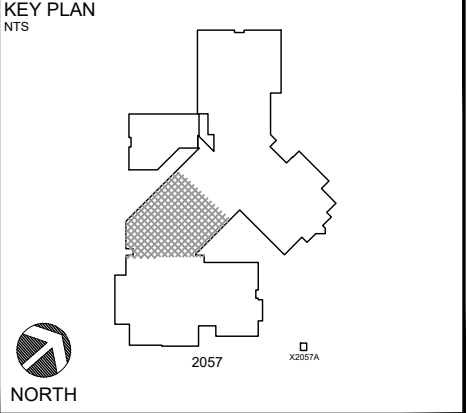

Updated By:	FUS Review:	100% Submittal Date:
AA	MRS	01 MAY 2020
0 2 4 8 16 FT		




DEPARTMENT OF DEFENSE EDUCATION ACTIVITY

FACILITY UTILIZATION SURVEY

NAPLES
ELEMENTARY SCHOOL
BUILDING NUMBER: 2057
COUNTRY: ITALY
INSTALLATION: NAVAL SUPPORT ACTIVITY NAPLES
SITE: SUPPORT SITE
REGION-DISTRICT: DODEA EUROPE SOUTH

DoDAAC Number:	Floor:	Survey Date:
HE5549 / HE5605	LEVEL 1	JANUARY 2020
Sheet Name:	Sheet Seq:	
2057_1 (3)	9 of 17	

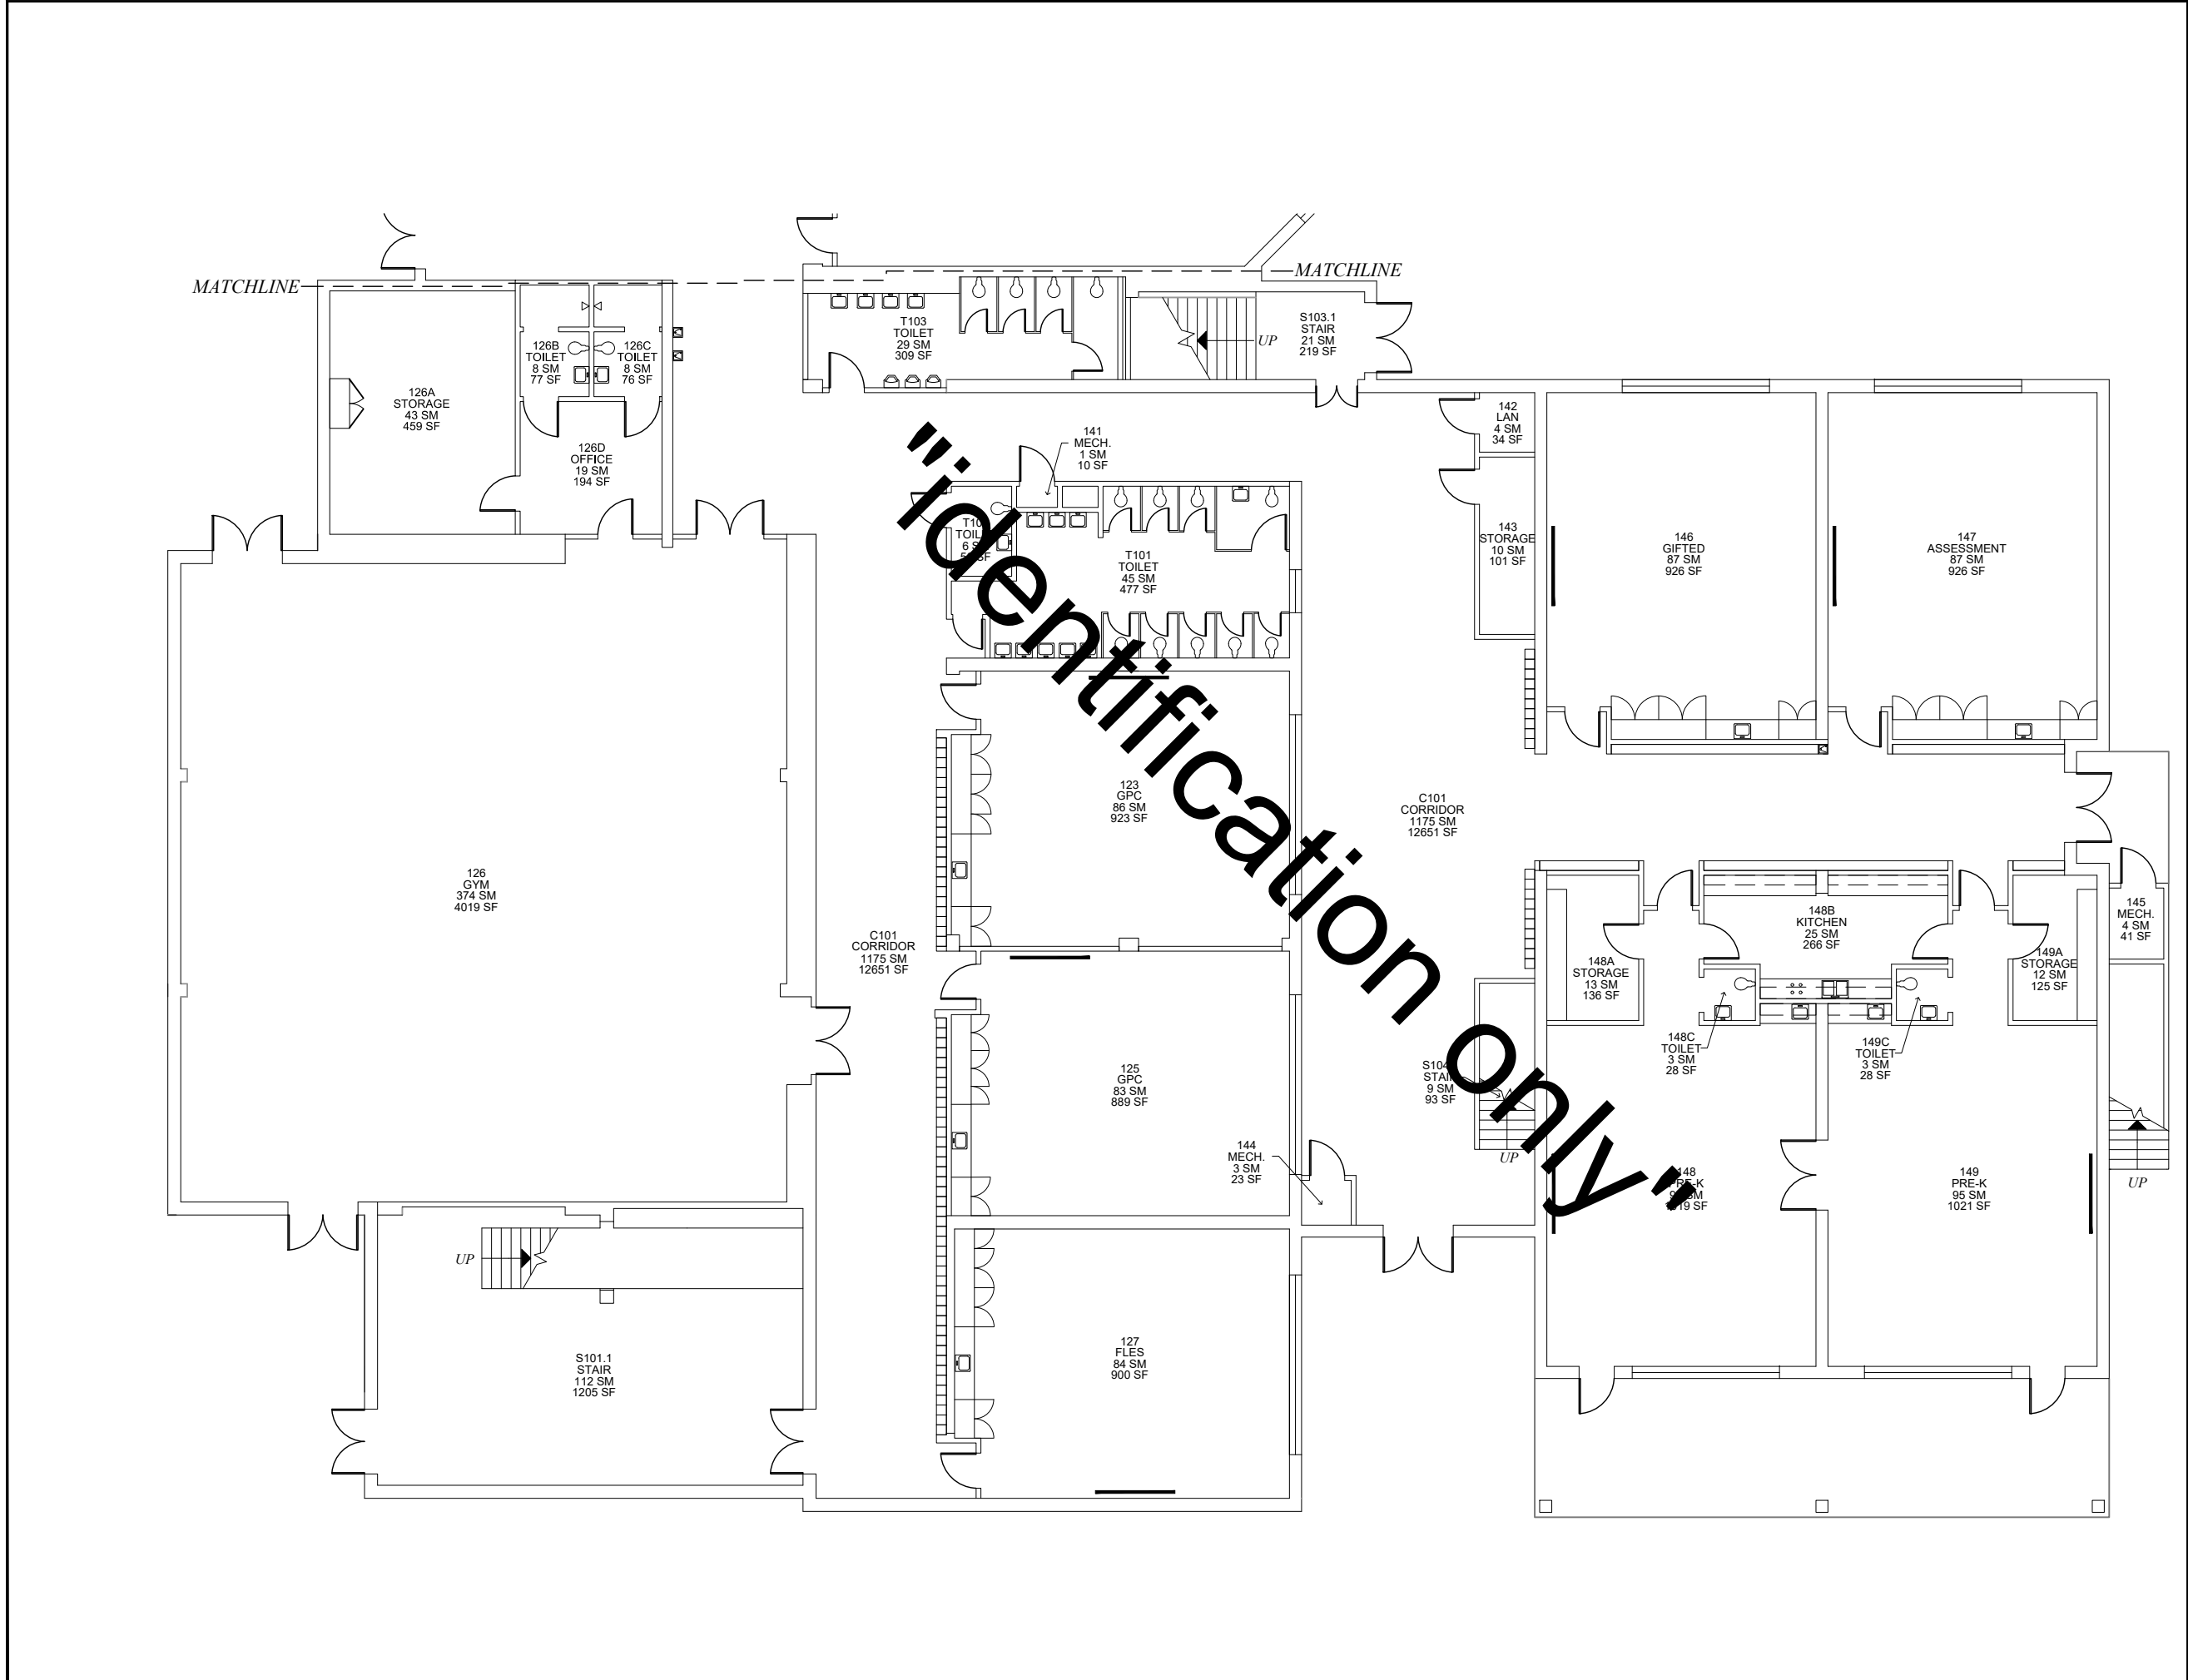

DOOR

SLIDING DOOR

ACCORDION PARTITION

STACK OR FOLDING PARTITION

WINDOW/GLAZING

HIGH WINDOW

SKYLIGHT

STOOP/STEP UP

STAIR

RAMP

ACCESS LADDER

COLD STORAGE

AREA CALCULATED @ 50 %

SLOPING ROOF

DRINKING FOUNTAIN

LAVATORY

SINK

TOILET

URINAL

LOCKER

LAN DISTRIBUTION FRAME

VENT HOOD

WALL SHELVING

UPPER CABINET

BASE CABINET

TEACHER CABINET

FLAT ROOF

TITLEBLOCK LEGEND

SHEET NAME:

BLDG #_FLOOR # (# IN SERIES)

KEY PLAN

NTS

NORTH

0 2 4 8 16 FT

dodea

DEPARTMENT OF DEFENSE EDUCATION ACTIVITY

FACILITY UTILIZATION SURVEY

NAPLES

ELEMENTARY SCHOOL

BUILDING NUMBER: 2057

COUNTRY: ITALY

INSTALLATION: NAVAL SUPPORT ACTIVITY NAPLES

SITE: SUPPORT SITE

REGION-DISTRICT: DODEA EUROPE SOUTH

DoDAAC Number:

HE5549 / HE5605

Floor:

LEVEL 1

Survey Date:


JANUARY 2020

Sheet Name:

2057_1 (4)

Sheet Seq:

10 of 17

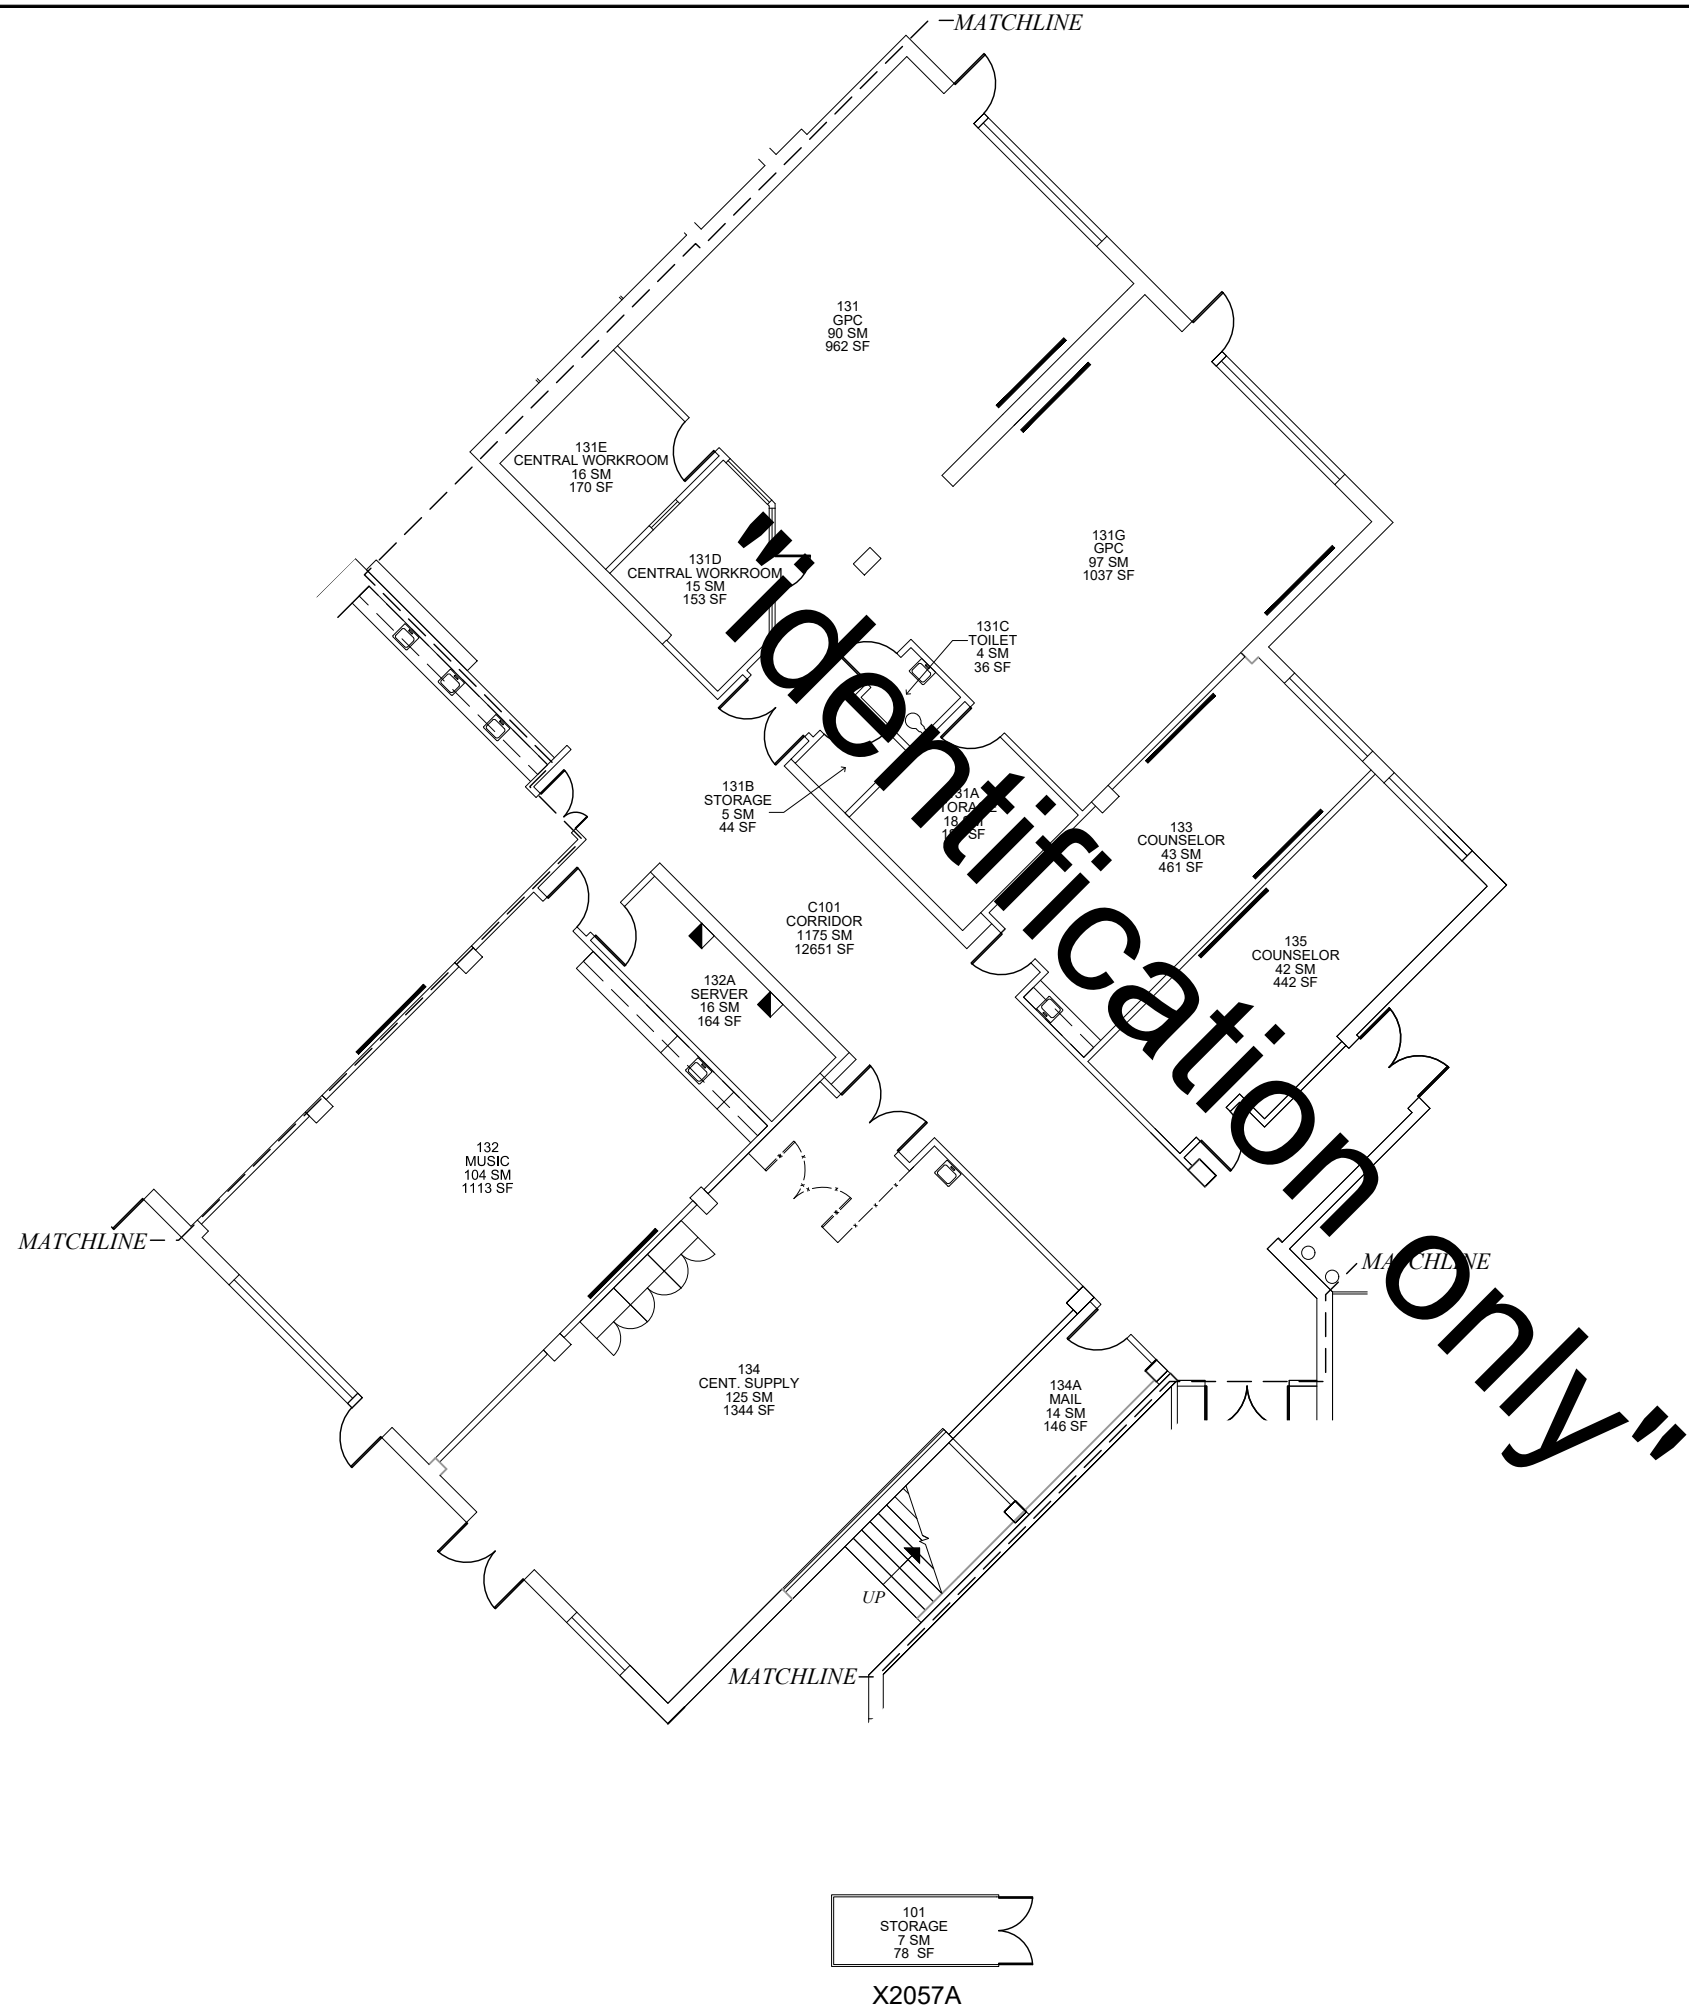

SYMBOL LEGEND

DOOR	DRINKING FOUNTAIN
SLIDING DOOR	LAVATORY
ACCORDION PARTITION	SINK
STACK OR FOLDING PARTITION	TOILET
WINDOW/GLAZING	URINAL
HIGH WINDOW	LOCKER
SKYLIGHT	LAN DISTRIBUTION FRAME
STOOP/STEP UP	VENT HOOD
STAIR	WALL SHELVING
RAMP	UPPER CABINET
ACCESS LADDER	BASE CABINET
COLD STORAGE	TEACHER CABINET
AREA CALCULATED @ 50 %	MATCHLINE
SLOPING ROOF	FLAT ROOF

TITLEBLOCK LEGEND

SHEET NAME:	BLDG #_FLOOR # (# IN SERIES)

KEY PLAN

NTS

NORTH

Updated By:	FUS Review:	100% Submittal Date:
AA	MRS	01 MAY 2020

0

2

4

8

16

FT

dodea

DEPARTMENT OF DEFENSE EDUCATION ACTIVITY

FACILITY UTILIZATION SURVEY

NAPLES

ELEMENTARY SCHOOL

BUILDING NUMBER: 2057, X2057A


COUNTRY: ITALY

INSTALLATION: NAVAL SUPPORT ACTIVITY NAPLES

SITE: SUPPORT SITE

REGION-DISTRICT: DODEA EUROPE SOUTH

DoDAAC Number:	Floor:	Survey Date:
HE5549 / HE5605	LEVEL 1	JANUARY 2020
Sheet Name:		Sheet Seq:
2057_1 (5)		11 of 17

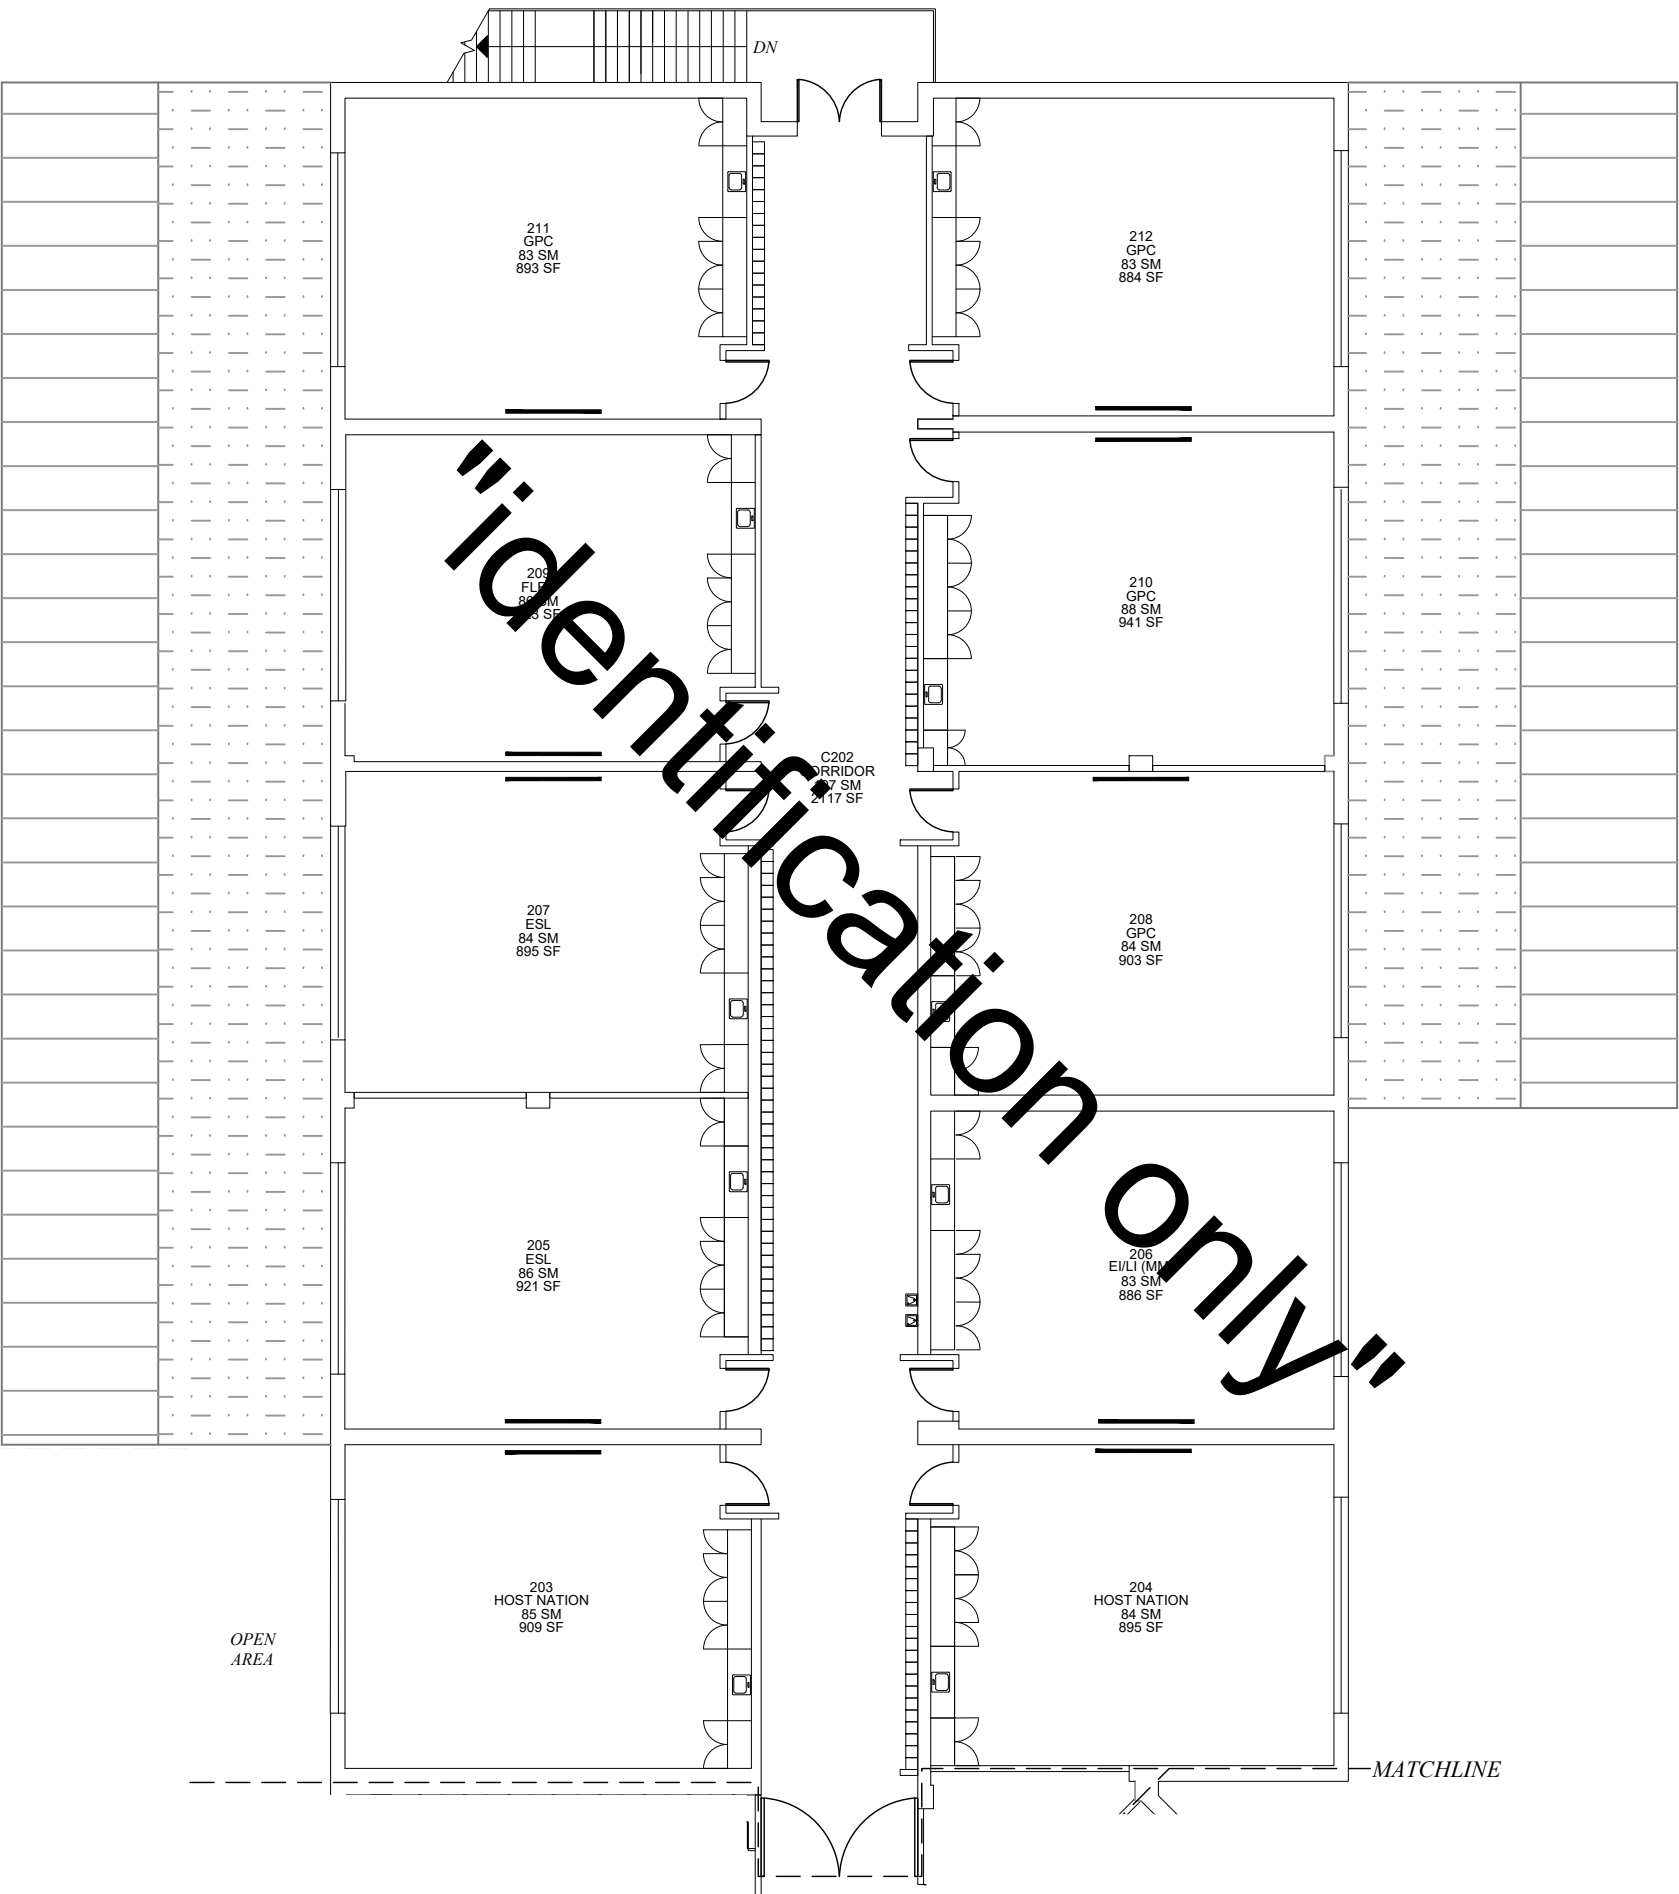

SYMBOL LEGEND

DOOR	DRINKING FOUNTAIN
SLIDING DOOR	LAVATORY
ACCORDION PARTITION	SINK
STACK OR FOLDING PARTITION	TOILET
WINDOW/GLAZING	URINAL
HIGH WINDOW	LOCKER
SKYLIGHT	LAN DISTRIBUTION FRAME
STOOP/STEP UP	VENT HOOD
STAIR	WALL SHELVING
RAMP	UPPER CABINET
ACCESS LADDER	BASE CABINET
COLD STORAGE	TEACHER CABINET
AREA CALCULATED @ 50 %	MATCHLINE
SLOPING ROOF	FLAT ROOF

TITLEBLOCK LEGEND

SHEET NAME:	BLDG #_FLOOR # (# IN SERIES)

KEY PLAN

NTS

NORTH

Updated By:	FUS Review:	100% Submittal Date:
AA	MRS	01 MAY 2020

0

2

4

8

16

FT

dodea

DEPARTMENT OF DEFENSE EDUCATION ACTIVITY

FACILITY UTILIZATION SURVEY

NAPLES

ELEMENTARY SCHOOL

BUILDING NUMBER: 2057

COUNTRY: ITALY


INSTALLATION: NAVAL SUPPORT ACTIVITY NAPLES

SITE: SUPPORT SITE

REGION-DISTRICT: DODEA EUROPE SOUTH

DoDAAC Number:	Floor:	Survey Date:
HE5549 / HE5605	LEVEL 2	JANUARY 2020

Sheet Name:	Sheet Seq:
2057_2 (1)	13 of 17

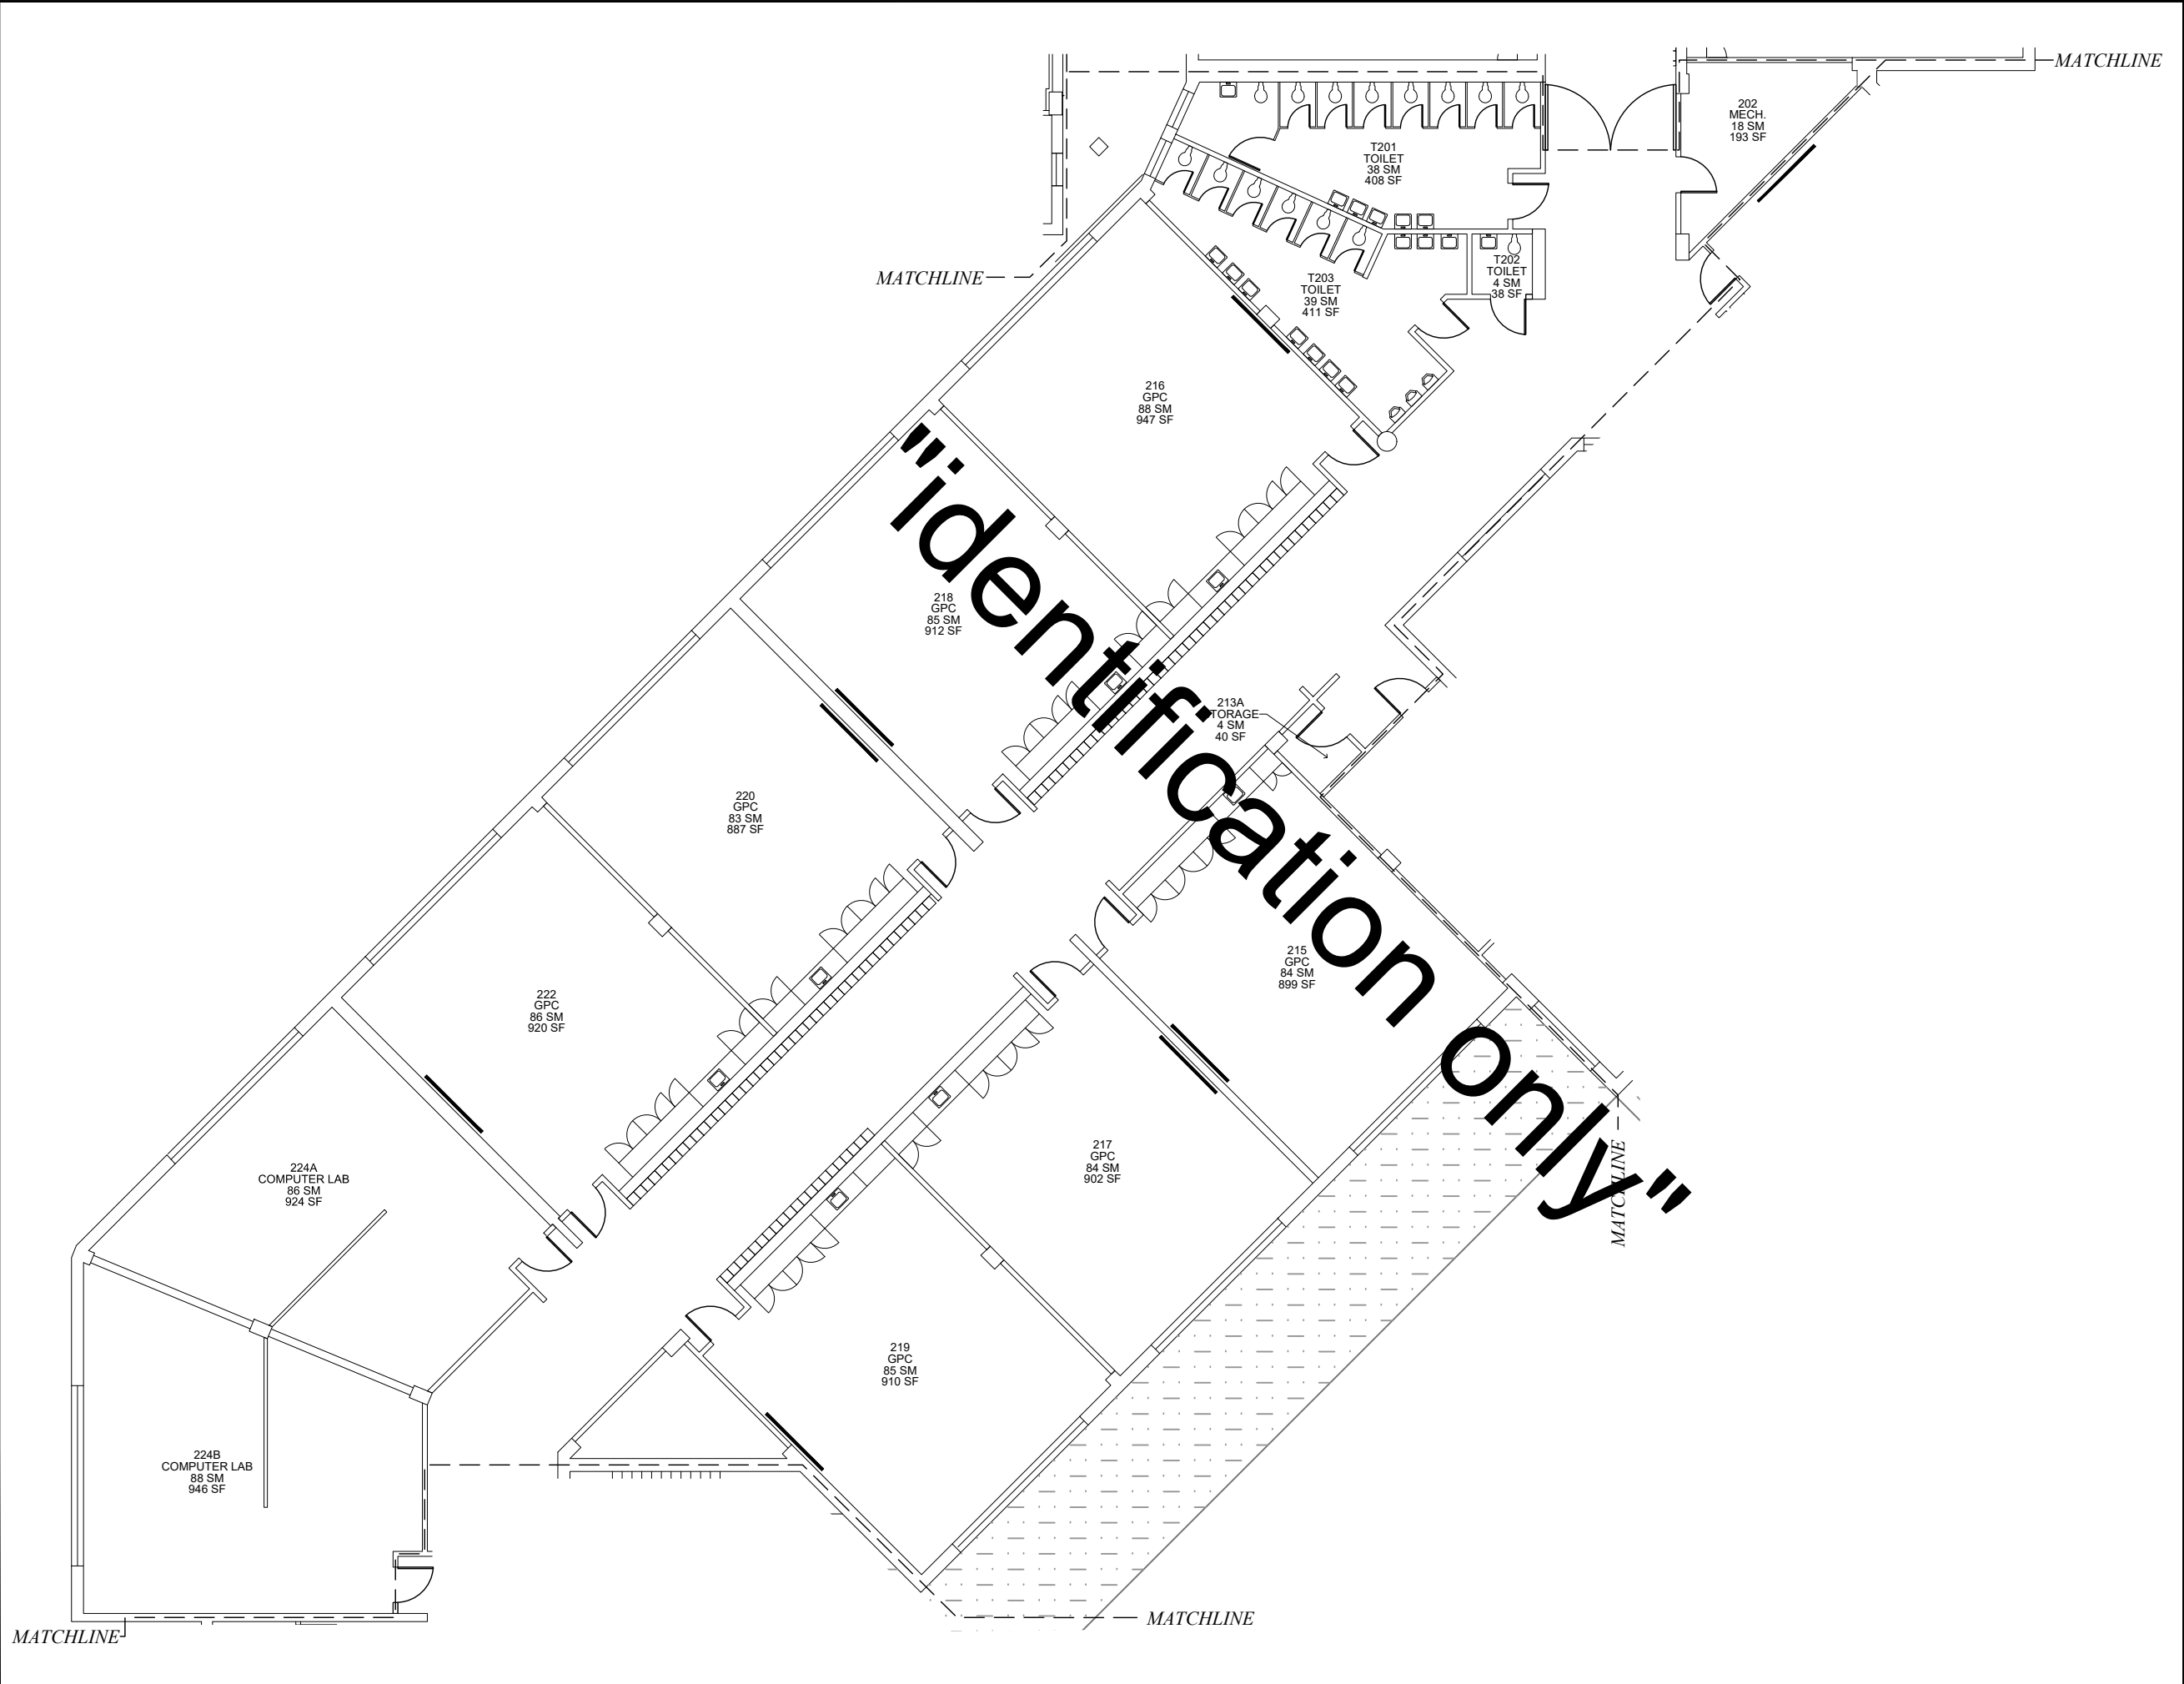

SYMBOL LEGEND

DOOR	DRINKING FOUNTAIN
SLIDING DOOR	LAVATORY
ACCORDION PARTITION	SINK
STACK OR FOLDING PARTITION	TOILET
WINDOW/GLAZING	URINAL
HIGH WINDOW	LOCKER
SKYLIGHT	LAN DISTRIBUTION FRAME
STOOP/STEP UP	VENT HOOD
STAIR	WALL SHELVING
RAMP	UPPER CABINET
ACCESS LADDER	BASE CABINET
COLD STORAGE	TEACHER CABINET
AREA CALCULATED @ 50 %	MATCHLINE
SLOPING ROOF	FLAT ROOF

TITLEBLOCK LEGEND

SHEET NAME:	BLDG #_FLOOR # (# IN SERIES)

KEY PLAN

NTS

NORTH

Updated By:

AA

FUS Review:

MRS

100% Submittal Date:

01 MAY 2020

0

2

4

8

16

FT

dodea

DEPARTMENT OF DEFENSE EDUCATION ACTIVITY

FACILITY UTILIZATION SURVEY

NAPLES

ELEMENTARY SCHOOL

BUILDING NUMBER: 2057

COUNTRY: ITALY

INSTALLATION: NAVAL SUPPORT ACTIVITY NAPLES

SITE: SUPPORT SITE

REGION-DISTRICT: DODEA EUROPE SOUTH

DoDAAC Number:

HE5549 / HE5605

Floor:

LEVEL 2

Survey Date:


JANUARY 2020

Sheet Name:

2057_2 (2)

Sheet Seq:

14 of 17

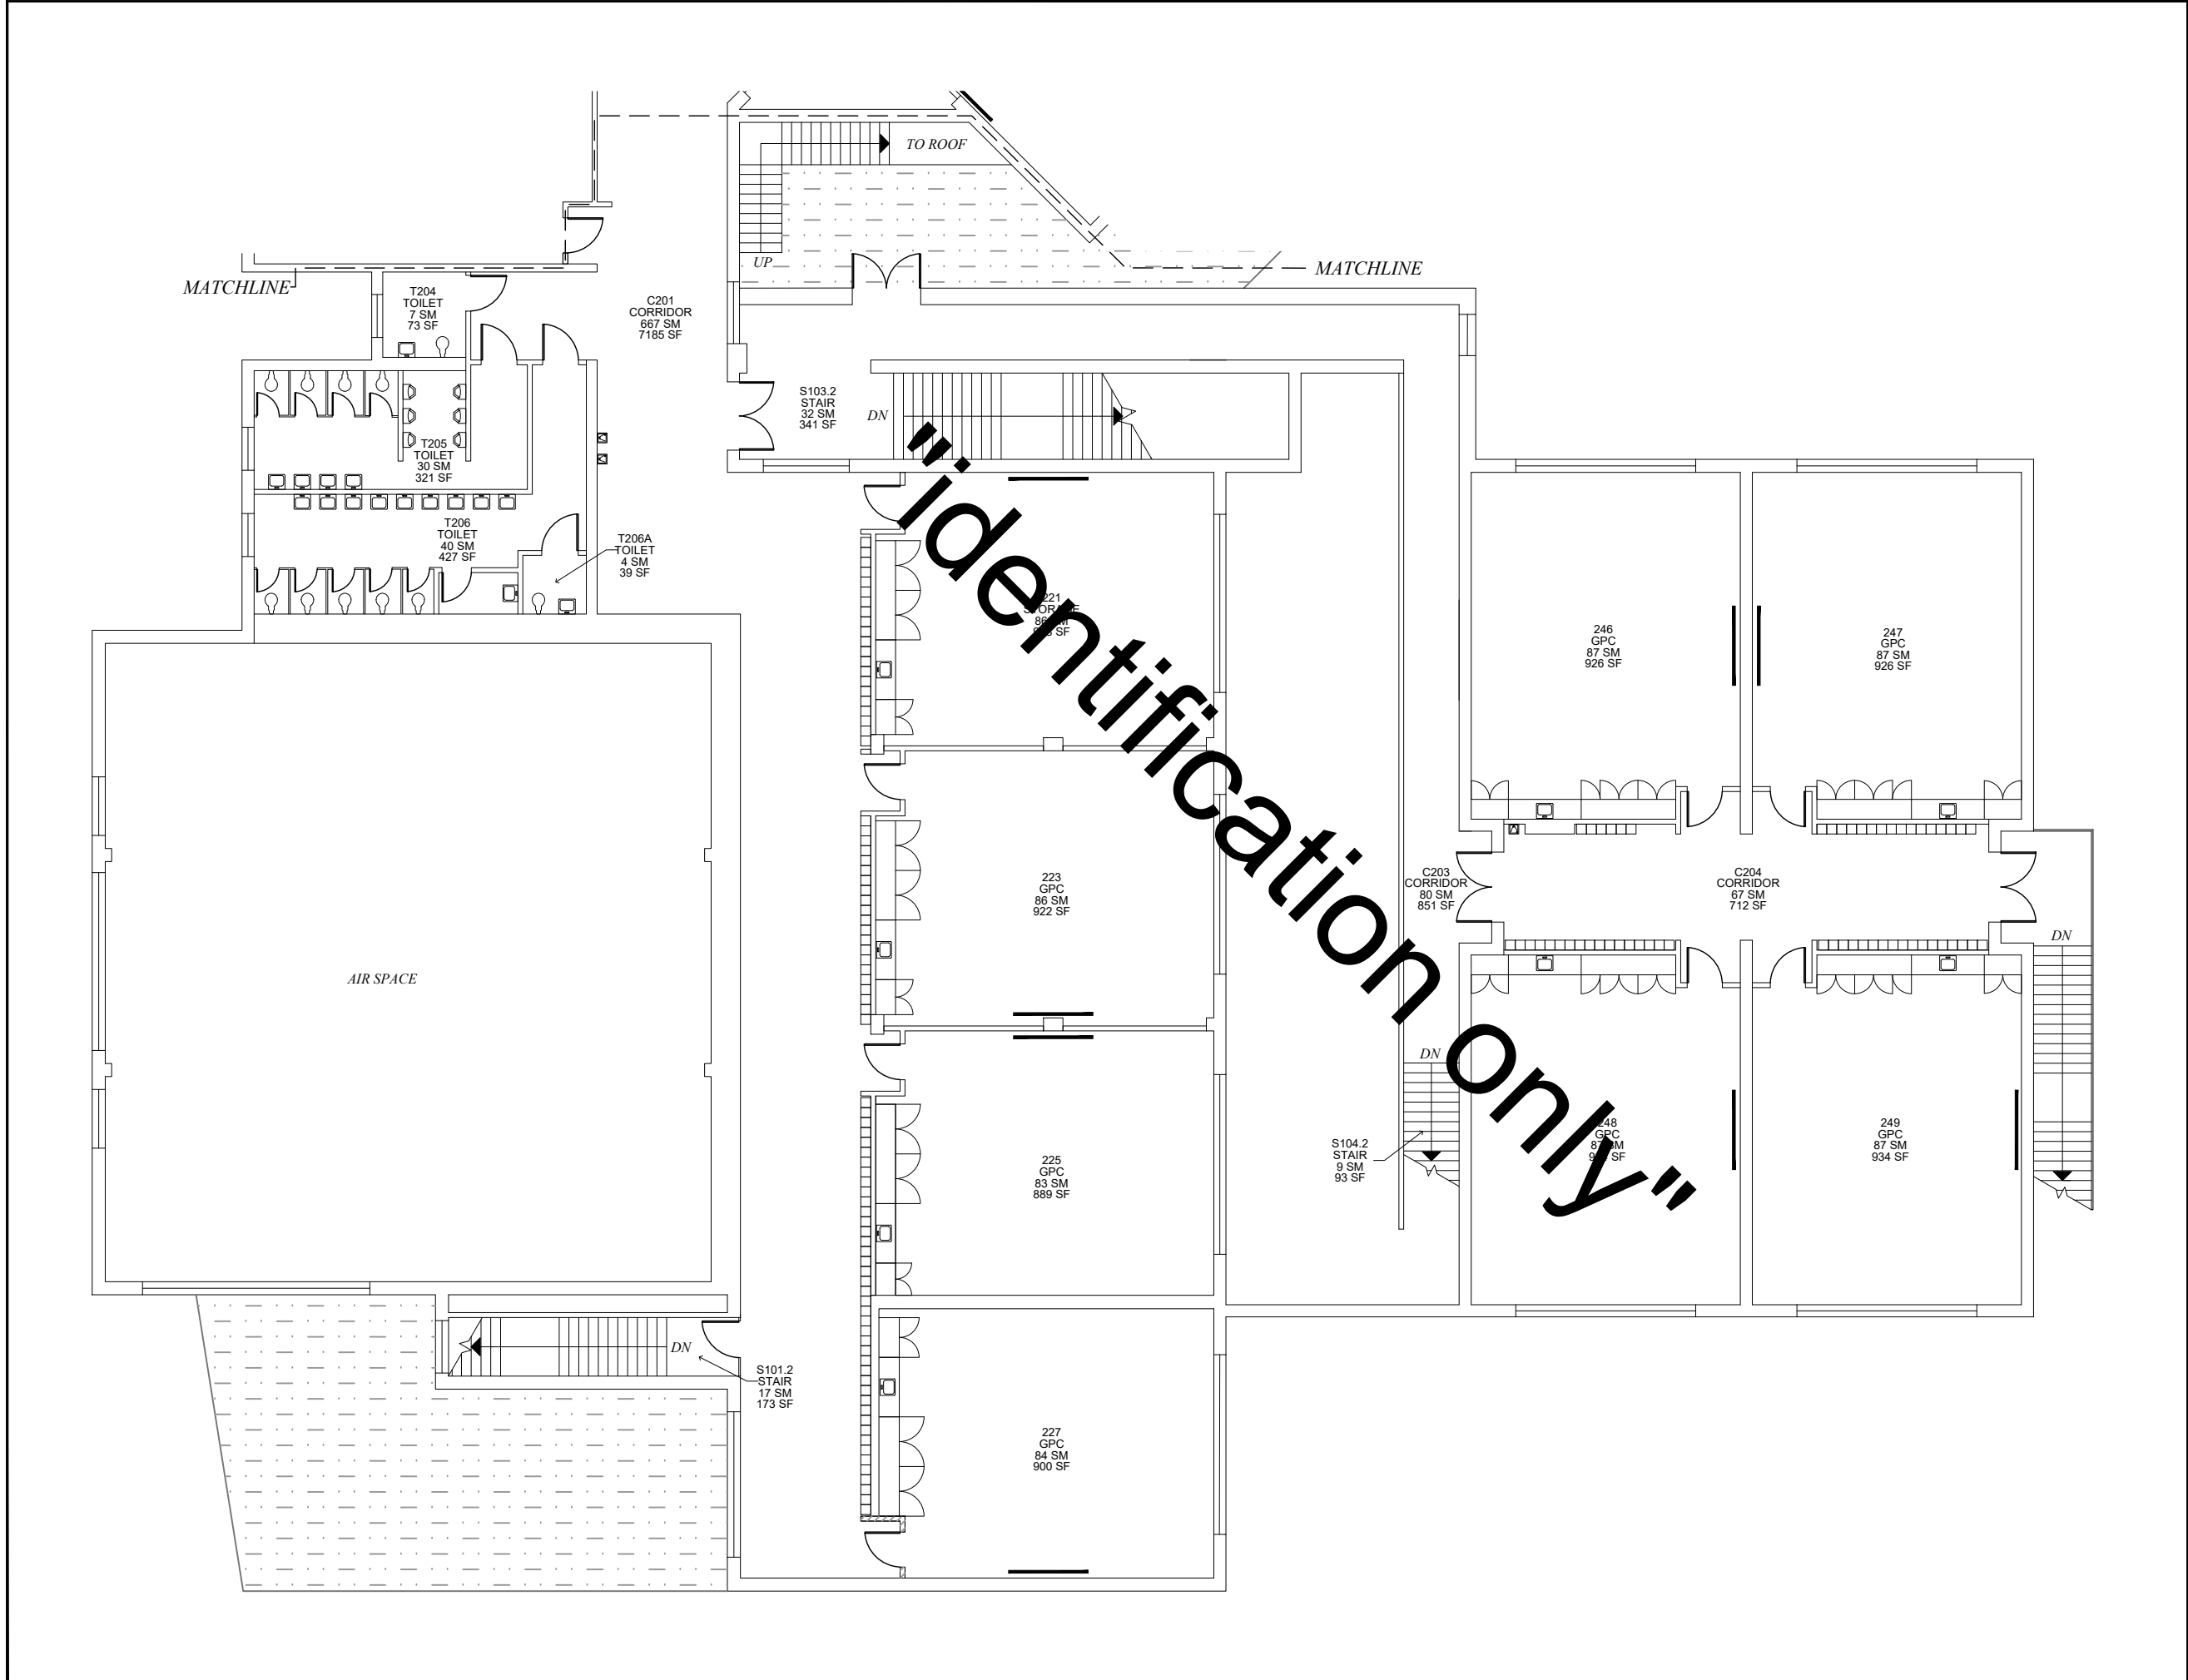

DOOR

SLIDING DOOR

ACCORDION PARTITION

STACK OR FOLDING PARTITION

WINDOW/GLAZING

HIGH WINDOW

SKYLIGHT

STOOP/STEP UP

STAIR

RAMP

ACCESS LADDER

COLD STORAGE

AREA CALCULATED @ 50 %

SLOPING ROOF

DRINKING FOUNTAIN

LAVATORY

SINK

TOILET

URINAL

LOCKER

LAN DISTRIBUTION FRAME

VENT HOOD

WALL SHELVING

UPPER CABINET

BASE CABINET

TEACHER CABINET

MATCHLINE

FLAT ROOF

TITLEBLOCK LEGEND

SHEET NAME:

BLDG #_FLOOR # (# IN SERIES)

KEY PLAN

NTS

NORTH

0 2 4 8 16 FT

dodea

DEPARTMENT OF DEFENSE EDUCATION ACTIVITY

FACILITY UTILIZATION SURVEY

NAPLES

ELEMENTARY SCHOOL

BUILDING NUMBER: 2057

COUNTRY: ITALY

INSTALLATION: NAVAL SUPPORT ACTIVITY NAPLES

SITE: SUPPORT SITE

REGION-DISTRICT: DODEA EUROPE SOUTH

DoDAAC Number:

HE5549 / HE5605

Floor:

LEVEL 2

Survey Date:


JANUARY 2020

Sheet Name:

2057_2 (3)

Sheet Seq:

15 of 17

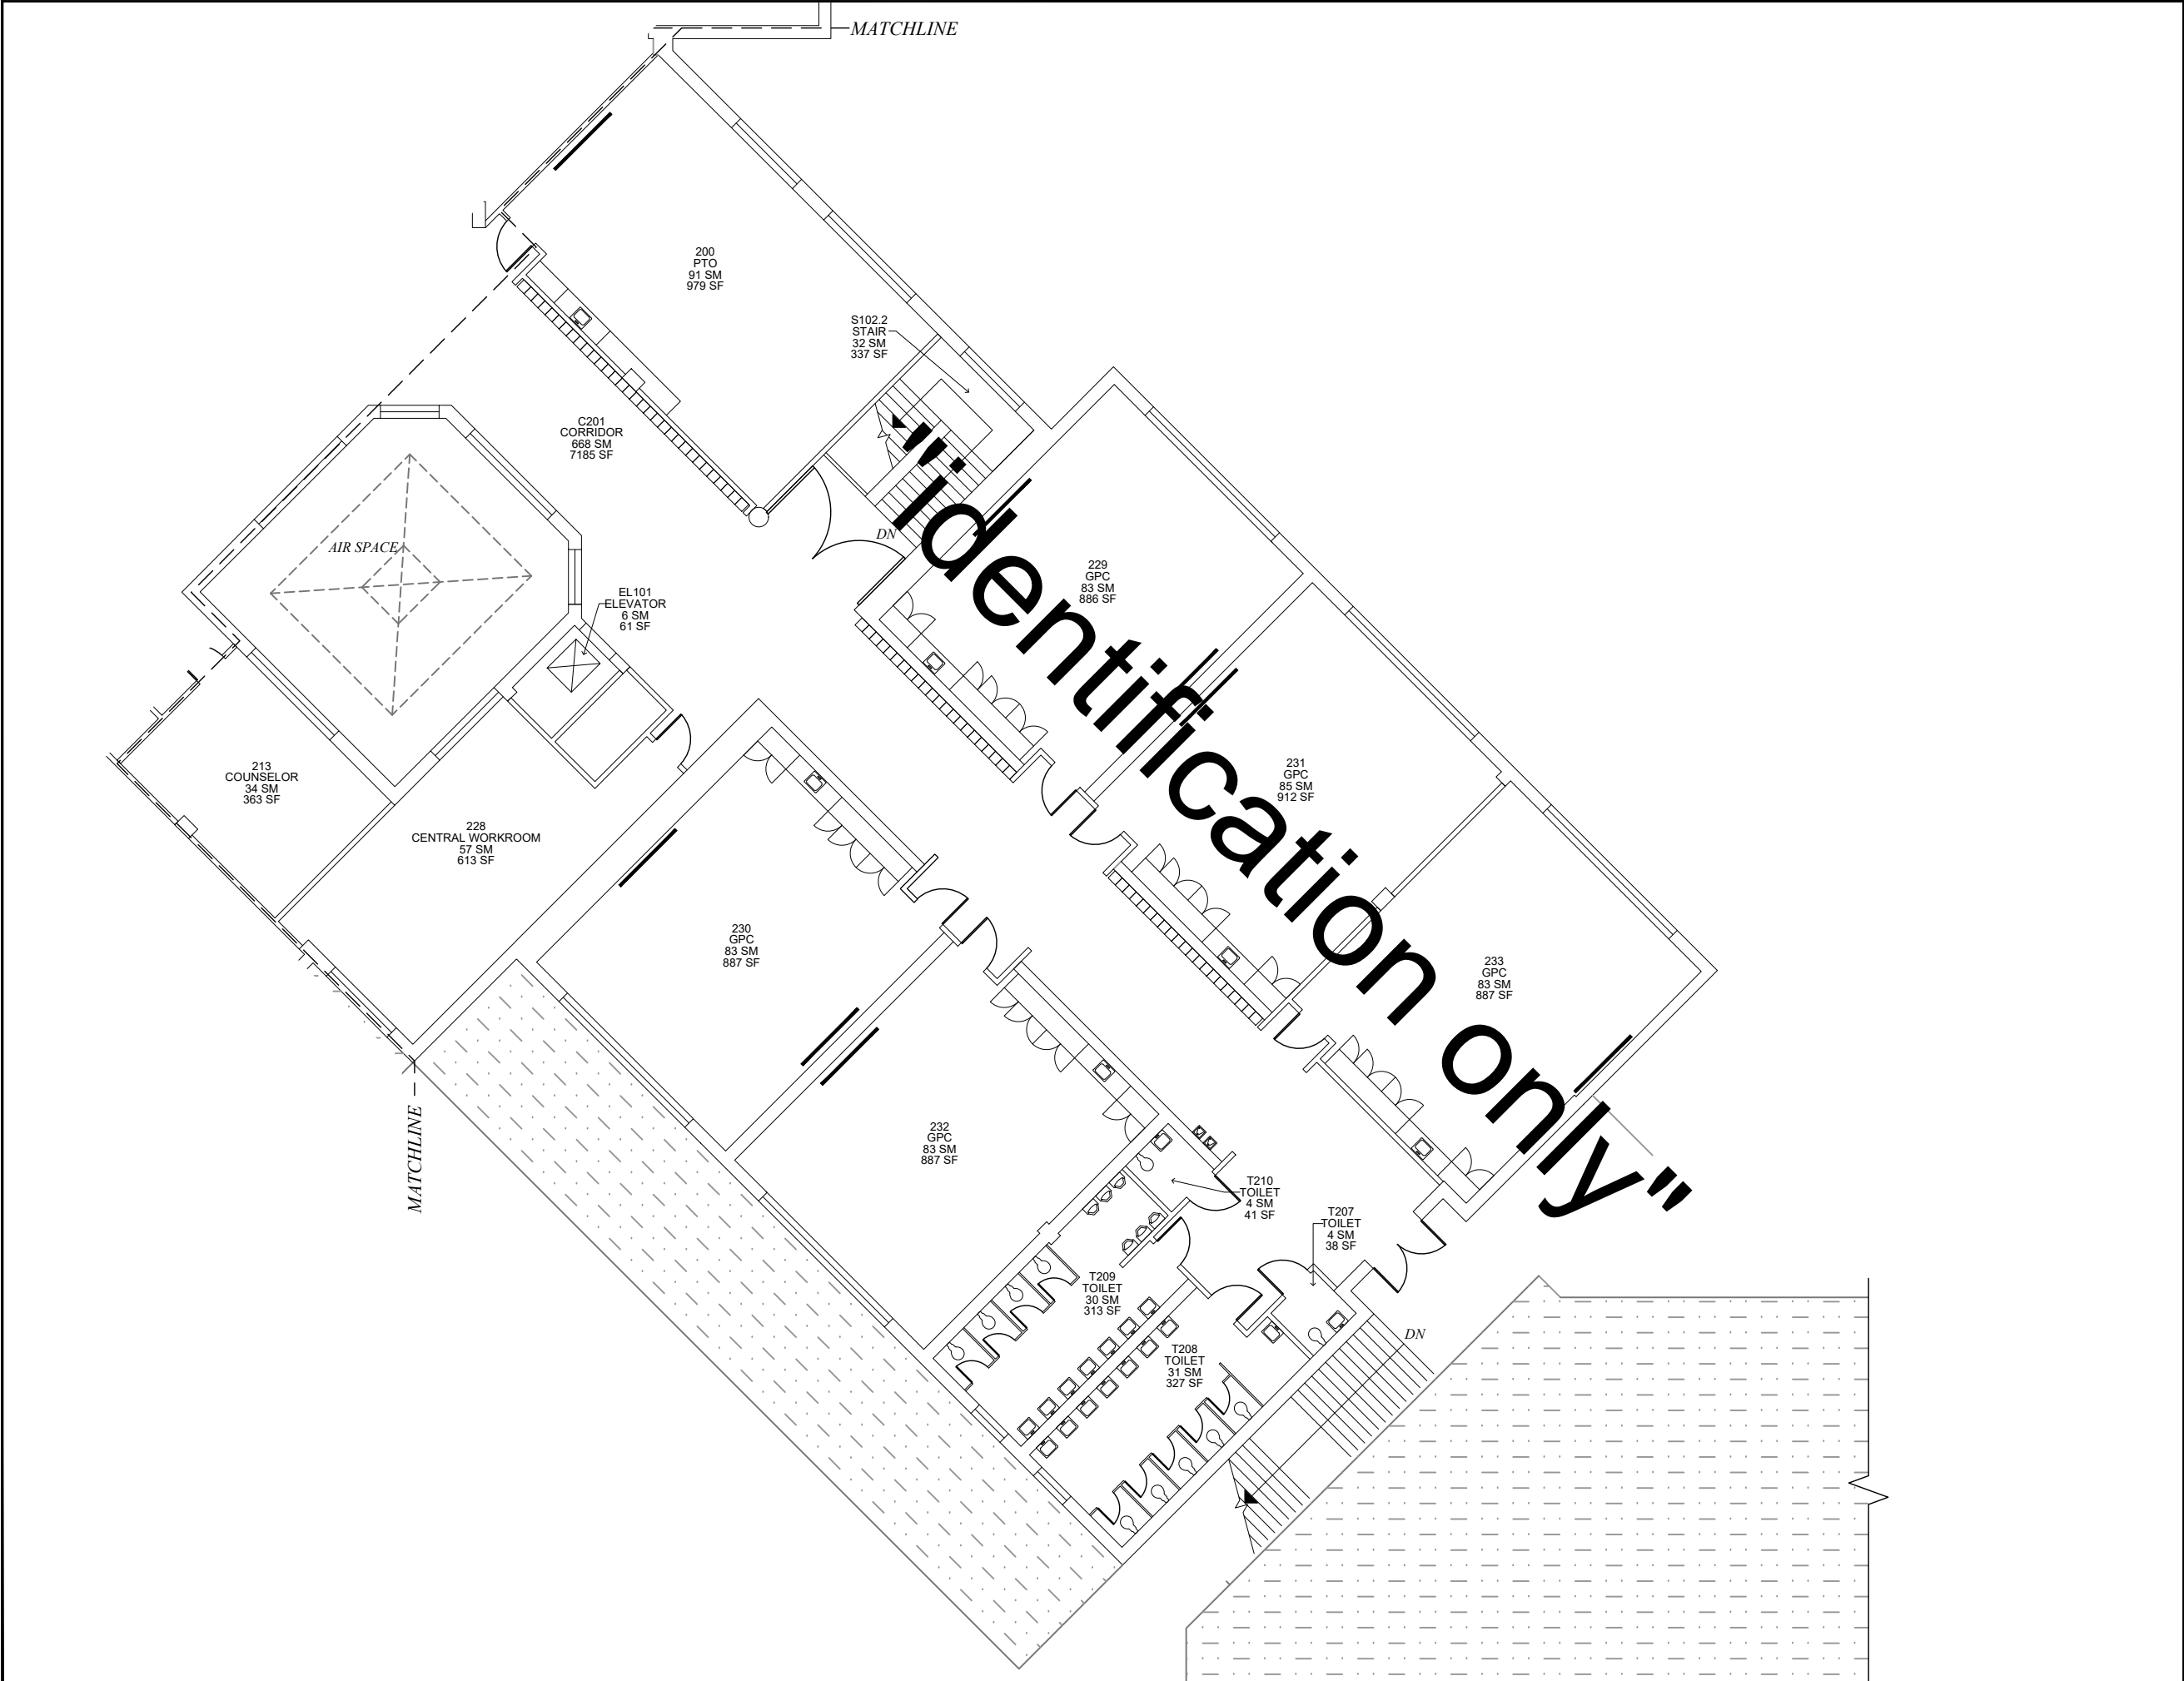

SYMBOL LEGEND

DOOR	DRINKING FOUNTAIN
SLIDING DOOR	LAVATORY
ACCORDION PARTITION	SINK
STACK OR FOLDING PARTITION	TOILET
WINDOW/GLAZING	URINAL
HIGH WINDOW	LOCKER
SKYLIGHT	LAN DISTRIBUTION FRAME
STOOP/STEP UP	VENT HOOD
STAIR	WALL SHELVING
RAMP	UPPER CABINET
ACCESS LADDER	BASE CABINET
COLD STORAGE	TEACHER CABINET
AREA CALCULATED @ 50 %	MATCHLINE
SLOPING ROOF	FLAT ROOF

TITLEBLOCK LEGEND

SHEET NAME:	BLDG #_ FLOOR # (# IN SERIES)

KEY PLAN

NTS

2057

X2057A

NORTH

Updated By: AA

FUS Review: MRS

100% Submittal Date: 01 MAY 2020

0 2 4 8 16 FT

dodea

DEPARTMENT OF DEFENSE EDUCATION ACTIVITY

FACILITY UTILIZATION SURVEY

NAPLES

ELEMENTARY SCHOOL

BUILDING NUMBER: 2057

COUNTRY: ITALY

INSTALLATION: NAVAL SUPPORT ACTIVITY NAPLES

SITE: SUPPORT SITE

REGION-DISTRICT: DODEA EUROPE SOUTH


DoDAAC Number: HE5549 / HE5605

Floor: LEVEL 2

Survey Date: JANUARY 2020


Sheet Name: 2057_2 (4)

Sheet Seq: 16 of 17

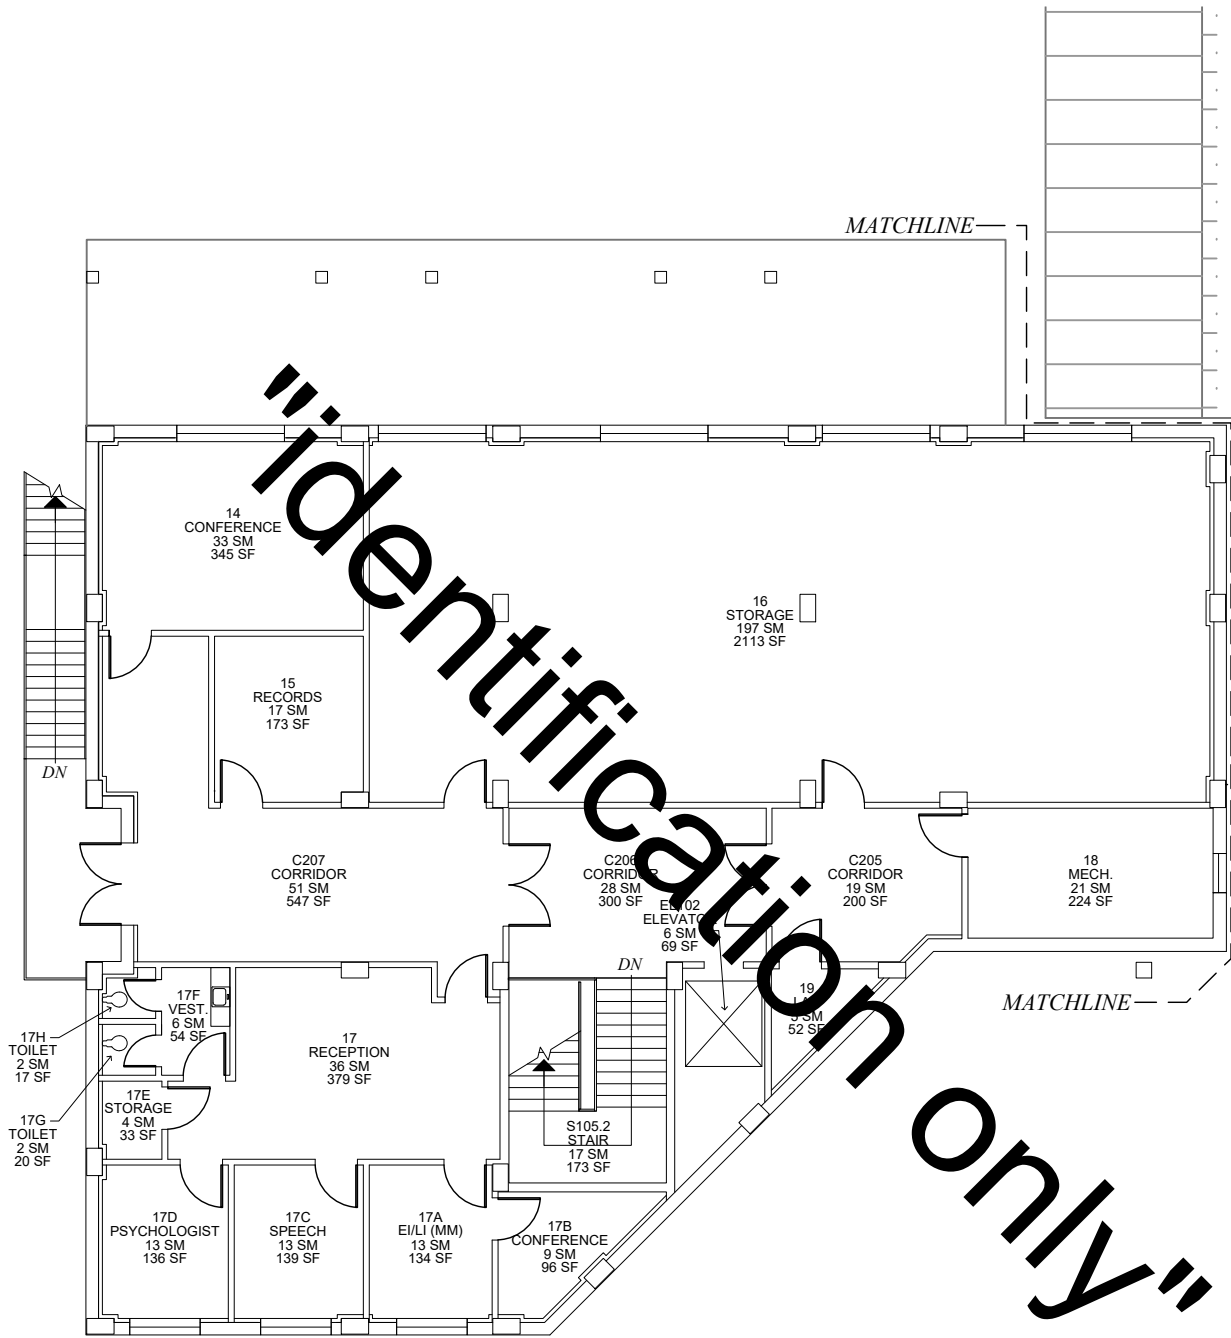

SYMBOL LEGEND	
	DOOR
	DRINKING FOUNTAIN
	SLIDING DOOR
	LAVATORY
	ACCORDION PARTITION
	SINK
	STACK OR FOLDING PARTITION
	TOILET
	WINDOW/GLAZING
	URINAL
	HIGH WINDOW
	LOCKER
	SKYLIGHT
	LAN DISTRIBUTION FRAME
	STOOP/STEP UP
	VENT HOOD
	STAIR
	WALL SHELVING
	RAMP
	UPPER CABINET
	ACCESS LADDER
	BASE CABINET
	COLD STORAGE
	TEACHER CABINET
	AREA CALCULATED @ 50 %
	MATCHLINE
	SLOPING ROOF
	FLAT ROOF

TITLEBLOCK LEGEND	
SHEET NAME:	BLDG #_FLOOR # (# IN SERIES)

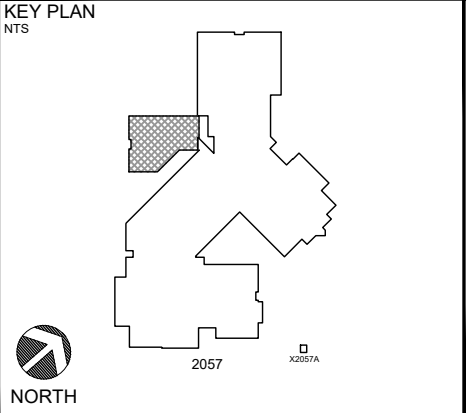

Updated By:	FUS Review:	100% Submittal Date:
AA	MRS	01 MAY 2020
0 2 4 8 16 FT		

dodea
DEPARTMENT OF DEFENSE EDUCATION ACTIVITY
FACILITY UTILIZATION SURVEY

NAPLES ELEMENTARY SCHOOL BUILDING NUMBER: 2057 COUNTRY: ITALY INSTALLATION: NAVAL SUPPORT ACTIVITY NAPLES SITE: SUPPORT SITE REGION-DISTRICT: DODEA EUROPE SOUTH		
DoDAAC Number: HE5549 / HE5605	Floor: LEVEL 2	Survey Date: JANUARY 2020
Sheet Name: 2057_2 (5)	Sheet Seq: 17 of 17	