



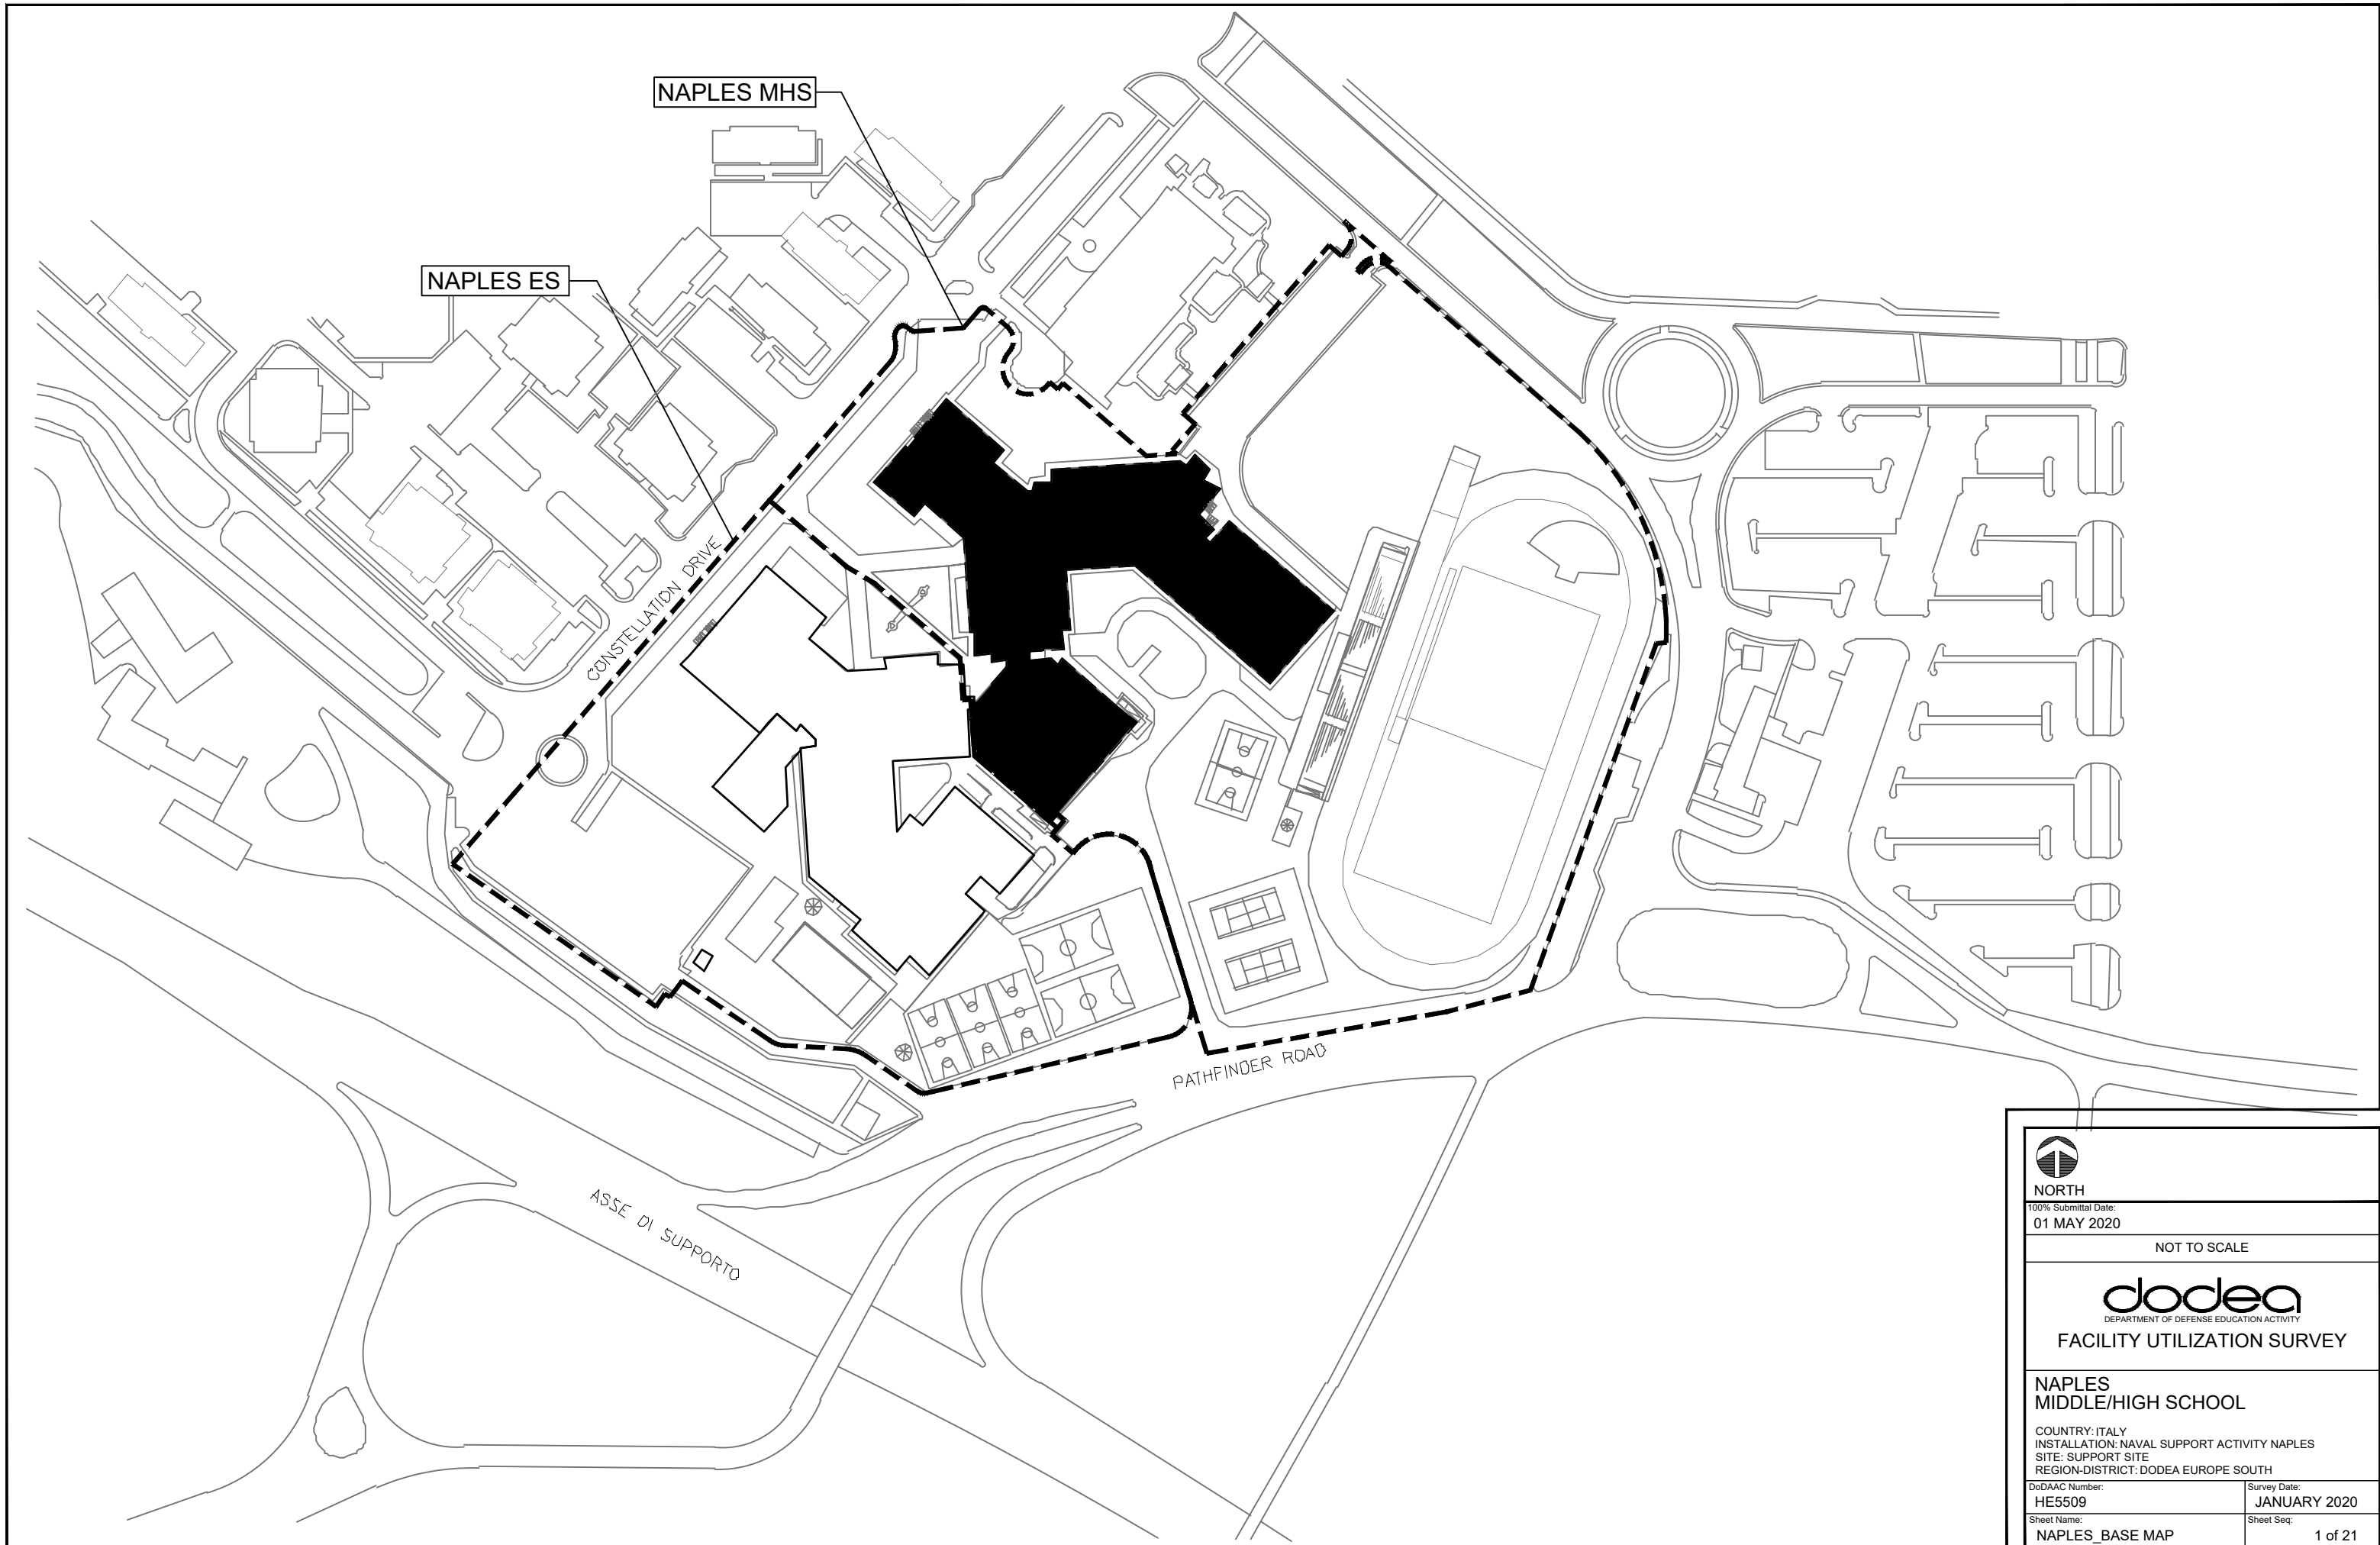

 NORTH	
100% Submittal Date: 01 MAY 2020	
NOT TO SCALE	
 DEPARTMENT OF DEFENSE EDUCATION ACTIVITY FACILITY UTILIZATION SURVEY	
NAPLES MIDDLE/HIGH SCHOOL	
COUNTRY: ITALY INSTALLATION: NAVAL SUPPORT ACTIVITY NAPLES SITE: SUPPORT SITE REGION-DISTRICT: DODEA EUROPE SOUTH	
DoDAAC Number: HE5509	Survey Date: JANUARY 2020
Sheet Name: NAPLES_BASE MAP	Sheet Seq: 1 of 21

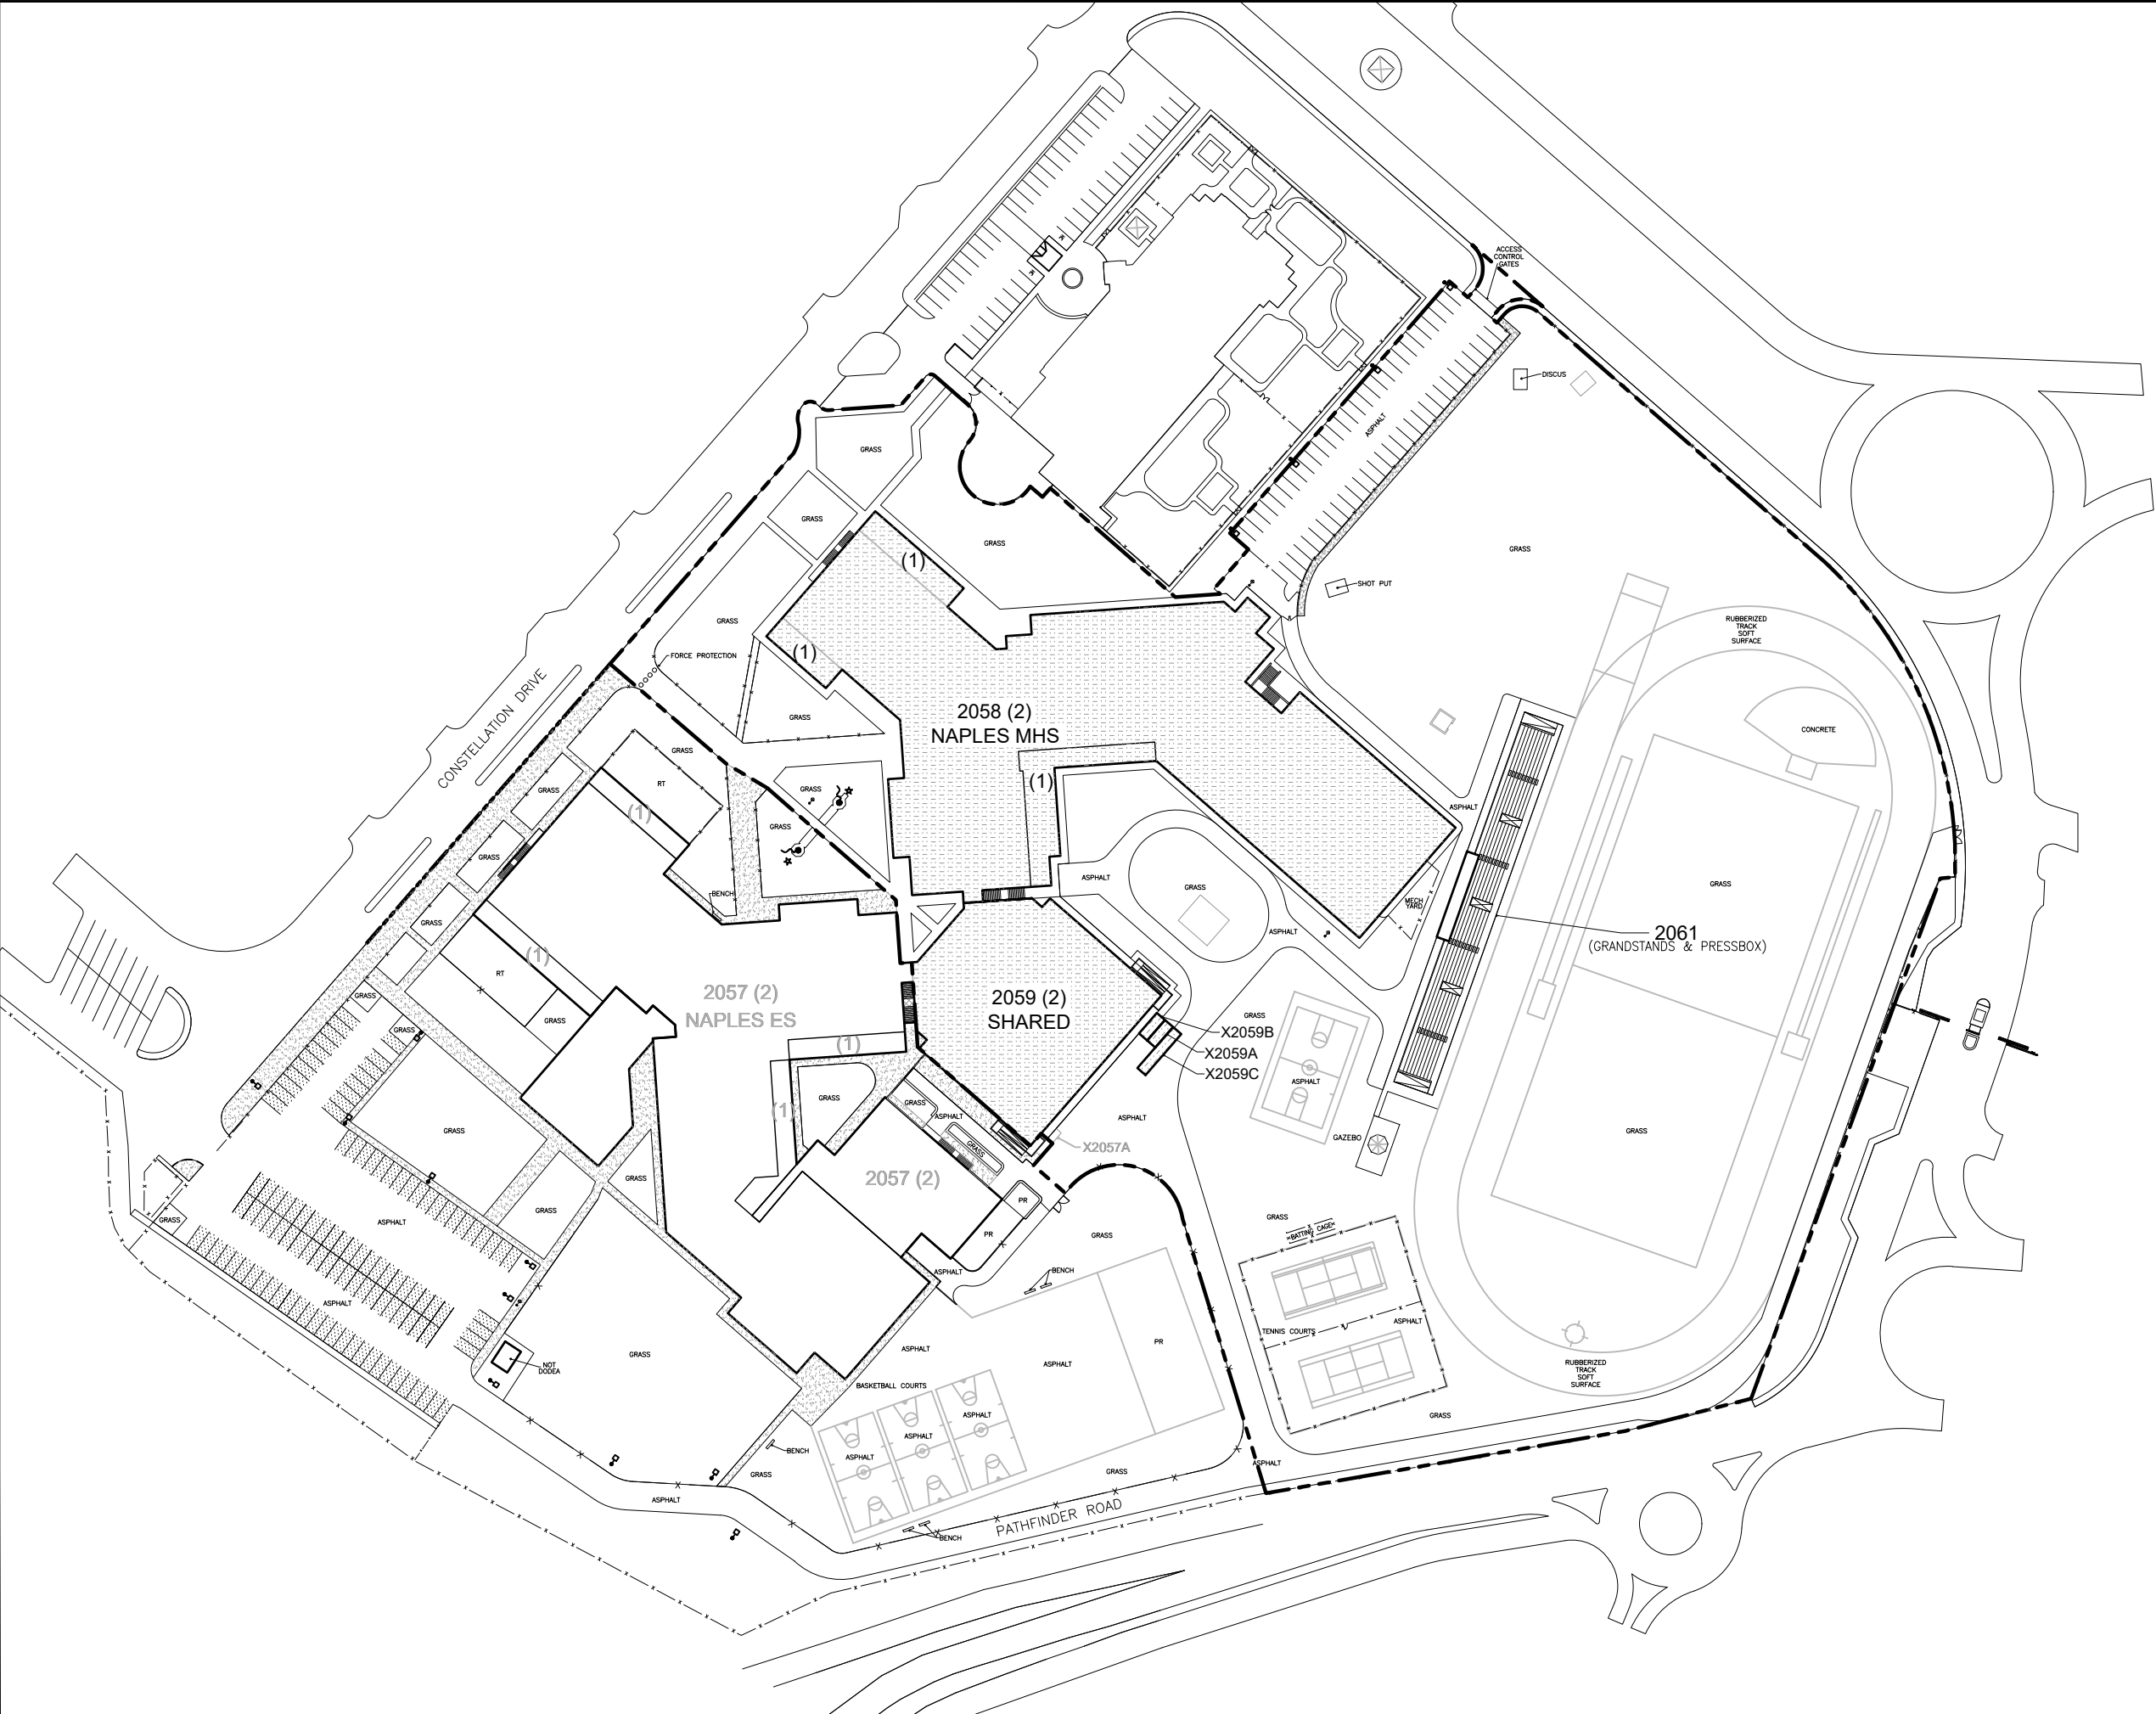


SYMBOL LEGEND	
	BASKETBALL GOAL
	STADIUM LIGHT
	SIGN
	FOOTBALL GOAL
	BASEBALL BACKSTOP
	PARKING AREA
	FLAT ROOF
	SLOPE
	COVERED WALKWAY
	SLOPING ROOF
	AREA LIGHT
	FLAG POLE
	MONUMENT
	SOCCER GOAL
	MAIN ENTRY
	CONCRETE
	PLAYGROUND
	FIRE HYDRANT
PROPERTY LINE (APPROX. 47,743 SM) (APPROX. 11.80 AC)	
FENCE LINE	

LEGEND	
PLAYGROUND SURFACING	
WC - WOOD CHIPS	PR - POURED RUBBER M - MULCH
SRT - SHREDDED RUBBER TIRES	S - SAND
PG - PEA GRAVEL	RT - RUBBER TILES

BUILDING LABEL	BLDG # (# OF FLOORS)
----------------	----------------------

KEY PLAN
NTS

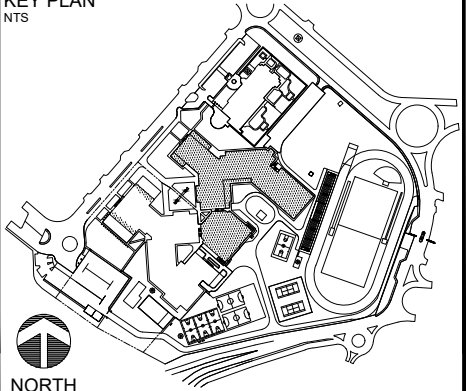

Updated By: AA	FUS Review: MRS	100% Submittal Date: 01 MAY 2020
-------------------	--------------------	-------------------------------------


NOT TO SCALE

dodea
DEPARTMENT OF DEFENSE EDUCATION ACTIVITY
FACILITY UTILIZATION SURVEY

NAPLES MIDDLE/HIGH SCHOOL

COUNTRY: ITALY
INSTALLATION: NAVAL SUPPORT ACTIVITY NAPLES
SITE: SUPPORT SITE
REGION-DISTRICT: DODEA EUROPE SOUTH

DoDAAC Number: HE5509	Survey Date: JANUARY 2020
Sheet Name: NAPLES MHS_OVERALL	Sheet Seq: 2 of 21

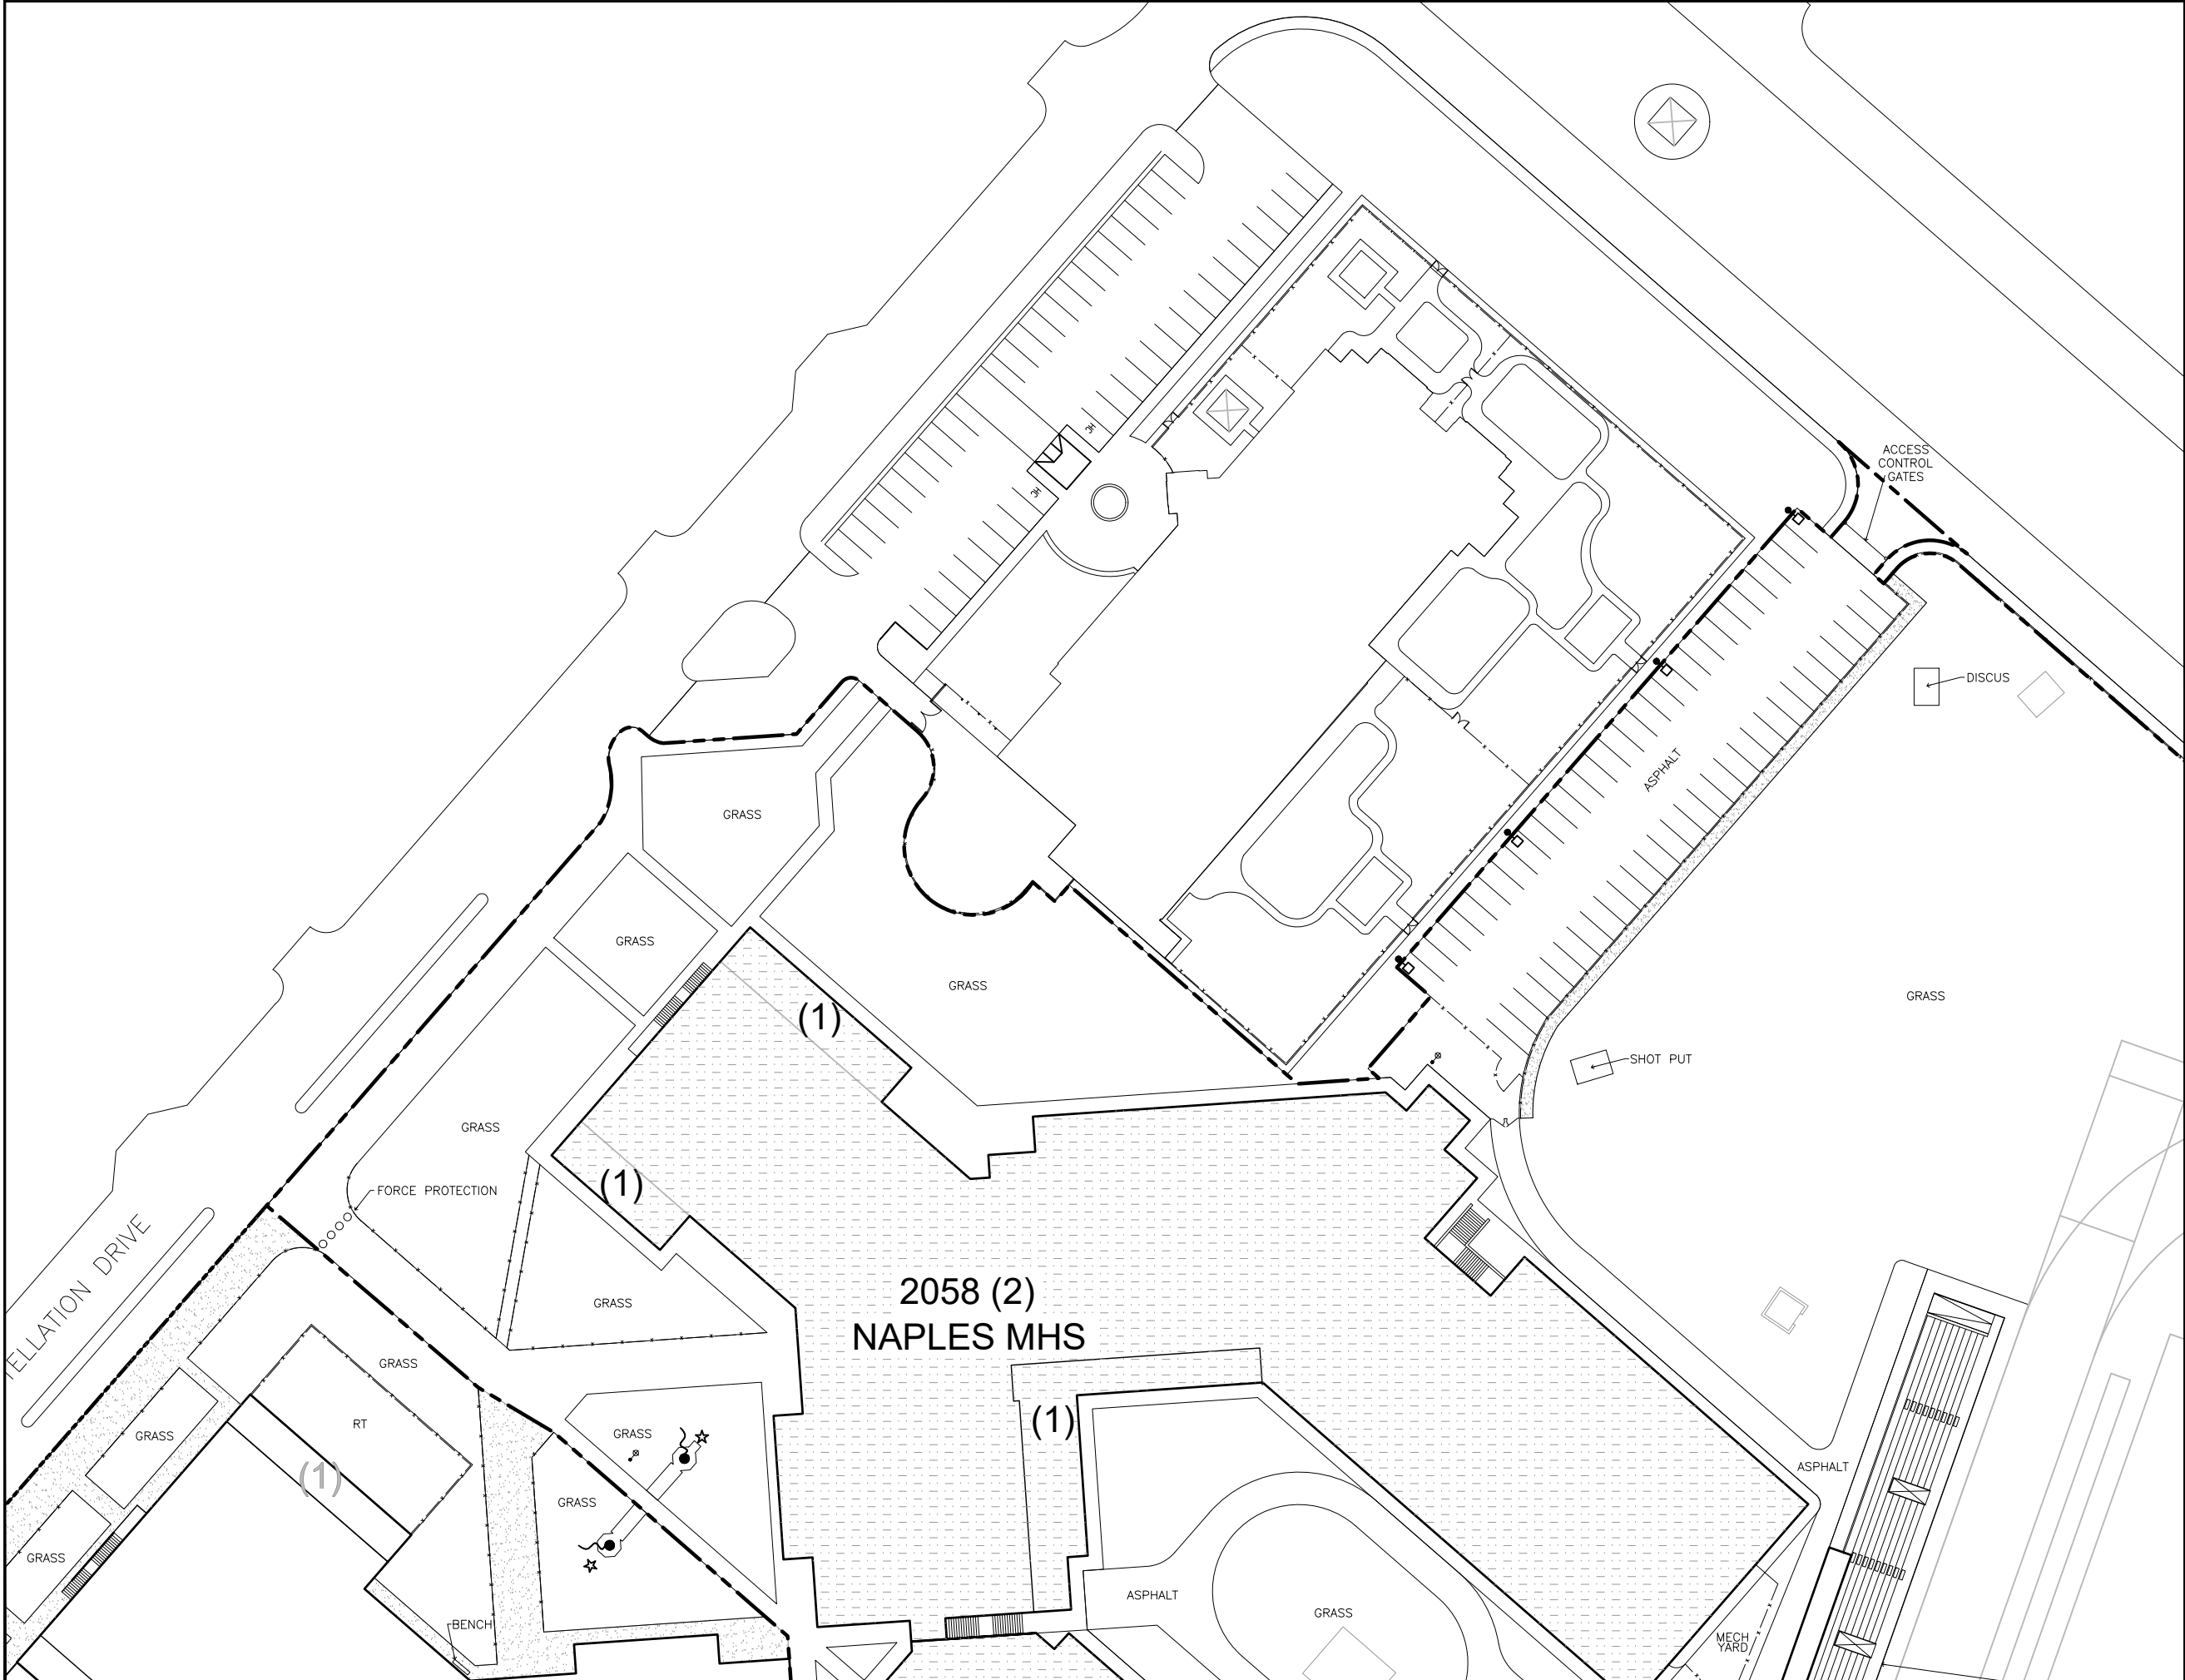


SYMBOL LEGEND	
	BASKETBALL GOAL
	STADIUM LIGHT
	SIGN
	FOOTBALL GOAL
	BASEBALL BACKSTOP
	PARKING AREA
	FLAT ROOF
	SLOPE
	COVERED WALKWAY
	SLOPING ROOF
	AREA LIGHT
	FLAG POLE
	MONUMENT
	SOCCER GOAL
	MAIN ENTRY
	CONCRETE
	PLAYGROUND
	FIRE HYDRANT
PROPERTY LINE (APPROX. 47,743 SM) (APPROX. 11.80 AC)	
FENCE LINE	

LEGEND	
PLAYGROUND SURFACING	
WC - WOOD CHIPS	PR - POURED RUBBER
M - MULCH	
SRT - SHREDDED RUBBER TIRES	S - SAND
PG - PEA GRAVEL	RT - RUBBER TILES

BUILDING LABEL	BLDG # (# OF FLOORS)
----------------	----------------------


KEY PLAN
NTS

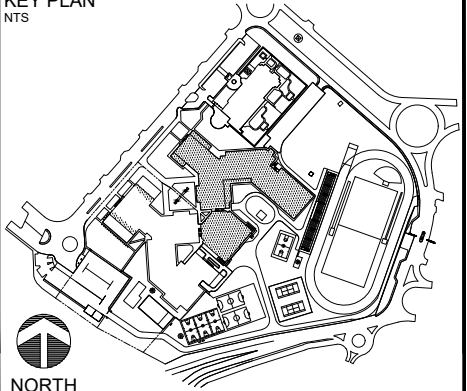

Updated By: AA	FUS Review: MRS	100% Submittal Date: 01 MAY 2020


DEPARTMENT OF DEFENSE EDUCATION ACTIVITY
FACILITY UTILIZATION SURVEY

NAPLES MIDDLE/HIGH SCHOOL	
COUNTRY: ITALY INSTALLATION: NAVAL SUPPORT ACTIVITY NAPLES SITE: SUPPORT SITE REGION-DISTRICT: DODEA EUROPE SOUTH	
DoDAAC Number: HE5509	Survey Date: JANUARY 2020
Sheet Name: NAPLES MHS 32ND SC (1)	Sheet Seq: 3 of 21

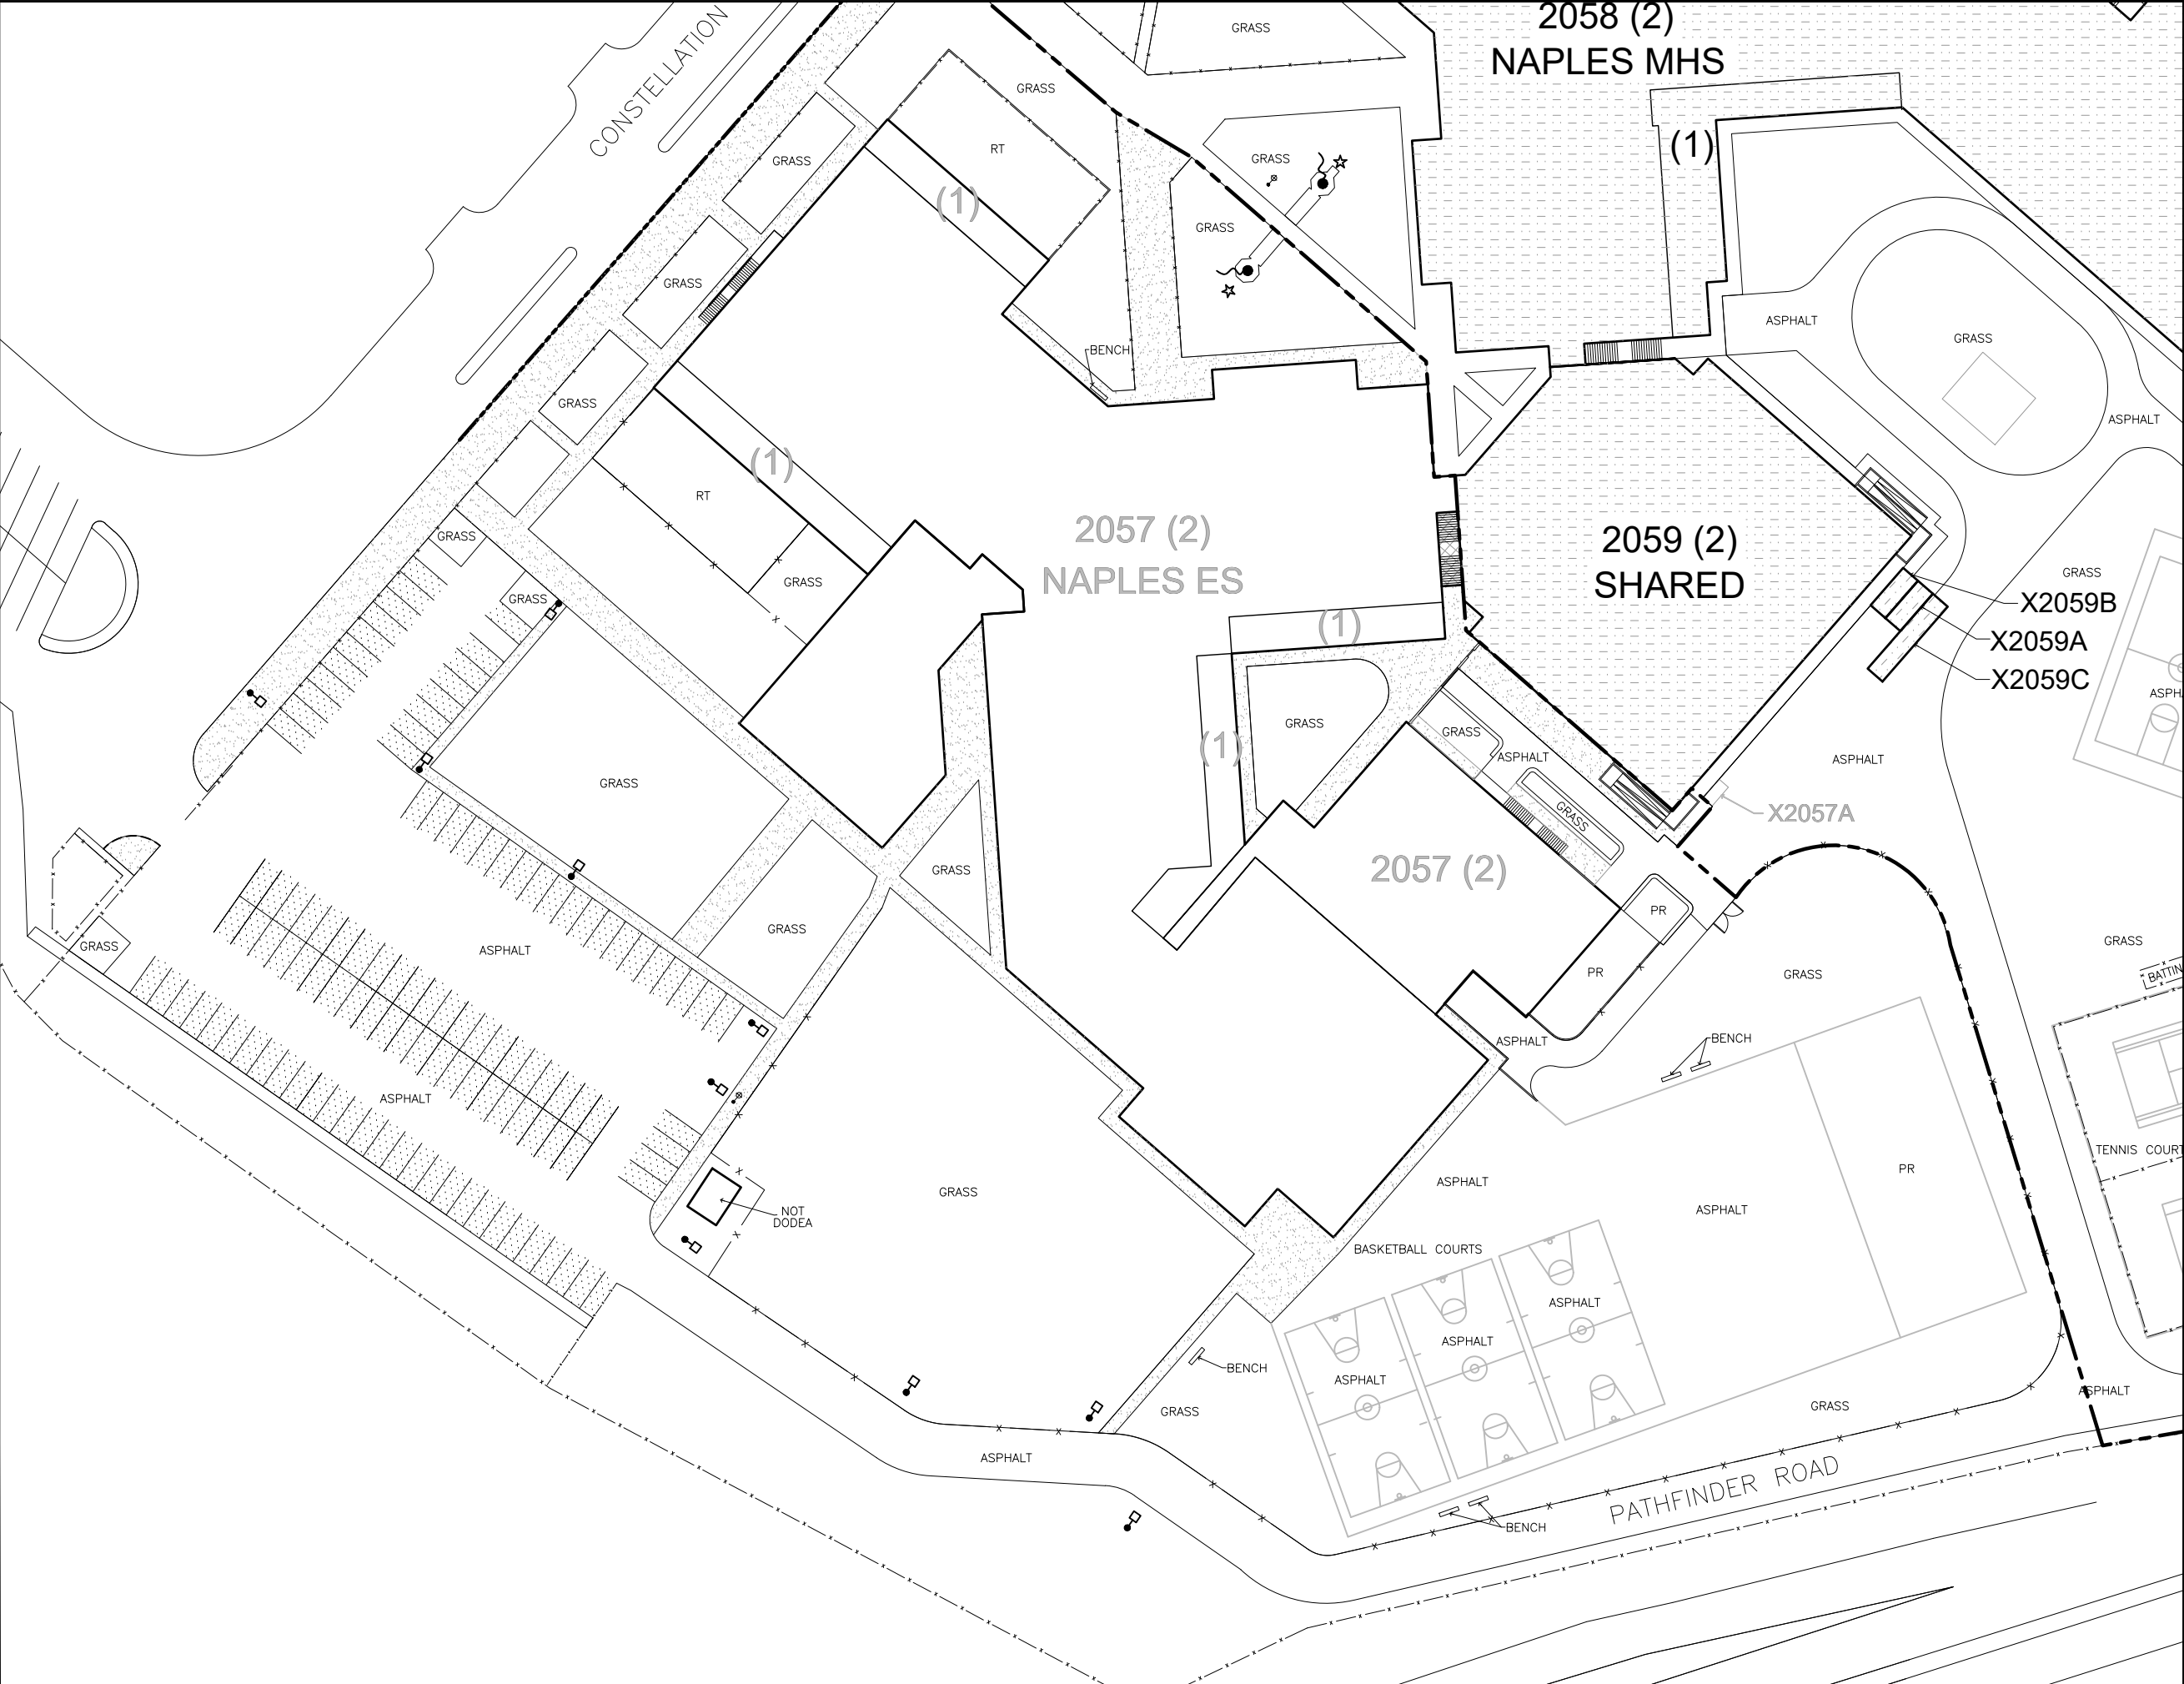

SYMBOL LEGEND	
	BASKETBALL GOAL
	STADIUM LIGHT
	SIGN
	FOOTBALL GOAL
	BASEBALL BACKSTOP
	PARKING AREA
	FLAT ROOF
	SLOPE
	COVERED WALKWAY
	SLOPING ROOF
	AREA LIGHT
	FLAG POLE
	MONUMENT
	SOCCER GOAL
	MAIN ENTRY
	CONCRETE
	PLAYGROUND
	FIRE HYDRANT
PROPERTY LINE (APPROX. 47,743 SM) (APPROX. 11.80 AC)	
FENCE LINE	

LEGEND	
PLAYGROUND SURFACING	
WC - WOOD CHIPS	PR - POURED RUBBER
M - MULCH	SRT - SHREDDED RUBBER TIRES
S - SAND	PG - PEA GRAVEL
RT - RUBBER TILES	
BUILDING LABEL	BLDG # (# OF FLOORS)

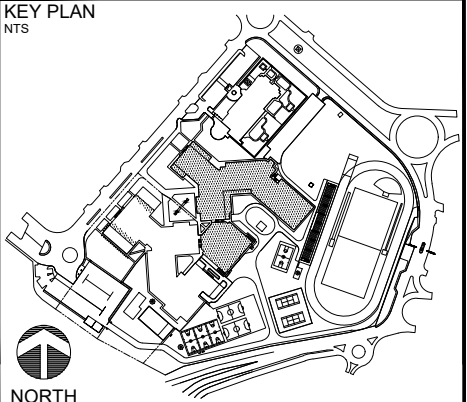

Updated By:	FUS Review:	100% Submittal Date:
AA	MRS	01 MAY 2020

dodea
DEPARTMENT OF DEFENSE EDUCATION ACTIVITY
FACILITY UTILIZATION SURVEY

NAPLES MIDDLE/HIGH SCHOOL	
COUNTRY: ITALY INSTALLATION: NAVAL SUPPORT ACTIVITY NAPLES SITE: SUPPORT SITE REGION-DISTRICT: DODEA EUROPE SOUTH	
DoDAAC Number: HE5509	Survey Date: JANUARY 2020
Sheet Name: NAPLES MHS 32ND SC (3)	Sheet Seq: 5 of 21



BUILDING 2058 - FIRST FLOOR

GSF CALCULATIONS


BUILDING 2058 - SECOND FLOOR

Building 2058	
Floor 1	67,989
Floor 2	42,837
Total Area (SF)	109,706
50% Area (SF)	1,401
Gross Area (SF)	111,107

Building 2059	
Floor 1	20,930
Total Area (SF)	20,930
50% Area (SF)	0
Gross Area (SF)	20,930

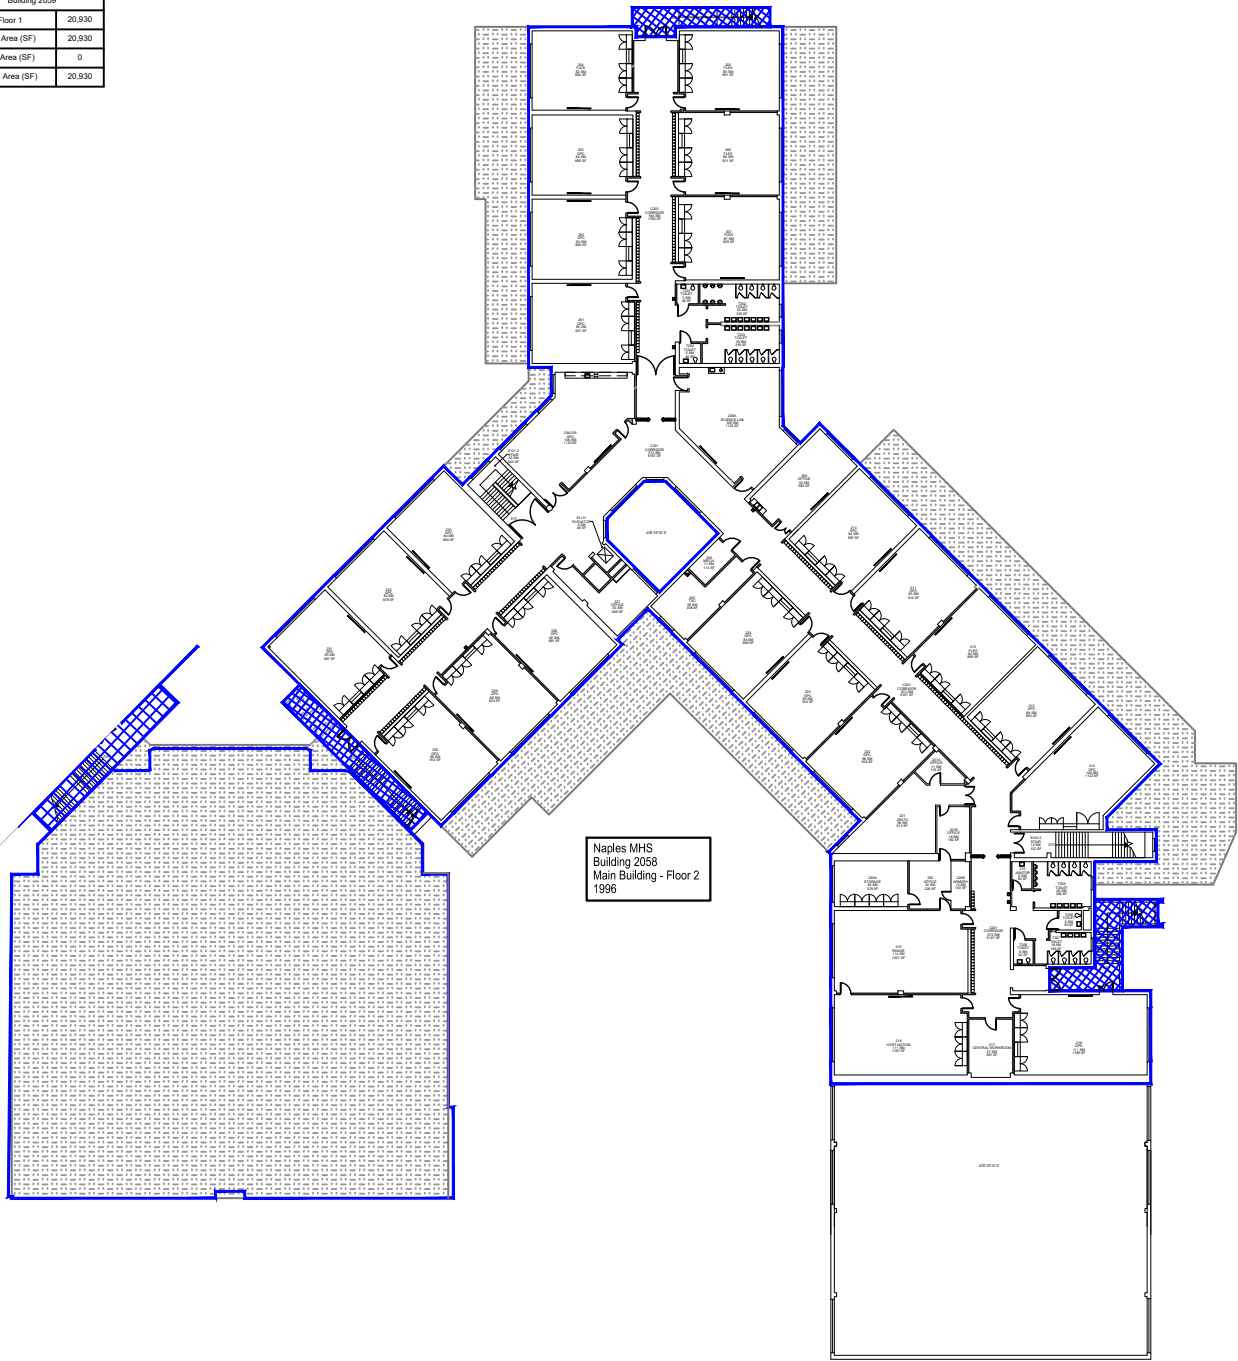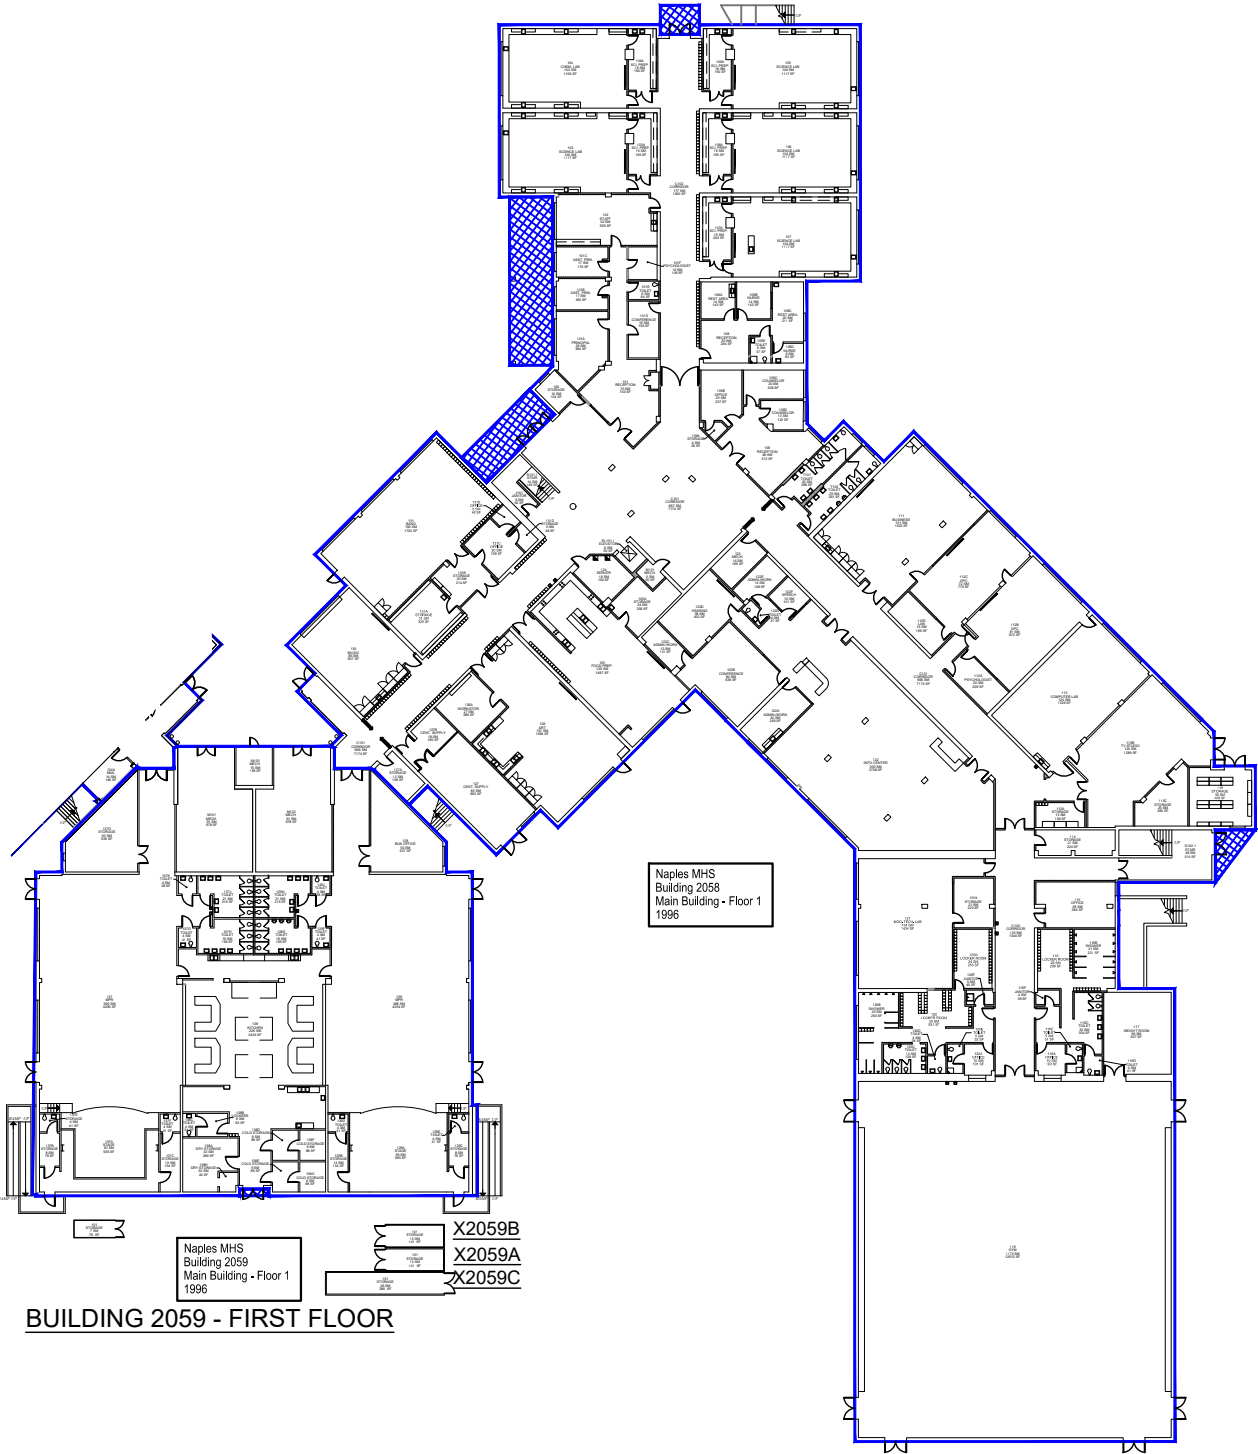

BUILDING 2059 - FIRST FLOOR

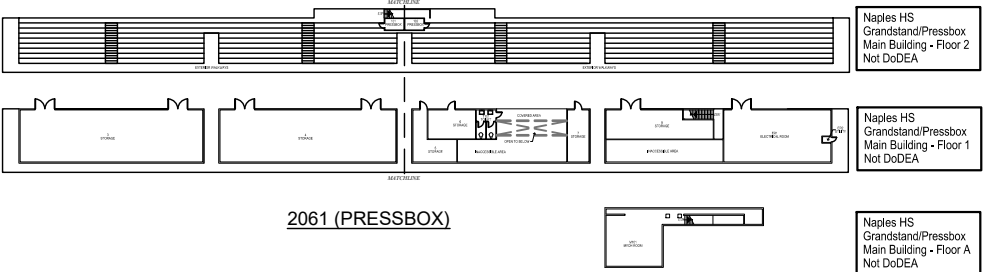

NOTE 1: APPROXIMATELY 50% OF BUILDING 2059 (MPR) IS UTILIZED BY NAPLES ELEMENTARY SCHOOL.
NOTE 2: GSF CALCULATIONS BASED ON ARMY RPI DoA PAMPHLET 415-28.

DOOR

SLIDING DOOR

ACCORDION PARTITION

STACK OR FOLDING PARTITION

WINDOW/GLAZING

HIGH WINDOW

SKYLIGHT

STOOP/STEP UP

STAIR

RAMP

ACCESS LADDER

COLD STORAGE

AREA CALCULATED @ 50 %

SLOPING ROOF

DRINKING FOUNTAIN

LAVATORY

SINK

TOILET

URINAL

LOCKER

LAN DISTRIBUTION FRAME

VENT HOOD

WALL SHELVING

UPPER CABINET

BASE CABINET

TEACHER CABINET

MATCHLINE

FLAT ROOF

TITLEBLOCK LEGEND

SHEET NAME:

BLDG # FLOOR # (# IN SERIES)

KEY PLAN

NTS

NORTH

Updated By: AA

FUS Review: MRS

100% Submittal Date: 01 APRIL 2020

NOT TO SCALE

dodea

DEPARTMENT OF DEFENSE EDUCATION ACTIVITY

FACILITY UTILIZATION SURVEY

NAPLES

MIDDLE/HIGH SCHOOL

BUILDING NUMBER: 2058, 2059, X2059A-C, 2061S/PRESSBOX

COUNTRY: ITALY

INSTALLATION: NAVAL SUPPORT ACTIVITY NAPLES

SITE: SUPPORT SITE

REGION-DISTRICT: DODEA EUROPE SOUTH

DoDAAC Number: HE5509

Floor: LEVEL 1, 2

Survey Date: JANUARY 2020

Sheet Name: GSF_1 (1)

Sheet Seq: 6 of 21


SYMBOL LEGEND

 DOOR	 DRINKING FOUNTAIN
 SLIDING DOOR	 LAVATORY
 ACCORDION PARTITION	 SINK
 STACK OR FOLDING PARTITION	 TOILET
 WINDOW/GLAZING	 URINAL
 HIGH WINDOW	 LOCKER
 SKYLIGHT	 LAN DISTRIBUTION FRAME
 STOOP/STEP UP	 VENT HOOD
 STAIR	 WALL SHELVING
 RAMP	 UPPER CABINET
 ACCESS LADDER	 BASE CABINET
 COLD STORAGE	 TEACHER CABINET
 AREA CALCULATED @ 50 %	 MATCHLINE
 SLOPING ROOF	 FLAT ROOF

TITLEBLOCK LEGEND

SHEET NAME:	BLDG #_ FLOOR # (# IN SERIES)
-------------	-------------------------------

KEY PLAN
NTS

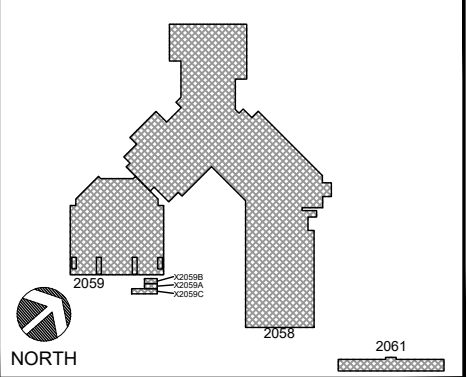



Updated By:	FUS Review:	100% Submittal Date:
AA	MRS	01 APRIL 2020


NOT TO SCALE

dodea
DEPARTMENT OF DEFENSE EDUCATION ACTIVITY
FACILITY UTILIZATION SURVEY

NAPLES MIDDLE/HIGH SCHOOL
BUILDING NUMBER: 2058, 2059, X2059A-C, 2061S/PRESSBOX
COUNTRY: ITALY
INSTALLATION: NAVAL SUPPORT ACTIVITY NAPLES
SITE: SUPPORT SITE
REGION-DISTRICT: DODEA EUROPE SOUTH


DoDAAC Number:	Floor:	Survey Date:
HE5509	LEVEL 1, 2	JANUARY 2020
Sheet Name:	Sheet Seq:	
KEY PLAN	8 of 21	

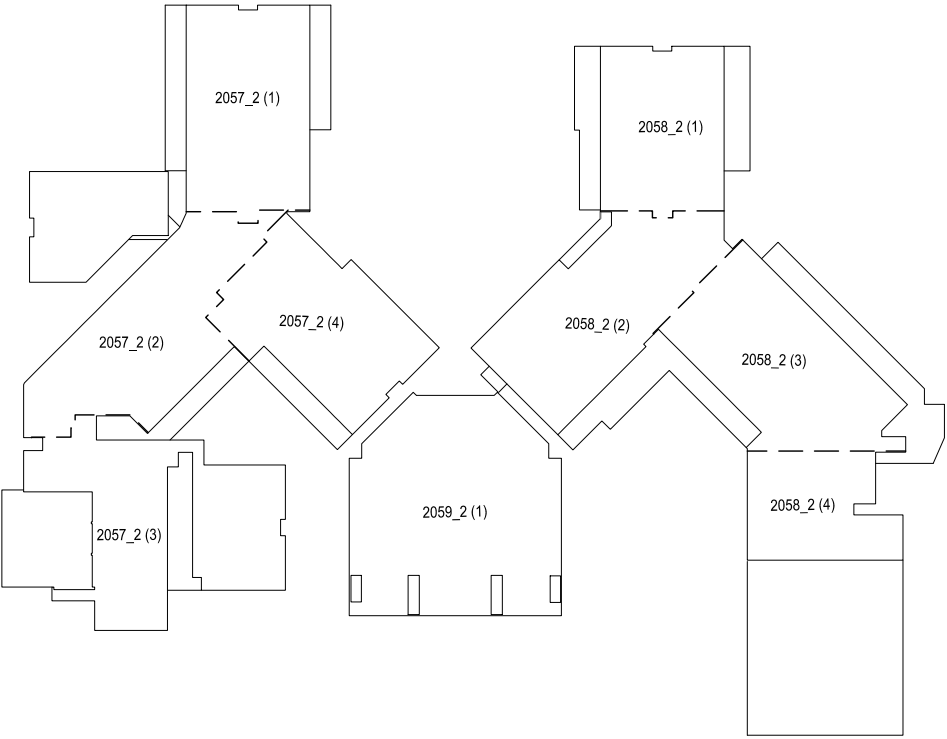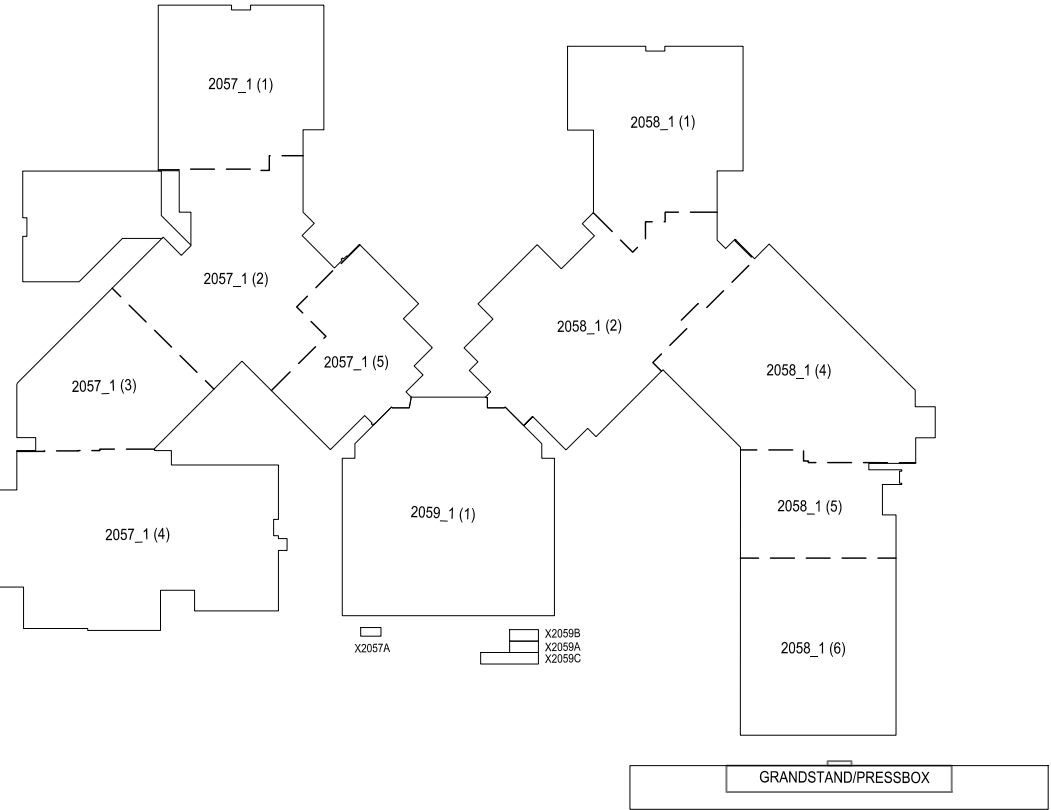

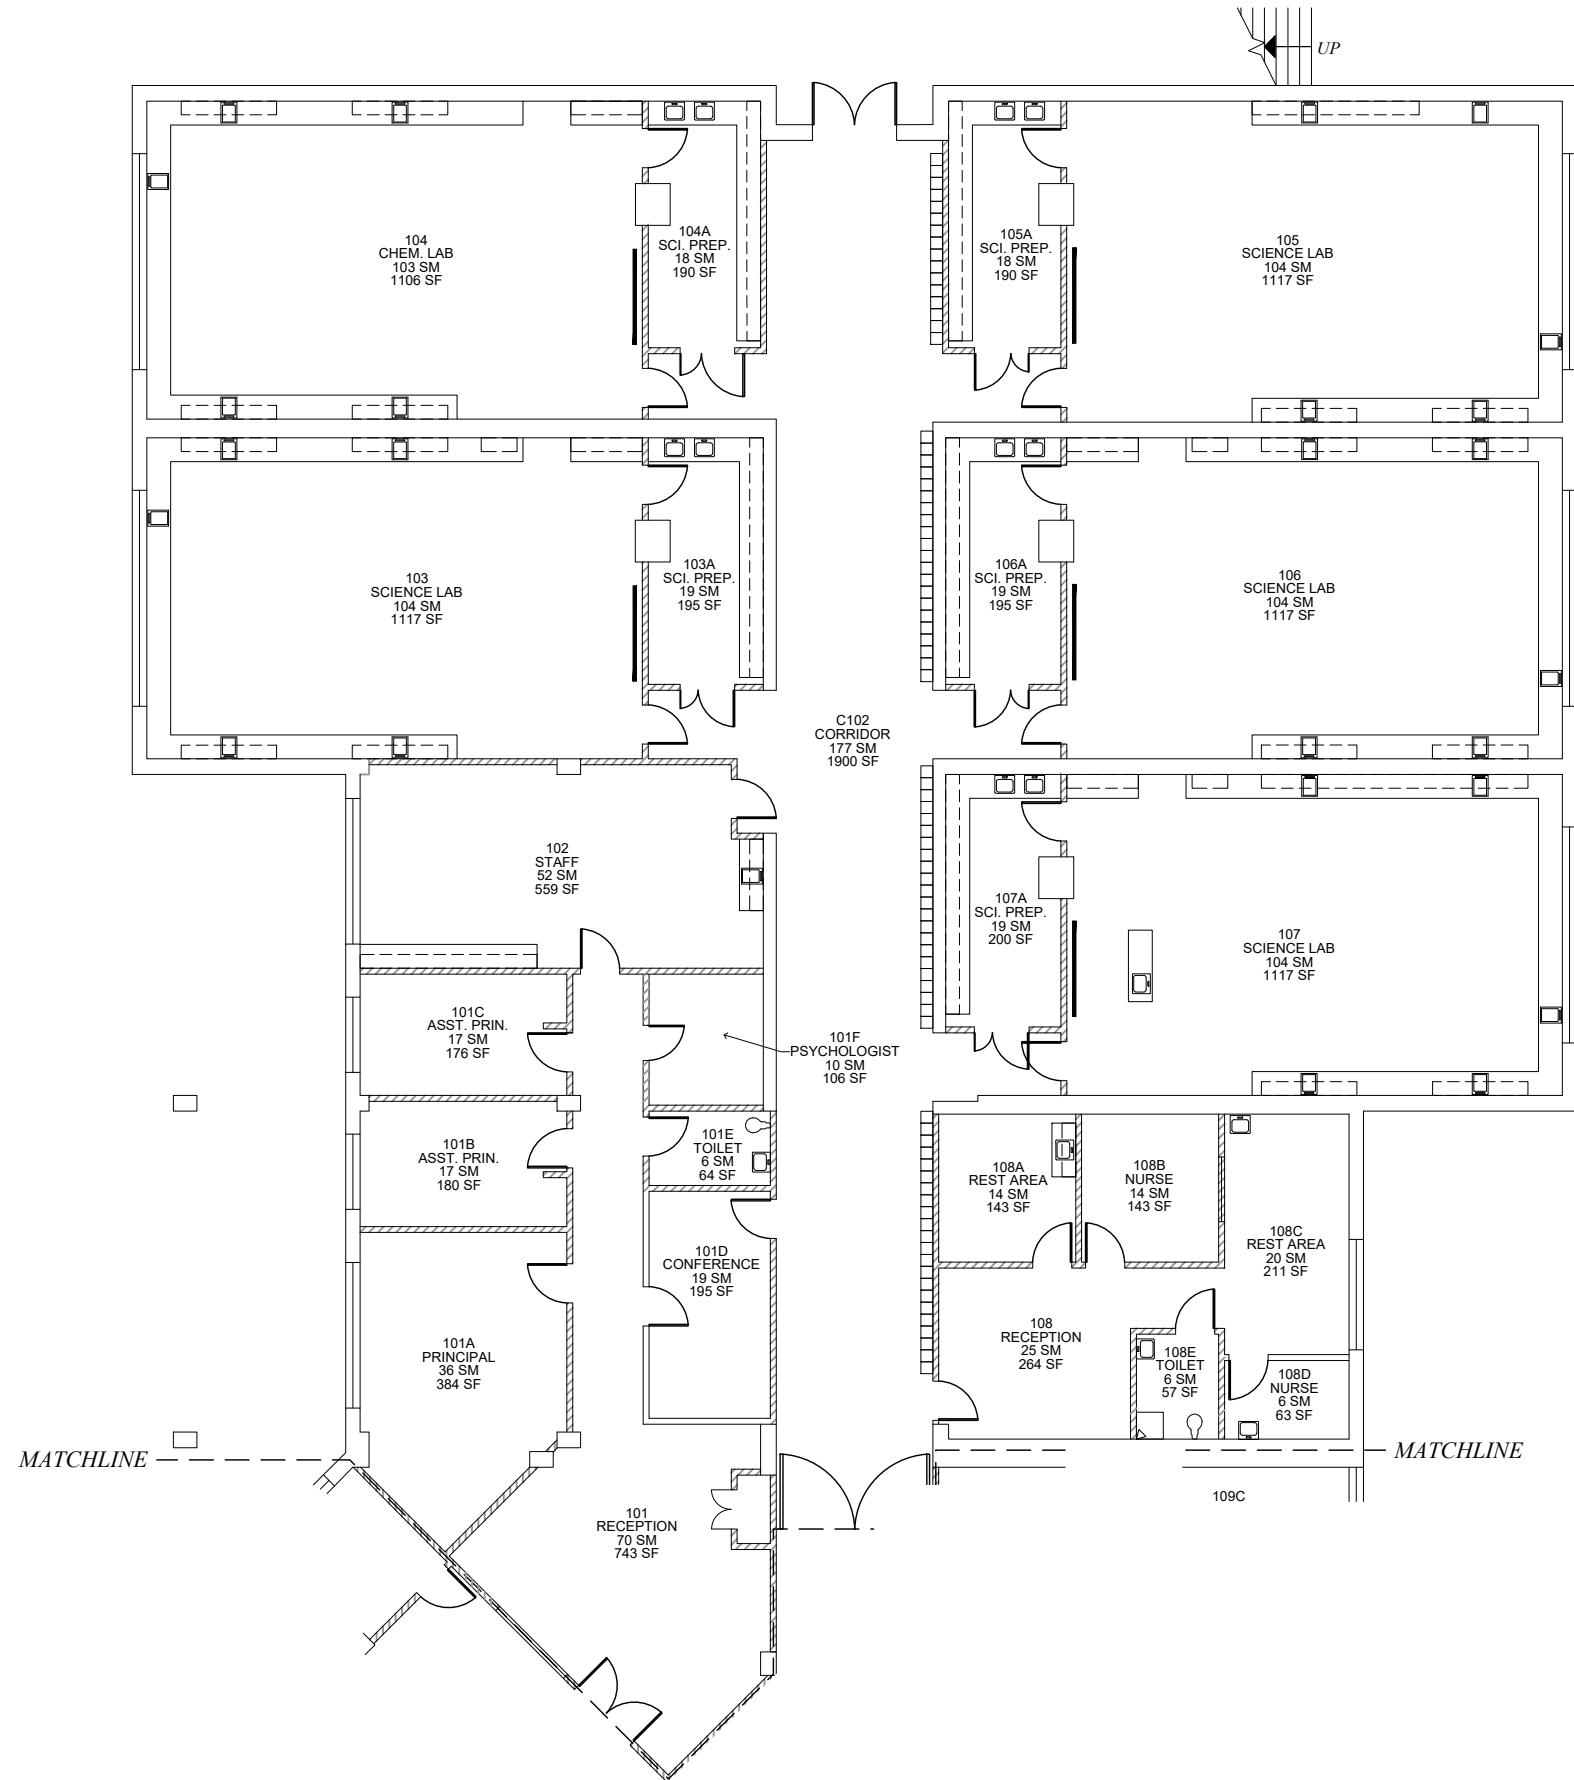

SYMBOL LEGEND	
	DOOR
	DRINKING FOUNTAIN
	SLIDING DOOR
	LAVATORY
	ACCORDION PARTITION
	SINK
	STACK OR FOLDING PARTITION
	TOILET
	WINDOW/GLAZING
	URINAL
	HIGH WINDOW
	LOCKER
	SKYLIGHT
	LAN DISTRIBUTION FRAME
	STOOP/STEP UP
	VENT HOOD
	STAIR
	WALL SHELVING
	RAMP
	UPPER CABINET
	ACCESS LADDER
	BASE CABINET
	COLD STORAGE
	TEACHER CABINET
	AREA CALCULATED @ 50 %
	MATCHLINE
	SLOPING ROOF
	FLAT ROOF

TITLEBLOCK LEGEND	
SHEET NAME:	BLDG #_FLOOR # (# IN SERIES)

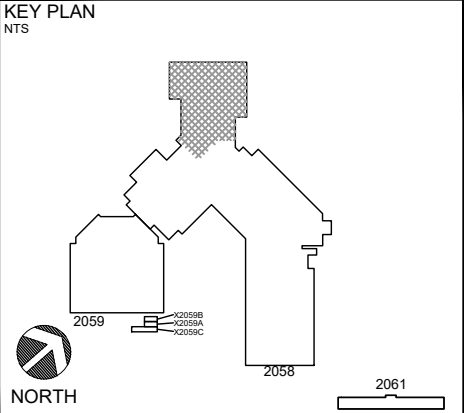


Updated By:	FUS Review:	100% Submittal Date:
AA	MRS	01 APRIL 2020
0 2 4 8 16 FT		

DEPARTMENT OF DEFENSE EDUCATION ACTIVITY
FACILITY UTILIZATION SURVEY

NAPLES
MIDDLE/HIGH SCHOOL
BUILDING NUMBER: 2058
COUNTRY: ITALY
INSTALLATION: NAVAL SUPPORT ACTIVITY NAPLES
SITE: SUPPORT SITE
REGION-DISTRICT: DODEA EUROPE SOUTH

DoDAAC Number:	Floor:	Survey Date:
HE5509	LEVEL 1	JANUARY 2020
Sheet Name:	Sheet Seq:	
2058_1 (1)	9 of 21	

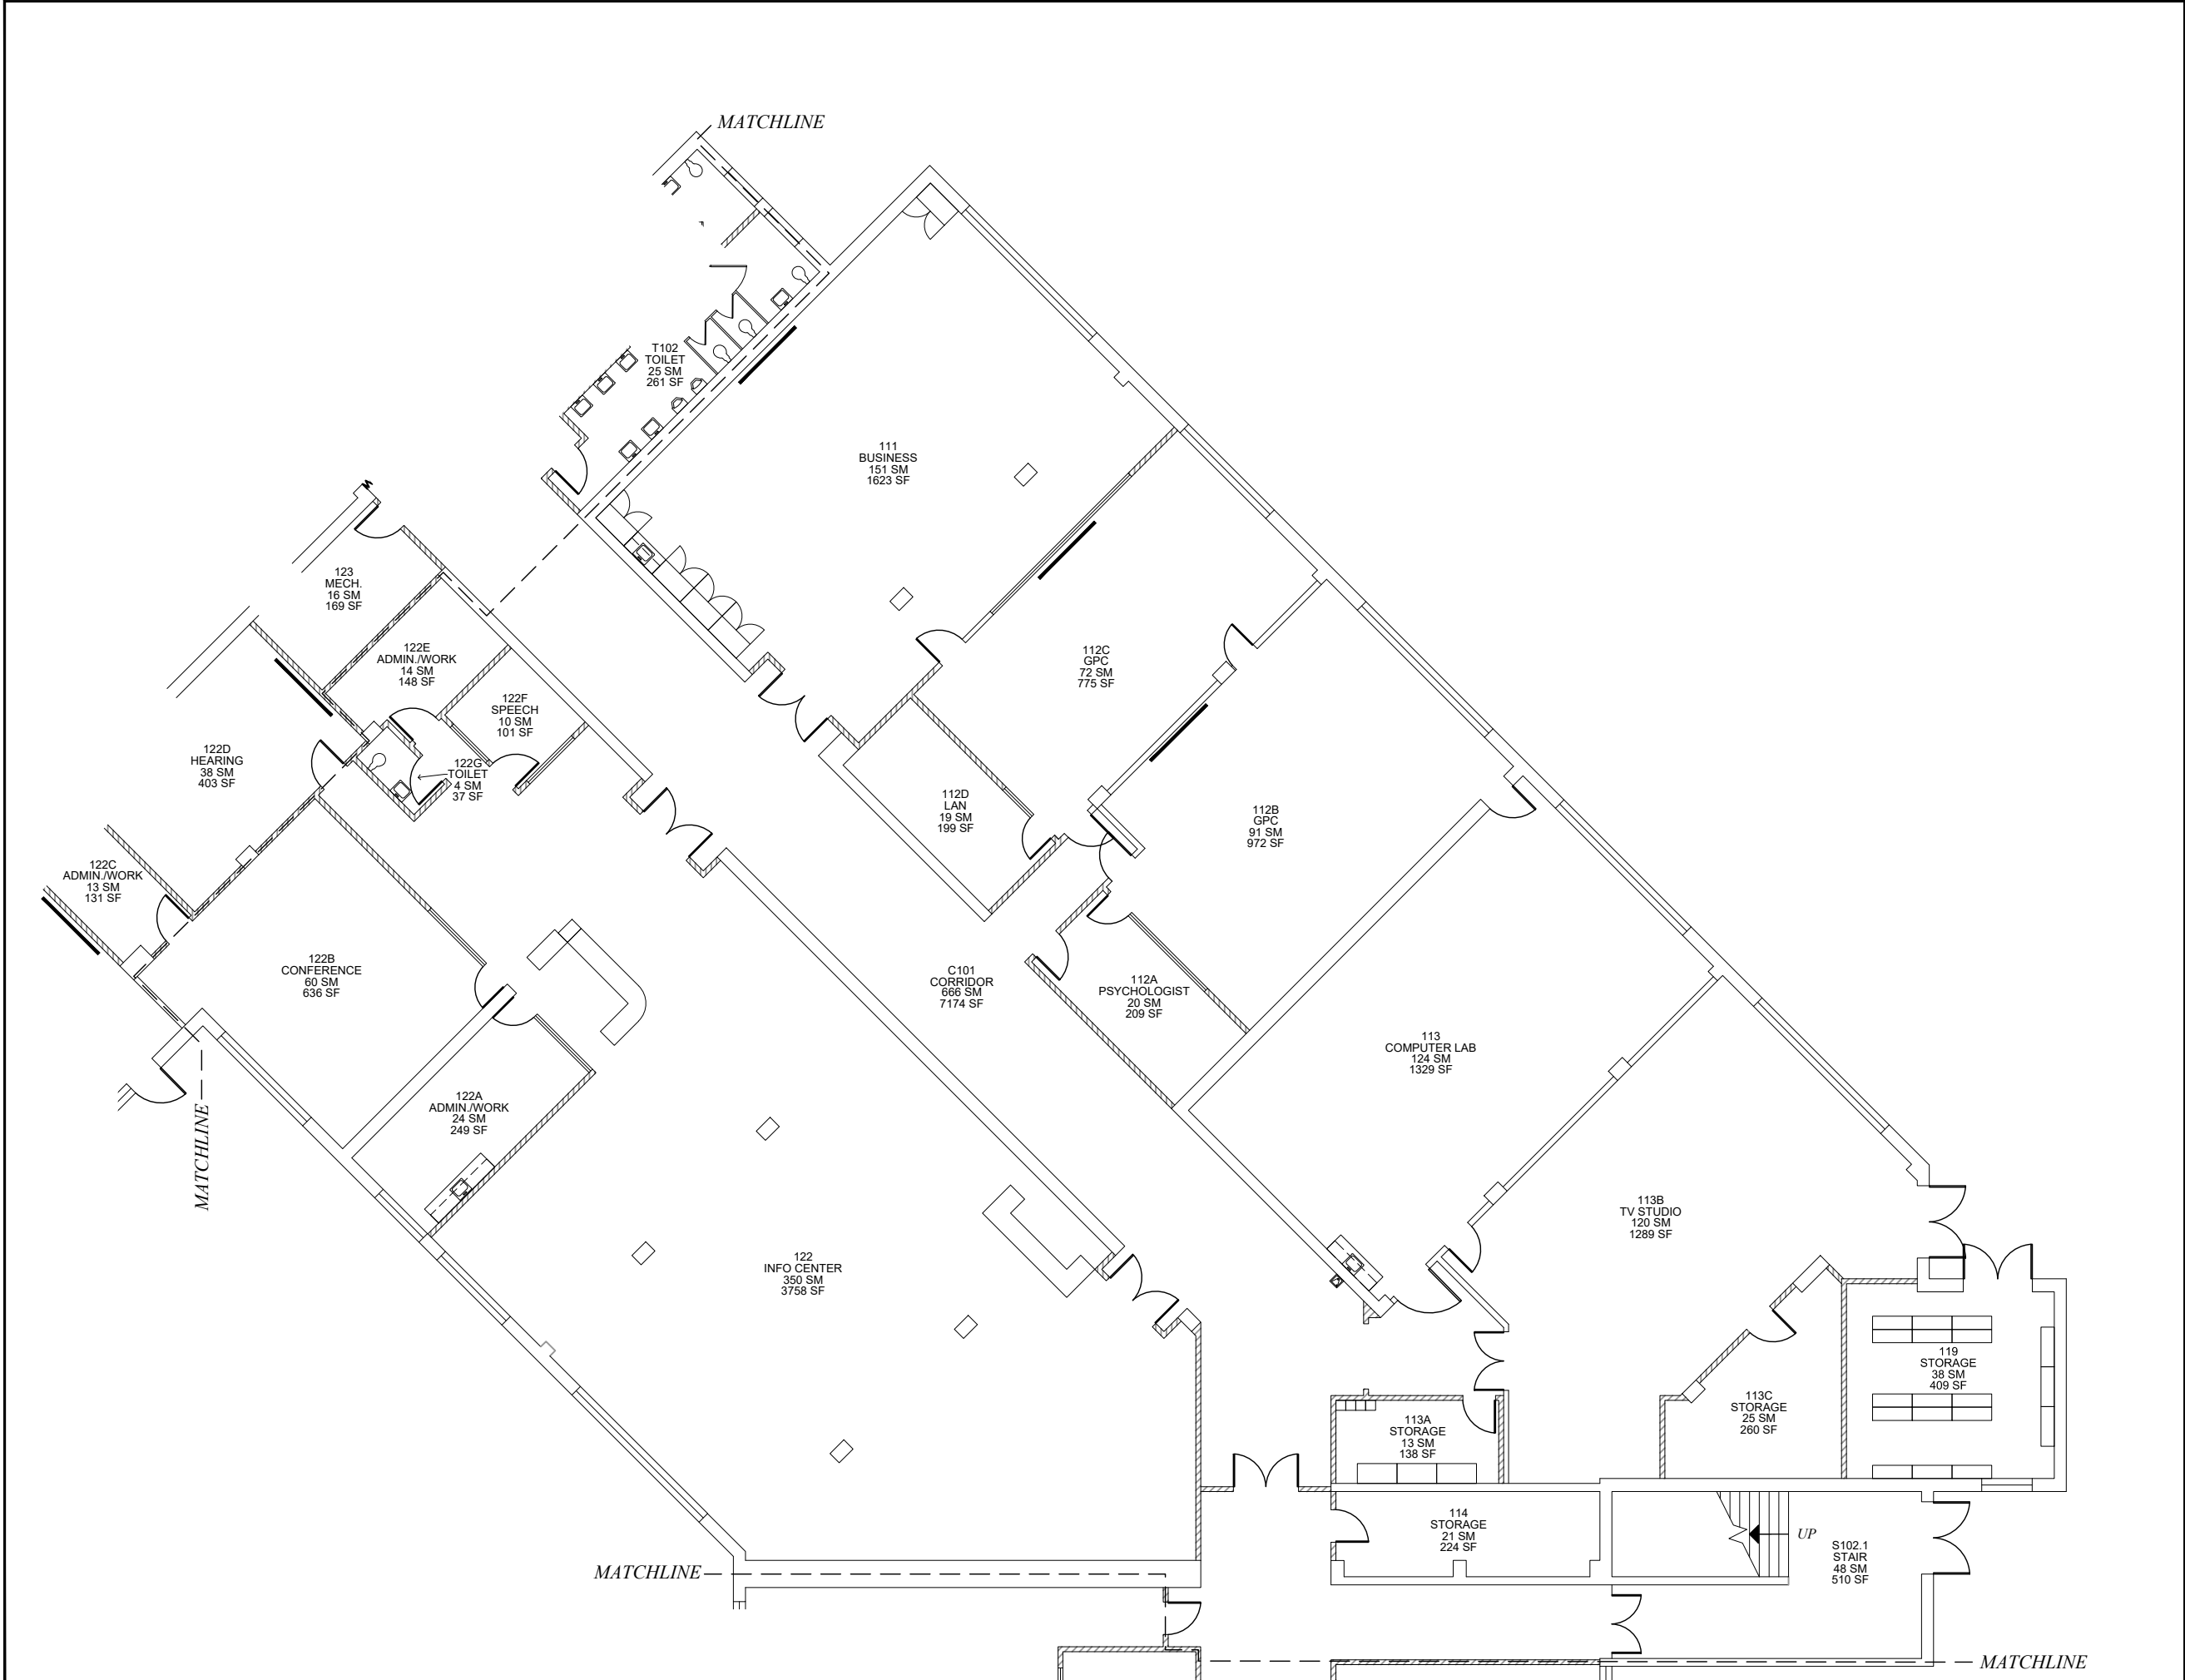

DOOR

SLIDING DOOR

ACCORDION PARTITION

STACK OR FOLDING PARTITION

WINDOW/GLAZING

HIGH WINDOW

SKYLIGHT

STOOP/STEP UP

STAIR

RAMP

ACCESS LADDER

COLD STORAGE

AREA CALCULATED @ 50 %

SLOPING ROOF

DRINKING FOUNTAIN

LAVATORY

SINK

TOILET

URINAL

LOCKER

LAN DISTRIBUTION FRAME

VENT HOOD

WALL SHELVING

UPPER CABINET

BASE CABINET

TEACHER CABINET

MATCHLINE

FLAT ROOF

TITLEBLOCK LEGEND

SHEET NAME:

BLDG #_FLOOR # (# IN SERIES)

KEY PLAN

NTS

NORTH

Updated By: AA

FUS Review: MRS

100% Submittal Date: 01 APRIL 2020

0 2 4 8 16 FT

dodea

DEPARTMENT OF DEFENSE EDUCATION ACTIVITY

FACILITY UTILIZATION SURVEY

NAPLES

MIDDLE/HIGH SCHOOL

BUILDING NUMBER: 2058

COUNTRY: ITALY

INSTALLATION: NAVAL SUPPORT ACTIVITY NAPLES

SITE: SUPPORT SITE

REGION-DISTRICT: DODEA EUROPE SOUTH


DoDAAC Number: HE5509

Floor: LEVEL 1

Survey Date: JANUARY 2020


Sheet Name: 2058_1 (3)

Sheet Seq: 11 of 21

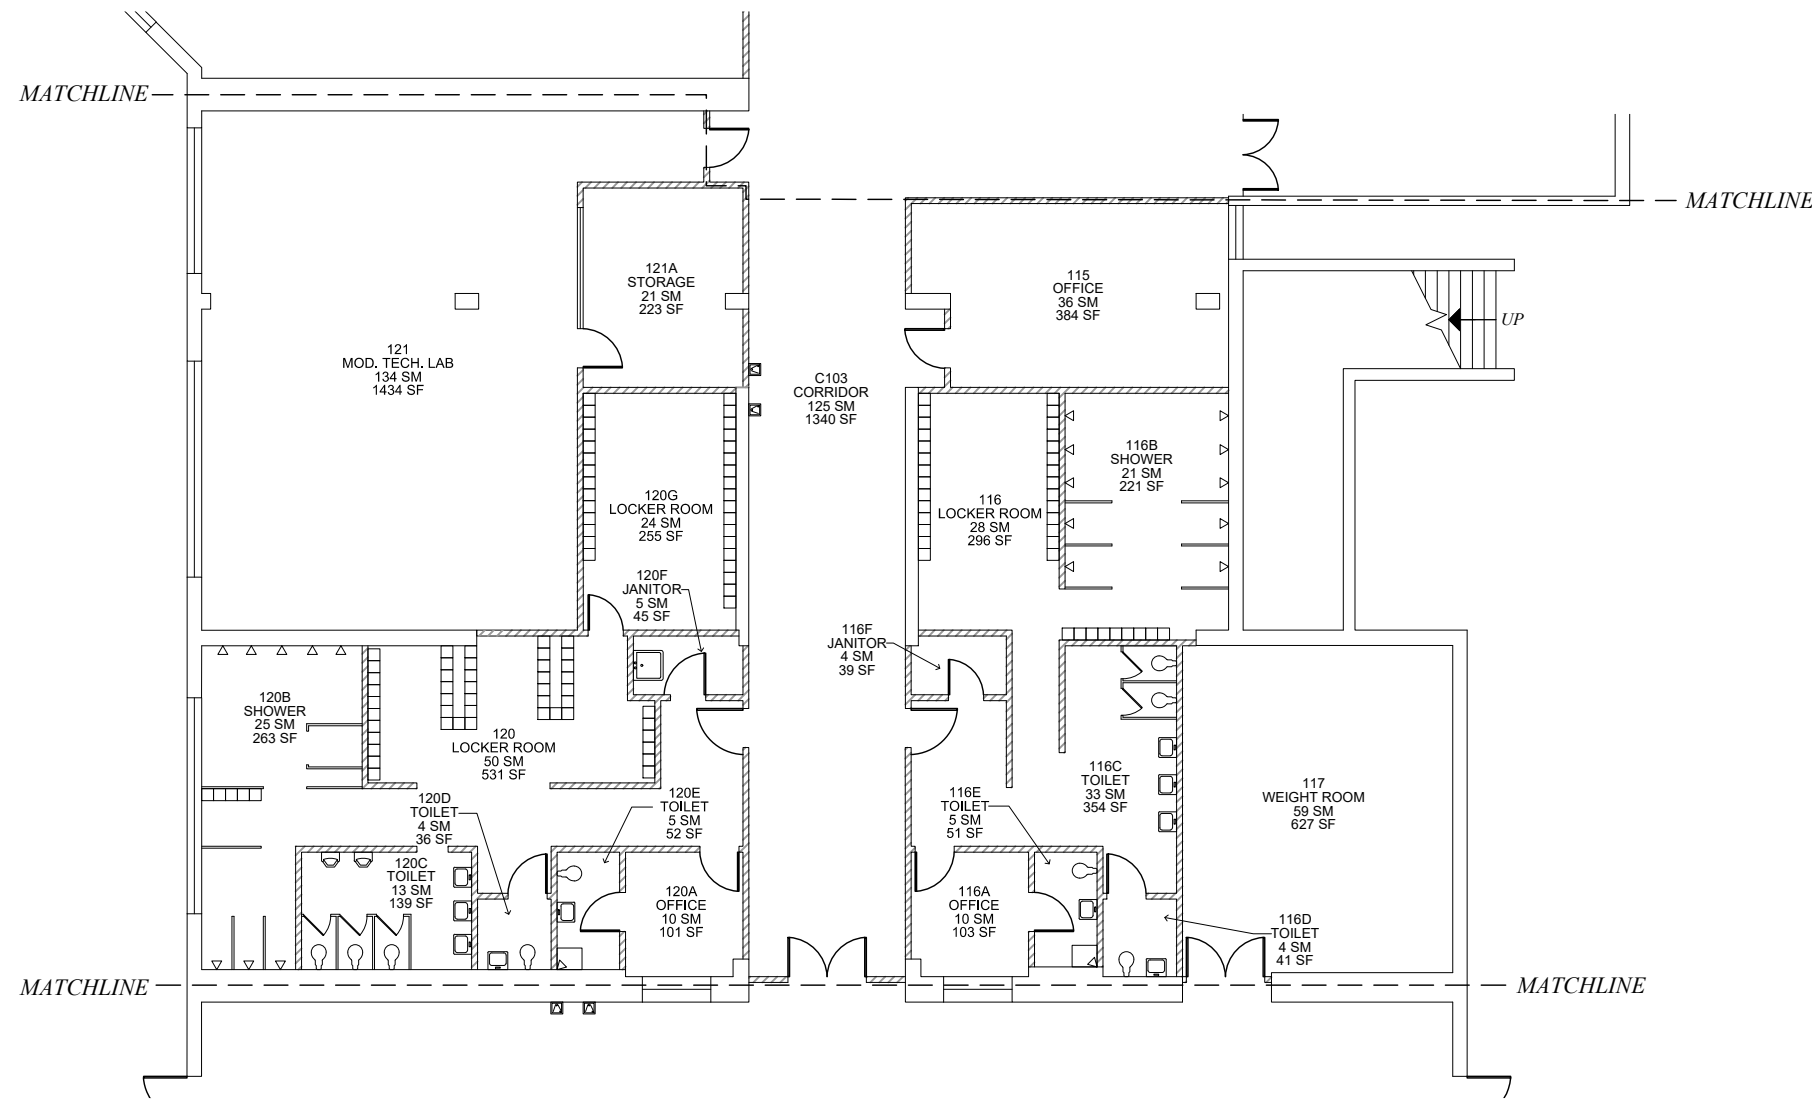

SYMBOL LEGEND	
	DOOR
	DRINKING FOUNTAIN
	SLIDING DOOR
	LAVATORY
	ACCORDION PARTITION
	SINK
	STACK OR FOLDING PARTITION
	TOILET
	WINDOW/GLAZING
	URINAL
	HIGH WINDOW
	LOCKER
	SKYLIGHT
	LAN DISTRIBUTION FRAME
	STOOP/STEP UP
	VENT HOOD
	STAIR
	WALL SHELVING
	RAMP
	UPPER CABINET
	ACCESS LADDER
	BASE CABINET
	COLD STORAGE
	TEACHER CABINET
	AREA CALCULATED @ 50 %
	MATCHLINE
	SLOPING ROOF
	FLAT ROOF

TITLEBLOCK LEGEND	
SHEET NAME:	BLDG #_FLOOR # (# IN SERIES)

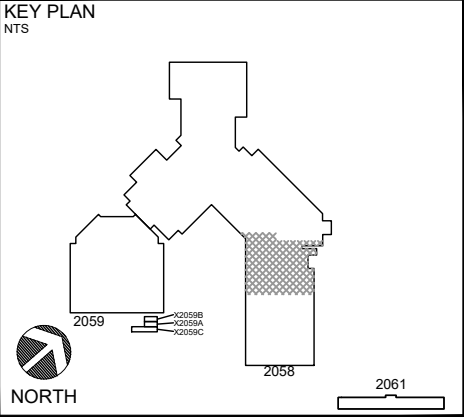


Updated By:	FUS Review:	100% Submittal Date:
AA	MRS	01 APRIL 2020
0 2 4 8 16 FT		

DEPARTMENT OF DEFENSE EDUCATION ACTIVITY
FACILITY UTILIZATION SURVEY


NAPLES
MIDDLE/HIGH SCHOOL
BUILDING NUMBER: 2058
COUNTRY: ITALY
INSTALLATION: NAVAL SUPPORT ACTIVITY NAPLES
SITE: SUPPORT SITE
REGION-DISTRICT: DODEA EUROPE SOUTH

DoDAAC Number: HE5509	Floor: LEVEL 1	Survey Date: JANUARY 2020
Sheet Name: 2058_1 (4)	Sheet Seq:	12 of 21

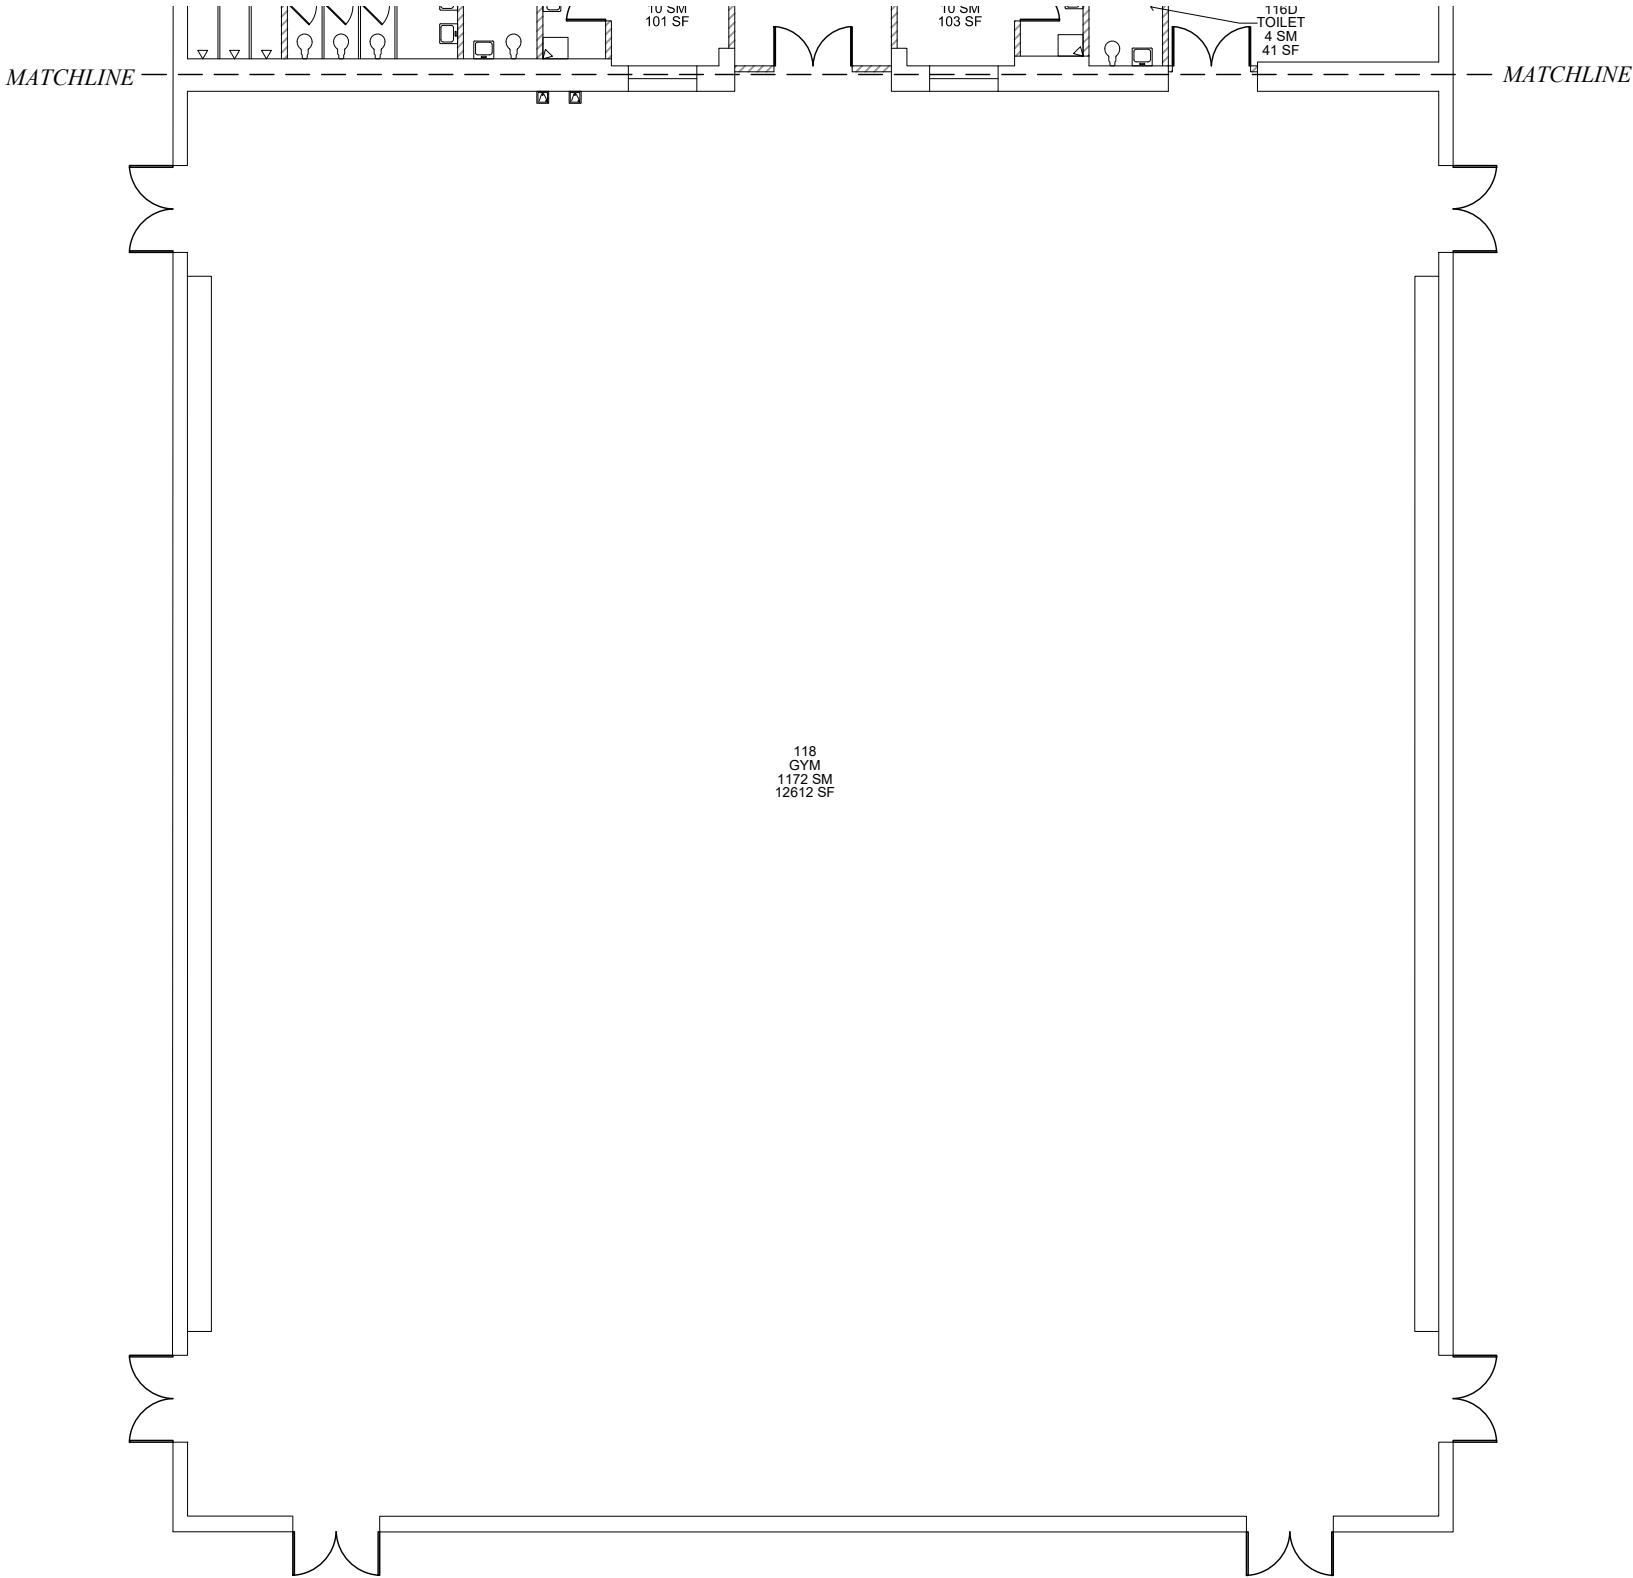

SYMBOL LEGEND	
	DOOR
	DRINKING FOUNTAIN
	SLIDING DOOR
	LAVATORY
	ACCORDION PARTITION
	SINK
	STACK OR FOLDING PARTITION
	TOILET
	WINDOW/GLAZING
	URINAL
	HIGH WINDOW
	LOCKER
	SKYLIGHT
	LAN DISTRIBUTION FRAME
	STOOP/STEP UP
	VENT HOOD
	STAIR
	WALL SHELVING
	RAMP
	UPPER CABINET
	ACCESS LADDER
	BASE CABINET
	COLD STORAGE
	TEACHER CABINET
	AREA CALCULATED @ 50 %
	MATCHLINE
	SLOPING ROOF
	FLAT ROOF

TITLEBLOCK LEGEND	
SHEET NAME:	BLDG #_FLOOR # (# IN SERIES)

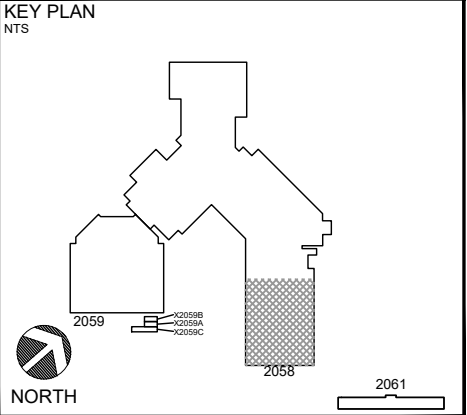


Updated By:	FUS Review:	100% Submittal Date:
AA	MRS	01 APRIL 2020
0 2 4 8 16 FT		

DEPARTMENT OF DEFENSE EDUCATION ACTIVITY
FACILITY UTILIZATION SURVEY


NAPLES
MIDDLE/HIGH SCHOOL
BUILDING NUMBER: 2058
COUNTRY: ITALY
INSTALLATION: NAVAL SUPPORT ACTIVITY NAPLES
SITE: SUPPORT SITE
REGION-DISTRICT: DODEA EUROPE SOUTH

DoDAAC Number: HE5509	Floor: LEVEL 1	Survey Date: JANUARY 2020
Sheet Name: 2058_1 (5)		Sheet Seq: 13 of 21

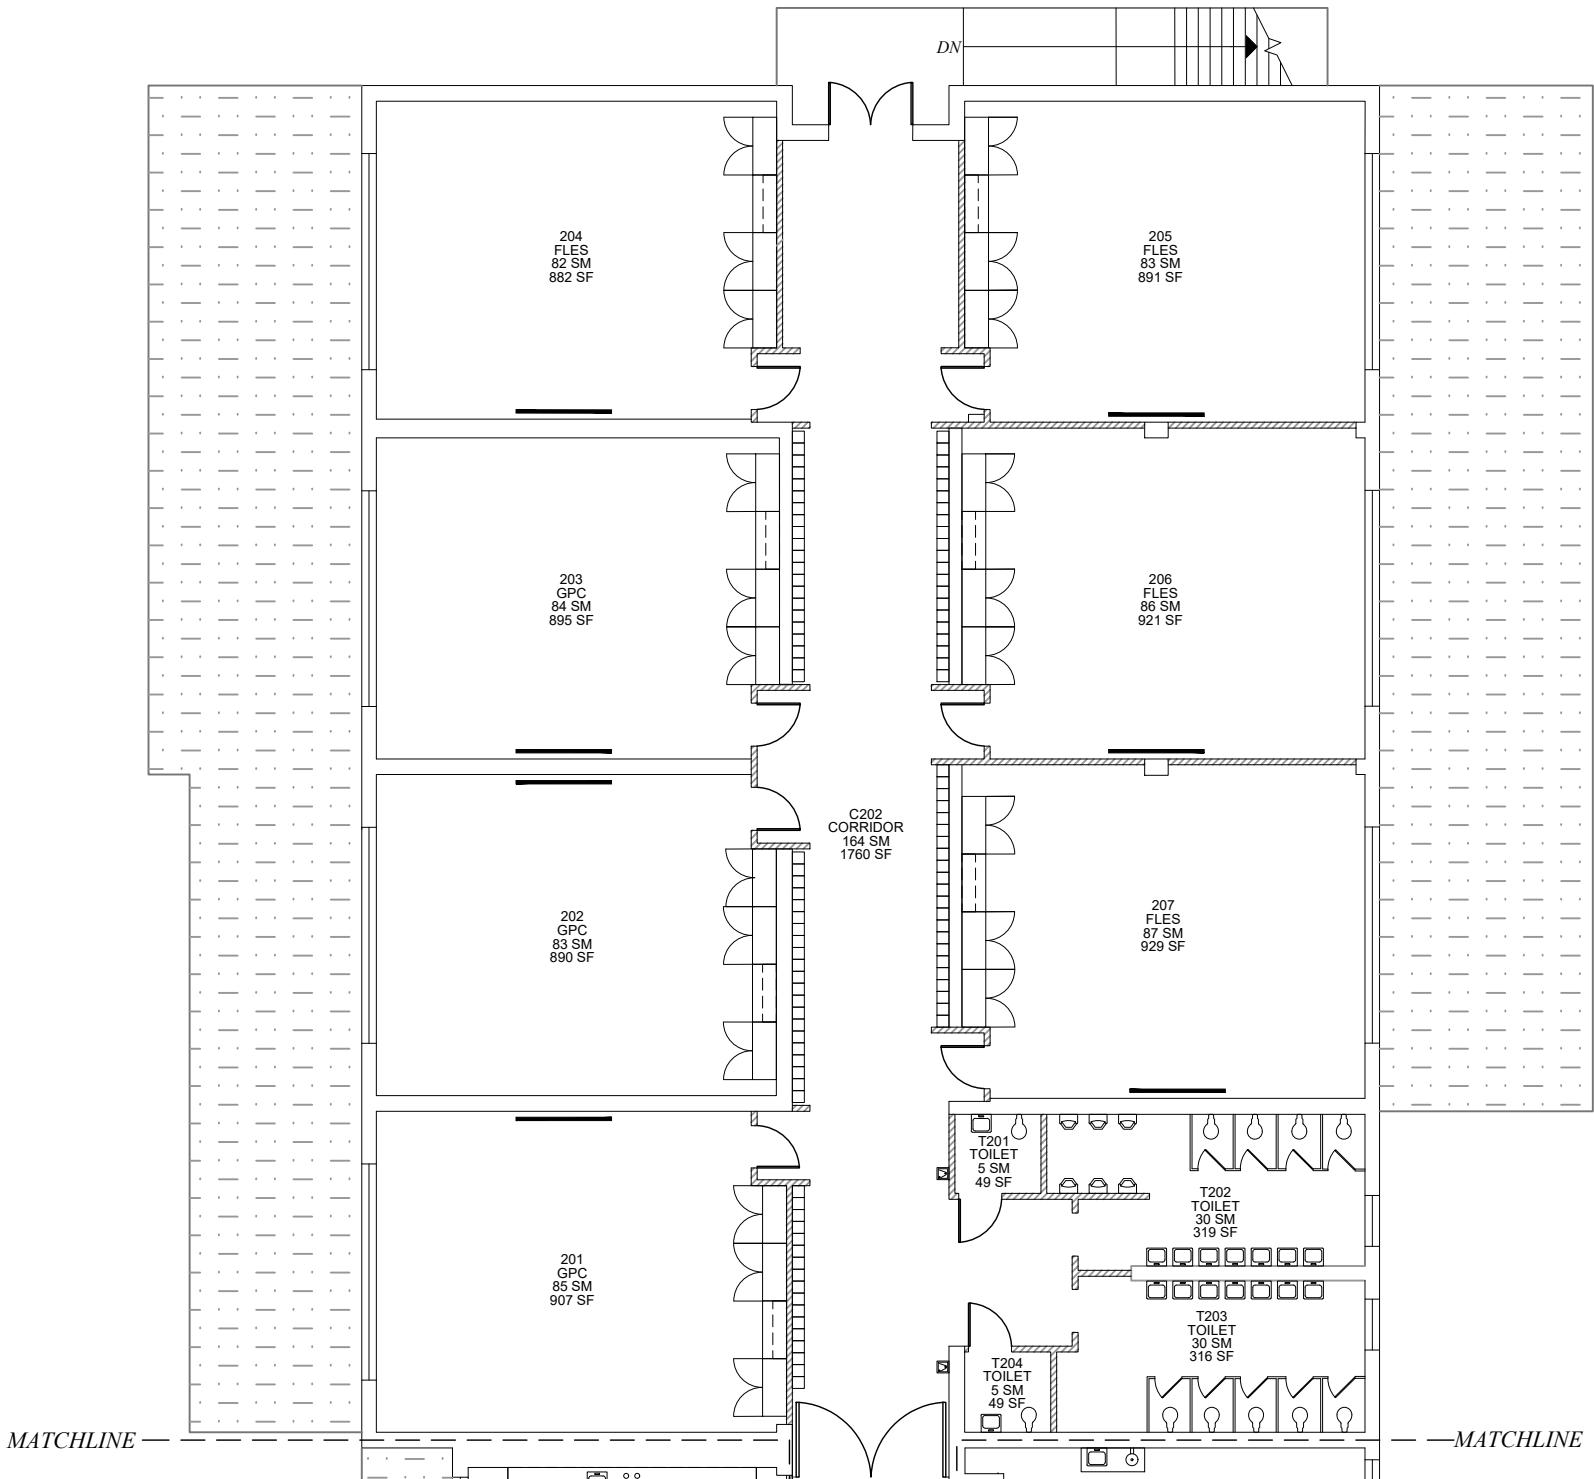

SYMBOL LEGEND	
	DOOR
	DRINKING FOUNTAIN
	SLIDING DOOR
	LAVATORY
	ACCORDION PARTITION
	SINK
	STACK OR FOLDING PARTITION
	TOILET
	WINDOW/GLAZING
	URINAL
	HIGH WINDOW
	LOCKER
	SKYLIGHT
	LAN DISTRIBUTION FRAME
	STOOP/STEP UP
	VENT HOOD
	STAIR
	WALL SHELVING
	RAMP
	UPPER CABINET
	ACCESS LADDER
	BASE CABINET
	COLD STORAGE
	TEACHER CABINET
	AREA CALCULATED @ 50 %
	MATCHLINE
	SLOPING ROOF
	FLAT ROOF

TITLEBLOCK LEGEND	
SHEET NAME:	BLDG #_FLOOR # (# IN SERIES)

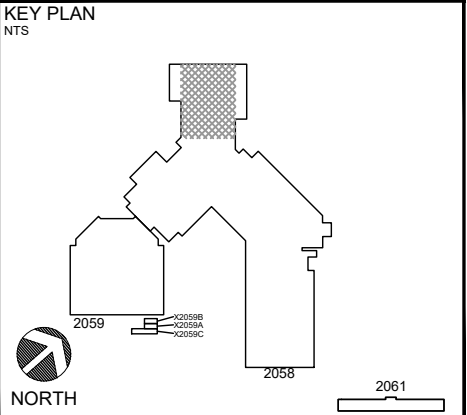

Updated By:	FUS Review:	100% Submittal Date:
AA	MRS	01 APRIL 2020

0 2 4 8 16 FT

dodea
DEPARTMENT OF DEFENSE EDUCATION ACTIVITY
FACILITY UTILIZATION SURVEY

**NAPLES
MIDDLE/HIGH SCHOOL**
BUILDING NUMBER: 2058
COUNTRY: ITALY
INSTALLATION: NAVAL SUPPORT ACTIVITY NAPLES
SITE: SUPPORT SITE
REGION-DISTRICT: DODEA EUROPE SOUTH

DoDAAC Number:	Floor:	Survey Date:
HE5509	LEVEL 2	JANUARY 2020
Sheet Name:	Sheet Seq:	
2058_2 (1)	14 of 21	



SYMBOL LEGEND

DOOR	DRINKING FOUNTAIN
SLIDING DOOR	LAVATORY
ACCORDION PARTITION	SINK
STACK OR FOLDING PARTITION	TOILET
WINDOW/GLAZING	URINAL
HIGH WINDOW	LOCKER
SKYLIGHT	LAN DISTRIBUTION FRAME
STOOP/STEP UP	VENT HOOD
STAIR	WALL SHELVING
RAMP	UPPER CABINET
ACCESS LADDER	BASE CABINET
COLD STORAGE	TEACHER CABINET
AREA CALCULATED @ 50 %	MATCHLINE
SLOPING ROOF	FLAT ROOF

TITLEBLOCK LEGEND

SHEET NAME:	BLDG # FLOOR # (# IN SERIES)

KEY PLAN

NTS

Updated By:	FUS Review:	100% Submittal Date:
AA	MRS	01 APRIL 2020

0

2

4

8

16

FT

dodea

DEPARTMENT OF DEFENSE EDUCATION ACTIVITY

FACILITY UTILIZATION SURVEY

NAPLES

MIDDLE/HIGH SCHOOL

BUILDING NUMBER: 2058

COUNTRY: ITALY


INSTALLATION: NAVAL SUPPORT ACTIVITY NAPLES

SITE: SUPPORT SITE

REGION-DISTRICT: DODEA EUROPE SOUTH

DoDAAC Number:	Floor:	Survey Date:
HE5509	LEVEL 2	JANUARY 2020

Sheet Name:	Sheet Seq:
2058_2 (2)	15 of 21

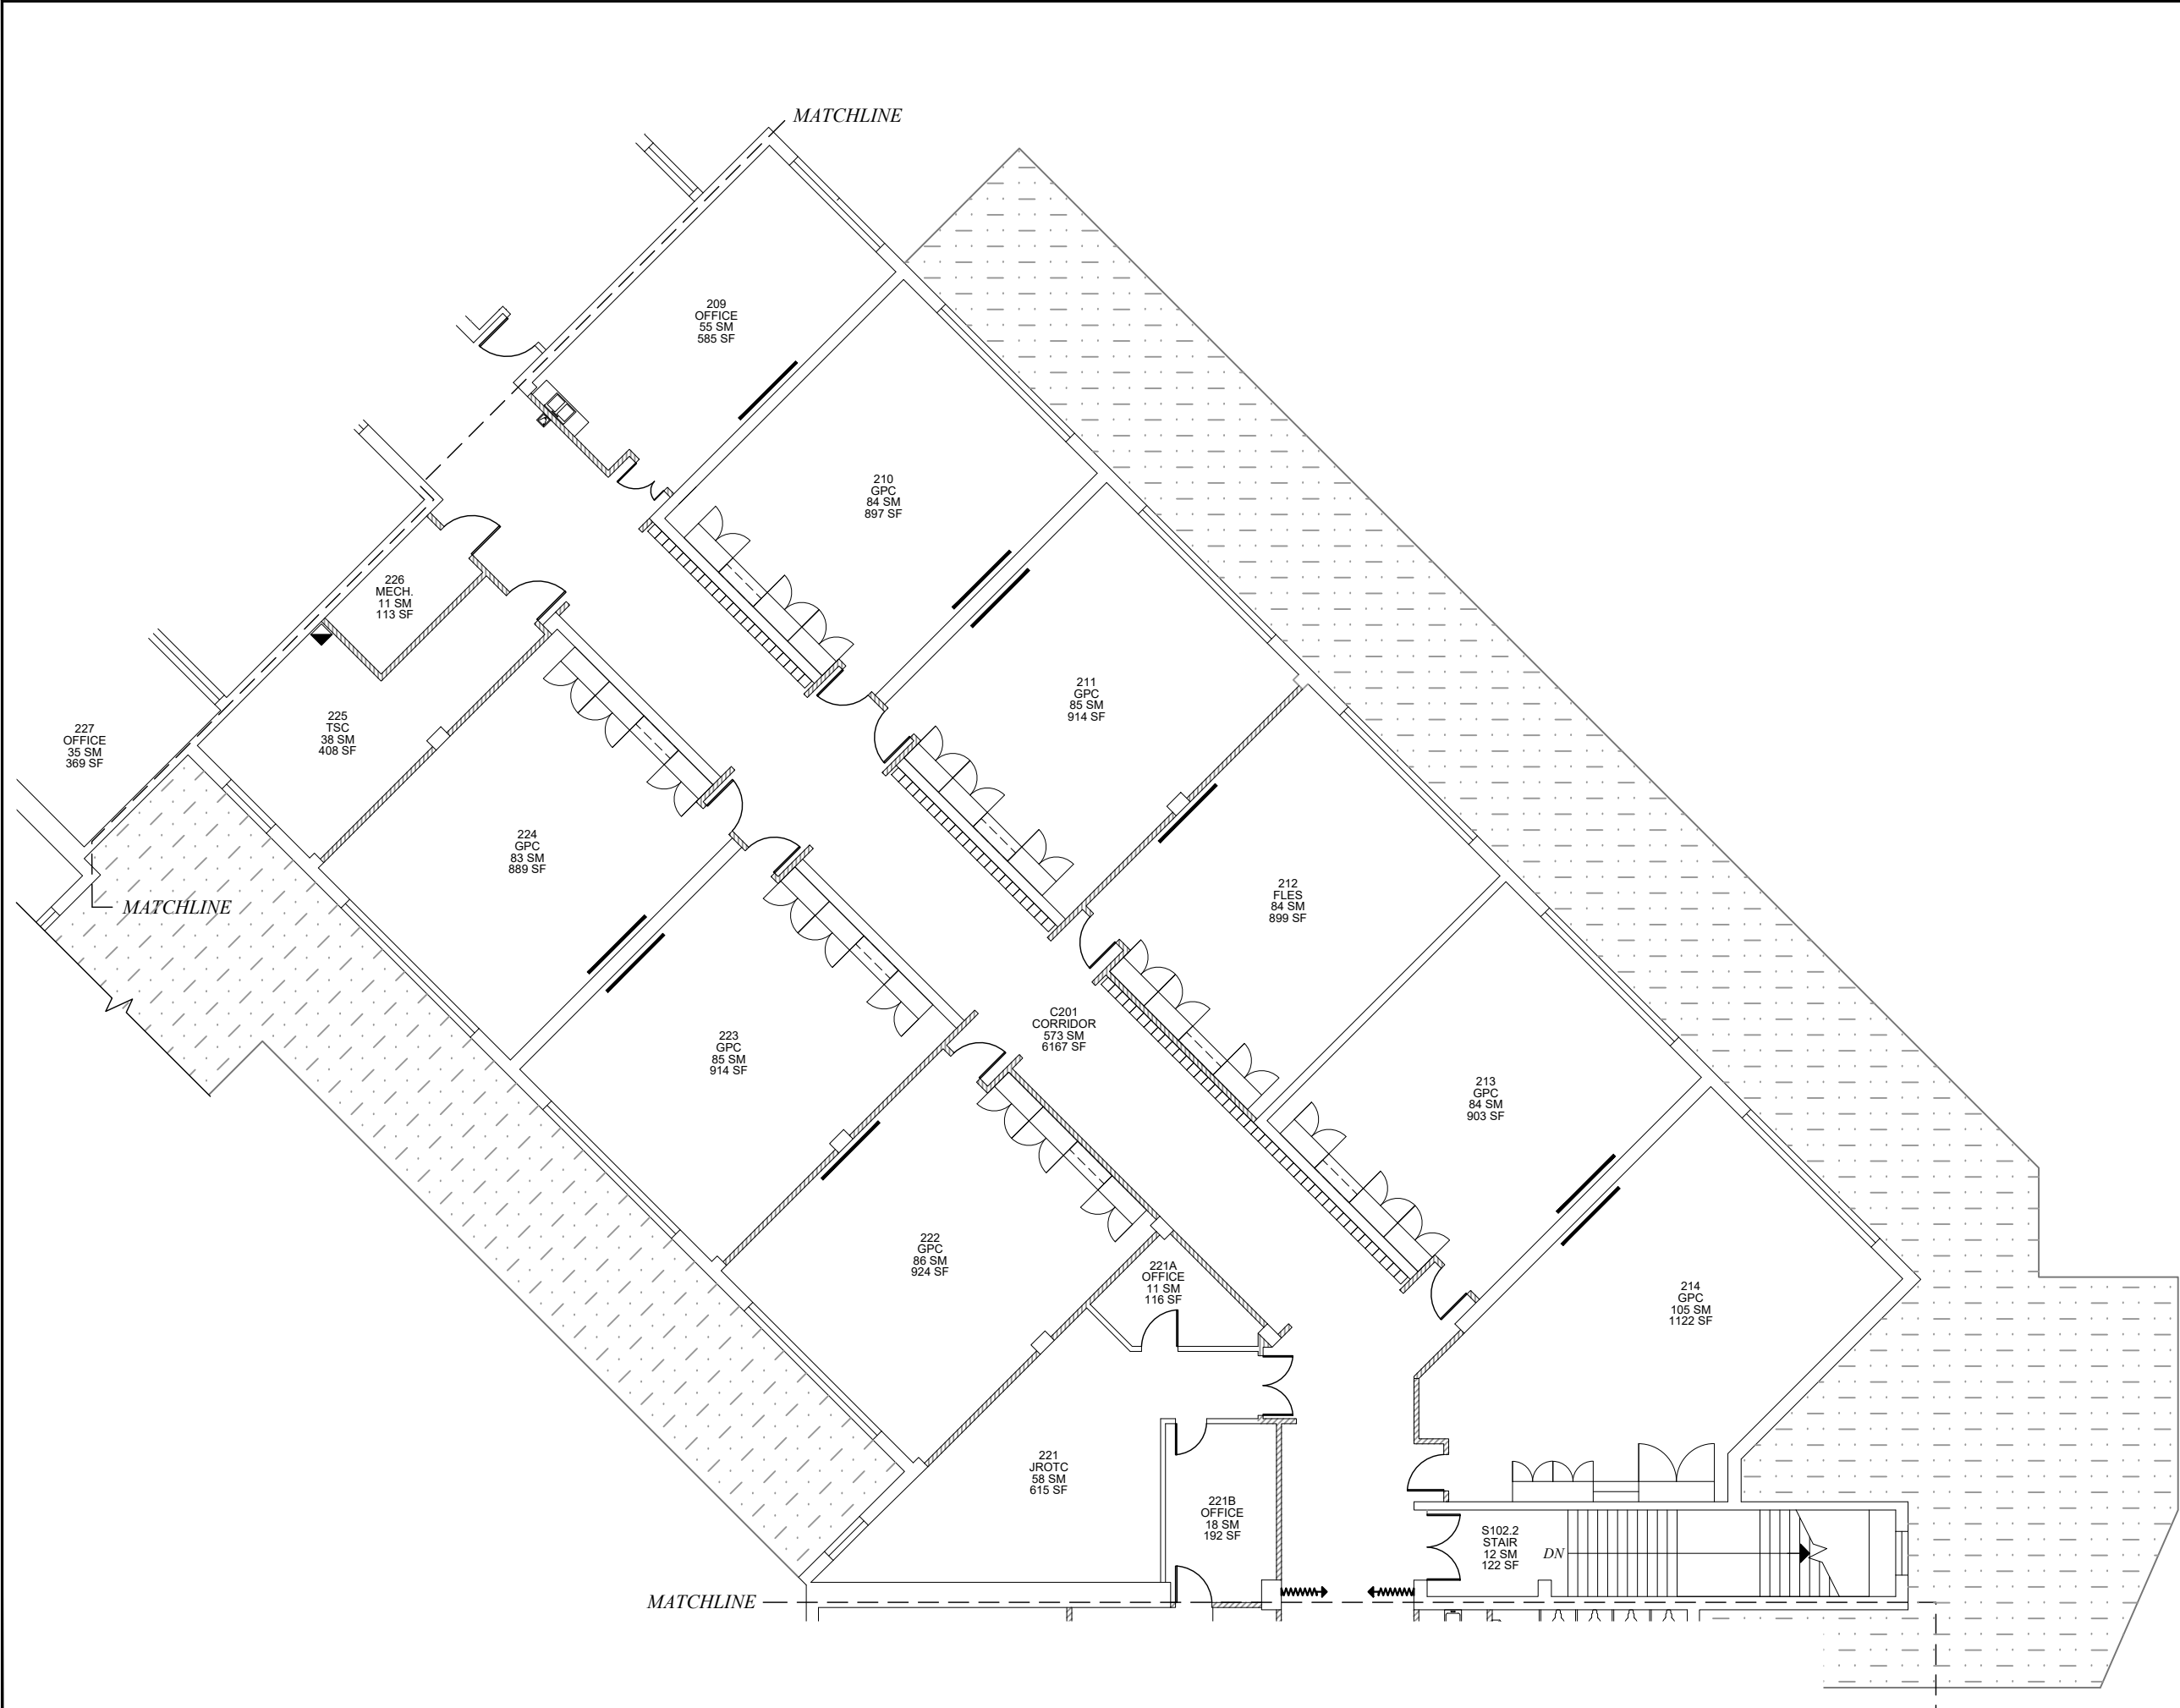

DOOR

SLIDING DOOR

ACCORDION PARTITION

STACK OR FOLDING PARTITION

WINDOW/GLAZING

HIGH WINDOW

SKYLIGHT

STOOP/STEP UP

STAIR

RAMP

ACCESS LADDER

COLD STORAGE

AREA CALCULATED @ 50 %

SLOPING ROOF

DRINKING FOUNTAIN

LAVATORY

SINK

TOILET

URINAL

LOCKER

LAN DISTRIBUTION FRAME

VENT HOOD

WALL SHELVING

UPPER CABINET

BASE CABINET

TEACHER CABINET

MATCHLINE

FLAT ROOF

TITLEBLOCK LEGEND

SHEET NAME:

BLDG #_FLOOR # (# IN SERIES)

KEY PLAN

NTS

Updated By:

FUS Review:

100% Submittal Date:

AA

MRS

01 APRIL 2020

0

2

4

8

16

FT

dodea

DEPARTMENT OF DEFENSE EDUCATION ACTIVITY

FACILITY UTILIZATION SURVEY

NAPLES

MIDDLE/HIGH SCHOOL

BUILDING NUMBER: 2058

COUNTRY: ITALY

INSTALLATION: NAVAL SUPPORT ACTIVITY NAPLES

SITE: SUPPORT SITE

REGION-DISTRICT: DODEA EUROPE SOUTH

DoDAAC Number:

Floor:

Survey Date:

HE5509

LEVEL 2


JANUARY 2020

Sheet Name:

Sheet Seq:

2058_2 (3)

16 of 21

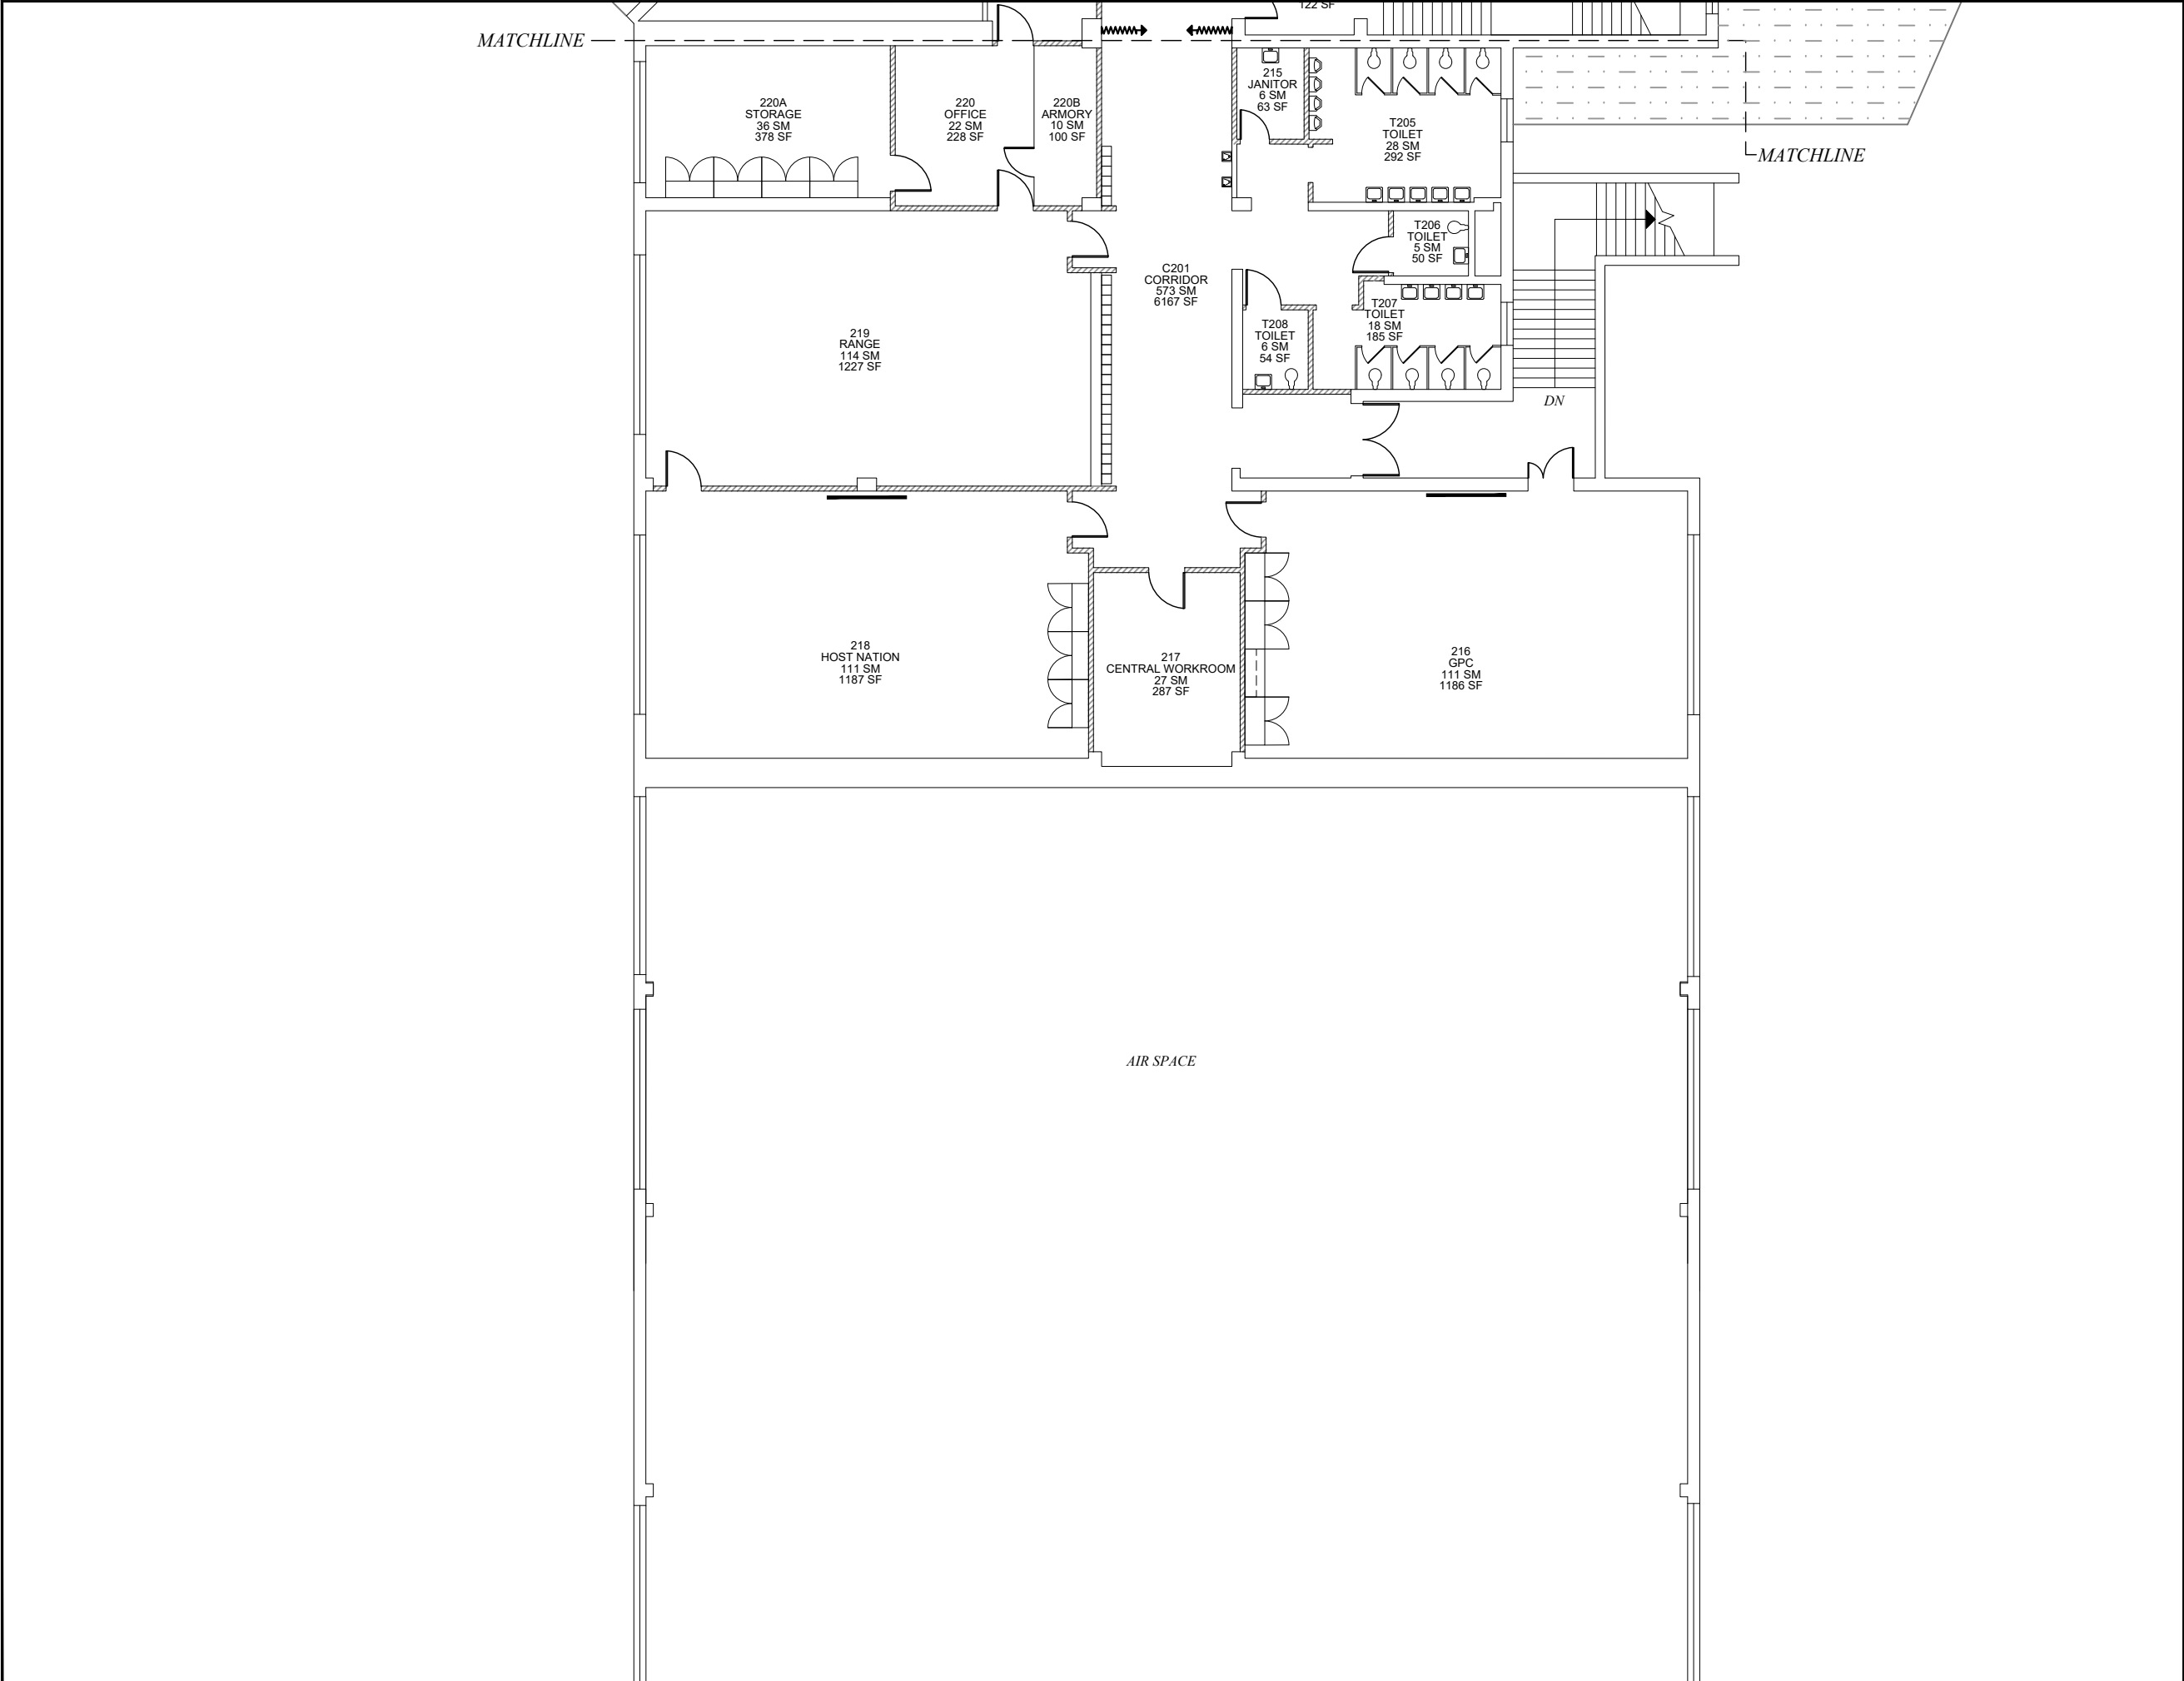

DOOR

SLIDING DOOR

ACCORDION PARTITION

STACK OR FOLDING PARTITION

WINDOW/GLAZING

HIGH WINDOW

SKYLIGHT

STOOP/STEP UP

STAIR

RAMP

ACCESS LADDER

COLD STORAGE

AREA CALCULATED @ 50 %

SLOPING ROOF

DRINKING FOUNTAIN

LAVATORY

SINK

TOILET

URINAL

LOCKER

LAN DISTRIBUTION FRAME

VENT HOOD

WALL SHELVING

UPPER CABINET

BASE CABINET

TEACHER CABINET

MATCHLINE

FLAT ROOF

TITLEBLOCK LEGEND

SHEET NAME:

BLDG #_FLOOR # (# IN SERIES)

KEY PLAN

NTS

Updated By:

AA

FUS Review:

MRS

100% Submittal Date:

01 APRIL 2020

0

2

4

8

16

FT

dodea

DEPARTMENT OF DEFENSE EDUCATION ACTIVITY

FACILITY UTILIZATION SURVEY

NAPLES

MIDDLE/HIGH SCHOOL

BUILDING NUMBER: 2058

COUNTRY: ITALY

INSTALLATION: NAVAL SUPPORT ACTIVITY NAPLES

SITE: SUPPORT SITE

REGION-DISTRICT: DODEA EUROPE SOUTH

DoDAAC Number:

HE5509

Floor:

LEVEL 2

Survey Date:


JANUARY 2020

Sheet Name:

2058_2 (4)


Sheet Seq:

17 of 21

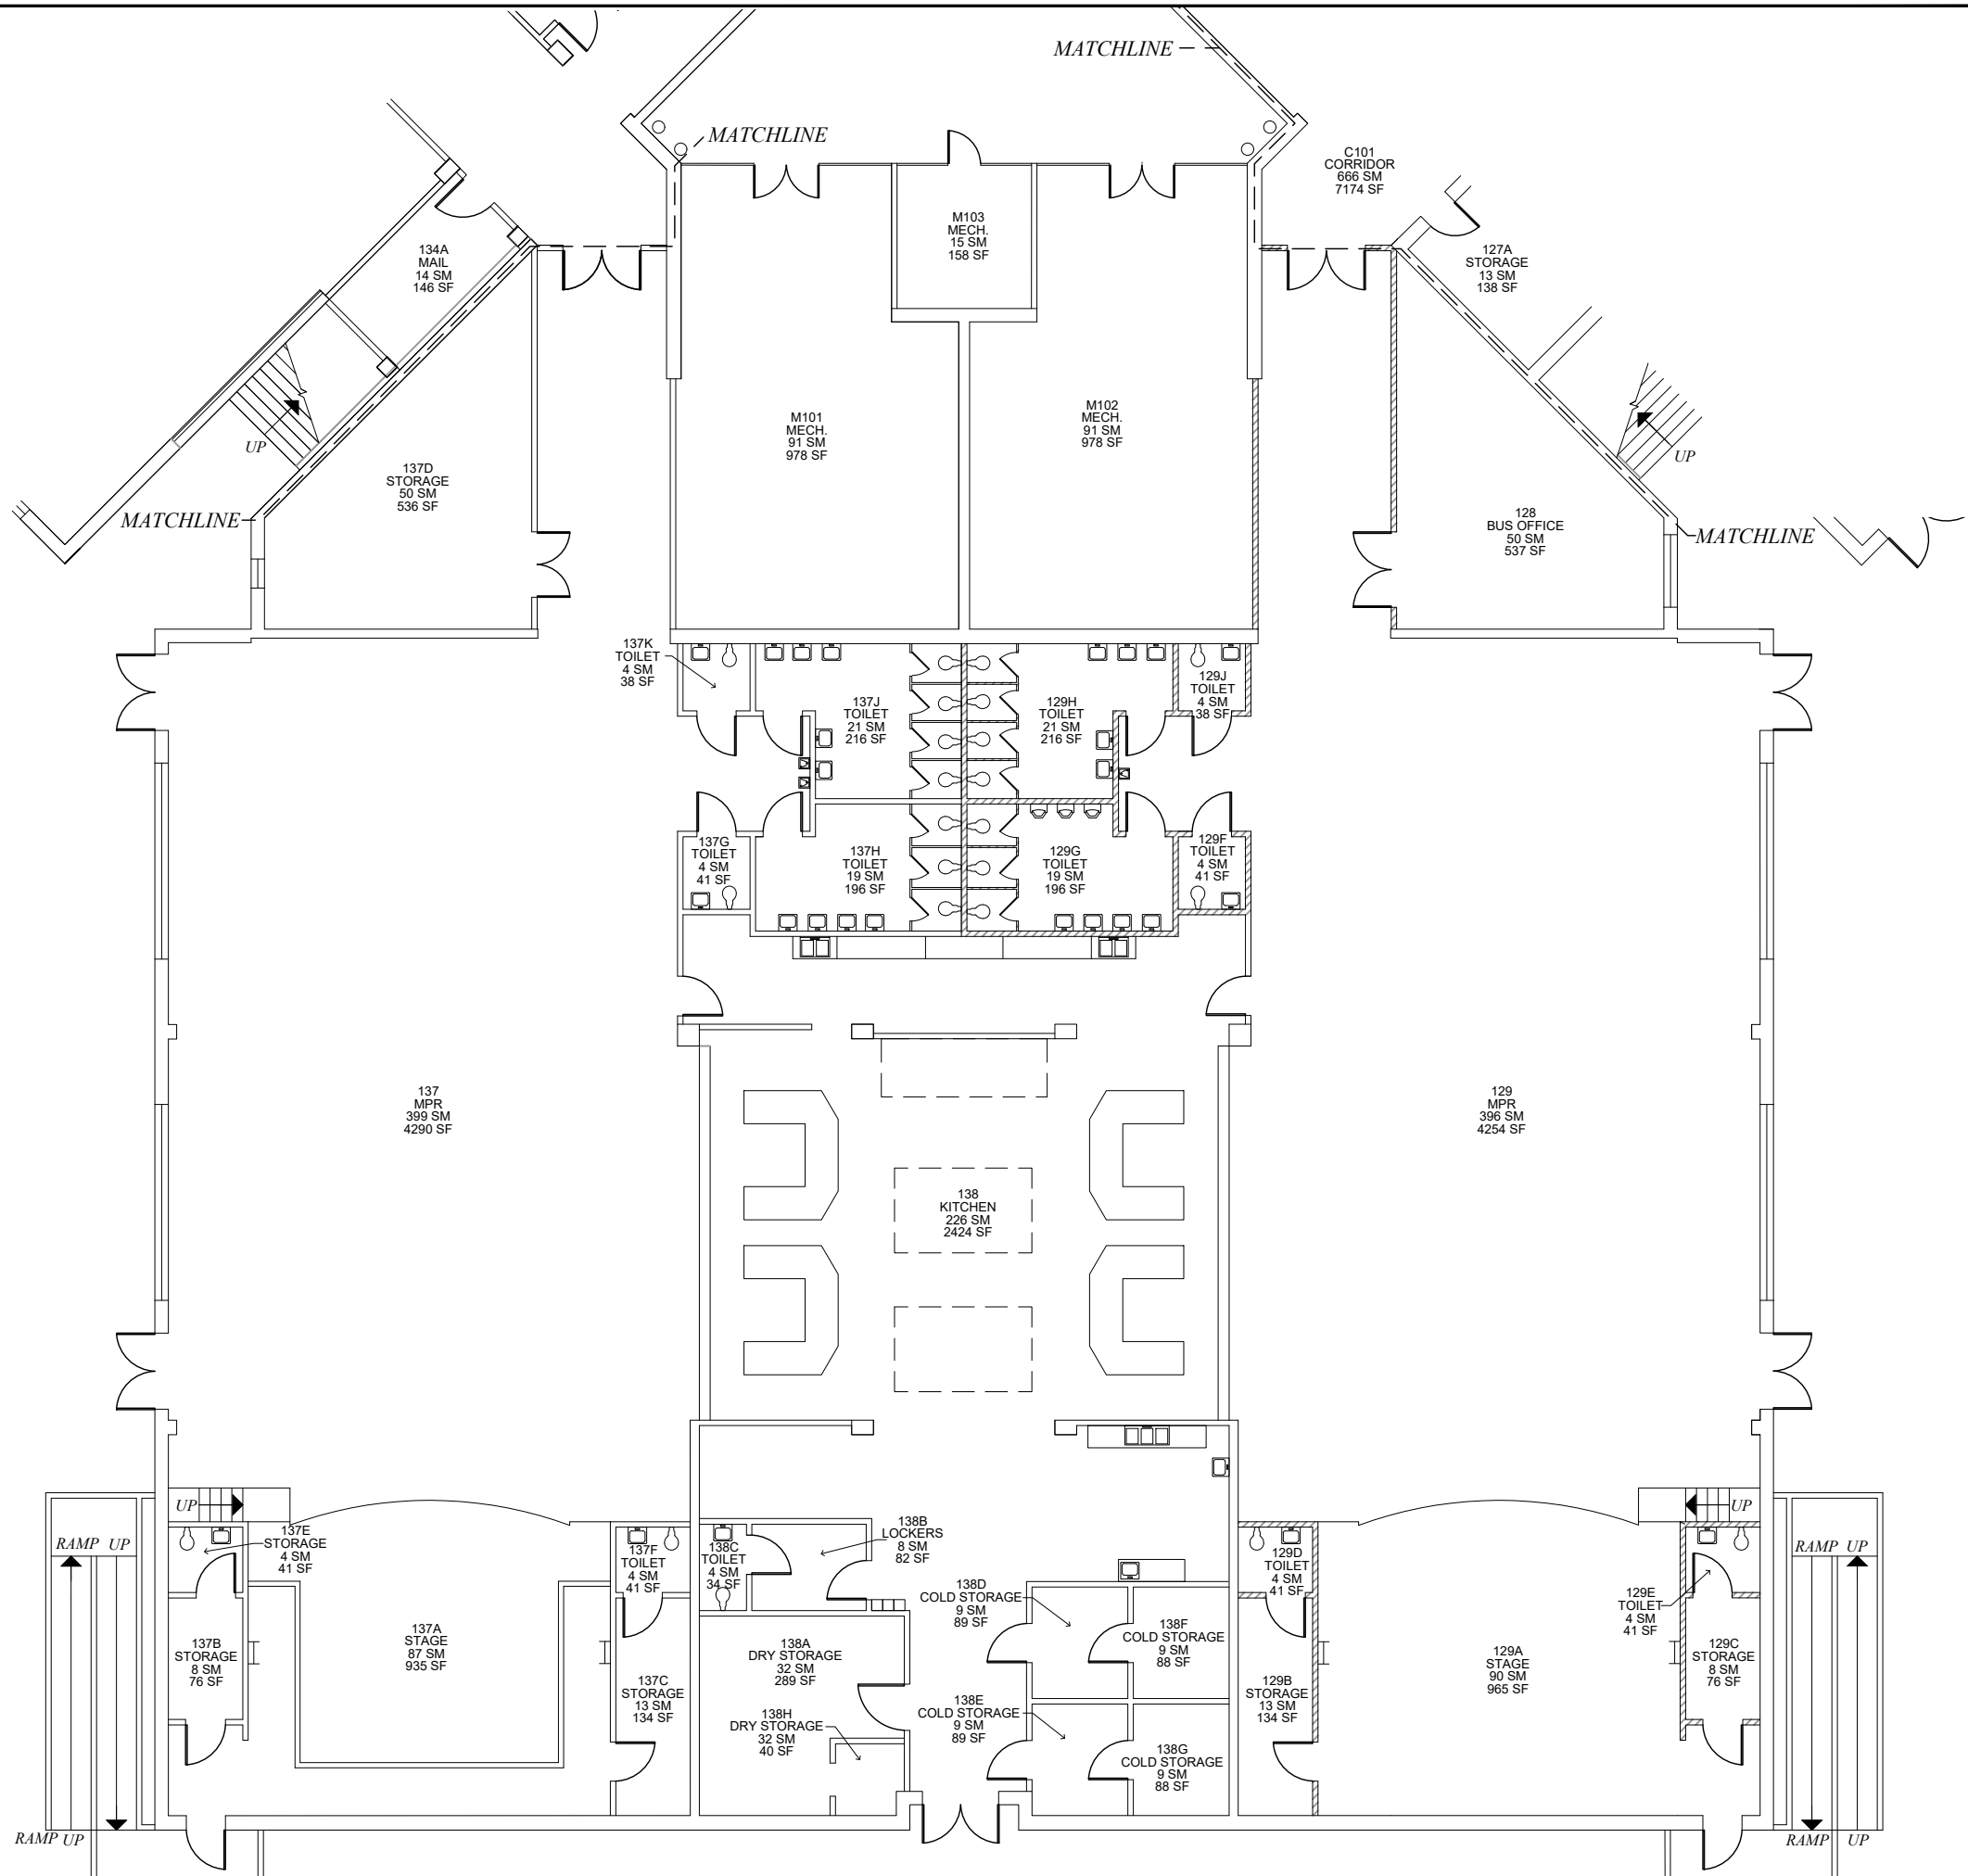

SYMBOL LEGEND	
	DOOR
	DRINKING FOUNTAIN
	SLIDING DOOR
	LAVATORY
	ACCORDION PARTITION
	SINK
	STACK OR FOLDING PARTITION
	TOILET
	WINDOW/GLAZING
	URINAL
	HIGH WINDOW
	LOCKER
	SKYLIGHT
	LAN DISTRIBUTION FRAME
	STOOP/STEP UP
	VENT HOOD
	STAIR
	WALL SHELVING
	RAMP
	UPPER CABINET
	ACCESS LADDER
	BASE CABINET
	COLD STORAGE
	TEACHER CABINET
	AREA CALCULATED @ 50 %
	SLOPING ROOF
	FLAT ROOF


TITLEBLOCK LEGEND	
SHEET NAME:	BLDG #_FLOOR # (# IN SERIES)

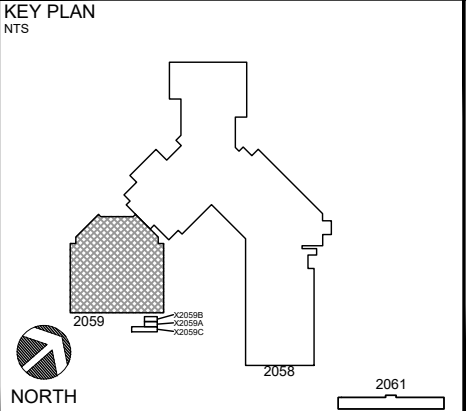

Updated By:	FUS Review:	100% Submittal Date:
AA	MRS	01 APRIL 2020
0 2 4 8 16 FT		

dodea
DEPARTMENT OF DEFENSE EDUCATION ACTIVITY
FACILITY UTILIZATION SURVEY

NAPLES MIDDLE/HIGH SCHOOL		
BUILDING NUMBER: 2059		
COUNTRY: ITALY		
INSTALLATION: NAVAL SUPPORT ACTIVITY NAPLES		
SITE: SUPPORT SITE		
REGION-DISTRICT: DODEA EUROPE SOUTH		
DoDAAC Number:	Floor:	Survey Date:
HE5509	LEVEL 1	JANUARY 2020
Sheet Name:	Sheet Seq:	
2059_1 (1)		18 of 21

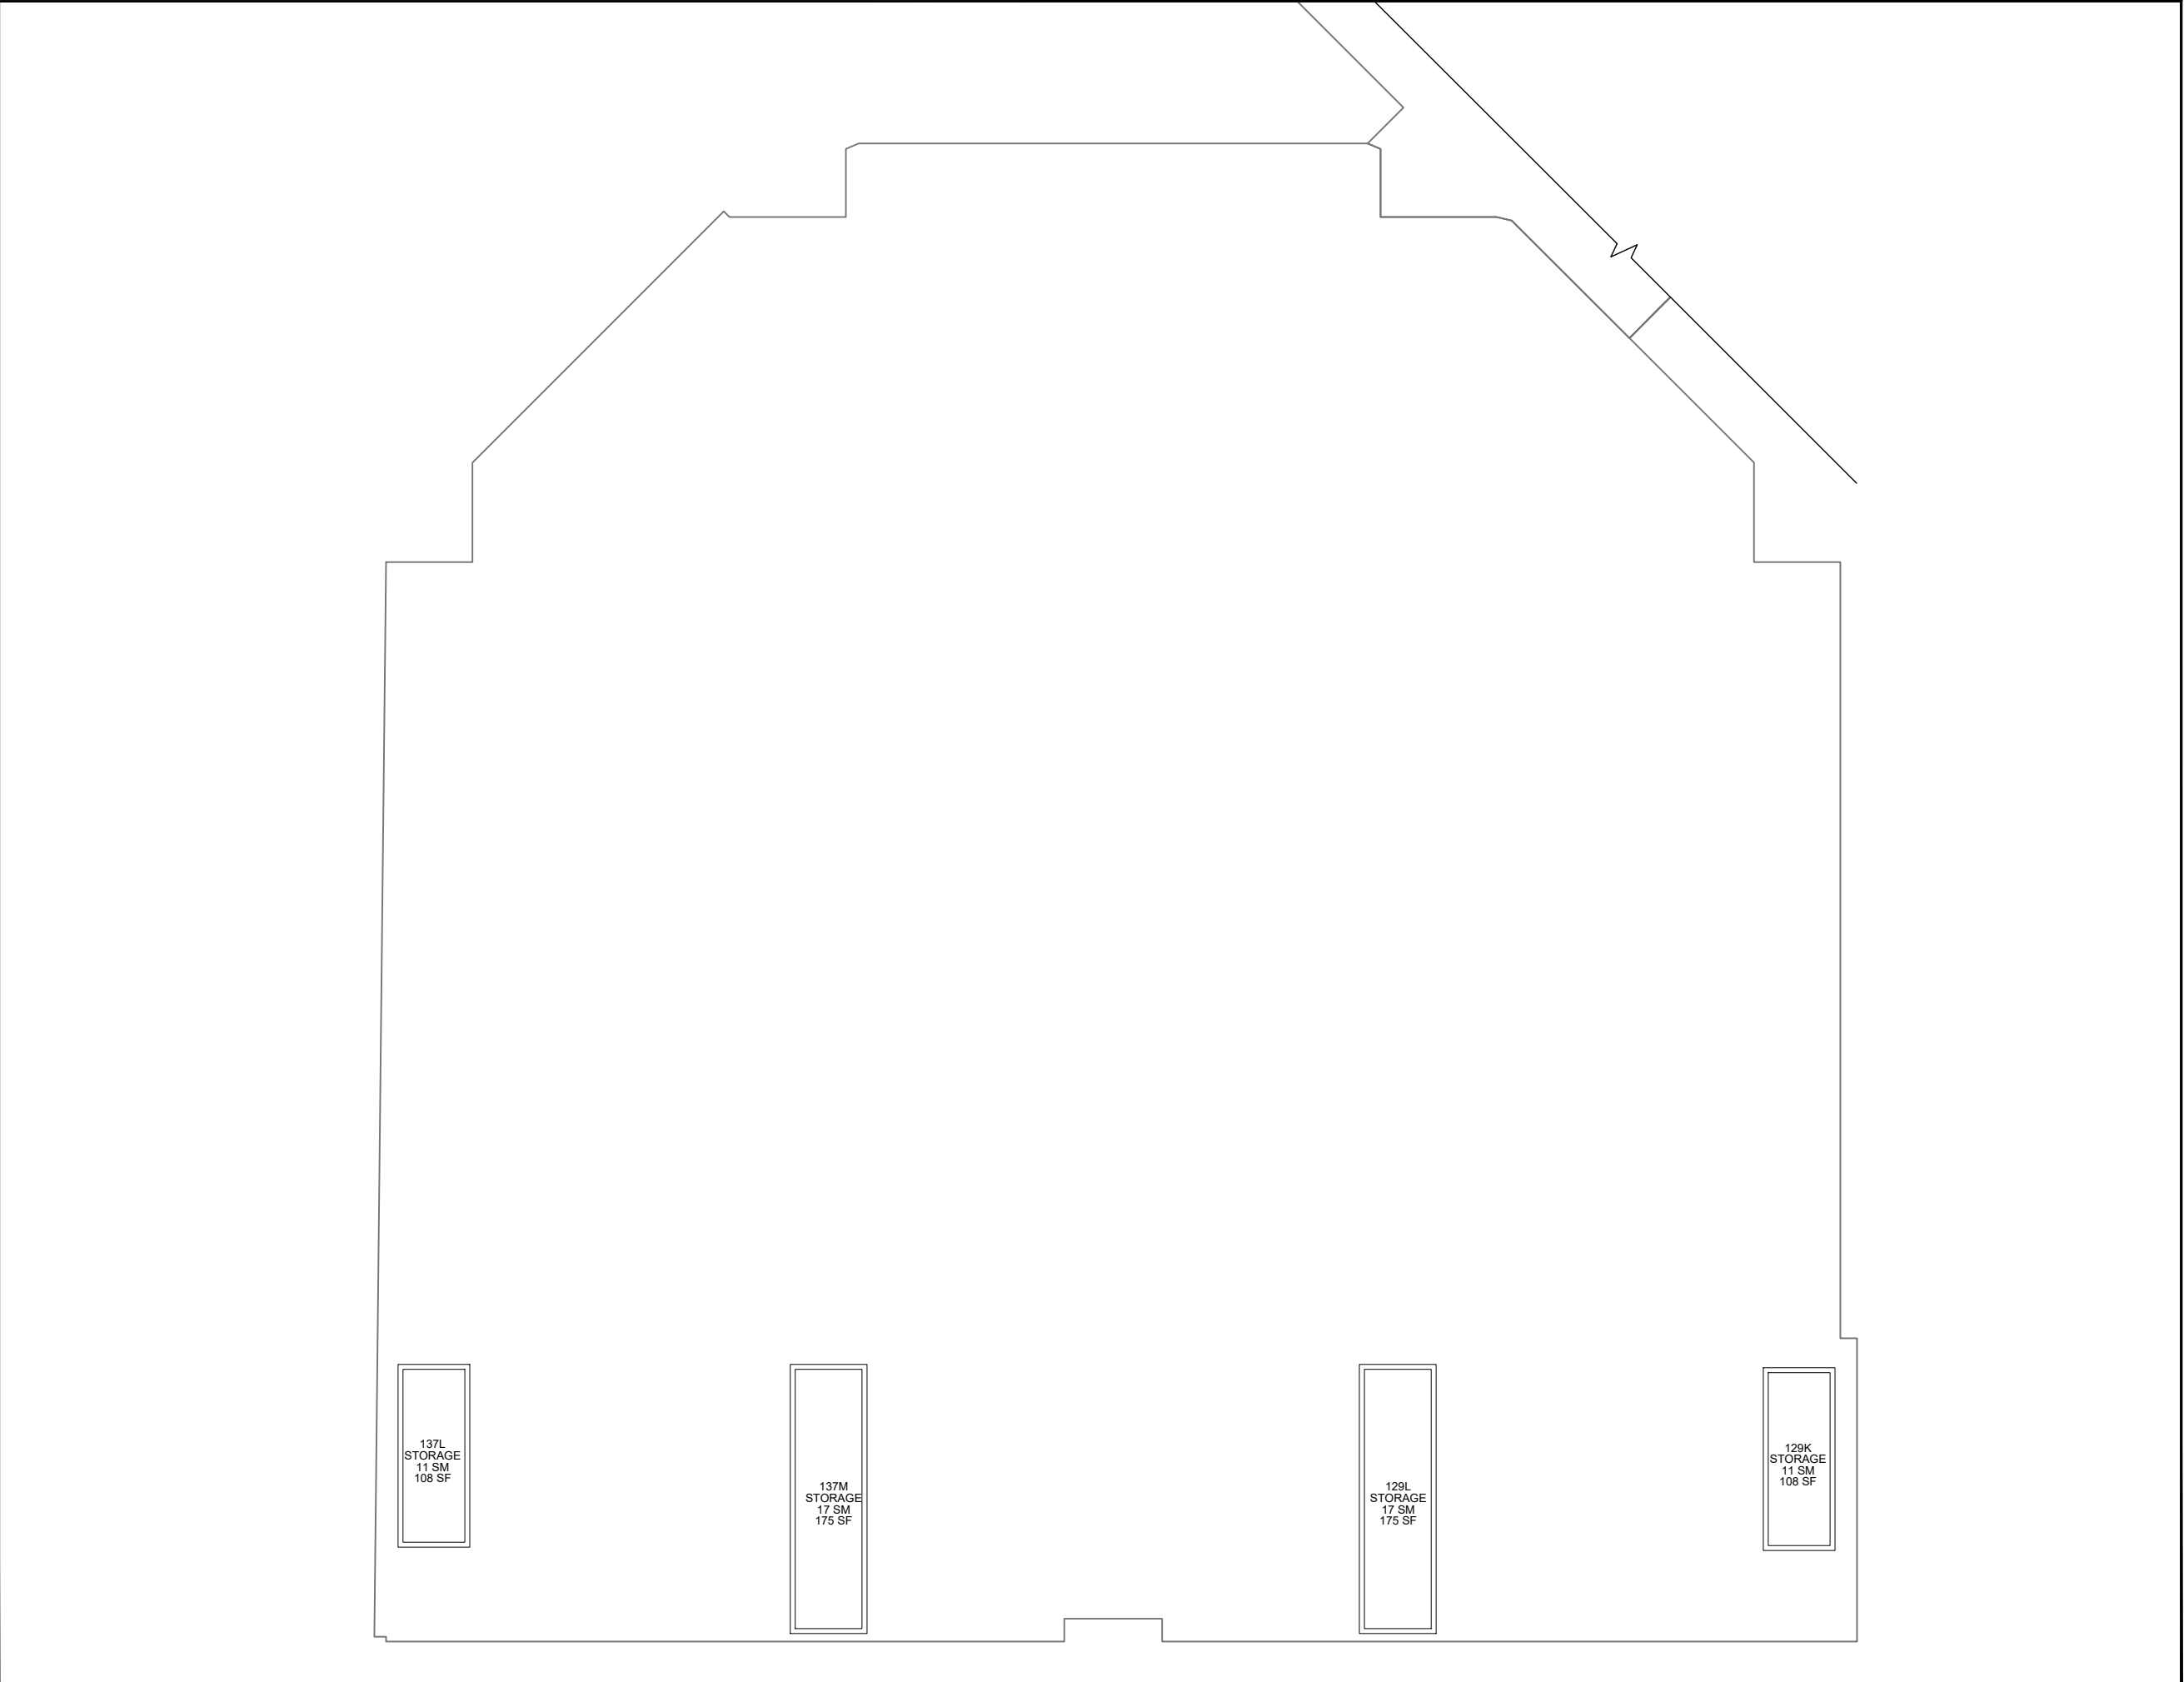

SYMBOL LEGEND	
	DOOR
	DRINKING FOUNTAIN
	SLIDING DOOR
	LAVATORY
	ACCORDION PARTITION
	SINK
	STACK OR FOLDING PARTITION
	TOILET
	WINDOW/GLAZING
	URINAL
	HIGH WINDOW
	LOCKER
	SKYLIGHT
	LAN DISTRIBUTION FRAME
	STOOP/STEP UP
	VENT HOOD
	STAIR
	WALL SHELVING
	RAMP
	UPPER CABINET
	ACCESS LADDER
	BASE CABINET
	COLD STORAGE
	TEACHER CABINET
	AREA CALCULATED @ 50 %
	MATCHLINE
	SLOPING ROOF
	FLAT ROOF

TITLEBLOCK LEGEND	
SHEET NAME:	BLDG #_FLOOR # (# IN SERIES)

KEY PLAN
NTS


Updated By:	FUS Review:	100% Submittal Date:
AA	MRS	01 APRIL 2020

DEPARTMENT OF DEFENSE EDUCATION ACTIVITY
FACILITY UTILIZATION SURVEY


NAPLES
MIDDLE/HIGH SCHOOL

BUILDING NUMBER: 2059
COUNTRY: ITALY
INSTALLATION: NAVAL SUPPORT ACTIVITY NAPLES
SITE: SUPPORT SITE
REGION-DISTRICT: DODEA EUROPE SOUTH


DoDAAC Number:	Floor:	Survey Date:
HE5509	LEVEL 2	JANUARY 2020
Sheet Name:	Sheet Seq:	
2059_2 (1)	19 of 21	

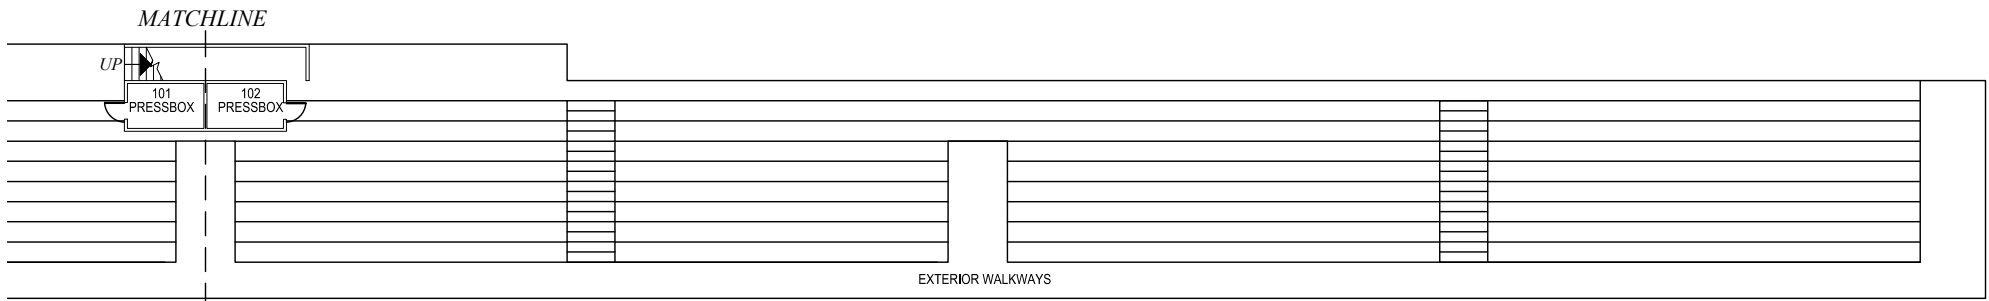

BUILDING 2061 - SECOND FLOOR

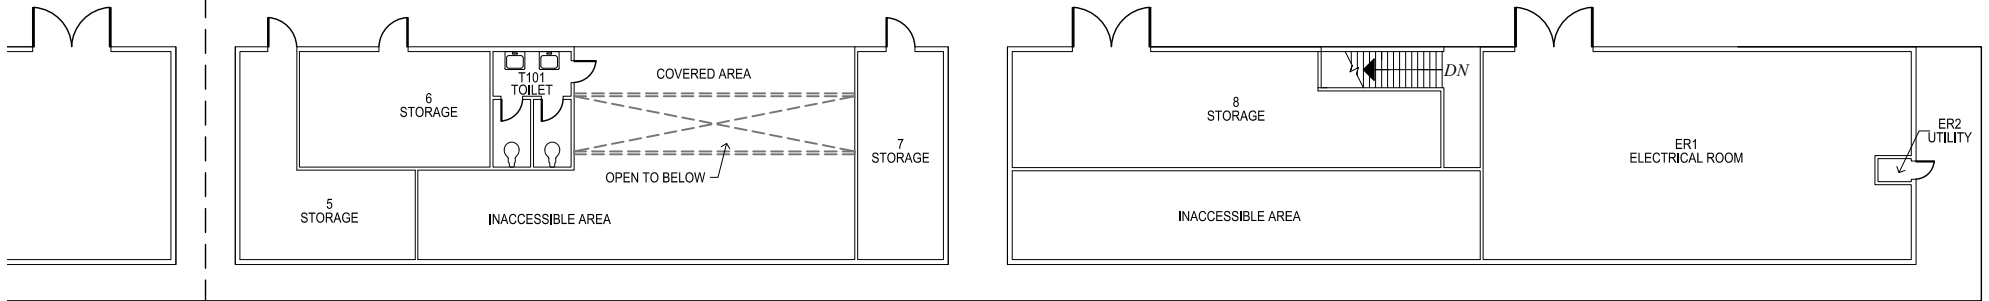


BUILDING 2061 - FIRST FLOOR

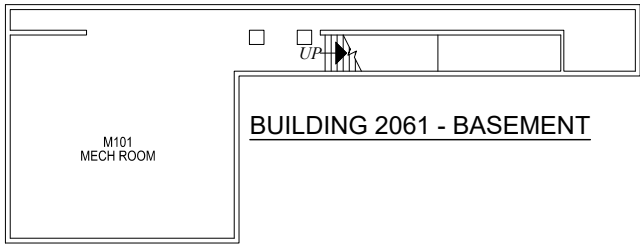


BUILDING 2061 - BASEMENT

SYMBOL LEGEND	
	DOOR
	DRINKING FOUNTAIN
	SLIDING DOOR
	LAVATORY
	ACCORDION PARTITION
	SINK
	STACK OR FOLDING PARTITION
	TOILET
	WINDOW/GLAZING
	URINAL
	HIGH WINDOW
	LOCKER
	SKYLIGHT
	LAN DISTRIBUTION FRAME
	STOOP/STEP UP
	VENT HOOD
	STAIR
	WALL SHELVING
	RAMP
	UPPER CABINET
	ACCESS LADDER
	BASE CABINET
	COLD STORAGE
	TEACHER CABINET
	AREA CALCULATED @ 50 %
	<i>MATCHLINE</i>
	SLOPING ROOF
	FLAT ROOF

TITLEBLOCK LEGEND	
<i>SHEET NAME:</i>	<i>BLDG #_FLOOR # (# IN SERIES)</i>

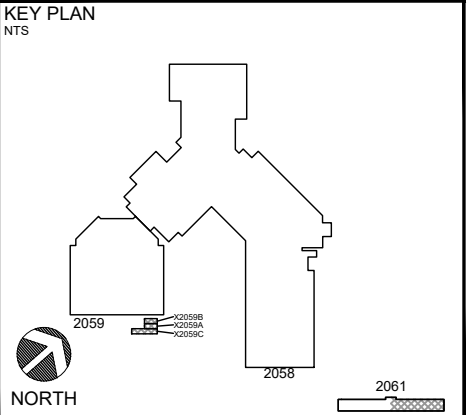


Updated By: AA	FUS Review: MRS	100% Submittal Date: 01 APRIL 2020
-------------------	--------------------	---------------------------------------

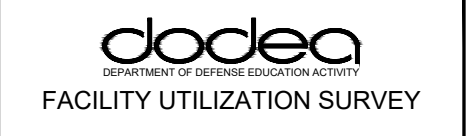


NAPLES MIDDLE/HIGH SCHOOL
BUILDING NUMBER: 2061, X2059A-C
COUNTRY: ITALY
INSTALLATION: NAVAL SUPPORT ACTIVITY NAPLES
SITE: SUPPORT SITE
REGION-DISTRICT: DODEA EUROPE SOUTH


DoDAAC Number: HE5509	Floor: LEVEL A-2	Survey Date: JANUARY 2020
Sheet Name: 2061 (1)	Sheet Seq: 20 of 21	

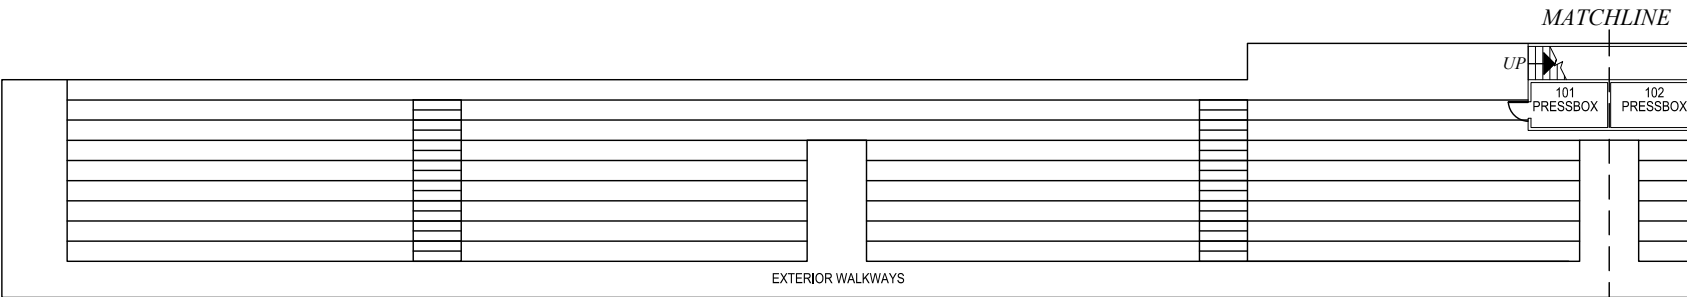

BUILDING 2061 - SECOND FLOOR

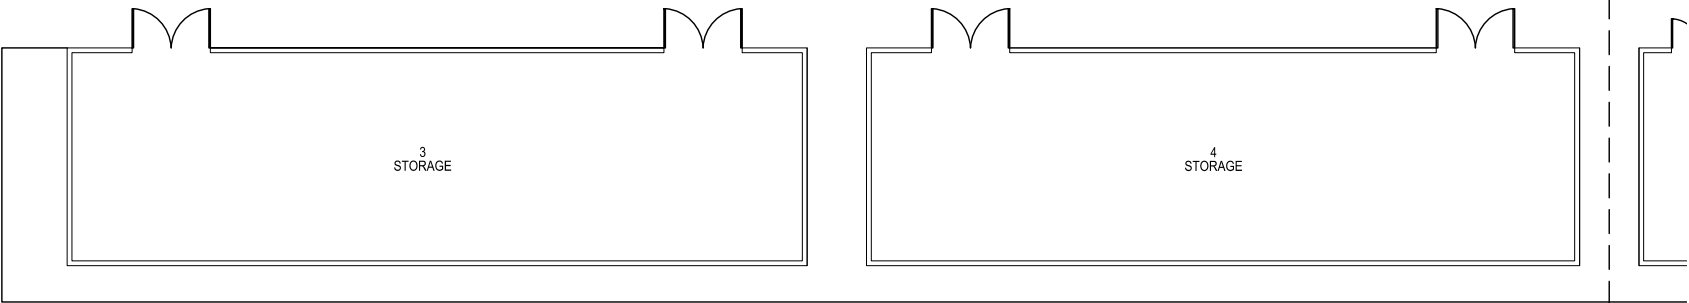


BUILDING 2061 - FIRST FLOOR

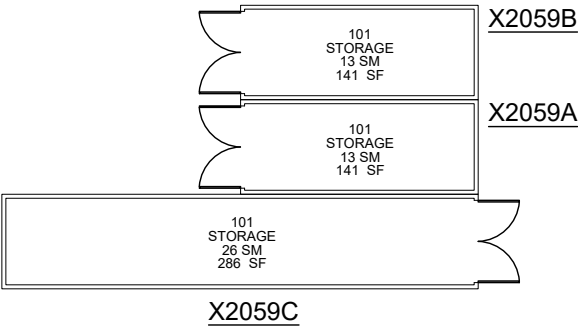

SYMBOL LEGEND	
	DOOR
	DRINKING FOUNTAIN
	SLIDING DOOR
	LAVATORY
	ACCORDION PARTITION
	SINK
	STACK OR FOLDING PARTITION
	TOILET
	WINDOW/GLAZING
	URINAL
	HIGH WINDOW
	LOCKER
	SKYLIGHT
	LAN DISTRIBUTION FRAME
	STOOP/STEP UP
	VENT HOOD
	STAIR
	WALL SHELVING
	RAMP
	UPPER CABINET
	ACCESS LADDER
	BASE CABINET
	COLD STORAGE
	TEACHER CABINET
	AREA CALCULATED @ 50 %
	MATCHLINE
	SLOPING ROOF
	FLAT ROOF

TITLEBLOCK LEGEND	
SHEET NAME:	BLDG #_FLOOR # (# IN SERIES)

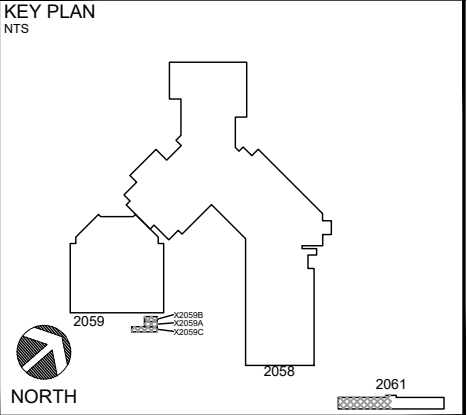

Updated By:	FUS Review:	100% Submittal Date:
AA	MRS	01 APRIL 2020
0 2 4 8 16 FT		

DEPARTMENT OF DEFENSE EDUCATION ACTIVITY
FACILITY UTILIZATION SURVEY

NAPLES MIDDLE/HIGH SCHOOL BUILDING NUMBER: 2061, X2059A-C COUNTRY: ITALY INSTALLATION: NAVAL SUPPORT ACTIVITY NAPLES SITE: SUPPORT SITE REGION-DISTRICT: DODEA EUROPE SOUTH		
DoDAAC Number: HE5509	Floor: LEVEL 1-2	Survey Date: JANUARY 2020
Sheet Name: 2061 (2)	Sheet Seq: 21 of 21	