


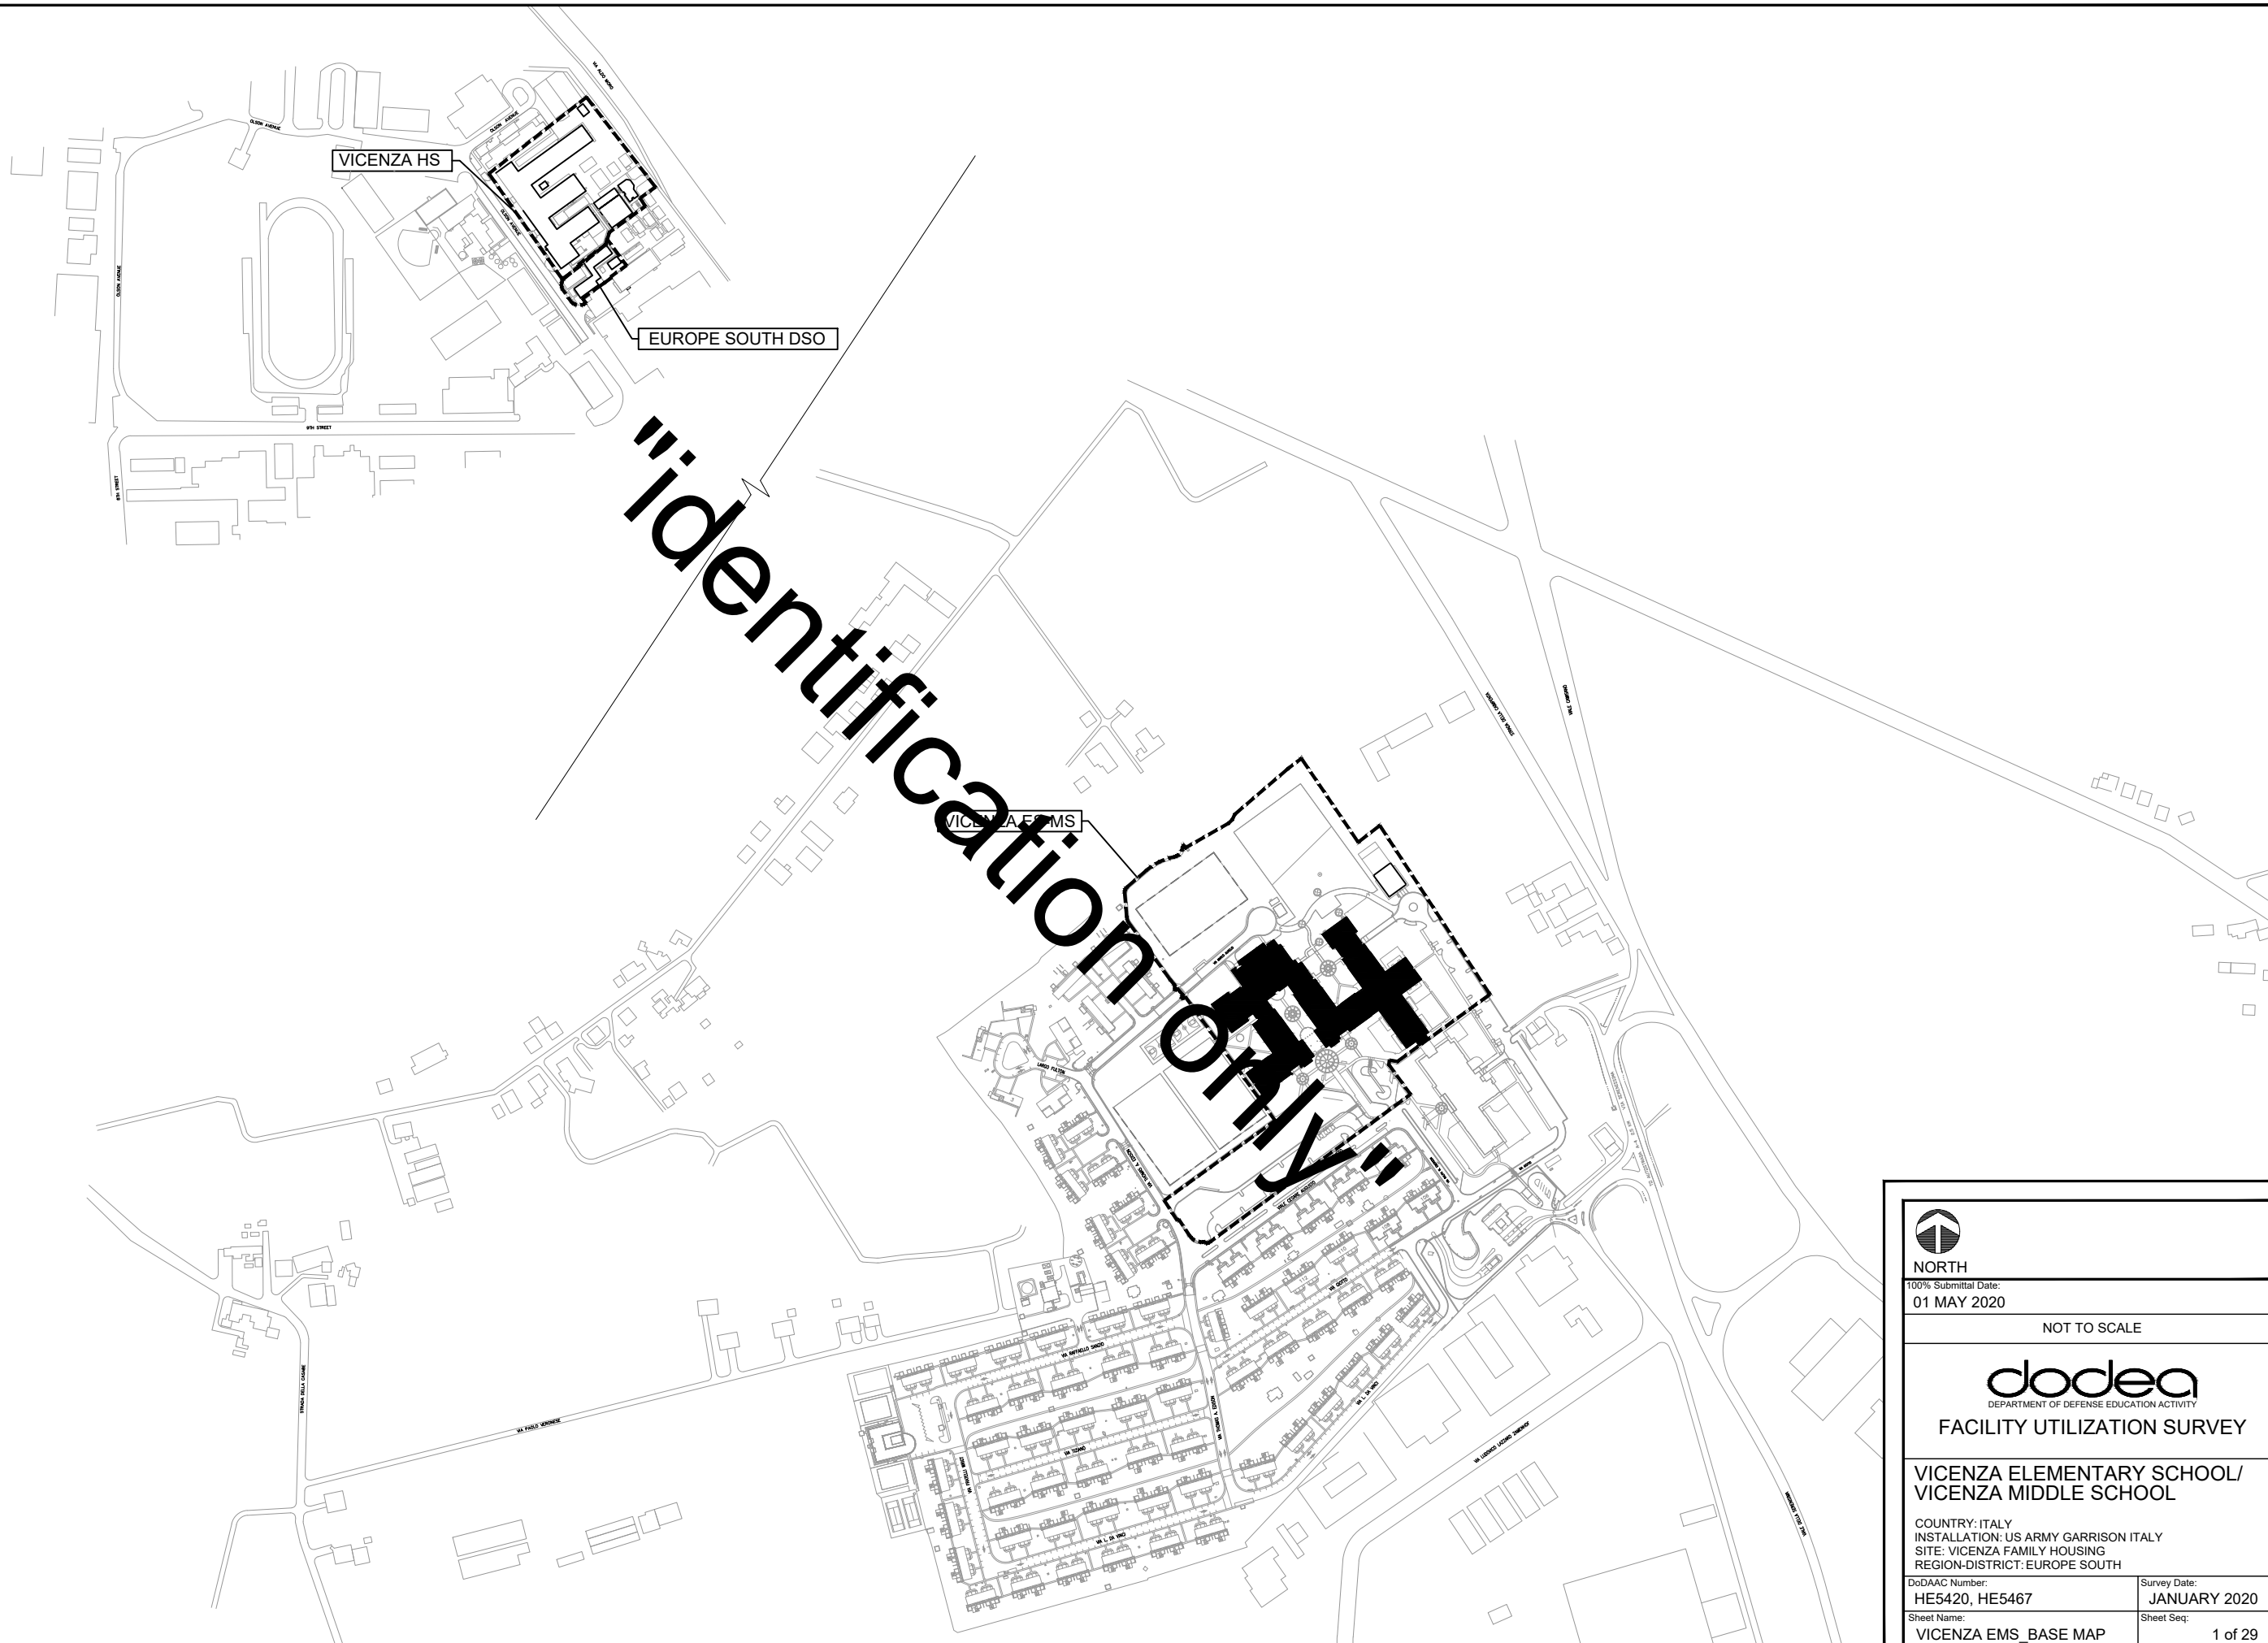

NORTH

100% Submittal Date:
01 MAY 2020

NOT TO SCALE



FACILITY UTILIZATION SURVEY

VICENZA ELEMENTARY SCHOOL/
VICENZA MIDDLE SCHOOL


COUNTRY: ITALY
INSTALLATION: US ARMY GARRISON ITALY
SITE: VICENZA FAMILY HOUSING
REGION-DISTRICT: EUROPE SOUTH

DoDAAC Number:
HE5420, HE5467

Survey Date:	JANUARY 2020
--------------	--------------

Sheet Name:
VICENZA EMS_BASE MAP



Sheet Seq: 1 of 29

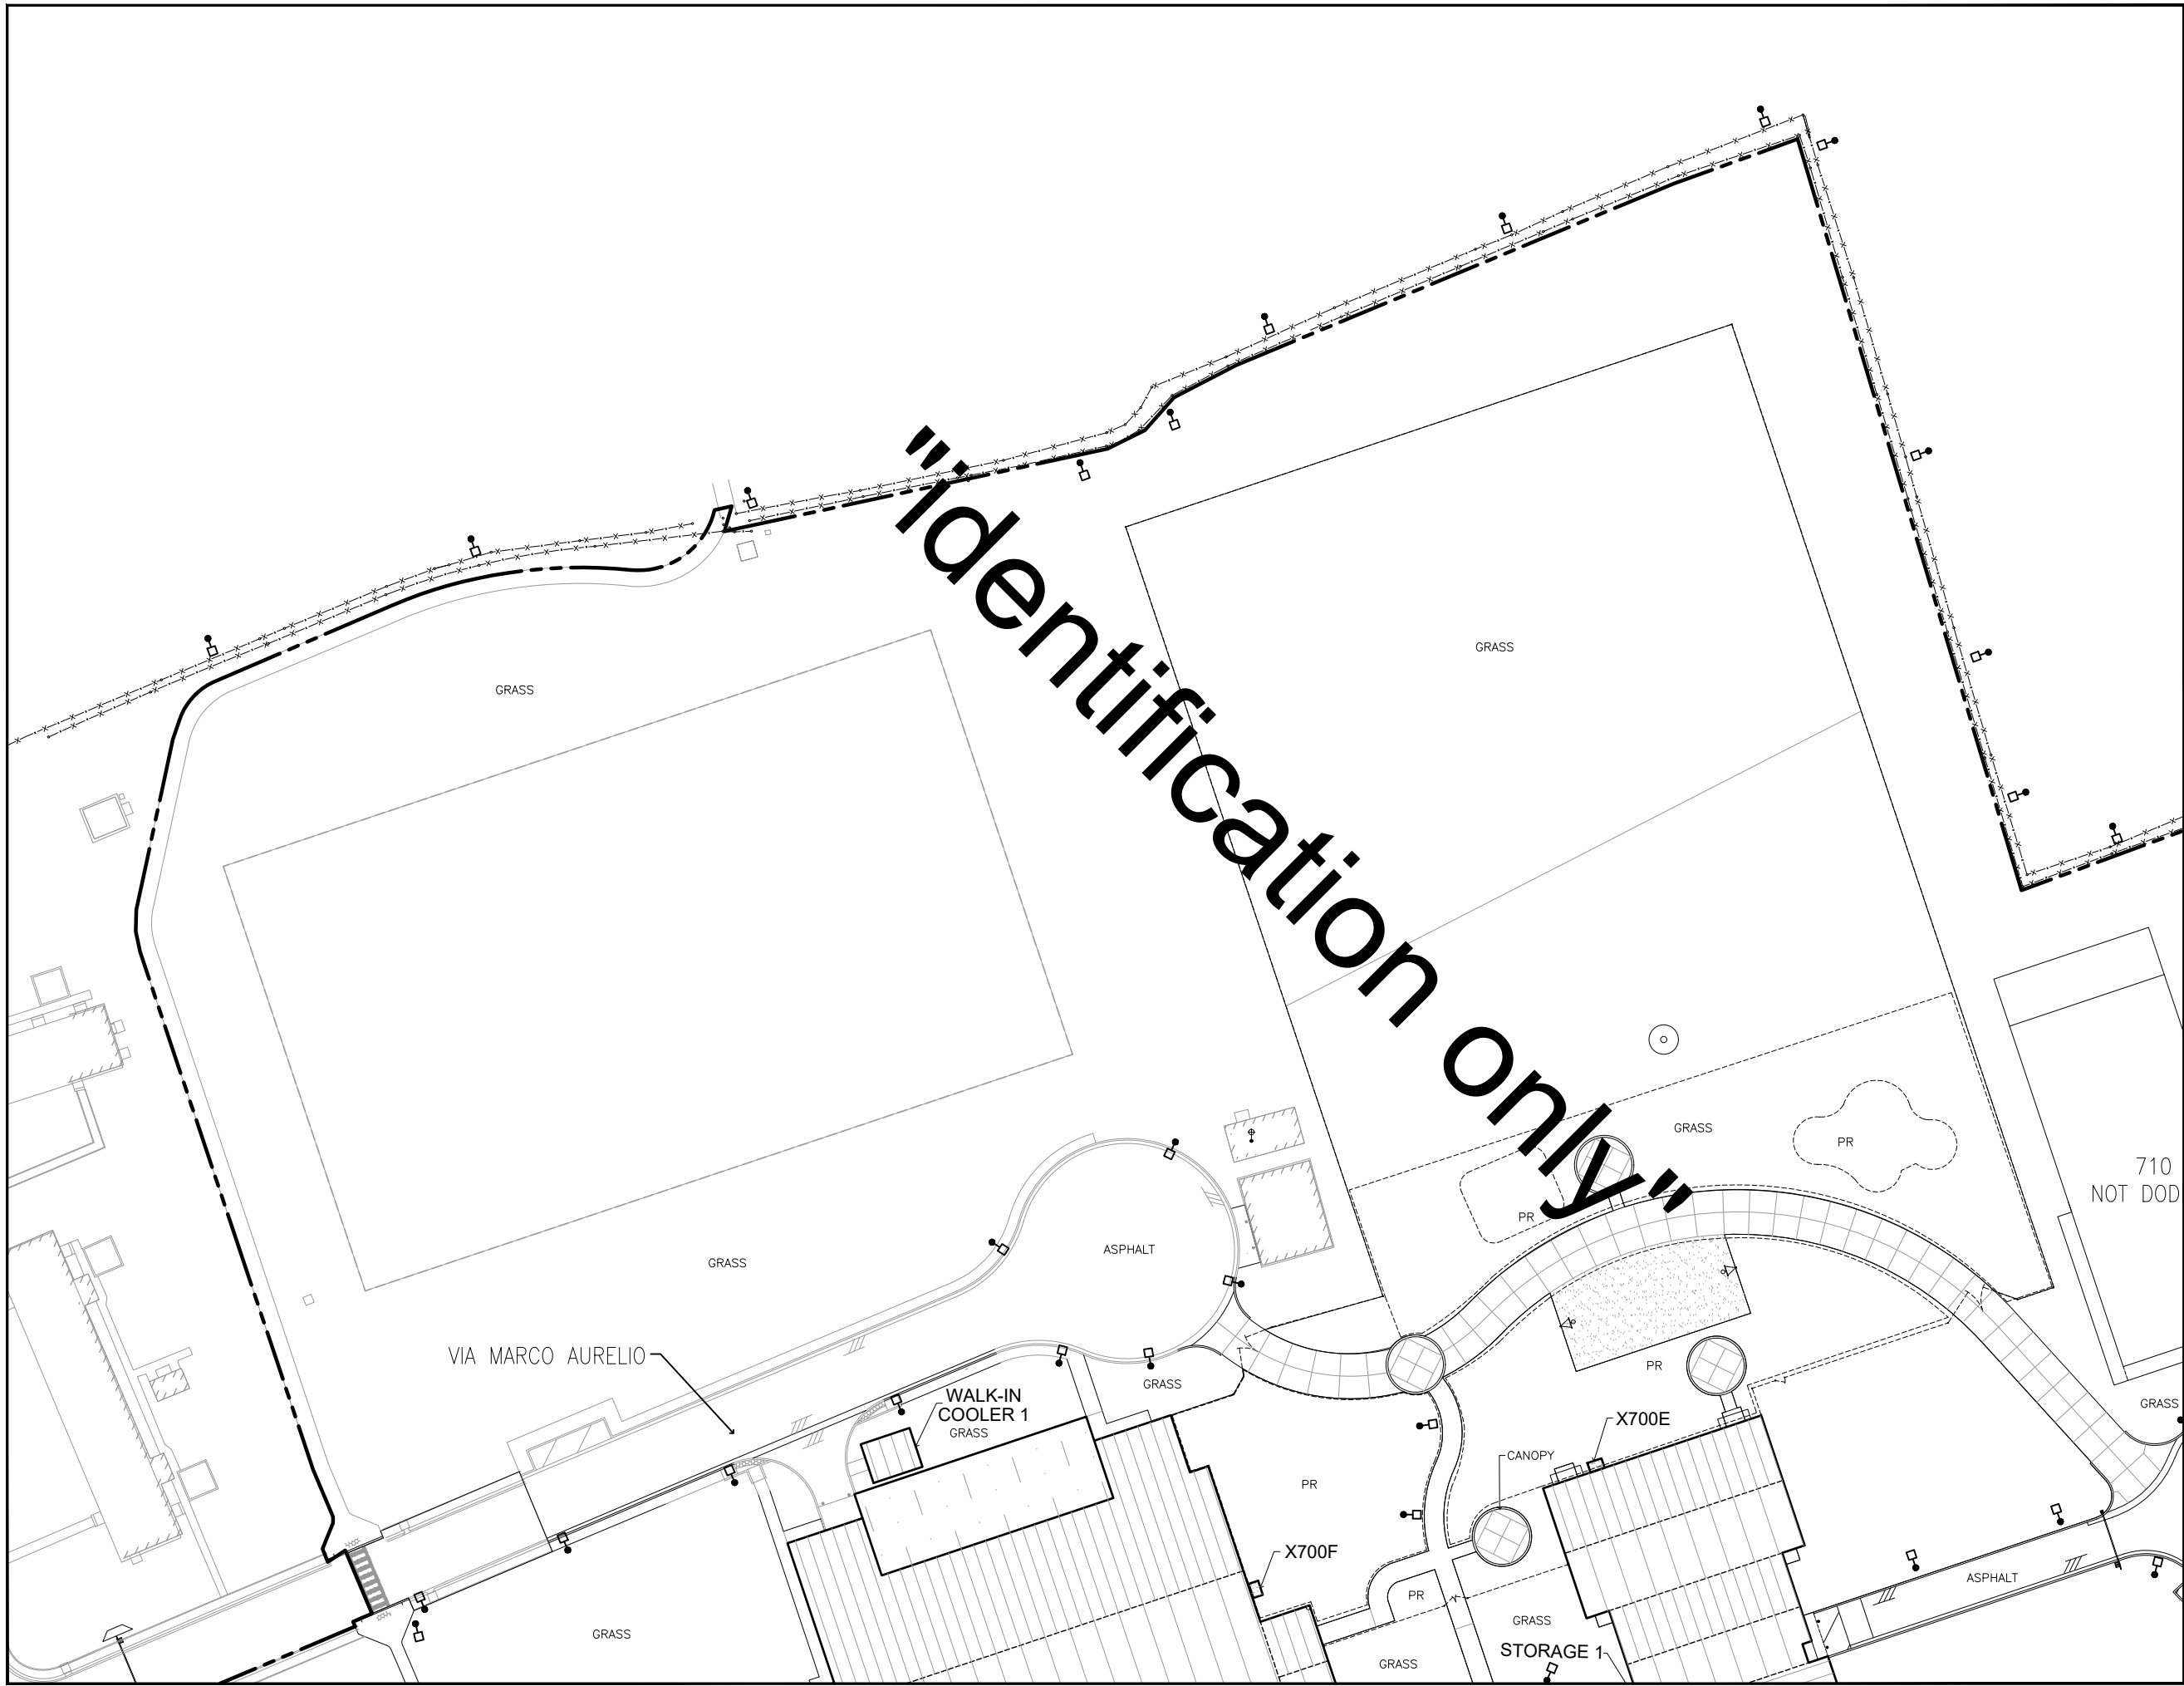

SYMBOL LEGEND	
	BASKETBALL GOAL
	AREA LIGHT
	STADIUM LIGHT
	FLAG POLE
	SIGN
	MONUMENT
	FOOTBALL GOAL
	SOCCER GOAL
	BASEBALL BACKSTOP
	MAIN ENTRY
	PARKING AREA
	CONCRETE
	FLAT ROOF
	PLAYGROUND
	SLOPE
	FIRE HYDRANT
	COVERED WALKWAY
	SLOPING ROOF
PROPERTY LINE (APPROX. 95,836 SM) (APPROX. 23.68 AC)	
FENCE LINE	


LEGEND	
PLAYGROUND SURFACING	
WC - WOOD CHIPS	PR - POURED RUBBER
M - MULCH	
SRT - SHREDDED RUBBER TIRES	S - SAND
PG - PEA GRAVEL	RT - RUBBER TILES

BUILDING LABEL	BLDG #_(# OF FLOORS)
----------------	----------------------

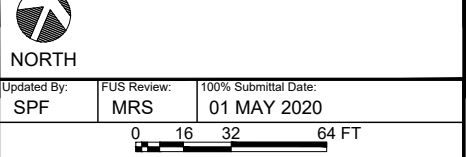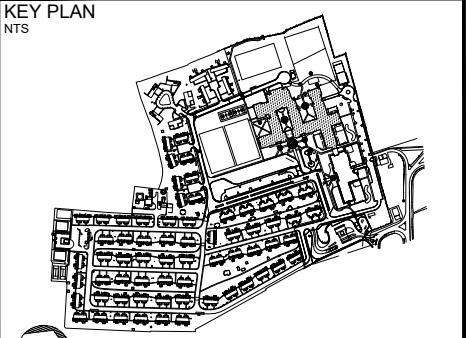


dodea
DEPARTMENT OF DEFENSE EDUCATION ACTIVITY
FACILITY UTILIZATION SURVEY


VICENZA ELEMENTARY SCHOOL/ VICENZA MIDDLE SCHOOL	
COUNTRY: ITALY INSTALLATION: US ARMY GARRISON ITALY SITE: VICENZA FAMILY HOUSING REGION-DISTRICT: DODEA EUROPE SOUTH	
DoDAAC Number: HE5420, HE5467	Survey Date: JANUARY 2020
Sheet Name: VICENZA EMS 32ND SC (1)	Sheet Seq: 3 of 29

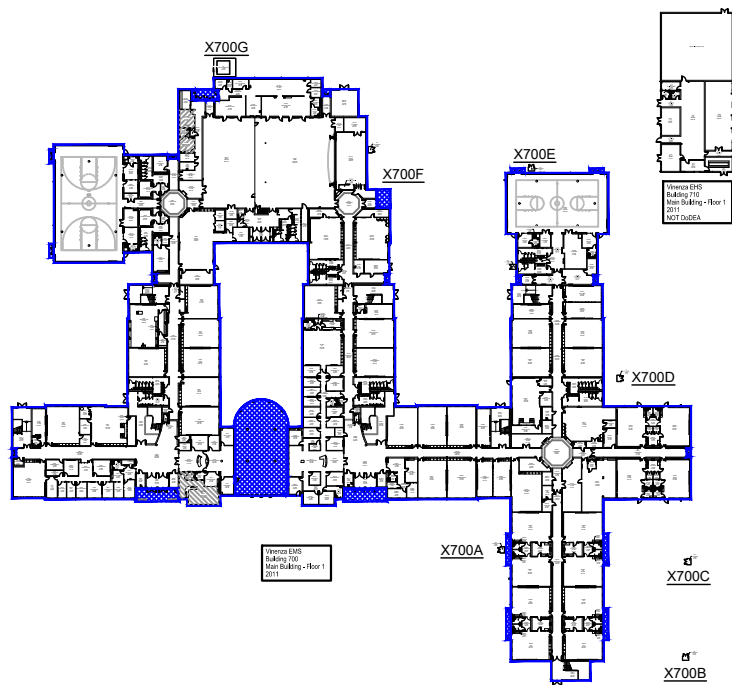

BUILDING 700 - FIRST FLOOR

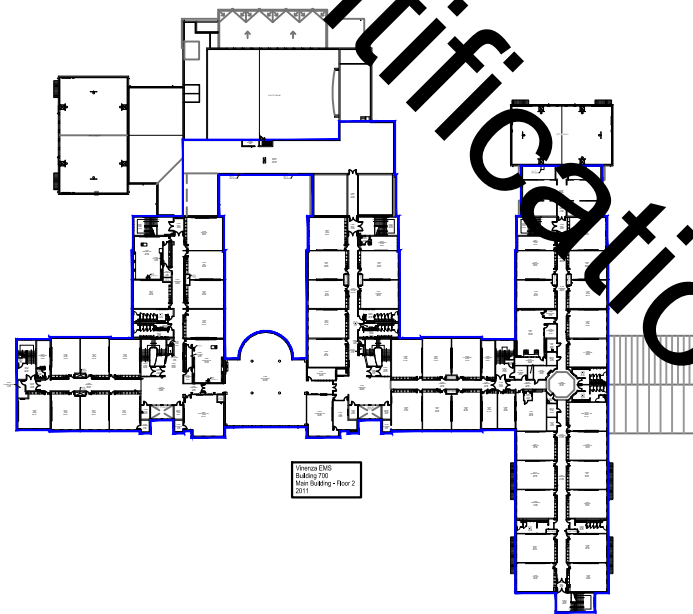

BUILDING 700 - SECOND FLOOR

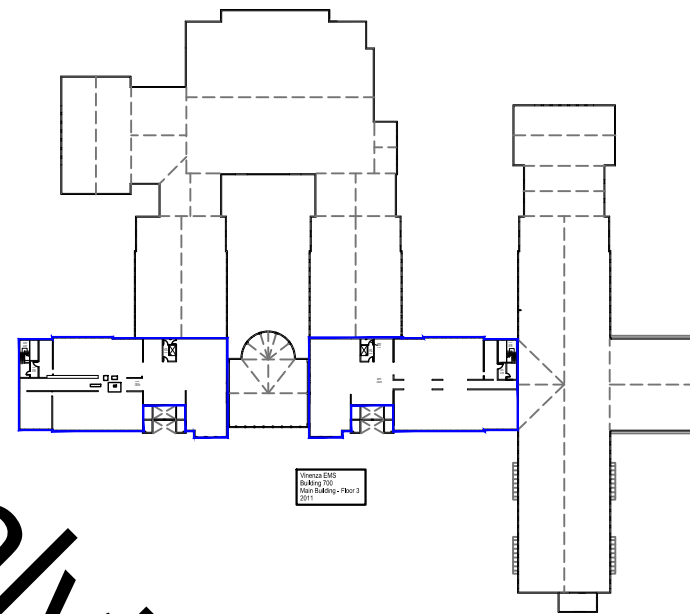

BUILDING 700 - THIRD FLOOR

GSF CALCULATIONS

Building 700	
Floor 1	135,737
Floor 2	96,792
Floor 3	30,207
Total Area (SF)	262,736
50% Area (SF)	131,368
Genie Area (SF)	267,825

NOTE 1: APPROXIMATELY 50% OF BUILDING 700 IS OCCUPIED BY VICENZA ELEMENTARY SCHOOL.
NOTE 2: APPROXIMATELY 1% OF BUILDING 700 IS OCCUPIED BY DODEA EUROPE SOUTH DSO.
NOTE 3: GSF CALCULATIONS BASED ON ARMY RPI DoA PAMPHLET 415-28.

DOOR

SLIDING DOOR

ACCORDION PARTITION

STACK OR FOLDING PARTITION

WINDOW/GLAZING

HIGH WINDOW

SKYLIGHT

STOOP/STEP UP

STAIR

RAMP

ACCESS LADDER

COLD STORAGE

AREA CALCULATED @ 50 %

SLOPING ROOF

DRINKING FOUNTAIN

LAVATORY

SINK

TOILET

URINAL

LOCKER

LAN DISTRIBUTION FRAME

VENT HOOD

WALL SHELVING

UPPER CABINET

BASE CABINET

TEACHER CABINET

MATCHLINE

FLAT ROOF

TITLEBLOCK LEGEND

SHEET NAME:

BLDG #_FLOOR # (# IN SERIES)

KEY PLAN

NTS

WALK-IN COOLER 1

STORAGE

710

700

X700A

X700B

X700C

X700D

X700E

X700F

NORTH

Updated By:SPF

FUS Review:MRS

100% Submittal Date:01 MAY 2020

NOT TO SCALE

dodea

DEPARTMENT OF DEFENSE EDUCATION ACTIVITY

FACILITY UTILIZATION SURVEY

VICENZA ELEMENTARY SCHOOL/
VICENZA MIDDLE SCHOOL

BUILDING NUMBER: 700, X700A-G

COUNTRY: ITALY

INSTALLATION: US ARMY GARRISON ITALY

SITE: VICENZA FAMILY HOUSING

REGION-DISTRICT: DODEA EUROPE SOUTH



DoDAAC Number:HE5420, HE5467

Floor:LEVEL 1-3


Survey Date:JANUARY 2020

Sheet Name:GSF_1 (1)

Sheet Seq:7 of 29

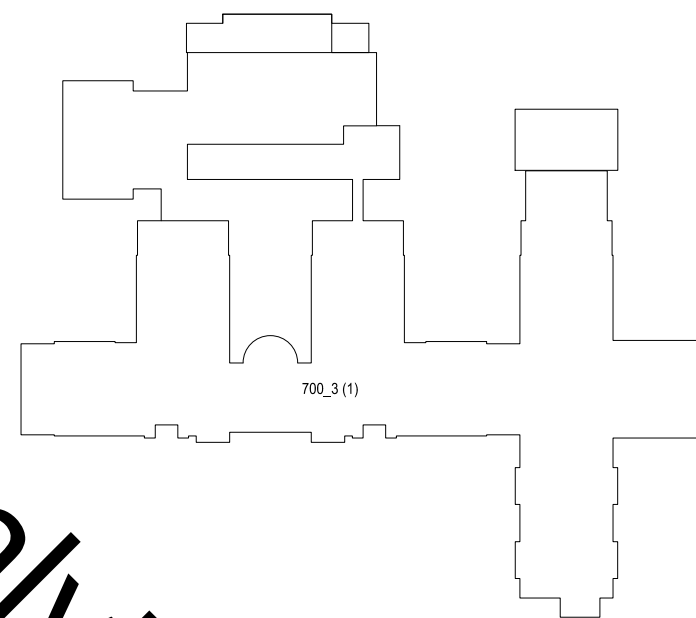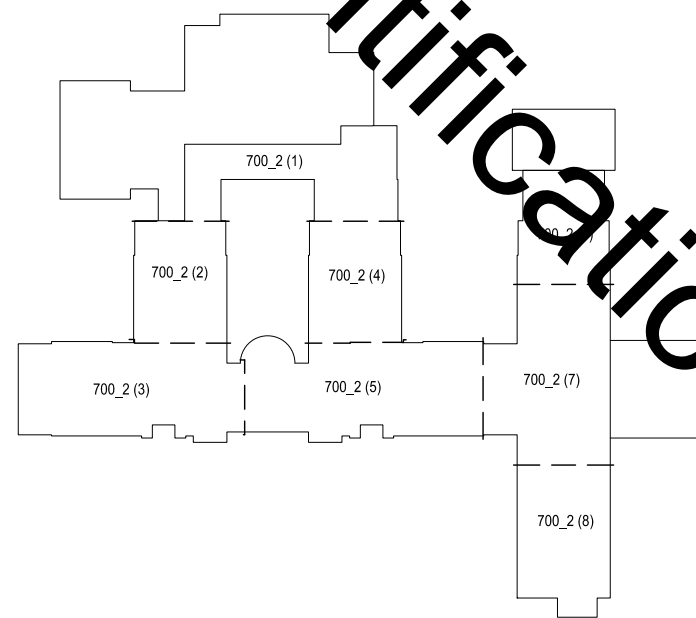

SYMBOL LEGEND		
	DOOR	DRINKING FOUNTAIN
	SLIDING DOOR	LAVATORY
	ACCORDION PARTITION	SINK
	STACK OR FOLDING PARTITION	TOILET
	WINDOW/GLAZING	URINAL
	HIGH WINDOW	LOCKER
	SKYLIGHT	LAN DISTRIBUTION FRAME
	STOOP/STEP UP	VENT HOOD
	STAIR	WALL SHELVING
	RAMP	UPPER CABINET
	ACCESS LADDER	BASE CABINET
	COLD STORAGE	TEACHER CABINET
	AREA CALCULATED @ 50 %	MATCHLINE
	SLOPING ROOF	FLAT ROOF
TITLEBLOCK LEGEND		
SHEET NAME:		BLDG #_FLOOR # (# IN SERIES)
KEY PLAN		
NTS		
The key plan shows a complex building footprint divided into several sections. A hatched area covers most of the footprint. Labels include 'WALK-IN COOLER 1' at the top left, 'X700F' and 'X700E' on the upper right, 'STORAGE 1' in the center, 'X700D' on the lower right, '700' and 'X700A' along the bottom edge, and 'X700C' and 'X700B' on the far right. A separate rectangular section labeled '710' is shown above the main footprint. A north arrow points towards the top-left.		
Updated By: SPF	FUS Review: MRS	100% Submittal Date: 01 MAY 2020
NOT TO SCALE		
 DEPARTMENT OF DEFENSE EDUCATION ACTIVITY FACILITY UTILIZATION SURVEY		
VICENZA ELEMENTARY SCHOOL/ VICENZA MIDDLE SCHOOL		
BUILDING NUMBER: 700, X700A-G		
COUNTRY: ITALY		
INSTALLATION: US ARMY GARRISON ITALY		
SITE: VICENZA FAMILY HOUSING		
REGION-DISTRICT: DODECA EUROPE SOUTH		
DODAAC Number: HE5420, HE5467	Floor: LEVEL 1-3	Survey Date: JANUARY 2020
Sheet Name: KEYPLAN		Sheet Seq: 9 of 29

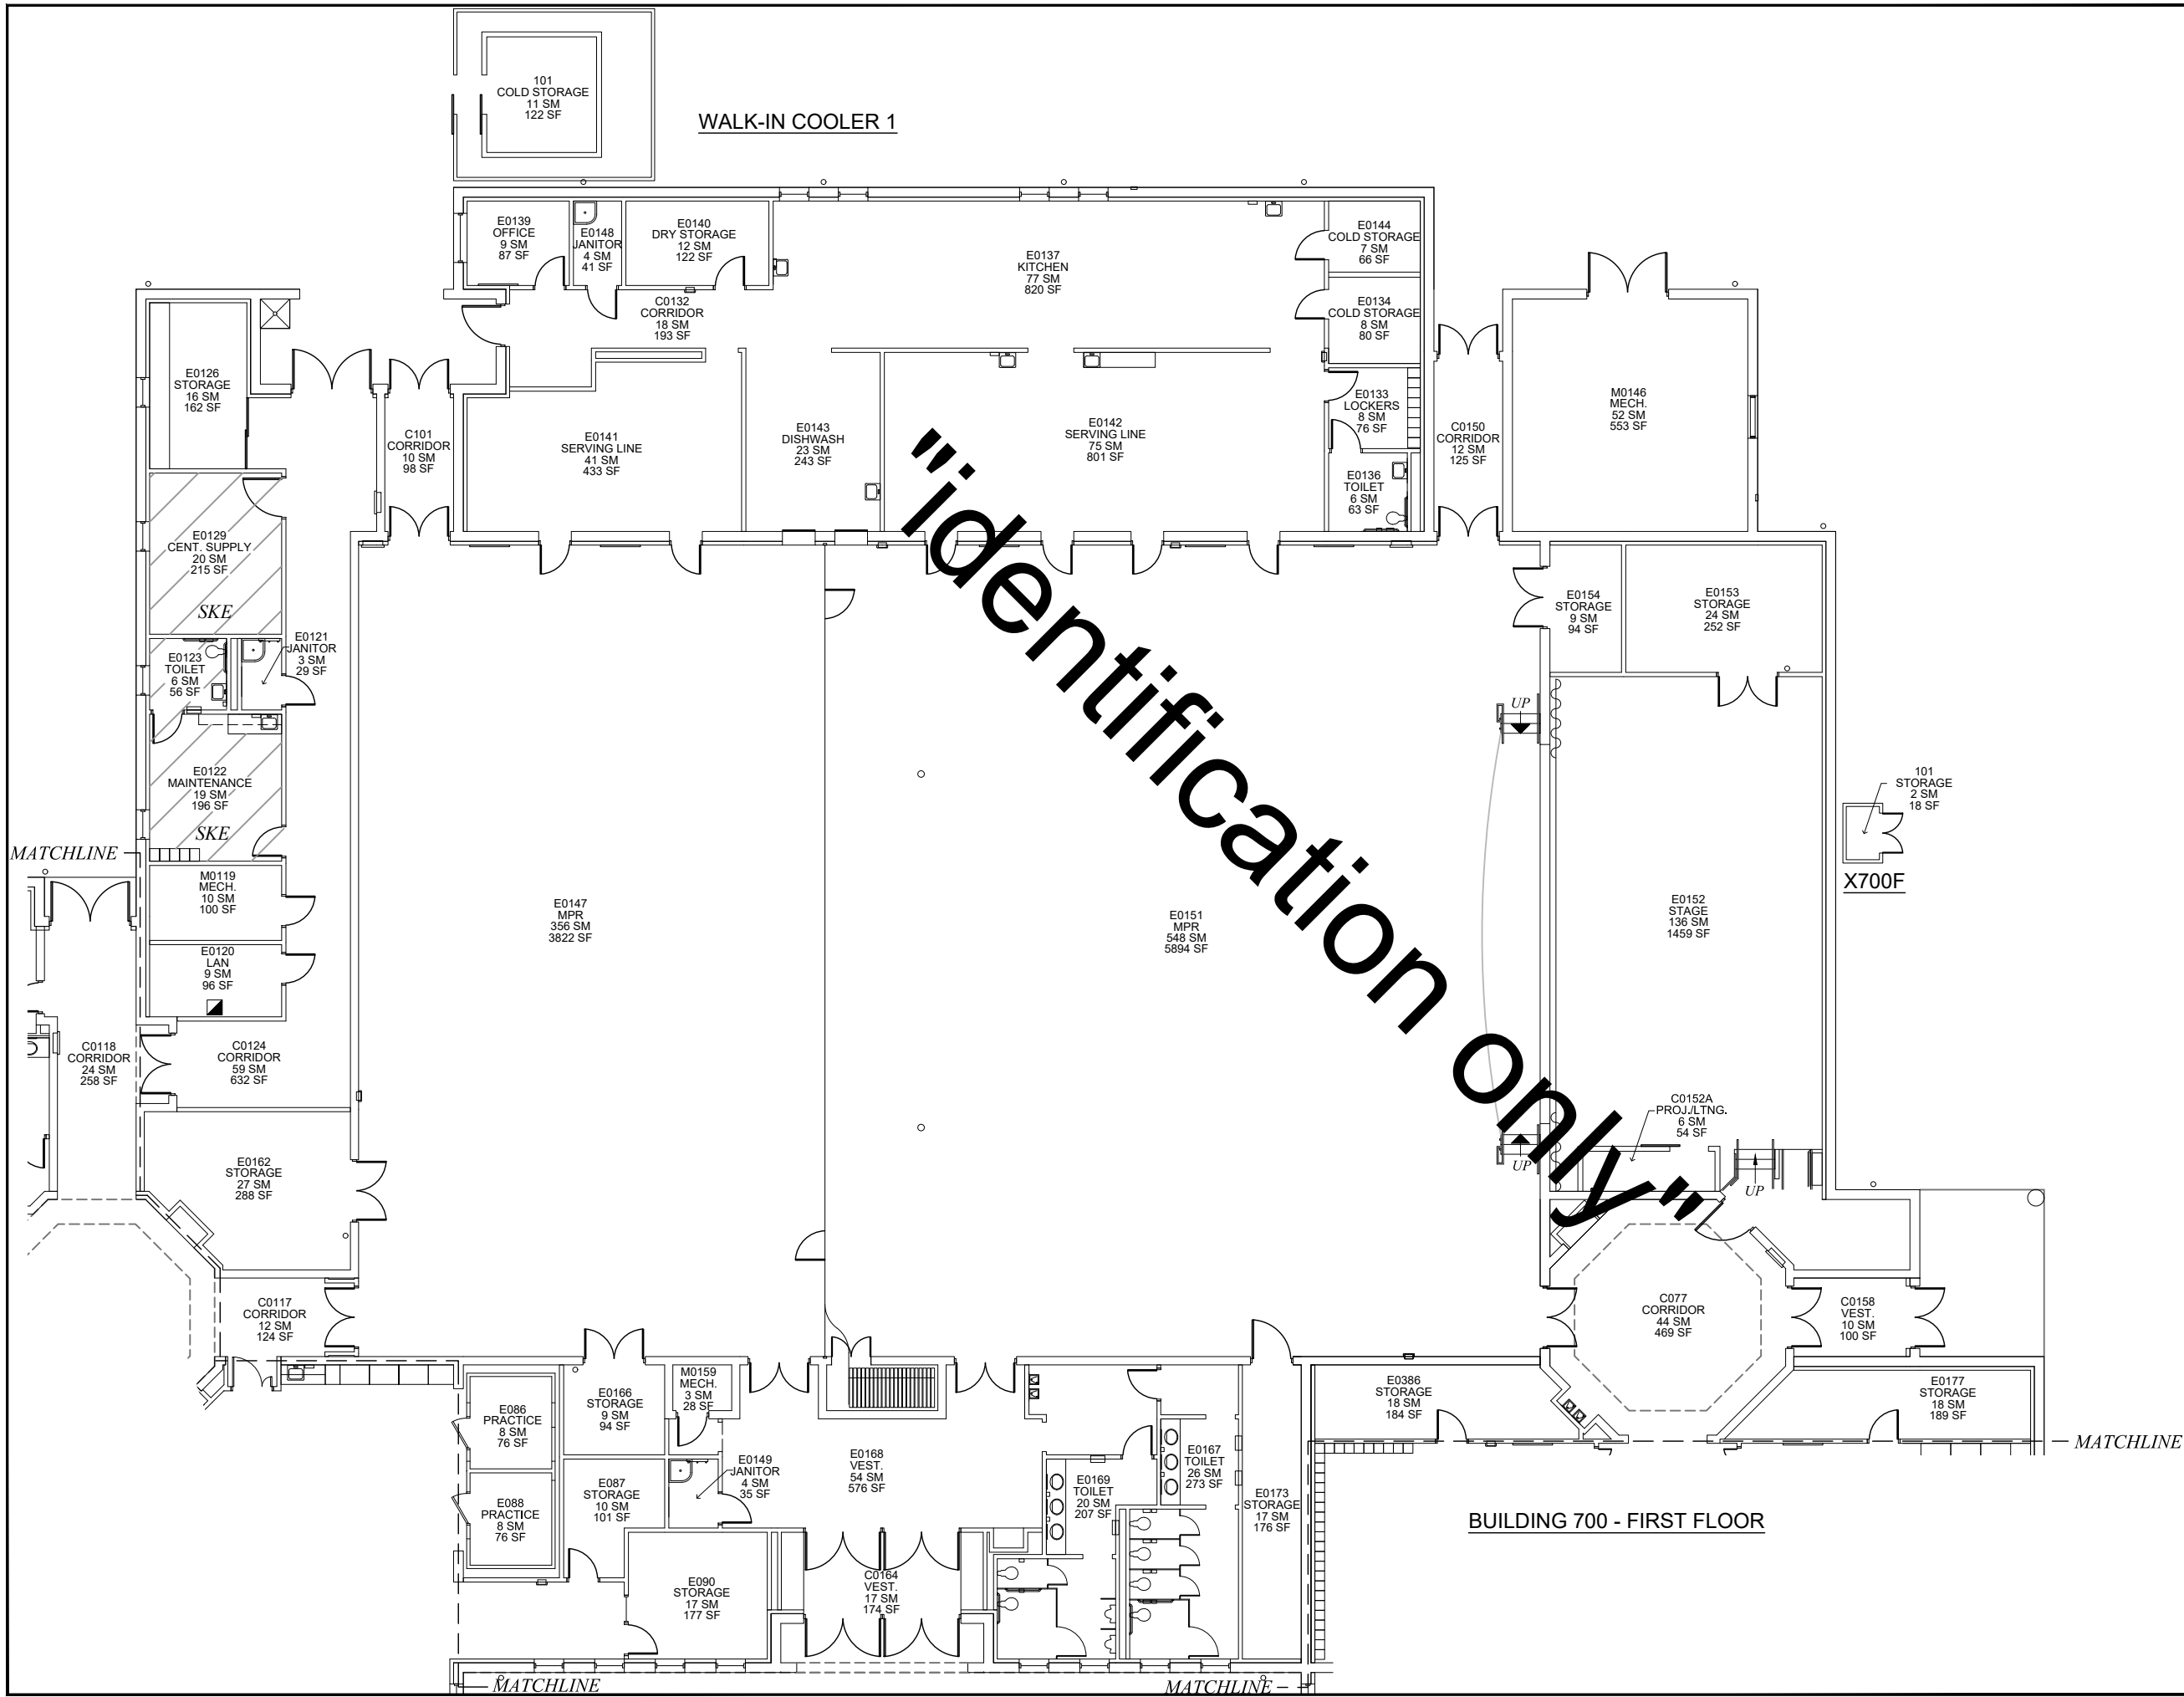

DOOR

SLIDING DOOR

ACCORDION PARTITION

STACK OR FOLDING PARTITION

WINDOW/GLAZING

HIGH WINDOW

SKYLIGHT

STOOP/STEP UP

STAIR

RAMP

ACCESS LADDER

COLD STORAGE

AREA CALCULATED @ 50 %

SLOPING ROOF

DRINKING FOUNTAIN

LAVATORY

SINK

TOILET

URINAL

LOCKER

LAN DISTRIBUTION FRAME

VENT HOOD

WALL SHELVING

UPPER CABINET

BASE CABINET

TEACHER CABINET

MATCHLINE

FLAT ROOF

TITLEBLOCK LEGEND

SHEET NAME:

BLDG #_FLOOR # (# IN SERIES)

KEY PLAN

NTS

NORTH

Updated By: SPF

FUS Review: MRS

100% Submittal Date: 01 MAY 2020

0 2 4 8 16 FT

dodea

DEPARTMENT OF DEFENSE EDUCATION ACTIVITY

FACILITY UTILIZATION SURVEY

VICENZA ELEMENTARY SCHOOL/

VICENZA MIDDLE SCHOOL

BUILDING NUMBER: 700, X700F, WALK-IN COOLER 1

COUNTRY: ITALY

INSTALLATION: US ARMY GARRISON ITALY

SITE: VICENZA FAMILY HOUSING

REGION-DISTRICT: DODEA EUROPE SOUTH


DoDAAC Number: HE5420, HE5467

Floor: LEVEL 1

Survey Date: JANUARY 2020


Sheet Name: 700_1 (1)

Sheet Seq: 10 of 29

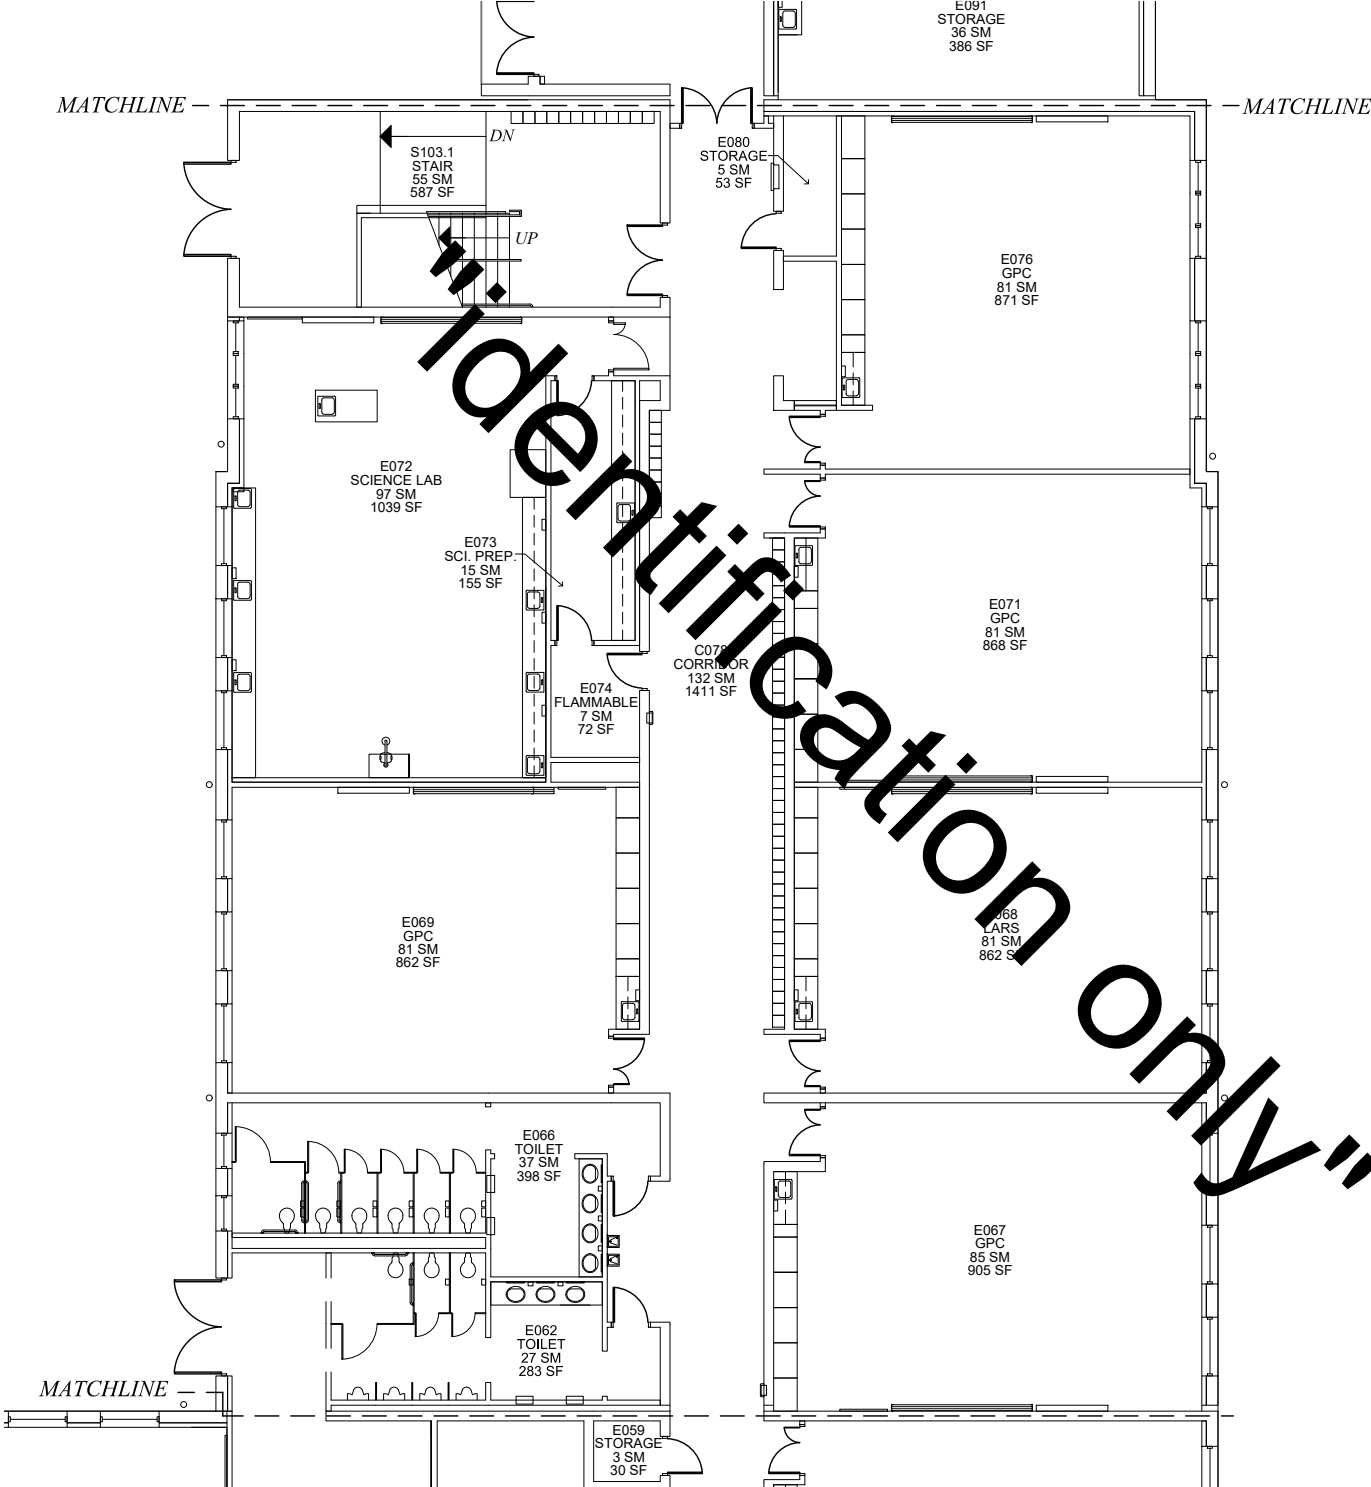


SYMBOL LEGEND	
	DOOR
	DRINKING FOUNTAIN
	SLIDING DOOR
	LAVATORY
	ACCORDION PARTITION
	SINK
	STACK OR FOLDING PARTITION
	TOILET
	WINDOW/GLAZING
	URINAL
	HIGH WINDOW
	LOCKER
	SKYLIGHT
	LAN DISTRIBUTION FRAME
	STOOP/STEP UP
	VENT HOOD
	STAIR
	WALL SHELVING
	RAMP
	UPPER CABINET
	ACCESS LADDER
	BASE CABINET
	COLD STORAGE
	TEACHER CABINET
	AREA CALCULATED @ 50 %
	SLOPING ROOF
	FLAT ROOF

TITLEBLOCK LEGEND	
SHEET NAME:	BLDG #_FLOOR # (# IN SERIES)

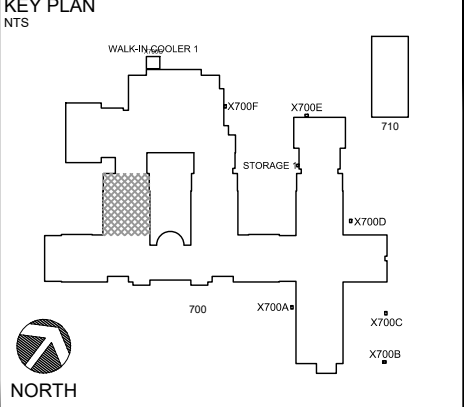

Updated By:	FUS Review:	100% Submittal Date:
SPF	MRS	01 MAY 2020
0 2 4 8 16 FT		
DEPARTMENT OF DEFENSE EDUCATION ACTIVITY		
FACILITY UTILIZATION SURVEY		
VICENZA ELEMENTARY SCHOOL/ VICENZA MIDDLE SCHOOL		
BUILDING NUMBER: 700		
COUNTRY: ITALY		
INSTALLATION: US ARMY GARRISON ITALY		
SITE: VICENZA FAMILY HOUSING		
REGION-DISTRICT: DODEA EUROPE SOUTH		
DoDAAC Number:	Floor:	Survey Date:
HE5420, HE5467	LEVEL 1	JANUARY 2020
Sheet Name:	Sheet Seq:	
700_1 (3)	12 of 29	

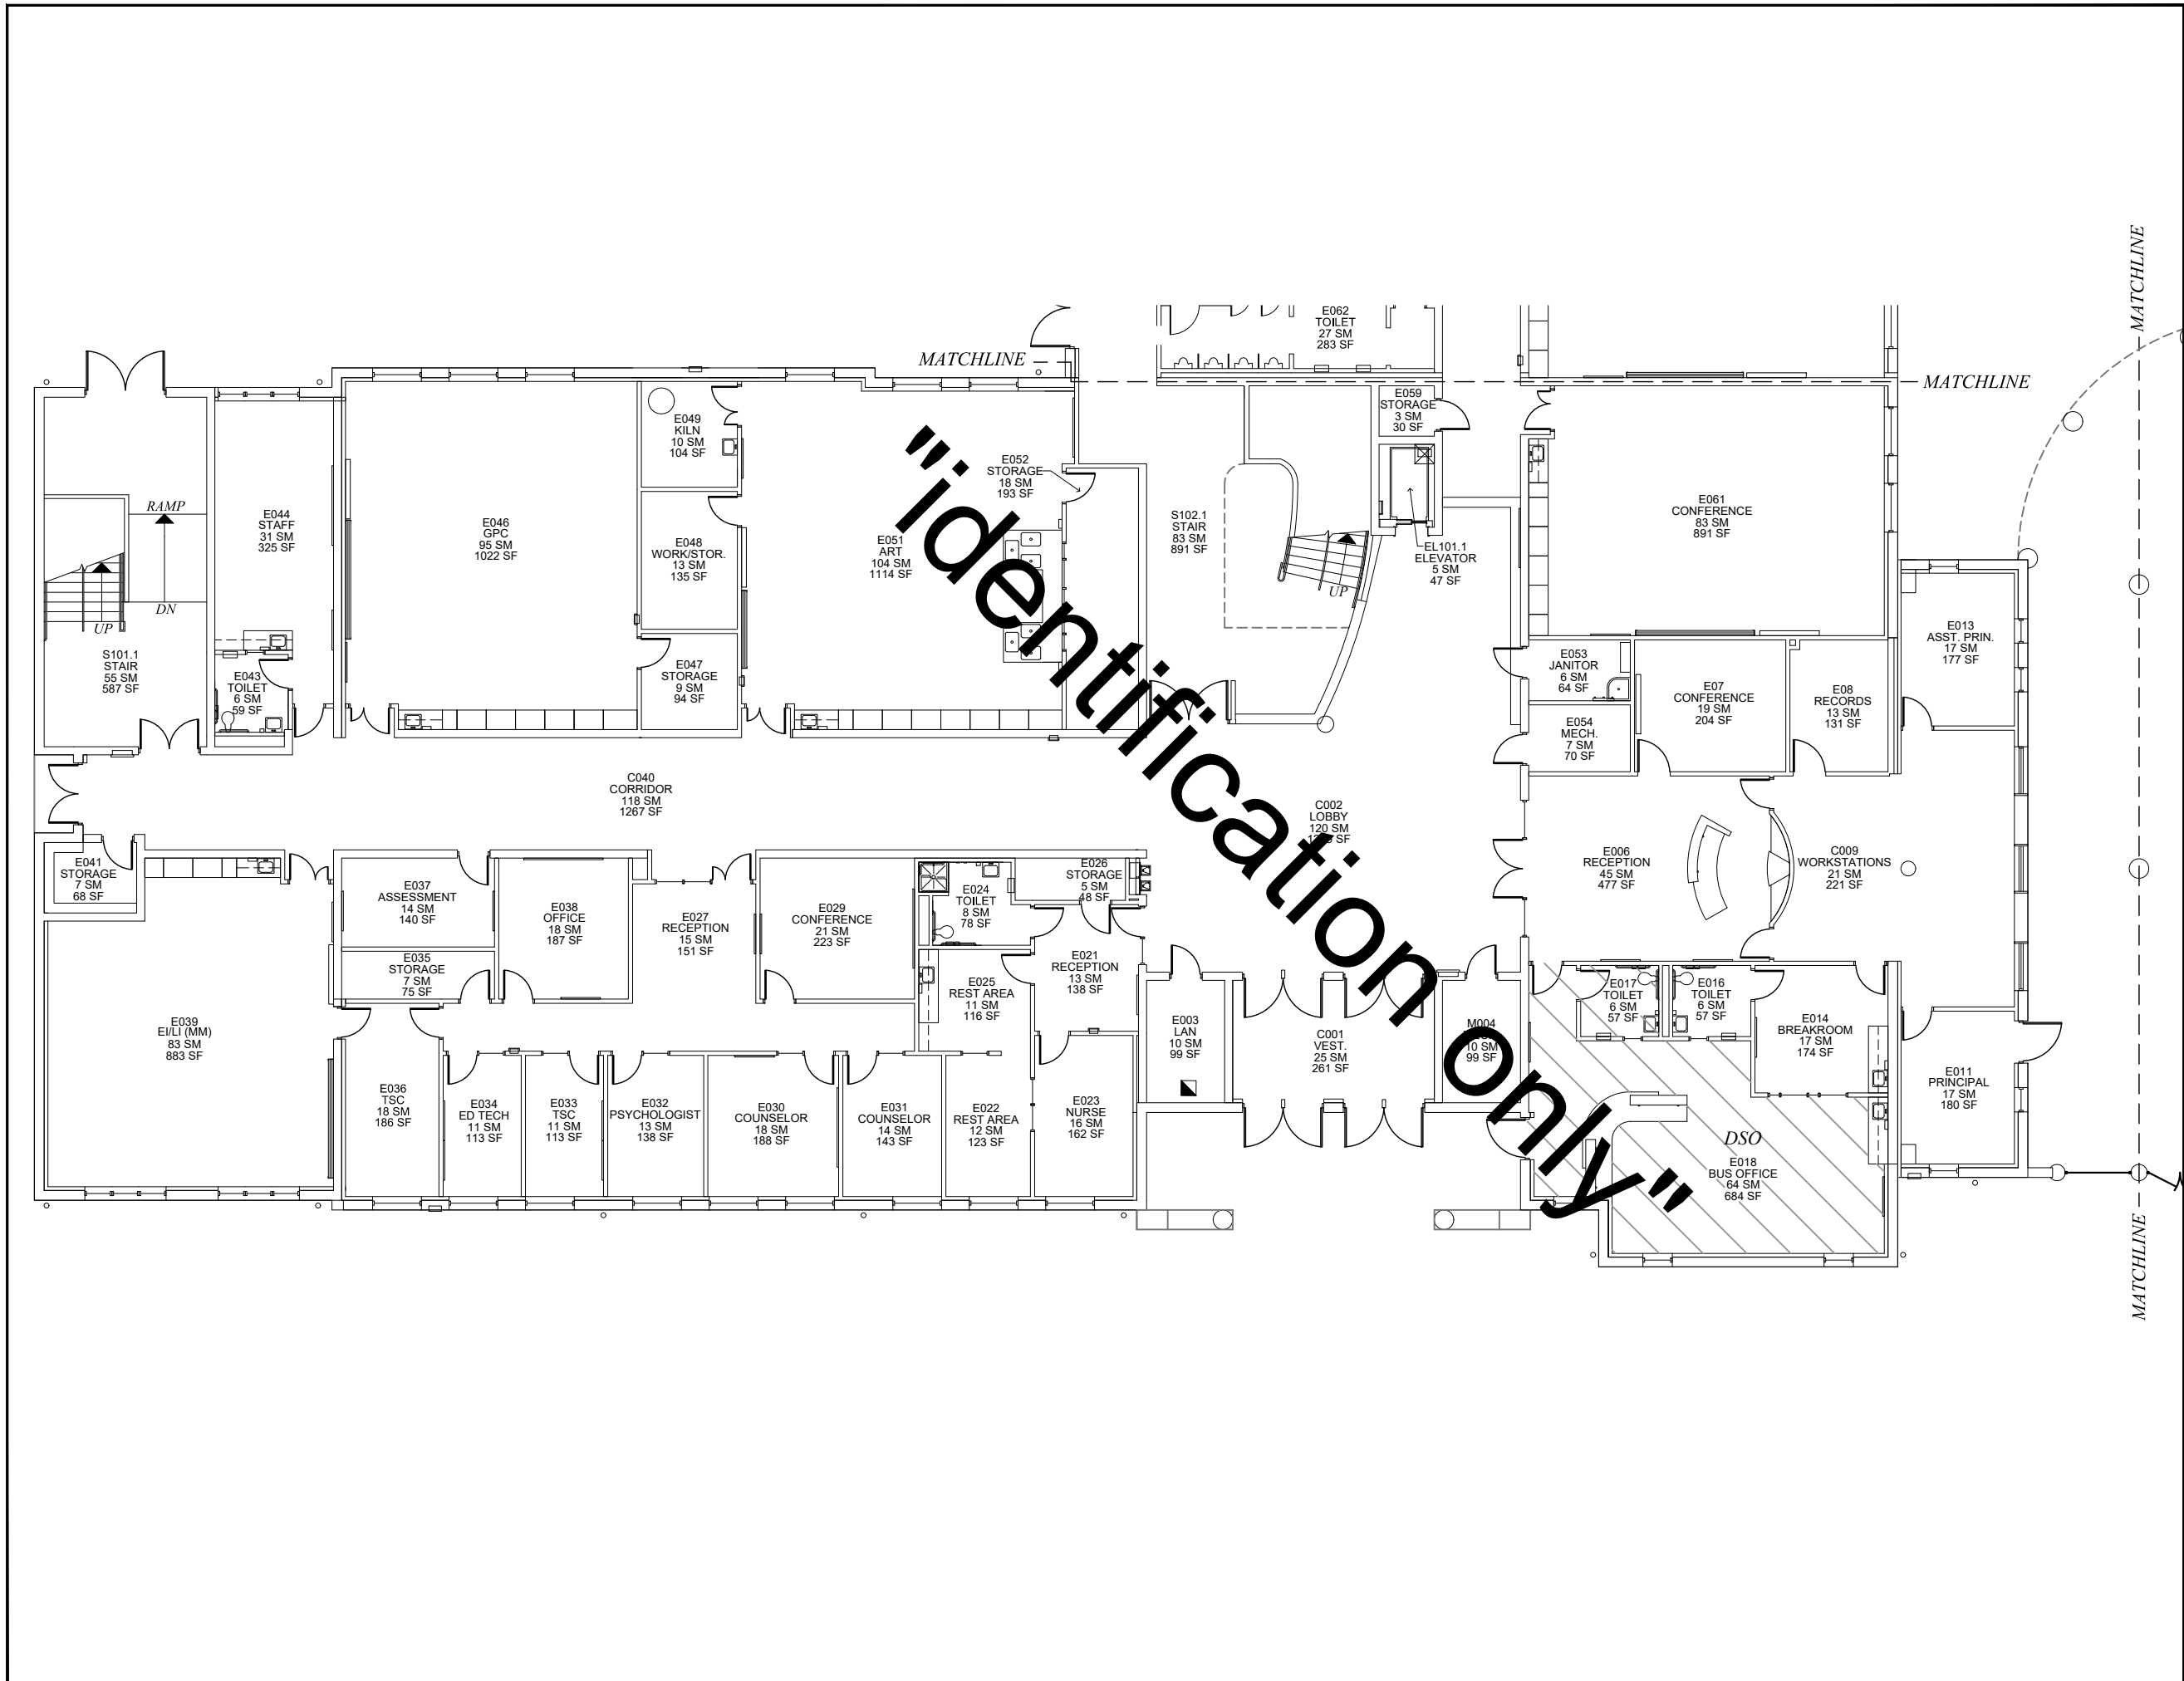

DOOR

SLIDING DOOR

ACCORDION PARTITION

STACK OR FOLDING PARTITION

WINDOW/GLAZING

HIGH WINDOW

SKYLIGHT

STOOP/STEP UP

STAIR

RAMP

ACCESS LADDER

COLD STORAGE

AREA CALCULATED @ 50 %

SLOPING ROOF

DRINKING FOUNTAIN

LAVATORY

SINK

TOILET

URINAL

LOCKER

LAN DISTRIBUTION FRAME

VENT HOOD

WALL SHELVING

UPPER CABINET

BASE CABINET

TEACHER CABINET

MATCHLINE

FLAT ROOF

TITLEBLOCK LEGEND

SHEET NAME:

BLDG #_ FLOOR # (# IN SERIES)

KEY PLAN

NTS

WALK-IN COOLER 1

X700F

X700E

710

STORAGE

X700D

700

X700A

X700C

X700B

NORTH

Updated By: SPF

FUS Review: MRS

100% Submittal Date: 01 MAY 2020

0 2 4 8 16 FT

dodea

DEPARTMENT OF DEFENSE EDUCATION ACTIVITY

FACILITY UTILIZATION SURVEY

VICENZA ELEMENTARY SCHOOL/

VICENZA MIDDLE SCHOOL

BUILDING NUMBER: 700

COUNTRY: ITALY

INSTALLATION: US ARMY GARRISON ITALY

SITE: VICENZA FAMILY HOUSING

REGION-DISTRICT: DODEA EUROPE SOUTH

DoDAAC Number:

HE5420, HE5467

Floor:

LEVEL 1

Survey Date:


JANUARY 2020

Sheet Name:

700_1 (4)


Sheet Seq:

13 of 29

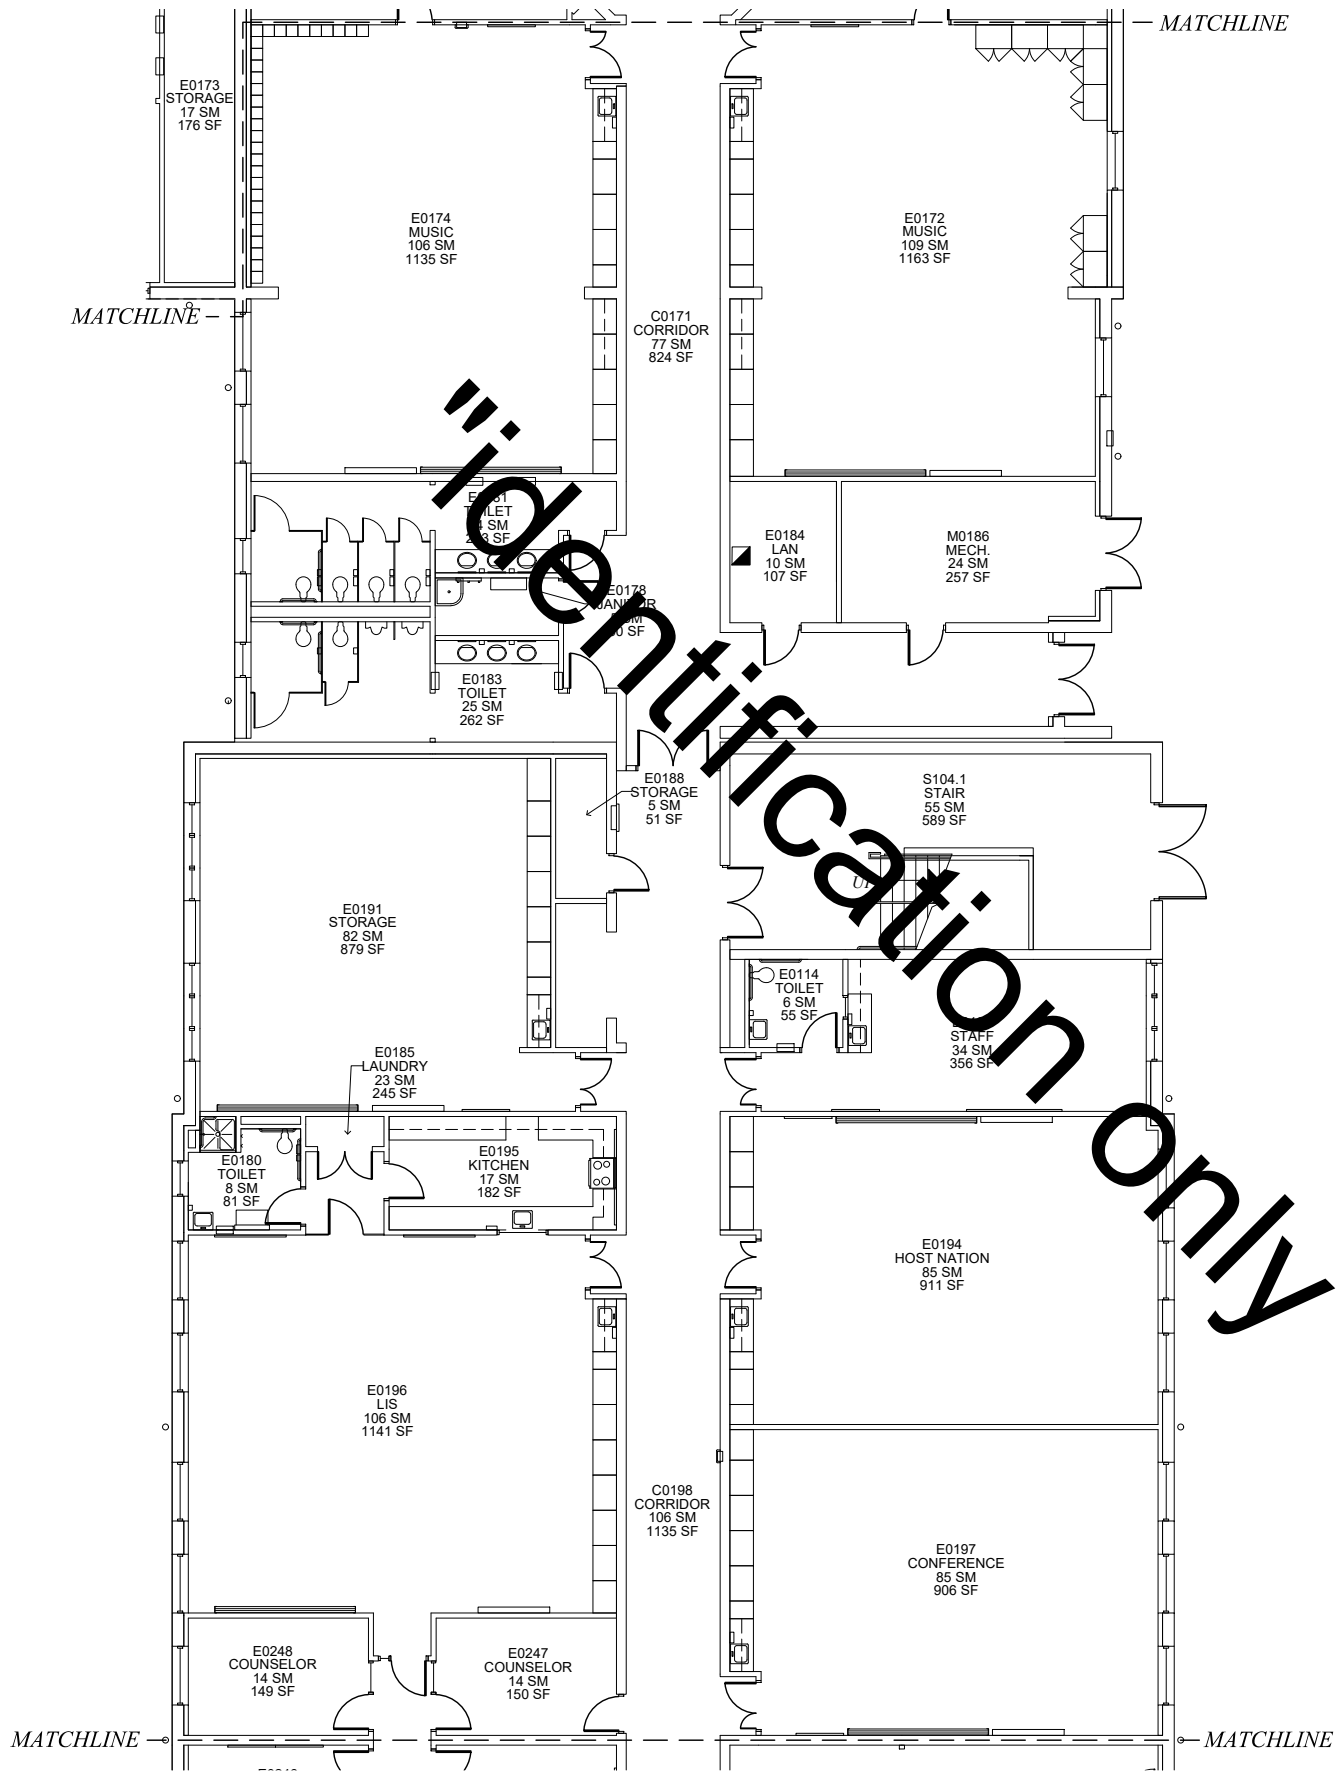

SYMBOL LEGEND	
	DOOR
	DRINKING FOUNTAIN
	SLIDING DOOR
	LAVATORY
	ACCORDION PARTITION
	SINK
	STACK OR FOLDING PARTITION
	TOILET
	WINDOW/GLAZING
	URINAL
	HIGH WINDOW
	LOCKER
	SKYLIGHT
	LAN DISTRIBUTION FRAME
	STOOP/STEP UP
	VENT HOOD
	STAIR
	WALL SHELVING
	RAMP
	UPPER CABINET
	ACCESS LADDER
	BASE CABINET
	COLD STORAGE
	TEACHER CABINET
	AREA CALCULATED @ 50 %
	MATCHLINE
	SLOPING ROOF
	FLAT ROOF

TITLEBLOCK LEGEND	
SHEET NAME:	BLDG #_FLOOR # (# IN SERIES)

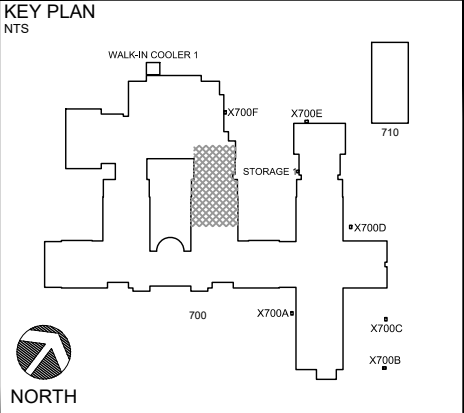


Updated By:	FUS Review:	100% Submittal Date:
SPF	MRS	01 MAY 2020
0 2 4 8 16 FT		

DEPARTMENT OF DEFENSE EDUCATION ACTIVITY
FACILITY UTILIZATION SURVEY

VICENZA ELEMENTARY SCHOOL/
VICENZA MIDDLE SCHOOL
BUILDING NUMBER: 700
COUNTRY: ITALY
INSTALLATION: US ARMY GARRISON ITALY
SITE: VICENZA FAMILY HOUSING
REGION-DISTRICT: DODEA EUROPE SOUTH

DoDAAC Number:	Floor:	Survey Date:
HE5420, HE5467	LEVEL 1	JANUARY 2020
Sheet Name:	Sheet Seq:	
700_1 (5)	14 of 29	

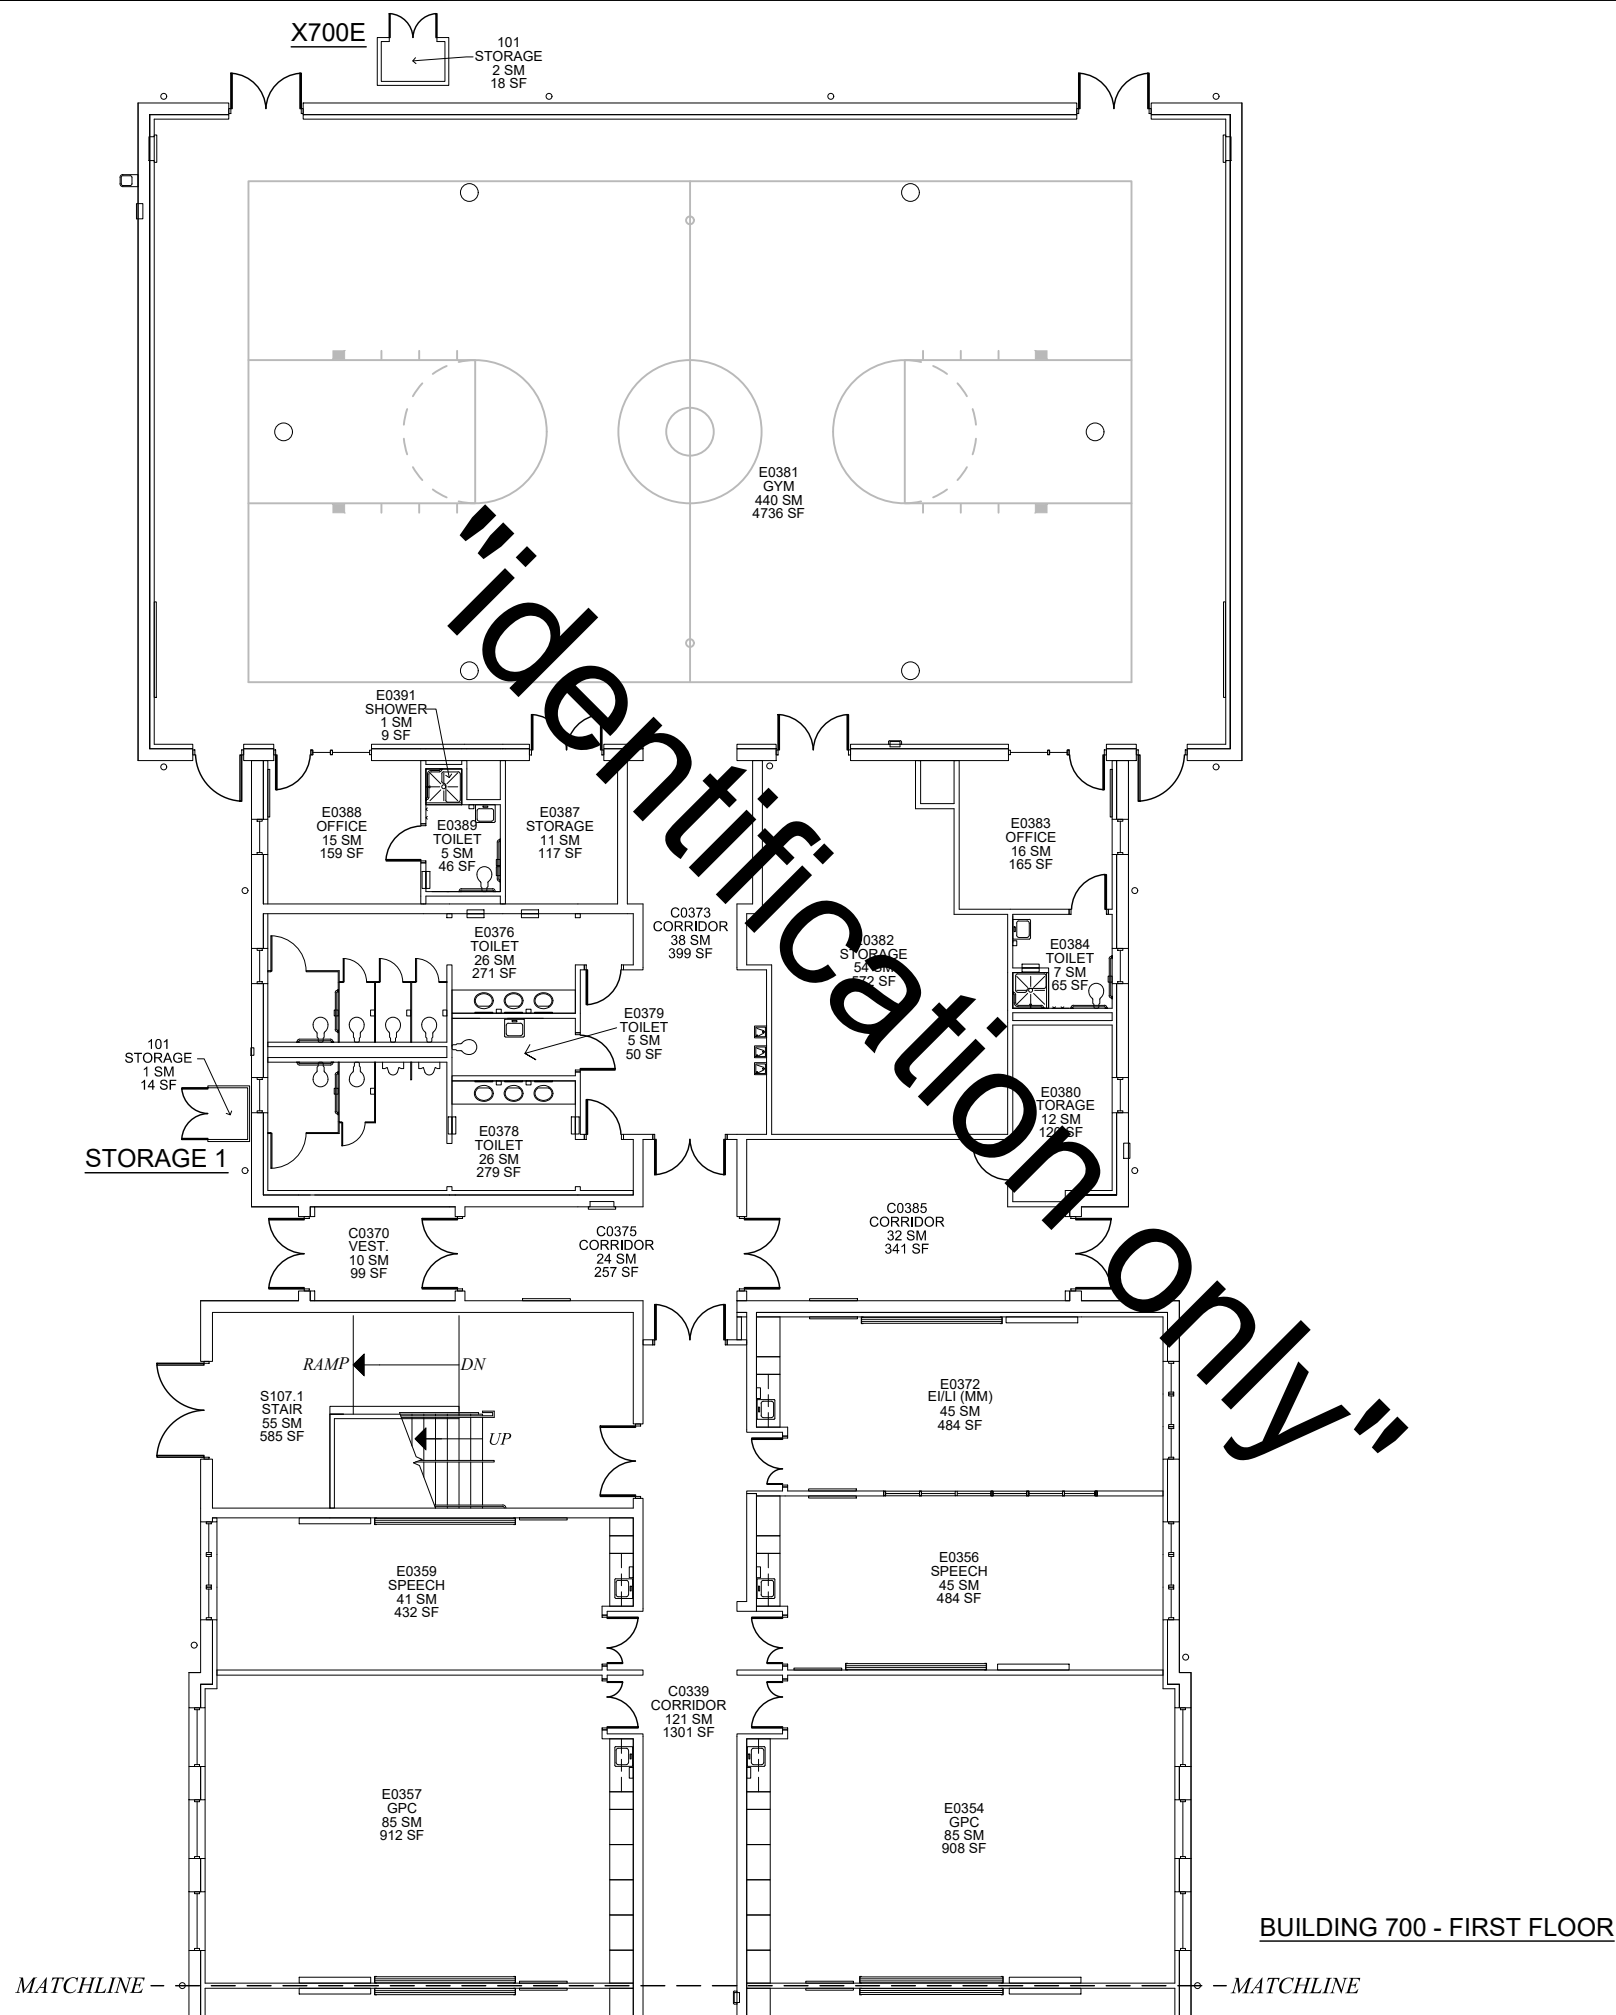

SYMBOL LEGEND	
DOOR	DRINKING FOUNTAIN
SLIDING DOOR	LAVATORY
ACCORDION PARTITION	SINK
STACK OR FOLDING PARTITION	TOILET
WINDOW/GLAZING	URINAL
HIGH WINDOW	LOCKER
SKYLIGHT	LAN DISTRIBUTION FRAME
STOOP/STEP UP	VENT HOOD
STAIR	WALL SHELVING
RAMP	UPPER CABINET
ACCESS LADDER	BASE CABINET
COLD STORAGE	TEACHER CABINET
AREA CALCULATED @ 50 %	MATCHLINE
SLOPING ROOF	FLAT ROOF

TITLEBLOCK LEGEND	
SHEET NAME:	BLDG #_FLOOR # (# IN SERIES)

KEY PLAN
NTS

NORTH


Updated By: SPF FUS Review: MRS 100% Submittal Date: 01 MAY 2020

0 2 4 8 16 FT

dodea
DEPARTMENT OF DEFENSE EDUCATION ACTIVITY
FACILITY UTILIZATION SURVEY

VICENZA ELEMENTARY SCHOOL/
VICENZA MIDDLE SCHOOL
BUILDING NUMBER: 700, X700E, STORAGE 1
COUNTRY: ITALY
INSTALLATION: US ARMY GARRISON ITALY
SITE: VICENZA FAMILY HOUSING
REGION-DISTRICT: DODEA EUROPE SOUTH




DoDAAC Number: HE5420, HE5467	Floor: LEVEL 1	Survey Date: JANUARY 2020
Sheet Name: 700_1 (7)		Sheet Seq: 16 of 29

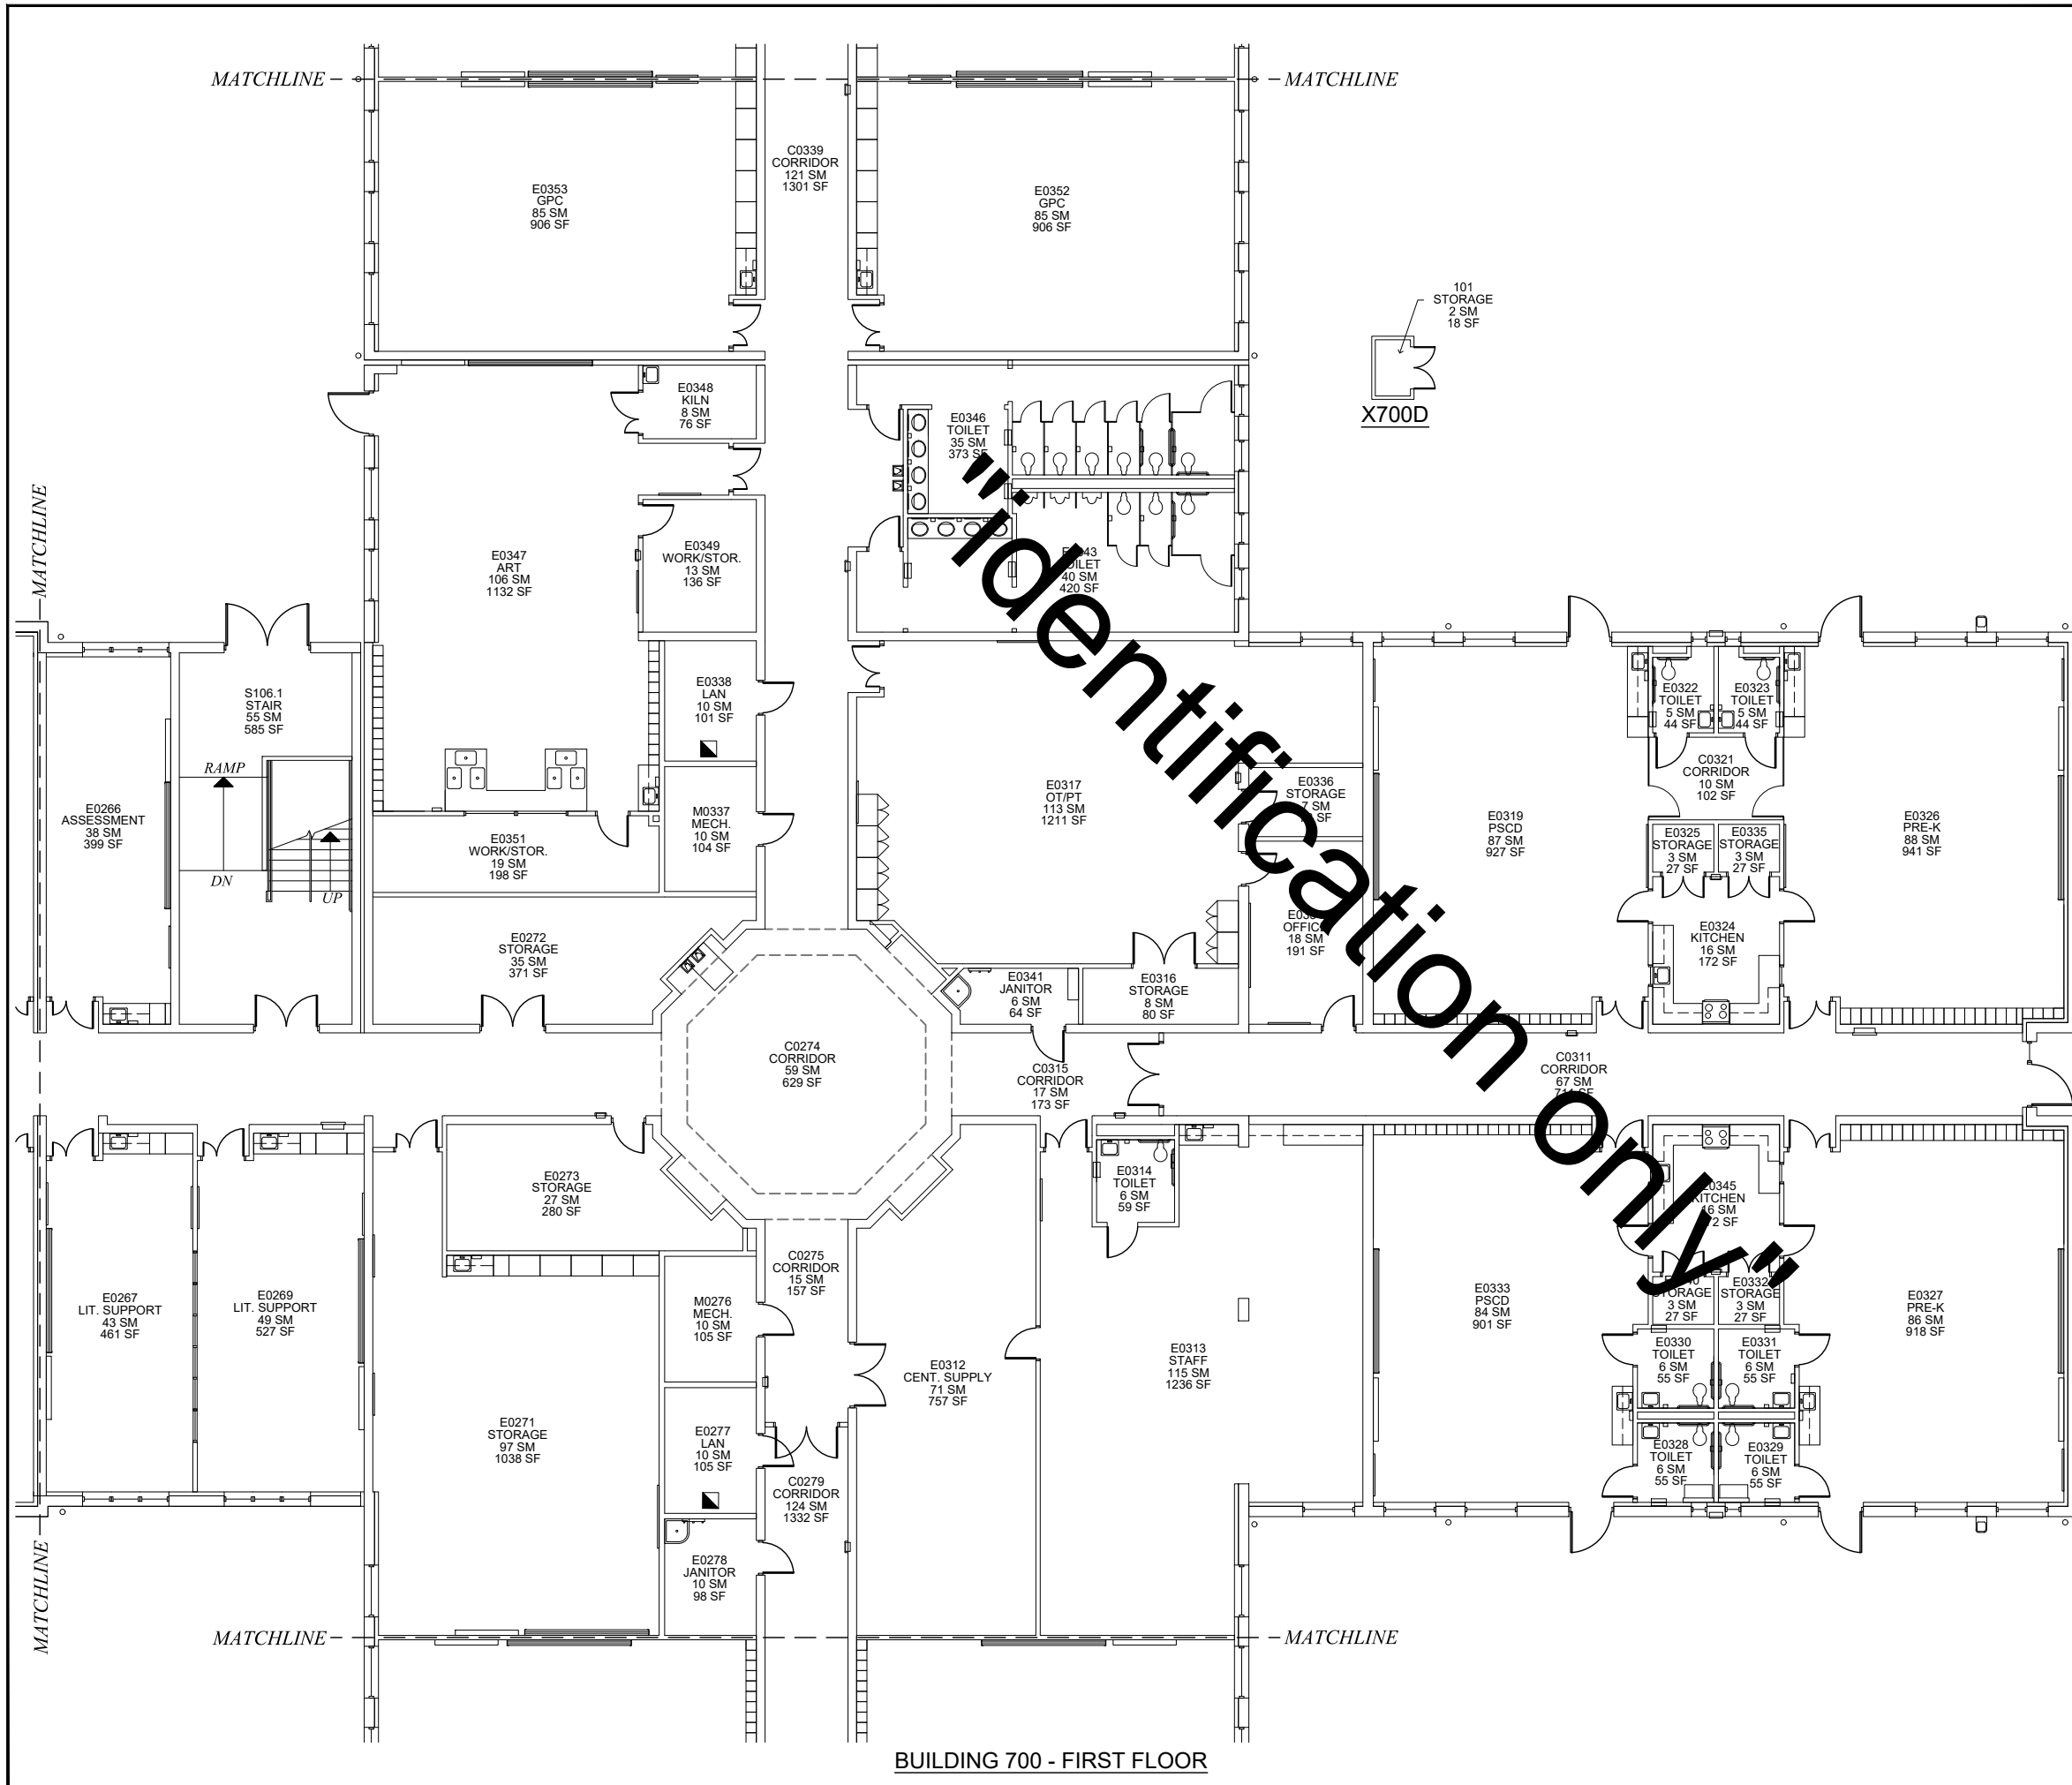



SYMBOL LEGEND	
 DOOR	 DRINKING FOUNTAIN
 SLIDING DOOR	 LAVATORY
 ACCORDION PARTITION	 SINK
 STACK OR FOLDING PARTITION	 TOILET
 WINDOW/GLAZING	 URINAL
 HIGH WINDOW	 LOCKER
 SKYLIGHT	 LAN DISTRIBUTION FRAME
 STOOP/STEP UP	 VENT HOOD
 STAIR	 WALL SHELVING
 RAMP	 UPPER CABINET
 ACCESS LADDER	 BASE CABINET
 COLD STORAGE	 TEACHER CABINET
 AREA CALCULATED @ 50 %	 MATCHLINE
 SLOPING ROOF	 FLAT ROOF

TITLEBLOCK LEGEND	
SHEET NAME:	BLDG #_ FLOOR # (# IN SERIES)

KEY PLAN	

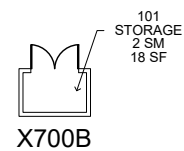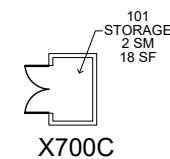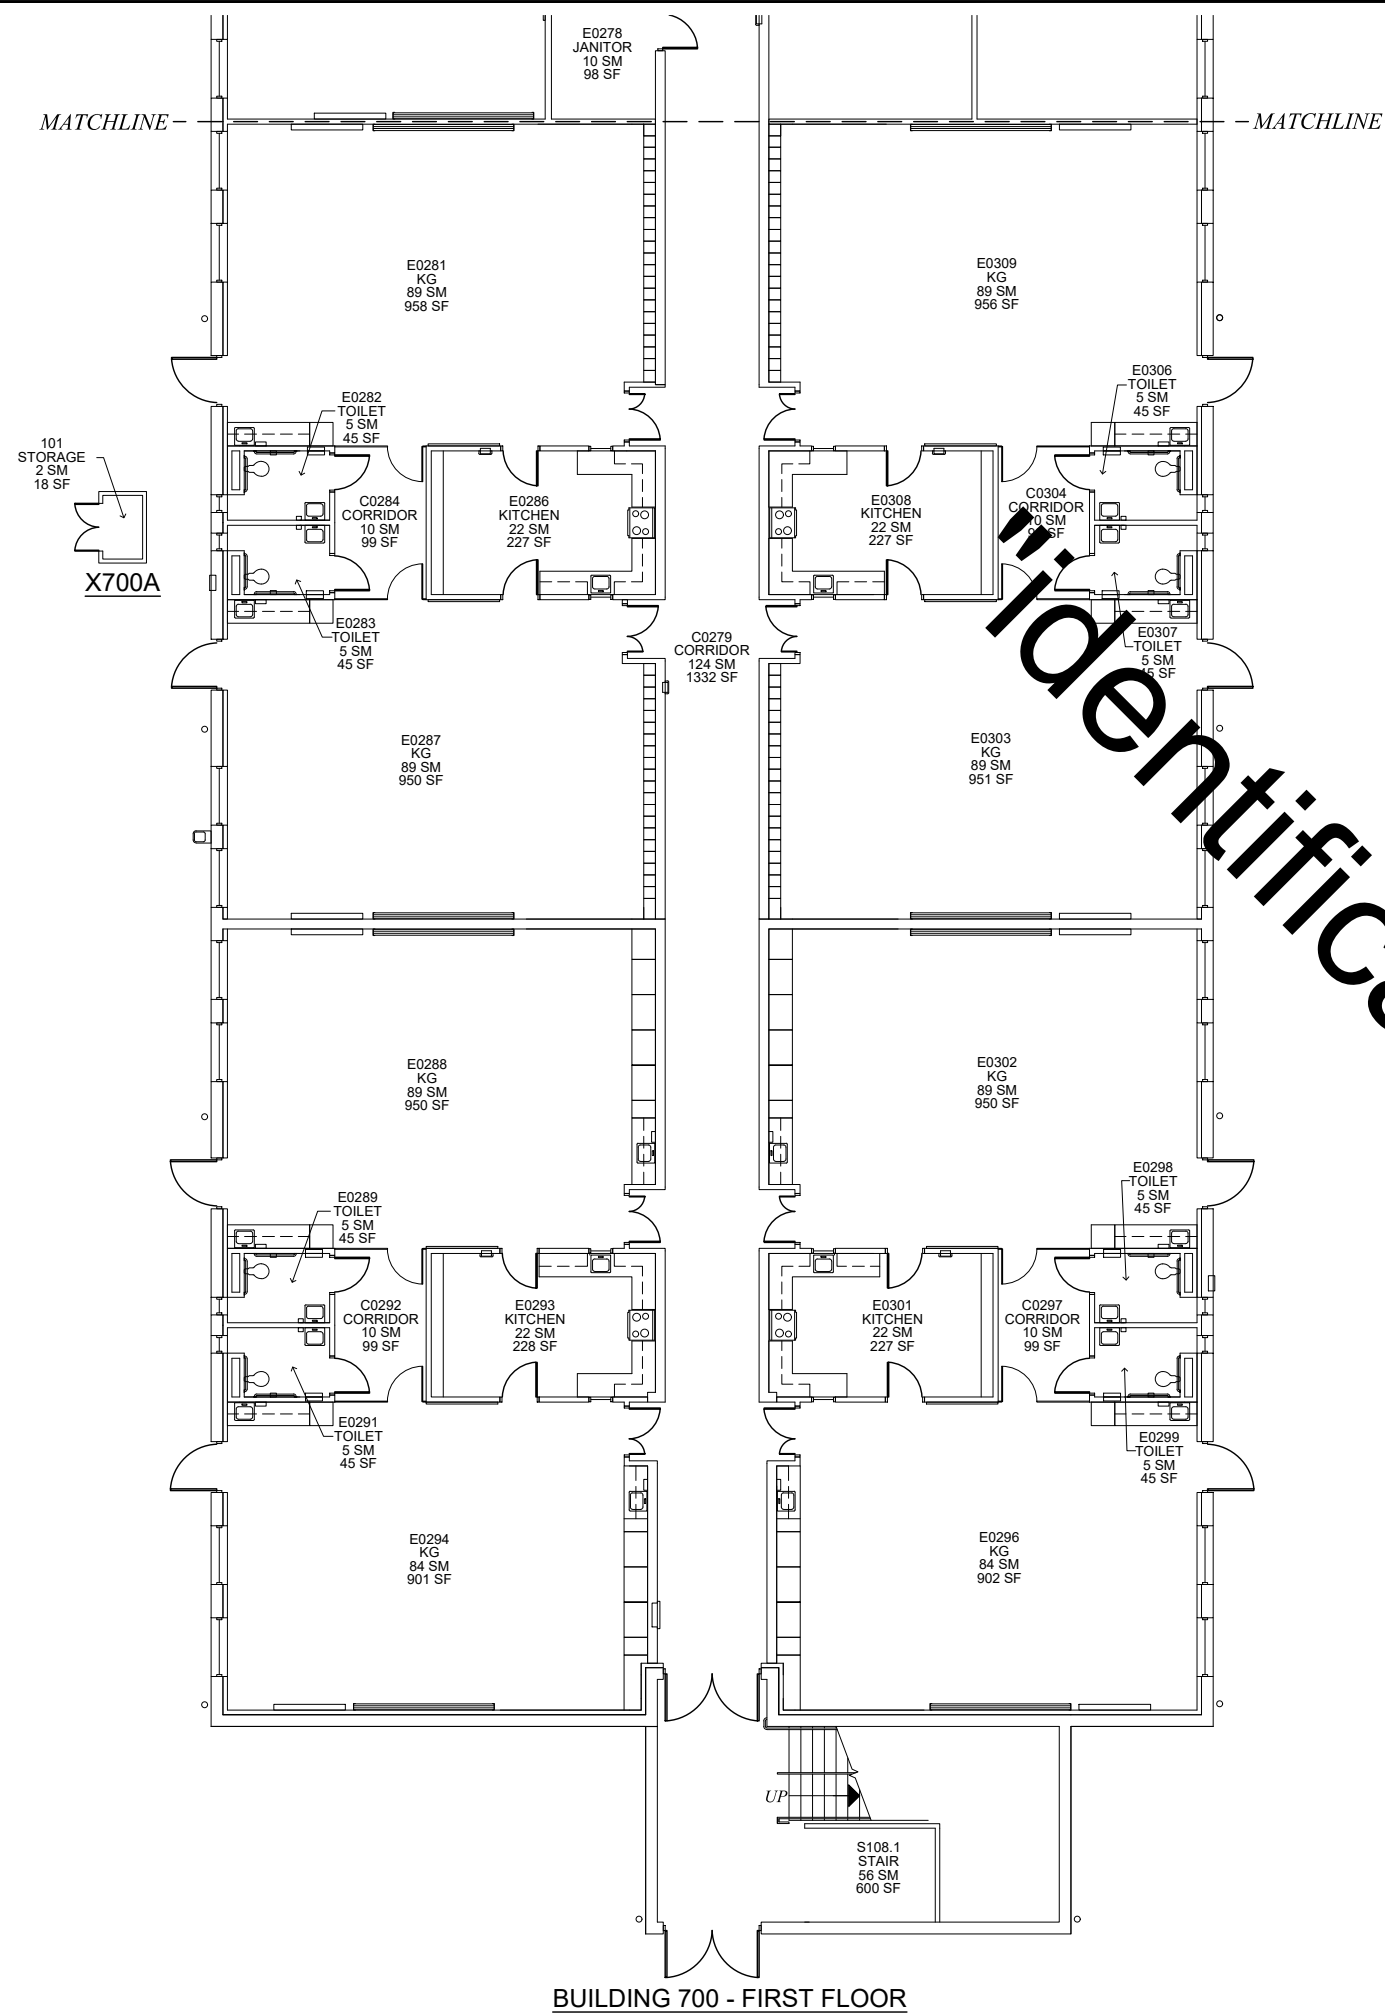


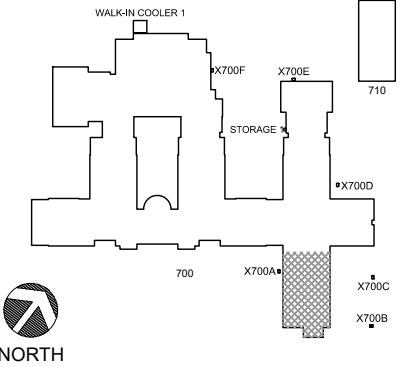SYMBOL LEGEND		
	DOOR	 DRINKING FOUNTAIN
	SLIDING DOOR	 LAVATORY
	ACCORDION PARTITION	 SINK
	STACK OR FOLDING PARTITION	 TOILET
	WINDOW/GLAZING	 URINAL
	HIGH WINDOW	 LOCKER
	SKYLIGHT	 LAN DISTRIBUTION FRAME
	STOOP/STEP UP	 VENT HOOD
	STAIR	 WALL SHELVING
	RAMP	 UPPER CABINET
	ACCESS LADDER	 BASE CABINET
	COLD STORAGE	 TEACHER CABINET
	AREA CALCULATED @ 50 %	 MATCHLINE
	SLOPING ROOF	 FLAT ROOF
TITLEBLOCK LEGEND		
SHEET NAME:		BLDG #_FLOOR # (# IN SERIES)
KEY PLAN		
NTS		
		
Updated By: FUS Review: 100% Submittal Date: SPF MRS 01 MAY 2020 0 2 4 8 16 FT  DEPARTMENT OF DEFENSE EDUCATION ACTIVITY FACILITY UTILIZATION SURVEY VICENZA ELEMENTARY SCHOOL/ VICENZA MIDDLE SCHOOL BUILDING NUMBER: 700, X700A, X700B, X700C COUNTRY: ITALY INSTALLATION: US ARMY GARRISON ITALY SITE: VICENZA FAMILY HOUSING REGION-DISTRICT: DODEA EUROPE SOUTH DoDAAC Number: Floor: Survey Date: HE5420, HE5467 LEVEL 1 JANUARY 2020 Sheet Name: Sheet Seq: 700_1 (9) 18 of 29		

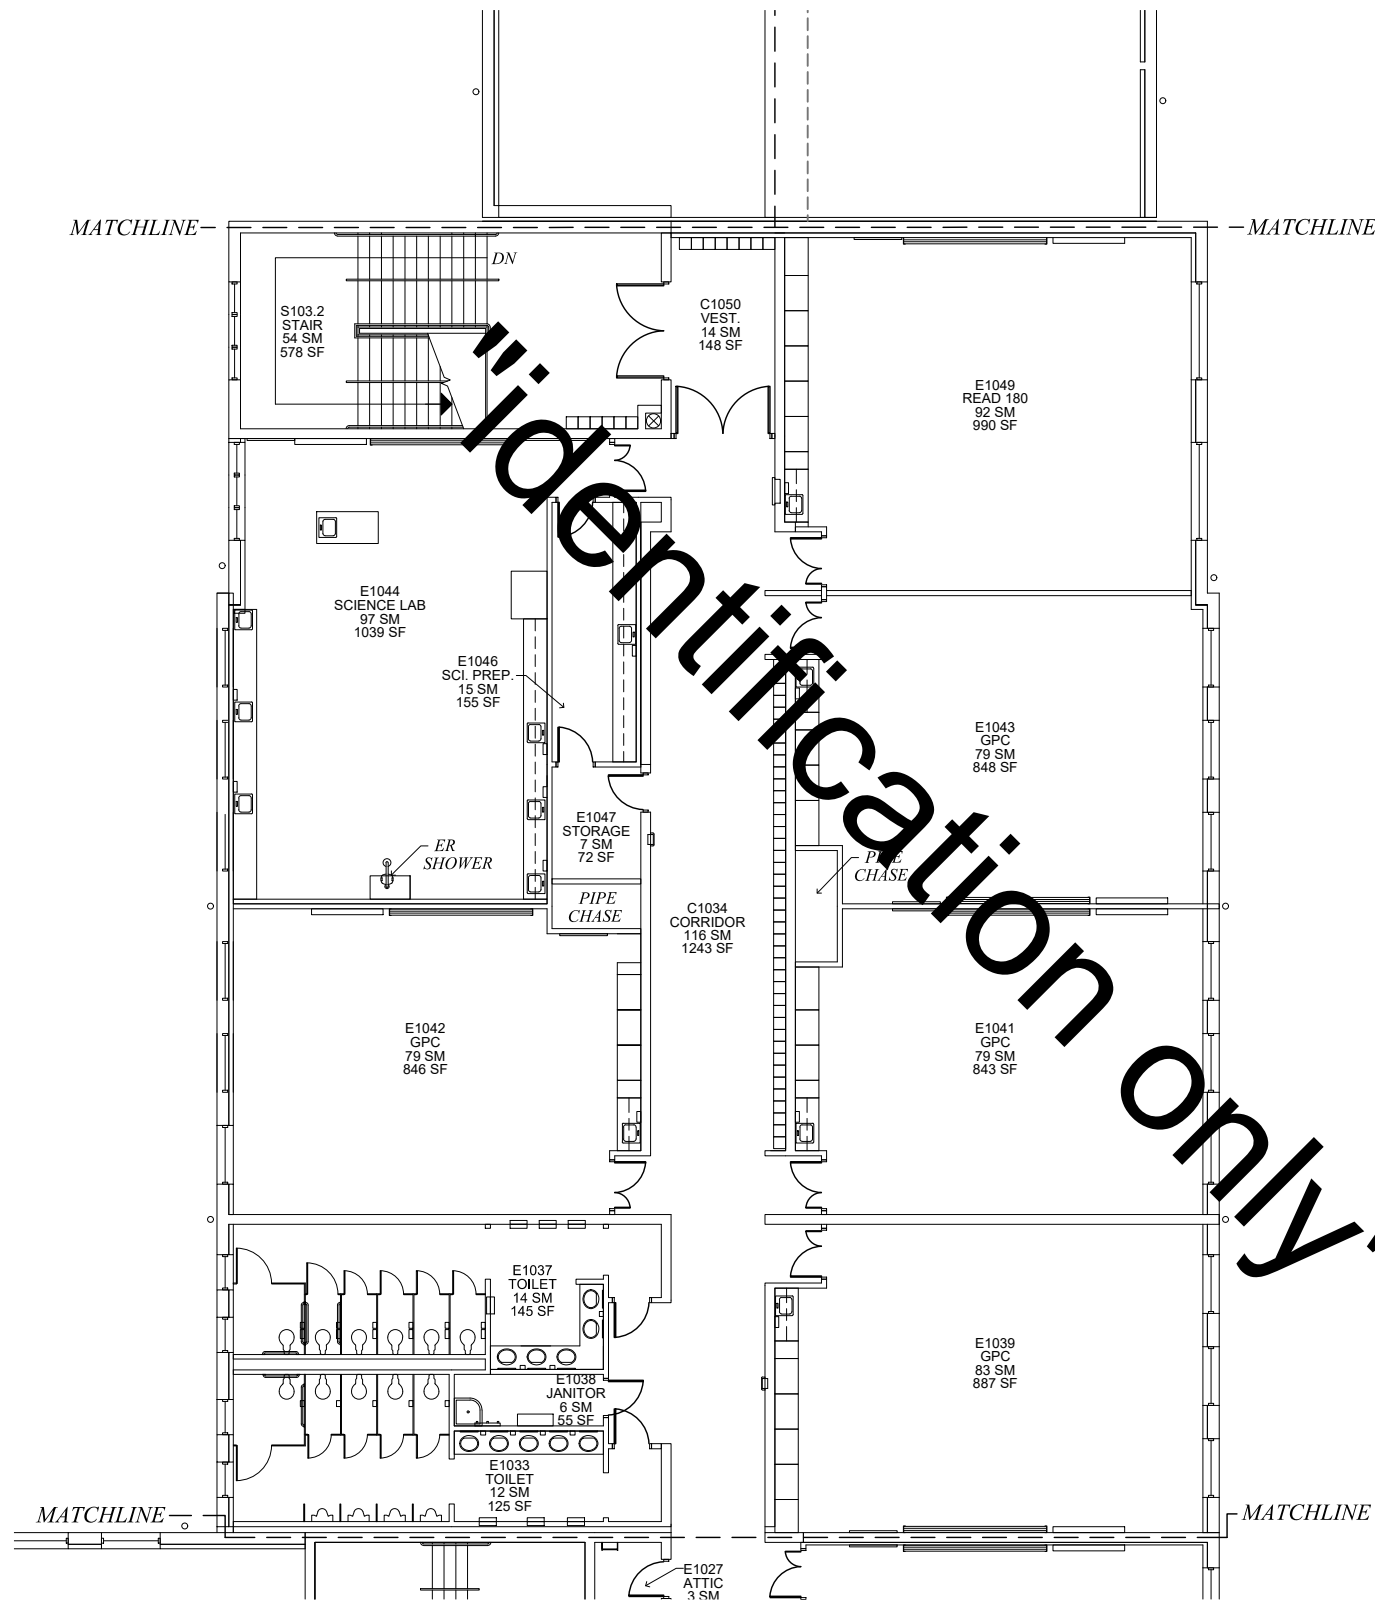

SYMBOL LEGEND	
 DOOR	 DRINKING FOUNTAIN
 SLIDING DOOR	 LAVATORY
 ACCORDION PARTITION	 SINK
 STACK OR FOLDING PARTITION	 TOILET
 WINDOW/GLAZING	 URINAL
 HIGH WINDOW	 LOCKER
 SKYLIGHT	 LAN DISTRIBUTION FRAME
 STOOP/STEP UP	 VENT HOOD
 STAIR	 WALL SHELVING
 RAMP	 UPPER CABINET
 ACCESS LADDER	 BASE CABINET
 COLD STORAGE	 TEACHER CABINET
 AREA CALCULATED @ 50 %	 MATCHLINE
 SLOPING ROOF	 FLAT ROOF

TITLEBLOCK LEGEND	
SHEET NAME:	BLDG #_FLOOR # (# IN SERIES)

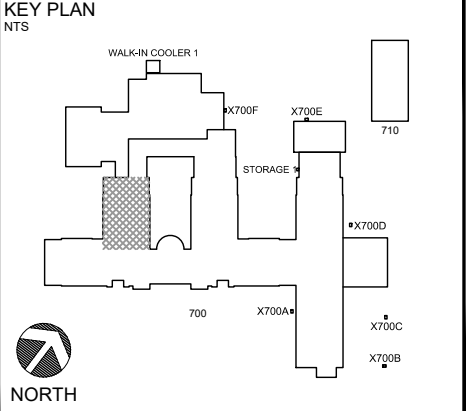


Updated By:	FUS Review:	100% Submittal Date:
SPF	MRS	01 MAY 2020
0 2 4 8 16 FT		

dodea
DEPARTMENT OF DEFENSE EDUCATION ACTIVITY
FACILITY UTILIZATION SURVEY

VICENZA ELEMENTARY SCHOOL/
VICENZA MIDDLE SCHOOL
BUILDING NUMBER: 700
COUNTRY: ITALY
INSTALLATION: US ARMY GARRISON ITALY
SITE: VICENZA FAMILY HOUSING
REGION-DISTRICT: DODEA EUROPE SOUTH

DoDAAC Number:	Floor:	Survey Date:
HE5420, HE5467	LEVEL 2	JANUARY 2020
Sheet Name:	Sheet Seq:	
700_2 (2)	20 of 29	

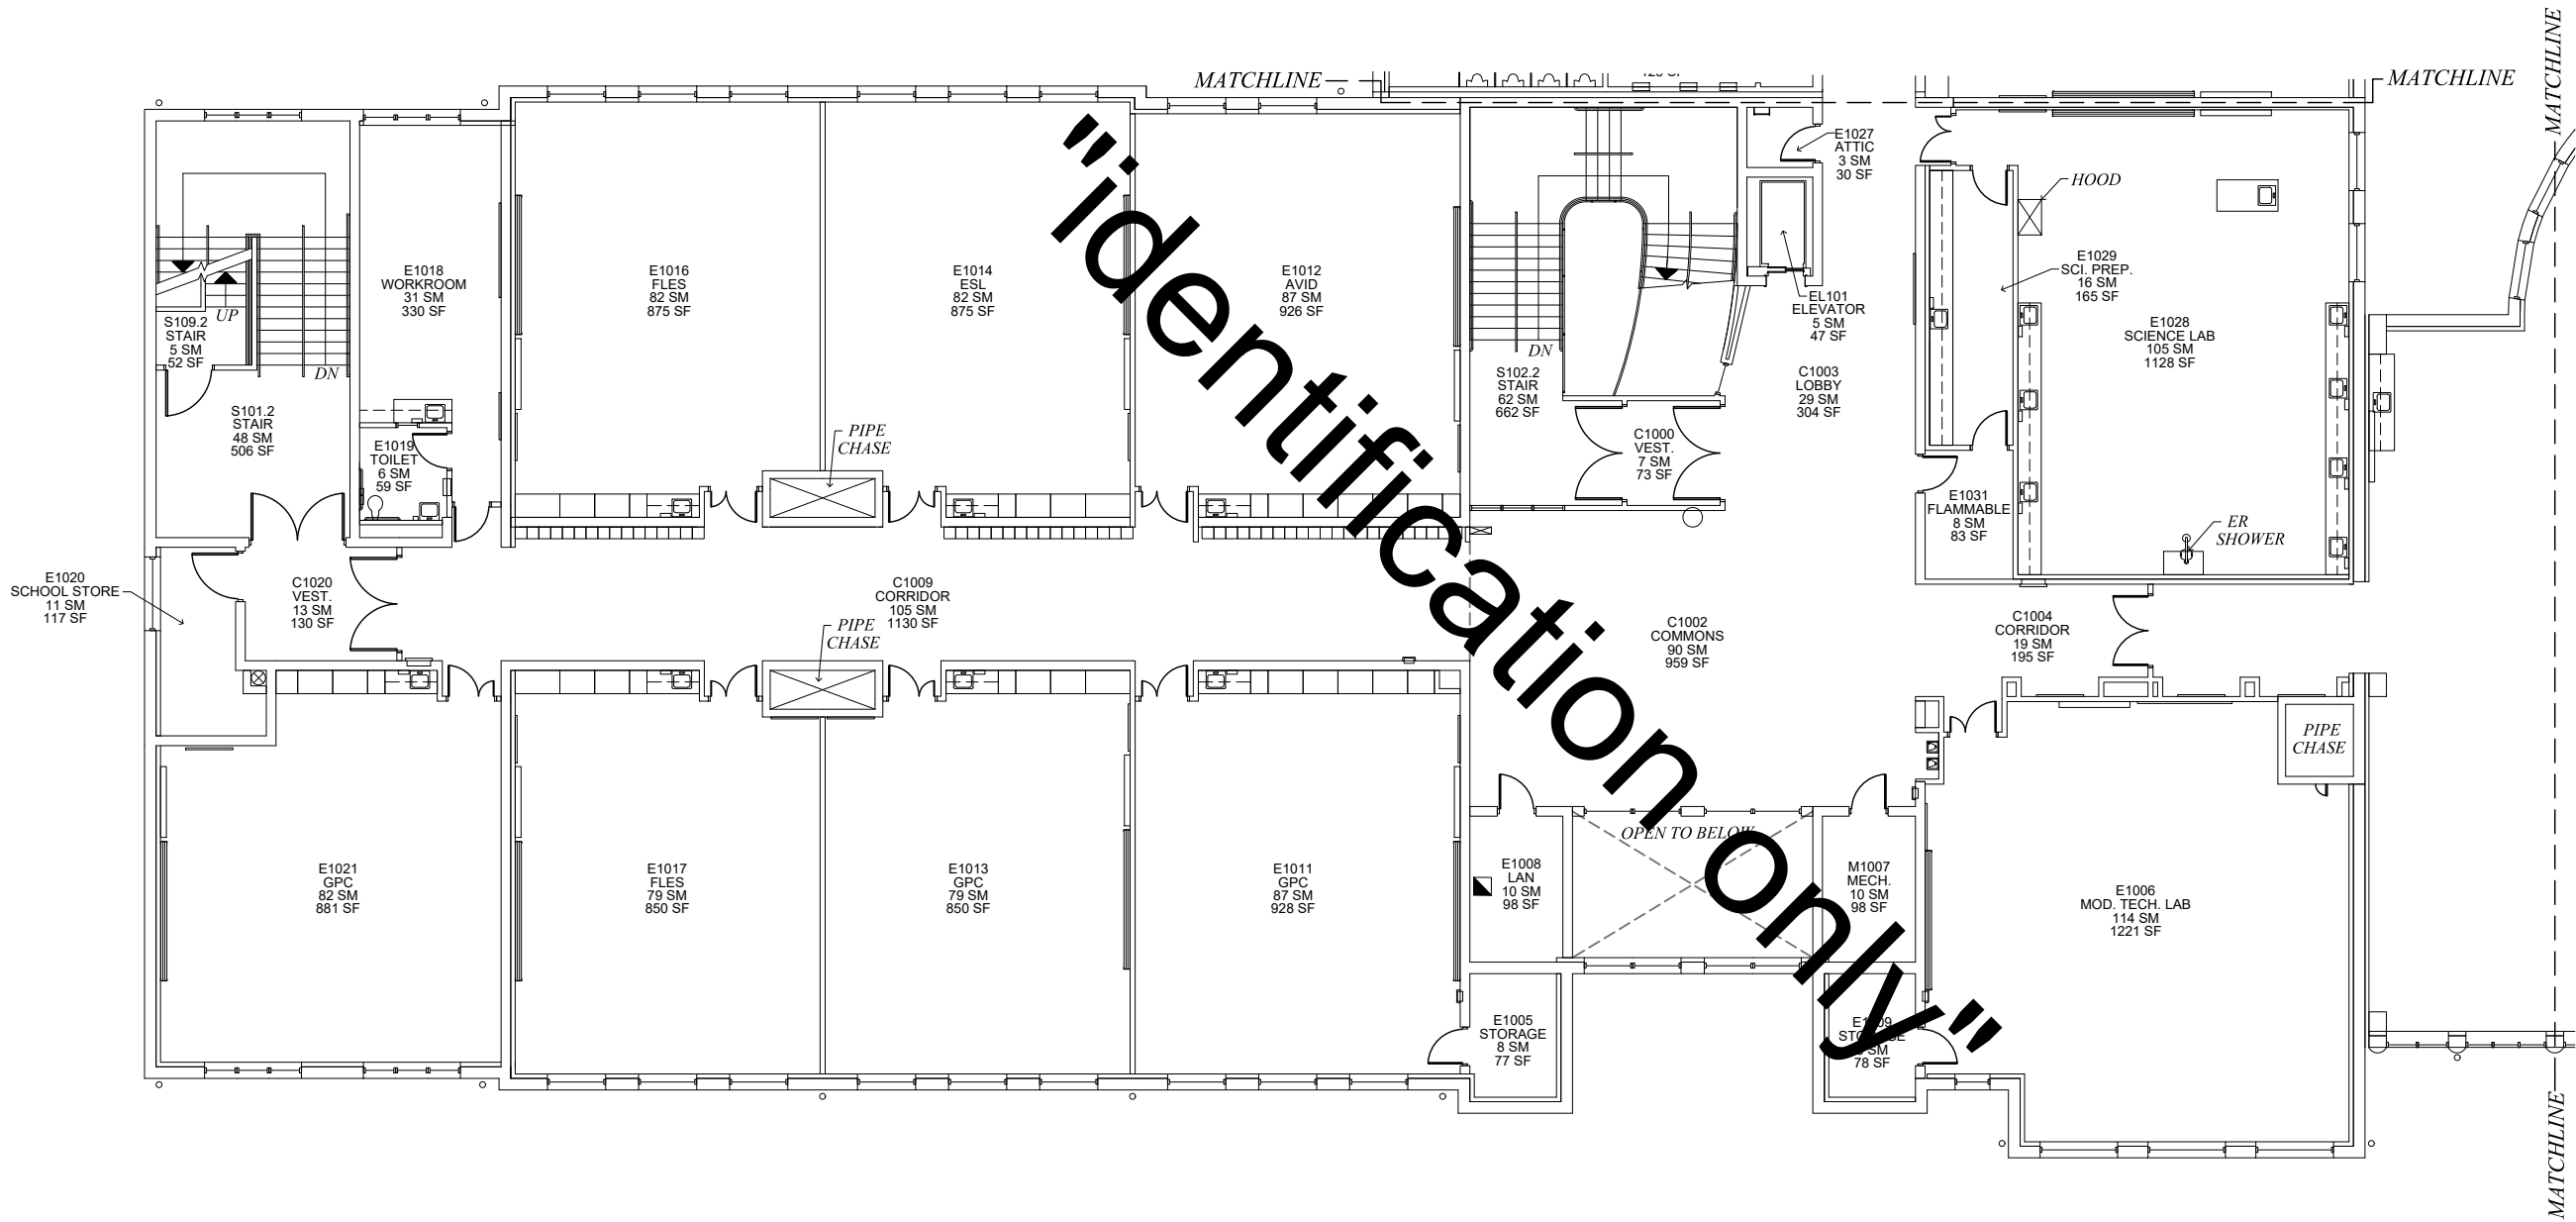

DOOR

SLIDING DOOR

ACCORDION PARTITION

STACK OR FOLDING PARTITION

WINDOW/GLAZING

HIGH WINDOW

SKYLIGHT

STOOP/STEP UP

STAIR

RAMP

ACCESS LADDER

COLD STORAGE

AREA CALCULATED @ 50 %

SLOPING ROOF

DRINKING FOUNTAIN

LAVATORY

SINK

TOILET

URINAL

LOCKER

LAN DISTRIBUTION FRAME

VENT HOOD

WALL SHELVING

UPPER CABINET

BASE CABINET

TEACHER CABINET

MATCHLINE

FLAT ROOF

TITLEBLOCK LEGEND

SHEET NAME:

BLDG #_FLOOR # (# IN SERIES)

KEY PLAN

NTS

WALK-IN COOLER 1

X700F

X700E

710

STORAGE

X700D

700

X700A

X700C

X700B

NORTH

Updated By: SPF

FUS Review: MRS

100% Submittal Date: 01 MAY 2020

0 2 4 8 16 FT

dodea

DEPARTMENT OF DEFENSE EDUCATION ACTIVITY

FACILITY UTILIZATION SURVEY

VICENZA ELEMENTARY SCHOOL/
VICENZA MIDDLE SCHOOL

BUILDING NUMBER: 700

COUNTRY: ITALY

INSTALLATION: US ARMY GARRISON ITALY

SITE: VICENZA FAMILY HOUSING

REGION-DISTRICT: DODEA EUROPE SOUTH


DoDAAC Number: HE5420, HE5467

Floor: LEVEL 2

Survey Date: JANUARY 2020

Sheet Name: 700_2 (3)

Sheet Seq: 21 of 29

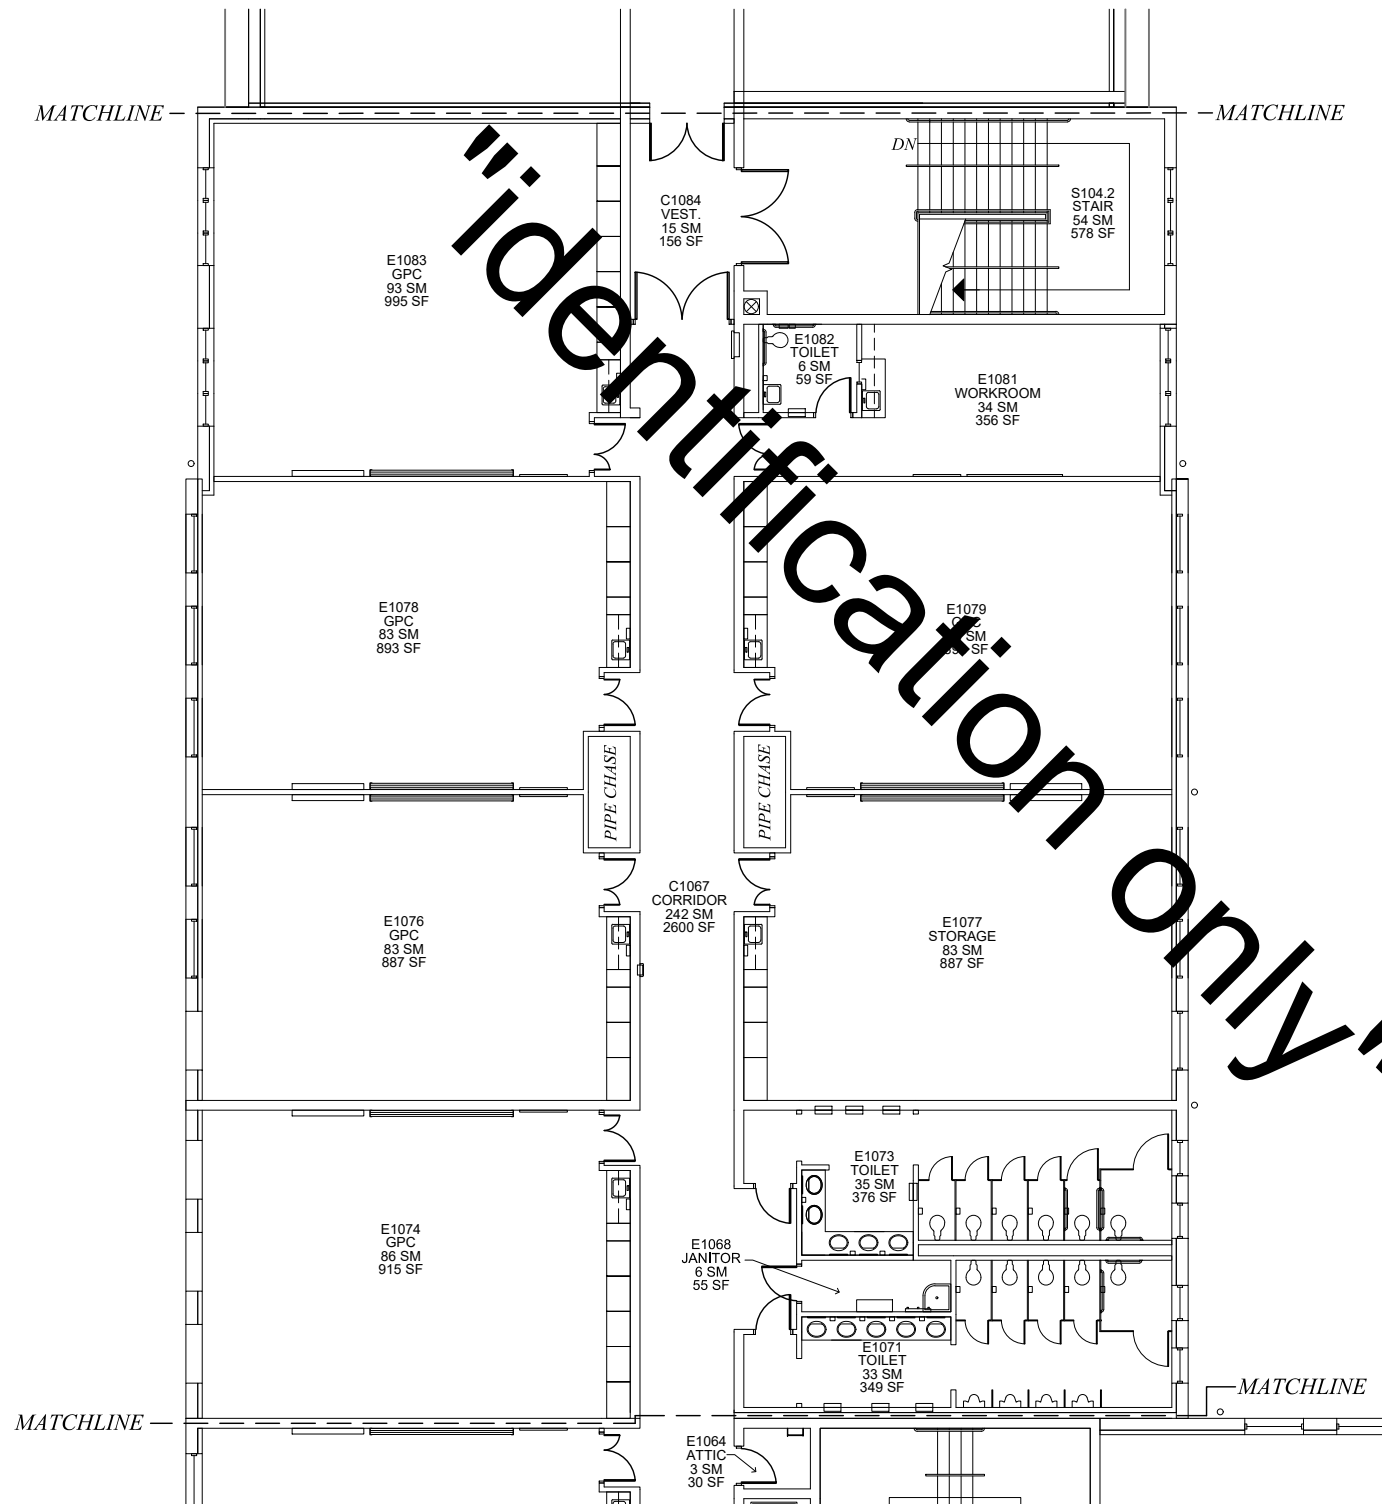

SYMBOL LEGEND	
DOOR	DRINKING FOUNTAIN
SLIDING DOOR	LAVATORY
ACCORDION PARTITION	SINK
STACK OR FOLDING PARTITION	TOILET
WINDOW/GLAZING	URINAL
HIGH WINDOW	LOCKER
SKYLIGHT	LAN DISTRIBUTION FRAME
STOOP/STEP UP	VENT HOOD
STAIR	WALL SHELVING
RAMP	UPPER CABINET
ACCESS LADDER	BASE CABINET
COLD STORAGE	TEACHER CABINET
AREA CALCULATED @ 50 %	MATCHLINE
SLOPING ROOF	FLAT ROOF

TITLEBLOCK LEGEND	
SHEET NAME:	BLDG #_FLOOR # (# IN SERIES)

KEY PLAN
NTS

NORTH


Updated By: SPF	FUS Review: MRS	100% Submittal Date: 01 MAY 2020
--------------------	--------------------	-------------------------------------

0 2 4 8 16 FT

dodea
DEPARTMENT OF DEFENSE EDUCATION ACTIVITY
FACILITY UTILIZATION SURVEY

VICENZA ELEMENTARY SCHOOL/
VICENZA MIDDLE SCHOOL
BUILDING NUMBER: 700
COUNTRY: ITALY
INSTALLATION: US ARMY GARRISON ITALY
SITE: VICENZA FAMILY HOUSING
REGION-DISTRICT: DODEA EUROPE SOUTH

DoDAAC Number: HE5420, HE5467	Floor: LEVEL 2	Survey Date: JANUARY 2020
Sheet Name: 700_2 (4)	Sheet Seq: 22 of 29	

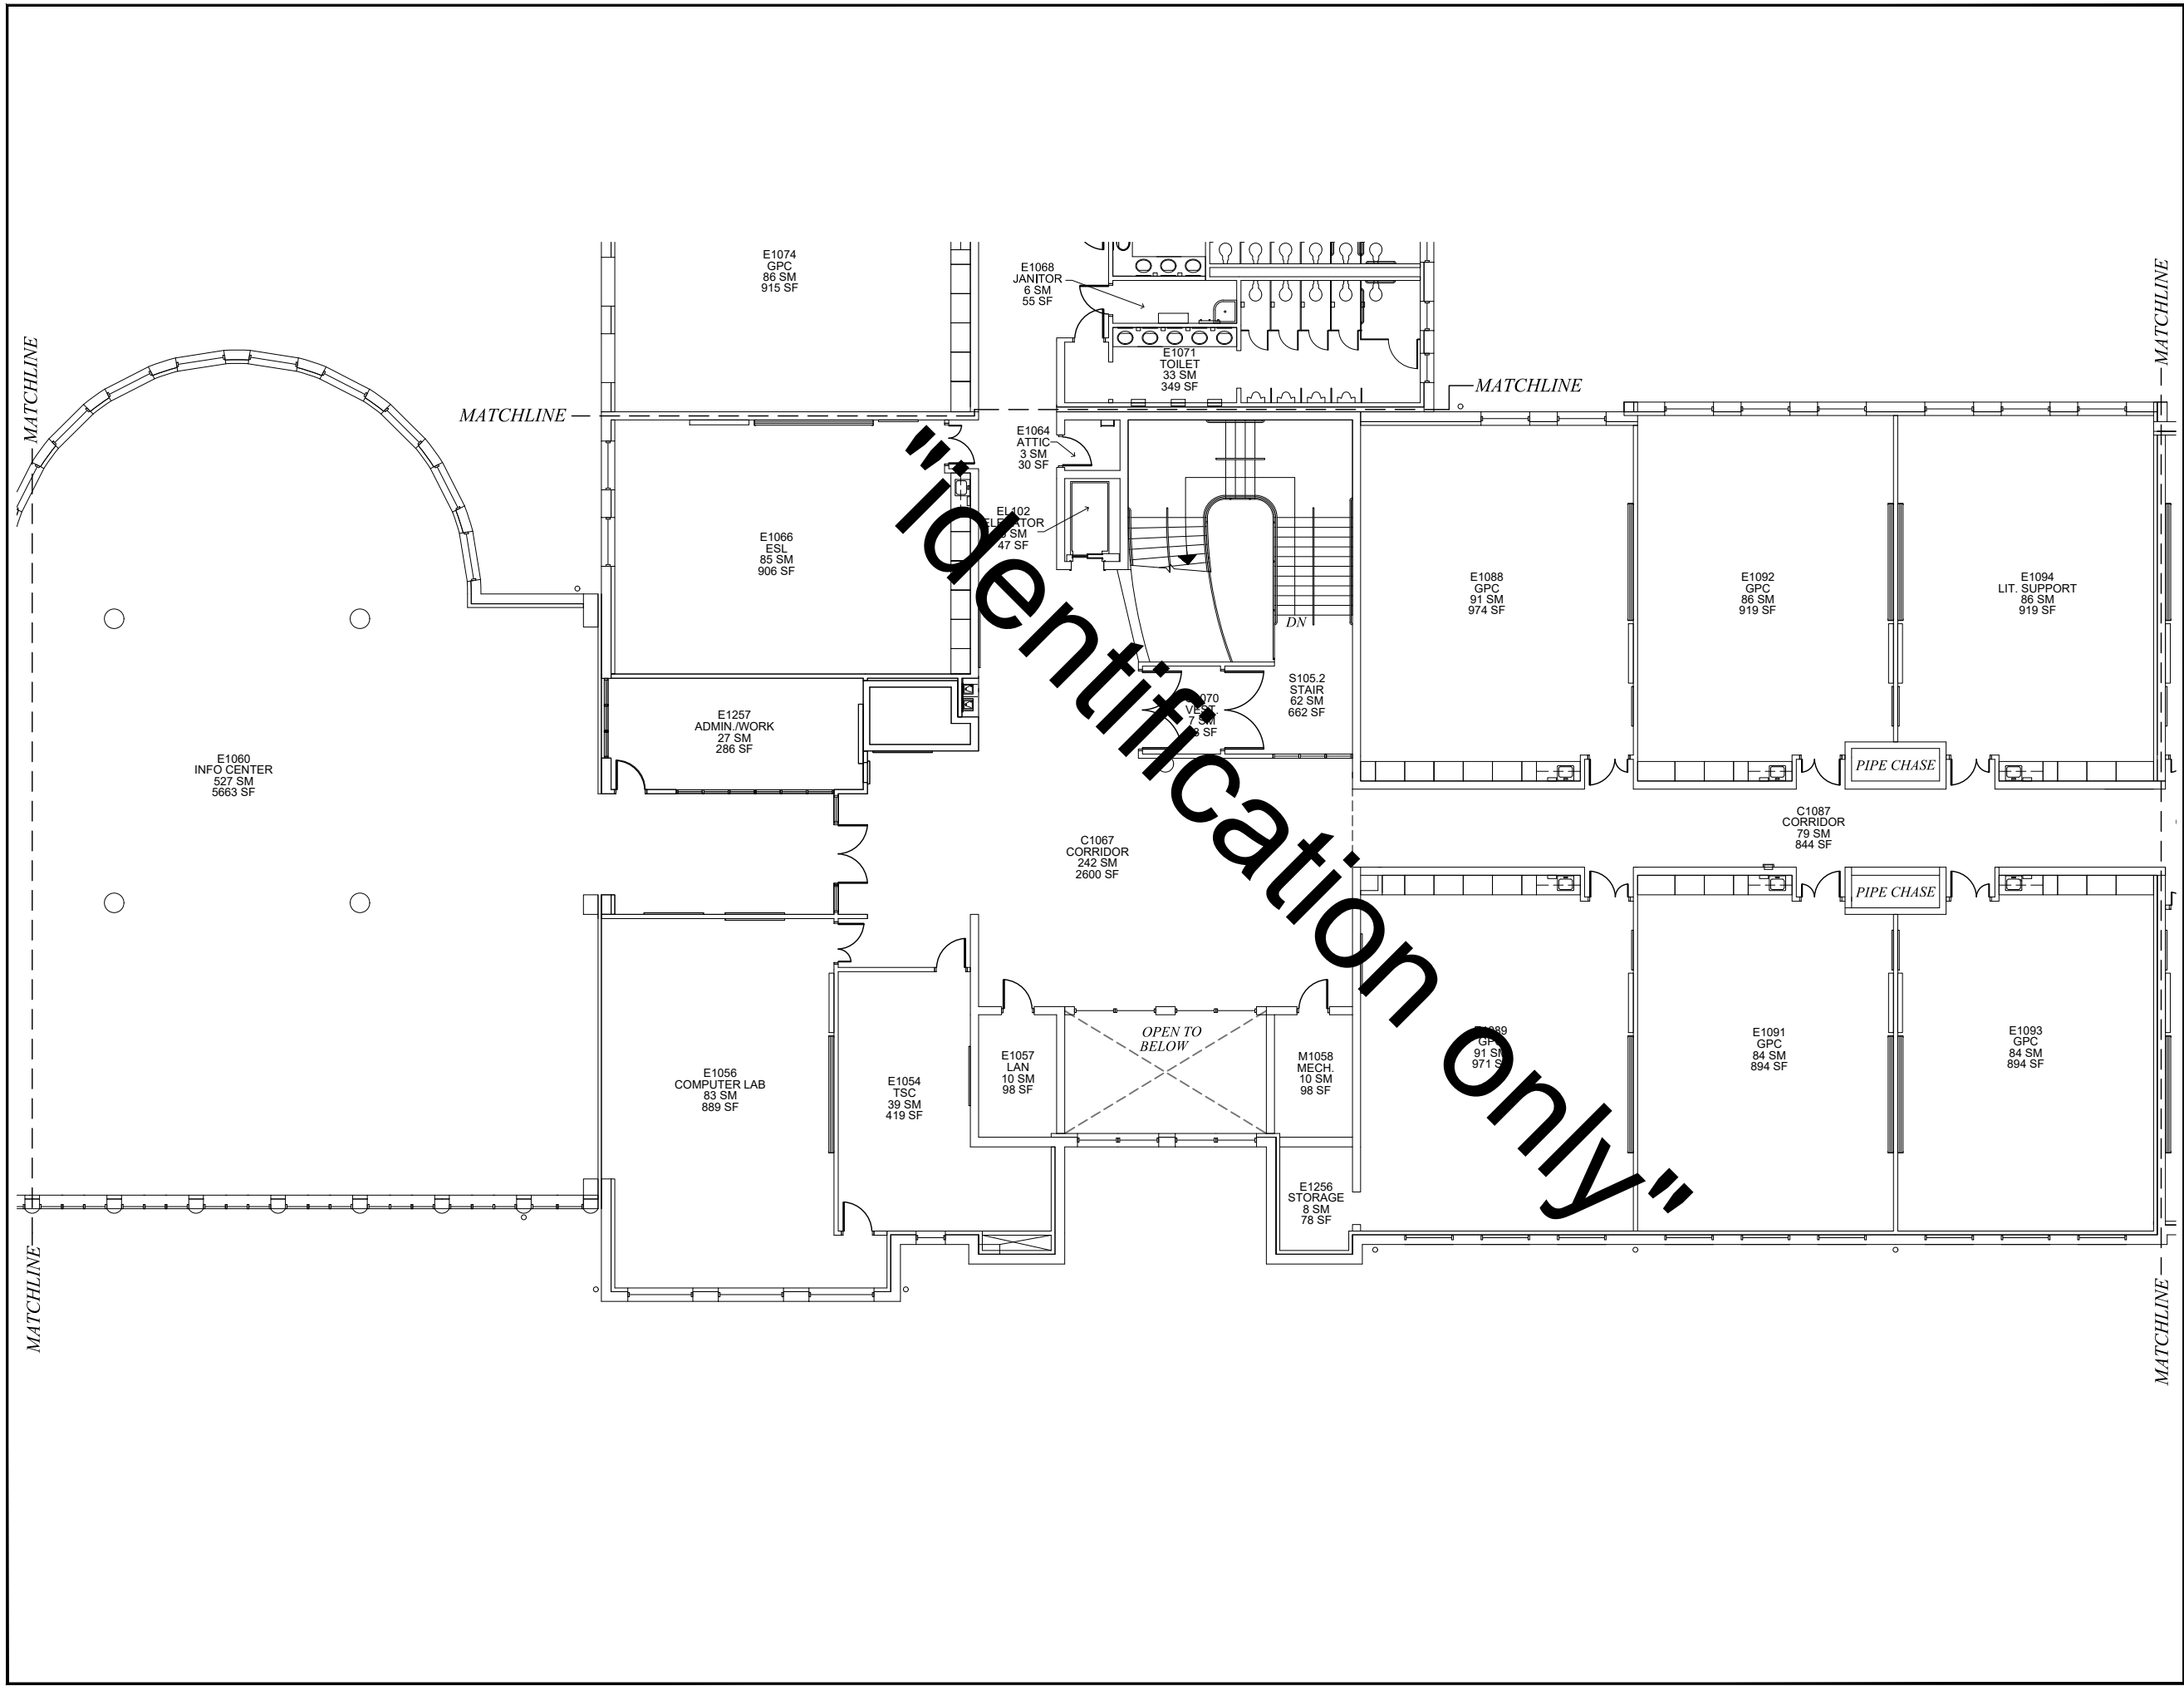

DOOR

SLIDING DOOR

ACCORDION PARTITION

STACK OR FOLDING PARTITION

WINDOW/GLAZING

HIGH WINDOW

SKYLIGHT

STOOP/STEP UP

STAIR

RAMP

ACCESS LADDER

COLD STORAGE

AREA CALCULATED @ 50 %

SLOPING ROOF

DRINKING FOUNTAIN

LAVATORY

SINK

TOILET

URINAL

LOCKER

LAN DISTRIBUTION FRAME

VENT HOOD

WALL SHELVING

UPPER CABINET

BASE CABINET

TEACHER CABINET

MATCHLINE

FLAT ROOF

TITLEBLOCK LEGEND

SHEET NAME:

BLDG #_FLOOR # (# IN SERIES)

KEY PLAN

NTS

WALK-IN COOLER 1

X700F

X700E

710

STORAGE

X700D

700

X700A

X700C

X700B

NORTH

Updated By: SPF

FUS Review: MRS

100% Submittal Date: 01 MAY 2020

0 2 4 8 16 FT

dodea

DEPARTMENT OF DEFENSE EDUCATION ACTIVITY

FACILITY UTILIZATION SURVEY

VICENZA ELEMENTARY SCHOOL/
VICENZA MIDDLE SCHOOL

BUILDING NUMBER: 700

COUNTRY: ITALY

INSTALLATION: US ARMY GARRISON ITALY

SITE: VICENZA FAMILY HOUSING

REGION-DISTRICT: DODEA EUROPE SOUTH


DoDAAC Number: HE5420, HE5467

Floor: LEVEL 2

Survey Date: JANUARY 2020


Sheet Name: 700_2 (5)

Sheet Seq: 23 of 29

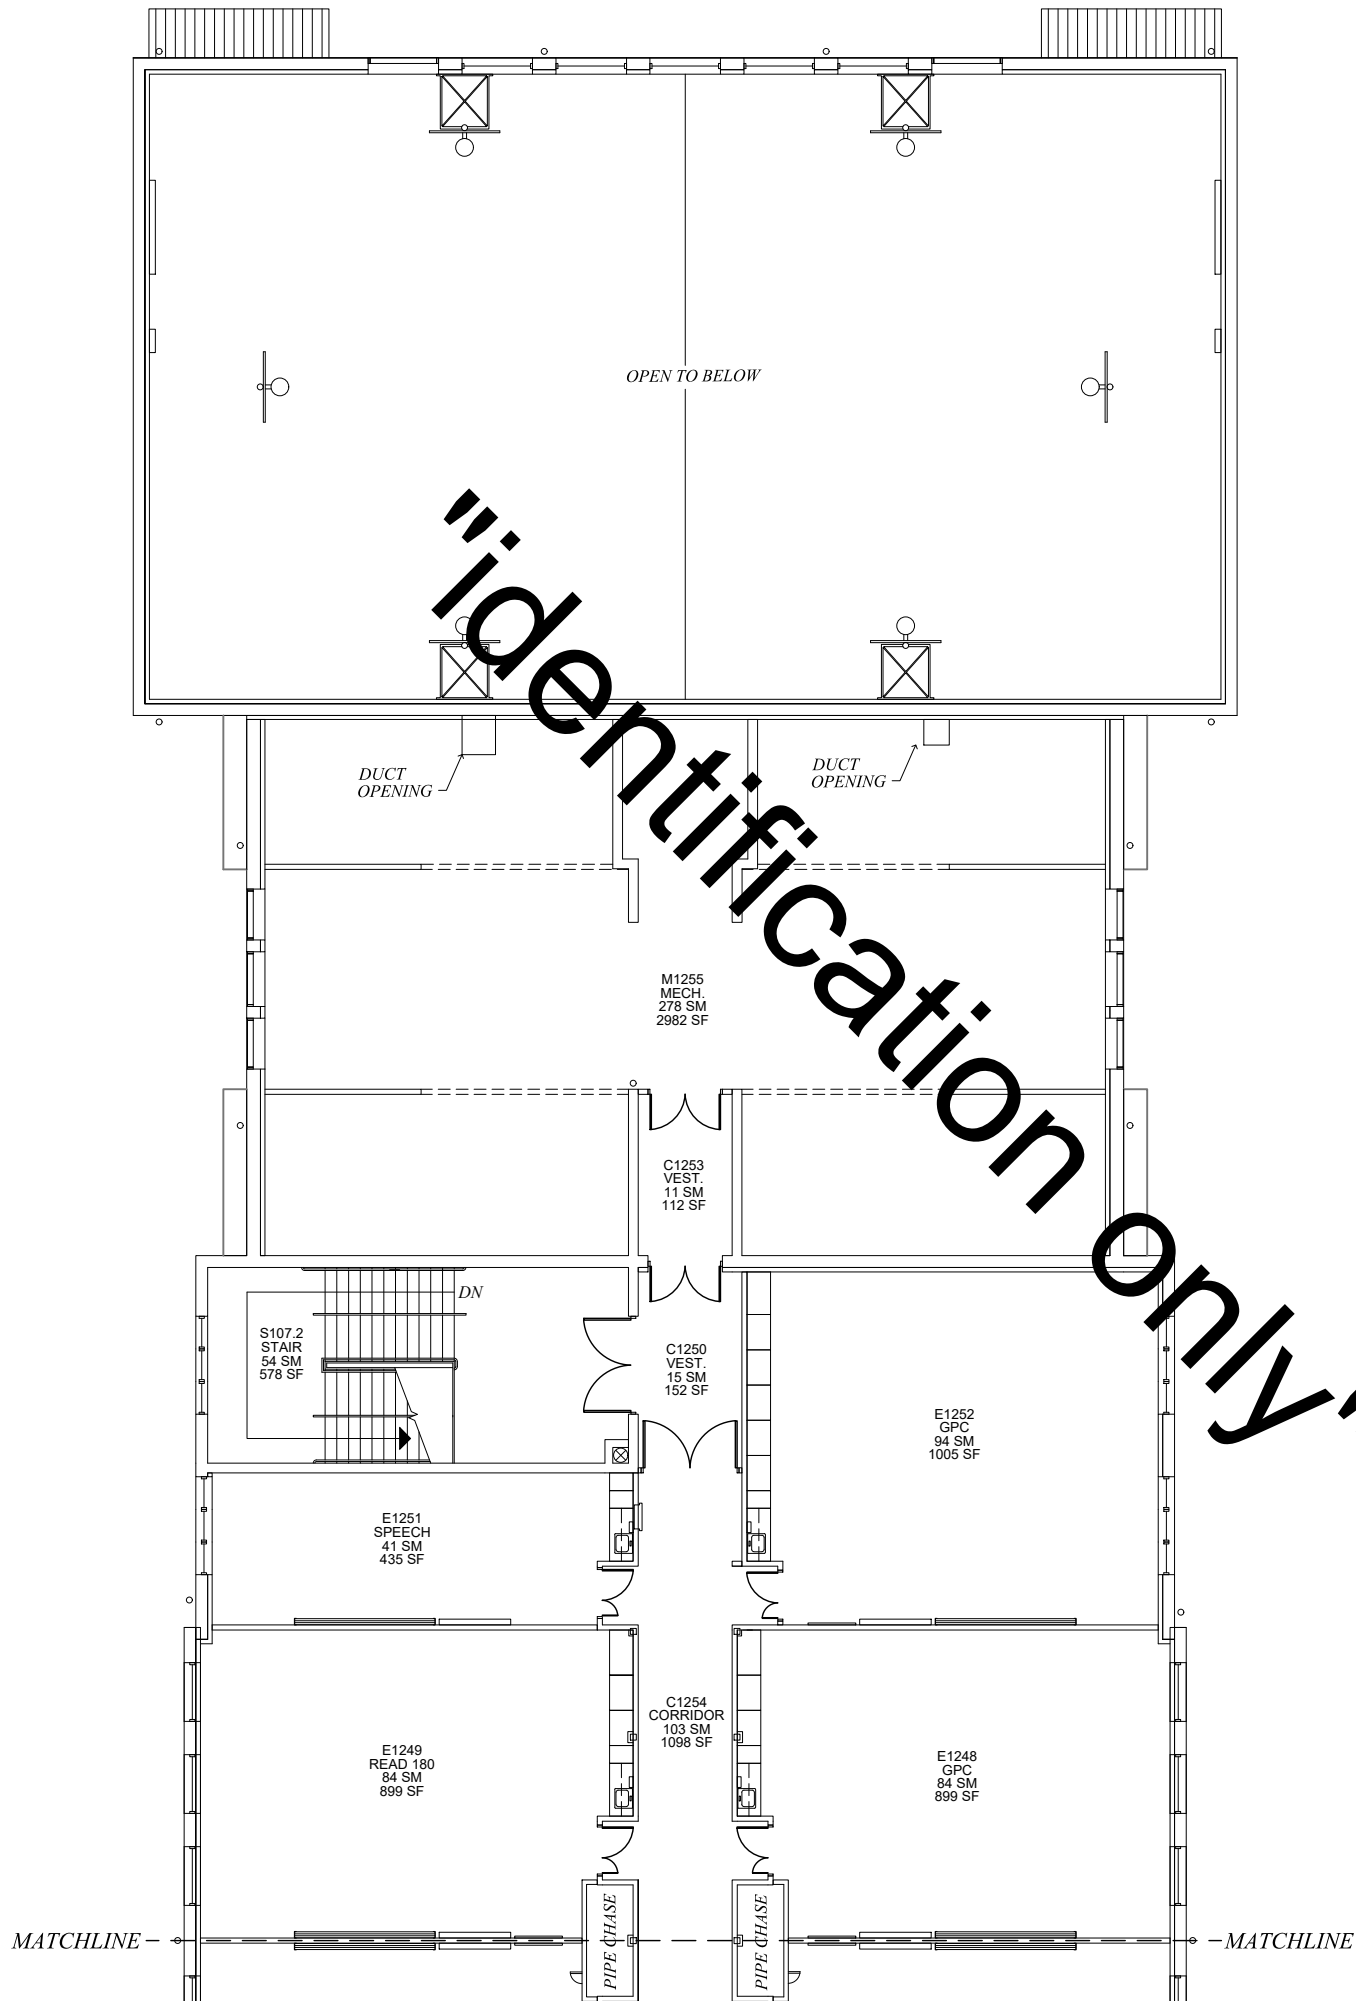

SYMBOL LEGEND	
DOOR	DRINKING FOUNTAIN
SLIDING DOOR	LAVATORY
ACCORDION PARTITION	SINK
STACK OR FOLDING PARTITION	TOILET
WINDOW/GLAZING	URINAL
HIGH WINDOW	LOCKER
SKYLIGHT	LAN DISTRIBUTION FRAME
STOOP/STEP UP	VENT HOOD
STAIR	WALL SHELVING
RAMP	UPPER CABINET
ACCESS LADDER	BASE CABINET
COLD STORAGE	TEACHER CABINET
AREA CALCULATED @ 50 %	MATCHLINE
SLOPING ROOF	FLAT ROOF

TITLEBLOCK LEGEND	
SHEET NAME:	BLDG #_FLOOR # (# IN SERIES)

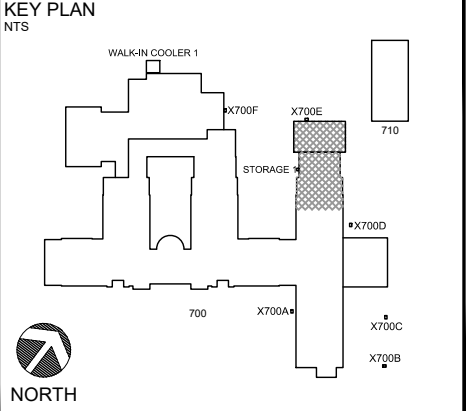


Updated By:	FUS Review:	100% Submittal Date:
SPF	MRS	01 MAY 2020
0 2 4 8 16 FT		

DEPARTMENT OF DEFENSE EDUCATION ACTIVITY
FACILITY UTILIZATION SURVEY


VICENZA ELEMENTARY SCHOOL/
VICENZA MIDDLE SCHOOL
BUILDING NUMBER: 700
COUNTRY: ITALY
INSTALLATION: US ARMY GARRISON ITALY
SITE: VICENZA FAMILY HOUSING
REGION-DISTRICT: DODEA EUROPE SOUTH

DoDAAC Number:	Floor:	Survey Date:
HE5420, HE5467	LEVEL 2	JANUARY 2020
Sheet Name:	Sheet Seq:	
700_2 (6)	24 of 29	

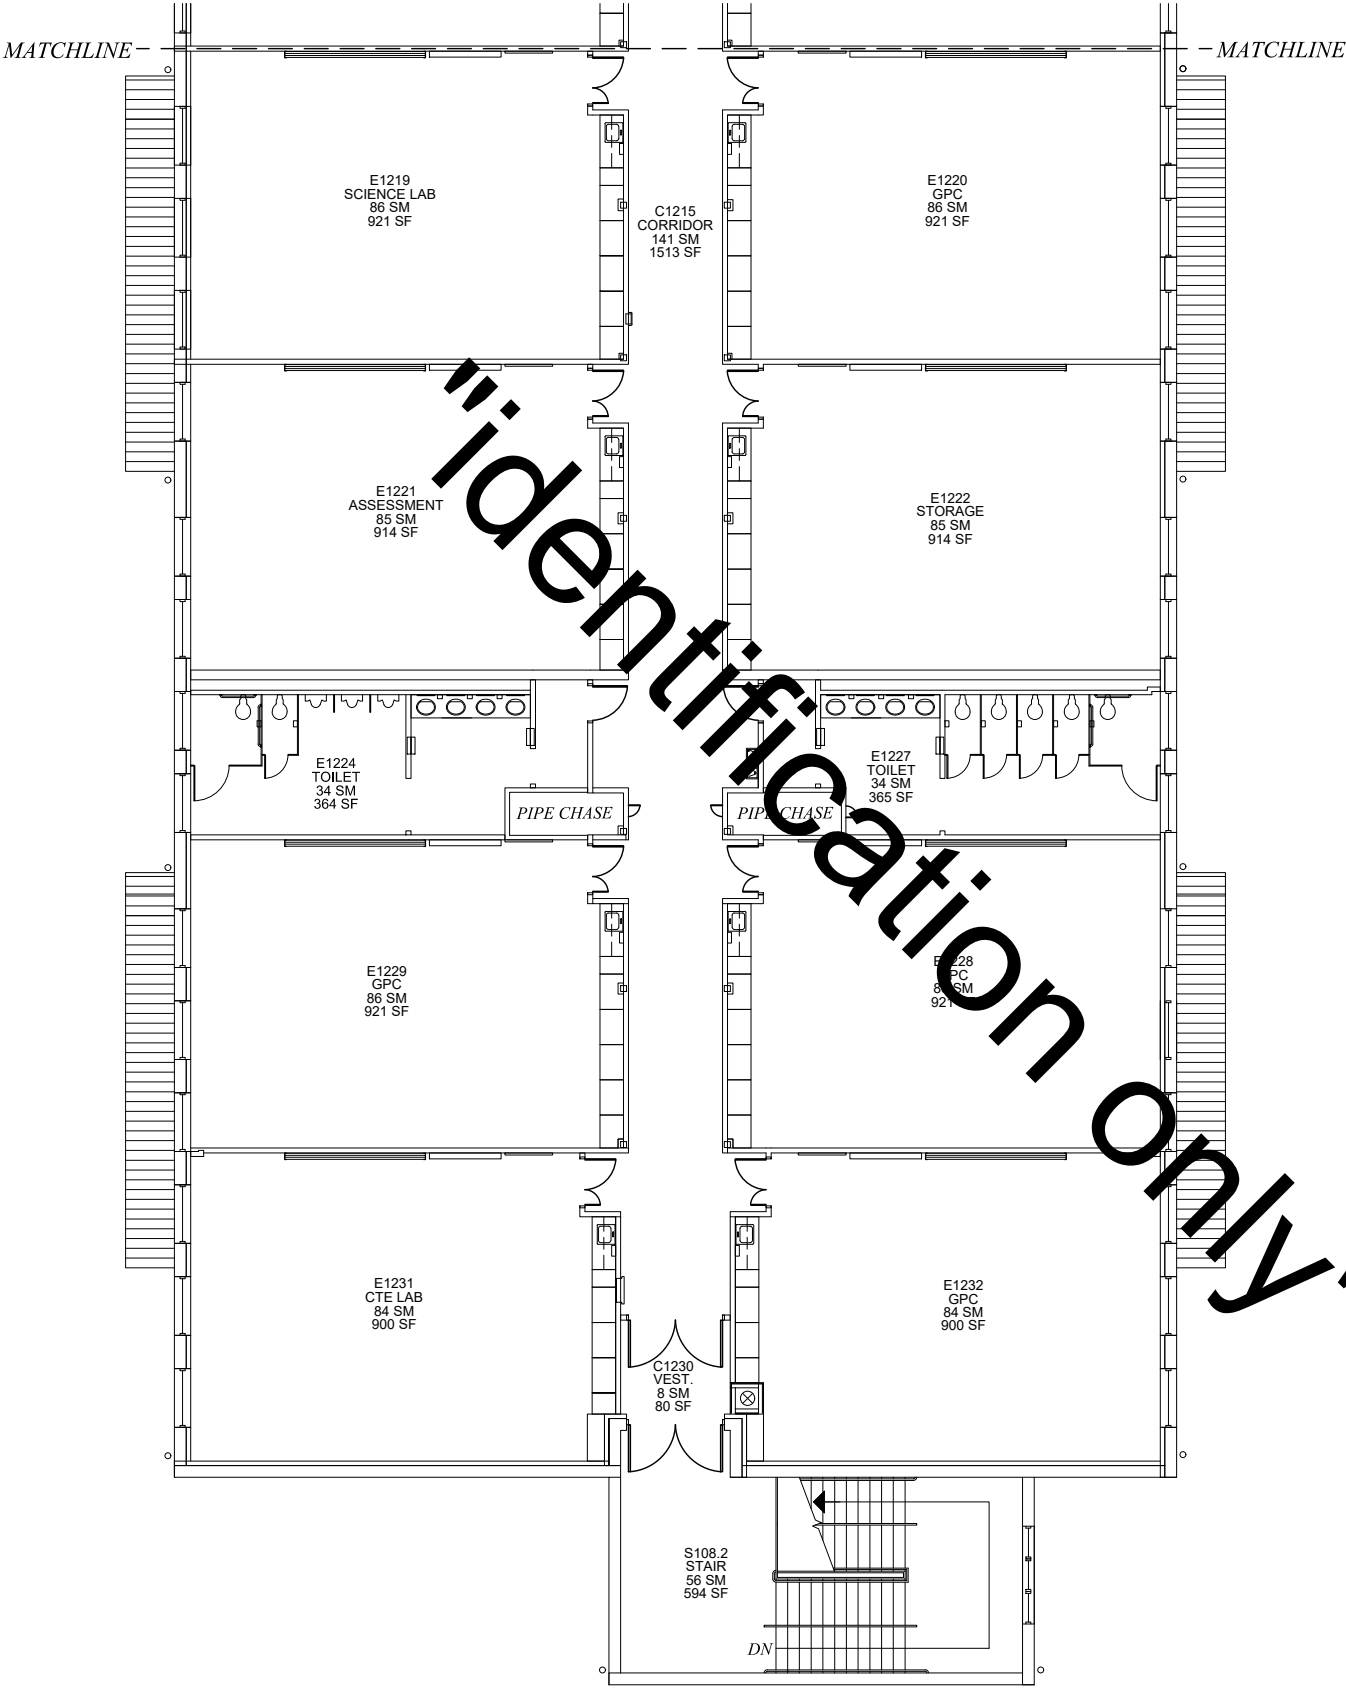

SYMBOL LEGEND	
 DOOR	 DRINKING FOUNTAIN
 SLIDING DOOR	 LAVATORY
 ACCORDION PARTITION	 SINK
 STACK OR FOLDING PARTITION	 TOILET
 WINDOW/GLAZING	 URINAL
 HIGH WINDOW	 LOCKER
 SKYLIGHT	 LAN DISTRIBUTION FRAME
 STOOP/STEP UP	 VENT HOOD
 STAIR	 WALL SHELVING
 RAMP	 UPPER CABINET
 ACCESS LADDER	 BASE CABINET
 COLD STORAGE	 TEACHER CABINET
 AREA CALCULATED @ 50 %	 MATCHLINE
 SLOPING ROOF	 FLAT ROOF

TITLEBLOCK LEGEND	
SHEET NAME:	BLDG #_FLOOR # (# IN SERIES)

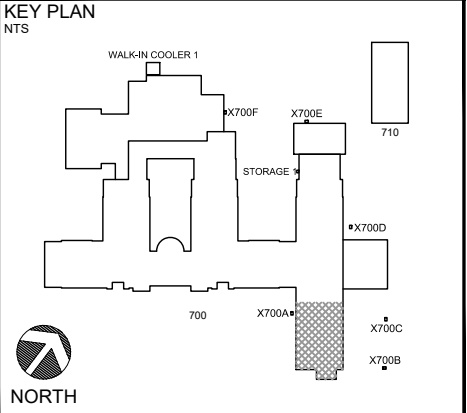

Updated By: SPF	FUS Review: MRS	100% Submittal Date: 01 MAY 2020
0 2 4 8 16 FT		




DEPARTMENT OF DEFENSE EDUCATION ACTIVITY

FACILITY UTILIZATION SURVEY

VICENZA ELEMENTARY SCHOOL/
VICENZA MIDDLE SCHOOL
BUILDING NUMBER: 700
COUNTRY: ITALY
INSTALLATION: US ARMY GARRISON ITALY
SITE: VICENZA FAMILY HOUSING
REGION-DISTRICT: DODEA EUROPE SOUTH

DoDAAC Number: HE5420, HE5467	Floor: LEVEL 2	Survey Date: JANUARY 2020
Sheet Name: 700_2 (8)	Sheet Seq: 26 of 29	

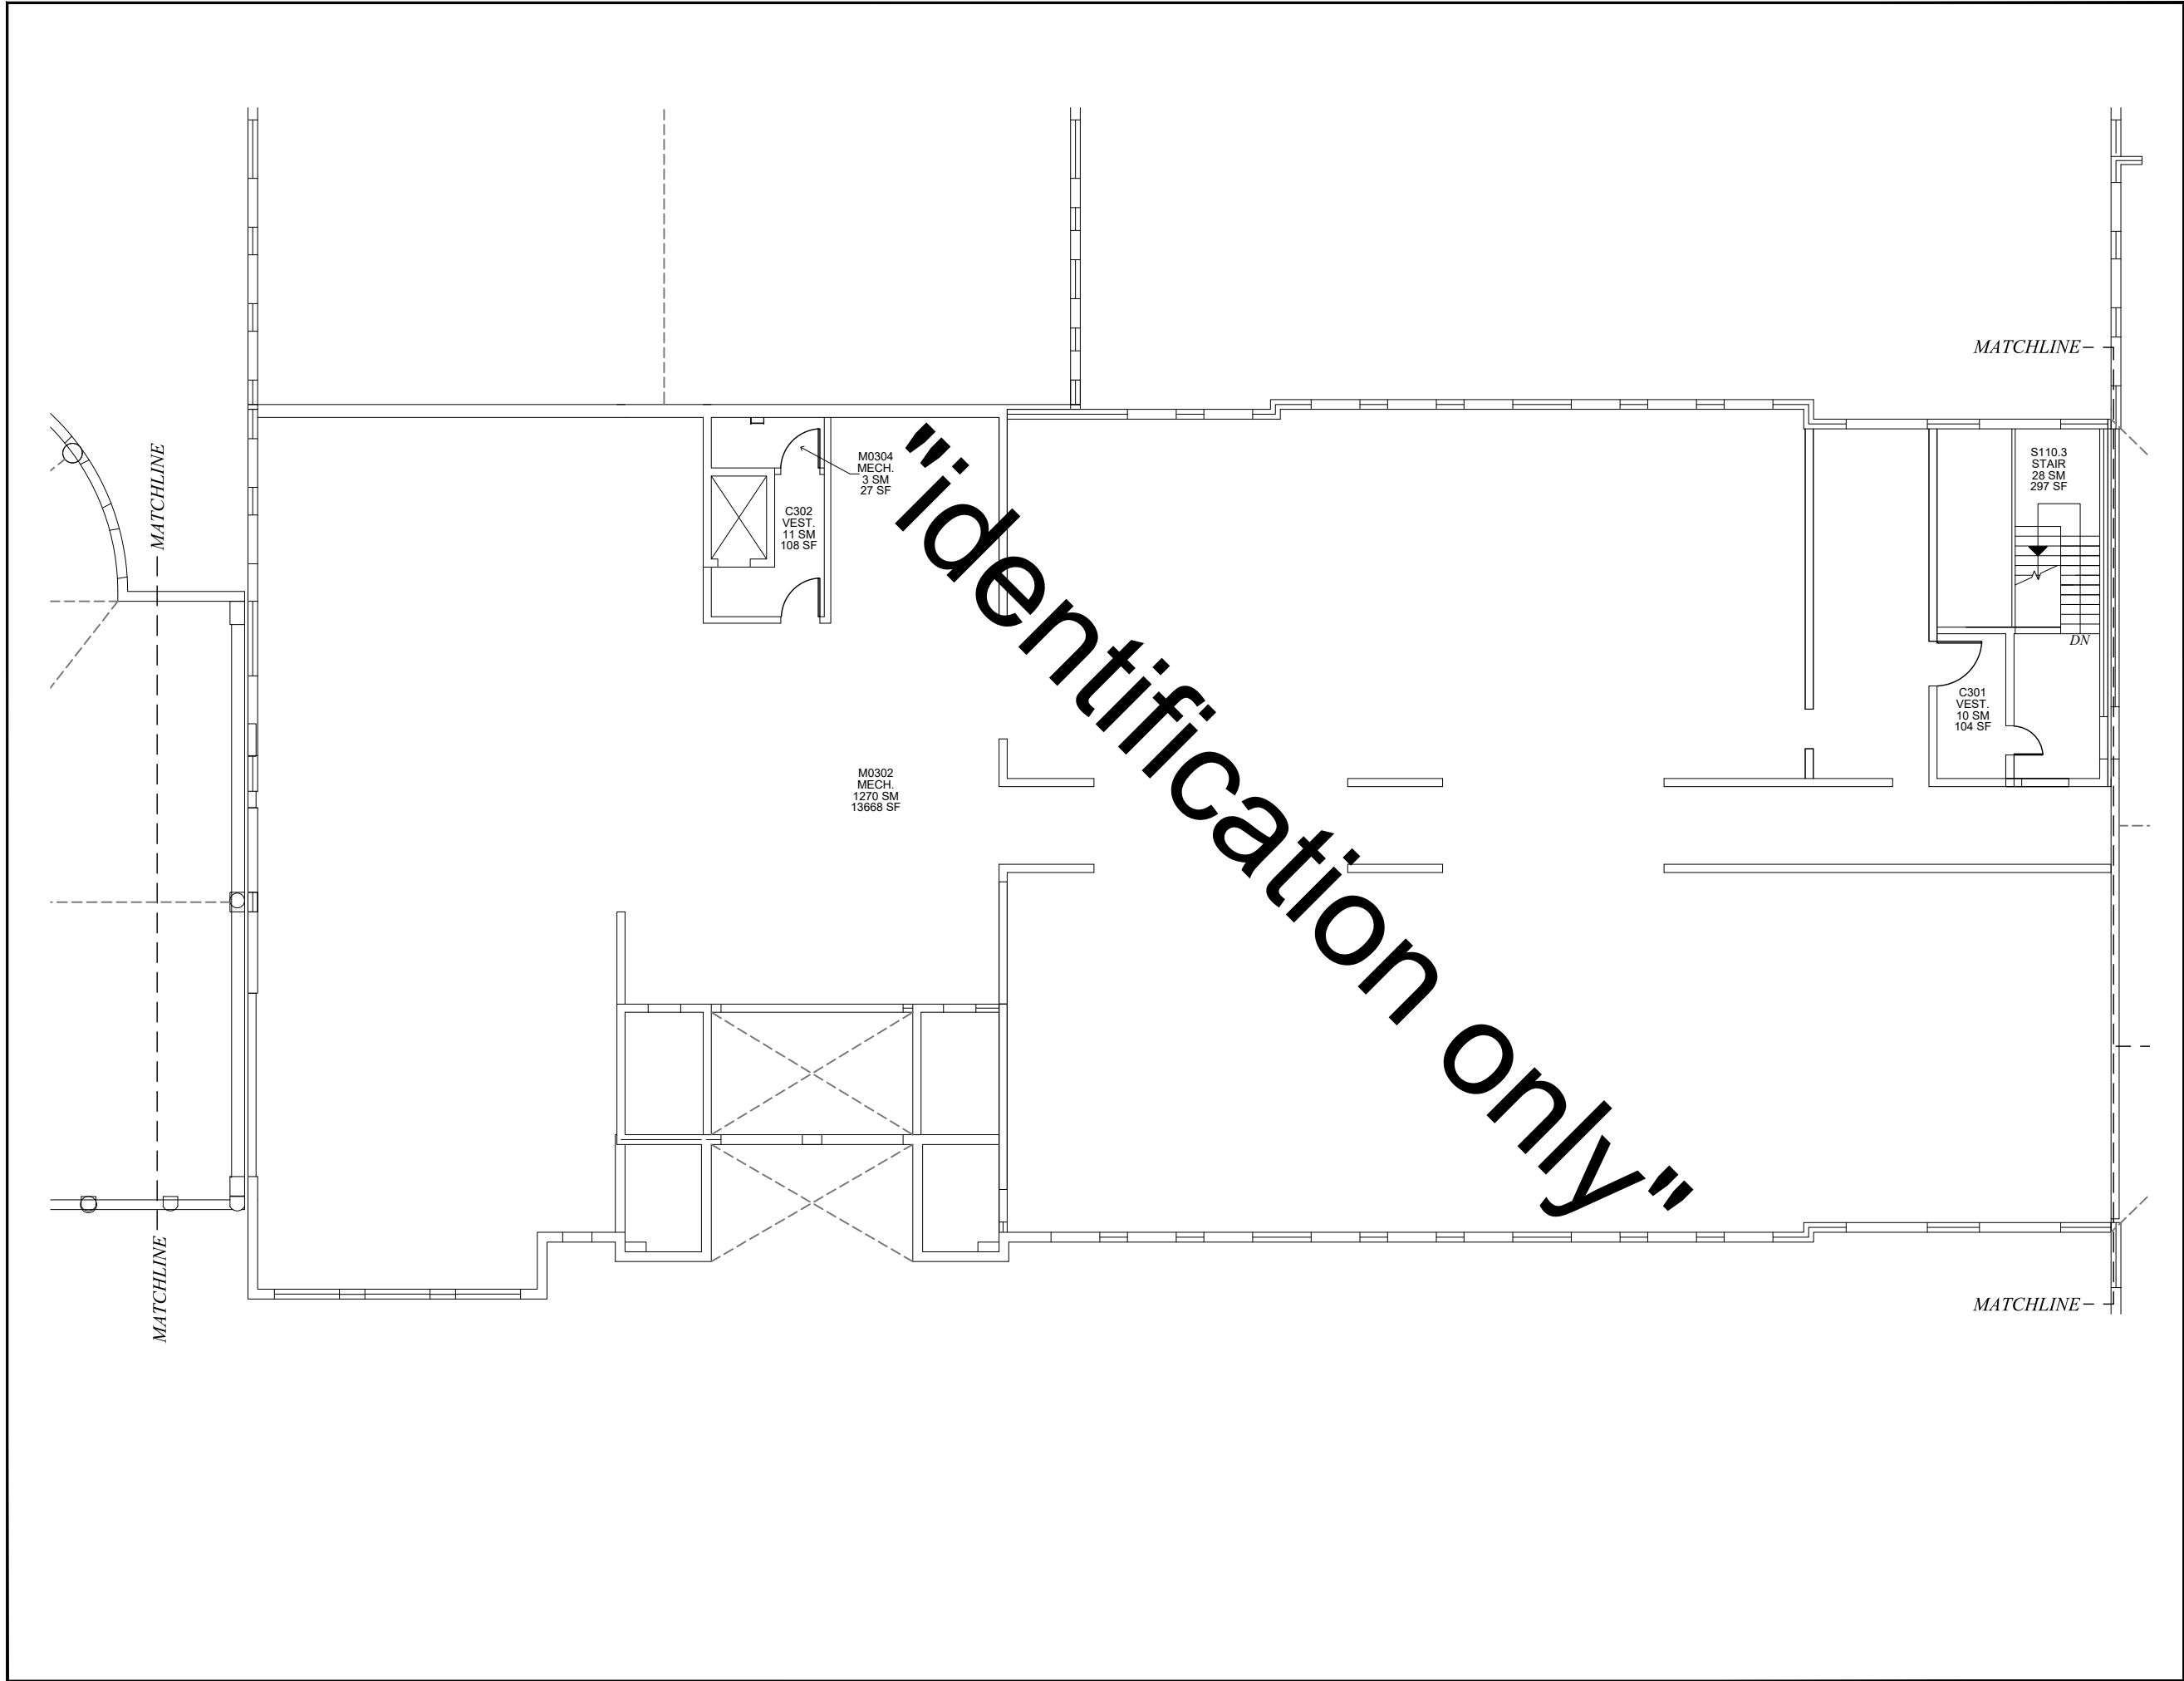

DOOR

SLIDING DOOR

ACCORDION PARTITION

STACK OR FOLDING PARTITION

WINDOW/GLAZING

HIGH WINDOW

SKYLIGHT

STOOP/STEP UP

STAIR

RAMP

ACCESS LADDER

COLD STORAGE

AREA CALCULATED @ 50 %

SLOPING ROOF

DRINKING FOUNTAIN

LAVATORY

SINK

TOILET

URINAL

LOCKER

LAN DISTRIBUTION FRAME

VENT HOOD

WALL SHELVING

UPPER CABINET

BASE CABINET

TEACHER CABINET

MATCHLINE

FLAT ROOF

TITLEBLOCK LEGEND

SHEET NAME:

BLDG #_FLOOR # (# IN SERIES)

KEY PLAN

NTS

WALK-IN COOLER 1

X700F

X700E

710

STORAGE

X700D

700

X700A

X700C

X700B

NORTH

Updated By: SPF

FUS Review: MRS

100% Submittal Date: 01 MAY 2020

0 2 4 8 16 FT

dodea

DEPARTMENT OF DEFENSE EDUCATION ACTIVITY

FACILITY UTILIZATION SURVEY

VICENZA ELEMENTARY SCHOOL/
VICENZA MIDDLE SCHOOL

BUILDING NUMBER: 700

COUNTRY: ITALY

INSTALLATION: US ARMY GARRISON ITALY

SITE: VICENZA FAMILY HOUSING

REGION-DISTRICT: DODEA EUROPE SOUTH


DoDAAC Number: HE5420, HE5467

Floor: LEVEL 3

Survey Date: JANUARY 2020


Sheet Name: 700_3 (3)

Sheet Seq: 28 of 29

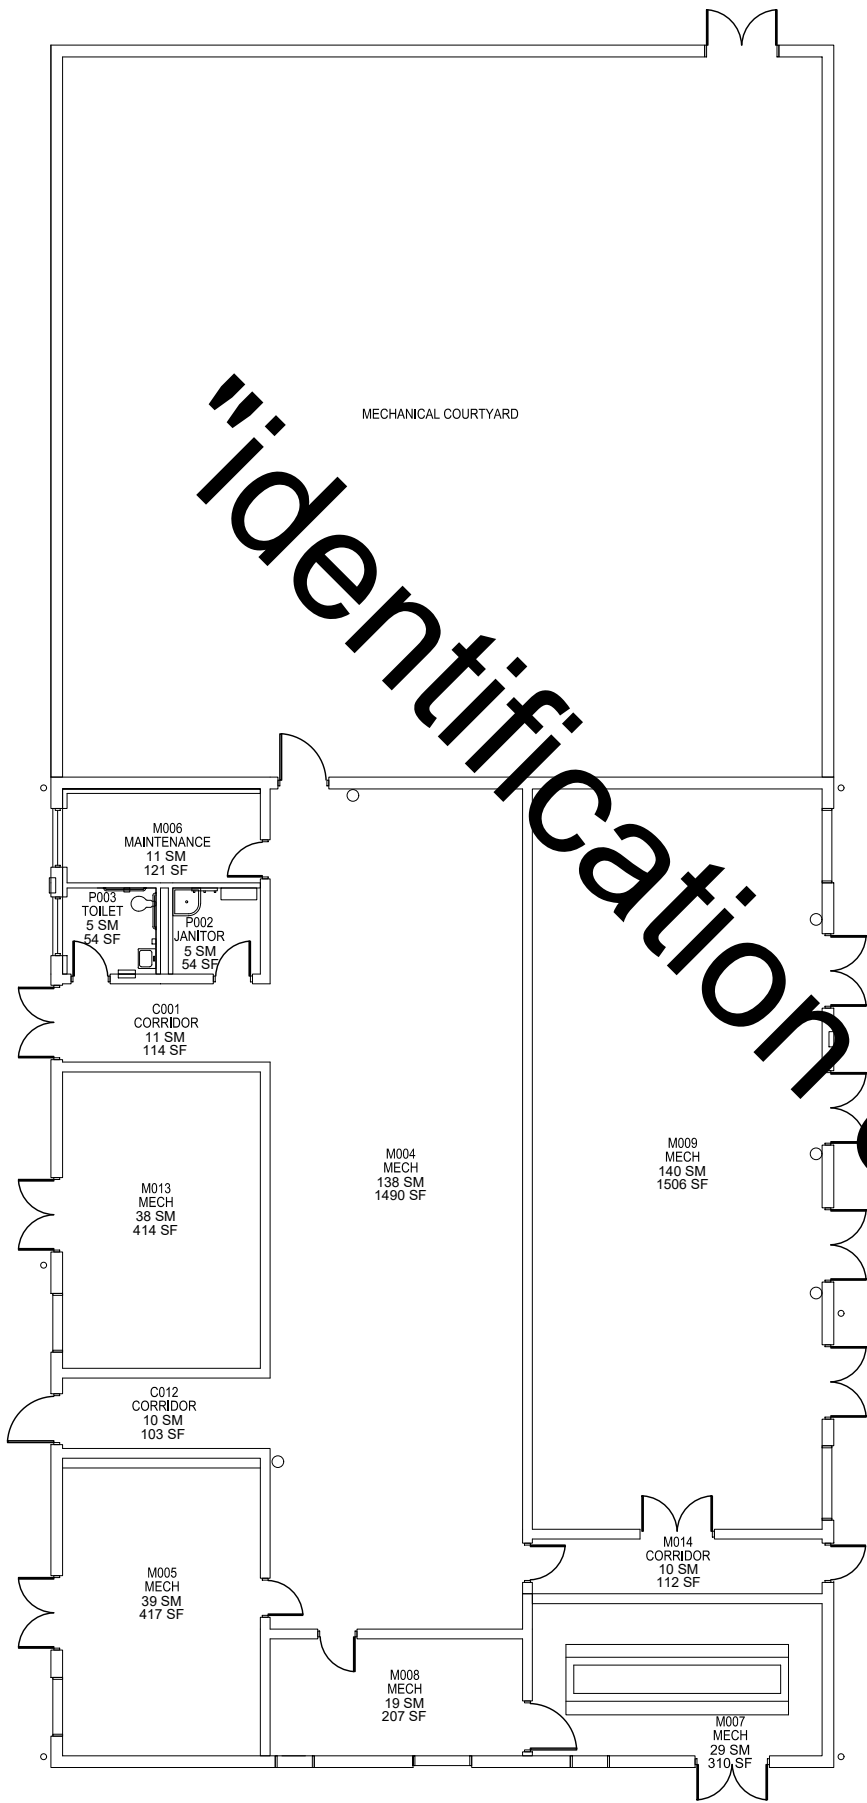

SYMBOL LEGEND	
	DOOR
	DRINKING FOUNTAIN
	SLIDING DOOR
	LAVATORY
	ACCORDION PARTITION
	SINK
	STACK OR FOLDING PARTITION
	TOILET
	WINDOW/GLAZING
	URINAL
	HIGH WINDOW
	LOCKER
	SKYLIGHT
	LAN DISTRIBUTION FRAME
	STOOP/STEP UP
	VENT HOOD
	STAIR
	WALL SHELVING
	RAMP
	UPPER CABINET
	ACCESS LADDER
	BASE CABINET
	COLD STORAGE
	TEACHER CABINET
	AREA CALCULATED @ 50 %
	MATCHLINE
	SLOPING ROOF
	FLAT ROOF

TITLEBLOCK LEGEND	
SHEET NAME:	BLDG #_FLOOR # (# IN SERIES)

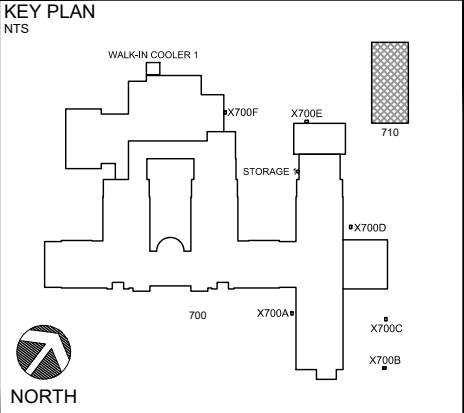

Updated By:	FUS Review:	100% Submittal Date:
SPF	MRS	01 MAY 2020
0 2 4 8 16 FT		

DEPARTMENT OF DEFENSE EDUCATION ACTIVITY
FACILITY UTILIZATION SURVEY

VICENZA ELEMENTARY SCHOOL/
VICENZA MIDDLE SCHOOL
BUILDING NUMBER: 710
COUNTRY: ITALY
INSTALLATION: US ARMY GARRISON ITALY
SITE: VICENZA FAMILY HOUSING
REGION-DISTRICT: DODEA EUROPE SOUTH

DoDAAC Number:	Floor:	Survey Date:
HE5420, HE5467	LEVEL 1	JANUARY 2020
Sheet Name:	Sheet Seq:	
710_1 (1)	29 of 29	