


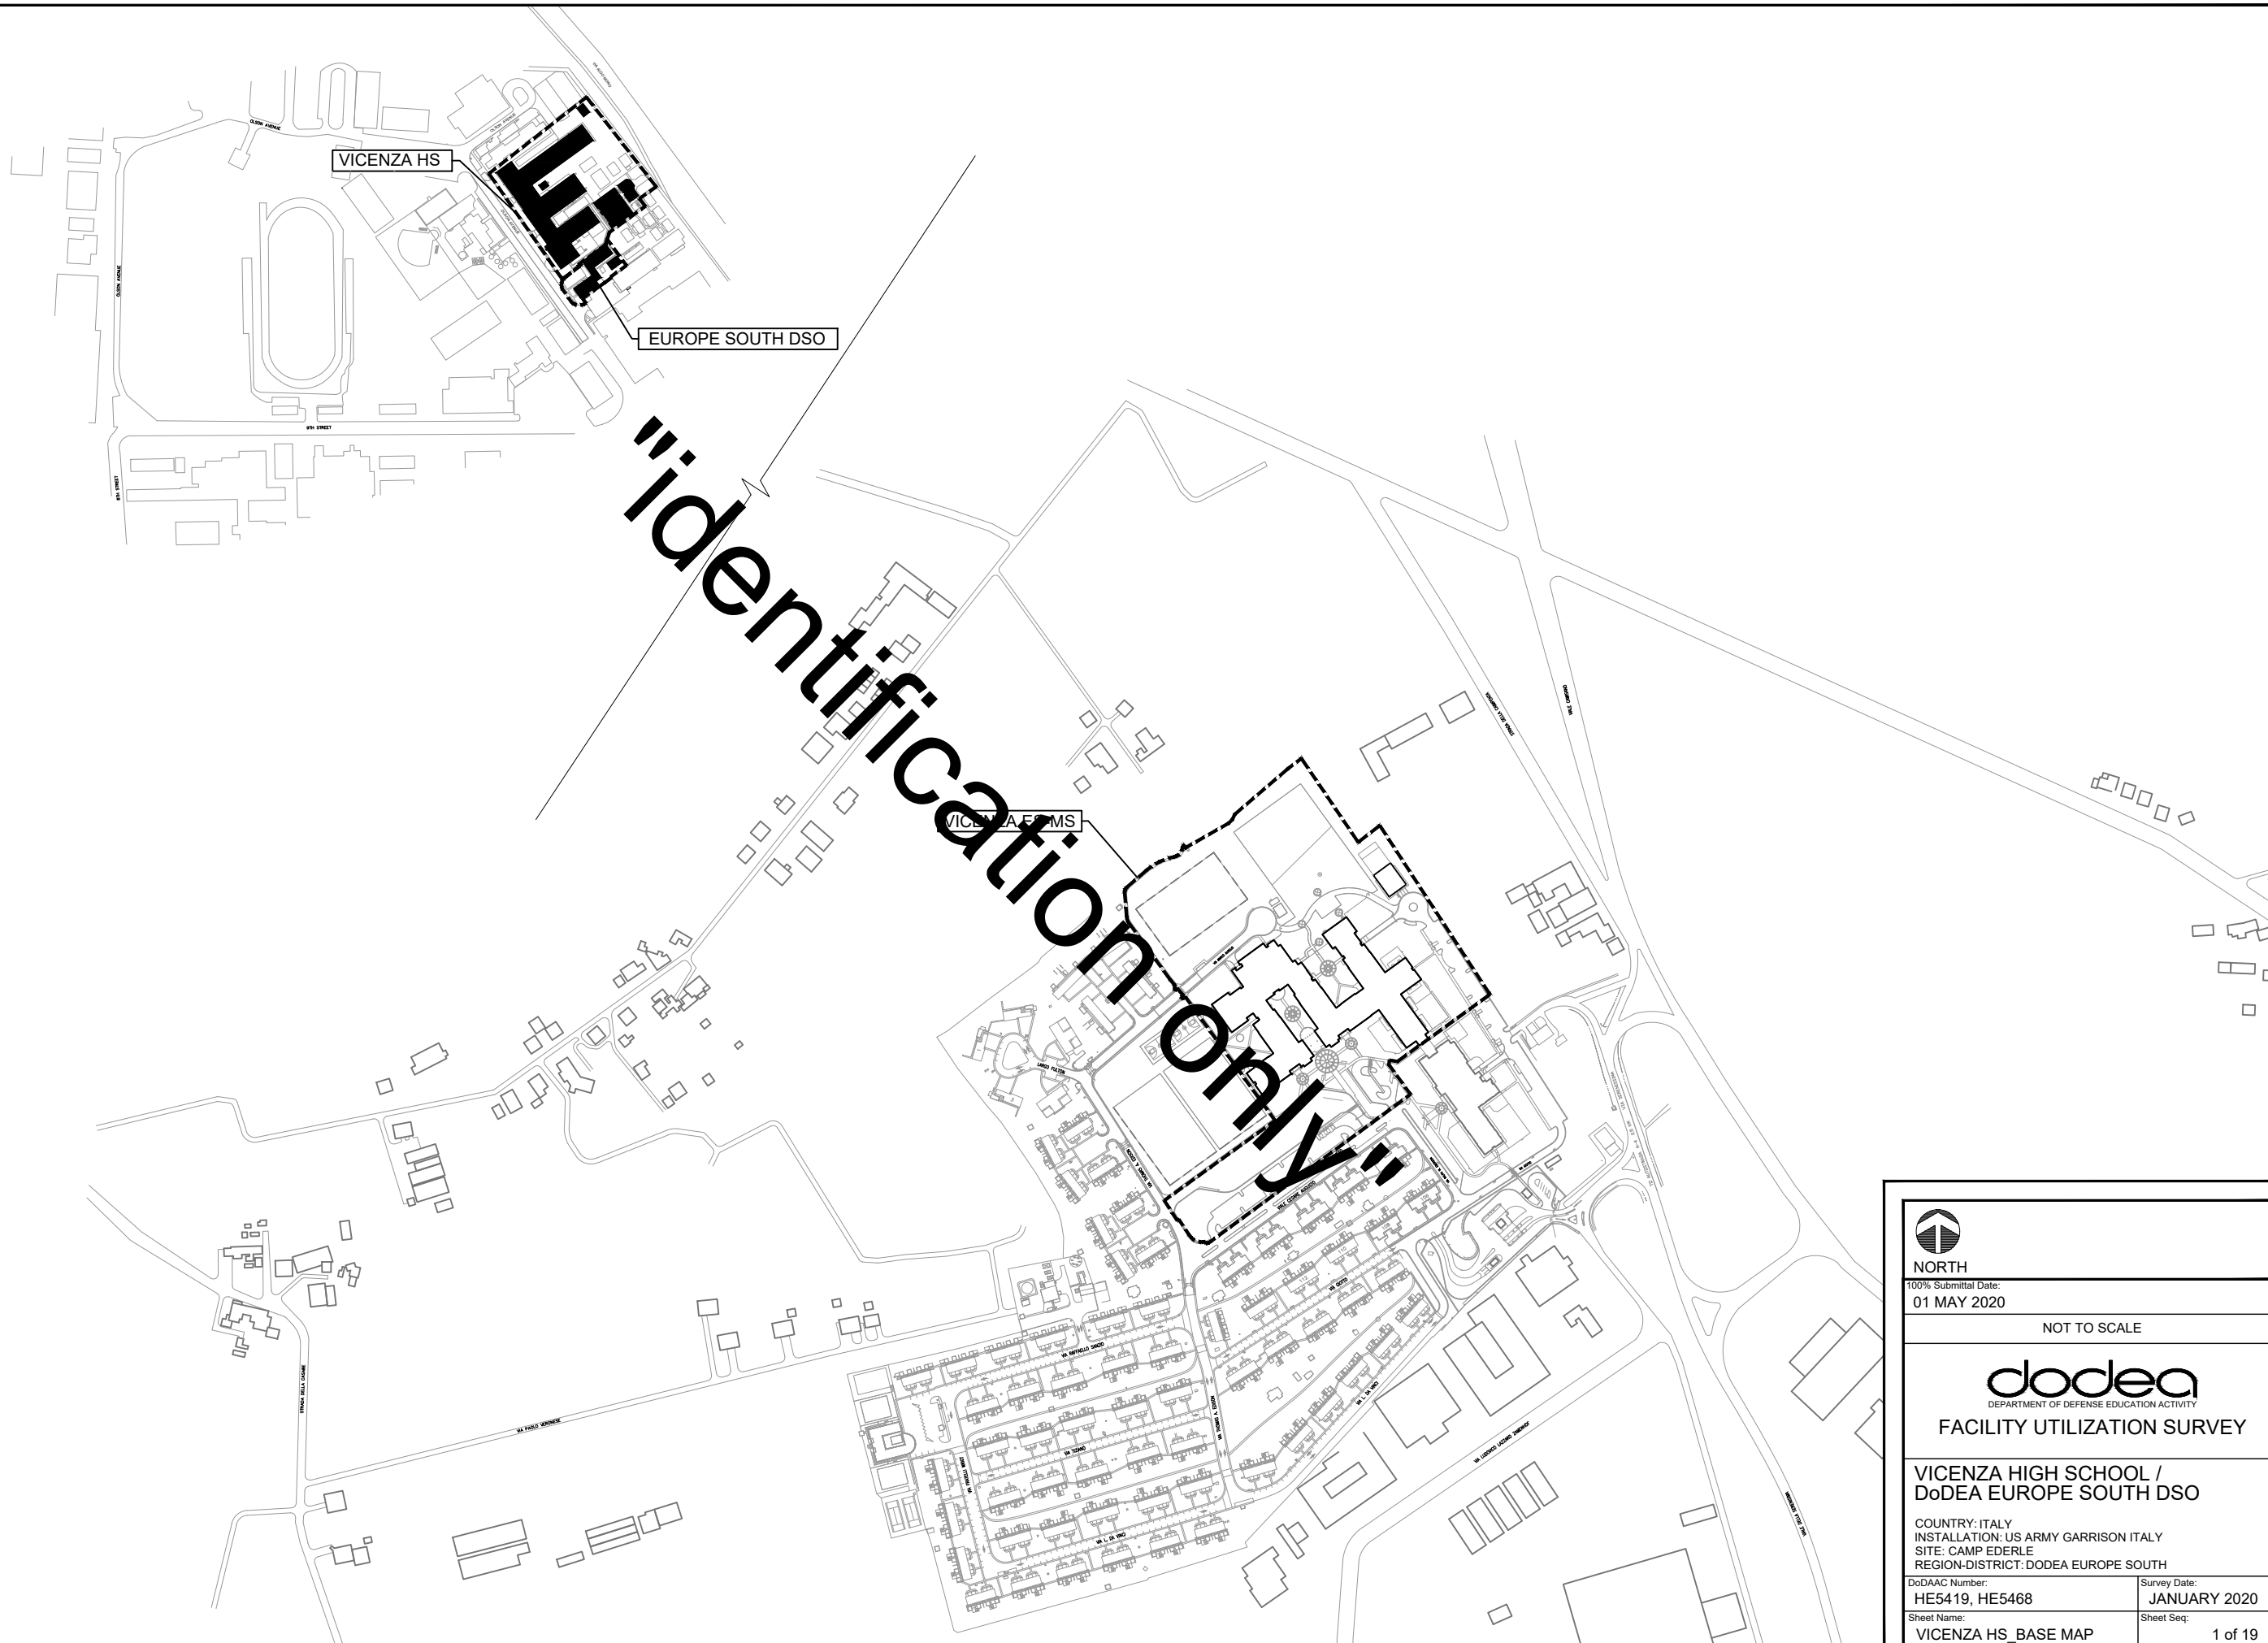

NORTH

100% Submittal Date:
01 MAY 2020

NOT TO SCALE



FACILITY UTILIZATION SURVEY

VICENZA HIGH SCHOOL /
DoDEA EUROPE SOUTH DSO

COUNTRY: ITALY
INSTALLATION: US ARMY GARRISON ITALY
SITE: CAMP EDERLE
REGION-DISTRICT: DODEA EUROPE SOUTH

DoDAAC Number:
HE5419, HE5468


Survey Date:	JANUARY 2020
--------------	--------------


Sheet Name:

VICENZA HS_BASE MAP

Sheet Seq:

1 of 19

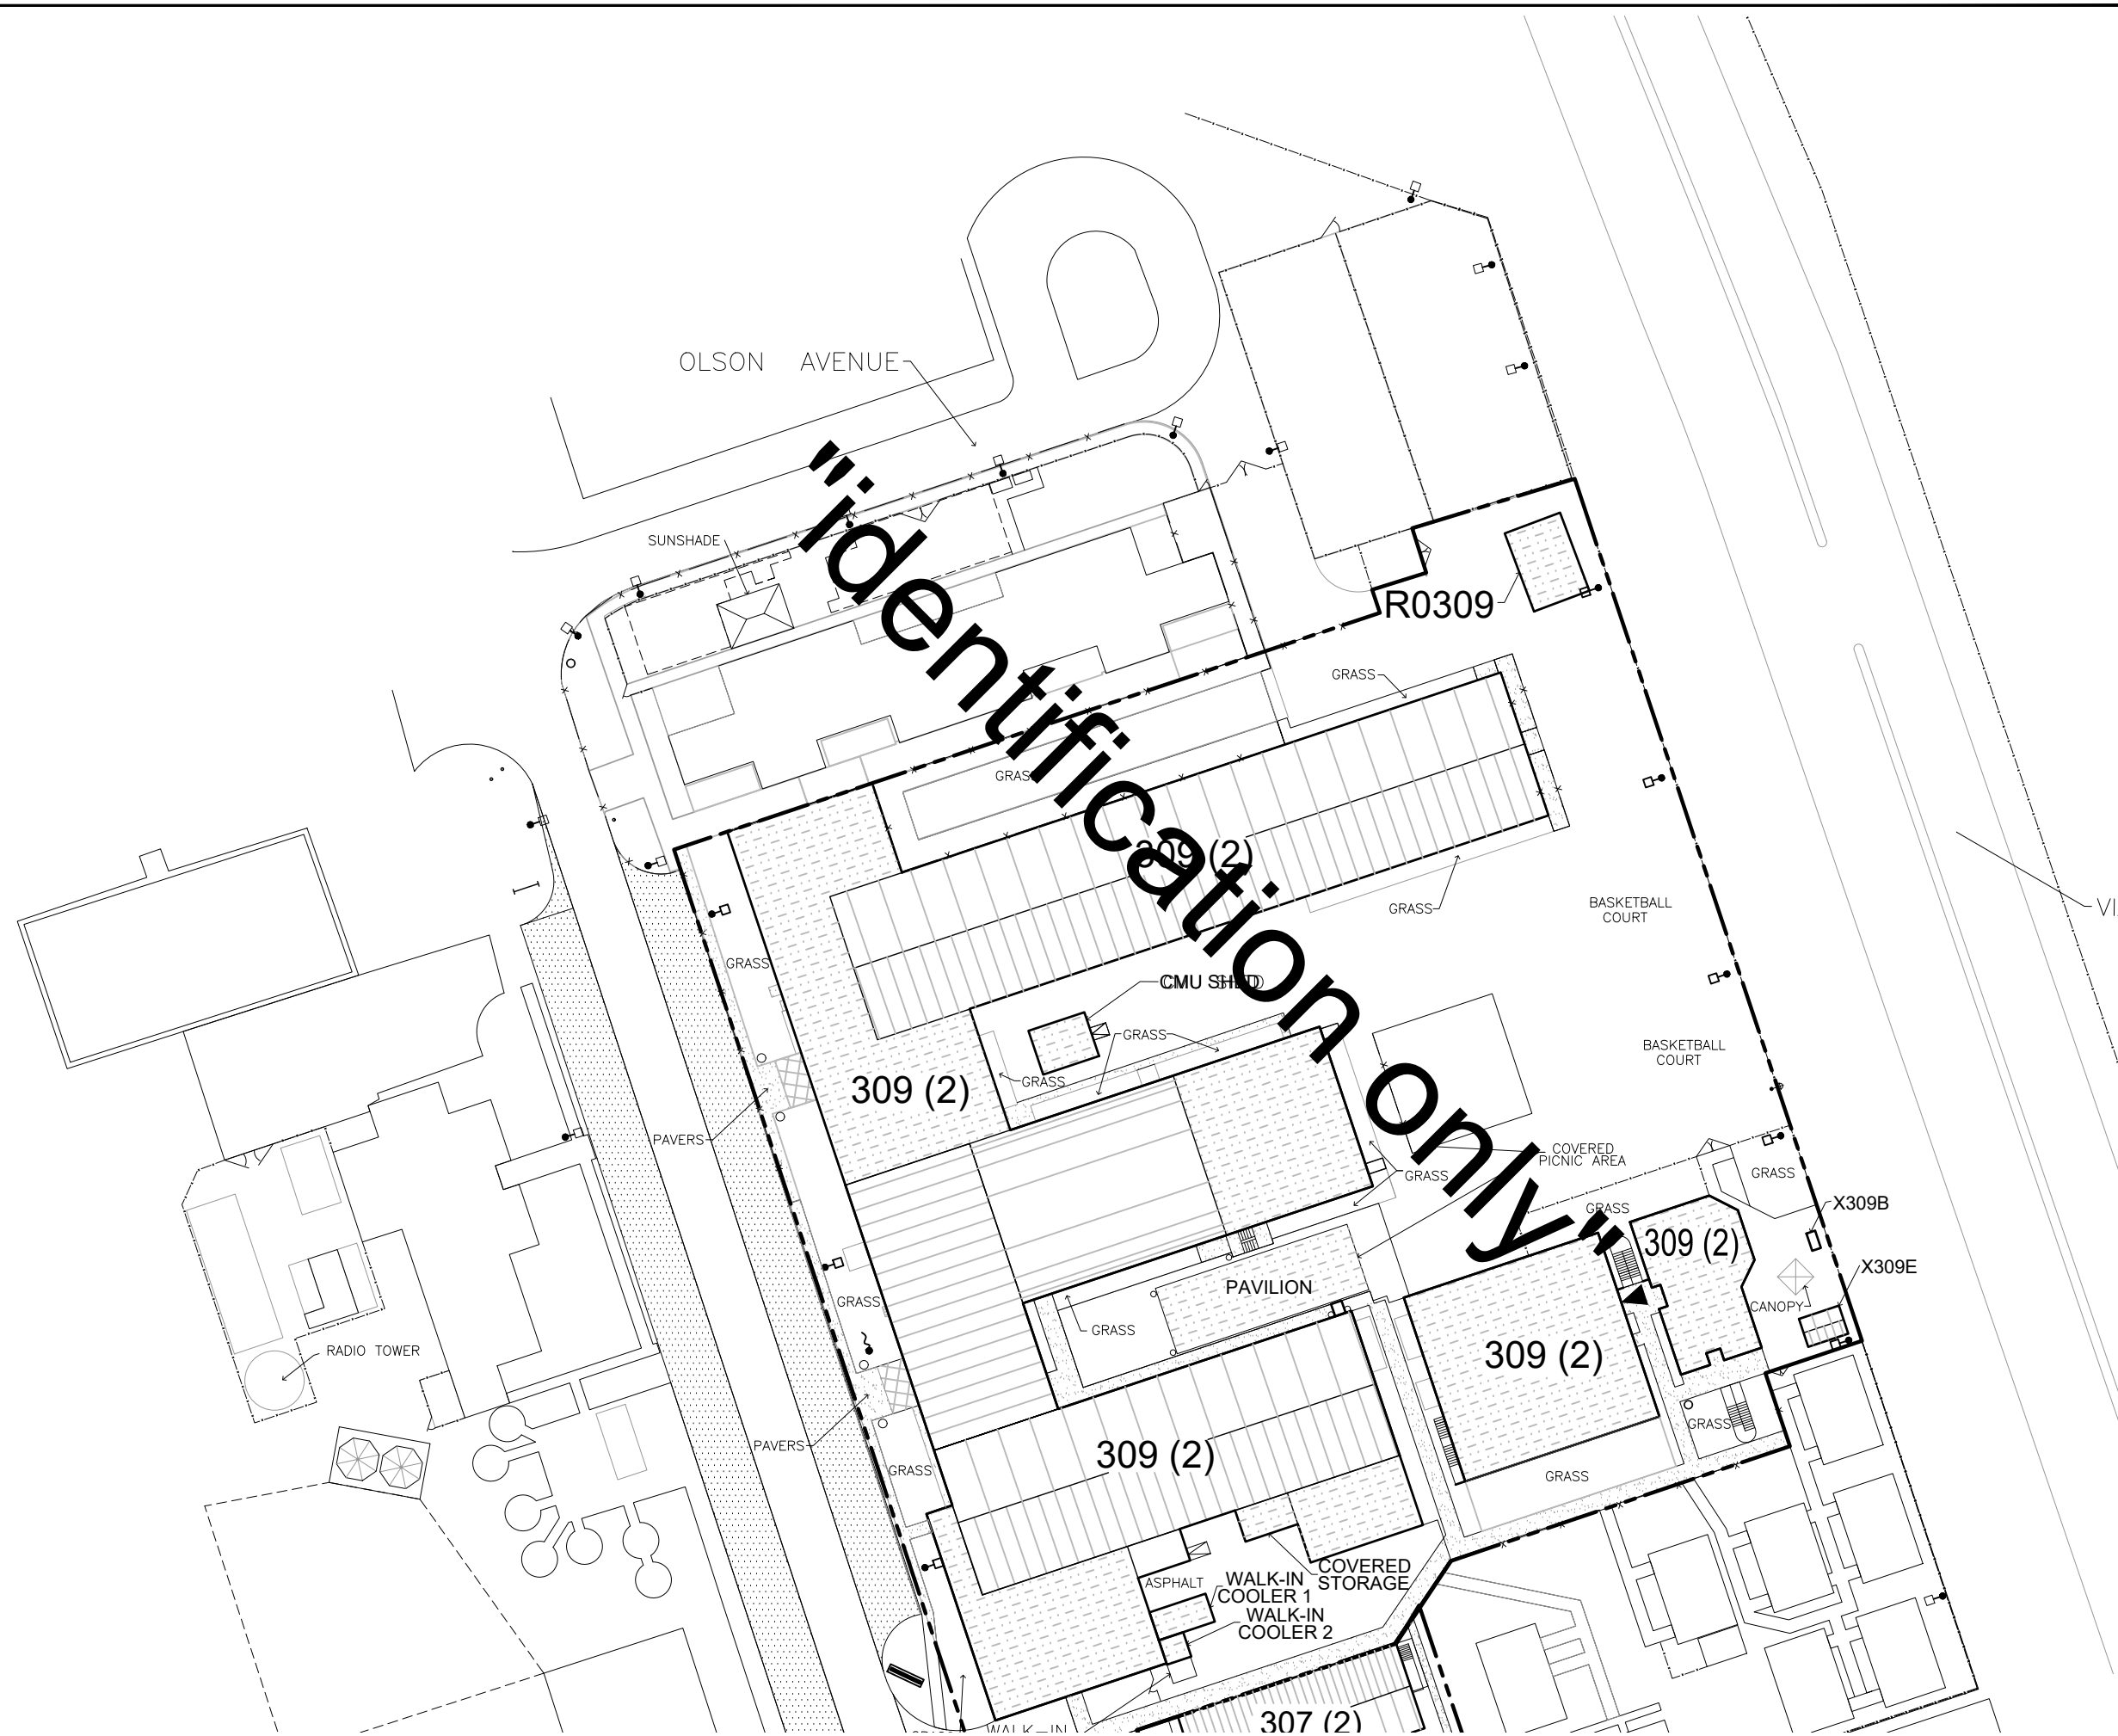[illegible]

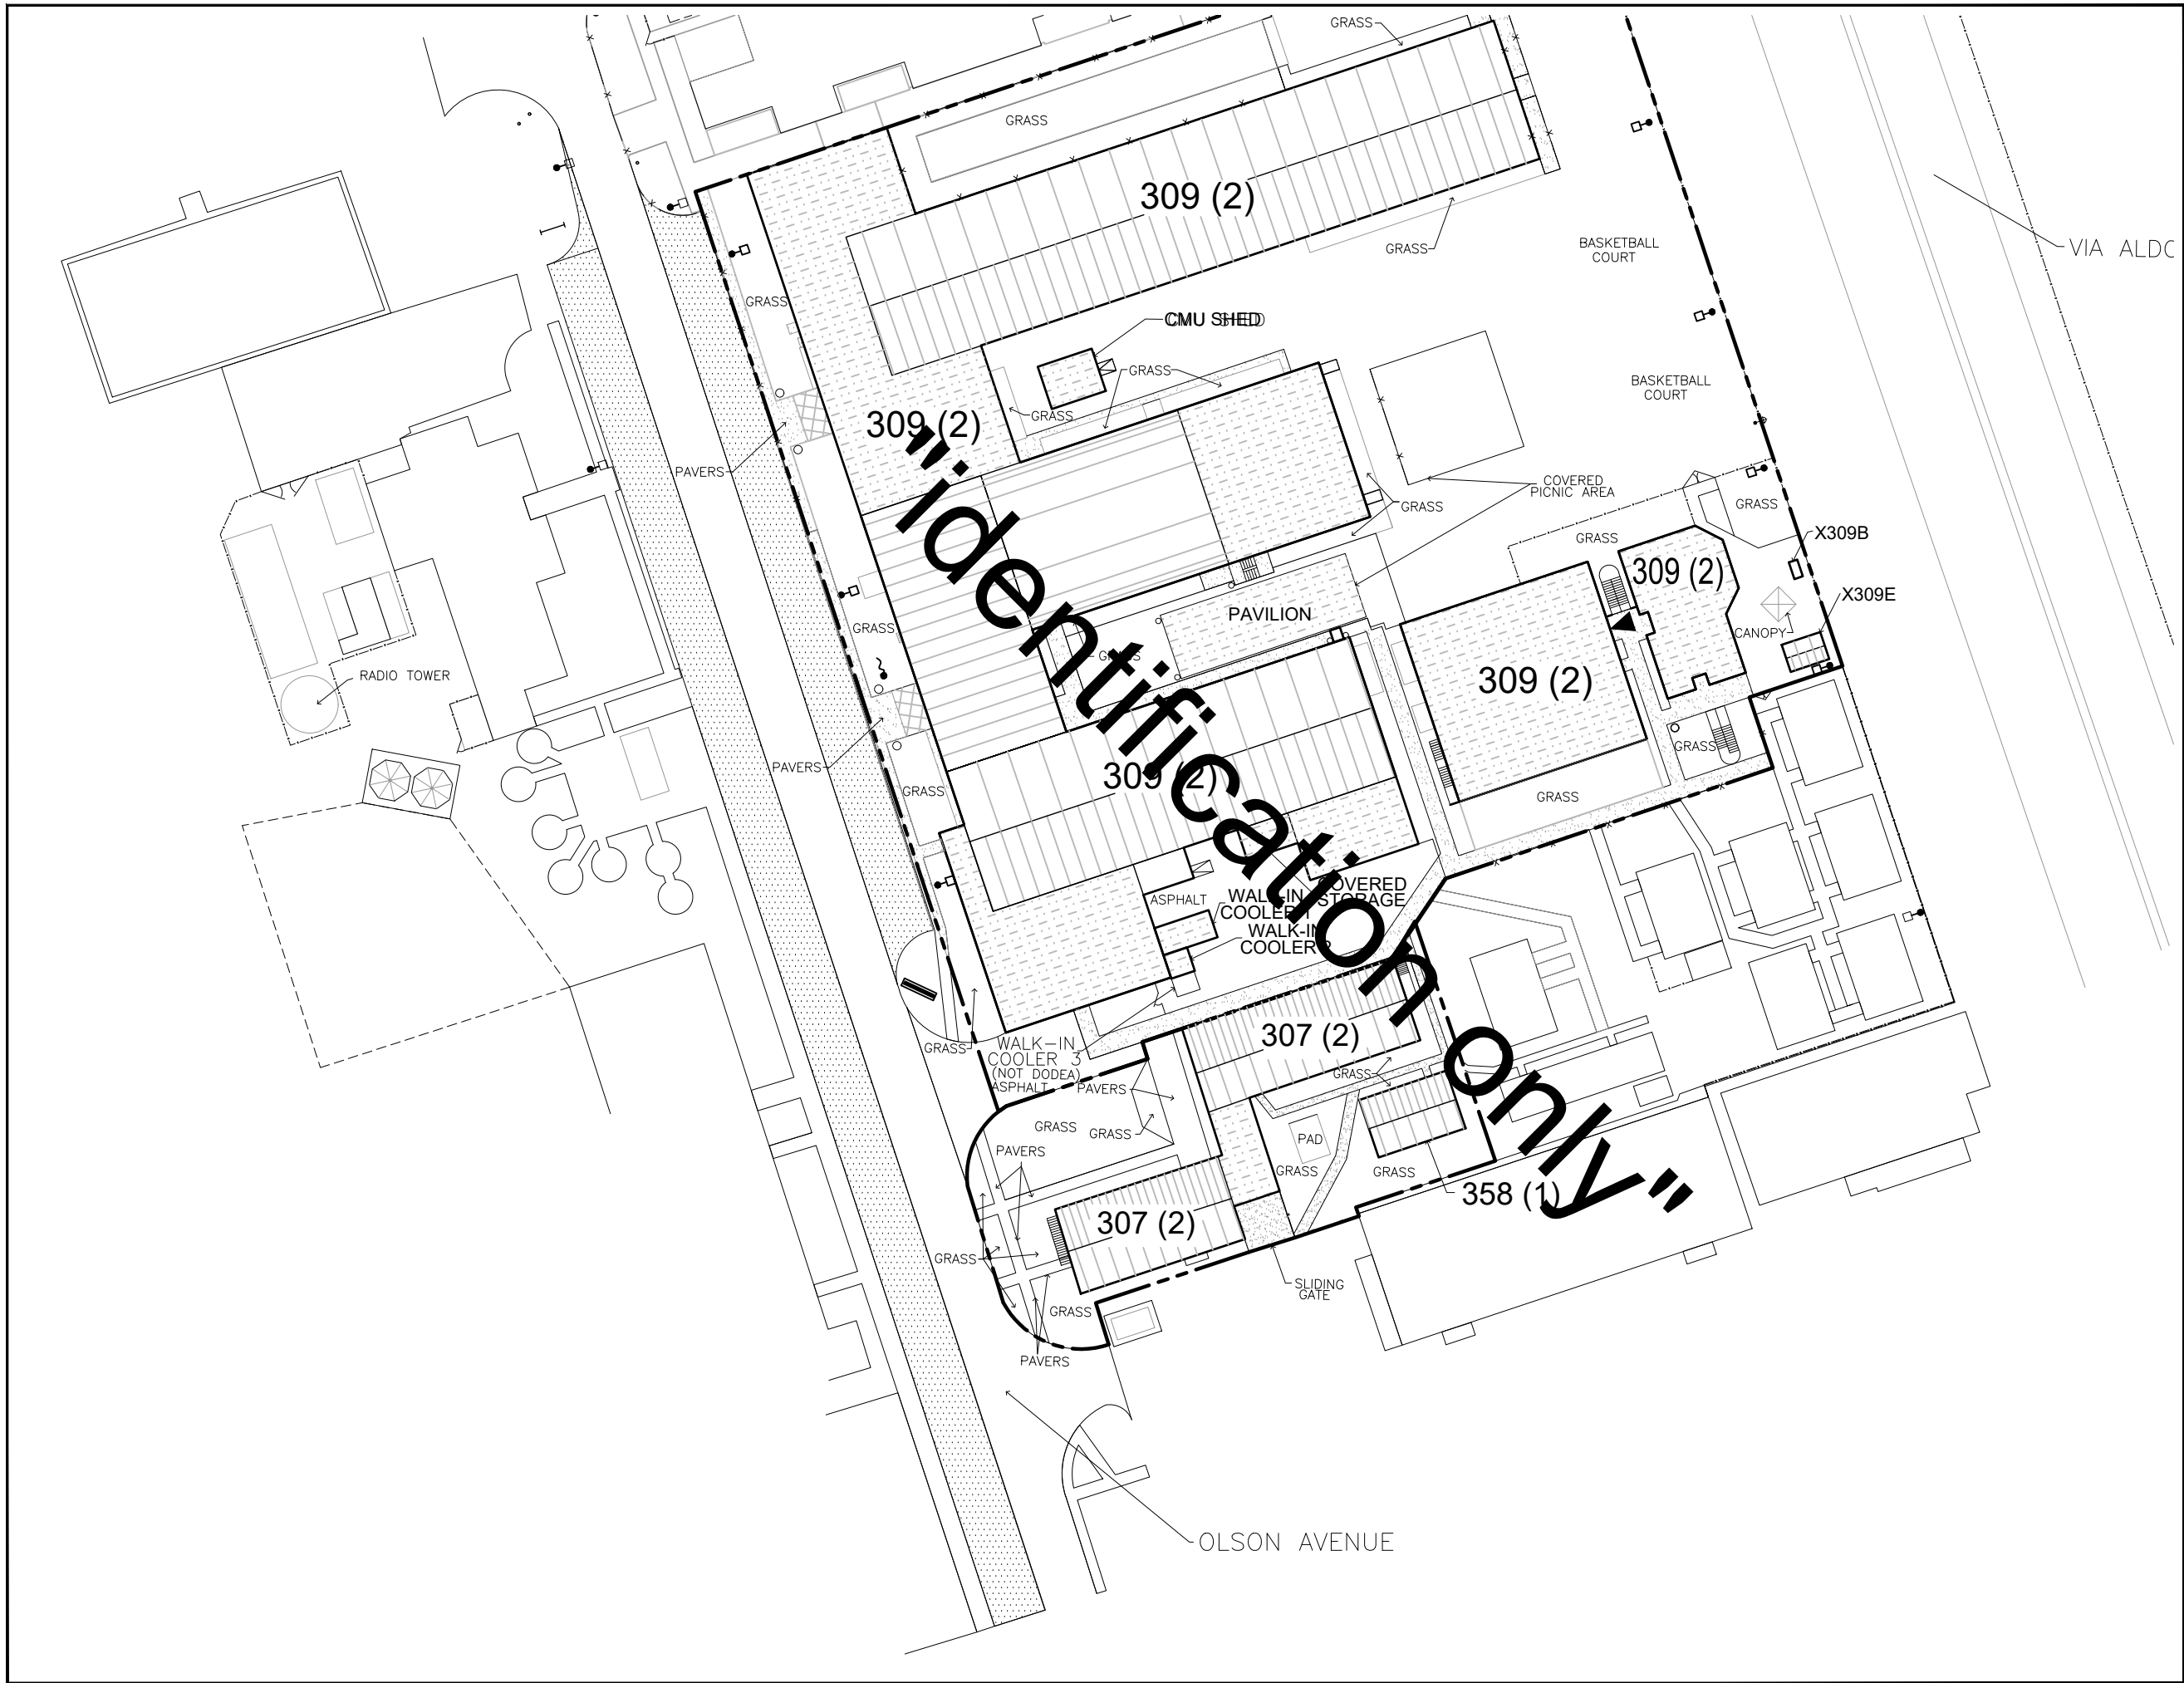

BASKETBALL GOAL

STADIUM LIGHT

SIGN

FOOTBALL GOAL

BASEBALL BACKSTOP

PARKING AREA

FLAT ROOF

SLOPE

COVERED WALKWAY

SLOPING ROOF

AREA LIGHT

FLAG POLE

MONUMENT

SOCCER GOAL

MAIN ENTRY

CONCRETE

PLAYGROUND

FIRE HYDRANT

PROPERTY LINE

FENCE LINE

(APPROX. 14,919 SM)

(APPROX. 3.69 AC)

LEGEND

PLAYGROUND SURFACING

WC - WOOD CHIPS PR - POURED RUBBER M - MULCH

SRT - SHREDDED RUBBER TIRES S - SAND

PG - PEA GRAVEL RT - RUBBER TILES

BUILDING LABEL	BLDG # (# OF FLOORS)

KEY PLAN

NTS

NORTH

Updated By:

SPF

FUS Review:

MRS

100% Submittal Date:

01 MAY 2020

0

16

32

64 FT

dodea

DEPARTMENT OF DEFENSE EDUCATION ACTIVITY

FACILITY UTILIZATION SURVEY

VICENZA HIGH SCHOOL /

DoDEA EUROPE SOUTH DSO


COUNTRY: ITALY

INSTALLATION: US ARMY GARRISON ITALY

SITE: CAMP EDERLE

REGION-DISTRICT: DODEA EUROPE SOUTH

DoDAAC Number:	Survey Date:
HE5419, HE5468	JANUARY 2020
Sheet Name:	Sheet Seq:
SITE 32ND SC (2)	4 of 19

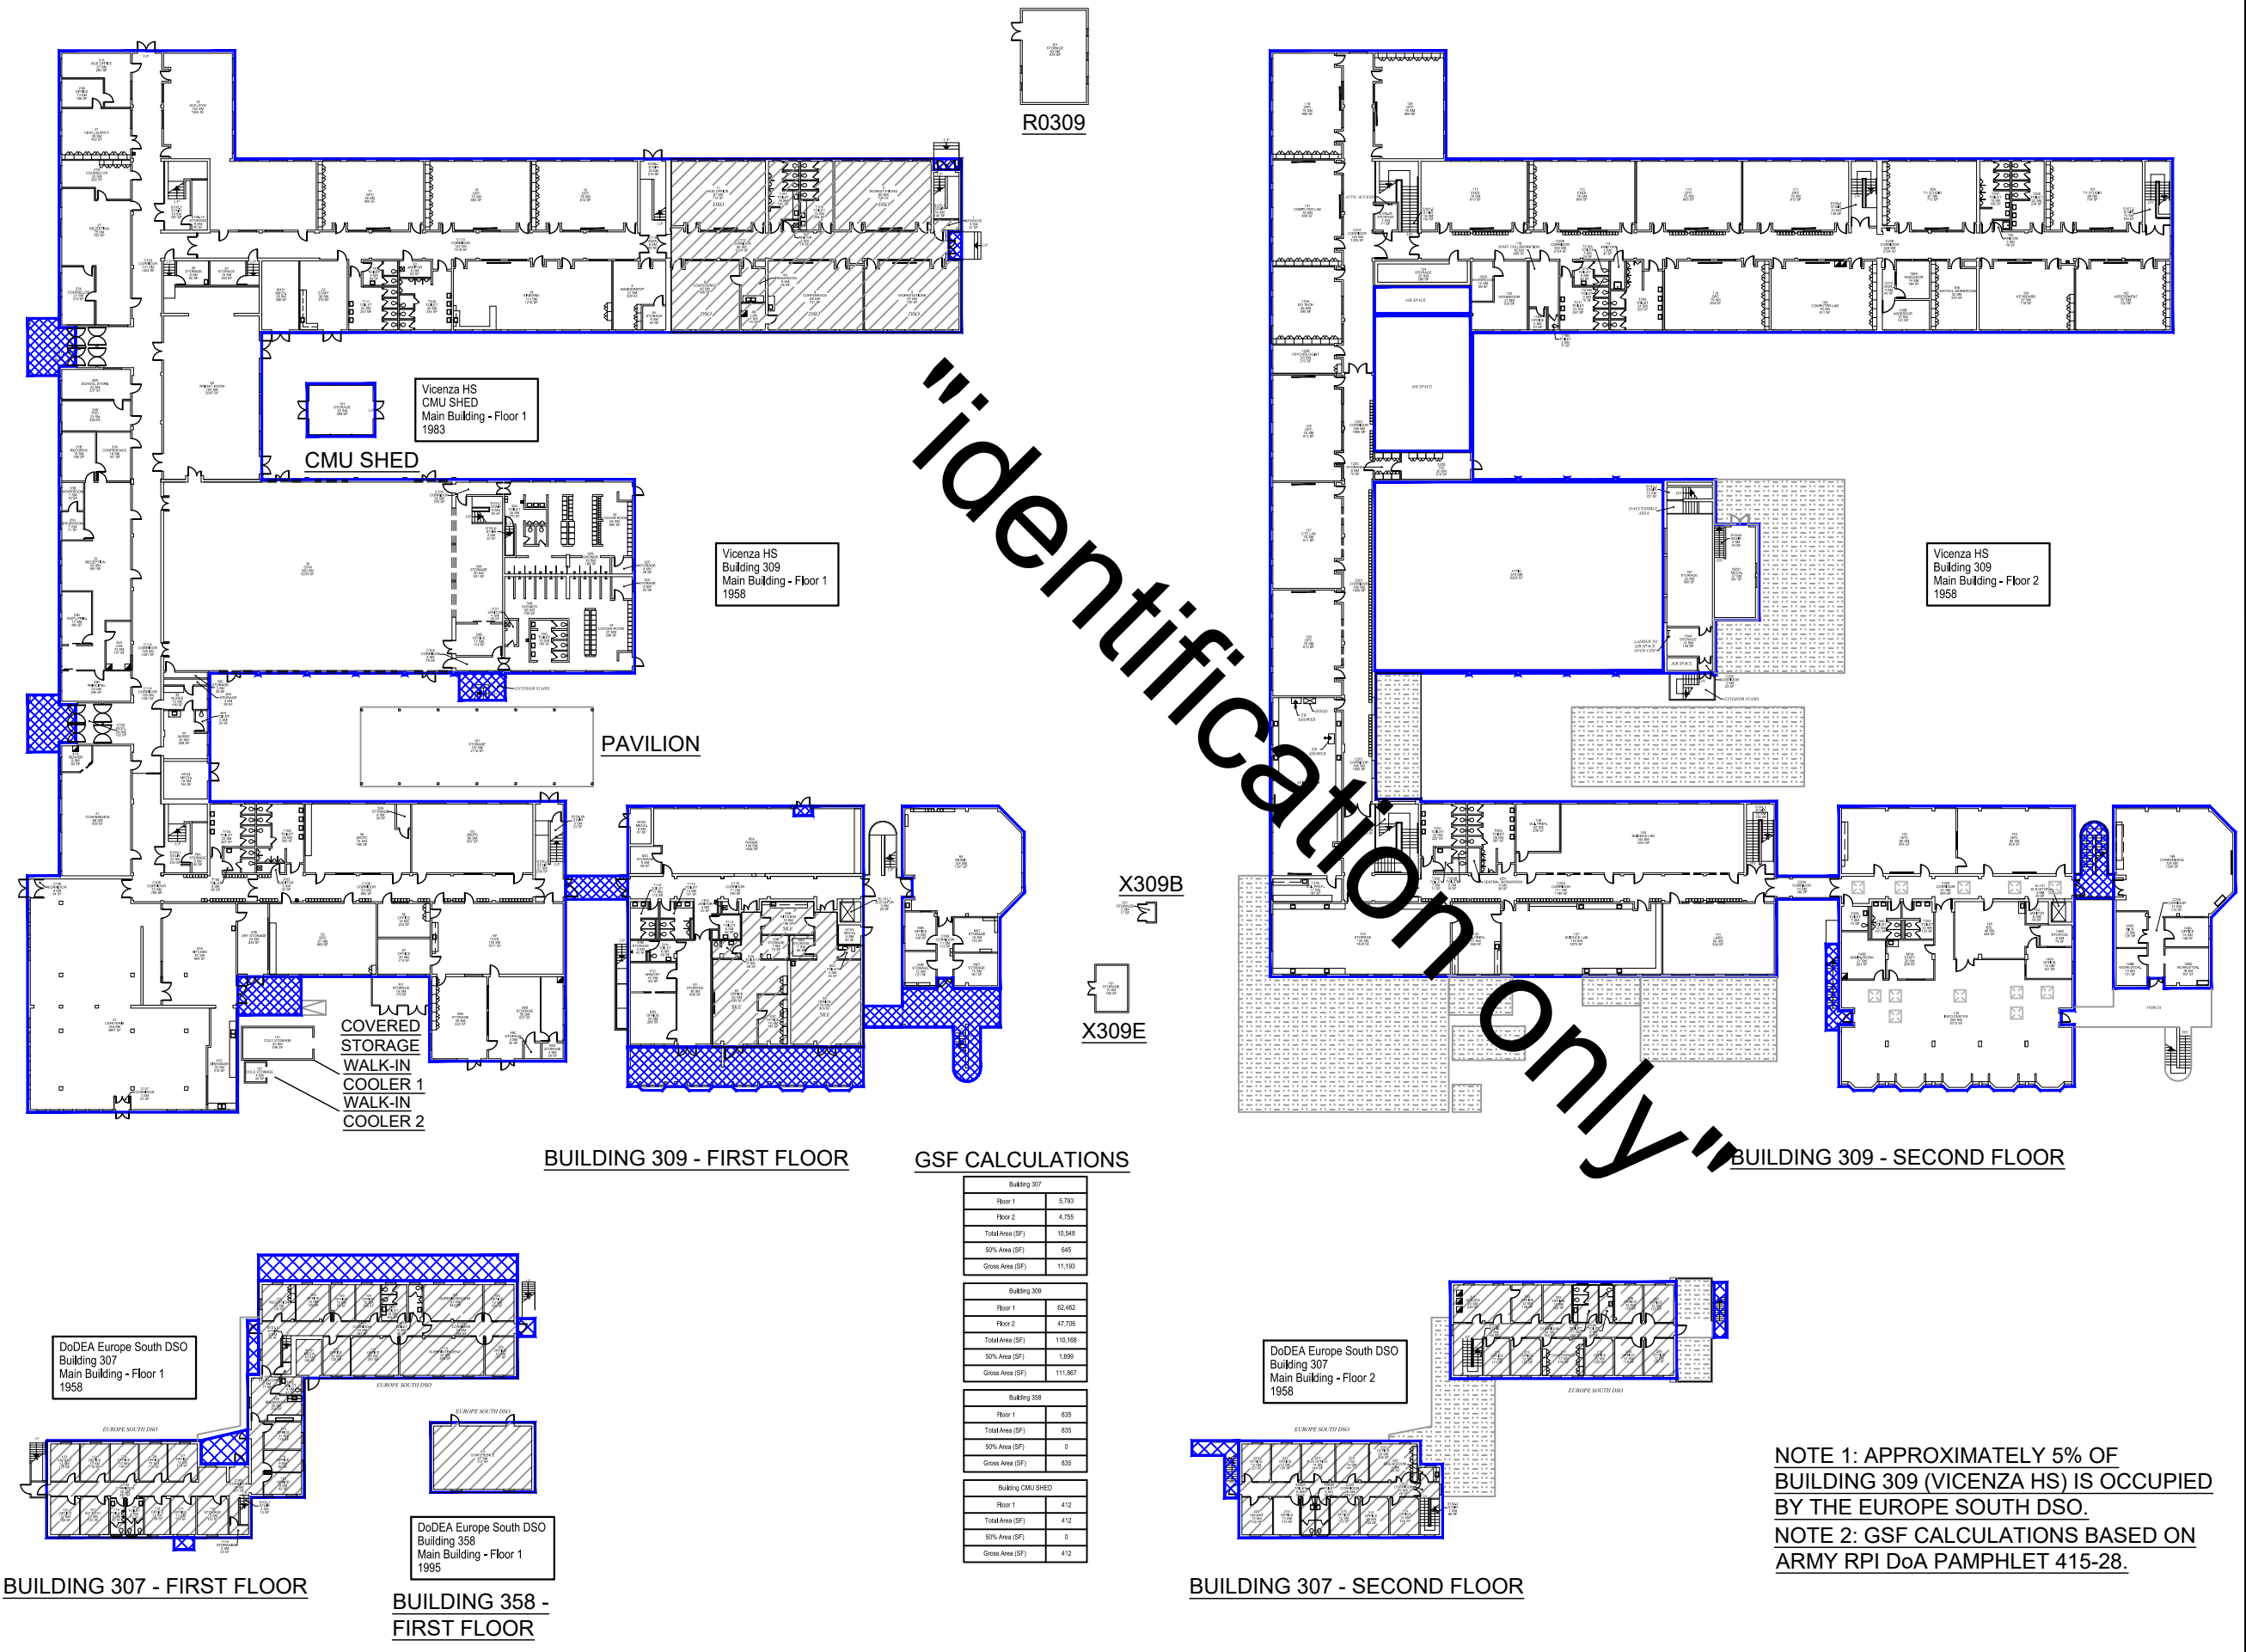

Identification only

GSF CALCULATIONS

Building 307	
Floor 1	5,793
Floor 2	4,755
Total Area (SF)	10,548
50% Area (SF)	5,274
Gross Area (SF)	11,193

Building 309	
Floor 1	52,482
Floor 2	47,796
Total Area (SF)	110,158
50% Area (SF)	5,508
Gross Area (SF)	111,867

Building 358	
Floor 1	835
Total Area (SF)	835
50% Area (SF)	0
Gross Area (SF)	835

Building CMU SHED	
Floor 1	412
Total Area (SF)	412
50% Area (SF)	0
Gross Area (SF)	412

NOTE 1: APPROXIMATELY 5% OF BUILDING 309 (VICENZA HS) IS OCCUPIED BY THE EUROPE SOUTH DSO.
NOTE 2: GSF CALCULATIONS BASED ON ARMY RPI DoA PAMPHLET 415-28.

SYMBOL LEGEND

DOOR	DRINKING FOUNTAIN
SLIDING DOOR	LAVATORY
ACCORDION PARTITION	SINK
STACK OR FOLDING PARTITION	TOILET
WINDOW/GLAZING	URINAL
HIGH WINDOW	LOCKER
SKYLIGHT	LAN DISTRIBUTION FRAME
STOOP/STEP UP	VENT HOOD
STAIR	WALL SHELVING
RAMP	UPPER CABINET
ACCESS LADDER	BASE CABINET
COLD STORAGE	TEACHER CABINET
AREA CALCULATED @ 50 %	MATCHLINE
SLOPING ROOF	FLAT ROOF

TITLEBLOCK LEGEND

SHEET NAME:	BLDG # FLOOR # (# IN SERIES)
--------------------	-------------------------------------

KEY PLAN

NTS


NOT TO SCALE

dodea
DEPARTMENT OF DEFENSE EDUCATION ACTIVITY
FACILITY UTILIZATION SURVEY

VICENZA HIGH SCHOOL / DoDEA EUROPE SOUTH DSO
BUILDING NUMBER: 309, R0309, X309B, X309F, CMU SHED, COVERED STORAGE, WALK-IN COOLER 1-2
COUNTRY: ITALY
INSTALLATION: US ARMY GARRISON ITALY
SITE: CAMP EDERLE
REGION-DISTRICT: DODEA EUROPE SOUTH

DoDAAC Number: HE5419, HE5468	Floor: LEVEL 1,2	Survey Date: JANUARY 2020
Sheet Name: GSF_1 (1)	Sheet Seq:	5 of 19

309						309						309						307					
Floor	Room	Current	Capacity	Area (SF)	Area (SM)	Floor	Room	Current	Capacity	Area (SF)	Area (SM)	Floor	Room	Current	Capacity	Area (SF)	Area (SM)	Floor	Room	Current	Capacity	Area (SF)	Area (SM)
1	1	STORAGE	OTHER	31 SF	3 SM	1	C111	VEST.	NET - GENERAL	96 SF	9 SM	2	M201	MECH.	NET - MECH	391 SF	37 SM	1	101	RECEPTION	OTHER	136 SF	13 SM
1	2	WORKSTATIONS	OTHER	720 SF	67 SM	1	C112	CORRIDOR	NET - GENERAL	1,024 SF	86 SM	2	S101.2	STAIR	NET - VERTICAL	127 SF	12 SM	1	102	OFFICE	OTHER	139 SF	13 SM
1	3	WORKSTATIONS	OTHER	734 SF	69 SM	1	C113	CORRIDOR	NET - GENERAL	1,518 SF	142 SM	2	S102.2	STAIR	NET - VERTICAL	34 SF	4 SM	1	103	OFFICE	OTHER	97 SF	10 SM
1	4	CONFERENCE	OTHER	731 SF	68 SM	1	C114	CORRIDOR	NET - GENERAL	1,461 SF	138 SM	2	S103.2	STAIR	NET - VERTICAL	200 SF	19 SM	1	104	OFFICE	OTHER	100 SF	10 SM
1	4A	BREAKROOM	OTHER	95 SF	9 SM	1	C115	VEST.	NET - GENERAL	89 SF	9 SM	2	S104.2	STAIR	NET - VERTICAL	125 SF	12 SM	1	107	SUPERINTENDENT	OTHER	243 SF	23 SM
1	4B	LAV	NET - MECH	75 SF	7 SM	1	C116	CORRIDOR	NET - GENERAL	769 SF	71 SM	2	S105.2	STAIR	NET - VERTICAL	190 SF	14 SM	1	108	OFFICE	OTHER	124 SF	12 SM
1	6	CONFERENCE	OTHER	528 SF	49 SM	1	EL101.1	ELEVATOR	NET - VERTICAL	29 SF	3 SM	2	S105.2A	STORAGE	OTHER	71 SF	7 SM	1	109	OFFICE	OTHER	127 SF	12 SM
1	8	ASSESSMENT	OTHER	329 SF	31 SM	1	J101	JANITOR	NET - GENERAL	35 SF	4 SM	2	S106.2	STAIR	NET - VERTICAL	139 SF	13 SM	1	110	SUPERINTENDENT	OTHER	370 SF	35 SM
1	8A	STORAGE	OTHER	64 SF	6 SM	1	J102	JANITOR	NET - GENERAL	32 SF	3 SM	2	S107.2	STAIR	NET - VERTICAL	155 SF	15 SM	1	111	OFFICE	OTHER	207 SF	20 SM
1	9	JANITOR	NET - GENERAL	19 SF	2 SM	1	J103	JANITOR	NET - GENERAL	25 SF	3 SM	2	T201	TOILET	NET - GENERAL	227 SF	22 SM	1	111A	STORAGE	OTHER	20 SF	2 SM
1	11	BUS OFFICE	OTHER	712 SF	67 SM	1	M101	MECH.	NET - MECH	298 SF	28 SM	2	T202	TOILET	NET - GENERAL	71 SF	7 SM	1	112	OFFICE	OTHER	120 SF	12 SM
1	12	GPC	STUDENT - FULL	812 SF	76 SM	1	M102	MECH.	NET - MECH	87 SF	9 SM	2	T202B	TOILET	NET - GENERAL	15 SF	2 SM	1	113	OFFICE	OTHER	116 SF	11 SM
1	15	GPC	STUDENT - FULL	805 SF	75 SM	1	M103	MECH.	NET - MECH	52 SF	5 SM	2	T203	TOILET	NET - GENERAL	297 SF	28 SM	1	114	OFFICE	OTHER	92 SF	9 SM
1	17	GPC	STUDENT - FULL	809 SF	76 SM	1	M104	MECH.	NET - MECH	194 SF	19 SM	2	T204	TOILET	NET - GENERAL	123 SF	12 SM	1	115	OFFICE	OTHER	92 SF	9 SM
1	18	BLU(NM)	STUDENT - FULL	1,216 SF	113 SM	1	S101.1	STAIR	NET - VERTICAL	93 SF	9 SM	2	T205	TOILET	NET - GENERAL	121 SF	12 SM	1	116	STORAGE	OTHER	132 SF	13 SM
1	19	AUX. GYM	STUDENT - FULL	1,695 SF	154 SM	1	S102.1	STAIR	NET - VERTICAL	33 SF	4 SM	2	T206	TOILET	NET - GENERAL	74 SF	7 SM	1	117	OFFICE	OTHER	108 SF	11 SM
1	20	JANITOR	NET - GENERAL	69 SF	6 SM	1	S103.1	STAIR	NET - VERTICAL	234 SF	22 SM	2	T207	TOILET	NET - GENERAL	198 SF	19 SM	1	118	OFFICE	OTHER	109 SF	11 SM
1	21	CENT. SUPPLY	OTHER	402 SF	38 SM	1	S104.1	STAIR	NET - VERTICAL	299 SF	27 SM	2	T208	TOILET	NET - GENERAL	234 SF	23 SM	1	119	TOILET	NET - GENERAL	90 SF	8 SM
1	21A	BUS OFFICE	OTHER	283 SF	27 SM	1	S104.1A	STAIR	NET - VERTICAL	23 SF	3 SM	2	T209	TOILET	NET - GENERAL	323 SF	31 SM	1	120	TOILET	NET - GENERAL	73 SF	7 SM
1	21B	OFFICE	OTHER	136 SF	13 SM	1	S105.1	STAIR	NET - VERTICAL	197 SF	19 SM	2	T210	TOILET	NET - GENERAL	55 SF	6 SM	1	121	ED TECH	OTHER	122 SF	12 SM
1	22	STAFF	OTHER	379 SF	36 SM	1	S105.1A	STORAGE	OTHER	90 SF	9 SM	2	T210A	TOILET	NET - GENERAL	24 SF	3 SM	1	122	OFFICE	OTHER	125 SF	12 SM
1	24	STORAGE	STUDENT - HALF	100 SF	10 SM	1	S106.1	STAIR	NET - VERTICAL	215 SF	20 SM	2	T210B	TOILET	NET - GENERAL	15 SF	2 SM	1	123	VACANT	OTHER	123 SF	12 SM
1	25A	BREAKROOM	OTHER	71 SF	7 SM	1	S107.1	STAIR	NET - VERTICAL	140 SF	14 SM	2	T211	TOILET	NET - GENERAL	247 SF	23 SM	1	124	OFFICE	OTHER	119 SF	12 SM
1	26	STORAGE	OTHER	90 SF	9 SM	1	T104	TOILET	NET - GENERAL	227 SF	22 SM	CMU SHED						1	125	OFFICE	OTHER	119 SF	12 SM
1	27	RECEPTION	OTHER	797 SF	75 SM	1	T105	TOILET	NET - GENERAL	98 SF	9 SM	Floor	Room	Current	Capacity	Area (SF)	Area (SM)	1	126	OFFICE	OTHER	118 SF	11 SM
1	27A	COUNSELOR	OTHER	219 SF	21 SM	1	T106	TOILET	NET - GENERAL	302 SF	29 SM	1	101	STORAGE	OTHER	369 SF	35 SM	1	127	OFFICE	OTHER	126 SF	12 SM
1	27B	COUNSELOR	OTHER	262 SF	25 SM	1	T107	TOILET	NET - GENERAL	197 SF	19 SM	1	128	BREAKROOM	OTHER			1	128	BREAKROOM	OTHER	206 SF	20 SM
1	28	WEIGHT ROOM	STUDENT - FULL	2,087 SF	194 SM	1	T108	TOILET	NET - GENERAL	234 SF	22 SM	1	129	STORAGE	OTHER			1	129	STORAGE	OTHER	11 SF	2 SM
1	28A	SCHOOL STORE	OTHER	237 SF	23 SM	1	T109	TOILET	NET - GENERAL	314 SF	30 SM	1	C101	CORRIDOR	NET - GENERAL			1	C101	CORRIDOR	NET - GENERAL	347 SF	33 SM
1	28B	PTO	OTHER	239 SF	23 SM	1	T110	TOILET	NET - GENERAL	94 SF	9 SM	1	C102	CORRIDOR	NET - GENERAL			1	C102	CORRIDOR	NET - GENERAL	340 SF	32 SM
1	30	GYM	STUDENT - FULL	6,225 SF	580 SM	1	T111	TOILET	NET - GENERAL	247 SF	23 SM	1	C103	CORRIDOR	NET - GENERAL			1	C103	CORRIDOR	NET - GENERAL	201 SF	19 SM
1	30A	STORAGE	OTHER	531 SF	50 SM	1	T113	TOILET	NET - GENERAL	58 SF	6 SM	1	C104	CORRIDOR	NET - GENERAL			1	C104	CORRIDOR	NET - GENERAL	148 SF	14 SM
1	30B	OFFICE	OTHER	174 SF	17 SM	1	T115	TOILET	NET - GENERAL	131 SF	13 SM	1	M101	MECH.	NET - MECH			1	M101	MECH.	NET - MECH	105 SF	10 SM
1	30C	STORAGE	OTHER	25 SF	3 SM	1	T116	TOILET	NET - GENERAL	110 SF	11 SM	1	S101.1	STAIR	NET - VERTICAL			1	S101.1	STAIR	NET - VERTICAL	13 SF	2 SM
1	31A	CONFERENCE	OTHER	181 SF	18 SM	2	101	TV STUDIO	OTHER	734 SF	69 SM	1	S102.1	STAIR	NET - VERTICAL			1	S102.1	STAIR	NET - VERTICAL	13 SF	2 SM
1	31B	RECORDS	OTHER	189 SF	18 SM	2	102	ASSESSMENT	OTHER	725 SF	67 SM	1	T101	TOILET	NET - GENERAL			1	T101	TOILET	NET - GENERAL	104 SF	10 SM
1	32	LOCKER ROOM	OTHER	682 SF	64 SM	2	104	KEYBOARD	STUDENT - FULL	718 SF	67 SM	1	T101A	TOILET	NET - GENERAL			1	T101A	TOILET	NET - GENERAL	56 SF	6 SM
1	32A	TOILET	OTHER	370 SF	35 SM	2	105	JANITOR	NET - GENERAL	19 SF	2 SM	1	T102	TOILET	NET - GENERAL			1	T102	TOILET	NET - GENERAL	41 SF	4 SM
1	32B	SHOWER	OTHER	198 SF	19 SM	2	106	CENTRAL WORKROOM	OTHER	334 SF	32 SM	2	201	SERVER	NET - MECH			2	201	SERVER	NET - MECH	246 SF	23 SM
1	32C	STORAGE	STUDENT - HALF	39 SF	4 SM	2	106A	ASSESSOR	OTHER	144 SF	14 SM	2	202	OFFICE	OTHER			2	202	OFFICE	OTHER	128 SF	12 SM
1	33	RECEPTION	OTHER	991 SF	93 SM	2	108B	ASSESSOR	OTHER	161 SF	15 SM	2	203	OFFICE	OTHER			2	203	OFFICE	OTHER	122 SF	12 SM
1	33A	LAV	NET - MECH	137 SF	13 SM	2	108	COMPUTER LAB	STUDENT - FULL	811 SF	76 SM	2	206	OFFICE	OTHER			2	206	OFFICE	OTHER	120 SF	12 SM
1	33B	PRINCIPAL	OTHER	240 SF	23 SM	2	109	TV STUDIO	OTHER	712 SF	67 SM	2	207	OFFICE	OTHER			2	207	OFFICE	OTHER	127 SF	12 SM
1	33D	ASST. PRIN.	OTHER	180 SF	17 SM	2	110	GPC	STUDENT - FULL	804 SF	75 SM	2	208	OFFICE	OTHER			2	208	OFFICE	OTHER	128 SF	12 SM
1	34	LOCKER ROOM	OTHER	288 SF	27 SM	2	111	GPC	STUDENT - FULL	812 SF	76 SM	2	209	OFFICE	OTHER			2	209	OFFICE	OTHER	118 SF	11 SM
1	35A	TOILET	OTHER	180 SF	15 SM	2	113	GPC	STUDENT - FULL	805 SF	75 SM	2	210	OFFICE	OTHER			2	210	OFFICE	OTHER	120 SF	12 SM
1	35B	SHOWER	OTHER	739 SF	69 SM	2	114	JANITOR	NET - GENERAL	47 SF	5 SM	2	211	CONFERENCE	OTHER			2	211	CONFERENCE	OTHER	178 SF	17 SM
1	34C	STORAGE	STUDENT - HALF	52 SF	5 SM	2	115	FLES	STUDENT - FULL	809 SF	76 SM	2	212	OFFICE	OTHER			2	212	OFFICE	OTHER	126 SF	12 SM
1	35B	WORKROOM	OTHER	79 SF	7 SM	2	117	FLES	STUDENT - FULL	813 SF	76 SM	2	213	OFFICE	OTHER			2	213	OFFICE	OTHER	111 SF	11 SM
1	38	NURSE	OTHER	119 SF	12 SM	2	118	STAFF COLLABORATION	OTHER	165 SF	16 SM	2	214	OFFICE	OTHER			2	214	OFFICE	OTHER	124 SF	12 SM
1	38A	STORAGE	OTHER	29 SF	3 SM	2	118A	OFFICE	OTHER	43 SF	4 SM	2	215	OFFICE	OTHER			2	215	OFFICE	OTHER	123 SF	12 SM
1	41	CONFERENCE	OTHER	839 SF	88 SM	2	118B	TOILET	NET - GENERAL	17 SF	2 SM	2	216	OFFICE	OTHER			2	216	OFFICE	OTHER	123 SF	12 SM
1	41A	SERVER	NET - MECH	82 SF	8 SM	2	119	GPC	STUDENT - FULL	808 SF	76 SM	2	218	OFFICE	OTHER			2	218	OFFICE	OTHER	113 SF	11 SM
1	44	NURSE	OTHER	209 SF	20 SM	2	121	COMPUTER LAB	STUDENT - FULL	809 SF	76 SM	2	219	OFFICE	OTHER			2	219	OFFICE	OTHER	132 SF	13 SM
1	44A	TOILET	OTHER	39 SF	3 SM	2	122	WORKROOM	OTHER	333 SF	31 SM	2	220	OFFICE	OTHER			2	220	OFFICE	OTHER	132 SF	13 SM
1	46A	STORAGE	OTHER	90 SF	9 SM	2	122A	WORKROOM	OTHER	95 SF	10 SM	2	221	OFFICE	OTHER			2	221	OFFICE	OTHER	144 SF	14 SM
1	47	CAFETERIA	OTHER	3,807 SF	354 SM	2	122B	TSC	OTHER	215 SF	20 SM	2	222	OFFICE	OTHER			2	222	OFFICE	OTHER	124 SF	12 SM
1	47A	KITCHEN	OTHER	864 SF	81 SM	2	122C	STORAGE	OTHER	78 SF	8 SM	2	223	OFFICE	OTHER			2	223	OFFICE	OTHER	123 SF	12 SM
1	47B	DRY STORAGE	OTHER	249 SF	24 SM	2	123A	ED TECH	OTHER	595 SF	56 SM	2	224	TSC	OTHER			2	224	TSC	OTHER	141 SF	14 SM
1	47C	DIRTY WASH	OTHER	316 SF	30 SM	2	123B	PSYCHOLOGIST	OTHER	212 SF	20 SM	2	225	OFFICE	OTHER			2	225	OFFICE	OTHER	208 SF	20 SM
1	53	GPC	STUDENT - FULL	165 SF	15 SM	2	124	STORAGE	OTHER	298 SF	25 SM	2	226	BREAKROOM	OTHER			2	226	BREAKROOM	OTHER	34 SF	4 SM
1	55	OFFICE	OTHER	284 SF	19 SM	2	125	GPC	STUDENT - FULL	813 SF	76 SM	2	C201	CORRIDOR	NET - GENERAL			2	C201	CORRIDOR	NET - GENERAL	350 SF	34 SM
1	56	JROTC	STUDENT - FULL	770 SF	74 SM	2	126	GPC	STUDENT - FULL	809 SF	76 SM	2	C202	CORRIDOR	NET - GENERAL			2	C202	CORRIDOR	NET - GENERAL	279 SF	26 SM
1	56A	STORAGE	OTHER	39 SF	4 SM	2	127	CTE LAB	STUDENT - FULL	811 SF	76 SM	2	C203	CORRIDOR	NET - GENERAL			2	C203	CORRIDOR	NET - GENERAL	42 SF	5 SM
1	57	OFFICE	OTHER	213 SF	20 SM	2	129	GPC	STUDENT - FULL	812 SF	76 SM	2	S101.2	STAIR	NET - VERTICAL			2	S101.2	STAIR	NET - VERTICAL	7 SF	1 SM
1	59	FLES	STUDENT - FULL	1,071 SF	100 SM	2	131	SCIENCE LAB	STUDENT - FULL	1,377 SF	128 SM	2	S102.2	TOILET	NET - GENERAL			2	S102.2	TOILET	NET - GENERAL	12 SF	2 SM
1	59A	STORAGE	OTHER	522 SF	49 SM	2	131A	SCL. PREP.	OTHER	181 SF	17 SM	2	T										

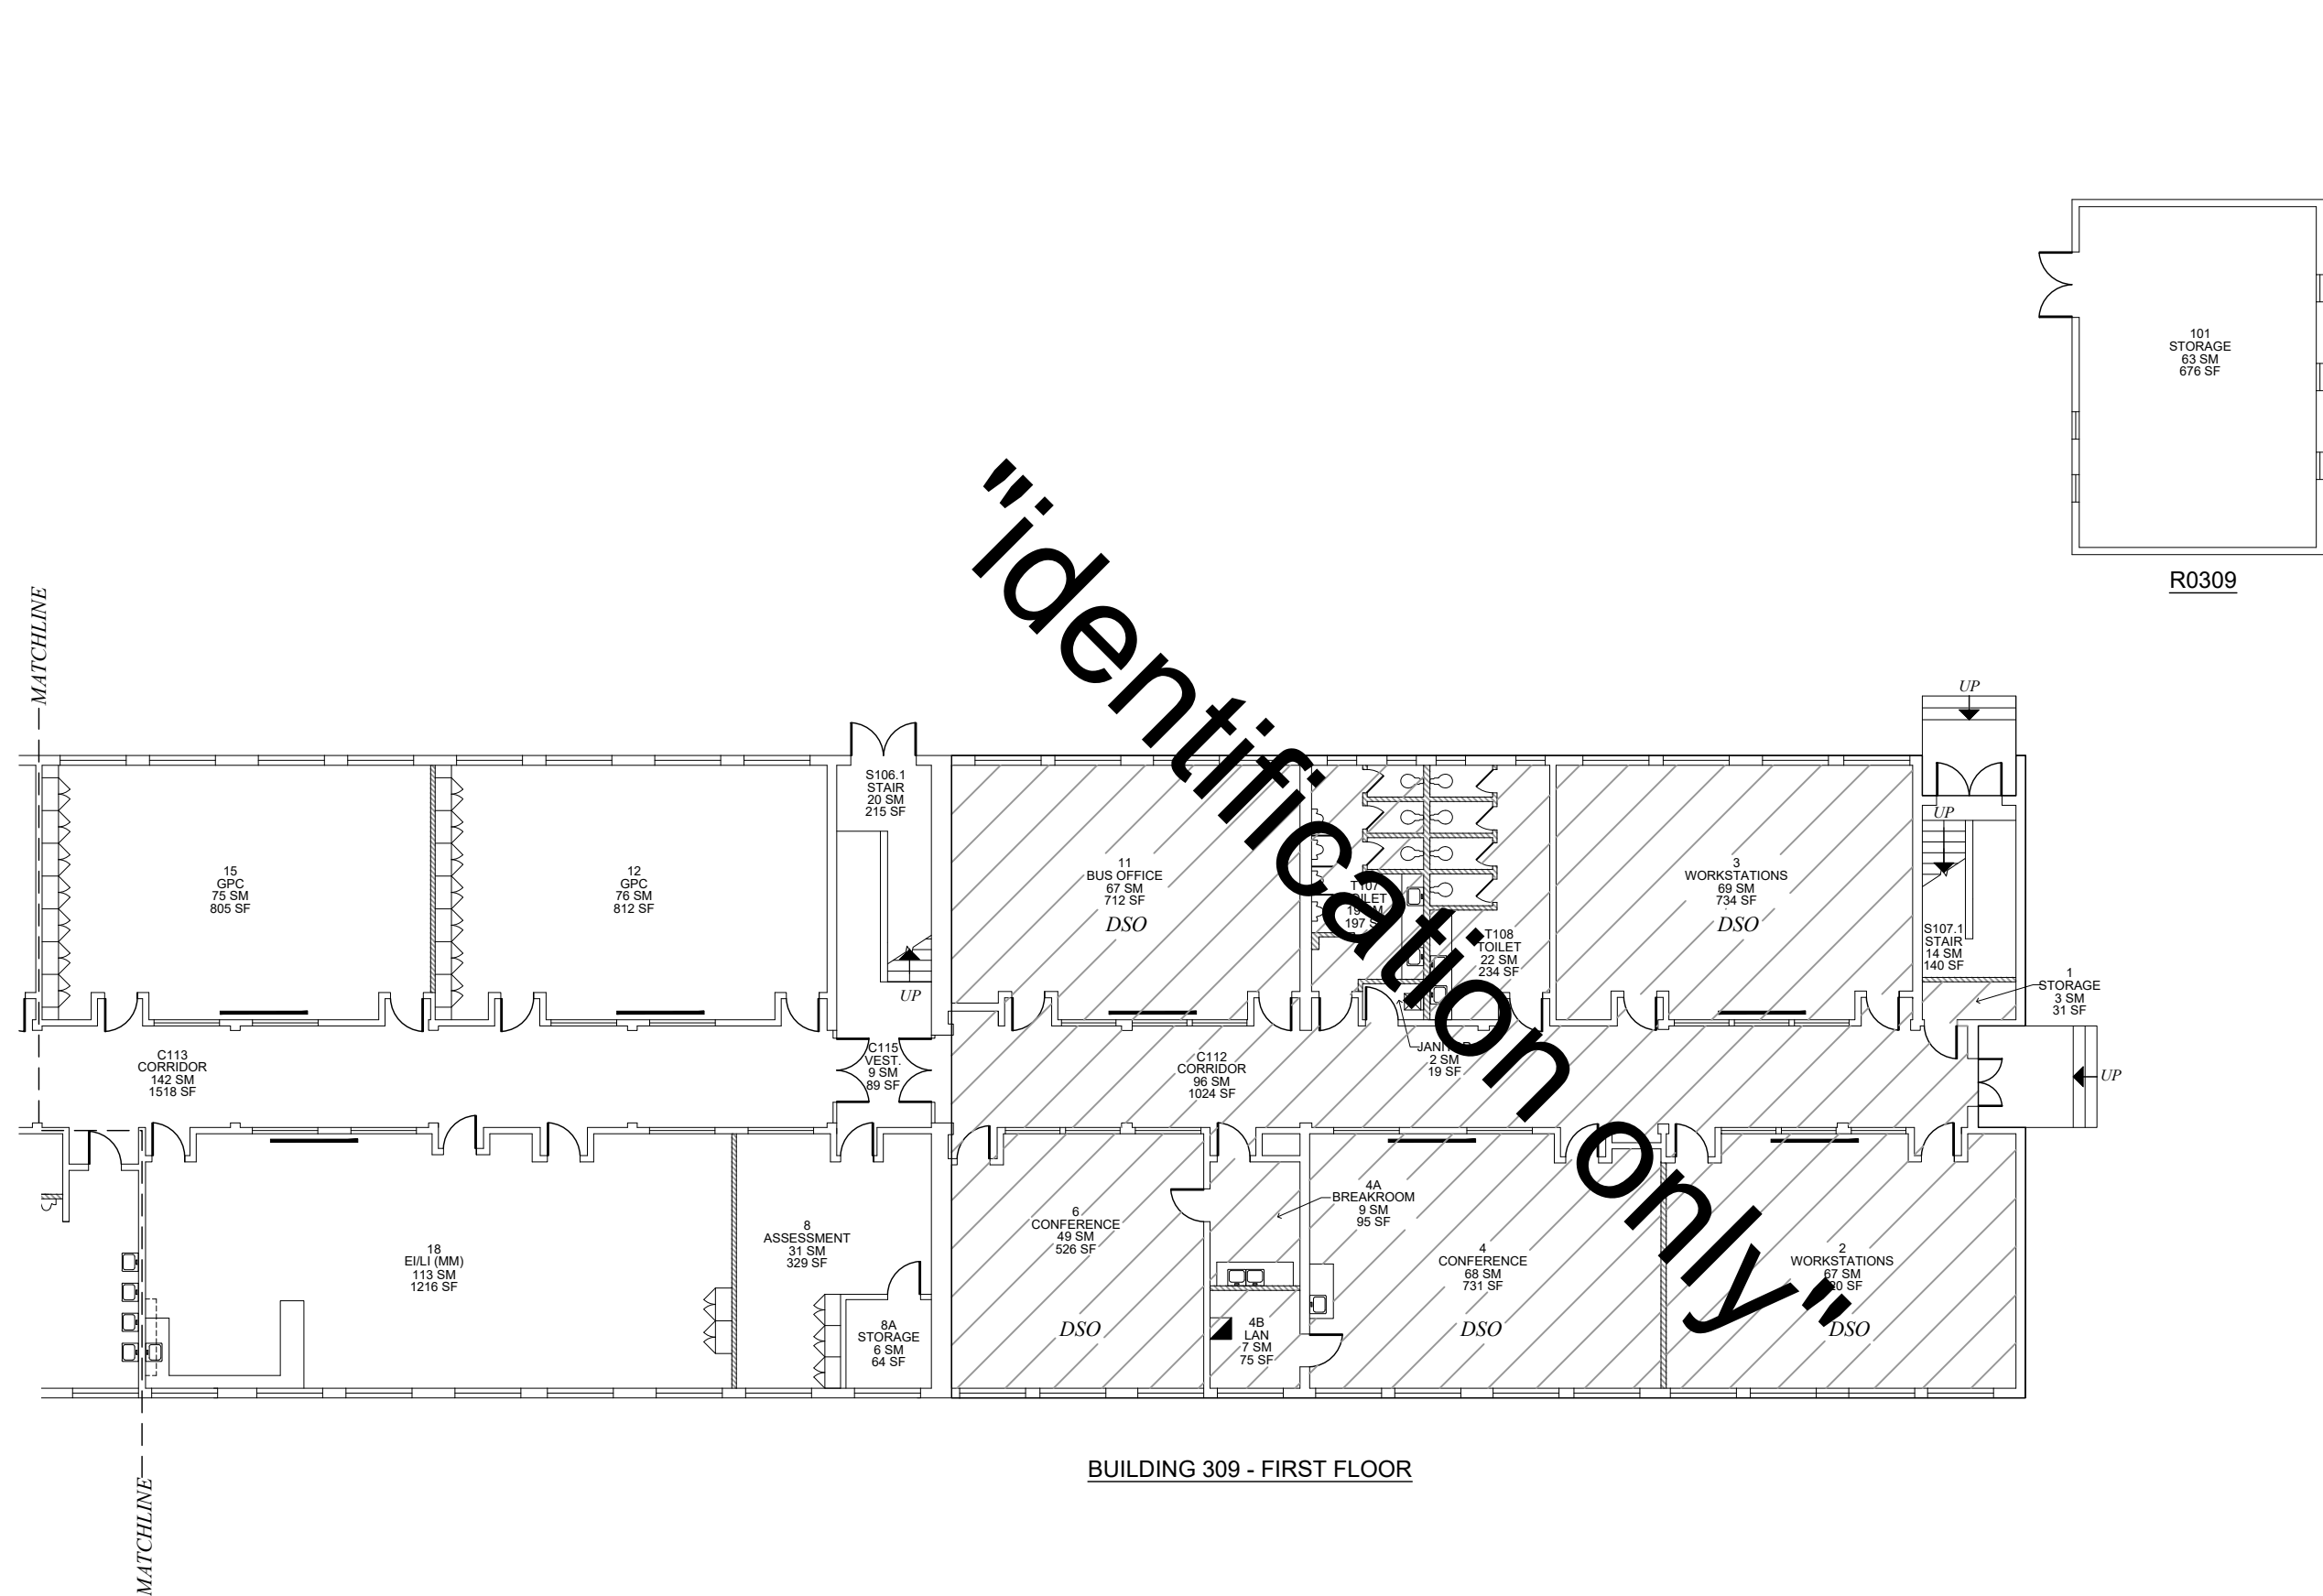

BUILDING 309 - FIRST FLOOR

SYMBOL LEGEND

DOOR	DRINKING FOUNTAIN
SLIDING DOOR	LAVATORY
ACCORDION PARTITION	SINK
STACK OR FOLDING PARTITION	TOILET
WINDOW/GLAZING	URINAL
HIGH WINDOW	LOCKER
SKYLIGHT	LAN DISTRIBUTION FRAME
STOOP/STEP UP	VENT HOOD
STAIR	WALL SHELVING
RAMP	UPPER CABINET
ACCESS LADDER	BASE CABINET
COLD STORAGE	TEACHER CABINET
AREA CALCULATED @ 50 %	MATCHLINE
SLOPING ROOF	FLAT ROOF

TITLEBLOCK LEGEND

SHEET NAME:	BLDG #_FLOOR # (# IN SERIES)
-------------	------------------------------

KEY PLAN

NTS

Updated By:

FUS Review:

100% Submittal Date:

SPF

MRS

01 MAY 2020

0

2

4

8

16

FT

dodea

DEPARTMENT OF DEFENSE EDUCATION ACTIVITY

FACILITY UTILIZATION SURVEY

VICENZA HIGH SCHOOL /

DoDEA EUROPE SOUTH DSO

BUILDING NUMBER: 309, R0309

COUNTRY: ITALY

INSTALLATION: US ARMY GARRISON ITALY

SITE: CAMP EDERLE

REGION-DISTRICT: DODEA EUROPE SOUTH

DoDAAC Number:

Floor:

Survey Date:

HE5419, HE5468

LEVEL 1


JANUARY 2020

Sheet Name:

Sheet Seq:


309_1 (1)

8 of 19

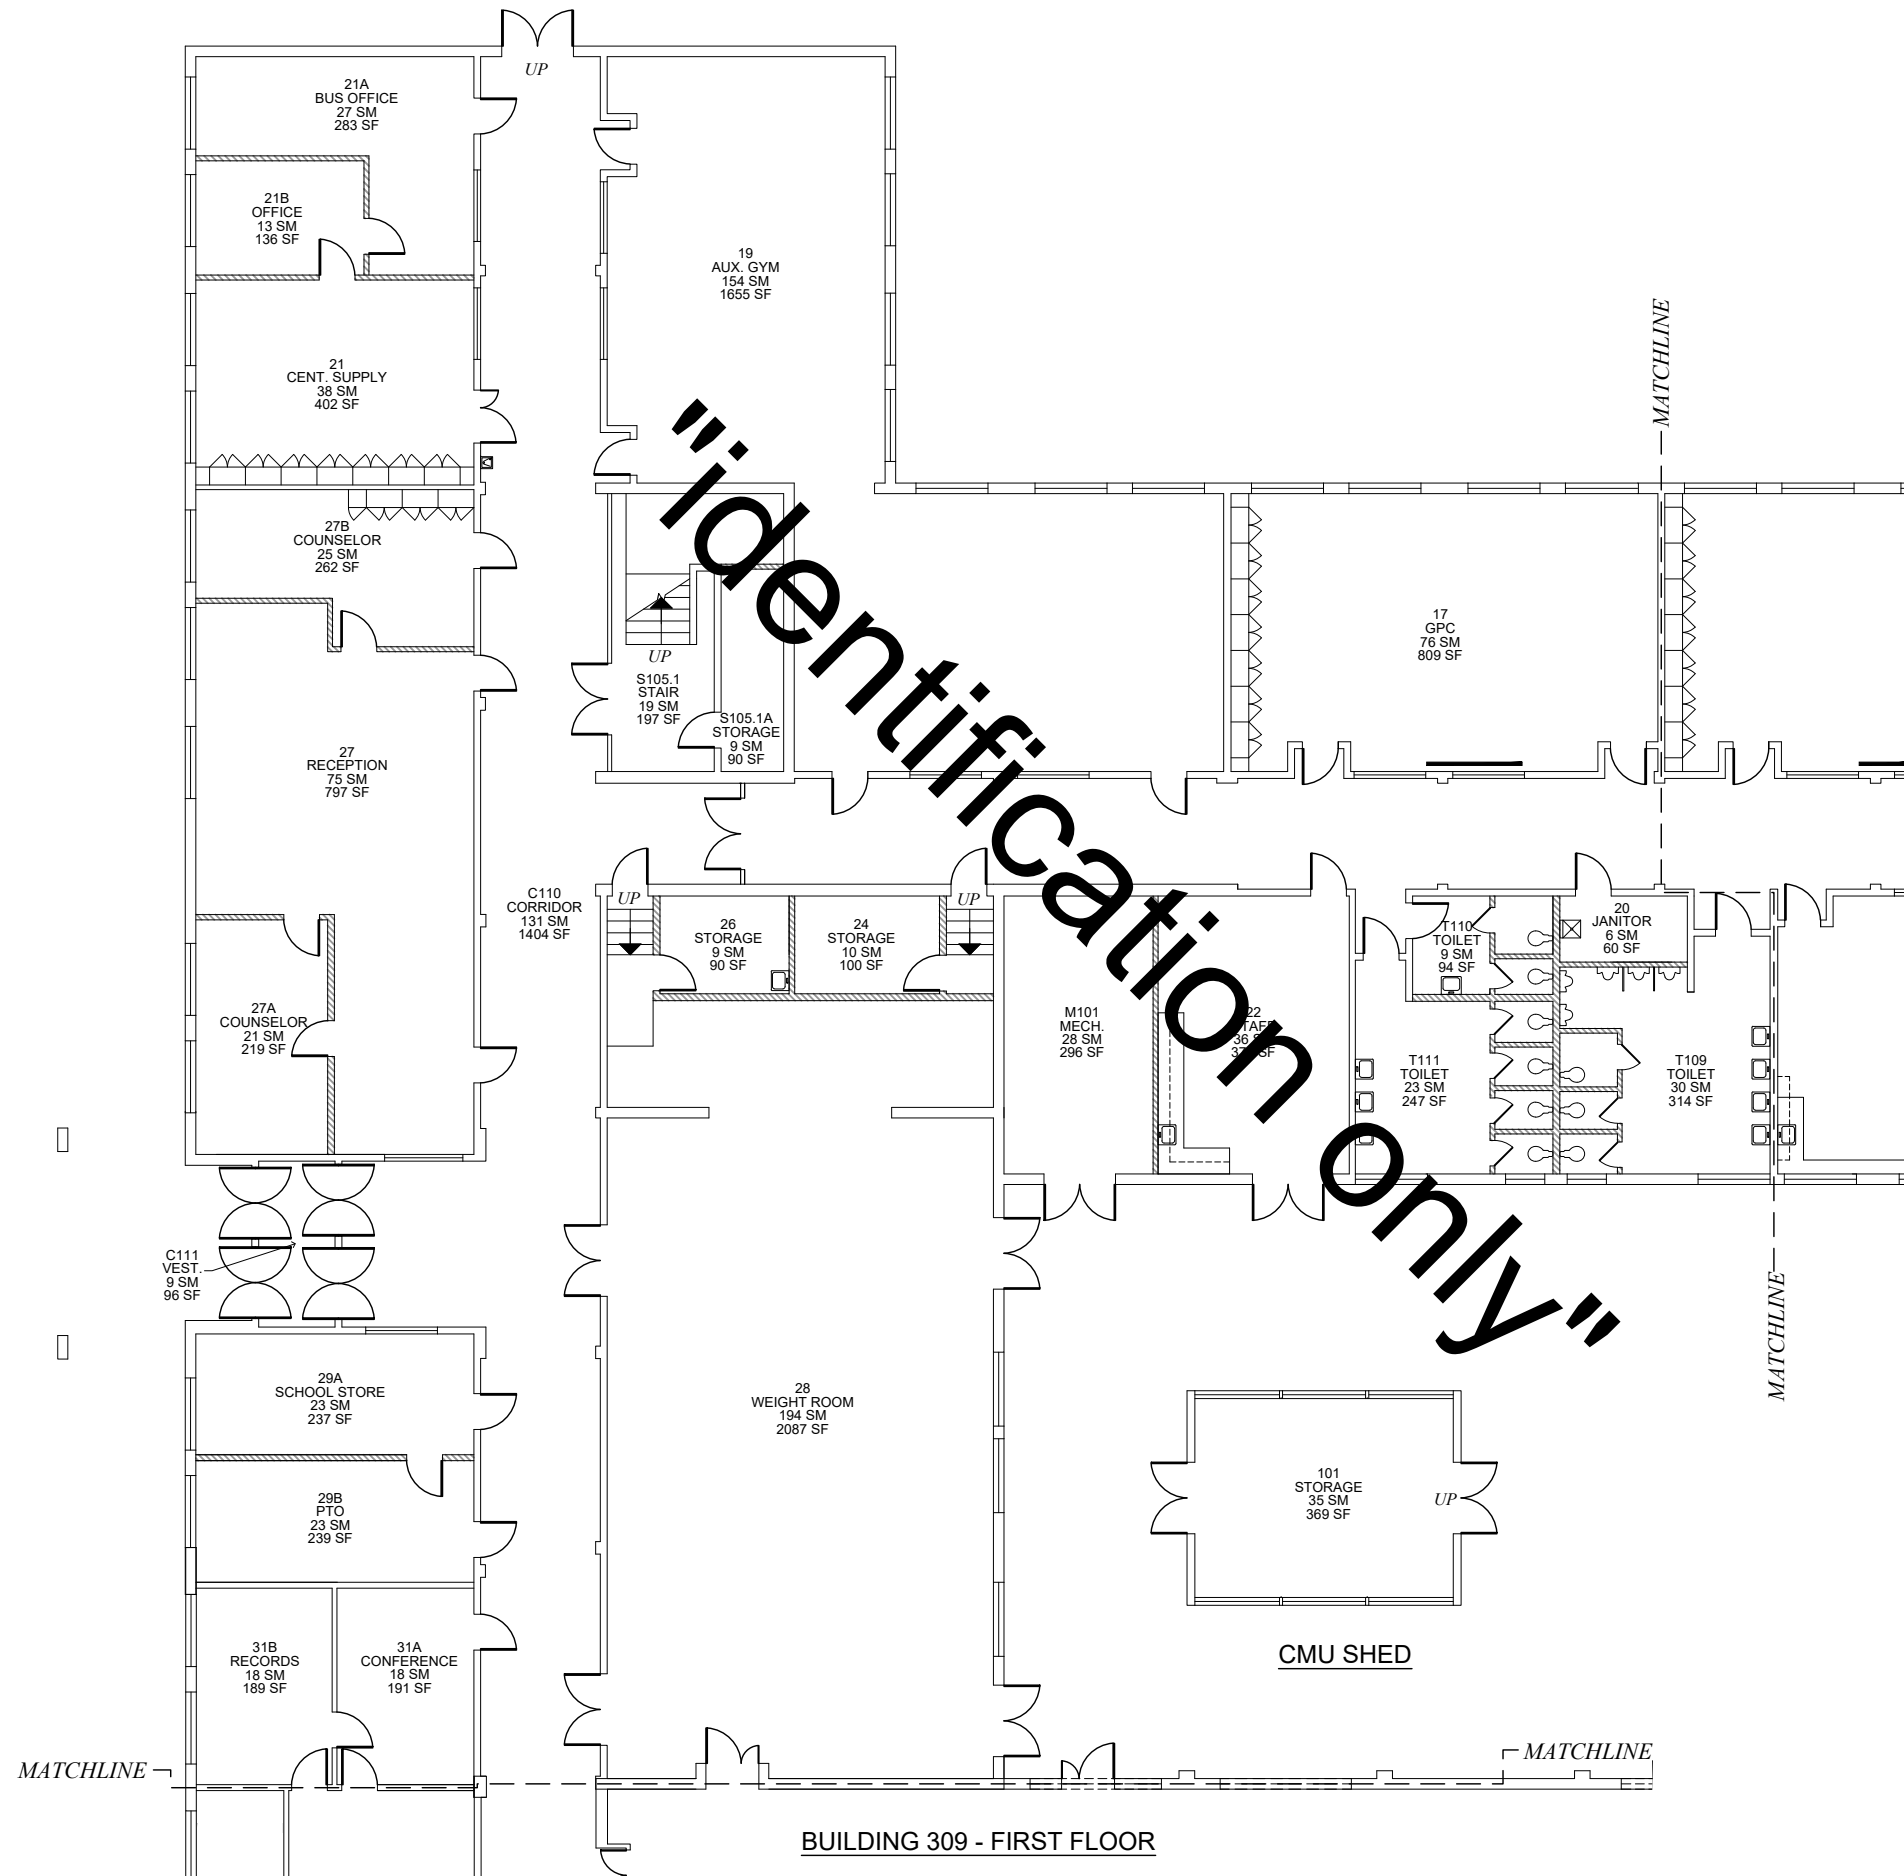

SYMBOL LEGEND	
	DOOR
	DRINKING FOUNTAIN
	SLIDING DOOR
	LAVATORY
	ACCORDION PARTITION
	SINK
	STACK OR FOLDING PARTITION
	TOILET
	WINDOW/GLAZING
	URINAL
	HIGH WINDOW
	LOCKER
	SKYLIGHT
	LAN DISTRIBUTION FRAME
	STOOP/STEP UP
	VENT HOOD
	STAIR
	WALL SHELVING
	RAMP
	UPPER CABINET
	ACCESS LADDER
	BASE CABINET
	COLD STORAGE
	TEACHER CABINET
	AREA CALCULATED @ 50 %
	MATCHLINE
	SLOPING ROOF
	FLAT ROOF

TITLEBLOCK LEGEND	
SHEET NAME:	BLDG #_FLOOR # (# IN SERIES)

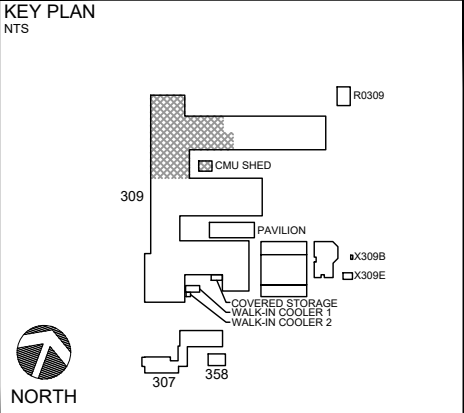


Updated By:	FUS Review:	100% Submittal Date:
SPF	MRS	01 MAY 2020
0 2 4 8 16 FT		

DEPARTMENT OF DEFENSE EDUCATION ACTIVITY
FACILITY UTILIZATION SURVEY


VICENZA HIGH SCHOOL /
DoDEA EUROPE SOUTH DSO
BUILDING NUMBER: 309, CMU SHED
COUNTRY: ITALY
INSTALLATION: US ARMY GARRISON ITALY
SITE: CAMP EDERLE
REGION-DISTRICT: DODEA EUROPE SOUTH

DoDAAC Number:	Floor:	Survey Date:
HE5419, HE5468	LEVEL 1	JANUARY 2020
Sheet Name:	Sheet Seq:	
309_1 (2)	9 of 19	

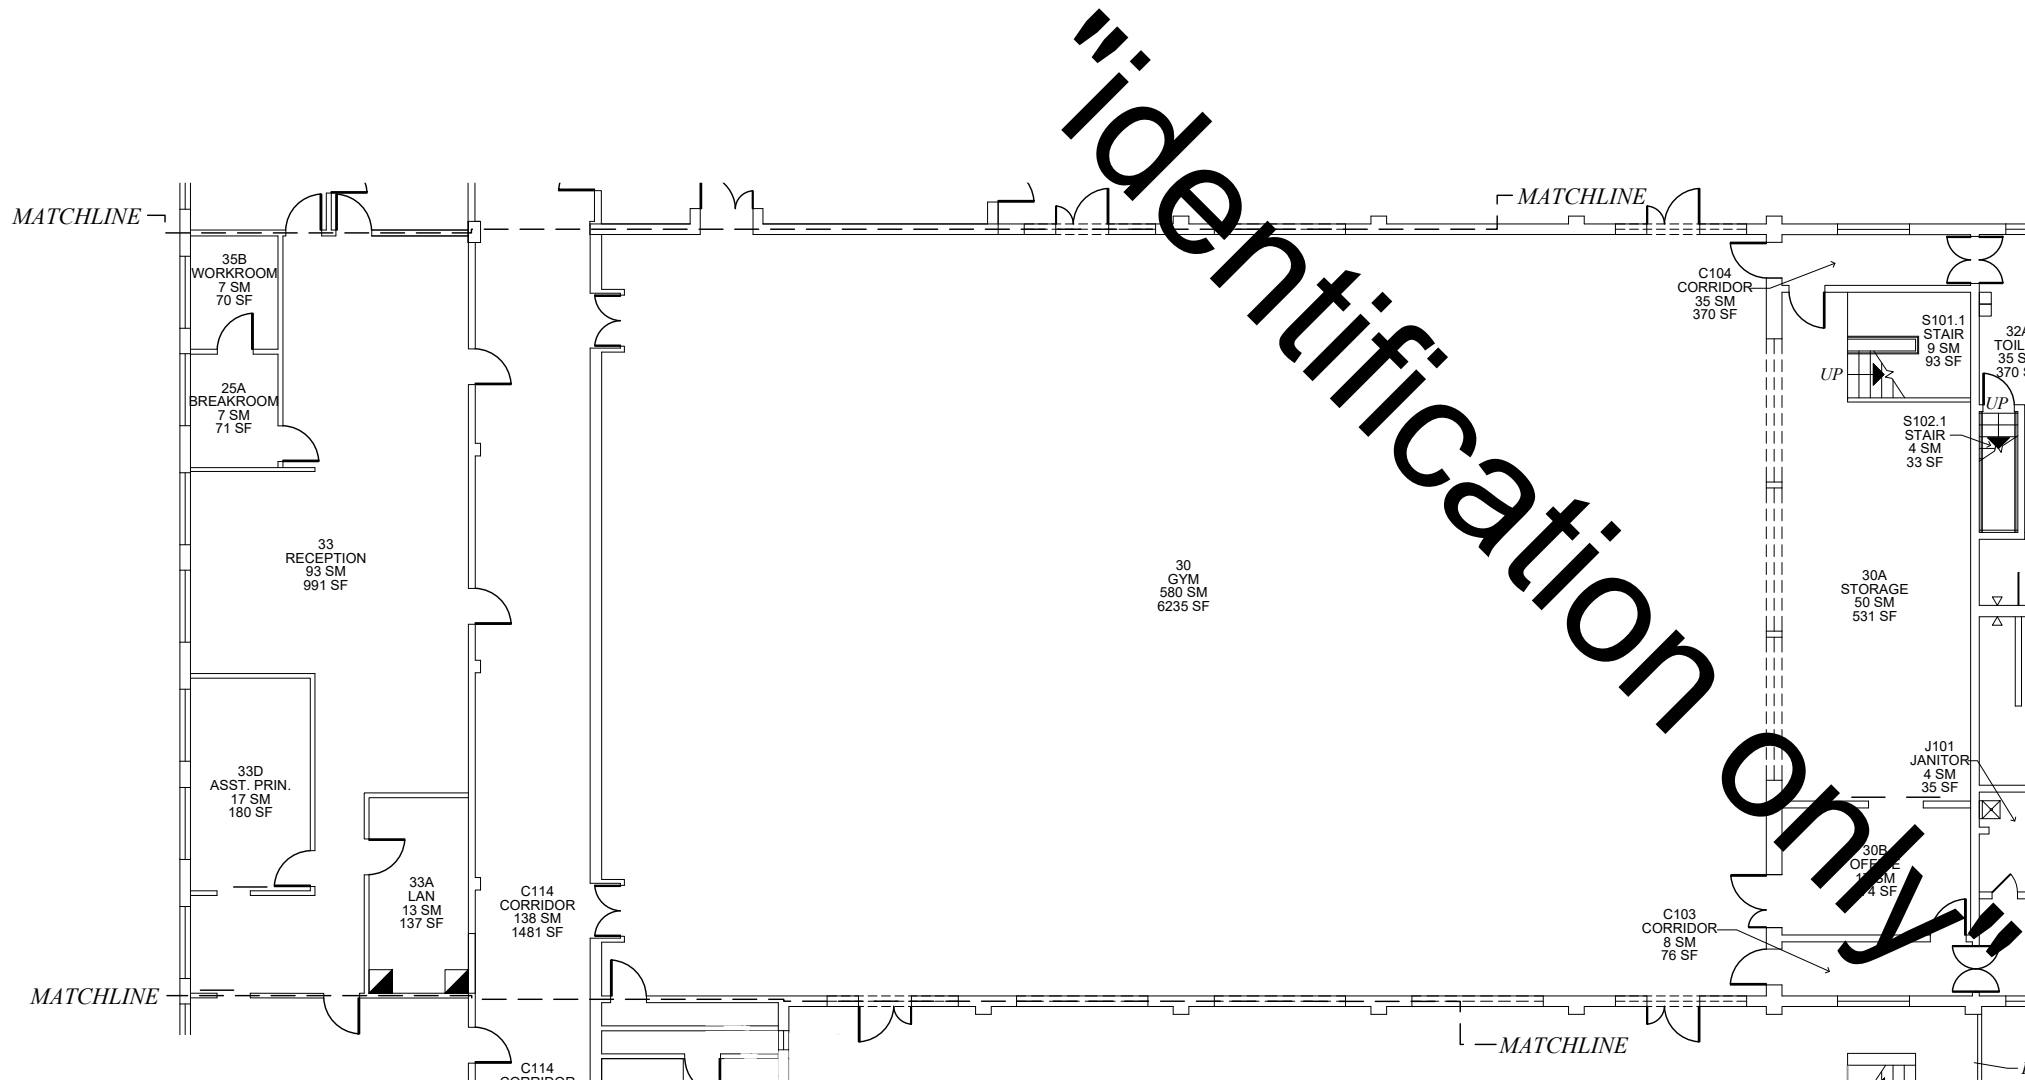

SYMBOL LEGEND	
	DOOR
	DRINKING FOUNTAIN
	SLIDING DOOR
	LAVATORY
	ACCORDION PARTITION
	SINK
	STACK OR FOLDING PARTITION
	TOILET
	WINDOW/GLAZING
	URINAL
	HIGH WINDOW
	LOCKER
	SKYLIGHT
	LAN DISTRIBUTION FRAME
	STOOP/STEP UP
	VENT HOOD
	STAIR
	WALL SHELVING
	RAMP
	UPPER CABINET
	ACCESS LADDER
	BASE CABINET
	COLD STORAGE
	TEACHER CABINET
	AREA CALCULATED @ 50 %
	MATCHLINE
	SLOPING ROOF
	FLAT ROOF

TITLEBLOCK LEGEND	
SHEET NAME:	BLDG #_FLOOR # (# IN SERIES)

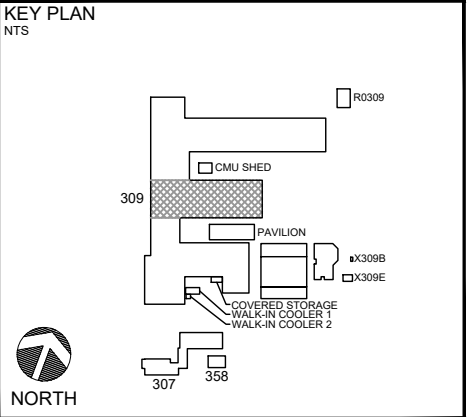


Updated By:	FUS Review:	100% Submittal Date:
SPF	MRS	01 MAY 2020
0 2 4 8 16 FT		

dodea
DEPARTMENT OF DEFENSE EDUCATION ACTIVITY
FACILITY UTILIZATION SURVEY

VICENZA HIGH SCHOOL /
DoDEA EUROPE SOUTH DSO
BUILDING NUMBER: 309
COUNTRY: ITALY
INSTALLATION: US ARMY GARRISON ITALY
SITE: CAMP EDERLE
REGION-DISTRICT: DODEA EUROPE SOUTH

DoDAAC Number:	Floor:	Survey Date:
HE5419, HE5468	LEVEL 1	JANUARY 2020
Sheet Name:	Sheet Seq:	
309_1 (3)		10 of 19

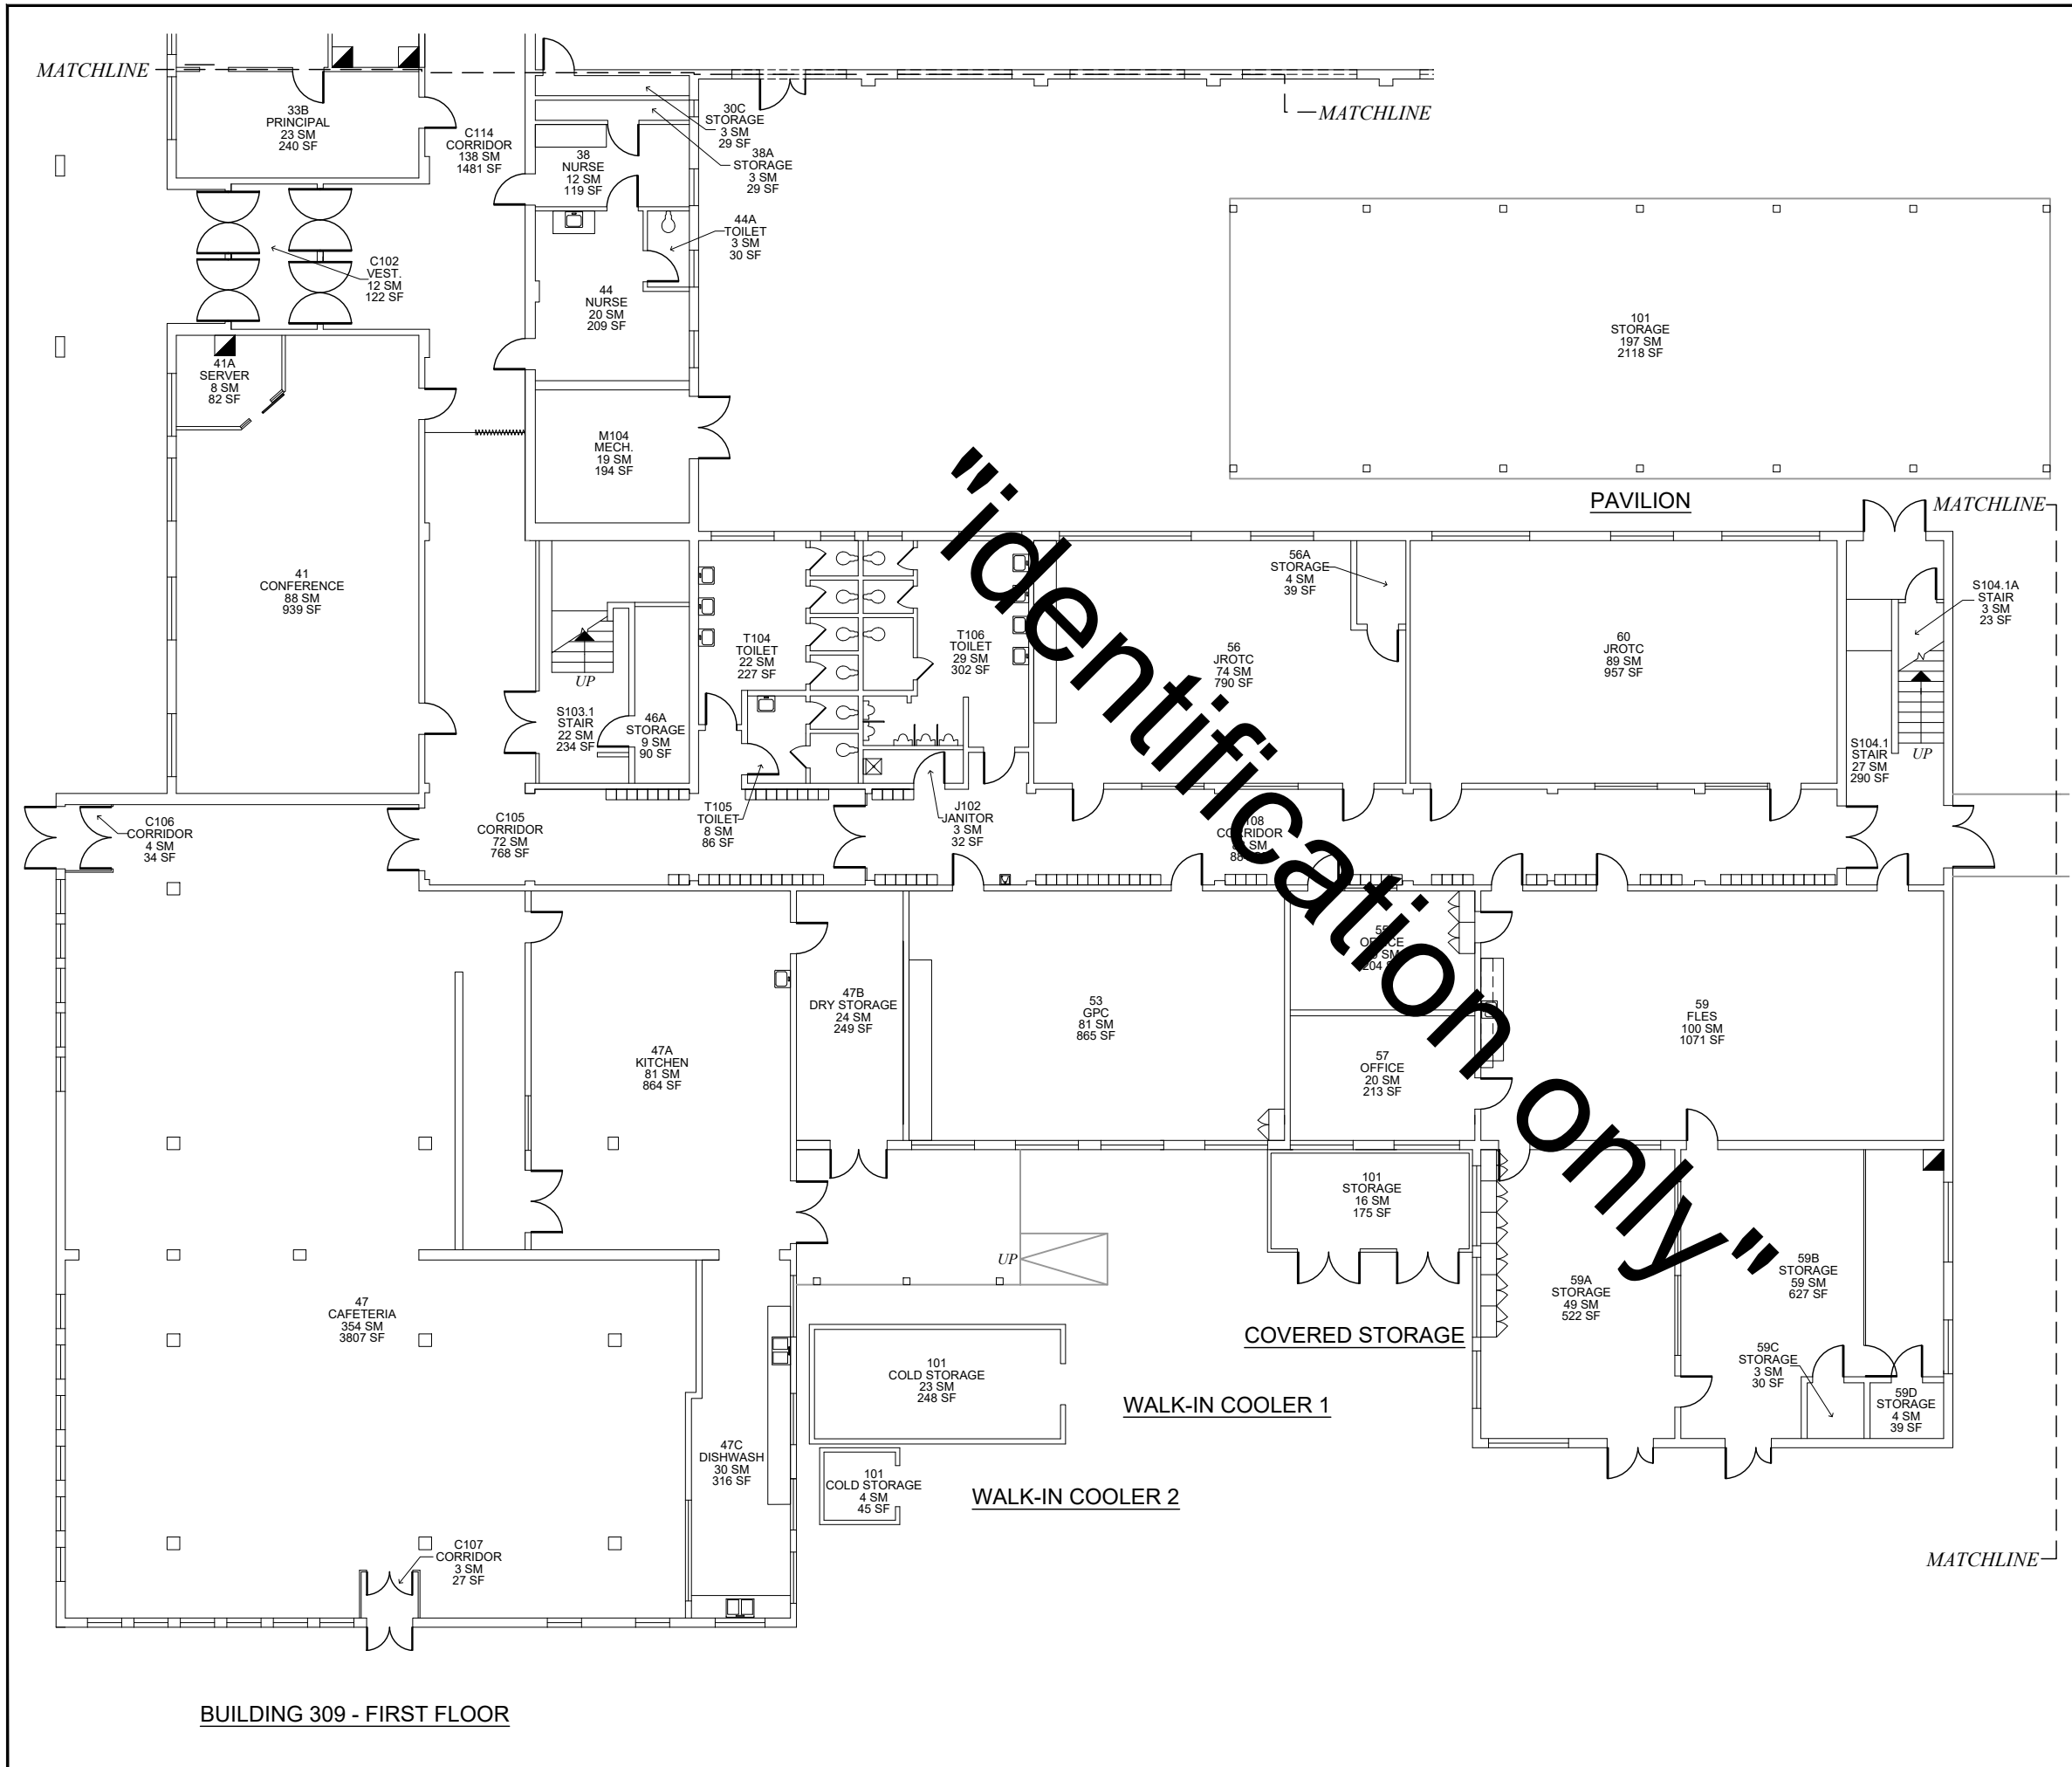

DOOR

SLIDING DOOR

ACCORDION PARTITION

STACK OR FOLDING PARTITION

WINDOW/GLAZING

HIGH WINDOW

SKYLIGHT

STOOP/STEP UP

STAIR

RAMP

ACCESS LADDER

COLD STORAGE

AREA CALCULATED @ 50 %

SLOPING ROOF

DRINKING FOUNTAIN

LAVATORY

SINK

TOILET

URINAL

LOCKER

LAN DISTRIBUTION FRAME

VENT HOOD

WALL SHELVING

UPPER CABINET

BASE CABINET

TEACHER CABINET

MATCHLINE

FLAT ROOF

TITLEBLOCK LEGEND

SHEET NAME:

BLDG # FLOOR # (# IN SERIES)

KEY PLAN

NTS

NORTH

Updated By: SPF

FUS Review: MRS

100% Submittal Date: 01 MAY 2020

0 2 4 8 16 FT

dodea

DEPARTMENT OF DEFENSE EDUCATION ACTIVITY

FACILITY UTILIZATION SURVEY

VICENZA HIGH SCHOOL / DoDEA EUROPE SOUTH DSO

BUILDING NUMBER: 309, PAVILION, COVERED STORAGE, WALK-IN COOLER(S) 1, 2,

COUNTRY: ITALY

INSTALLATION: US ARMY GARRISON ITALY

SITE: CAMP EDERLE

REGION-DISTRICT: DODEA EUROPE SOUTH

DoDAAC Number: HE5419, HE5468

Floor: LEVEL 1


Survey Date: JANUARY 2020

Sheet Name: 309_1 (4)


Sheet Seq: 11 of 19

MATCHLINE

MATCHLINE

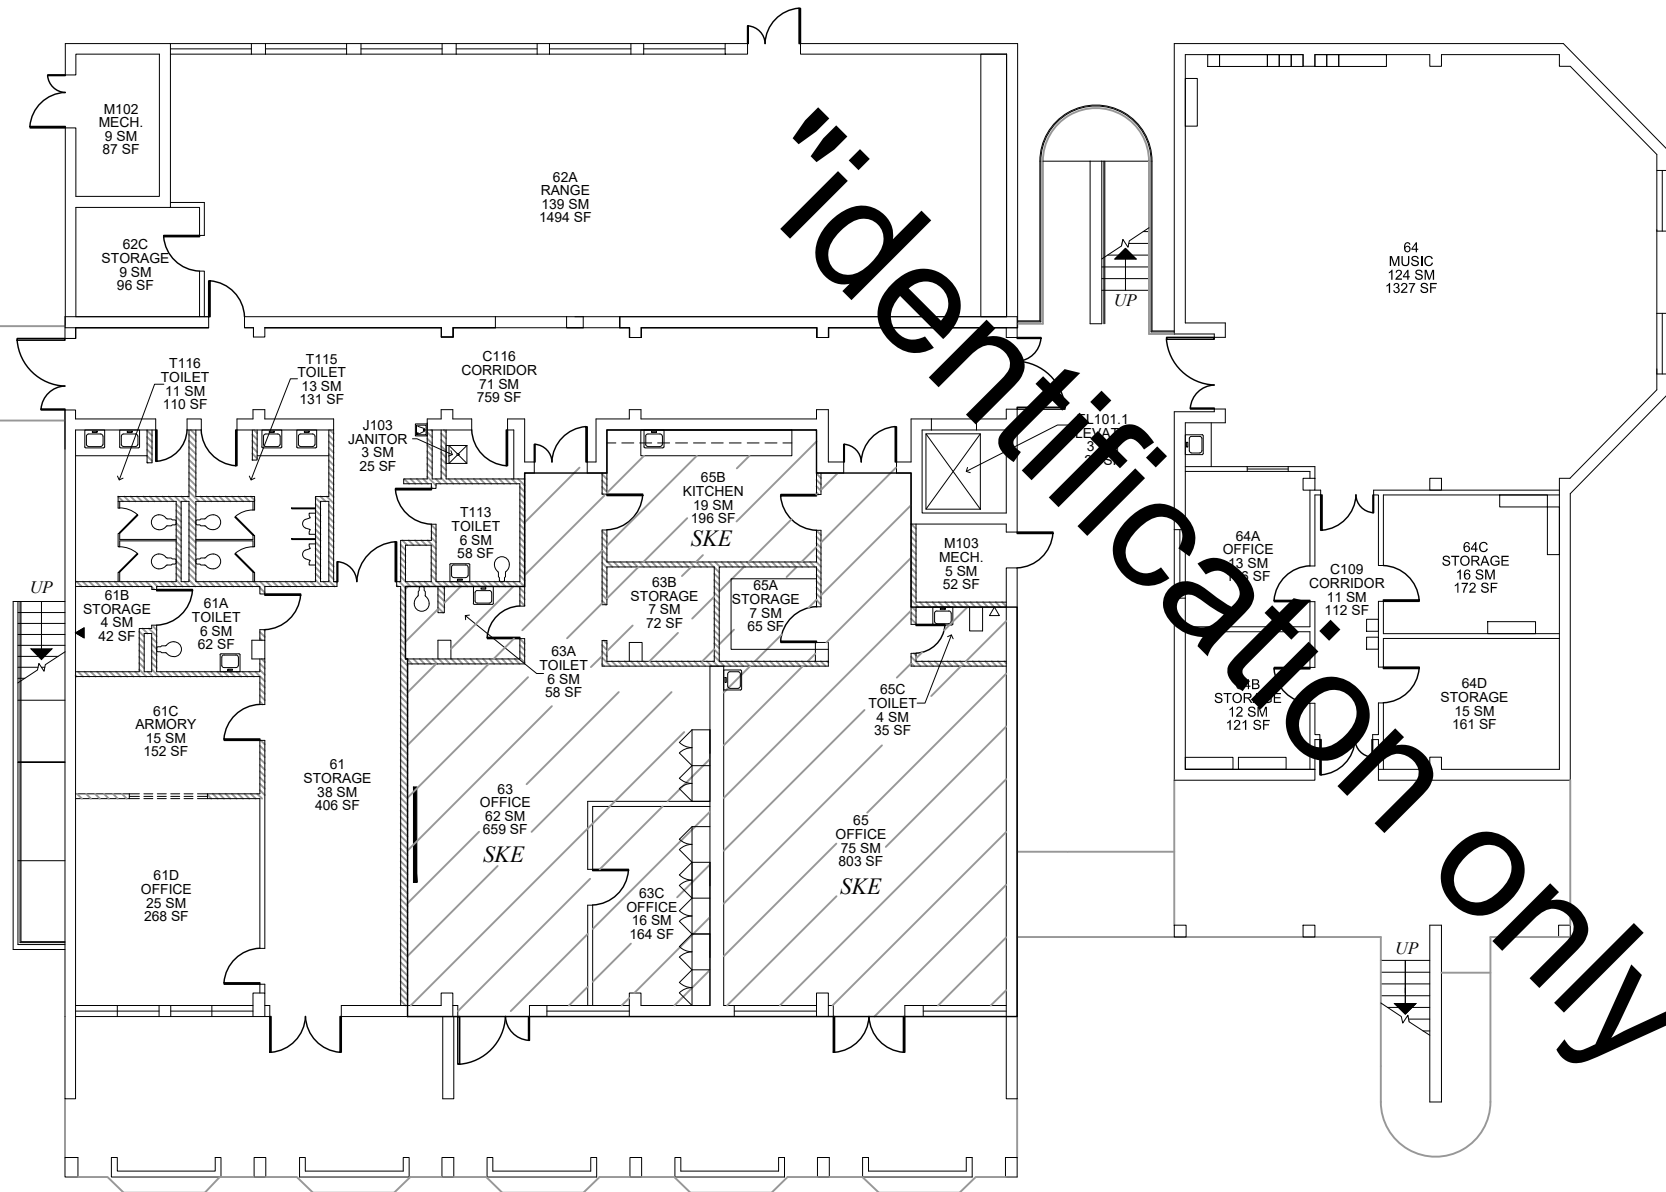


BUILDING 309 - FIRST FLOOR

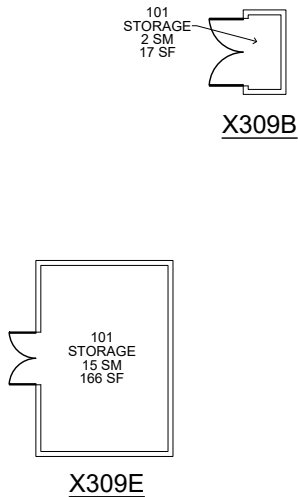

SYMBOL LEGEND	
	DOOR
	DRINKING FOUNTAIN
	SLIDING DOOR
	LAVATORY
	ACCORDION PARTITION
	SINK
	STACK OR FOLDING PARTITION
	TOILET
	WINDOW/GLAZING
	URINAL
	HIGH WINDOW
	LOCKER
	SKYLIGHT
	LAN DISTRIBUTION FRAME
	STOOP/STEP UP
	VENT HOOD
	STAIR
	WALL SHELVING
	RAMP
	UPPER CABINET
	ACCESS LADDER
	BASE CABINET
	COLD STORAGE
	TEACHER CABINET
	AREA CALCULATED @ 50 %
	MATCHLINE
	SLOPING ROOF
	FLAT ROOF

TITLEBLOCK LEGEND	
SHEET NAME:	BLDG #_FLOOR # (# IN SERIES)

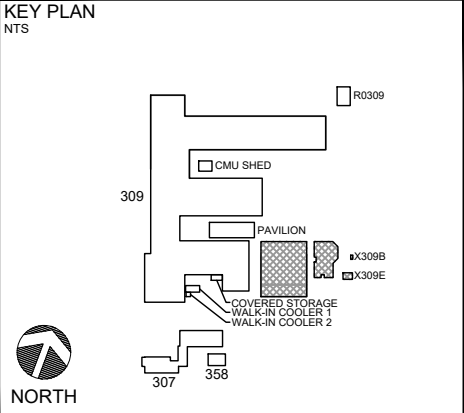


Updated By:	FUS Review:	100% Submittal Date:
SPF	MRS	01 MAY 2020
0 2 4 8 16 FT		

DEPARTMENT OF DEFENSE EDUCATION ACTIVITY
FACILITY UTILIZATION SURVEY


VICENZA HIGH SCHOOL /
DoDEA EUROPE SOUTH DSO
BUILDING NUMBER: 309, X309B, X309E
COUNTRY: ITALY
INSTALLATION: US ARMY GARRISON ITALY
SITE: CAMP EDERLE
REGION-DISTRICT: DODEA EUROPE SOUTH

DoDAAC Number:	Floor:	Survey Date:
HE5419, HE5468	LEVEL 1	JANUARY 2020
Sheet Name:	Sheet Seq:	
309_1 (5)		12 of 19

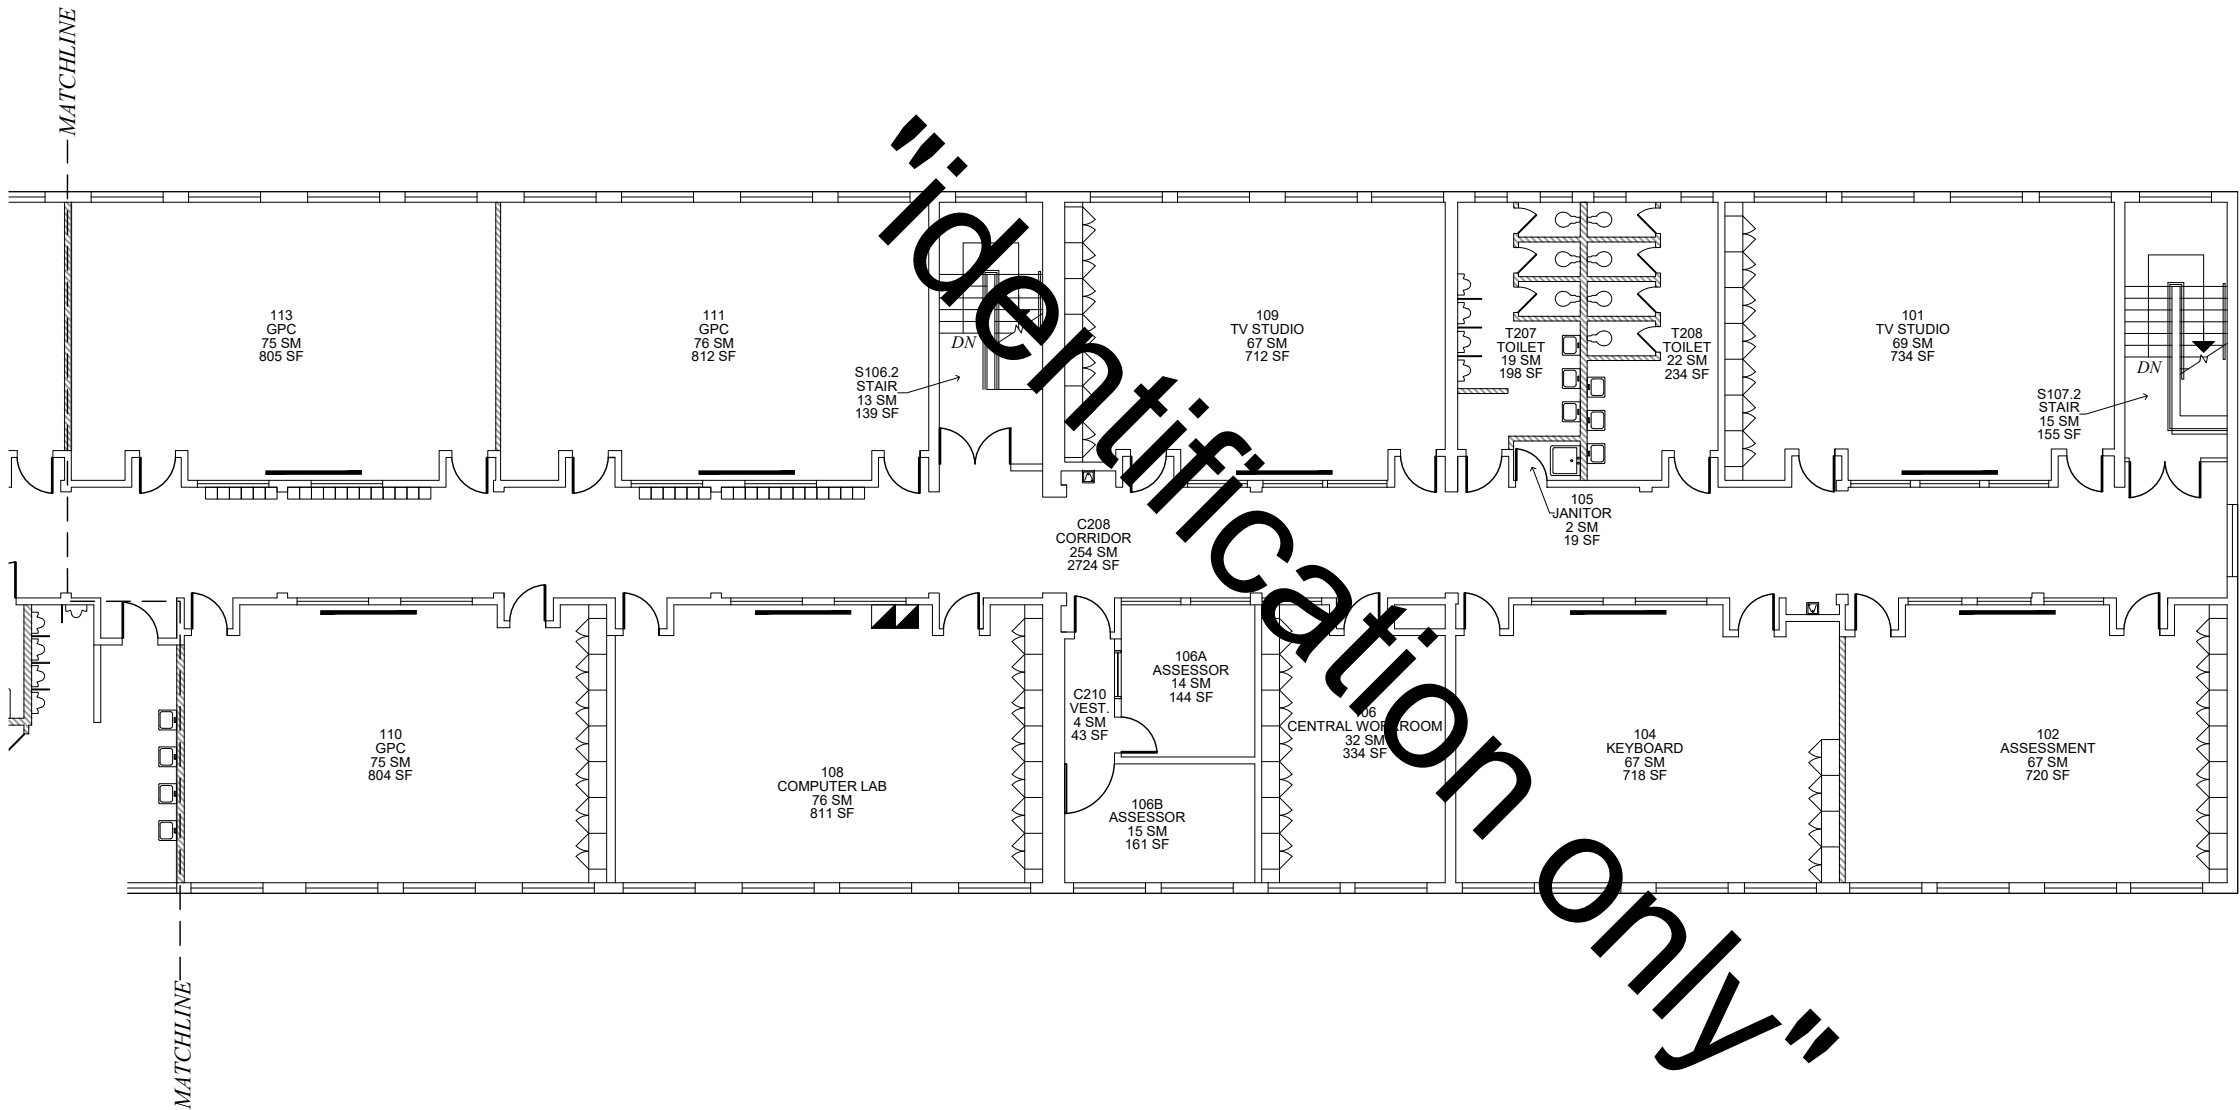

SYMBOL LEGEND	
	DOOR
	DRINKING FOUNTAIN
	SLIDING DOOR
	LAVATORY
	ACCORDION PARTITION
	SINK
	STACK OR FOLDING PARTITION
	TOILET
	WINDOW/GLAZING
	URINAL
	HIGH WINDOW
	LOCKER
	SKYLIGHT
	LAN DISTRIBUTION FRAME
	STOOP/STEP UP
	VENT HOOD
	STAIR
	WALL SHELVING
	RAMP
	UPPER CABINET
	ACCESS LADDER
	BASE CABINET
	COLD STORAGE
	TEACHER CABINET
	AREA CALCULATED @ 50 %
	MATCHLINE
	SLOPING ROOF
	FLAT ROOF

TITLEBLOCK LEGEND	
SHEET NAME:	BLDG # FLOOR # (# IN SERIES)

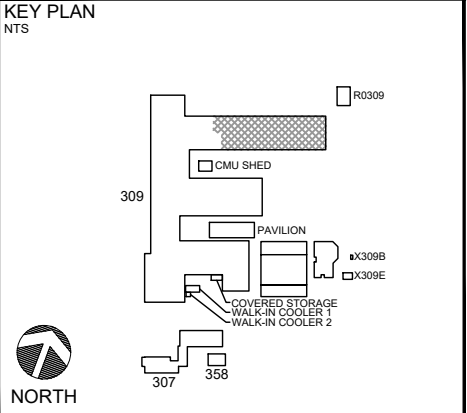


Updated By:	FUS Review:	100% Submittal Date:
SPF	MRS	01 MAY 2020
0 2 4 8 16 FT		

dodea
DEPARTMENT OF DEFENSE EDUCATION ACTIVITY
FACILITY UTILIZATION SURVEY


VICENZA HIGH SCHOOL /
DoDEA EUROPE SOUTH DSO
BUILDING NUMBER: 309
COUNTRY: ITALY
INSTALLATION: US ARMY GARRISON ITALY
SITE: CAMP EDERLE
REGION-DISTRICT: DODEA EUROPE SOUTH

DoDAAC Number:	Floor:	Survey Date:
HE5419, HE5468	LEVEL 2	JANUARY 2020
Sheet Name:	Sheet Seq:	
309_2 (1)	13 of 19	

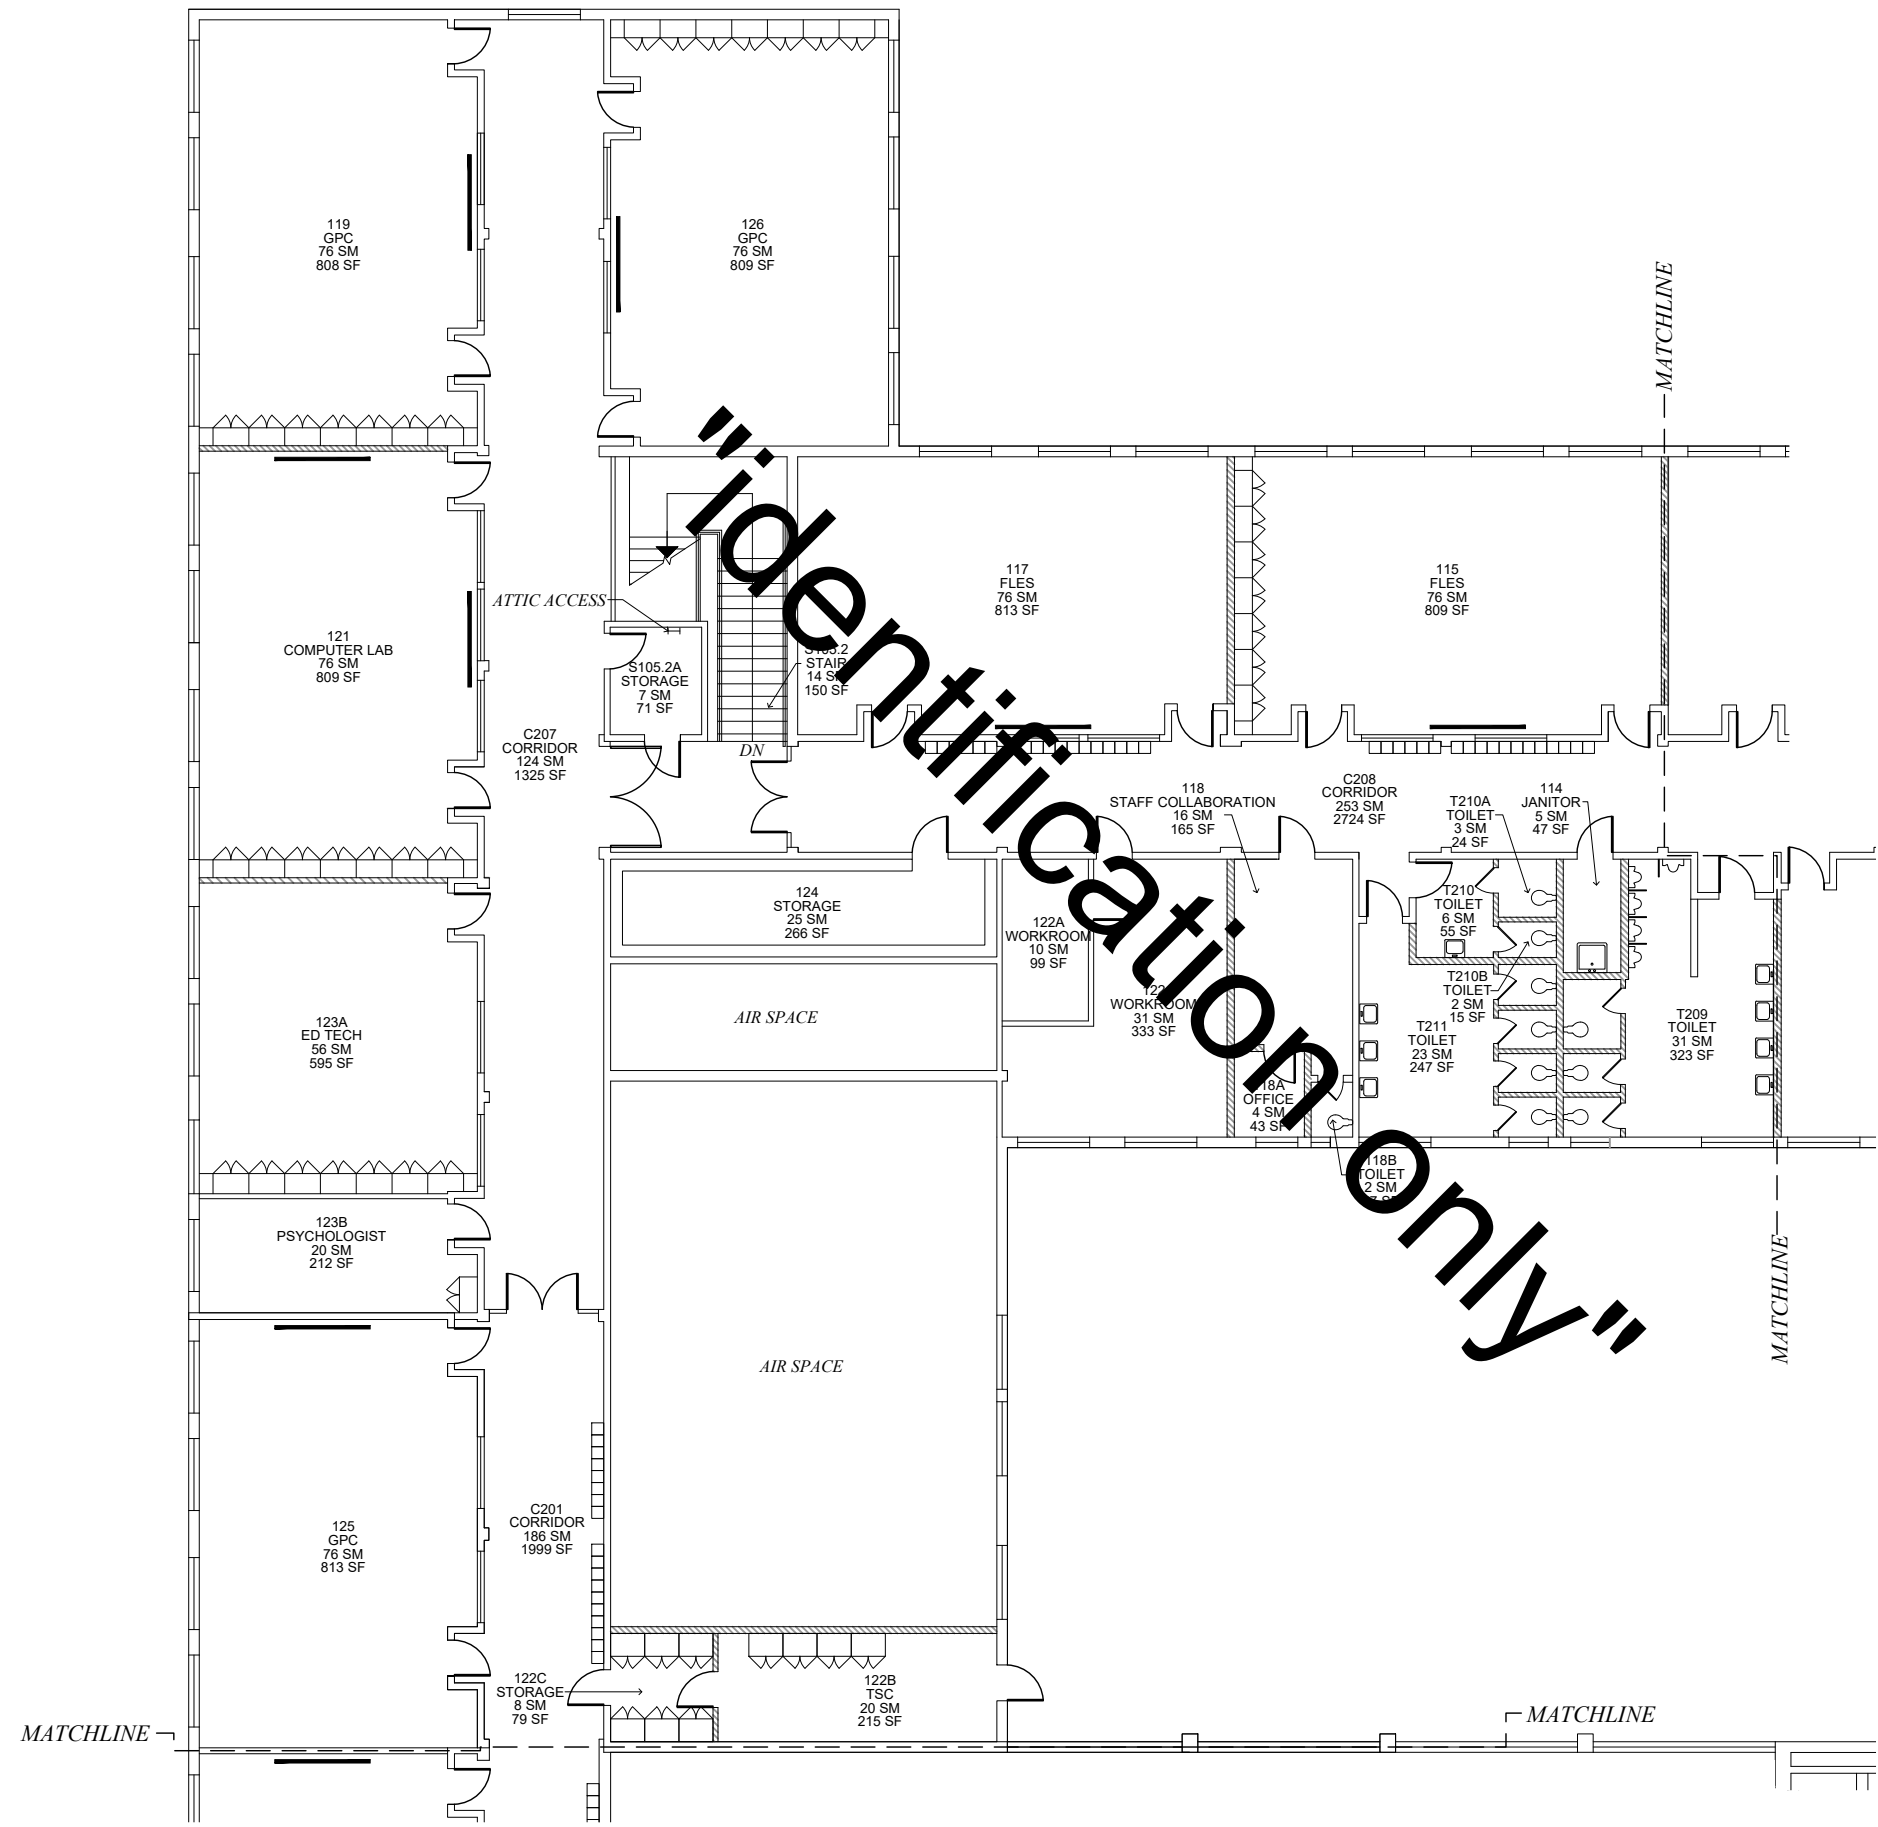

SYMBOL LEGEND	
	DOOR
	DRINKING FOUNTAIN
	SLIDING DOOR
	LAVATORY
	ACCORDION PARTITION
	SINK
	STACK OR FOLDING PARTITION
	TOILET
	WINDOW/GLAZING
	URINAL
	HIGH WINDOW
	LOCKER
	SKYLIGHT
	LAN DISTRIBUTION FRAME
	STOOP/STEP UP
	VENT HOOD
	STAIR
	WALL SHELVING
	RAMP
	UPPER CABINET
	ACCESS LADDER
	BASE CABINET
	COLD STORAGE
	TEACHER CABINET
	AREA CALCULATED @ 50 %
	SLOPING ROOF
	FLAT ROOF

TITLEBLOCK LEGEND	
SHEET NAME:	BLDG #_FLOOR # (# IN SERIES)

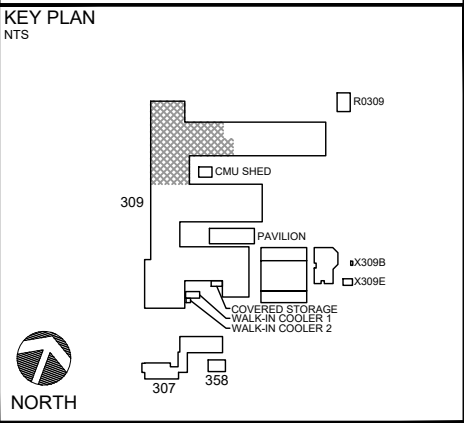


Updated By:	FUS Review:	100% Submittal Date:
SPF	MRS	01 MAY 2020

0 2 4 8 16 FT

dodea
DEPARTMENT OF DEFENSE EDUCATION ACTIVITY
FACILITY UTILIZATION SURVEY

VICENZA HIGH SCHOOL / DoDEA EUROPE SOUTH DSO		
BUILDING NUMBER: 309		
COUNTRY: ITALY		
INSTALLATION: US ARMY GARRISON ITALY		
SITE: CAMP EDERLE		
REGION-DISTRICT: DODEA EUROPE SOUTH		
DoDAAC Number:	Floor:	Survey Date:
HE5419, HE5468	LEVEL 2	JANUARY 2020
Sheet Name:	Sheet Seq:	
309_2 (2)	14 of 19	

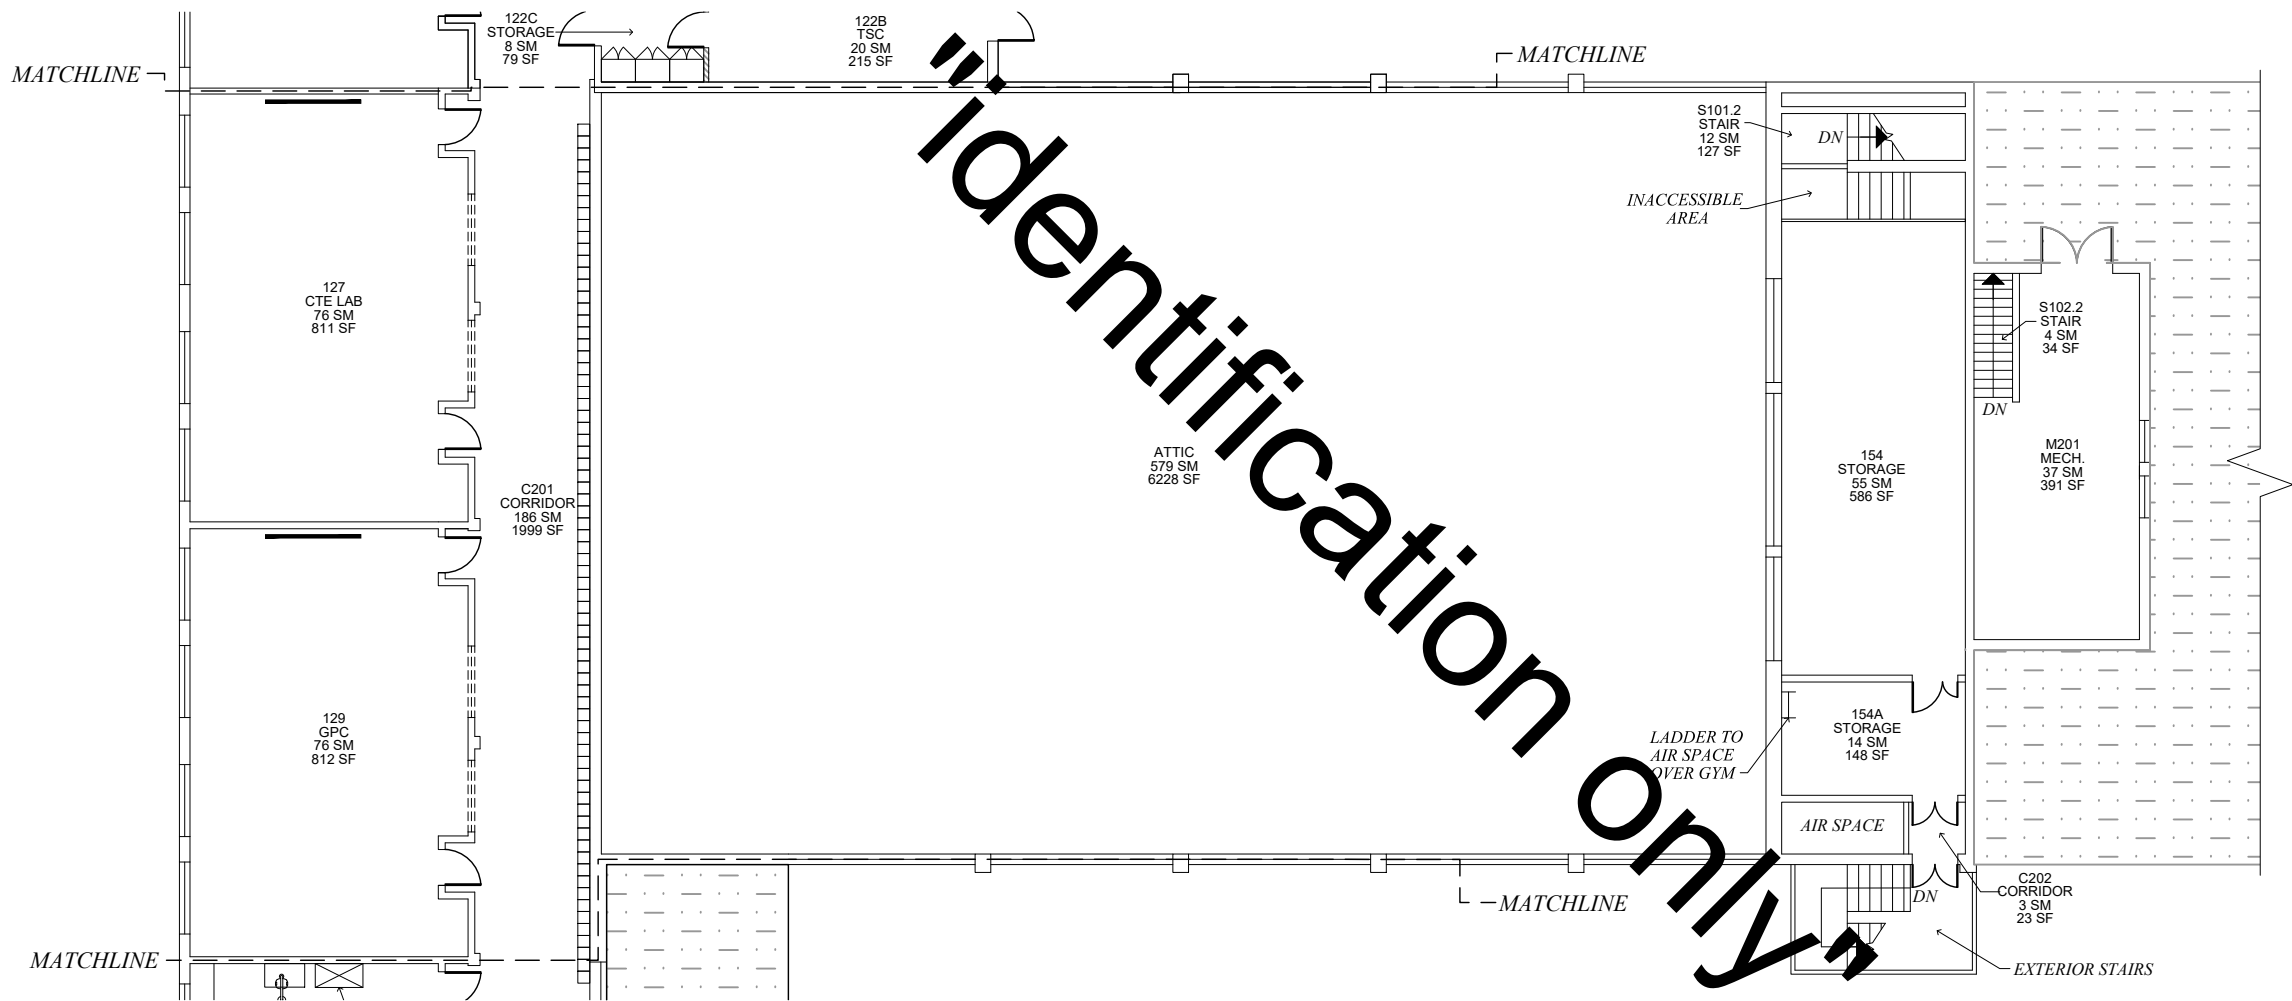

DOOR

SLIDING DOOR

ACCORDION PARTITION

STACK OR FOLDING PARTITION

WINDOW/GLAZING

HIGH WINDOW

SKYLIGHT

STOOP/STEP UP

STAIR

RAMP

ACCESS LADDER

COLD STORAGE

AREA CALCULATED @ 50 %

SLOPING ROOF

DRINKING FOUNTAIN

LAVATORY

SINK

TOILET

URINAL

LOCKER

LAN DISTRIBUTION FRAME

VENT HOOD

WALL SHELVING

UPPER CABINET

BASE CABINET

TEACHER CABINET

MATCHLINE

FLAT ROOF

TITLEBLOCK LEGEND

SHEET NAME:

BLDG #_FLOOR # (# IN SERIES)

KEY PLAN

NTS

NORTH

Updated By: SPF

FUS Review: MRS

100% Submittal Date: 01 MAY 2020

0 2 4 8 16 FT

dodea

DEPARTMENT OF DEFENSE EDUCATION ACTIVITY

FACILITY UTILIZATION SURVEY

VICENZA HIGH SCHOOL / DoDEA EUROPE SOUTH DSO

BUILDING NUMBER: 309

COUNTRY: ITALY

INSTALLATION: US ARMY GARRISON ITALY

SITE: CAMP EDERLE

REGION-DISTRICT: DODEA EUROPE SOUTH


DoDAAC Number: HE5419, HE5468

Floor: LEVEL 2

Survey Date: JANUARY 2020


Sheet Name: 309_2 (3)

Sheet Seq: 15 of 19

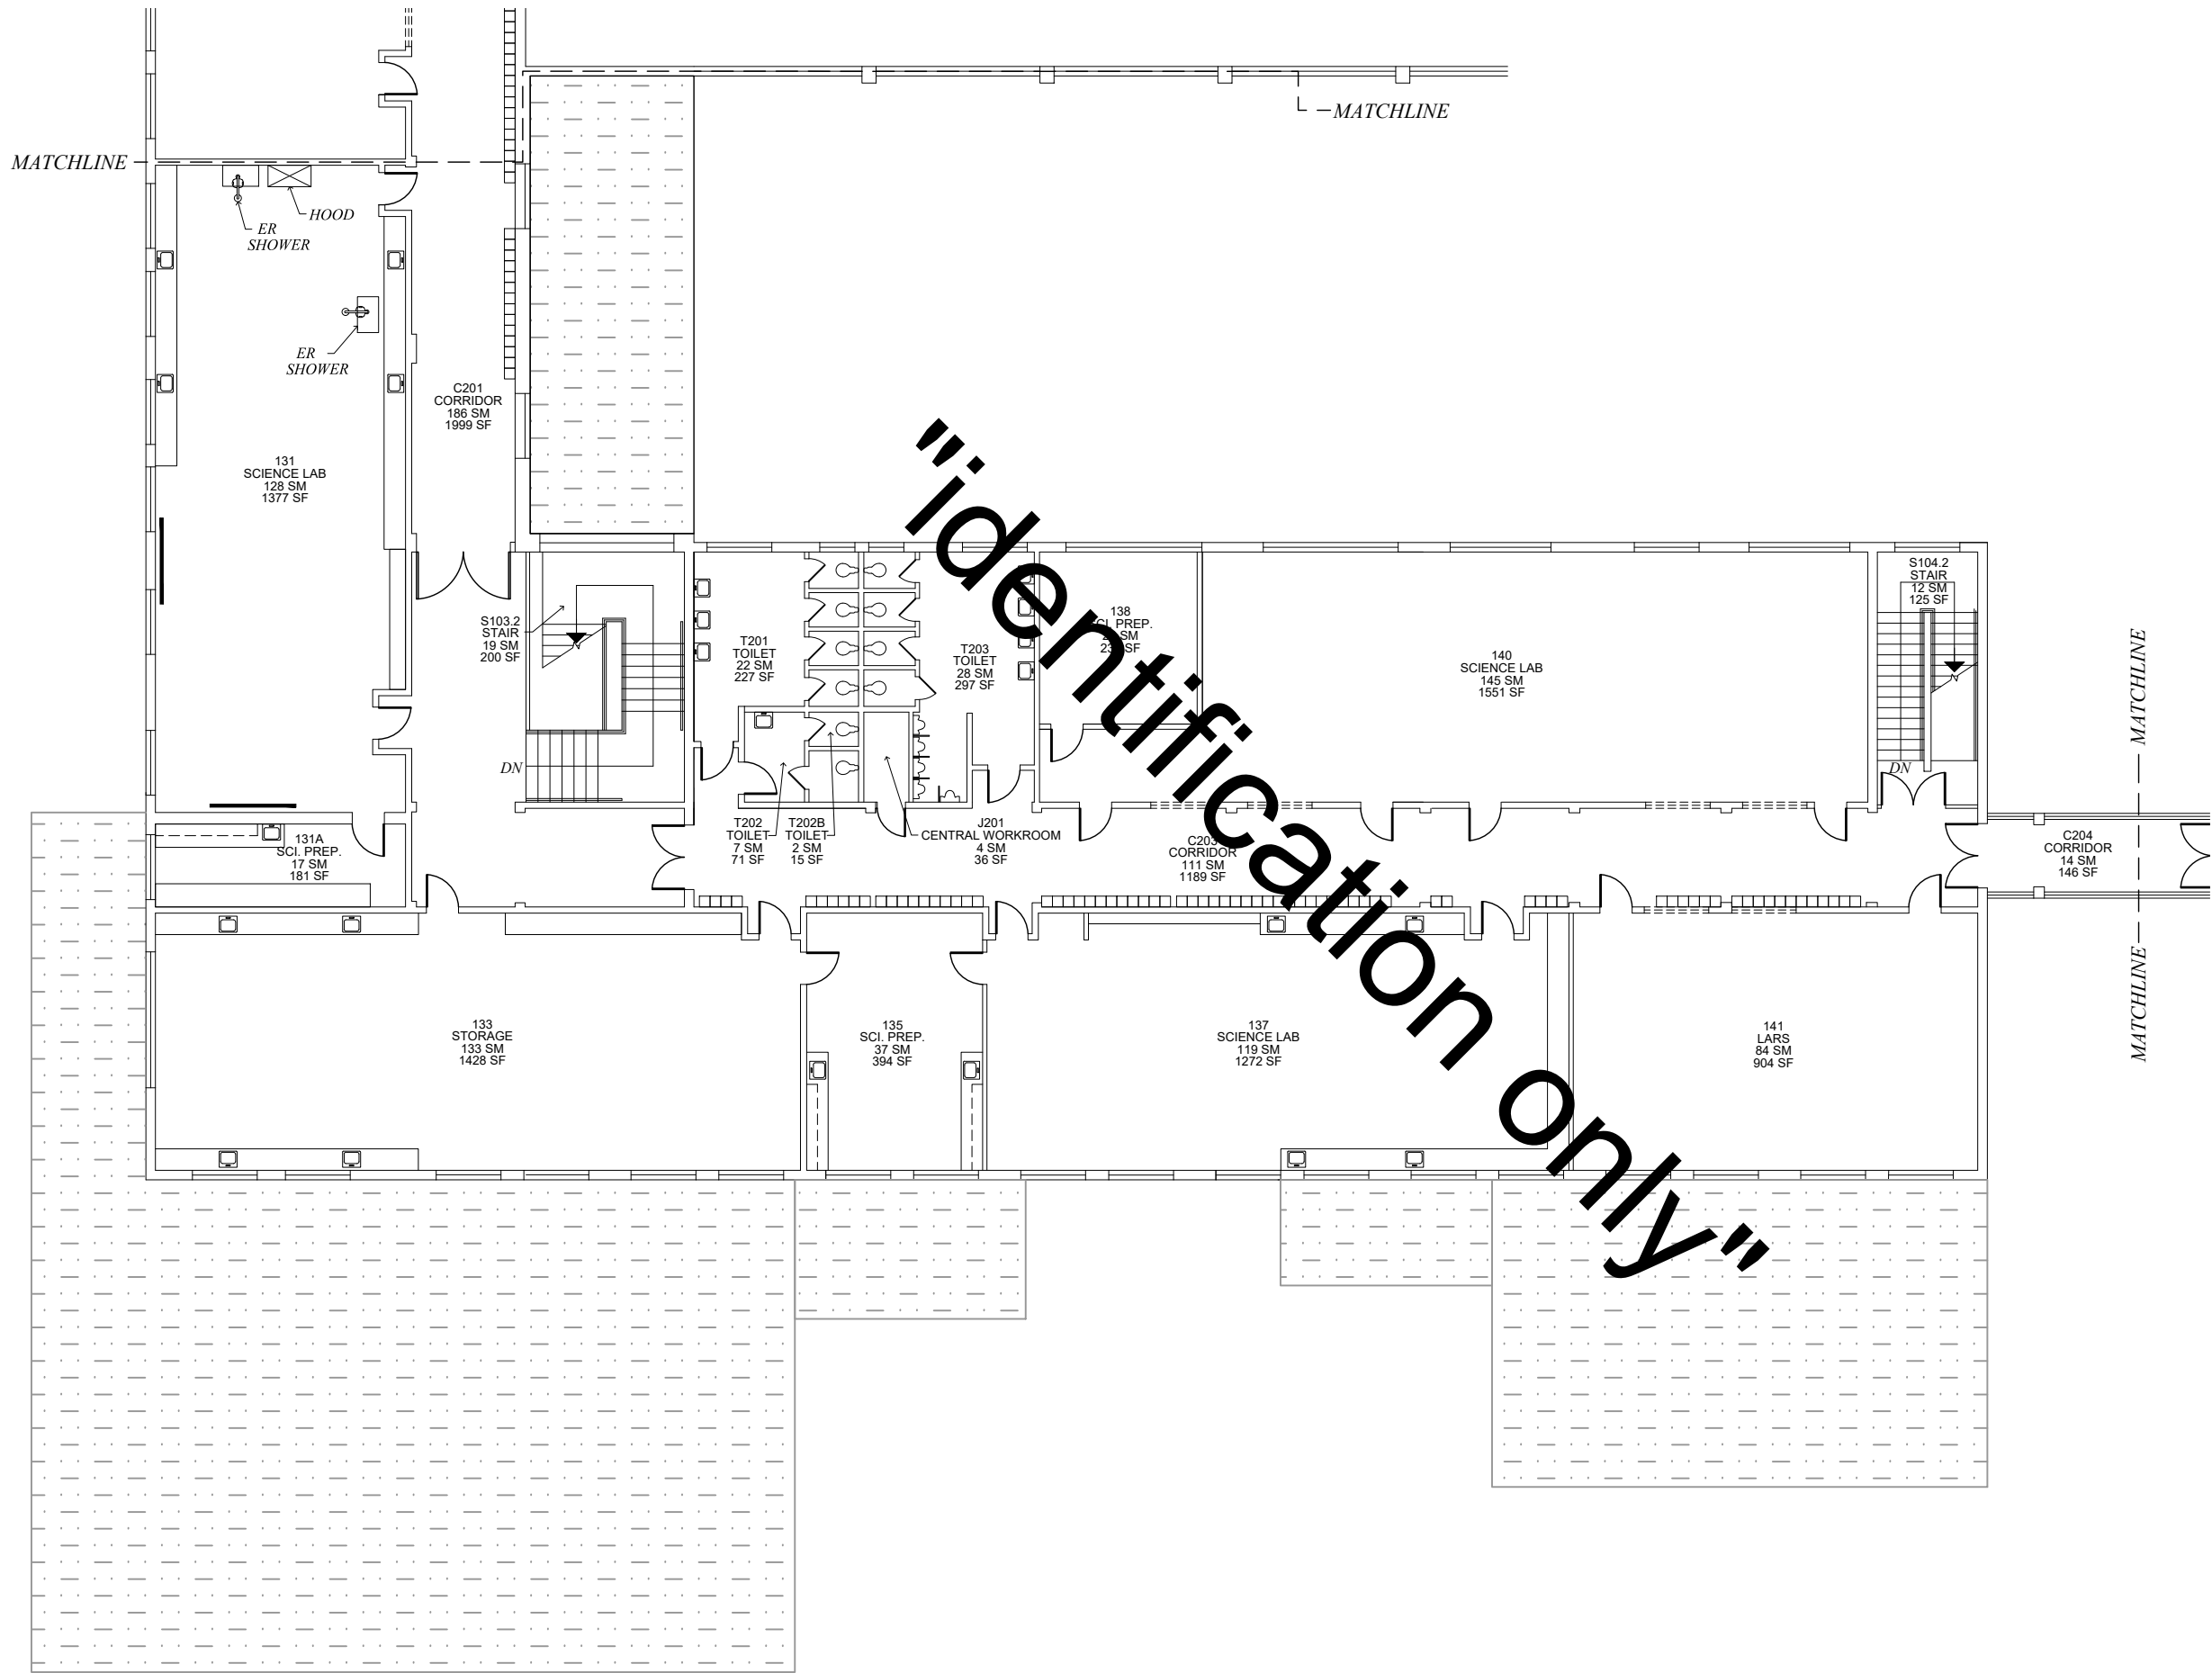

SYMBOL LEGEND	
	DOOR
	SLIDING DOOR
	ACCORDION PARTITION
	STACK OR FOLDING PARTITION
	WINDOW/GLAZING
	HIGH WINDOW
	SKYLIGHT
	STOOP/STEP UP
	STAIR
	RAMP
	ACCESS LADDER
	COLD STORAGE
	AREA CALCULATED @ 50 %
	SLOPING ROOF
	DRINKING FOUNTAIN
	LAVATORY
	SINK
	TOILET
	URINAL
	LOCKER
	LAN DISTRIBUTION FRAME
	VENT HOOD
	WALL SHELVING
	UPPER CABINET
	BASE CABINET
	TEACHER CABINET
	MATCHLINE


TITLEBLOCK LEGEND	
SHEET NAME:	BLDG #_FLOOR # (# IN SERIES)

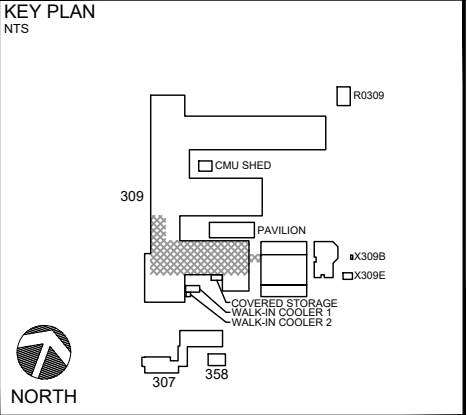

Updated By: SPF	FUS Review: MRS	100% Submittal Date: 01 MAY 2020
0 2 4 8 16 FT		

DEPARTMENT OF DEFENSE EDUCATION ACTIVITY
FACILITY UTILIZATION SURVEY

VICENZA HIGH SCHOOL / DoDEA EUROPE SOUTH DSO		
BUILDING NUMBER: 309		
COUNTRY: ITALY		
INSTALLATION: US ARMY GARRISON ITALY		
SITE: CAMP EDERLE		
REGION-DISTRICT: DODEA EUROPE SOUTH		
DoDAAC Number: HE5419, HE5468	Floor: LEVEL 2	Survey Date: JANUARY 2020
Sheet Name: 309_2 (4)	Sheet Seq: 16 of 17	

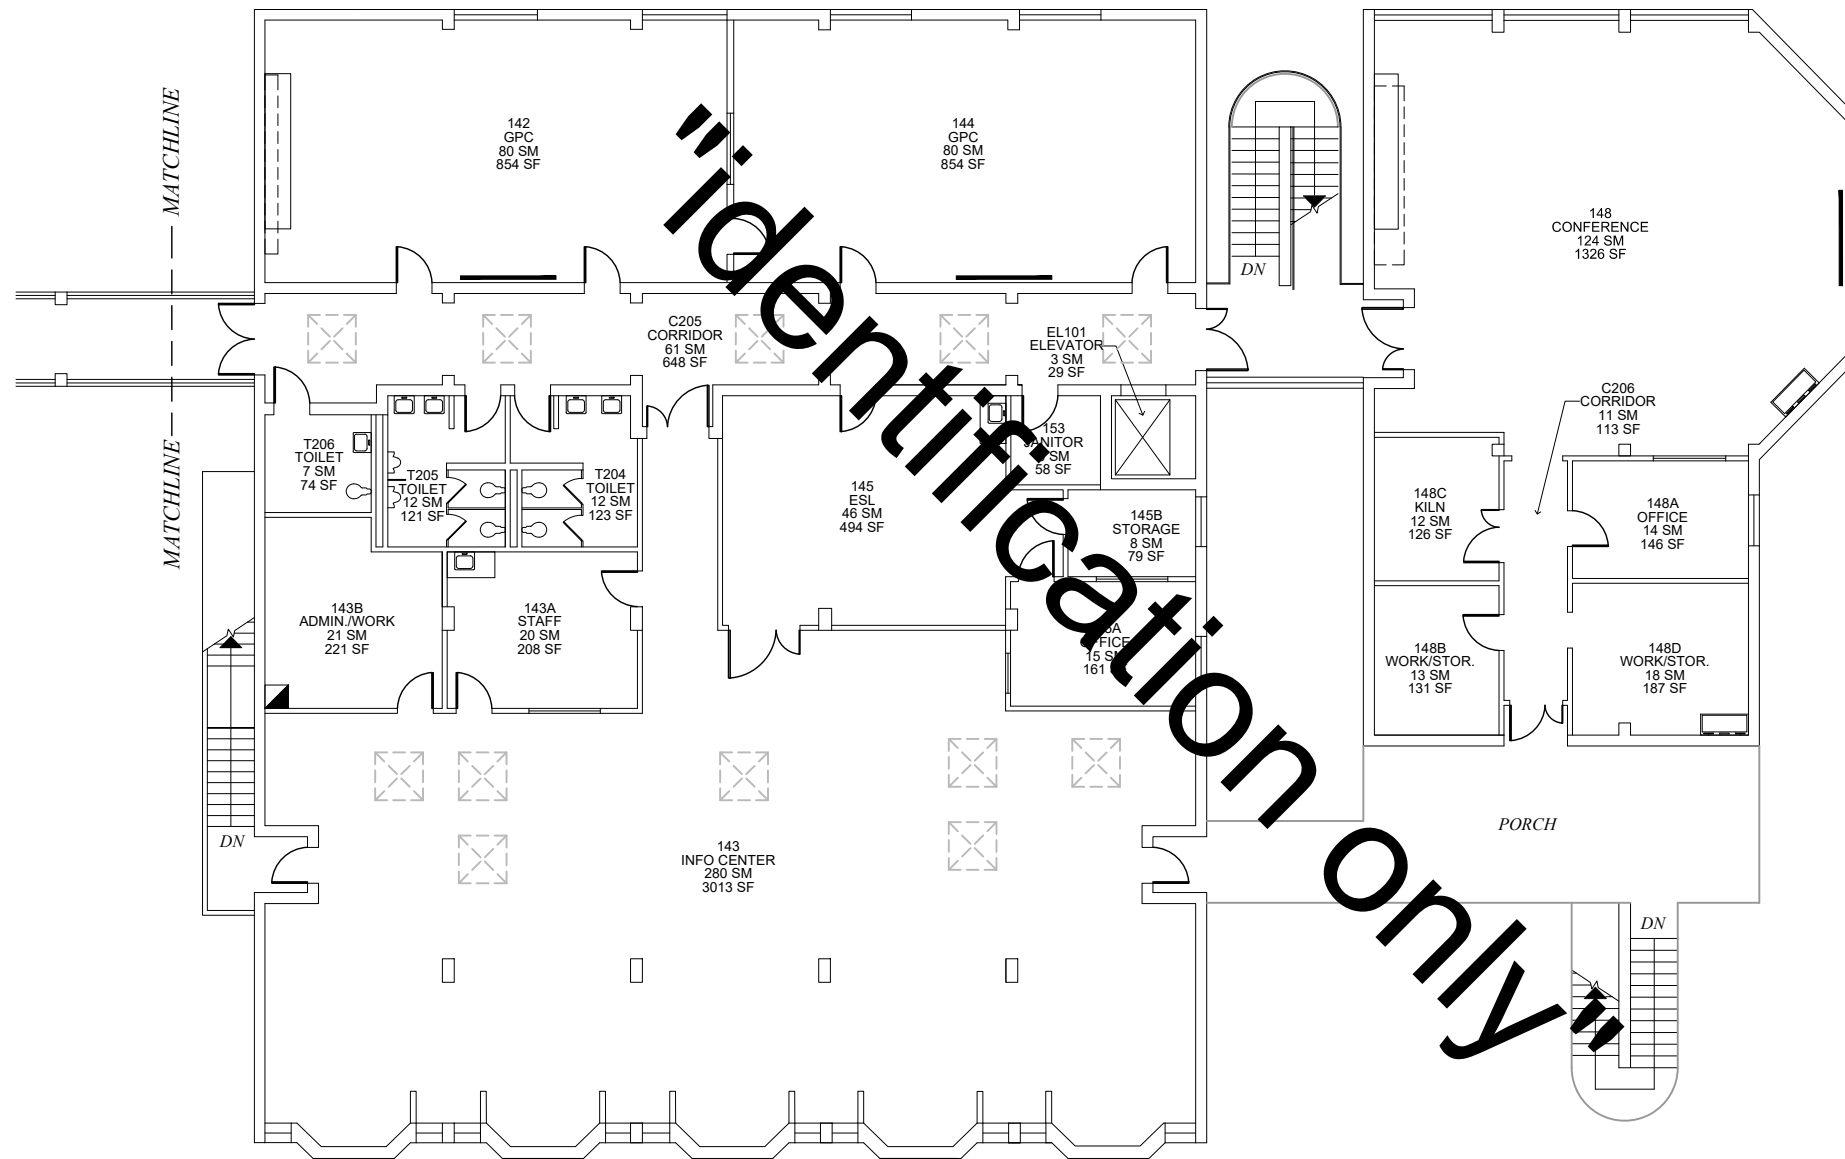

SYMBOL LEGEND

DOOR	DRINKING FOUNTAIN
SLIDING DOOR	LAVATORY
ACCORDION PARTITION	SINK
STACK OR FOLDING PARTITION	TOILET
WINDOW/GLAZING	URINAL
HIGH WINDOW	LOCKER
SKYLIGHT	LAN DISTRIBUTION FRAME
STOOP/STEP UP	VENT HOOD
STAIR	WALL SHELVING
RAMP	UPPER CABINET
ACCESS LADDER	BASE CABINET
COLD STORAGE	TEACHER CABINET
AREA CALCULATED @ 50 %	MATCHLINE
SLOPING ROOF	FLAT ROOF

TITLEBLOCK LEGEND

SHEET NAME:	BLDG #_FLOOR # (# IN SERIES)

KEY PLAN

NTS

Updated By: **SPF** FUS Review: **MRS** 100% Submittal Date: **01 MAY 2020**

0 2 4 8 16 FT


dodea

DEPARTMENT OF DEFENSE EDUCATION ACTIVITY

FACILITY UTILIZATION SURVEY


VICENZA HIGH SCHOOL /
DoDEA EUROPE SOUTH DSO
BUILDING NUMBER: 309
COUNTRY: ITALY
INSTALLATION: US ARMY GARRISON ITALY
SITE: CAMP EDERLE
REGION-DISTRICT: DODEA EUROPE SOUTH

DoDAAC Number: HE5419, HE5468	Floor: LEVEL 2	Survey Date: JANUARY 2020
Sheet Name: 309_2 (5)	Sheet Seq: 17 of 19	

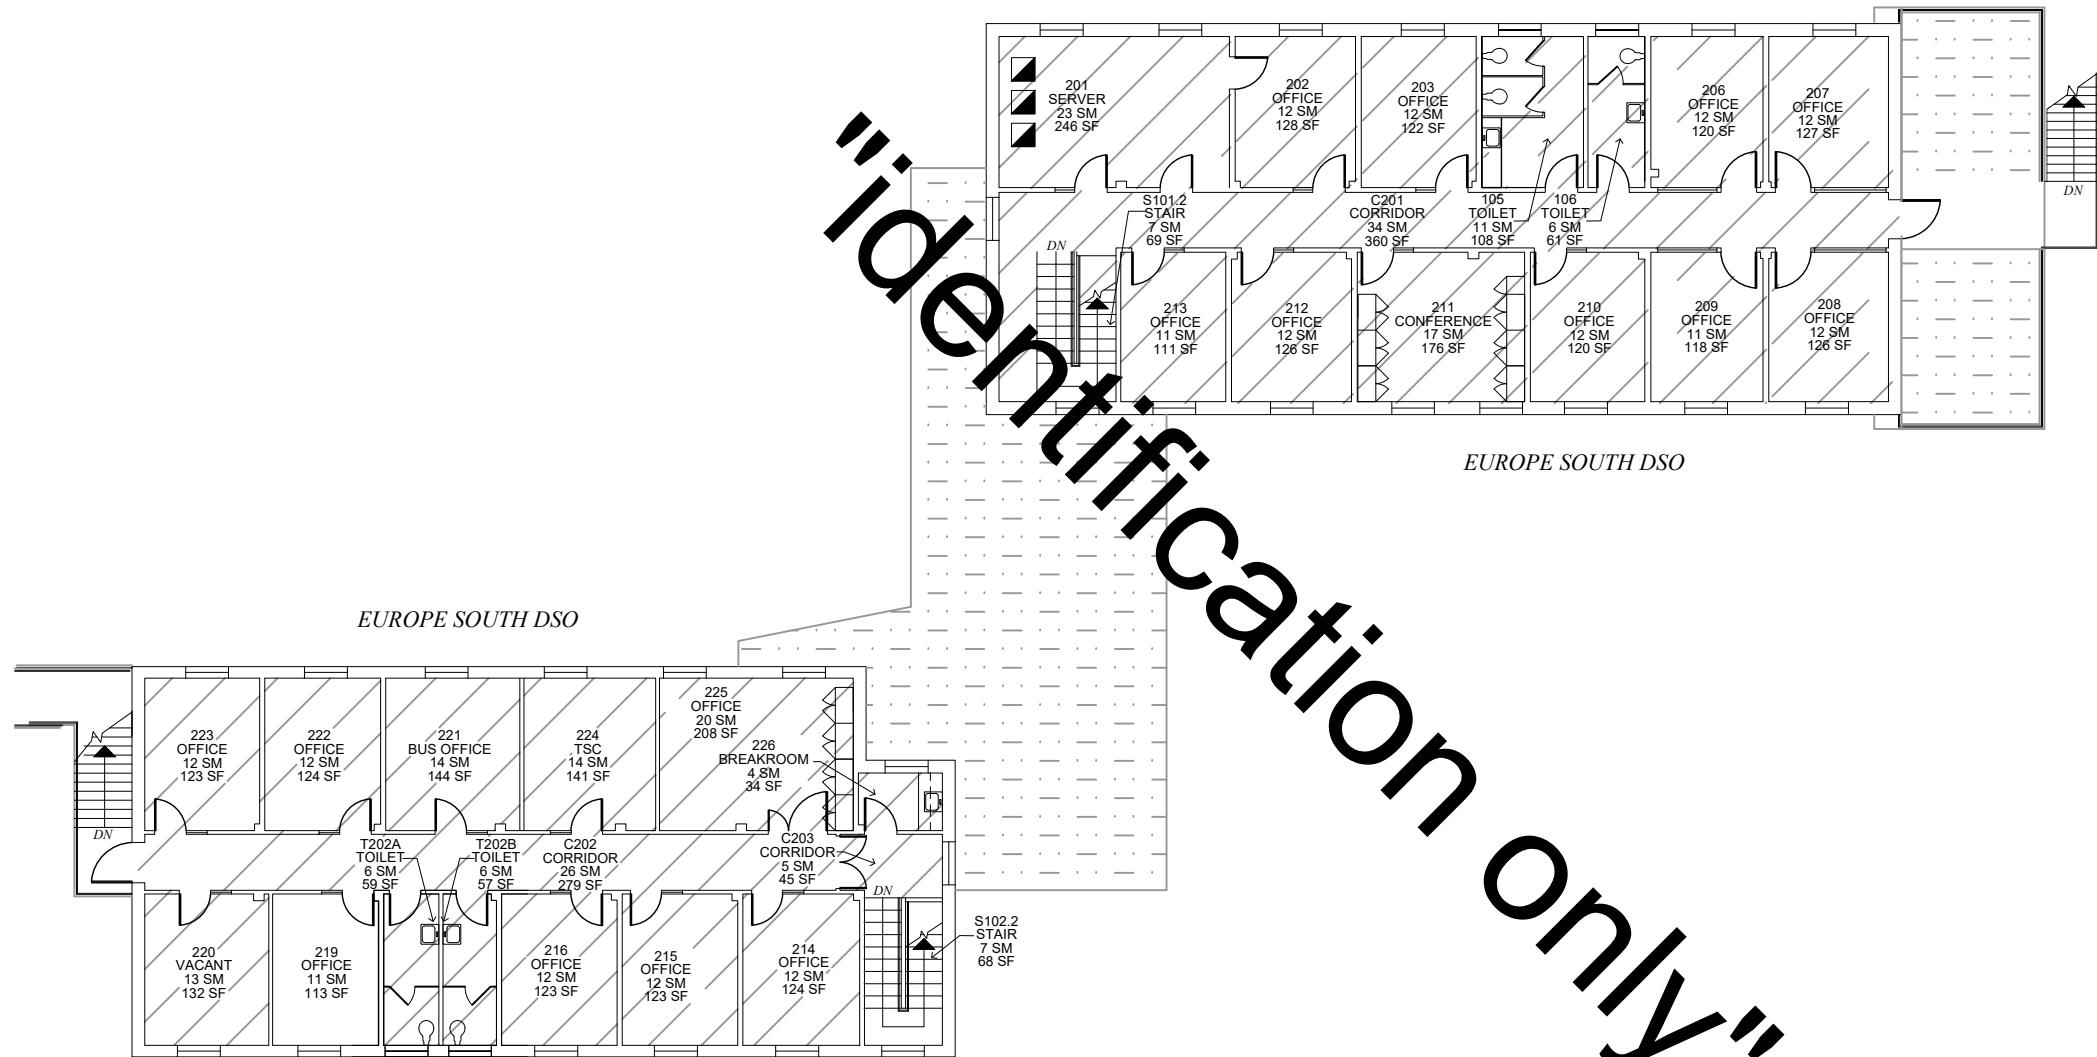

SYMBOL LEGEND	
	DOOR
	DRINKING FOUNTAIN
	SLIDING DOOR
	LAVATORY
	ACCORDION PARTITION
	SINK
	STACK OR FOLDING PARTITION
	TOILET
	WINDOW/GLAZING
	URINAL
	HIGH WINDOW
	LOCKER
	SKYLIGHT
	LAN DISTRIBUTION FRAME
	STOOP/STEP UP
	VENT HOOD
	STAIR
	WALL SHELVING
	RAMP
	UPPER CABINET
	ACCESS LADDER
	BASE CABINET
	COLD STORAGE
	TEACHER CABINET
	AREA CALCULATED @ 50 %
	MATCHLINE
	SLOPING ROOF
	FLAT ROOF

TITLEBLOCK LEGEND	
SHEET NAME:	BLDG #_FLOOR # (# IN SERIES)

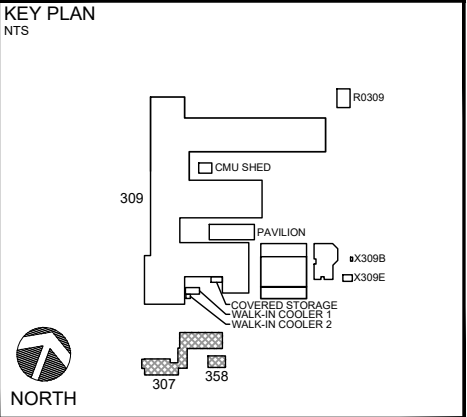

Updated By:	FUS Review:	100% Submittal Date:
SPF	MRS	01 MAY 2020
0 2 4 8 16 FT		

DEPARTMENT OF DEFENSE EDUCATION ACTIVITY
FACILITY UTILIZATION SURVEY

VICENZA HIGH SCHOOL /
DoDEA EUROPE SOUTH DSO
BUILDING NUMBER: 307
COUNTRY: ITALY
INSTALLATION: US ARMY GARRISON ITALY
SITE: CAMP EDERLE
REGION-DISTRICT: DODEA EUROPE SOUTH

DoDAAC Number: HE5419, HE5468	Floor: LEVEL 2	Survey Date: JANUARY 2020
Sheet Name: 307_2 (1)	Sheet Seq:	19 of 19